


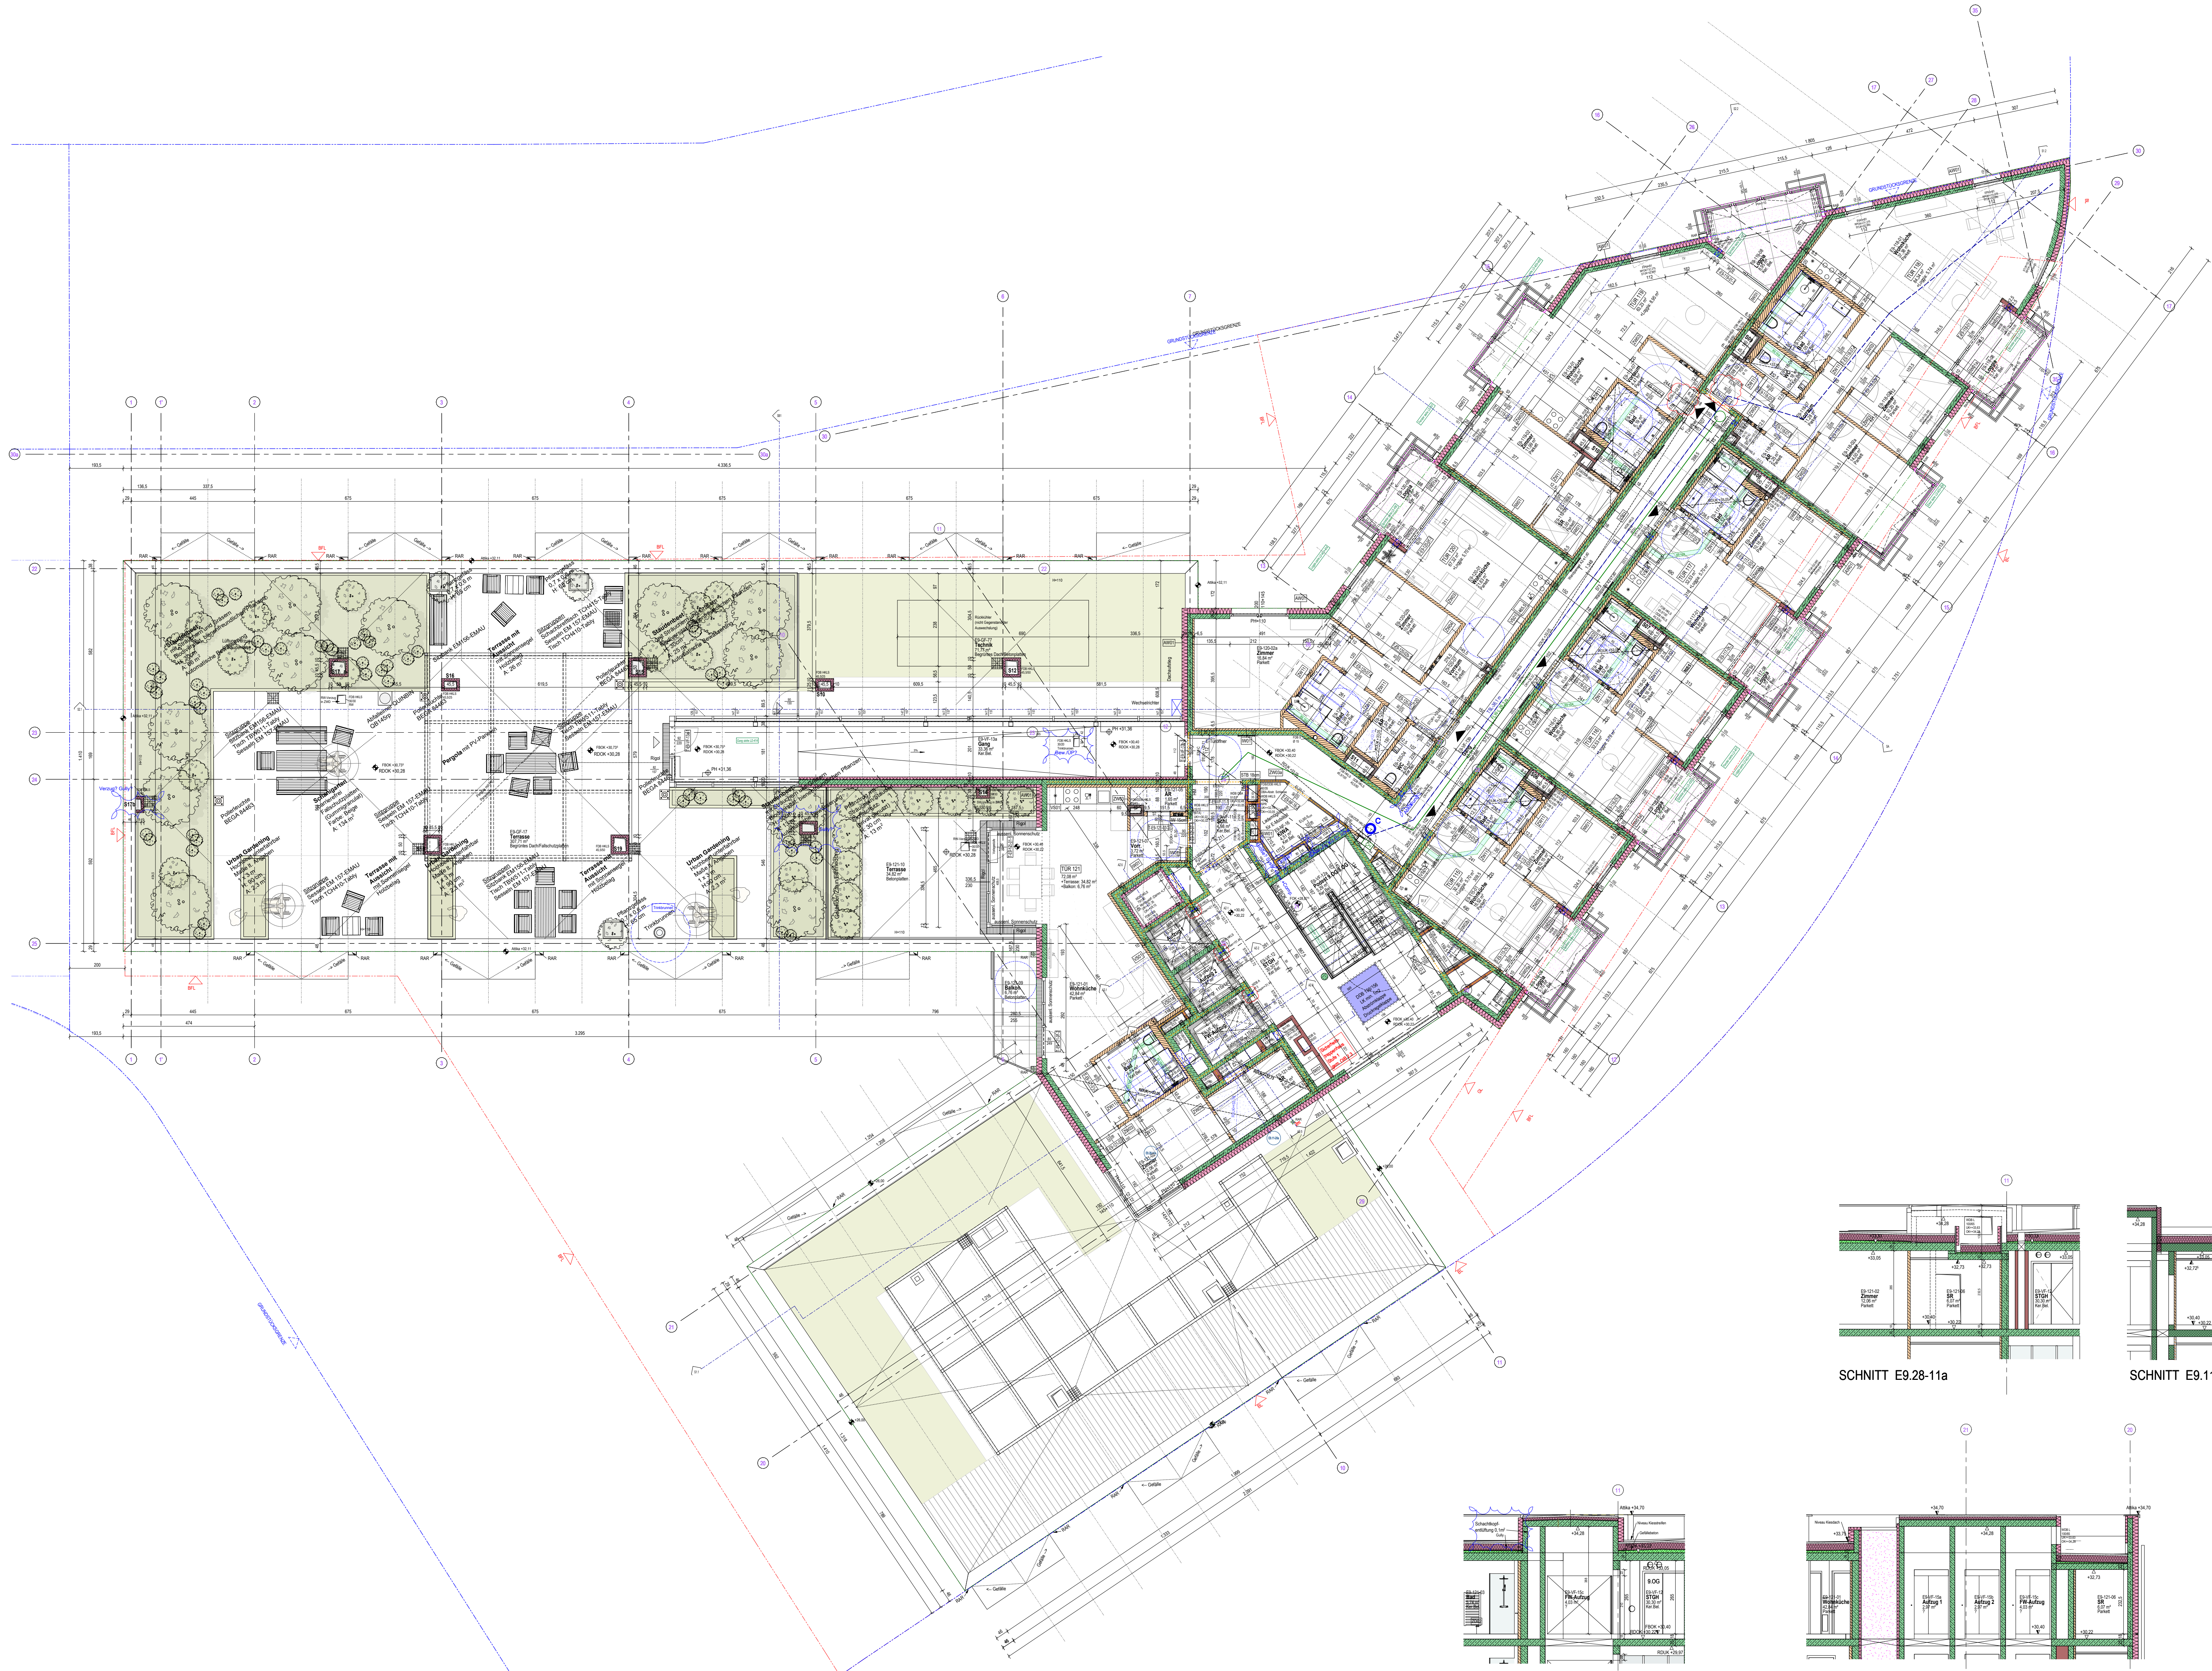

LEGENDE

- STAHLBETON
- BETON
- GIPSKARTONSTÄNDERWAND EI0
- GIPSKARTONSTÄNDERWAND EI30
- GIPSKARTONSTÄNDERWAND EI90
- ZIEGELMAUERWERK
- YTONG
- ALU-GLASKONSTRUKTIONEN
- WÄRMEDÄMMUNG
- BRANDABSCHNITT
- FLWL- FLUCHTWEGSLÄNGE
- TSL LÄNGE TSL
- TRÖCKENSTEIGLEITUNG

ABKÜRZUNGEN


- ADUK ... Unterkante abgehängter Decke
- AR ... Abstellraum
- BRE ... Brandschutzeinführung
- BST ... Brandschutzstürze
- DBA ... Druckbelüftungsanlage
- DDB ... Deckendurchbruch
- F+H ... Feuerlöscher und Hydrantenkasten
- FDB ... Fußbodendurchbruch
- FOK ... Fußbodenoberkante
- FSTZ ... Feinstreuzugbelag
- FW ... Feuerwehreinfahrt
- HT ... Haustechnikanlage
- NU ... Notüberlauf
- ROK ... Rohoberkante
- RR ... Regenrohr
- RUH ... Rohunterkante
- STGH ... Stiegenhaus
- UZUK ... Unterzugunterkante
- VR ... Vorraum
- WDB ... Wanddurchbruch

NATURMASSE NEHMEN KOTEN PRÜFEN
±0,00 = +6,90 ü. Wiener Null (ü. WN)

© HNP architects ZT GmbH
DIESER DOKUMENT IST URHEBERRECHTLICH GESCHÜTZT. JEDE WEITVERWENDUNG ODER BEARBEITUNG BEDARF DERAUSDRÜCKLICHEN ZUSTIMMUNG VON HNP architects

INDEX	DATUM	GEZ.	ÄNDERUNG
A	30.10.2025		Abstimmung erforderlich
B	20.01.2026		VORABZUG-Planstand Nutzwertgutachten
C	10.03.2026		Änderung zur Ausgabe
D	07.05.2026		Änderung zur Ausgabe

FREIGABE:	BH	ÖBA	ELT	HKLS	TWP	BP	BS
DATUM:							
NAME:							
UNTERSCHR.							

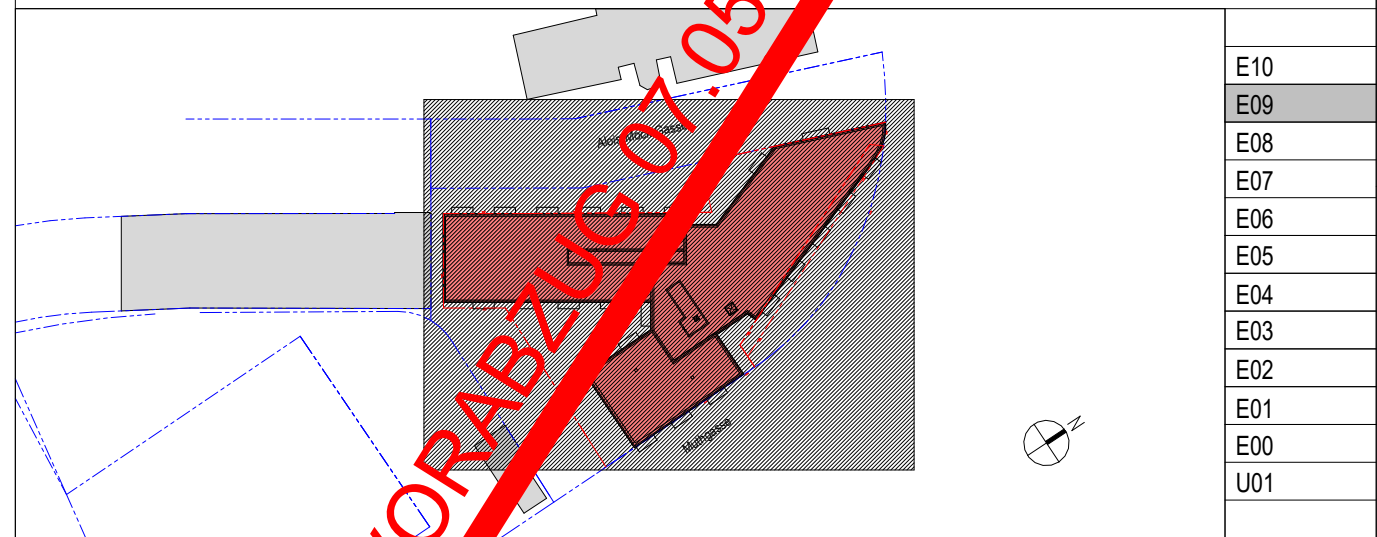

Bauherr:	GEWOG Gemeinnützige Wohnungsbau-Ges.m.b.H. Hermesgasse 1, 1170 Wien	at home Immobilien-GmbH Zweigniederlassung Wien Hermesgasse 1, 1170 Wien
ROHBAU POLIERPLAN Muthgasse 109B, 1190 WIEN		
PLANNUMMER:	4-992-23	PR NR: 4-992-23
PLANNUMMER:	4-992-23	DATUM: 22.04.2024
PLANNUMMER:	4-992-23	INDEXDATUM: 07.05.2026
PLANNUMMER:	4-992-23	PL GR: 1050x650
PLANNUMMER:	4-992-23	GEZ: HNP
PLANNUMMER:	4-992-23	GEPR: EZ
PLANNUMMER:	4-992-23	MASSSTAB: 1:100

HNP ARCHITECTS ZT GMBH
A-1190 WIEN - MUTHGASSE 109
+43 1 370 16 16-0 FAX DW6
OFFICE@HNP-ARCHITECTS.COM