

W01 | Markierungen am Originalausschnitt

Außenkante

Die äußere Begrenzung läuft um die Gebäudeecke.

Innenkante


Diese Kante grenzt die Mauer vom Raumboden ab.

Material

Die Schraffur liegt innerhalb des Wandkörpers.

Öffnung

Das Fenster unterbricht die Mauer; es ist kein freier Durchgang.

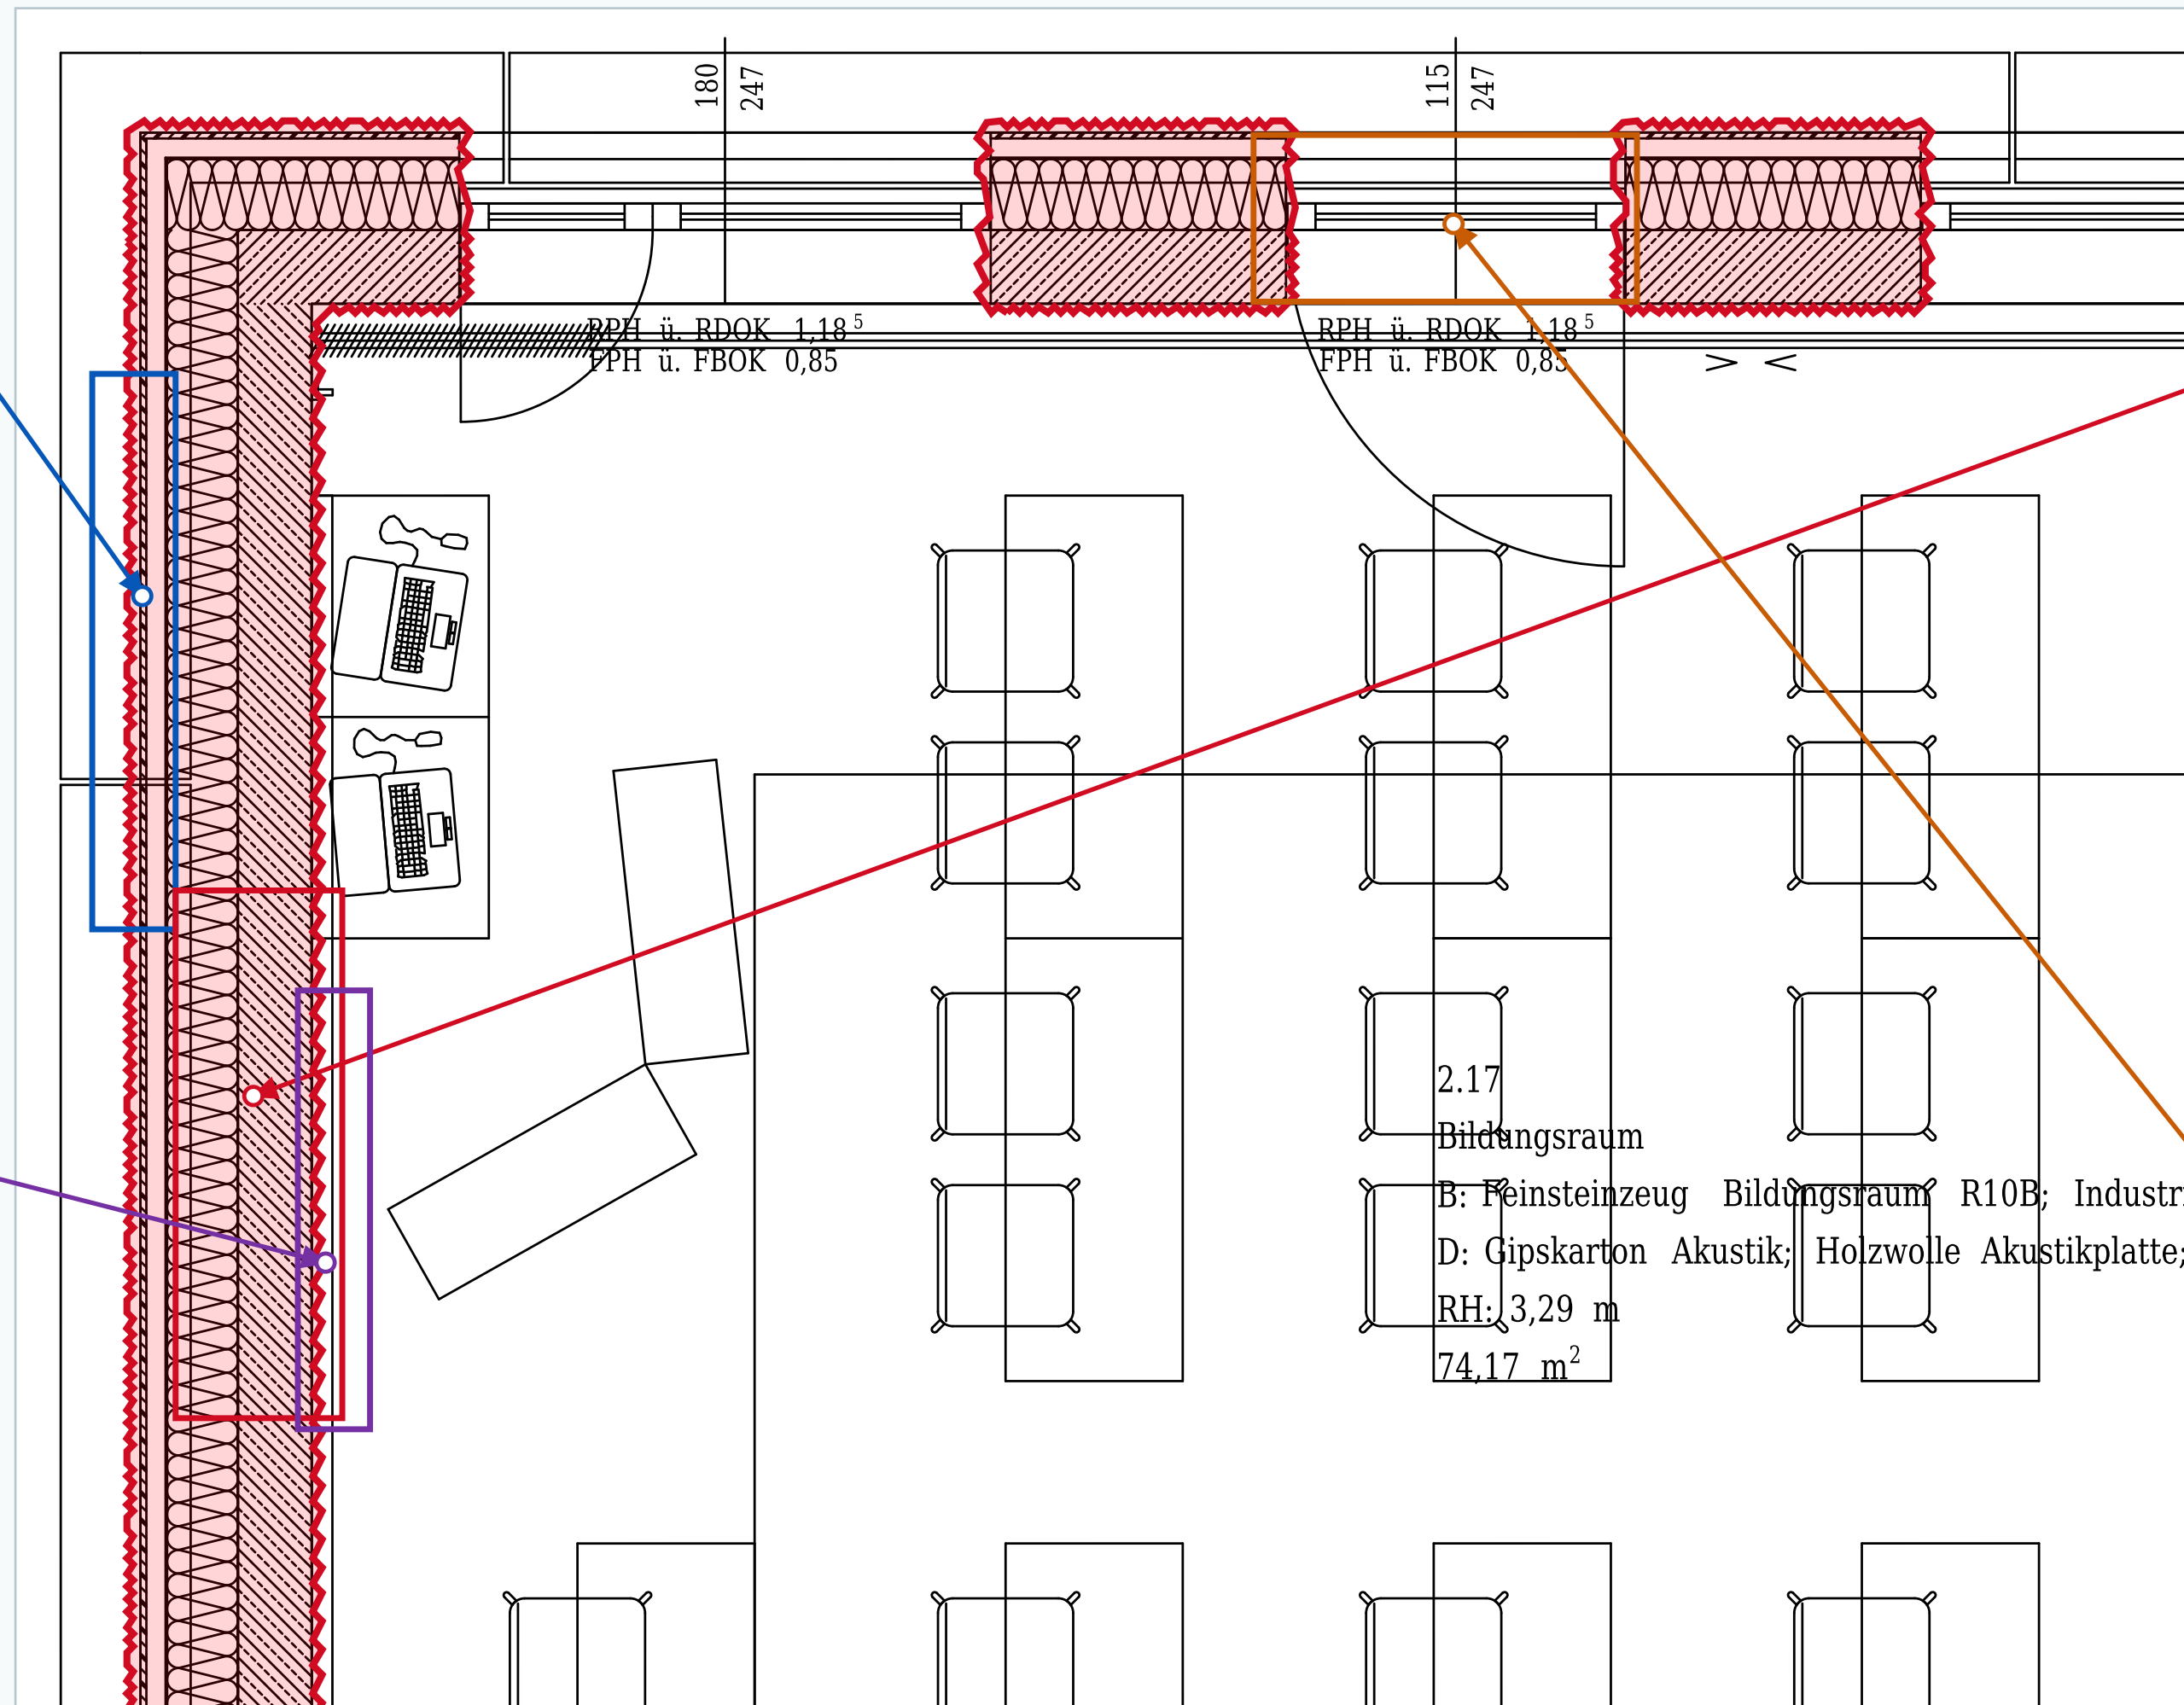

Geschlossener Rahmen + Pfeil: erklärter Bereich. Farblinien: hervorgehobene Merkmale.

W02 | Markierungen am Originalausschnitt

Breiter Aufbau

Der Rahmen umfasst den Wandquerschnitt mit seinen Schichten.

Dämmung


Wiederholte Schleifen und Schräglinien liegen zwischen den Kanten.

Eckanschluss

Die Außenmauer setzt sich am rechten Gebäuderand fort.

Raumseite

Auf der Innenseite beginnt die Bodenfläche des Bildungsraums.

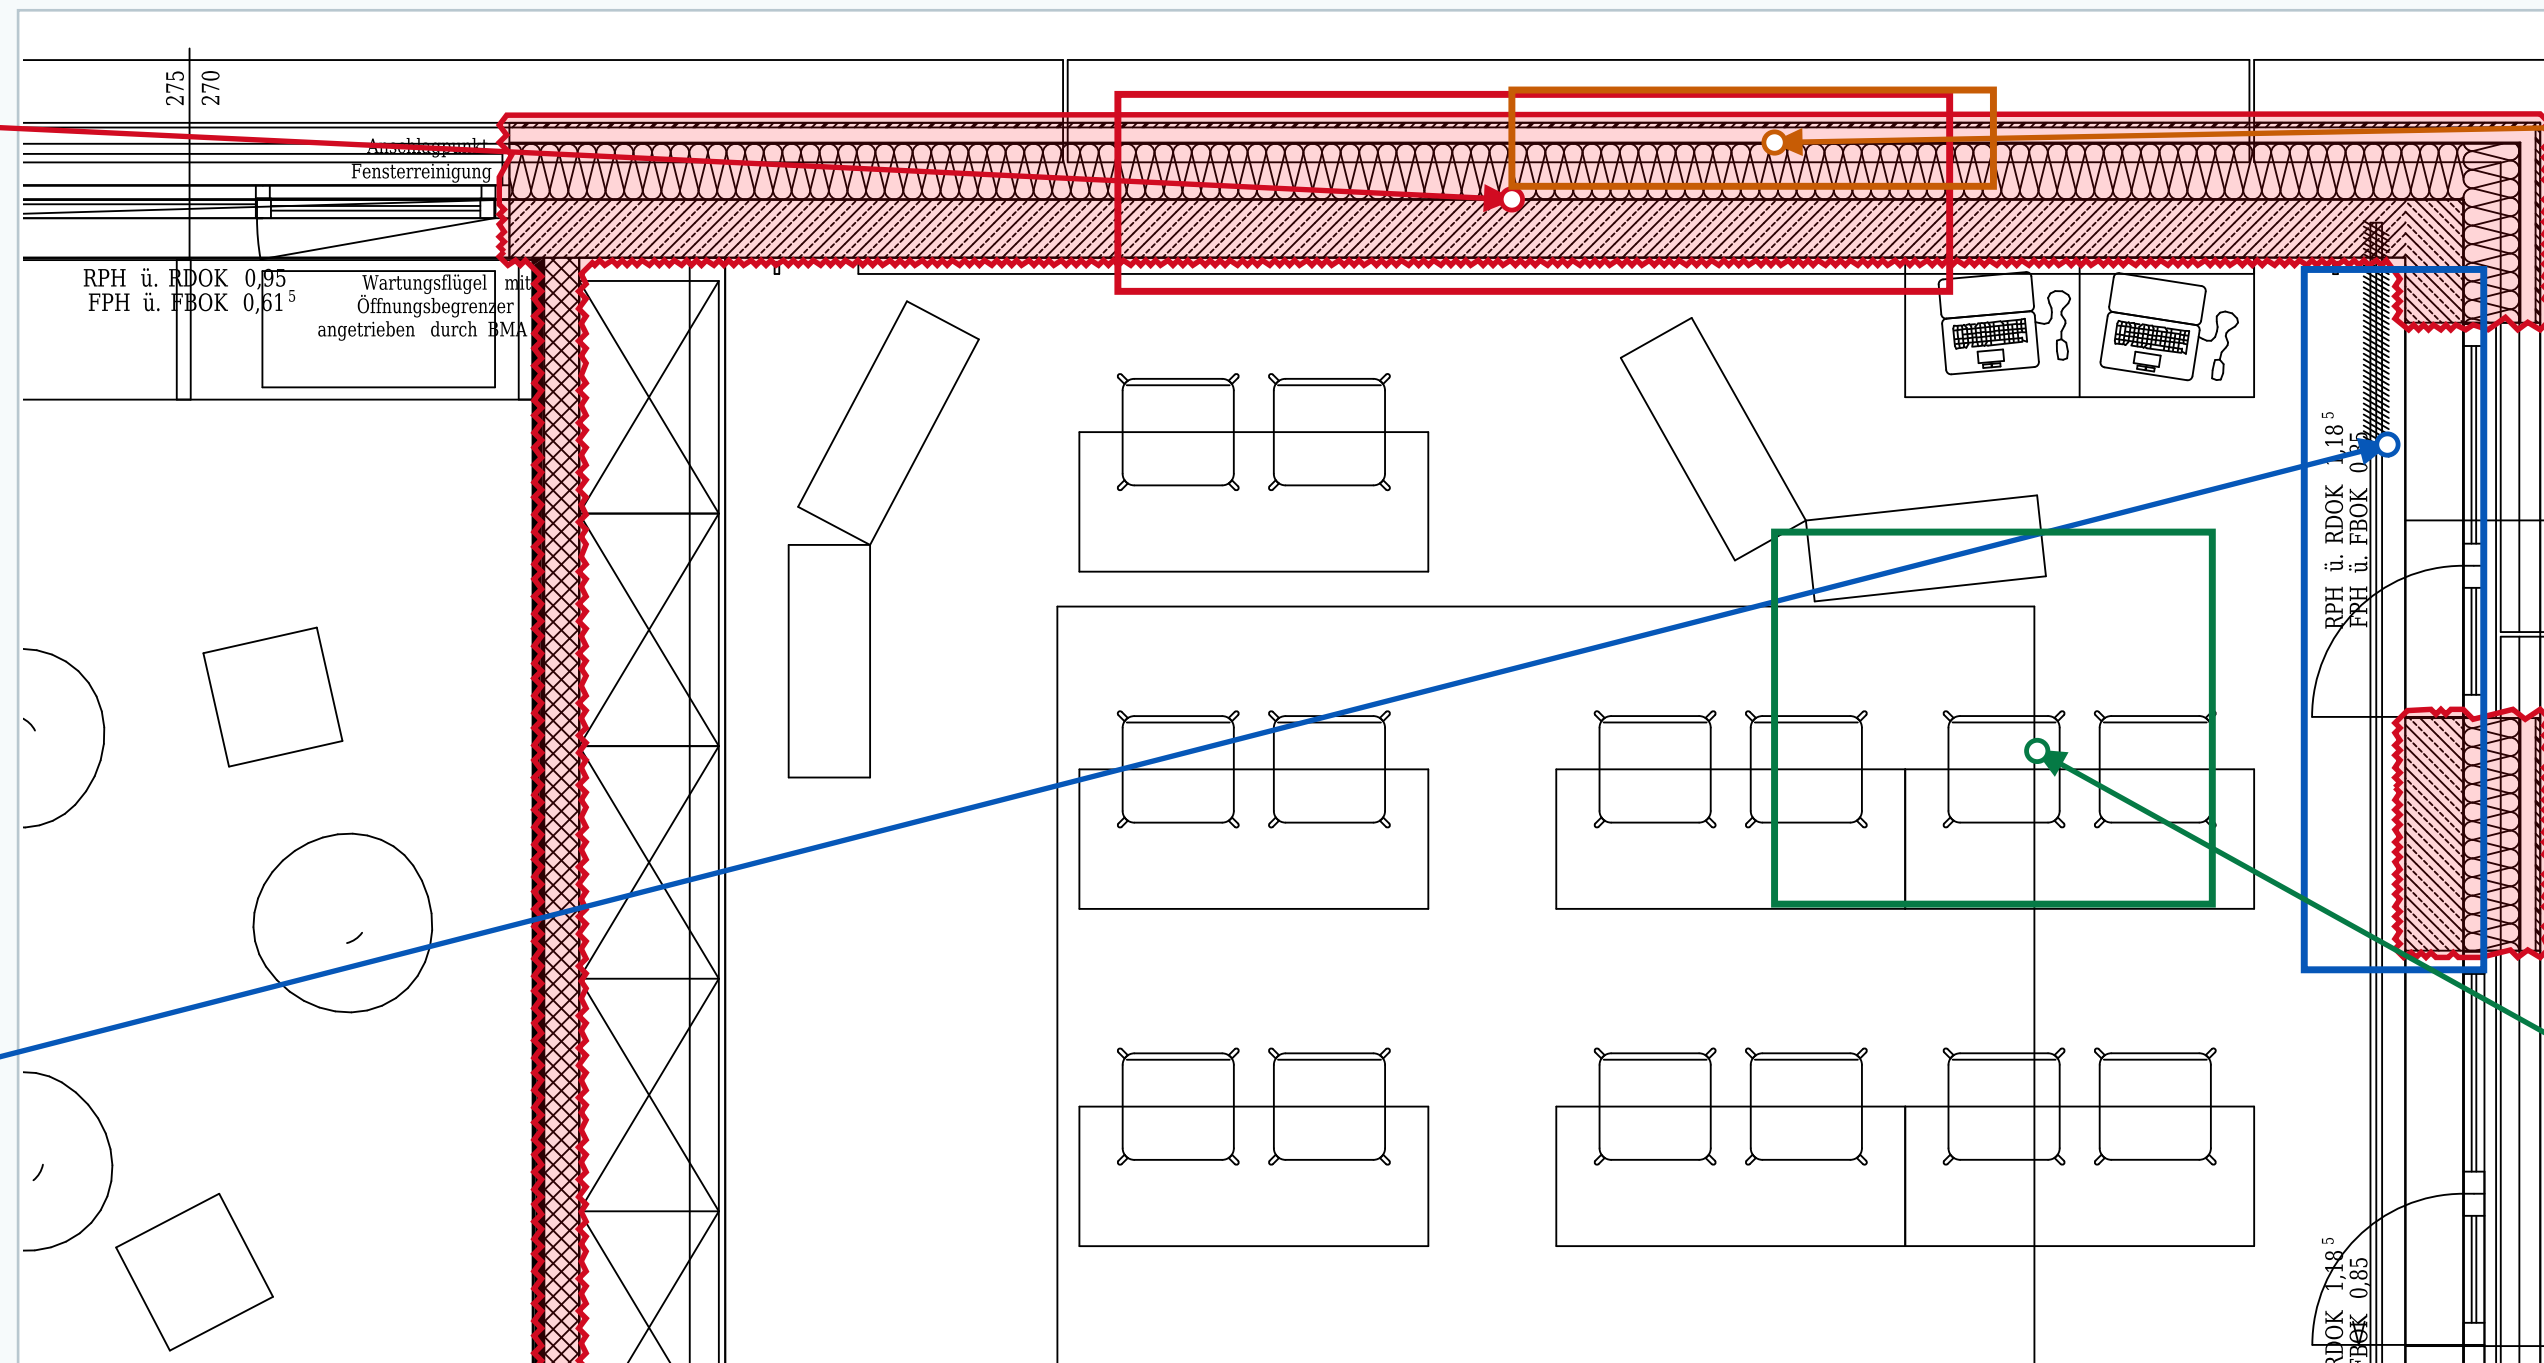

Geschlossener Rahmen + Pfeil: erklärter Bereich. Farblinien: hervorgehobene Merkmale.

W03 | Markierungen am Originalausschnitt

Wandstreifen

Die beiden Kanten fassen einen schraffierten Streifen ein.

Zwei Seiten


Links und rechts schließen verschiedene Bodenbereiche an.

Anschluss

Die Innenwand trifft am unteren Ende auf den Queraufbau.

Einbau daneben

Möbellinien sind eigenständige Objekte, keine Fortsetzung der Wand.

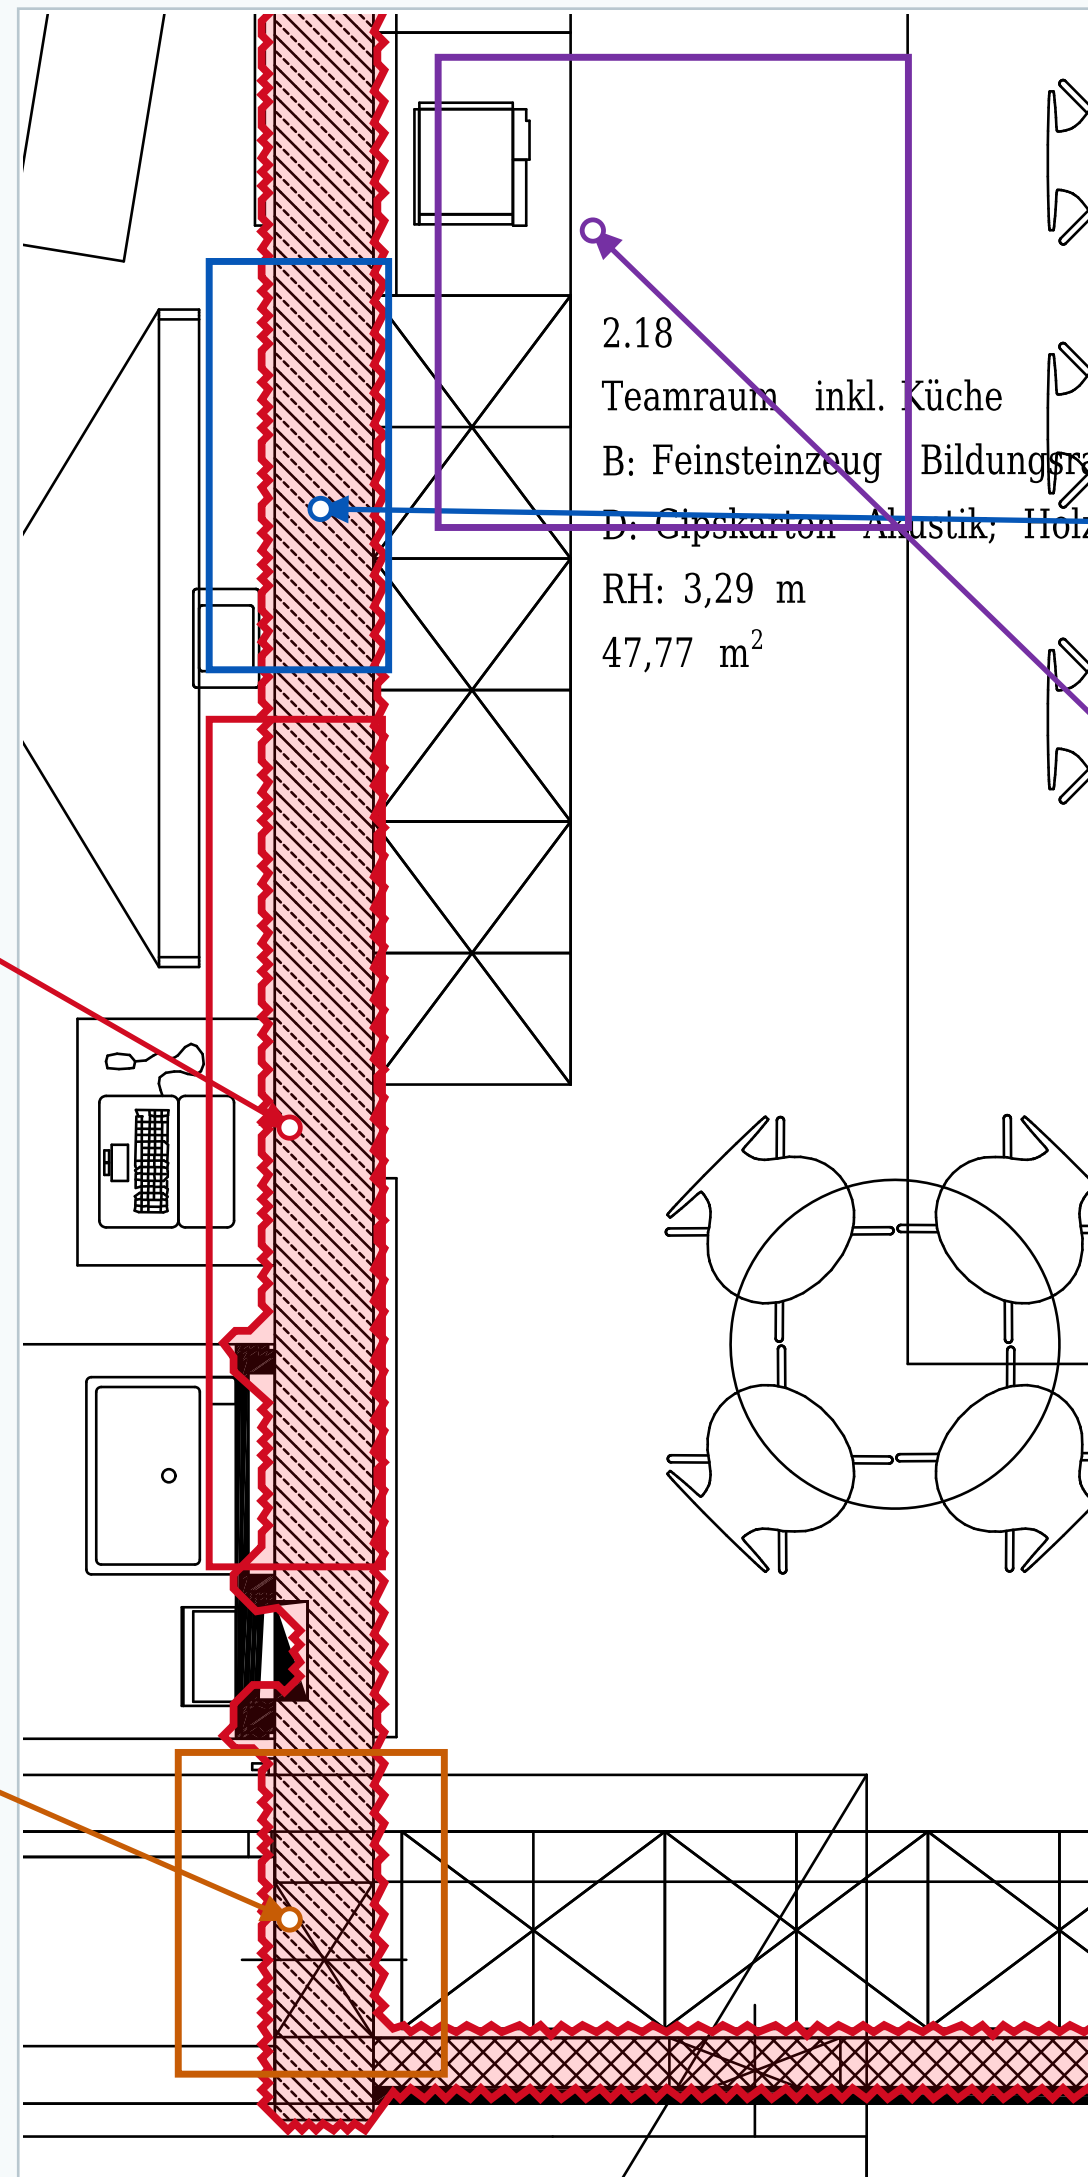

Geschlossener Rahmen + Pfeil: erklärter Bereich. Farblinien: hervorgehobene Merkmale.

W04 | Markierungen am Originalausschnitt

Seitliche Mauer

Der schraffierte Wandkörper läuft entlang des Kerns.

Querwand


Ein geschlossener Rahmen markiert das erklärte Querwandstück.

Anschluss

Hier treffen Längs- und Querwand ohne Durchgang aufeinander.

Sonderbereich

Die Beschriftung nennt einen Gitterrost-Wartungssteg.

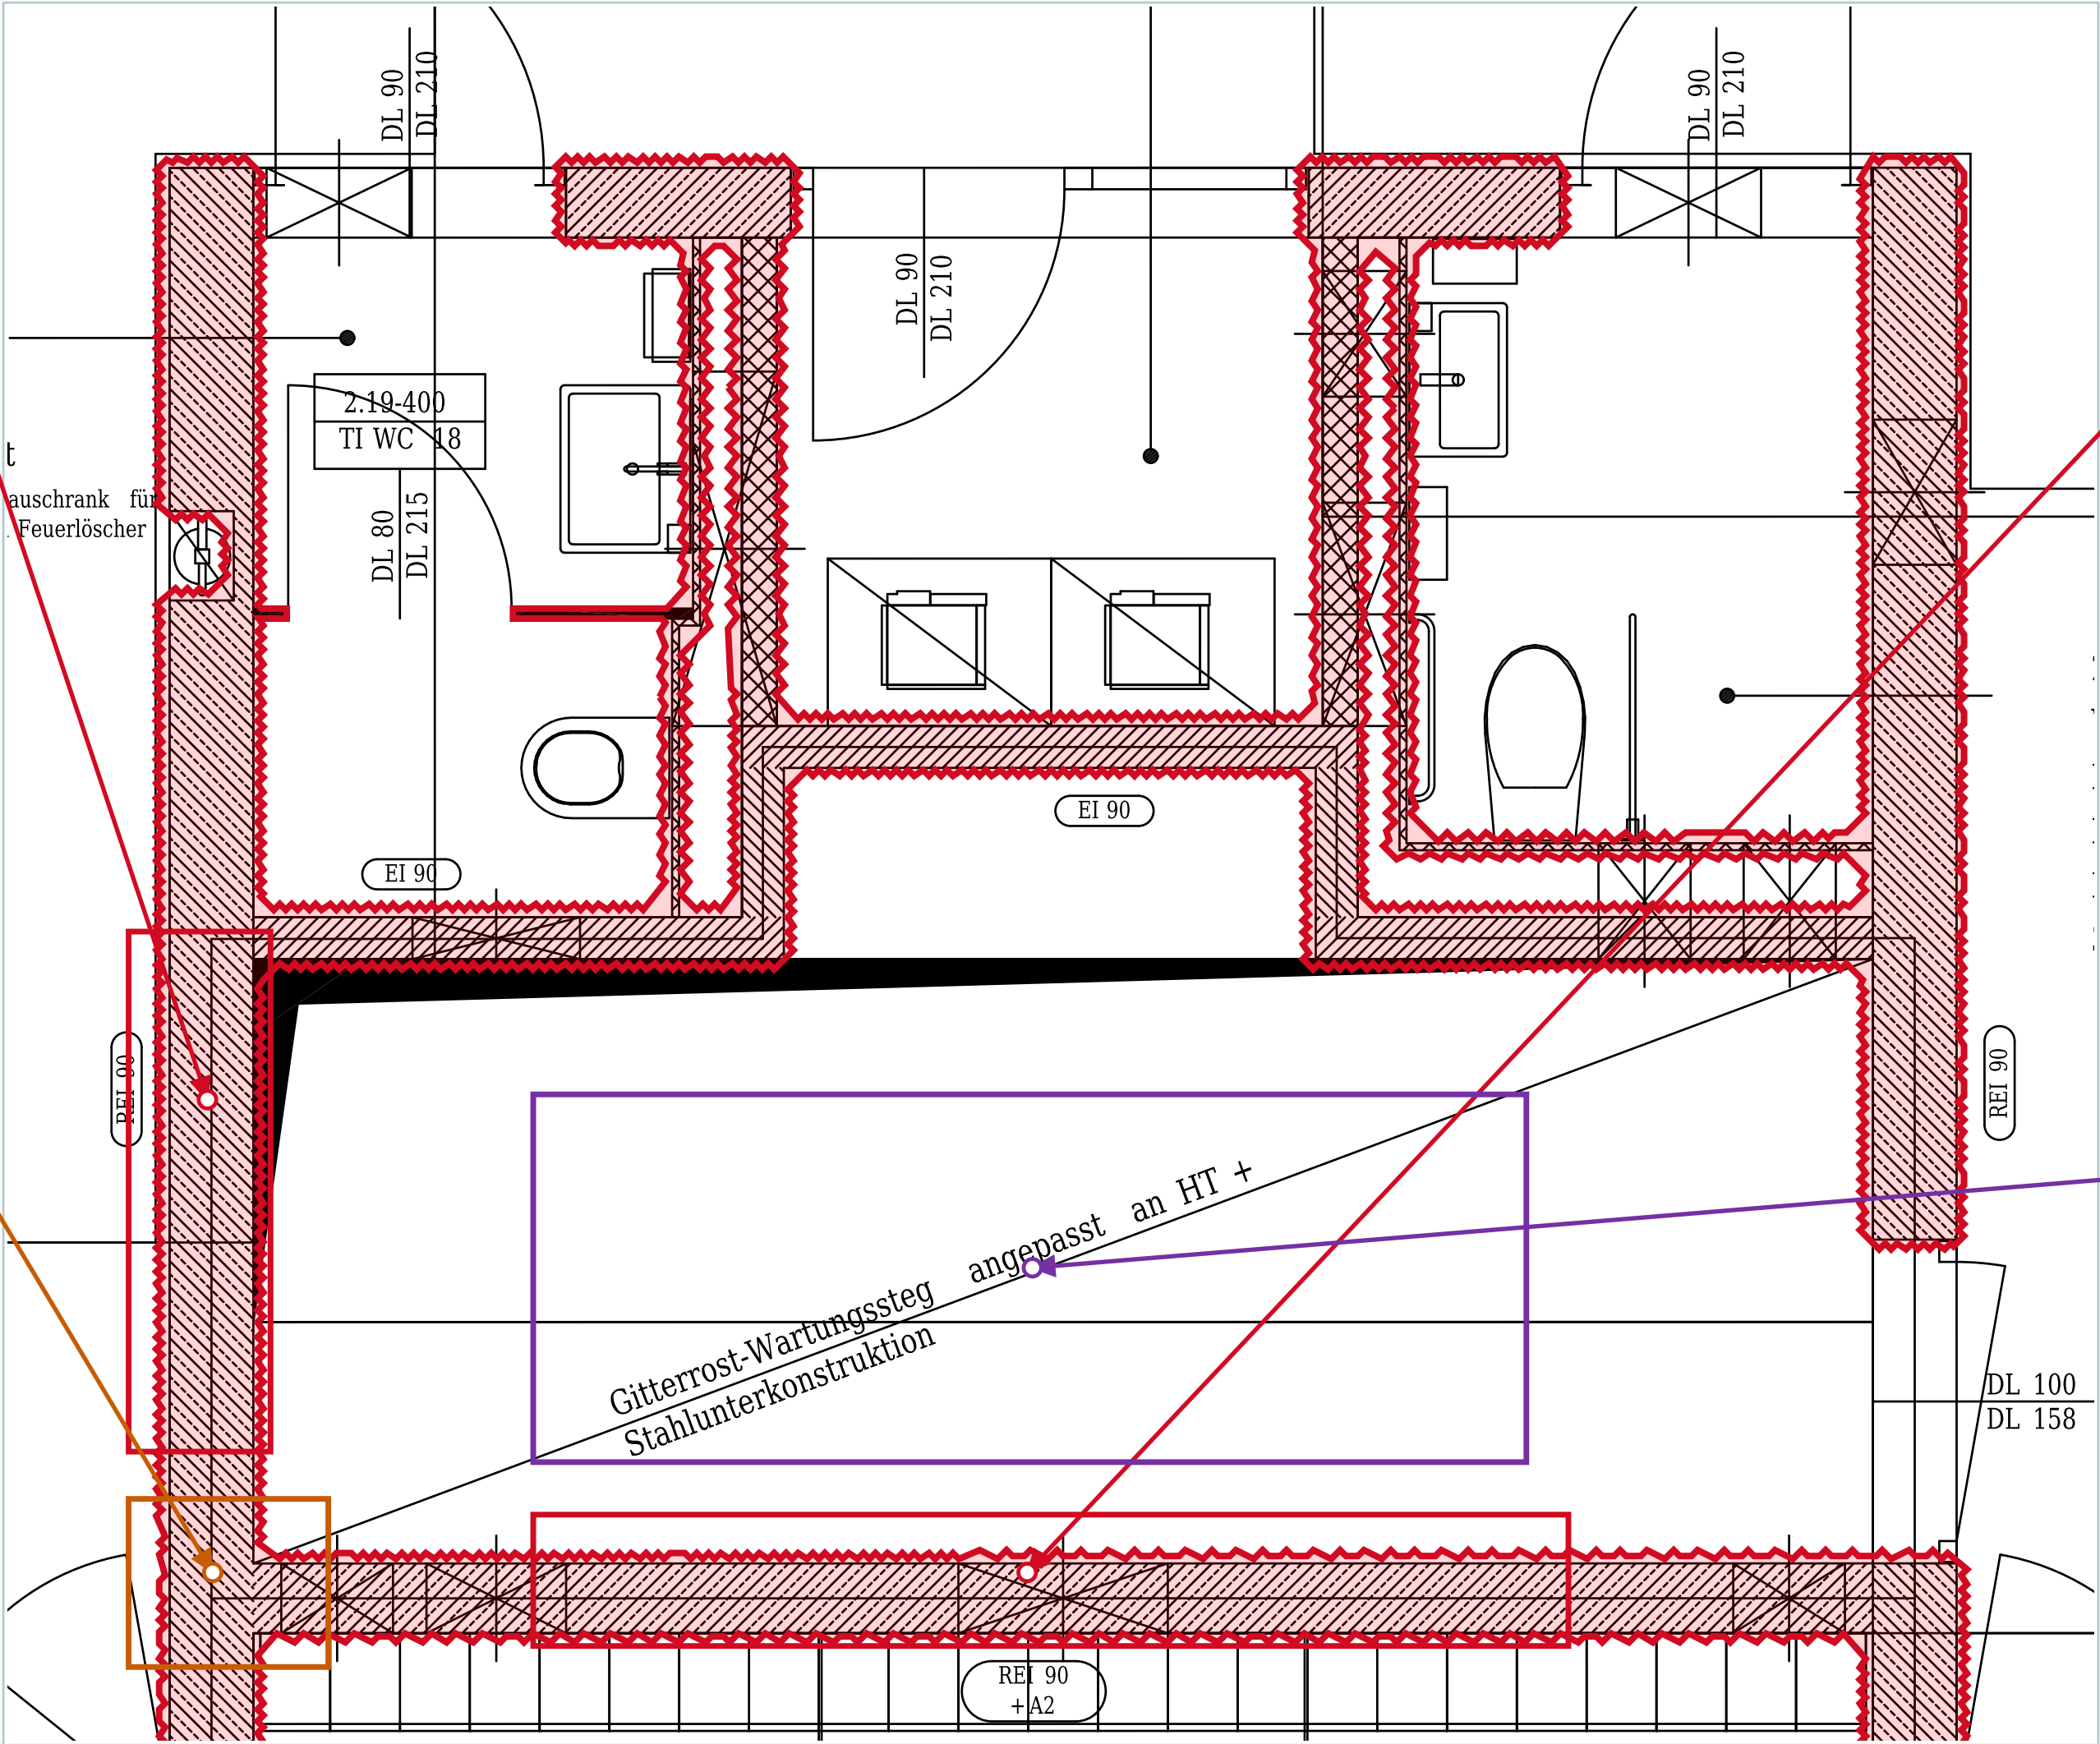

Geschlossener Rahmen + Pfeil: erklärter Bereich. Farblinien: hervorgehobene Merkmale.

W05 | Markierungen am Originalausschnitt

Dünne Trennwand

Zwei eng benachbarte Linien begrenzen das feste Trennwandstück.

Zweites Beispiel


Dasselbe Merkmal wiederholt sich an der nächsten Kabine.

Türblatt

Die bewegliche Linie im Öffnungsbereich ist keine feste Mauer.

Raumbegrenzung

Die seitliche und untere Einfassung schließt an feste Bauteile an.

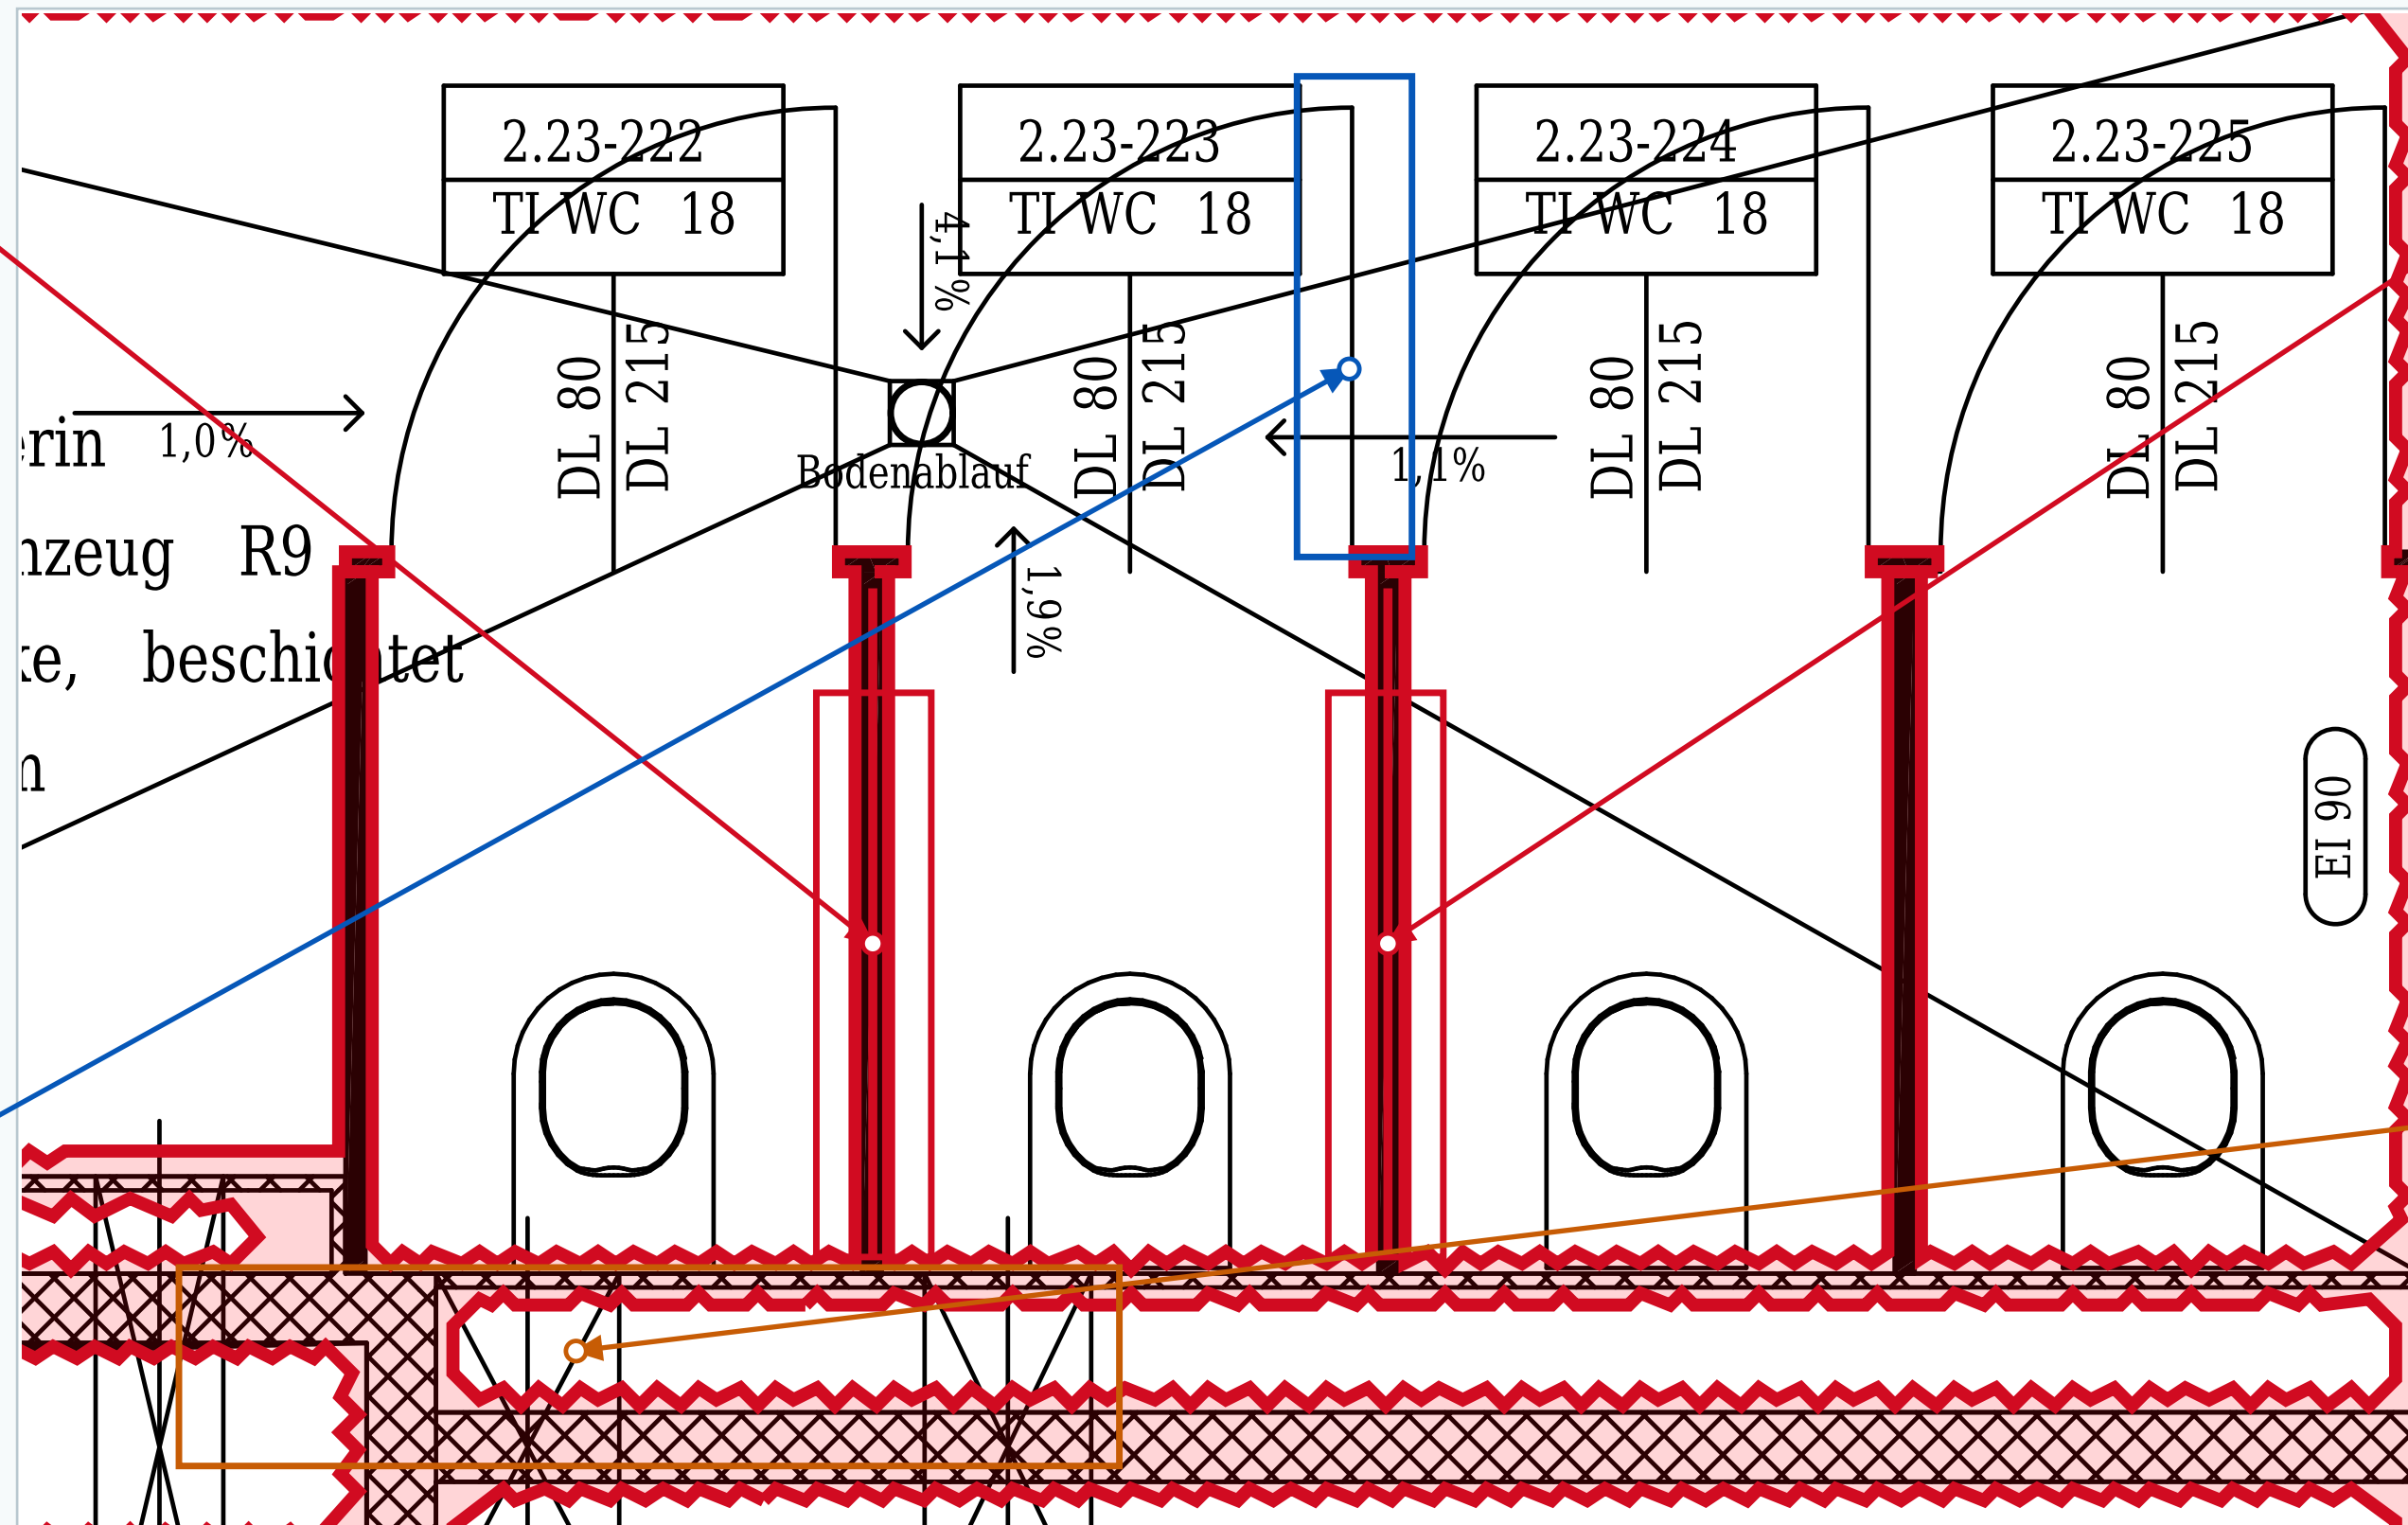

Geschlossener Rahmen + Pfeil: erklärter Bereich. Farblinien: hervorgehobene Merkmale.

W06 | Markierungen am Originalausschnitt

Feste Schachtwand

Der Rahmen umfasst den massiven seitlichen Wandstreifen.

Kabine


Die inneren Linien beschreiben den Aufzug, keinen Flur.

Türzone

Nur hier liegt der Zugang; nicht entlang der ganzen Schachtseite.

Bauteilbeleg

FWA und die Kabinenangaben stützen die Zuordnung.

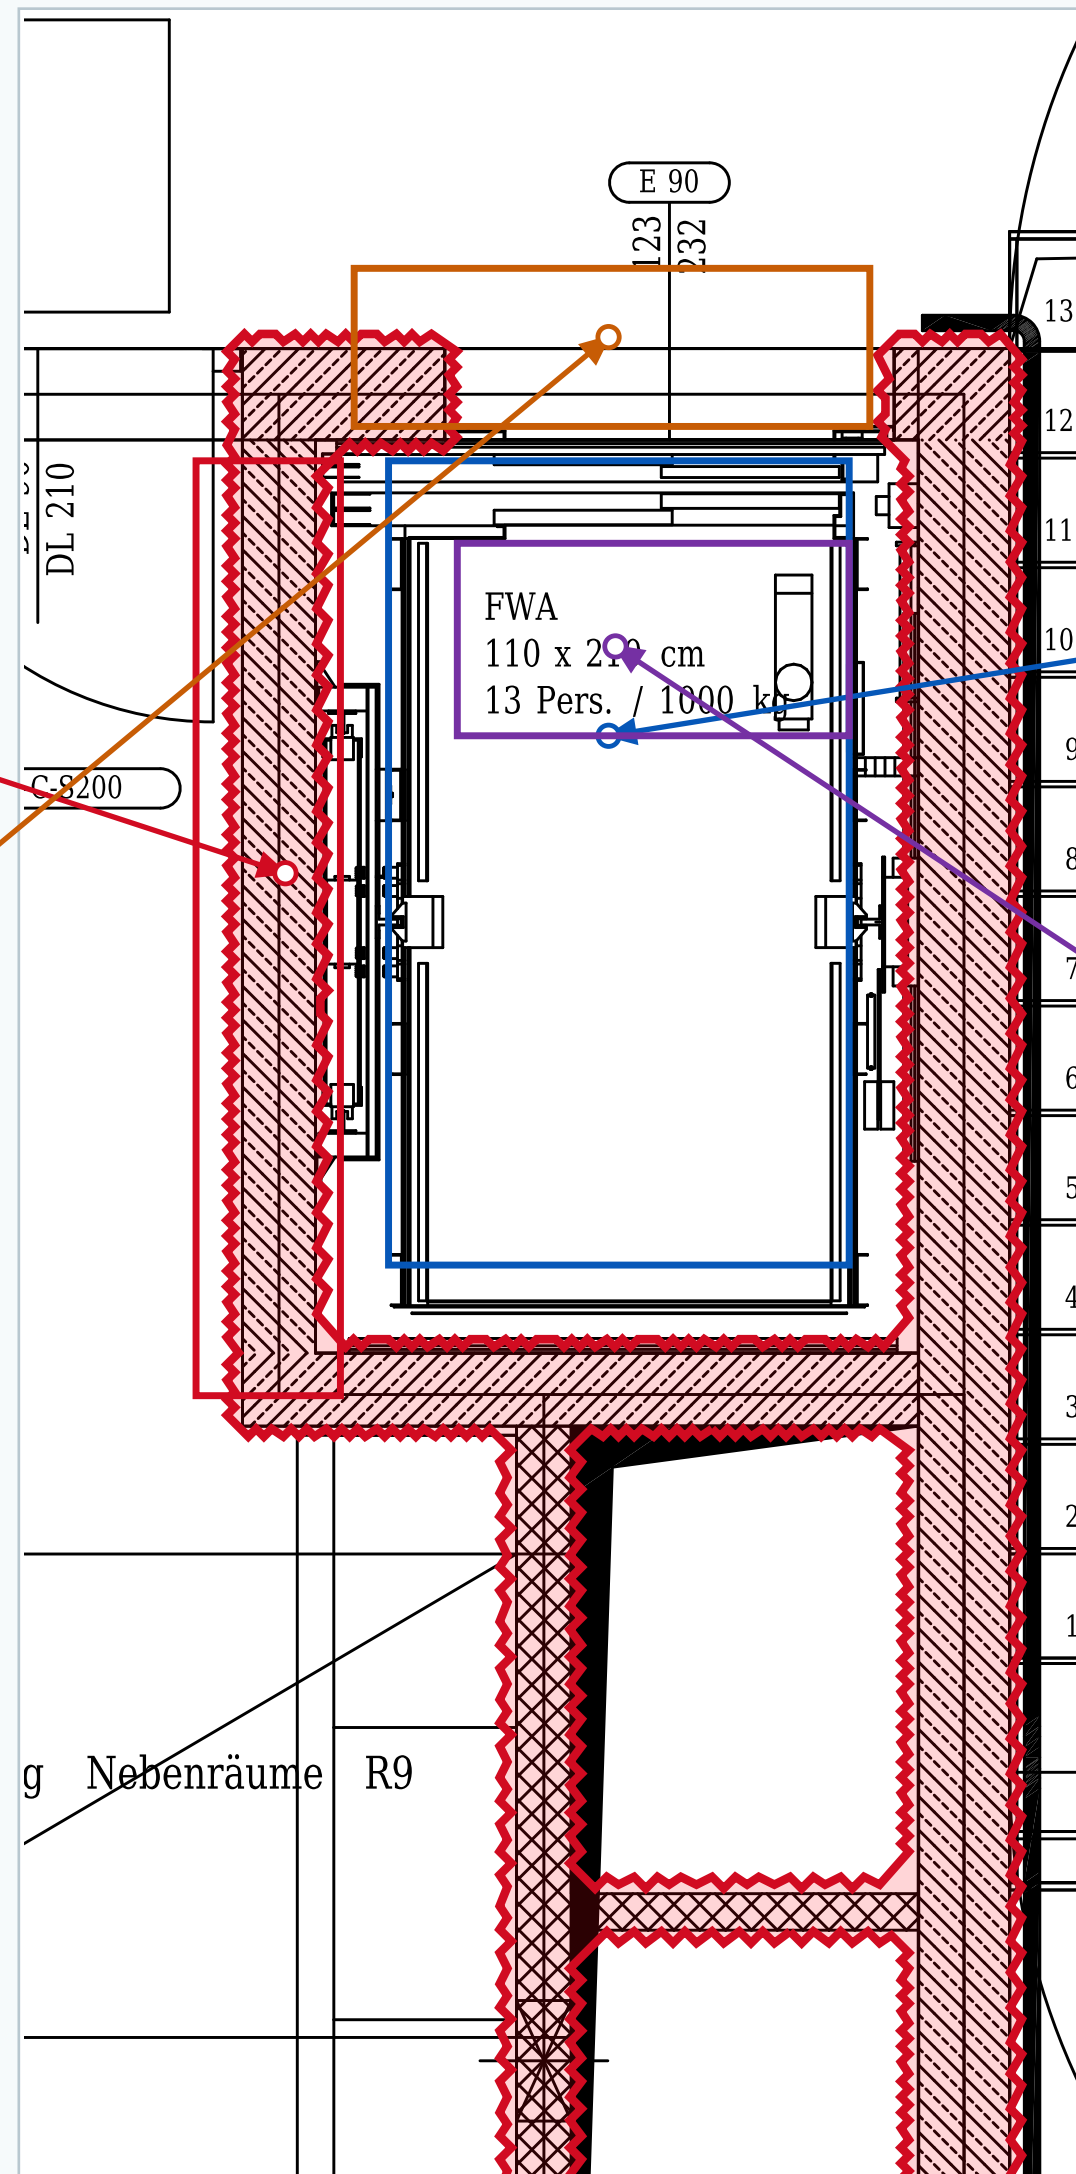

Geschlossener Rahmen + Pfeil: erklärter Bereich. Farblinien: hervorgehobene Merkmale.

W07 | Markierungen am Originalausschnitt

Stützenkörper

Ein kleiner geschlossener Körper mit Materialdarstellung.

Eigenes Hindernis


Auch ohne lange Wand ist der Körper nicht durchquerbar.

Umgehbare Fläche

Die Bodenfläche neben der Stütze ist gesondert erkennbar.

Maßhinweis

Die nahe Angabe 43/43 gehört zur Stütze.

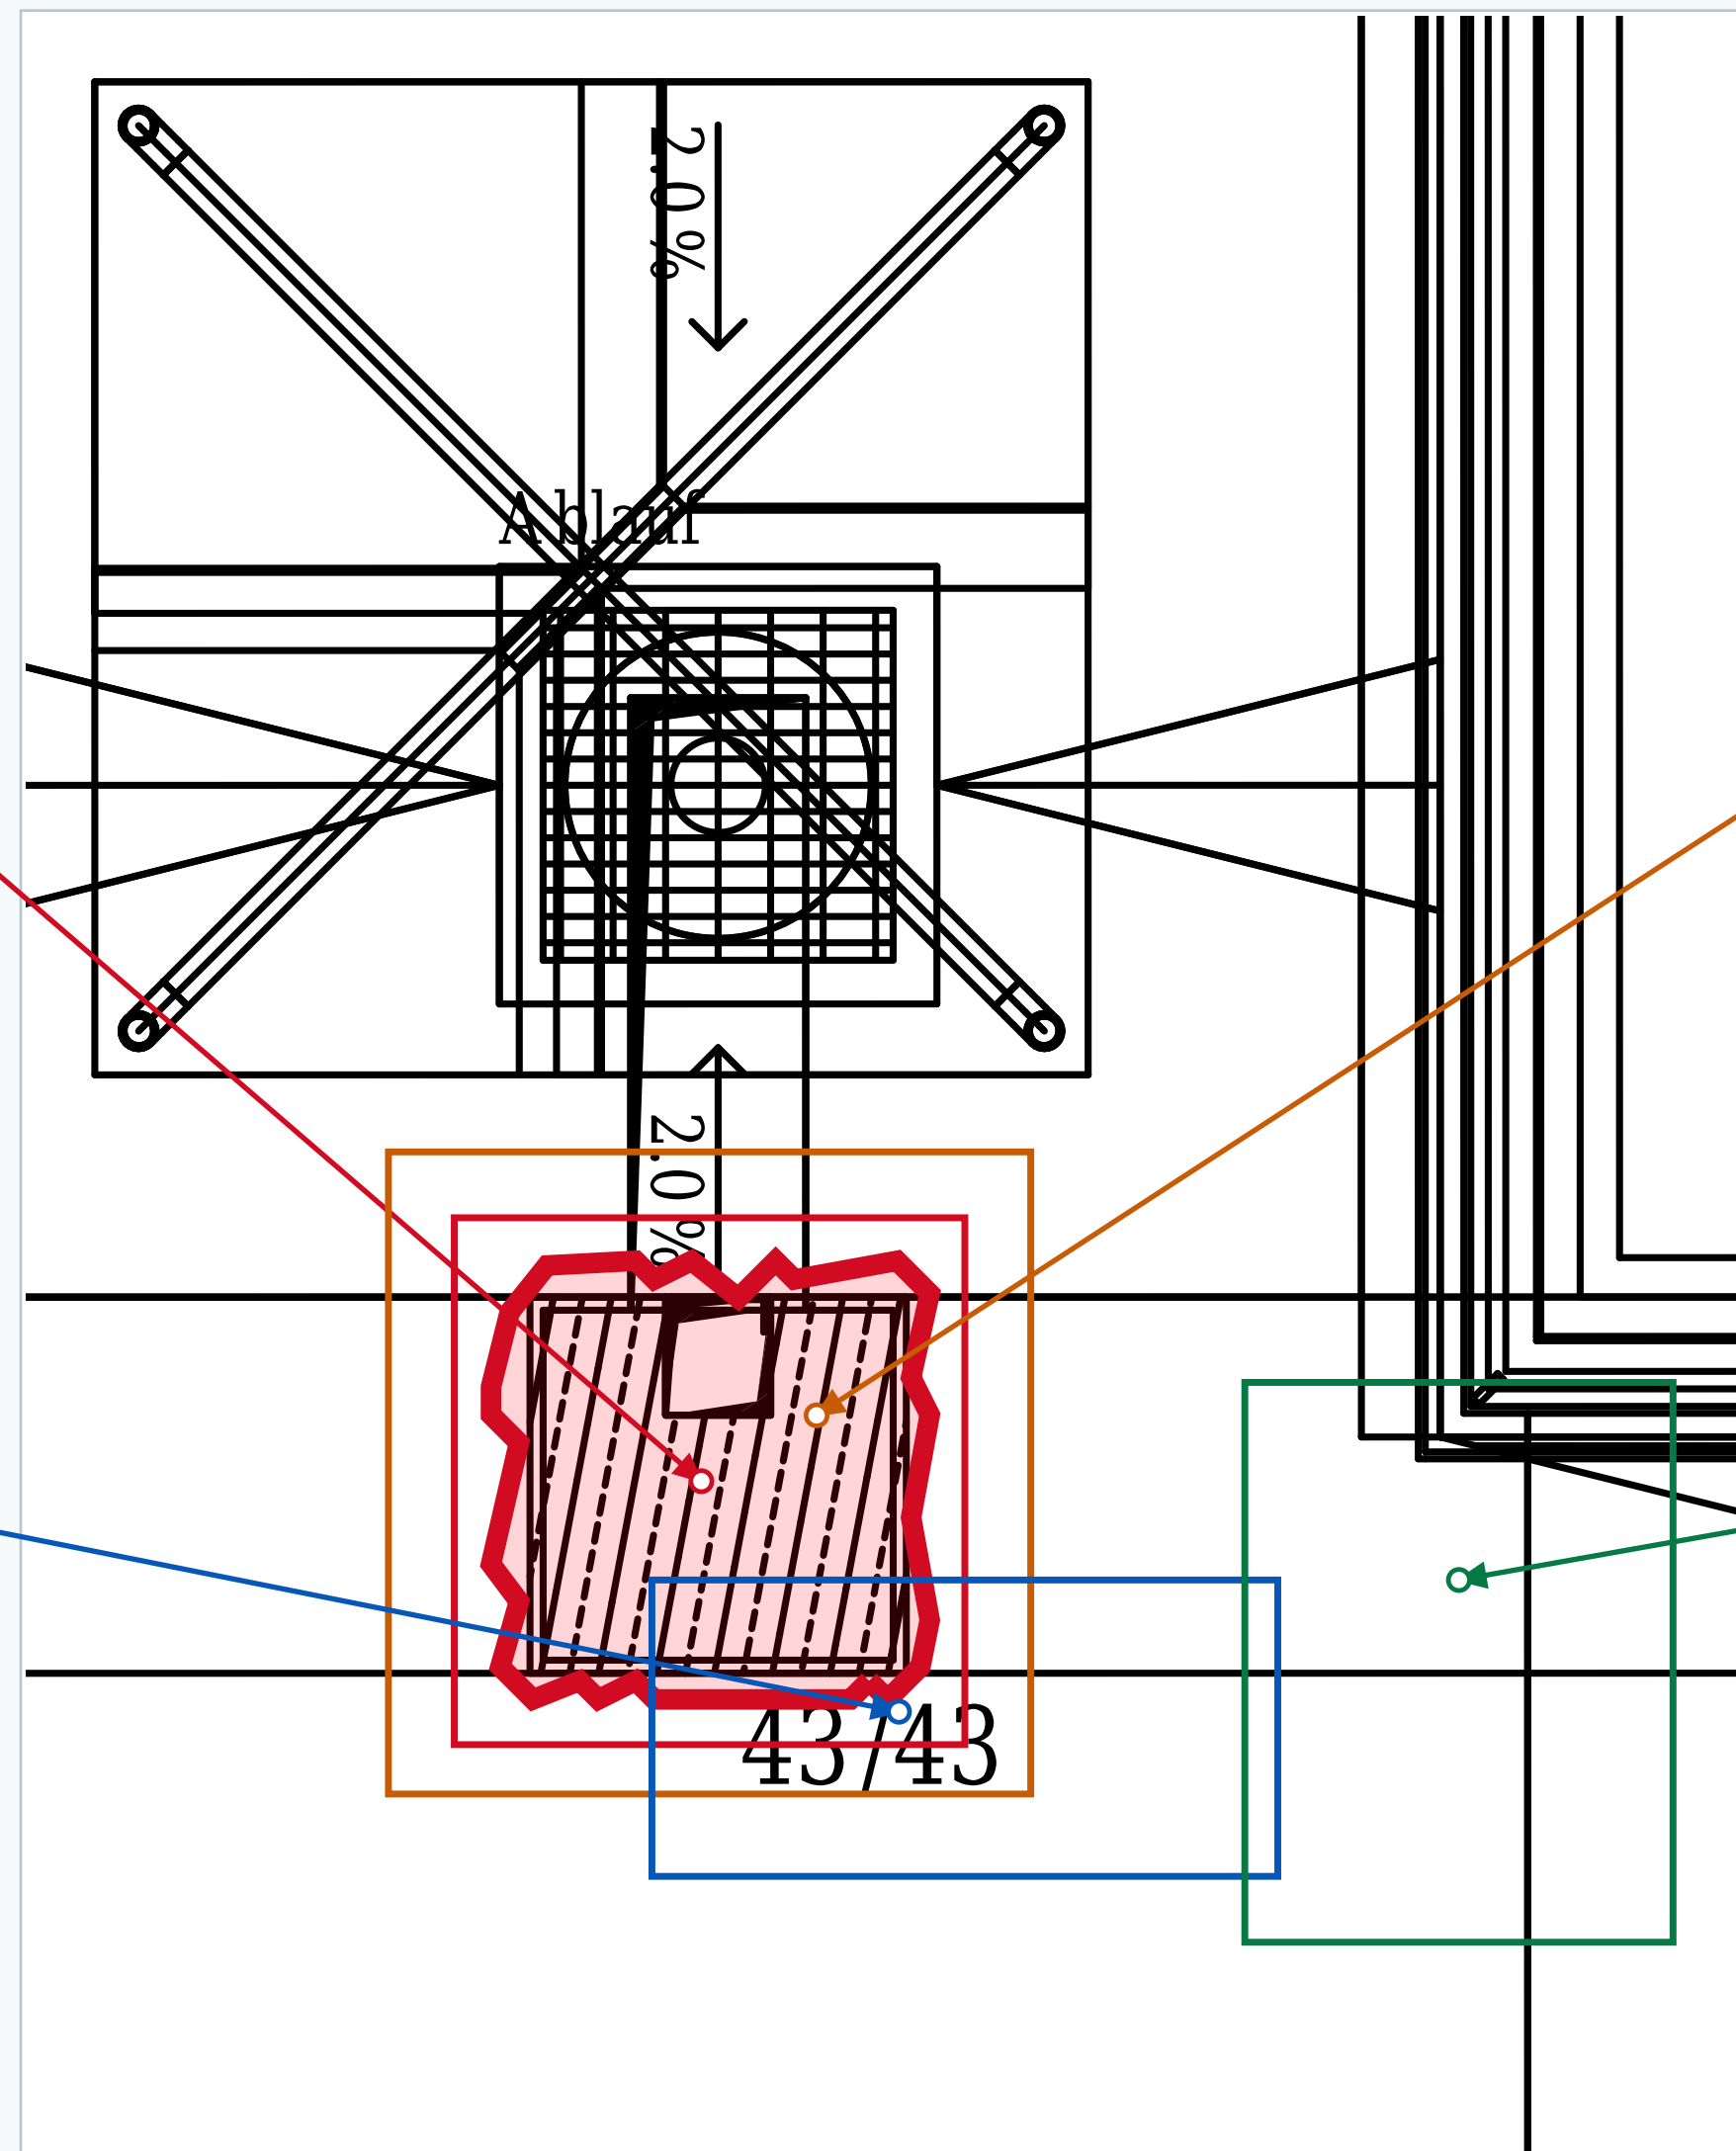

Geschlossener Rahmen + Pfeil: erklärter Bereich. Farblinien: hervorgehobene Merkmale.

W08 | Markierungen am Originalausschnitt

Absturzsicherung

Der Text benennt die Umwehrung ausdrücklich.

Raumhohe Grenze


Diese Kante wird nicht als massive Mauer umgedeutet.

Brüstung

Die nahe Beschriftung lautet Brüstung H=120cm.

Brückenbereich

Der schräge Bereich braucht einen belegten Niveauanschluss.

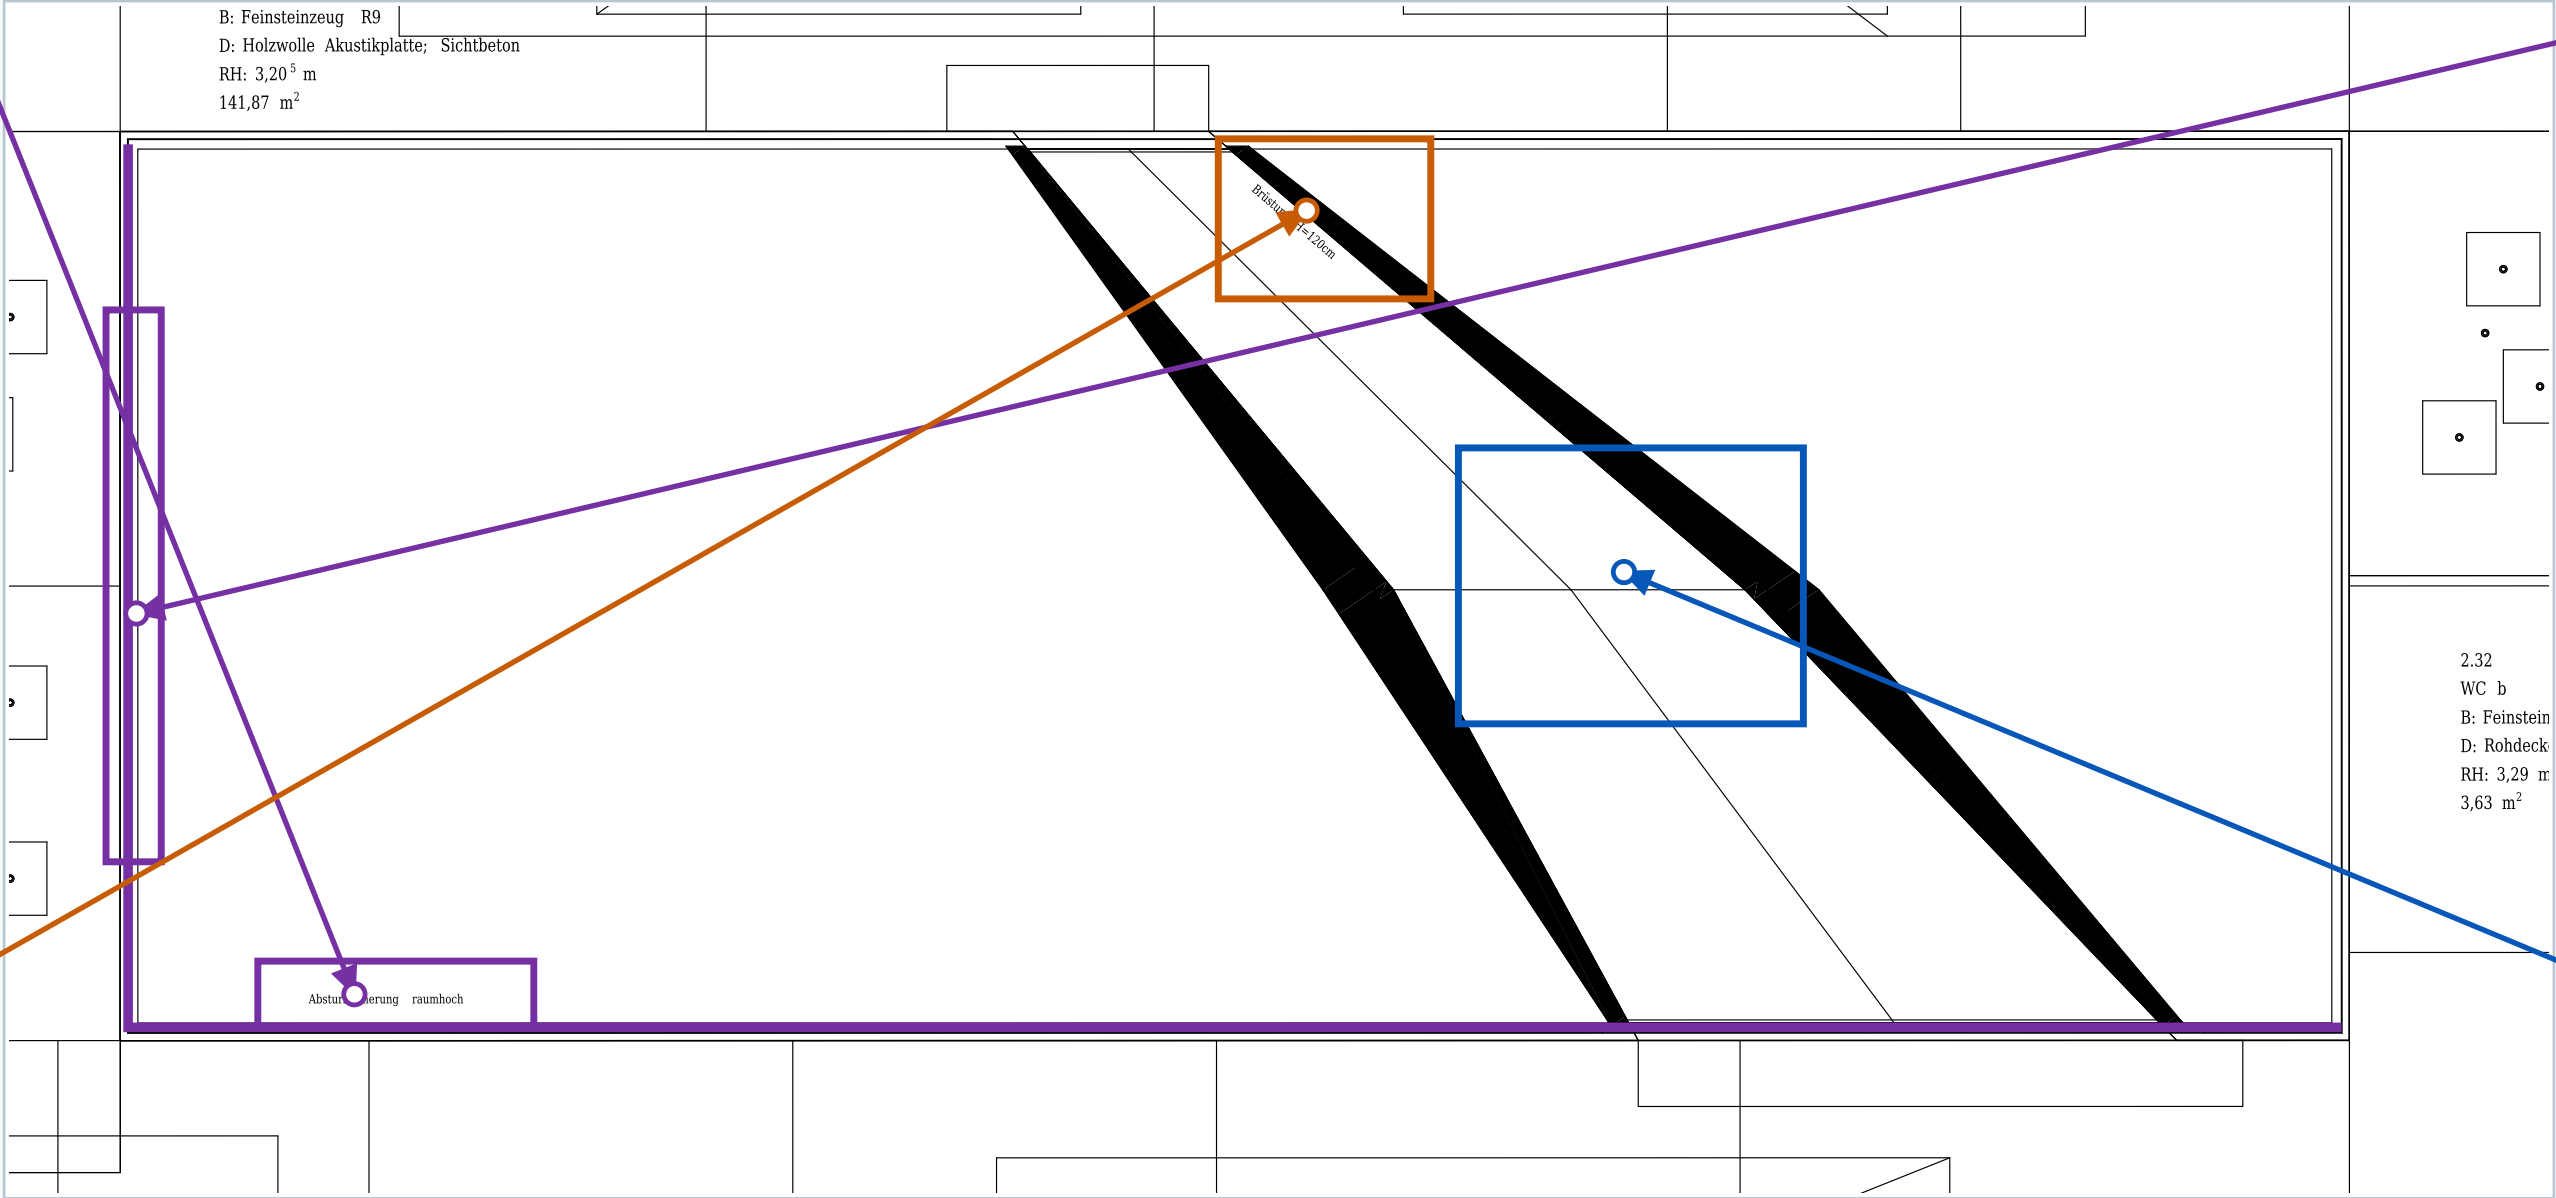

Geschlossener Rahmen + Pfeil: erklärter Bereich. Farblinien: hervorgehobene Merkmale.

D01 | Markierungen am Originalausschnitt

Wandlaibung

Der eingerahmte Wandabschluss begrenzt die Öffnung.

Schwenkbogen


Orange zeichnet den originalen Öffnungsbogen nach.

Türblatt

Blau liegt direkt auf der gezeichneten Blattlage.

Gedacht geschlossen

Violett gestrichelt: gedachte Schließlage, keine zusätzliche Mauer.

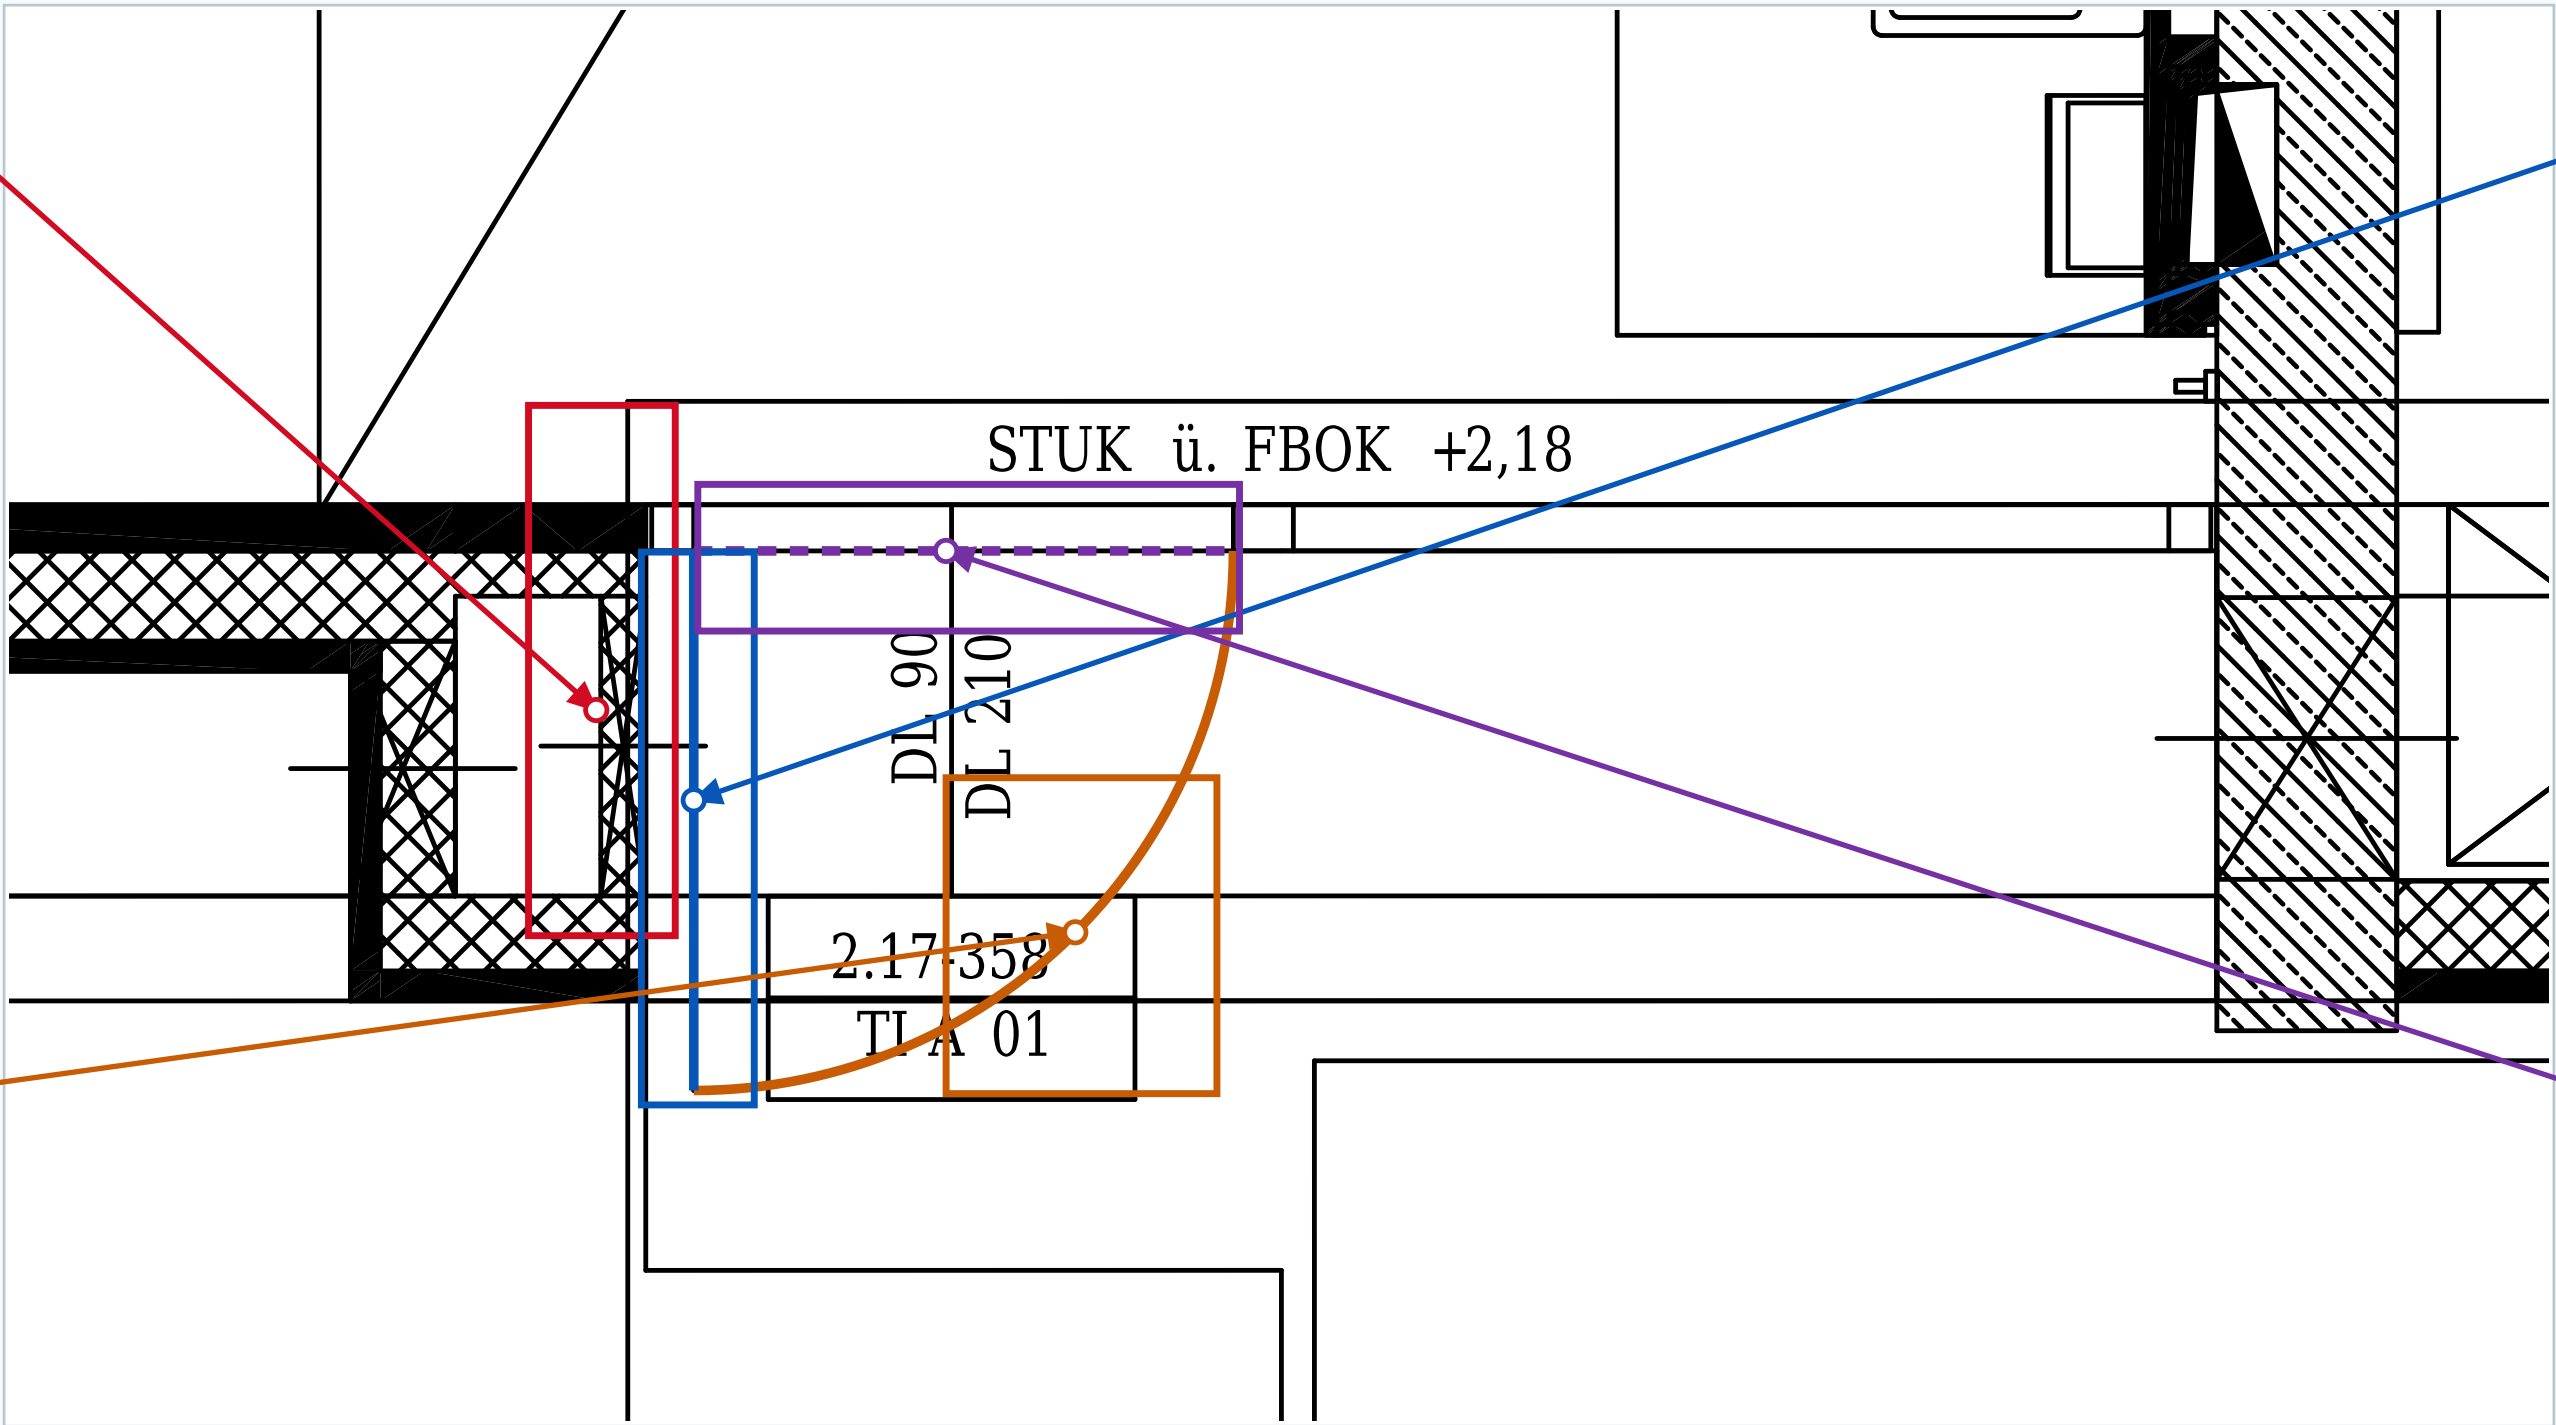

Geschlossener Rahmen + Pfeil: erklärter Bereich. Farblinien: hervorgehobene Merkmale.

D02 | Markierungen am Originalausschnitt

DL 90

Die erste
DL-Angabe benennt
die lichte Breite.

STUK +2,18


Unterkante des
Sturzes über der
Oberkante des
Fertigbodens.

DL 210

Die zweite
DL-Angabe benennt
die lichte Höhe.

Türkennung

2.17-358 / TI A 01
identifiziert das
Türelement.

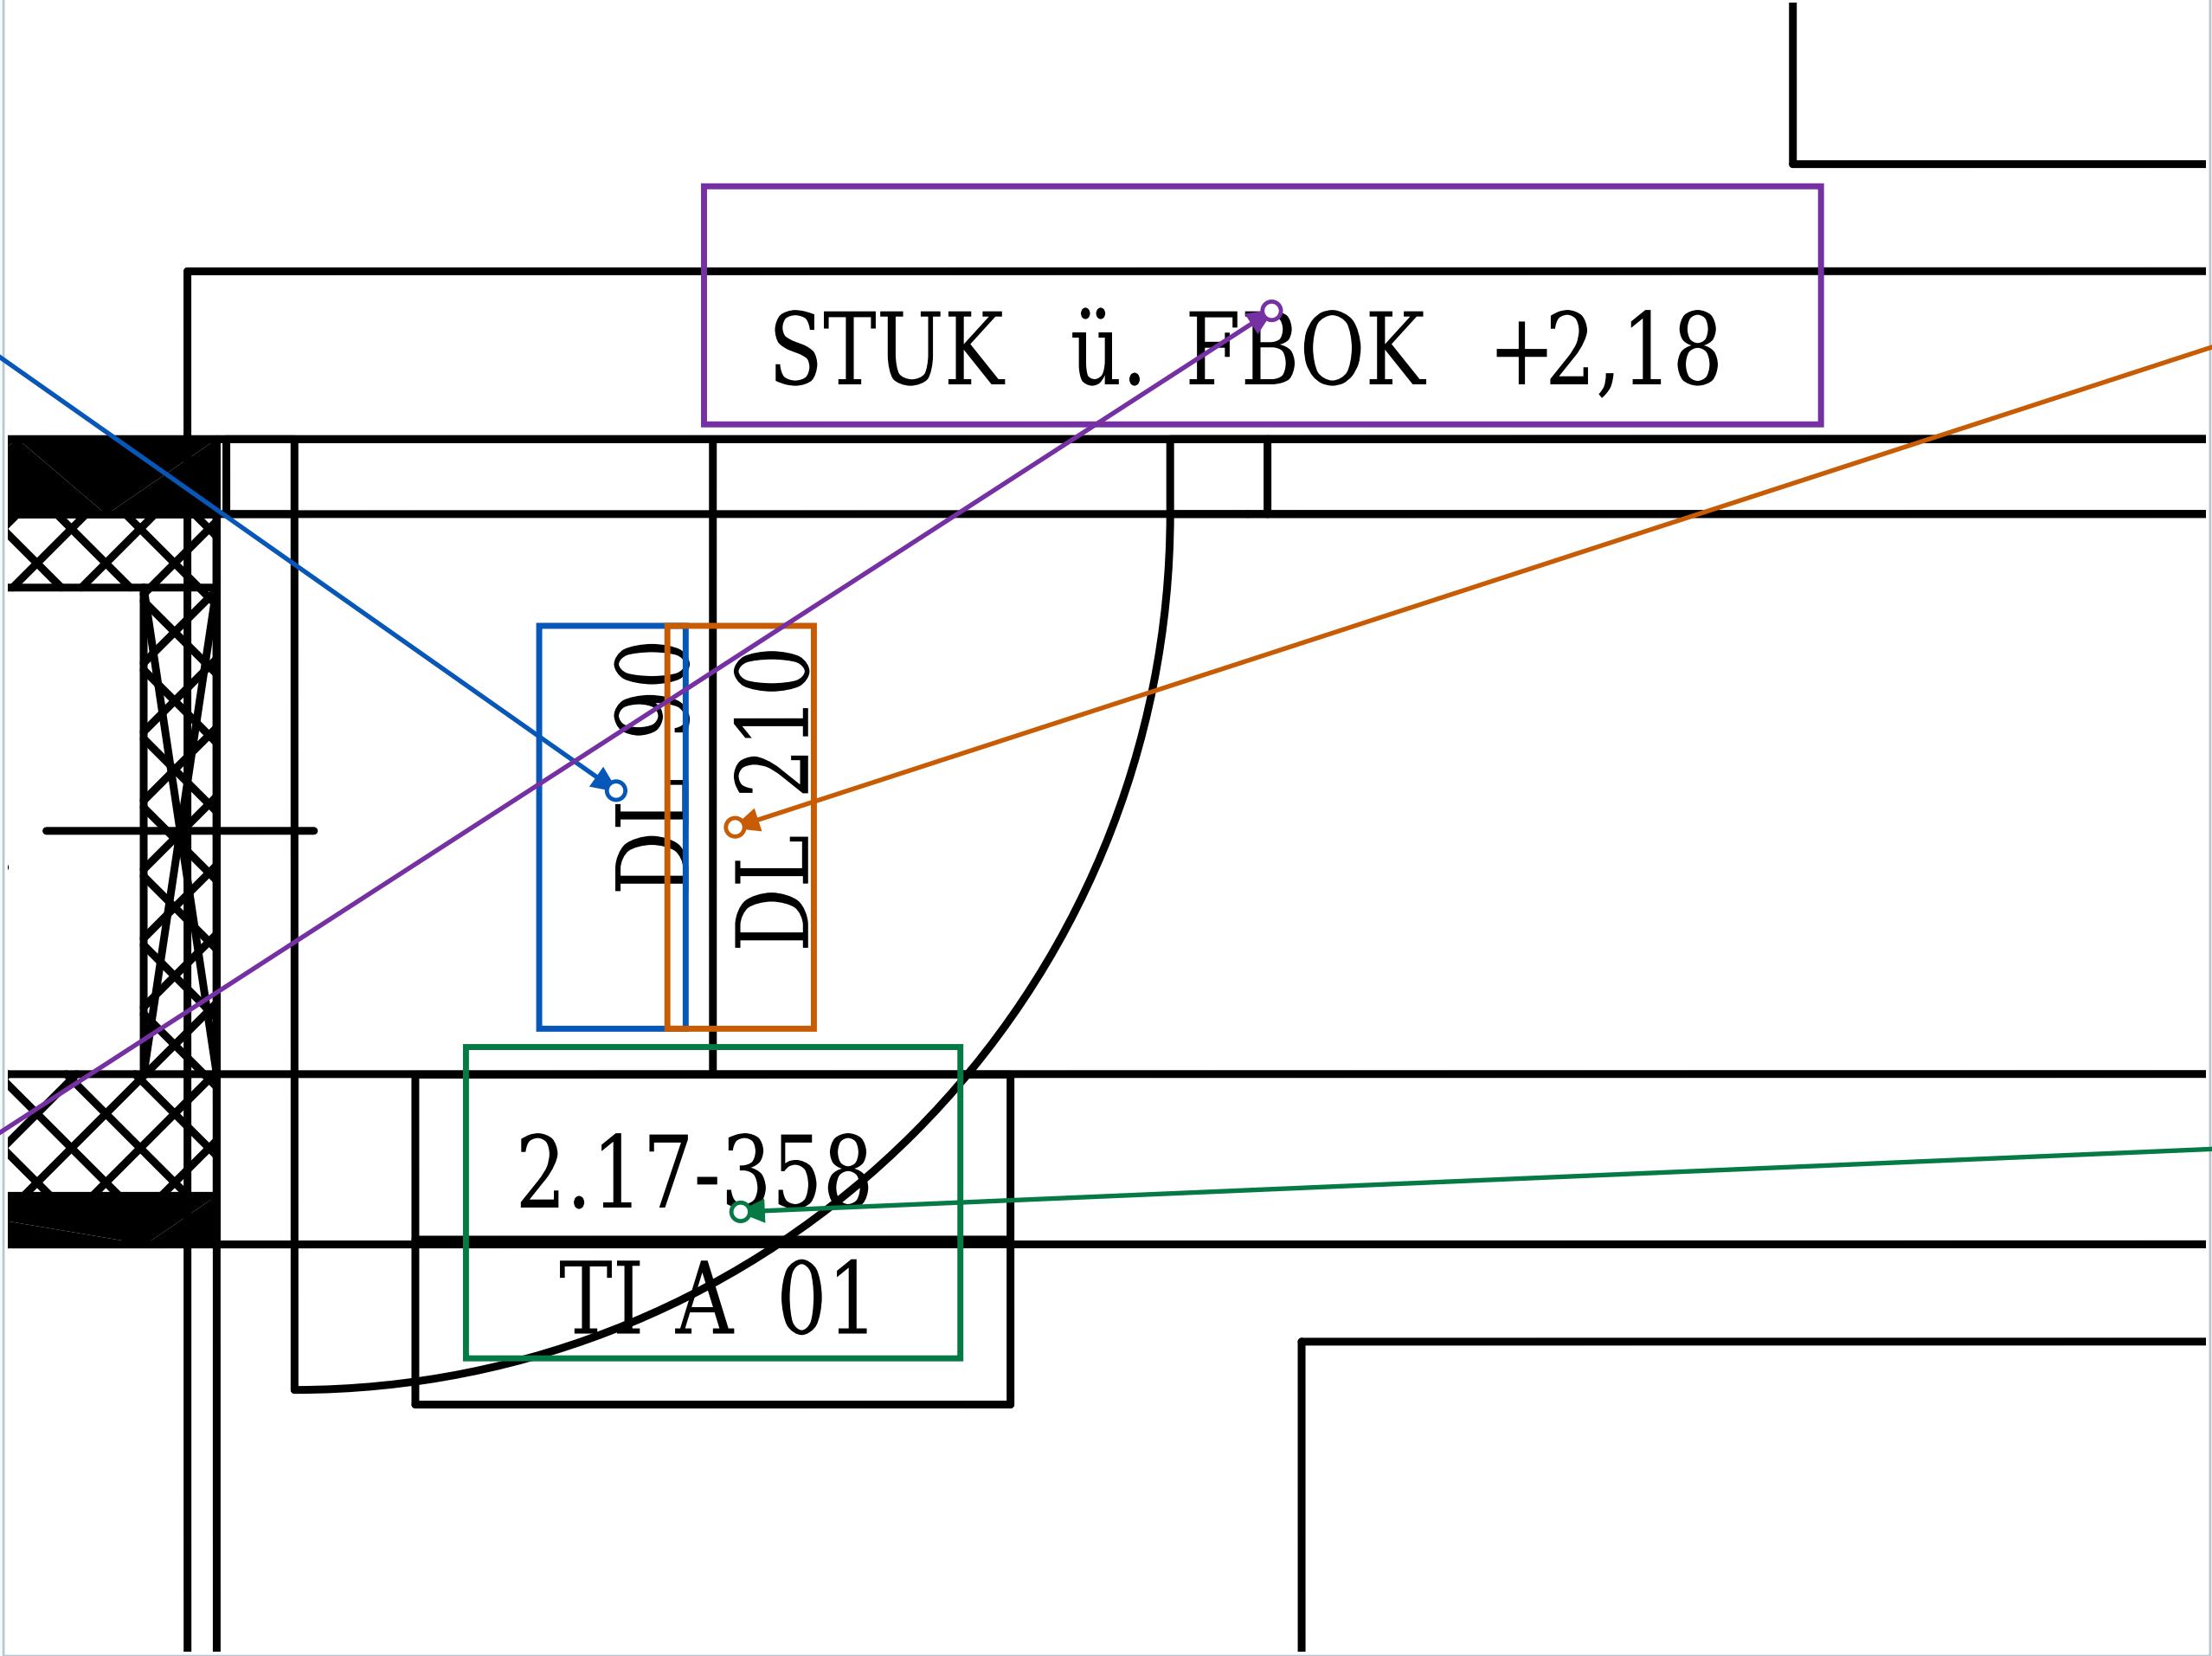

Geschlossener Rahmen + Pfeil: erklärter Bereich. Farblinien: hervorgehobene Merkmale.

D03 | Markierungen am Originalausschnitt

Zwei Anschläge

Je ein Flügel gehört zum oberen und unteren Anschlag.

Öffnungsstreifen


Die Passage liegt zwischen den Anschlägen in der Wandebene.

Zwei Bögen

Beide orange Kurven stammen aus der Originalzeichnung.

Feste Wand

Der feste Anschluss oberhalb der Tür bleibt vom Bogen getrennt.

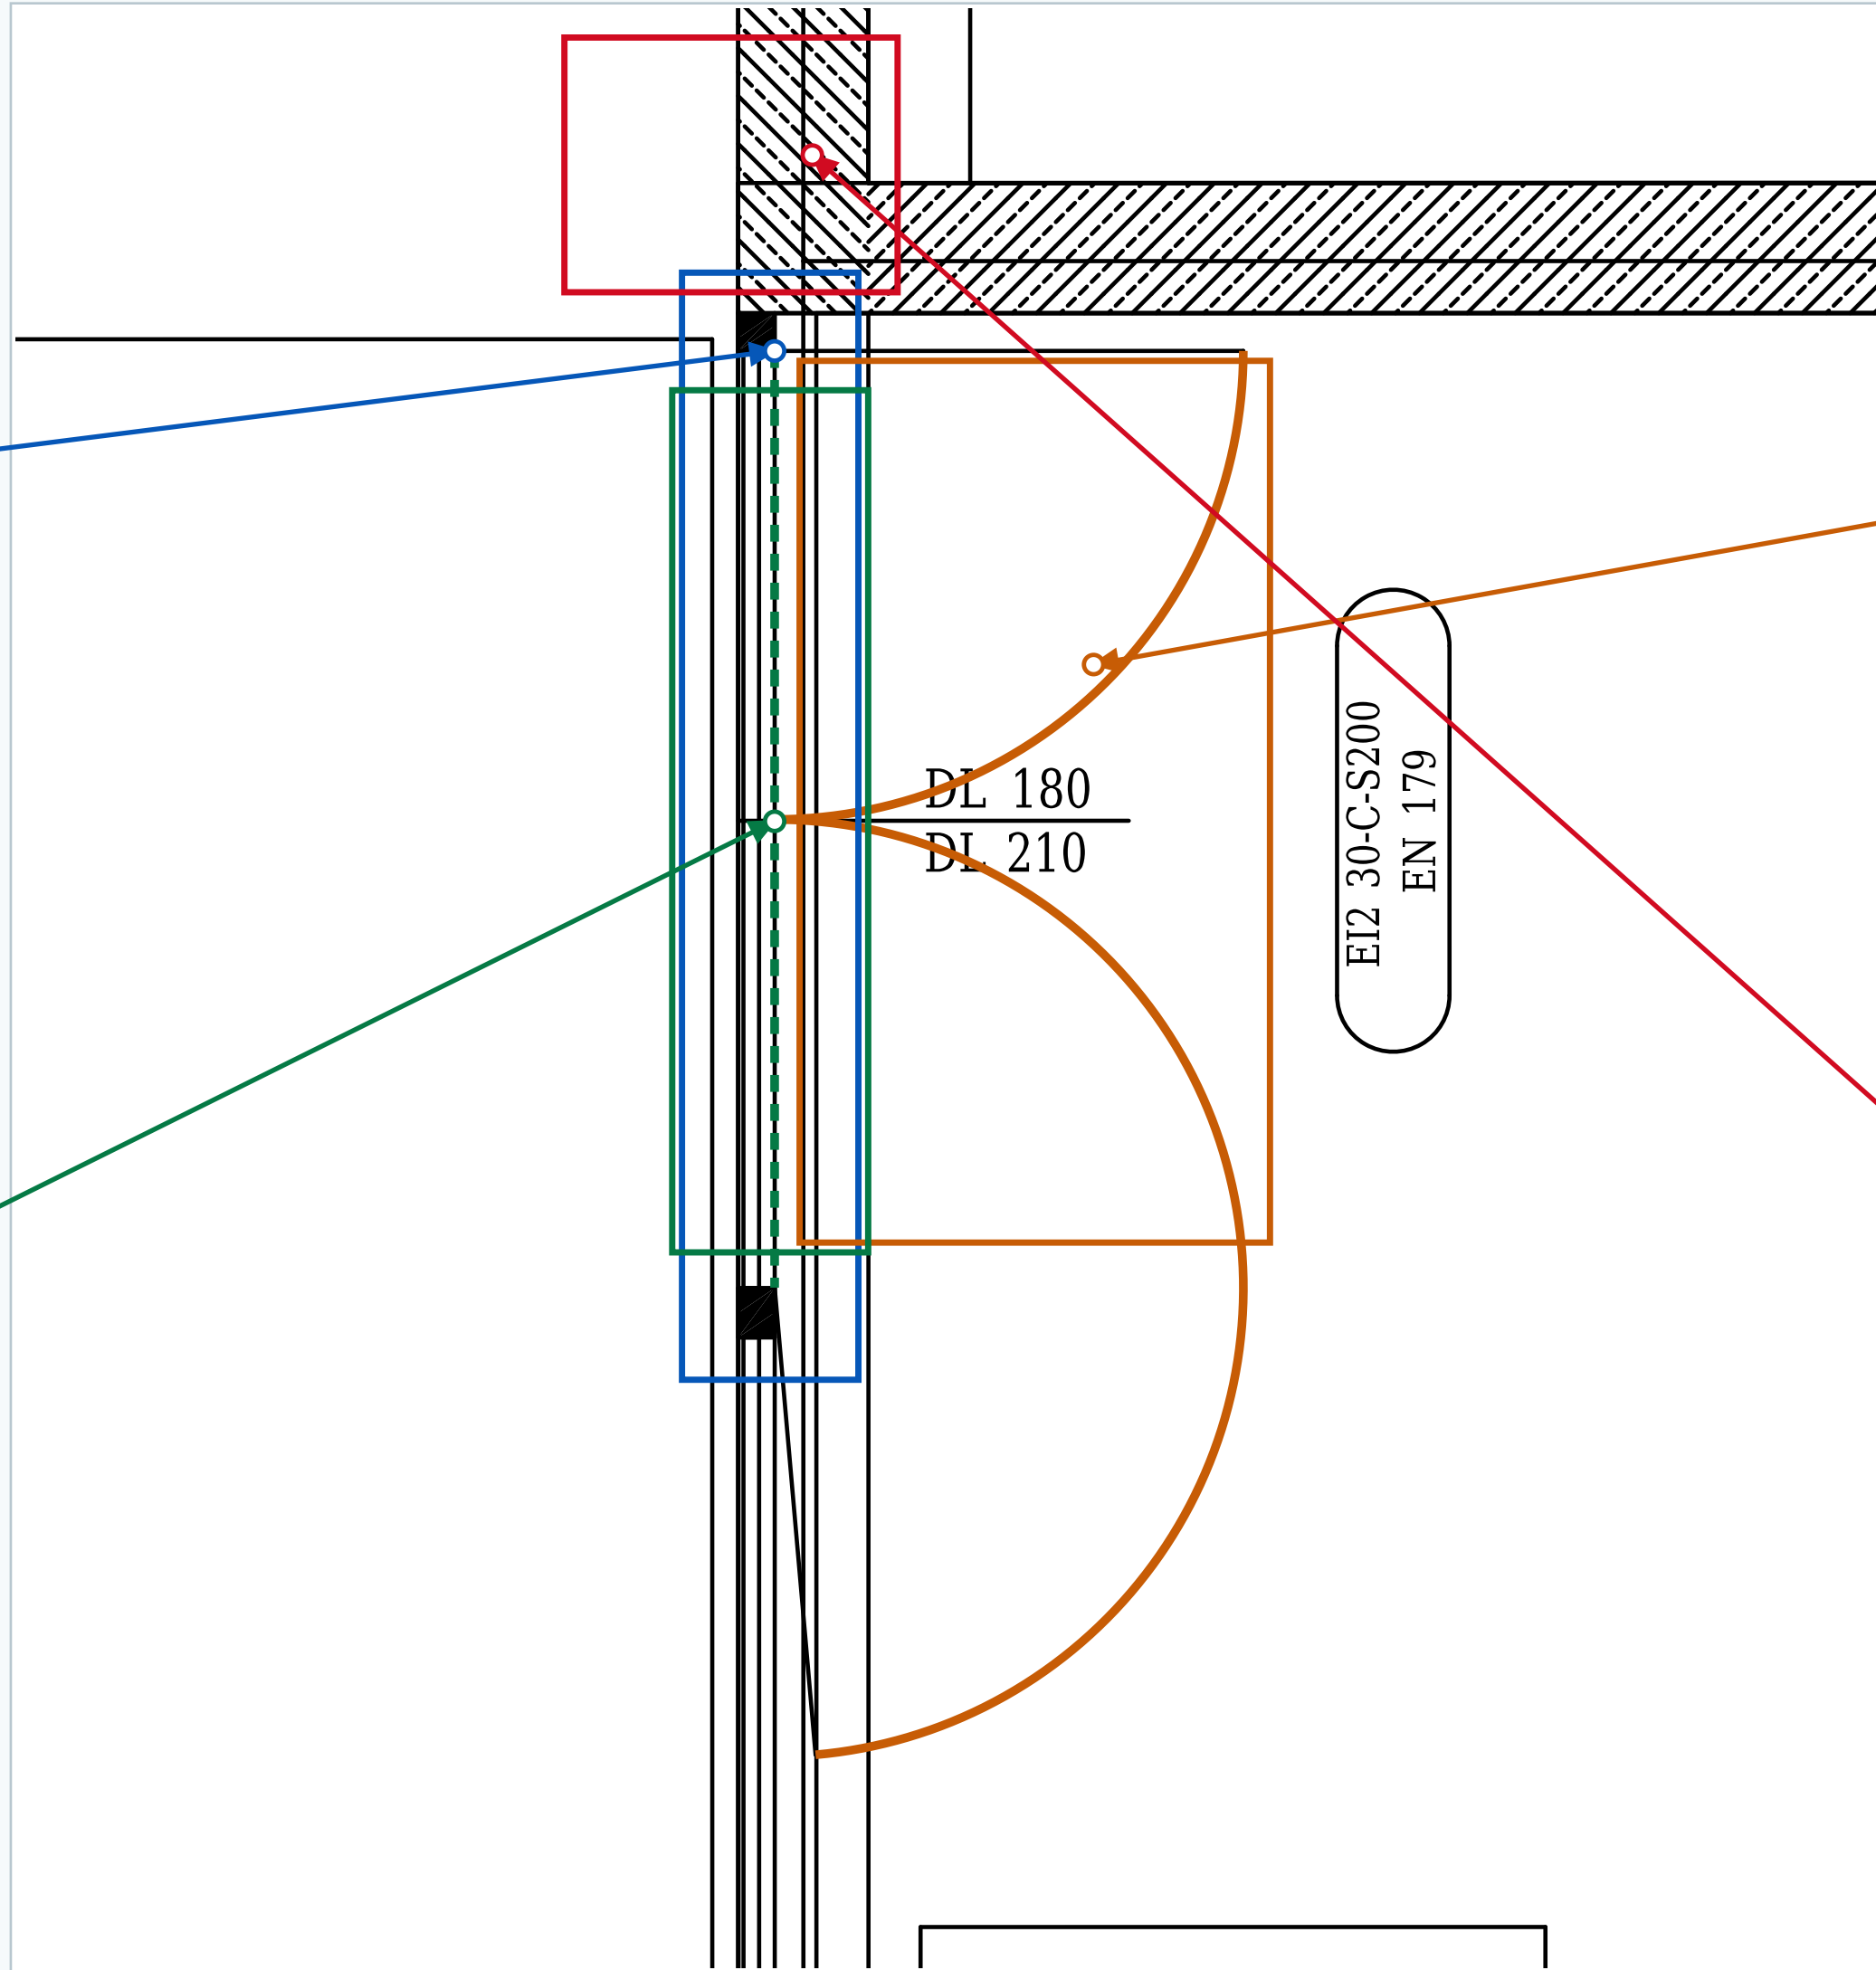

Geschlossener Rahmen + Pfeil: erklärter Bereich. Farblinien: hervorgehobene Merkmale.

D04 | Markierungen am Originalausschnitt

Fester Glasabschluss

Die durchgehende Rahmenzone bildet hier eine Grenze.

Rahmen / Pfosten


Senkrechte Teilungen gehören zum Fassadenelement.

Innenboden

Die Erschließung liegt auf der Innenseite.

Außenbereich

Die Freiklasse liegt jenseits des Abschlusses.

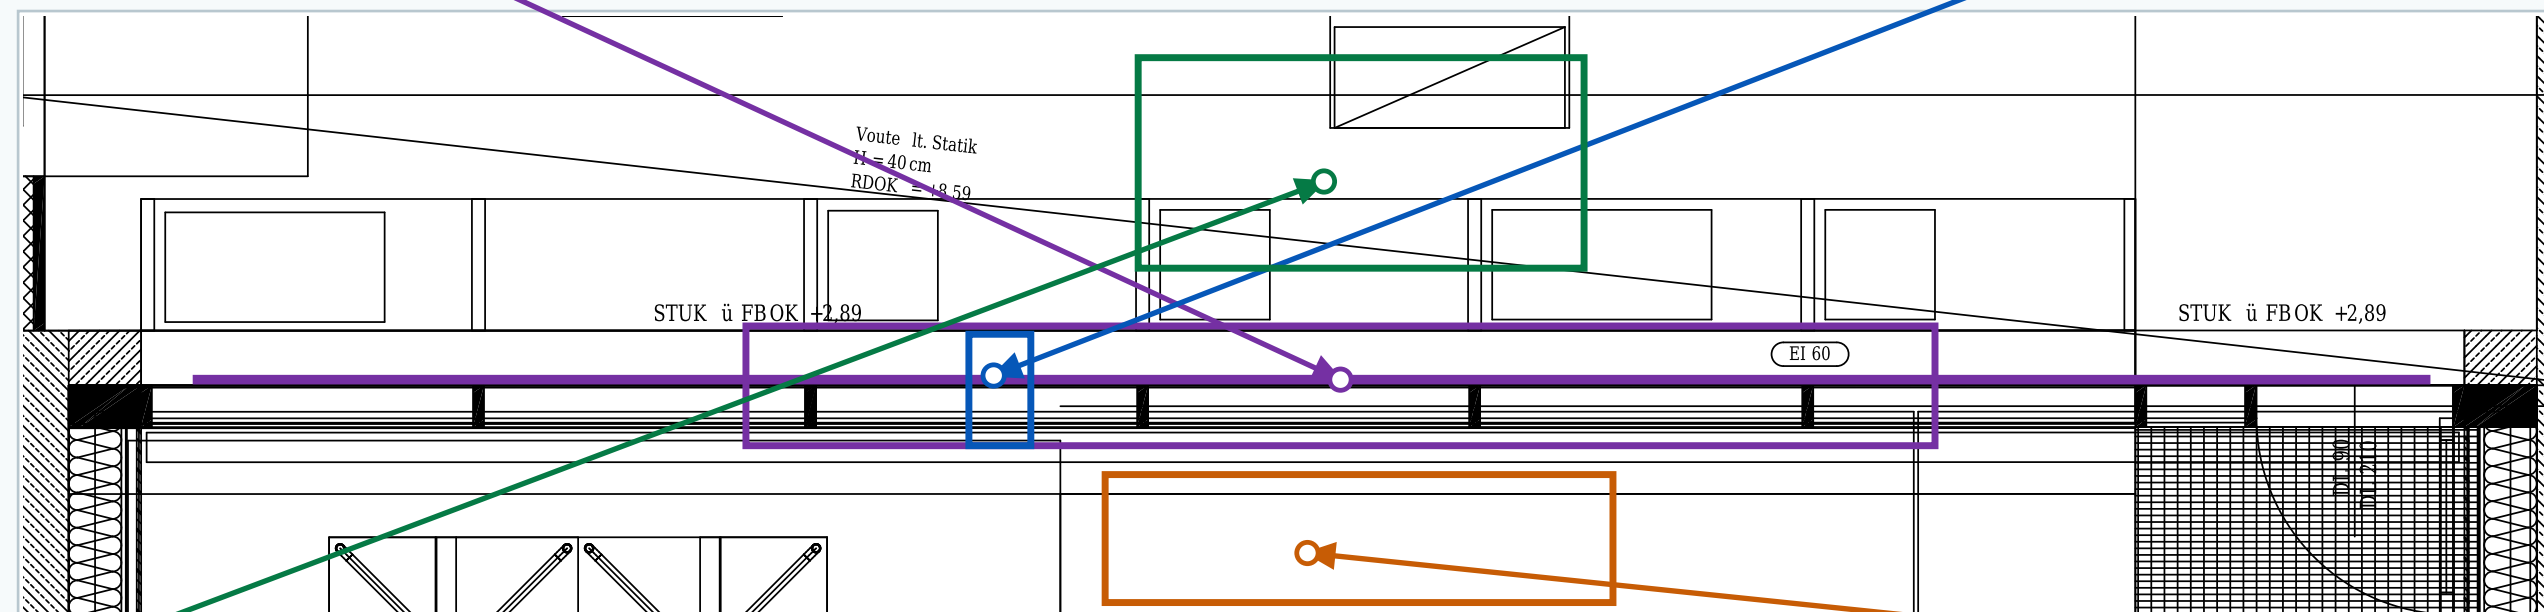

Geschlossener Rahmen + Pfeil: erklärter Bereich. Farblinien: hervorgehobene Merkmale.

F01 | Markierungen am Originalausschnitt

Rahmen und Glas

Mehrere dünne parallele Linien liegen in der Außenöffnung.

Fensterflügel


Der gezeichnete Flügel liegt am Rahmenanschlag.

Öffnungsbogen

Auch ein Fenster kann einen Viertelkreisbogen haben.

Parapethöhe

FPH ü. FBOK 0,85 bezeichnet die Fensterbrüstungshöhe.

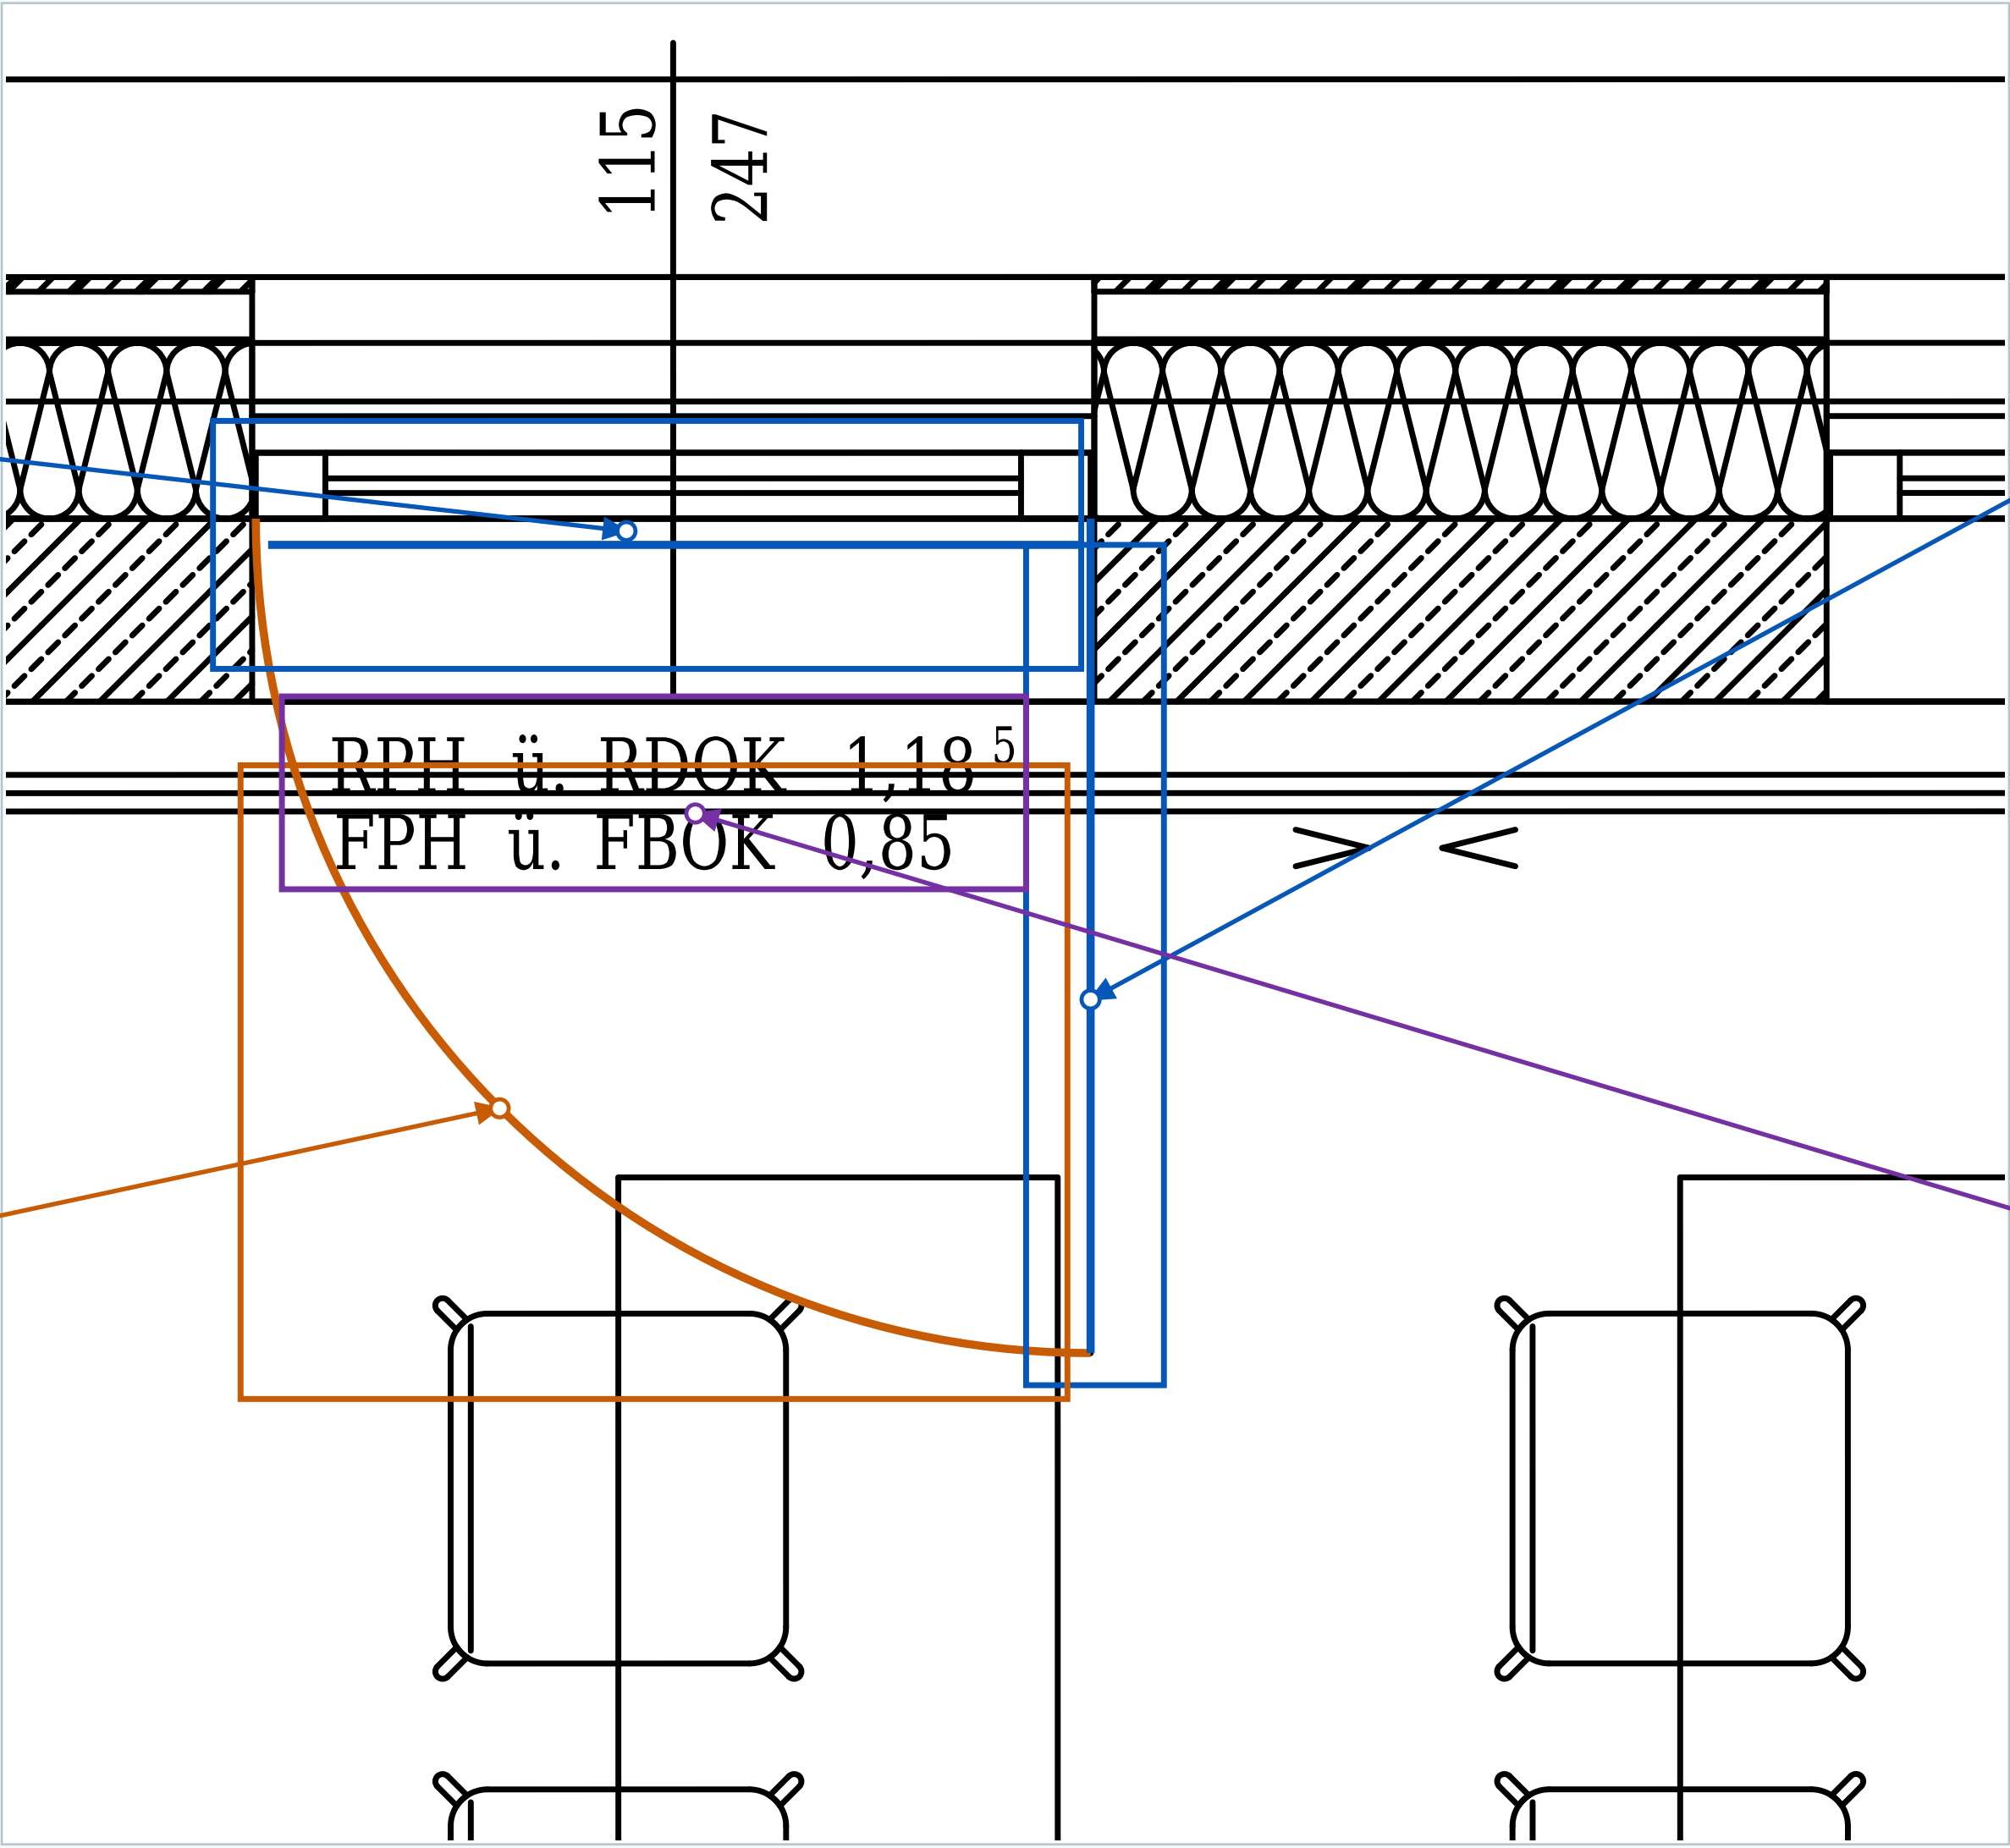

Geschlossener Rahmen + Pfeil: erklärter Bereich. Farblinien: hervorgehobene Merkmale.

F02 | Markierungen am Originalausschnitt

RPH

Rohparapethöhe wird auf RDOK bezogen.

FPH 0,85


Fertigparapethöhe wird auf FBOK bezogen.

Glaslinien

Die eng benachbarten Linien markieren das Fassadenfeld.

Wandstück

Materialzeichnung zwischen den Öffnungen bleibt ein fester Körper.

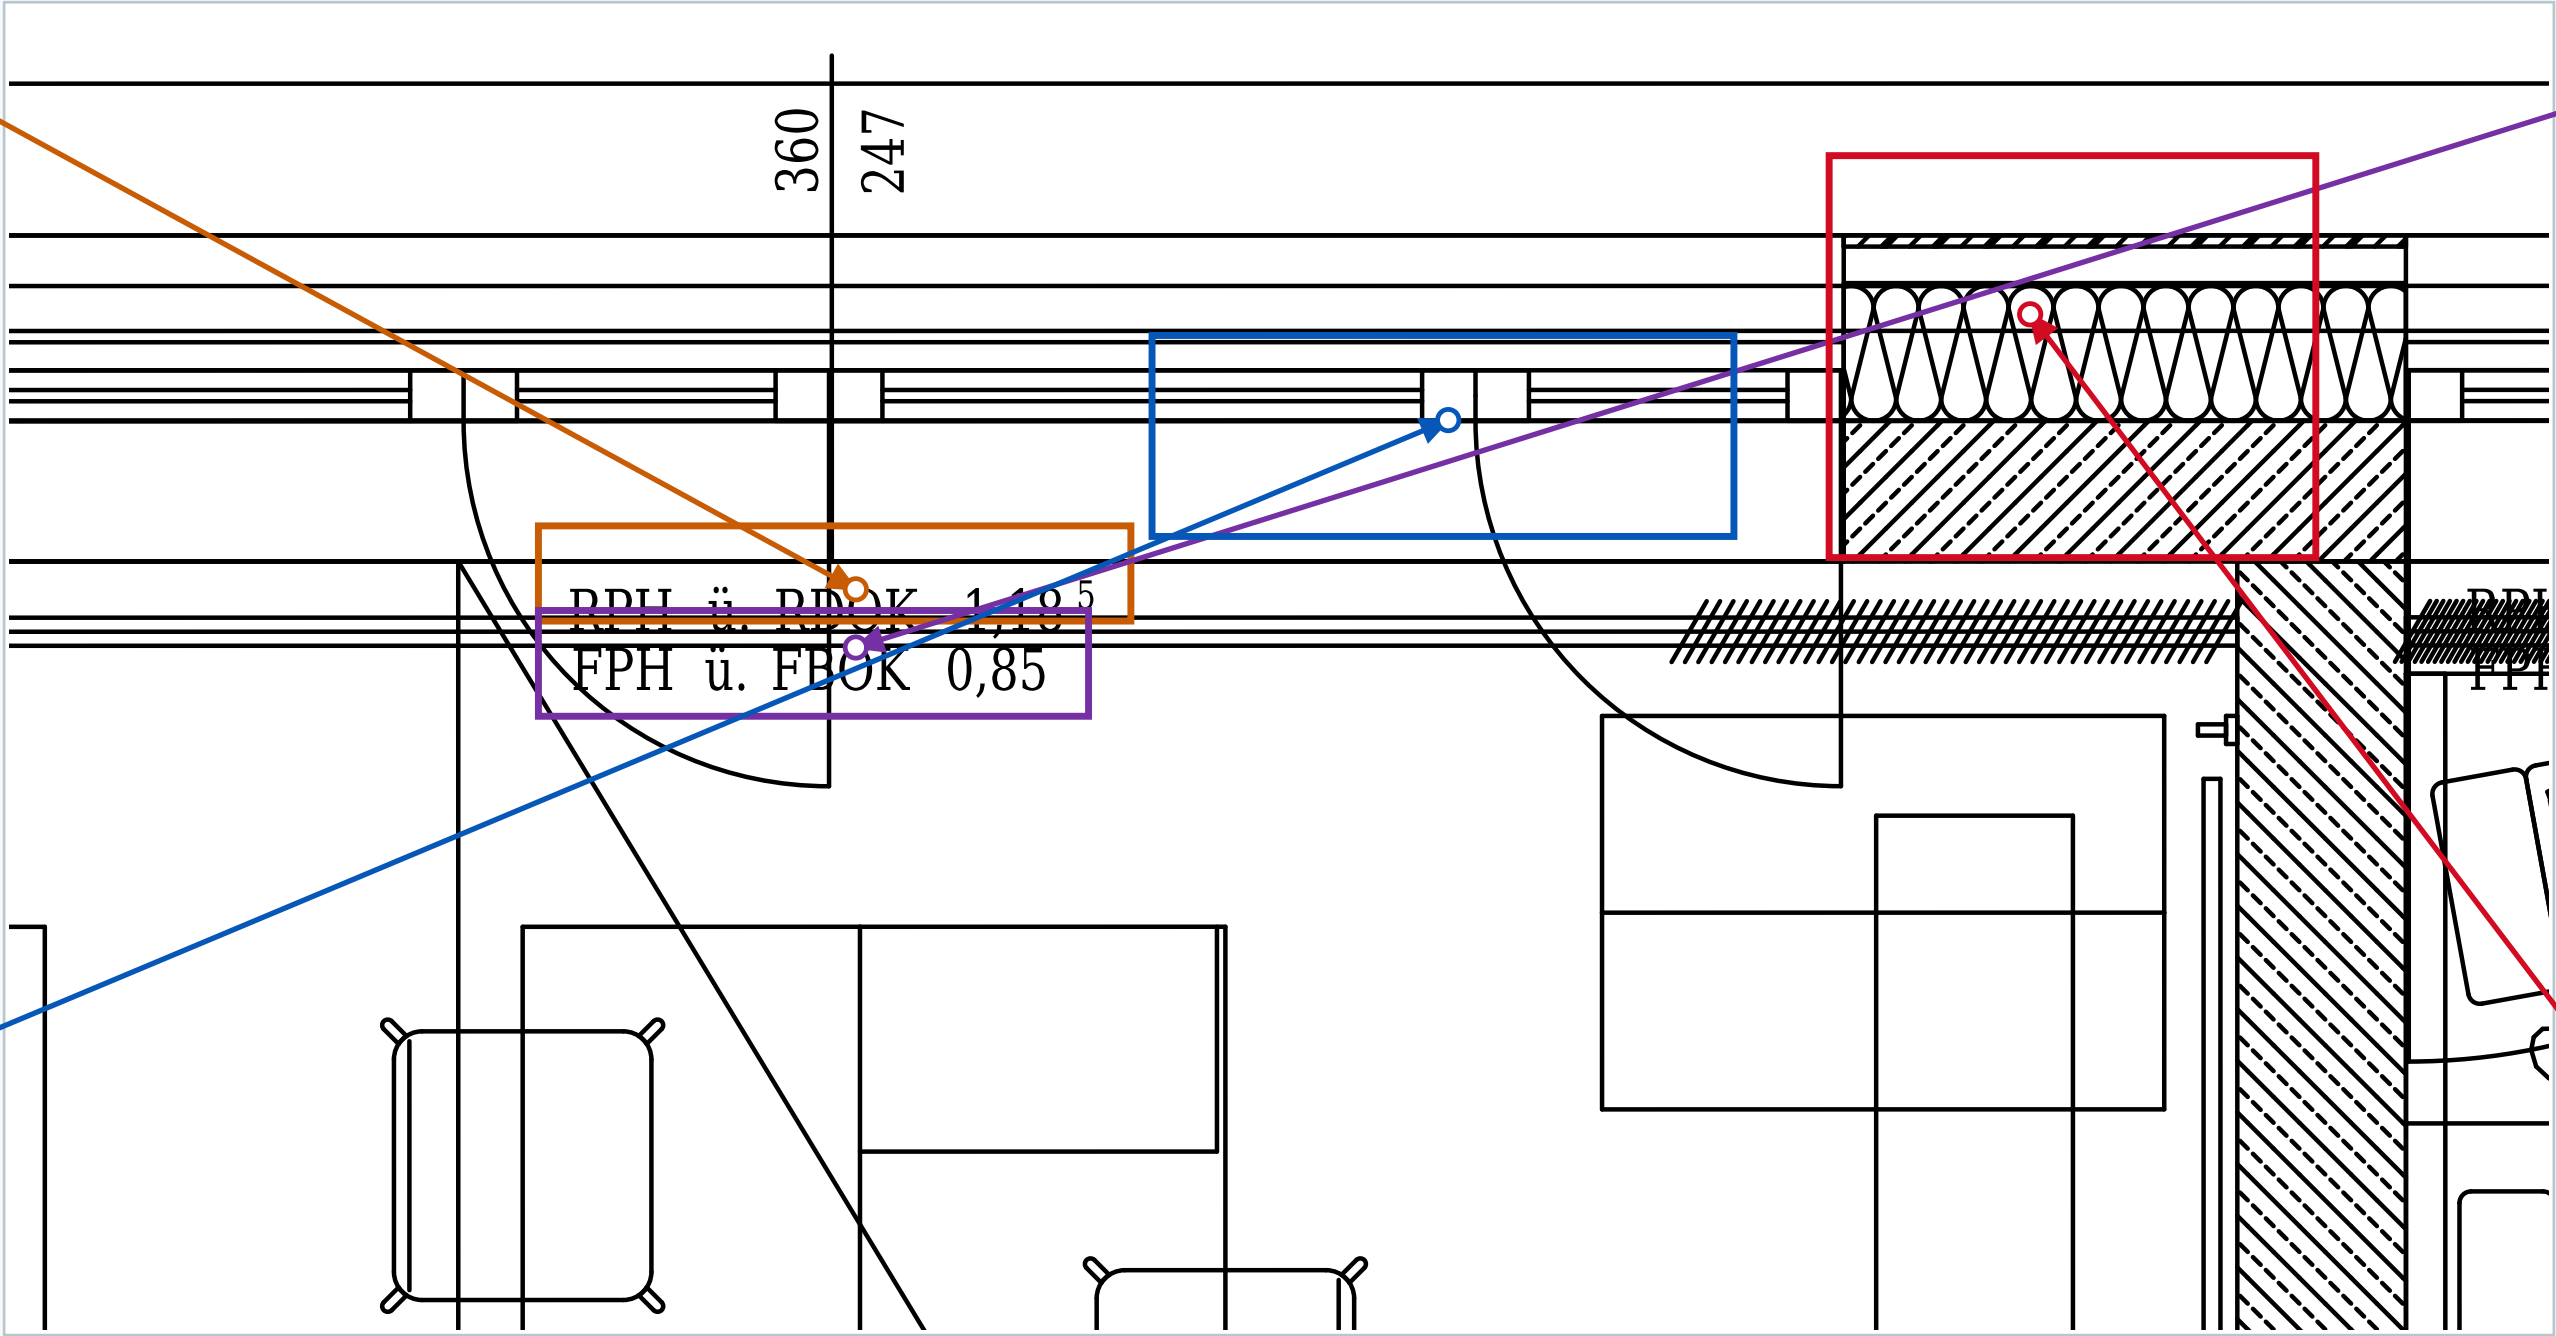

Geschlossener Rahmen + Pfeil: erklärter Bereich. Farblinien: hervorgehobene Merkmale.

F03 | Markierungen am Originalausschnitt

Wartungsflügel

Die Beschriftung nennt die Funktion ausdrücklich.

Rahmenzone


Der Flügel sitzt in der Fassadenöffnung.

Kleiner Bogen

Der kurze Originalbogen zeigt eine begrenzte Flügelstellung.

Begrenzung

Ein Wartungsflügel ist kein normaler Türdurchgang.

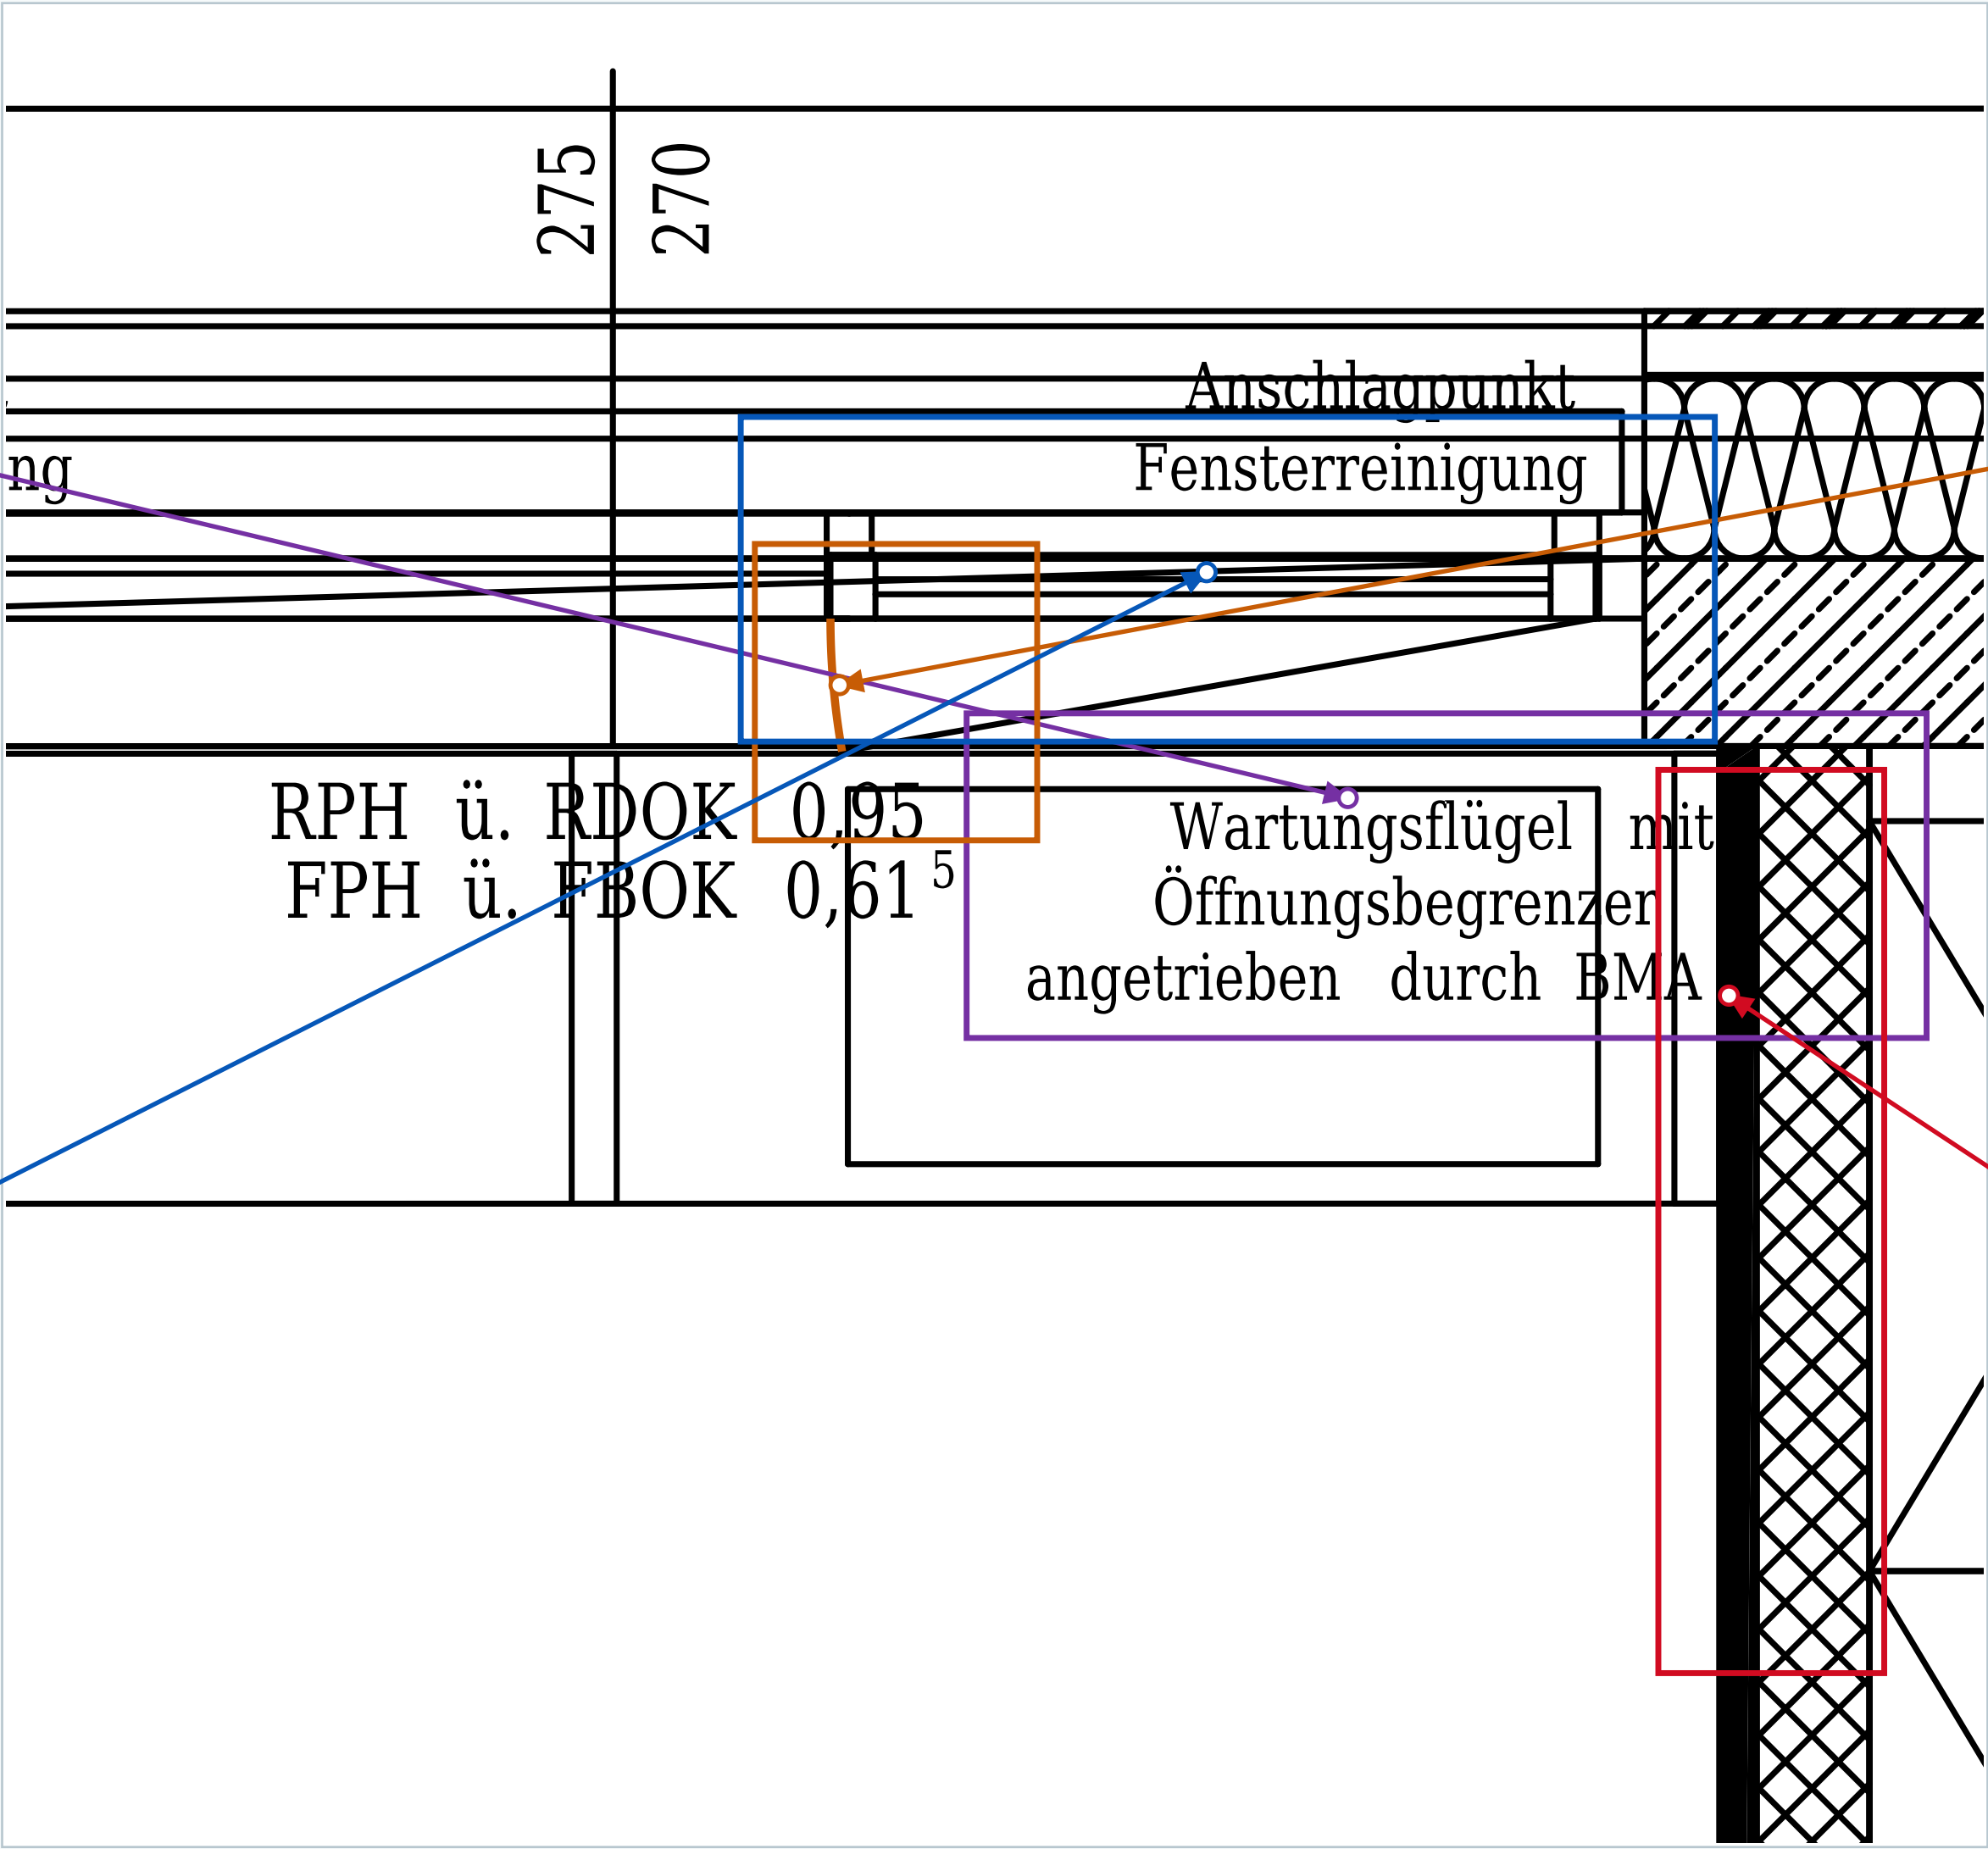

Geschlossener Rahmen + Pfeil: erklärter Bereich. Farblinien: hervorgehobene Merkmale.

G01 | Markierungen am Originalausschnitt

Flurfläche

Die grüne Füllung folgt dem Boden seitlich am Kern vorbei.

Türverbindung


An einer nachgewiesenen Tür kann der Weg in den Raum wechseln.

Wandgrenze

Die eingerahmte Querwand wird nicht grün überbrückt.

Zweite Flurseite

Ein weiterer Bodenstreifen erschließt die andere Kernseite.

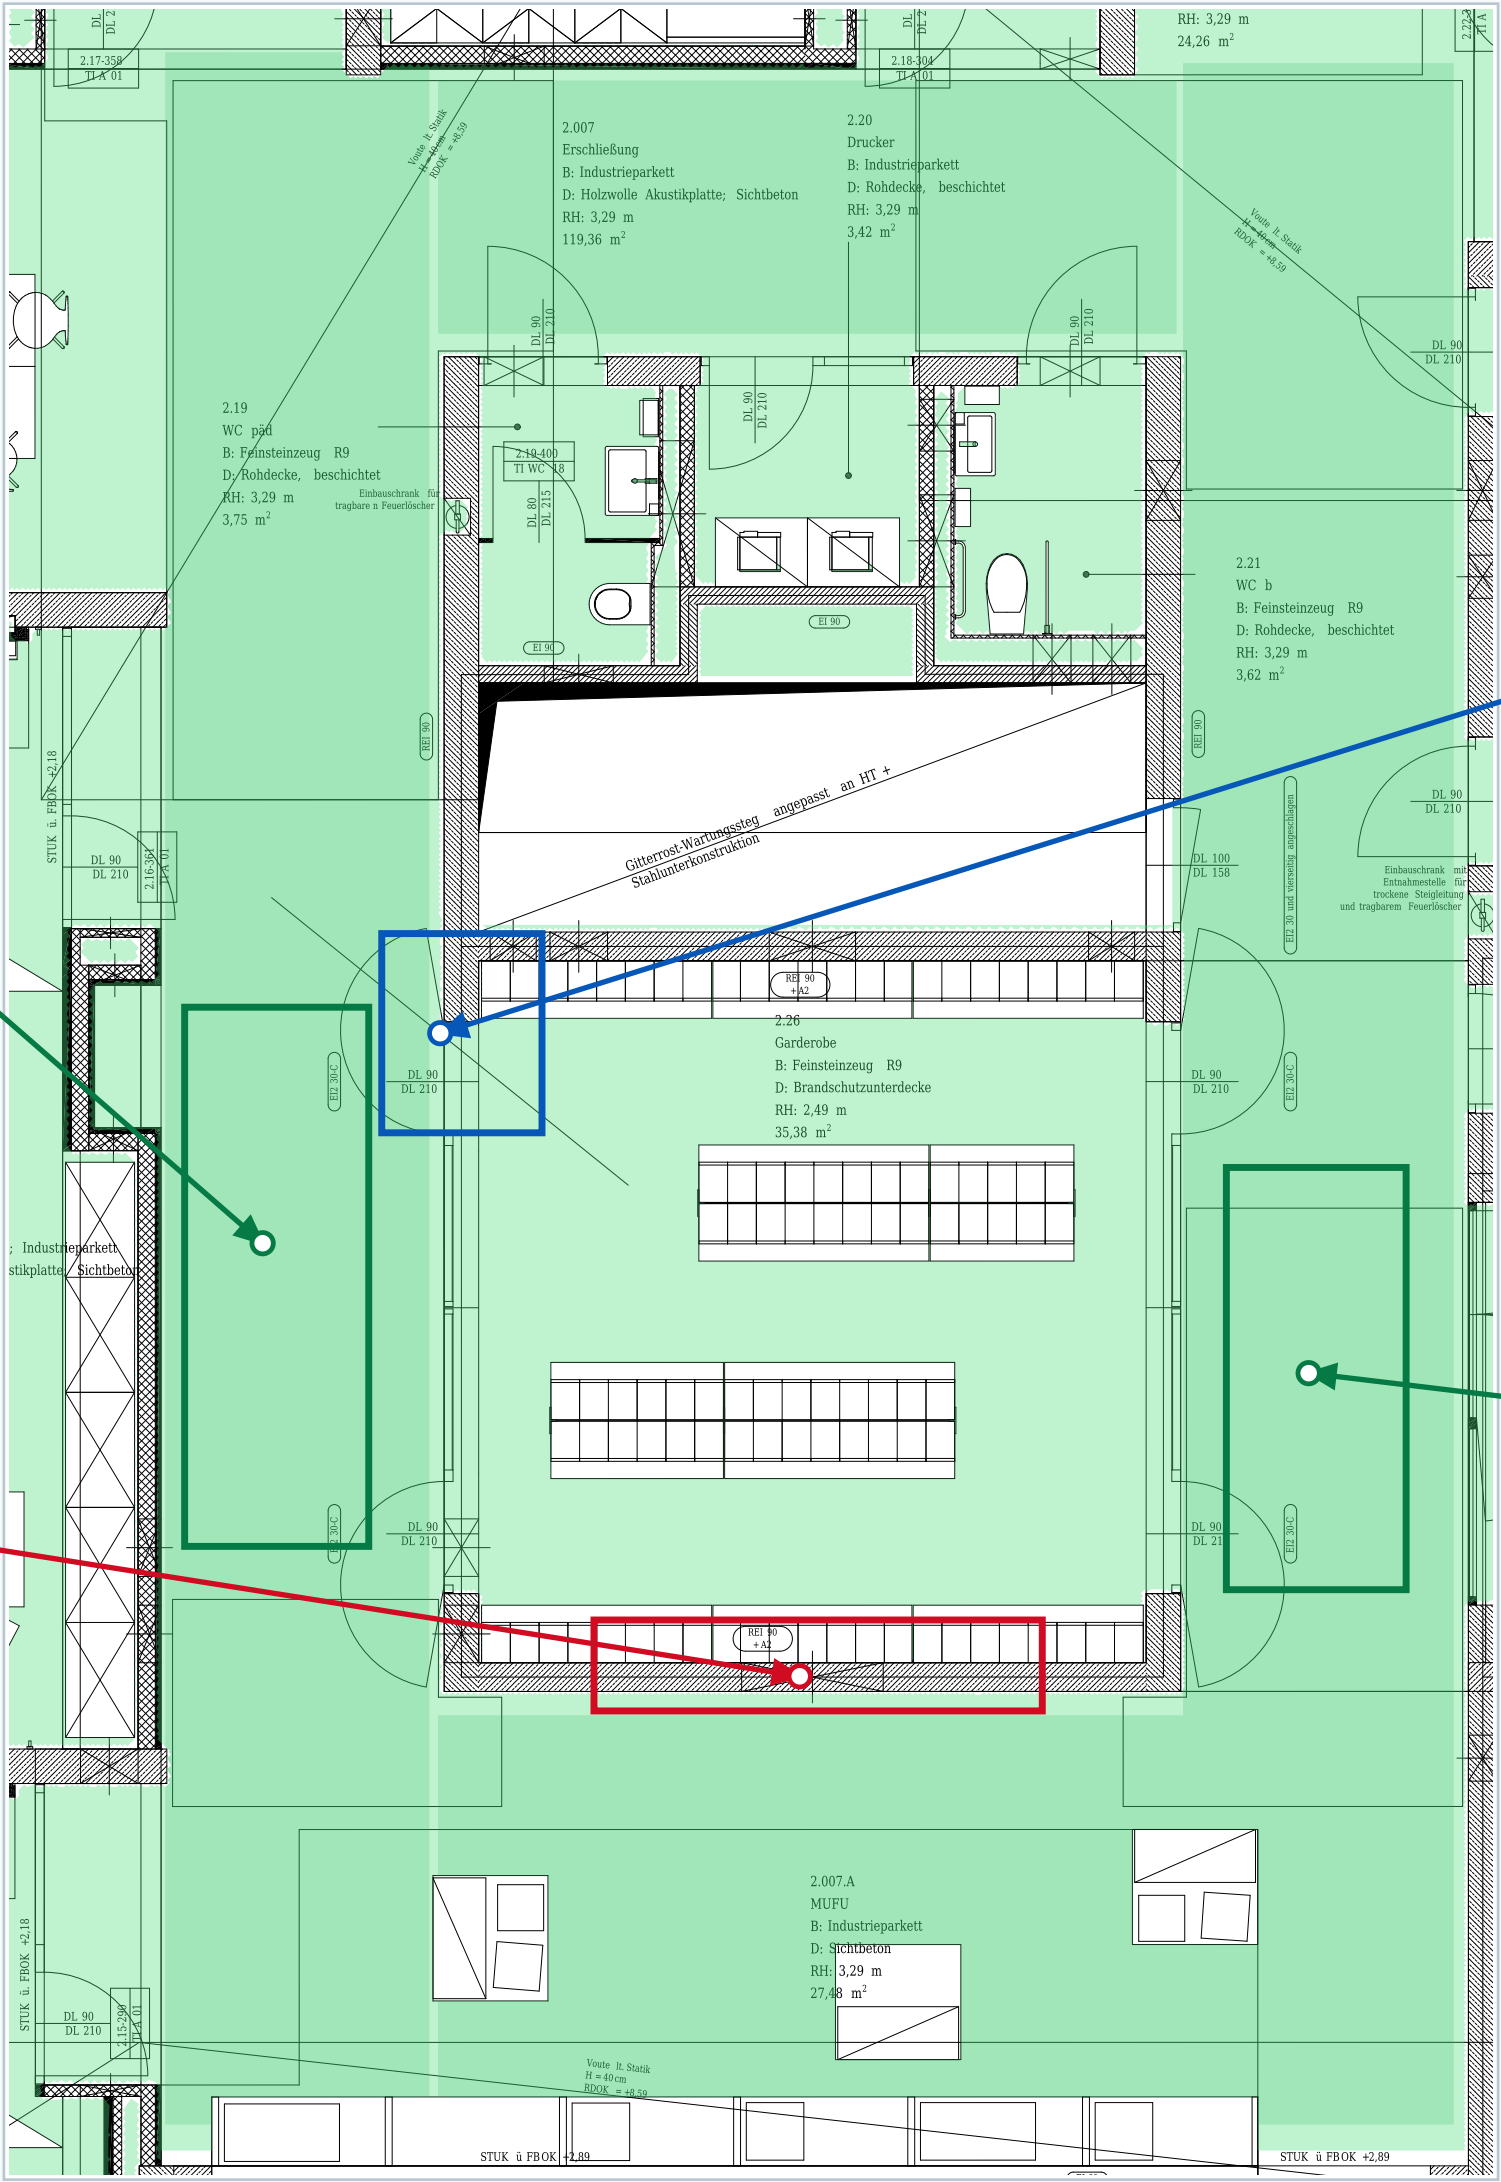

Geschlossener Rahmen + Pfeil: erklärter Bereich. Farblinien: hervorgehobene Merkmale.

G02 | Markierungen am Originalausschnitt

Oberer Umgang

Der Bodenstreifen verbindet die Seiten der Erschließung.

Unterer Umgang


Auch der untere Streifen wird flächig dargestellt.

Feste Grenze

Die Absturzsicherung unterbricht den direkten Körperweg.


Ungeklärter Anschluss

Die Brückendarstellung ist kein pauschaler Bodenfüllbereich.

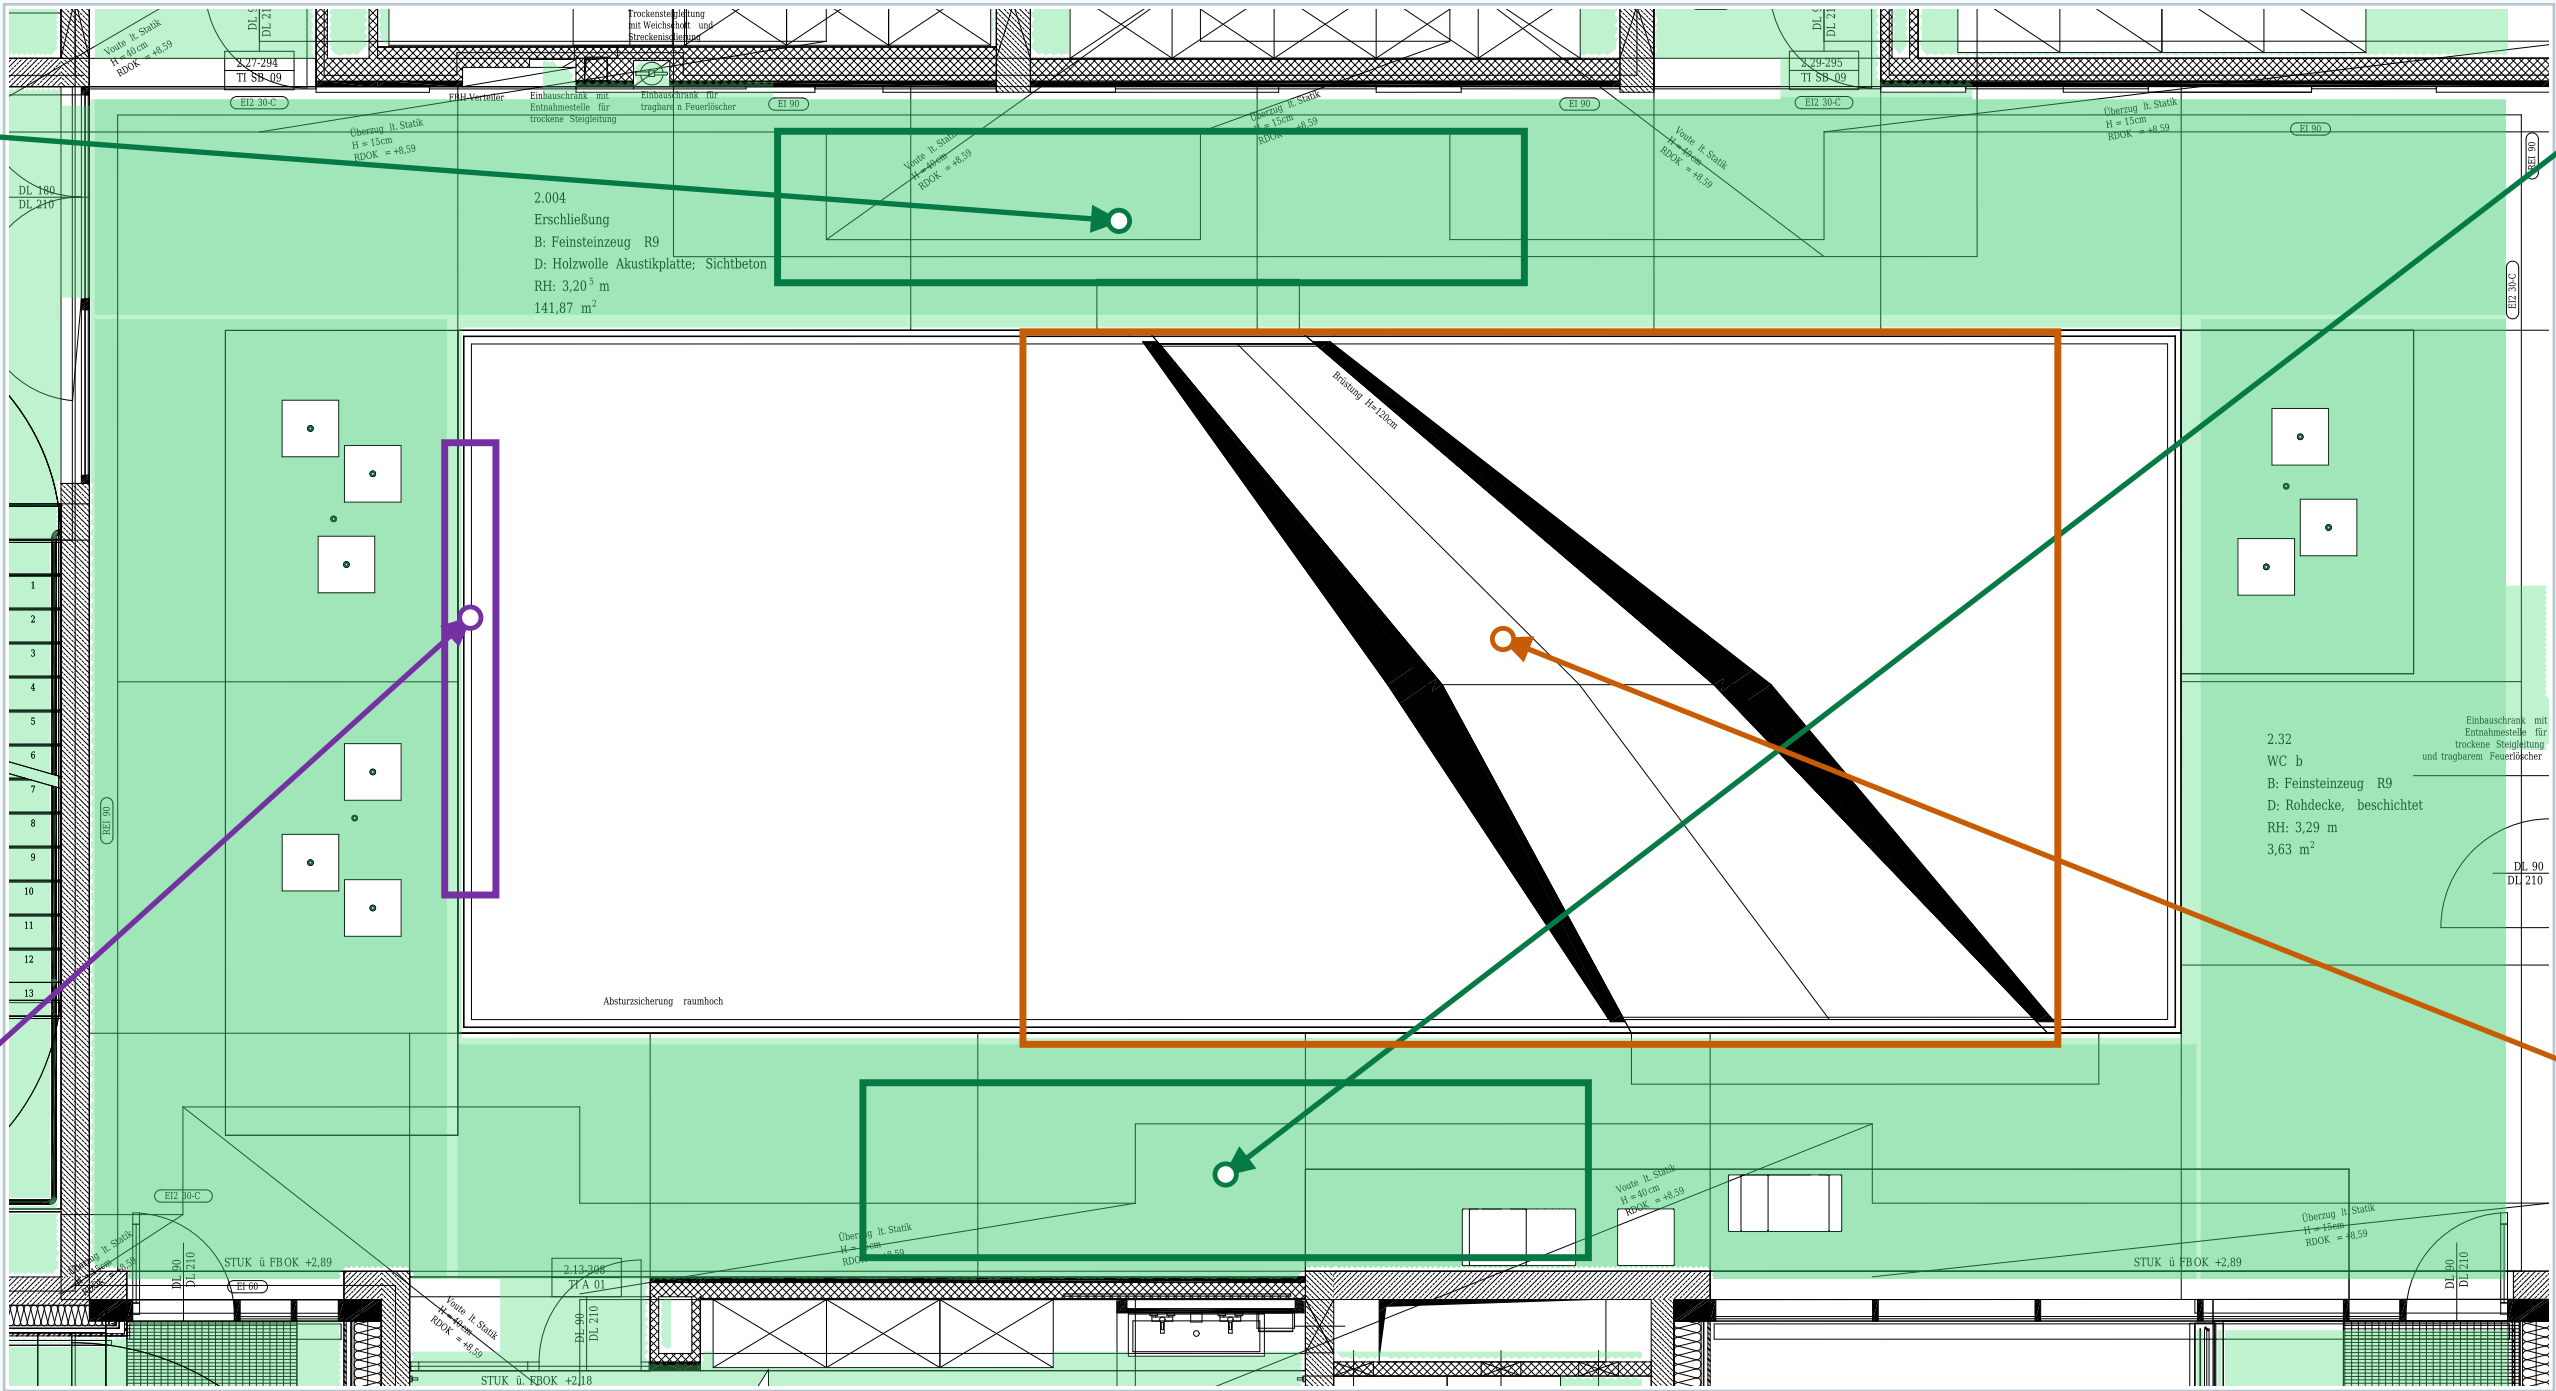


Geschlossener Rahmen + Pfeil: erklärter Bereich. Farblinien: hervorgehobene Merkmale.

G03 | Markierungen am Originalausschnitt

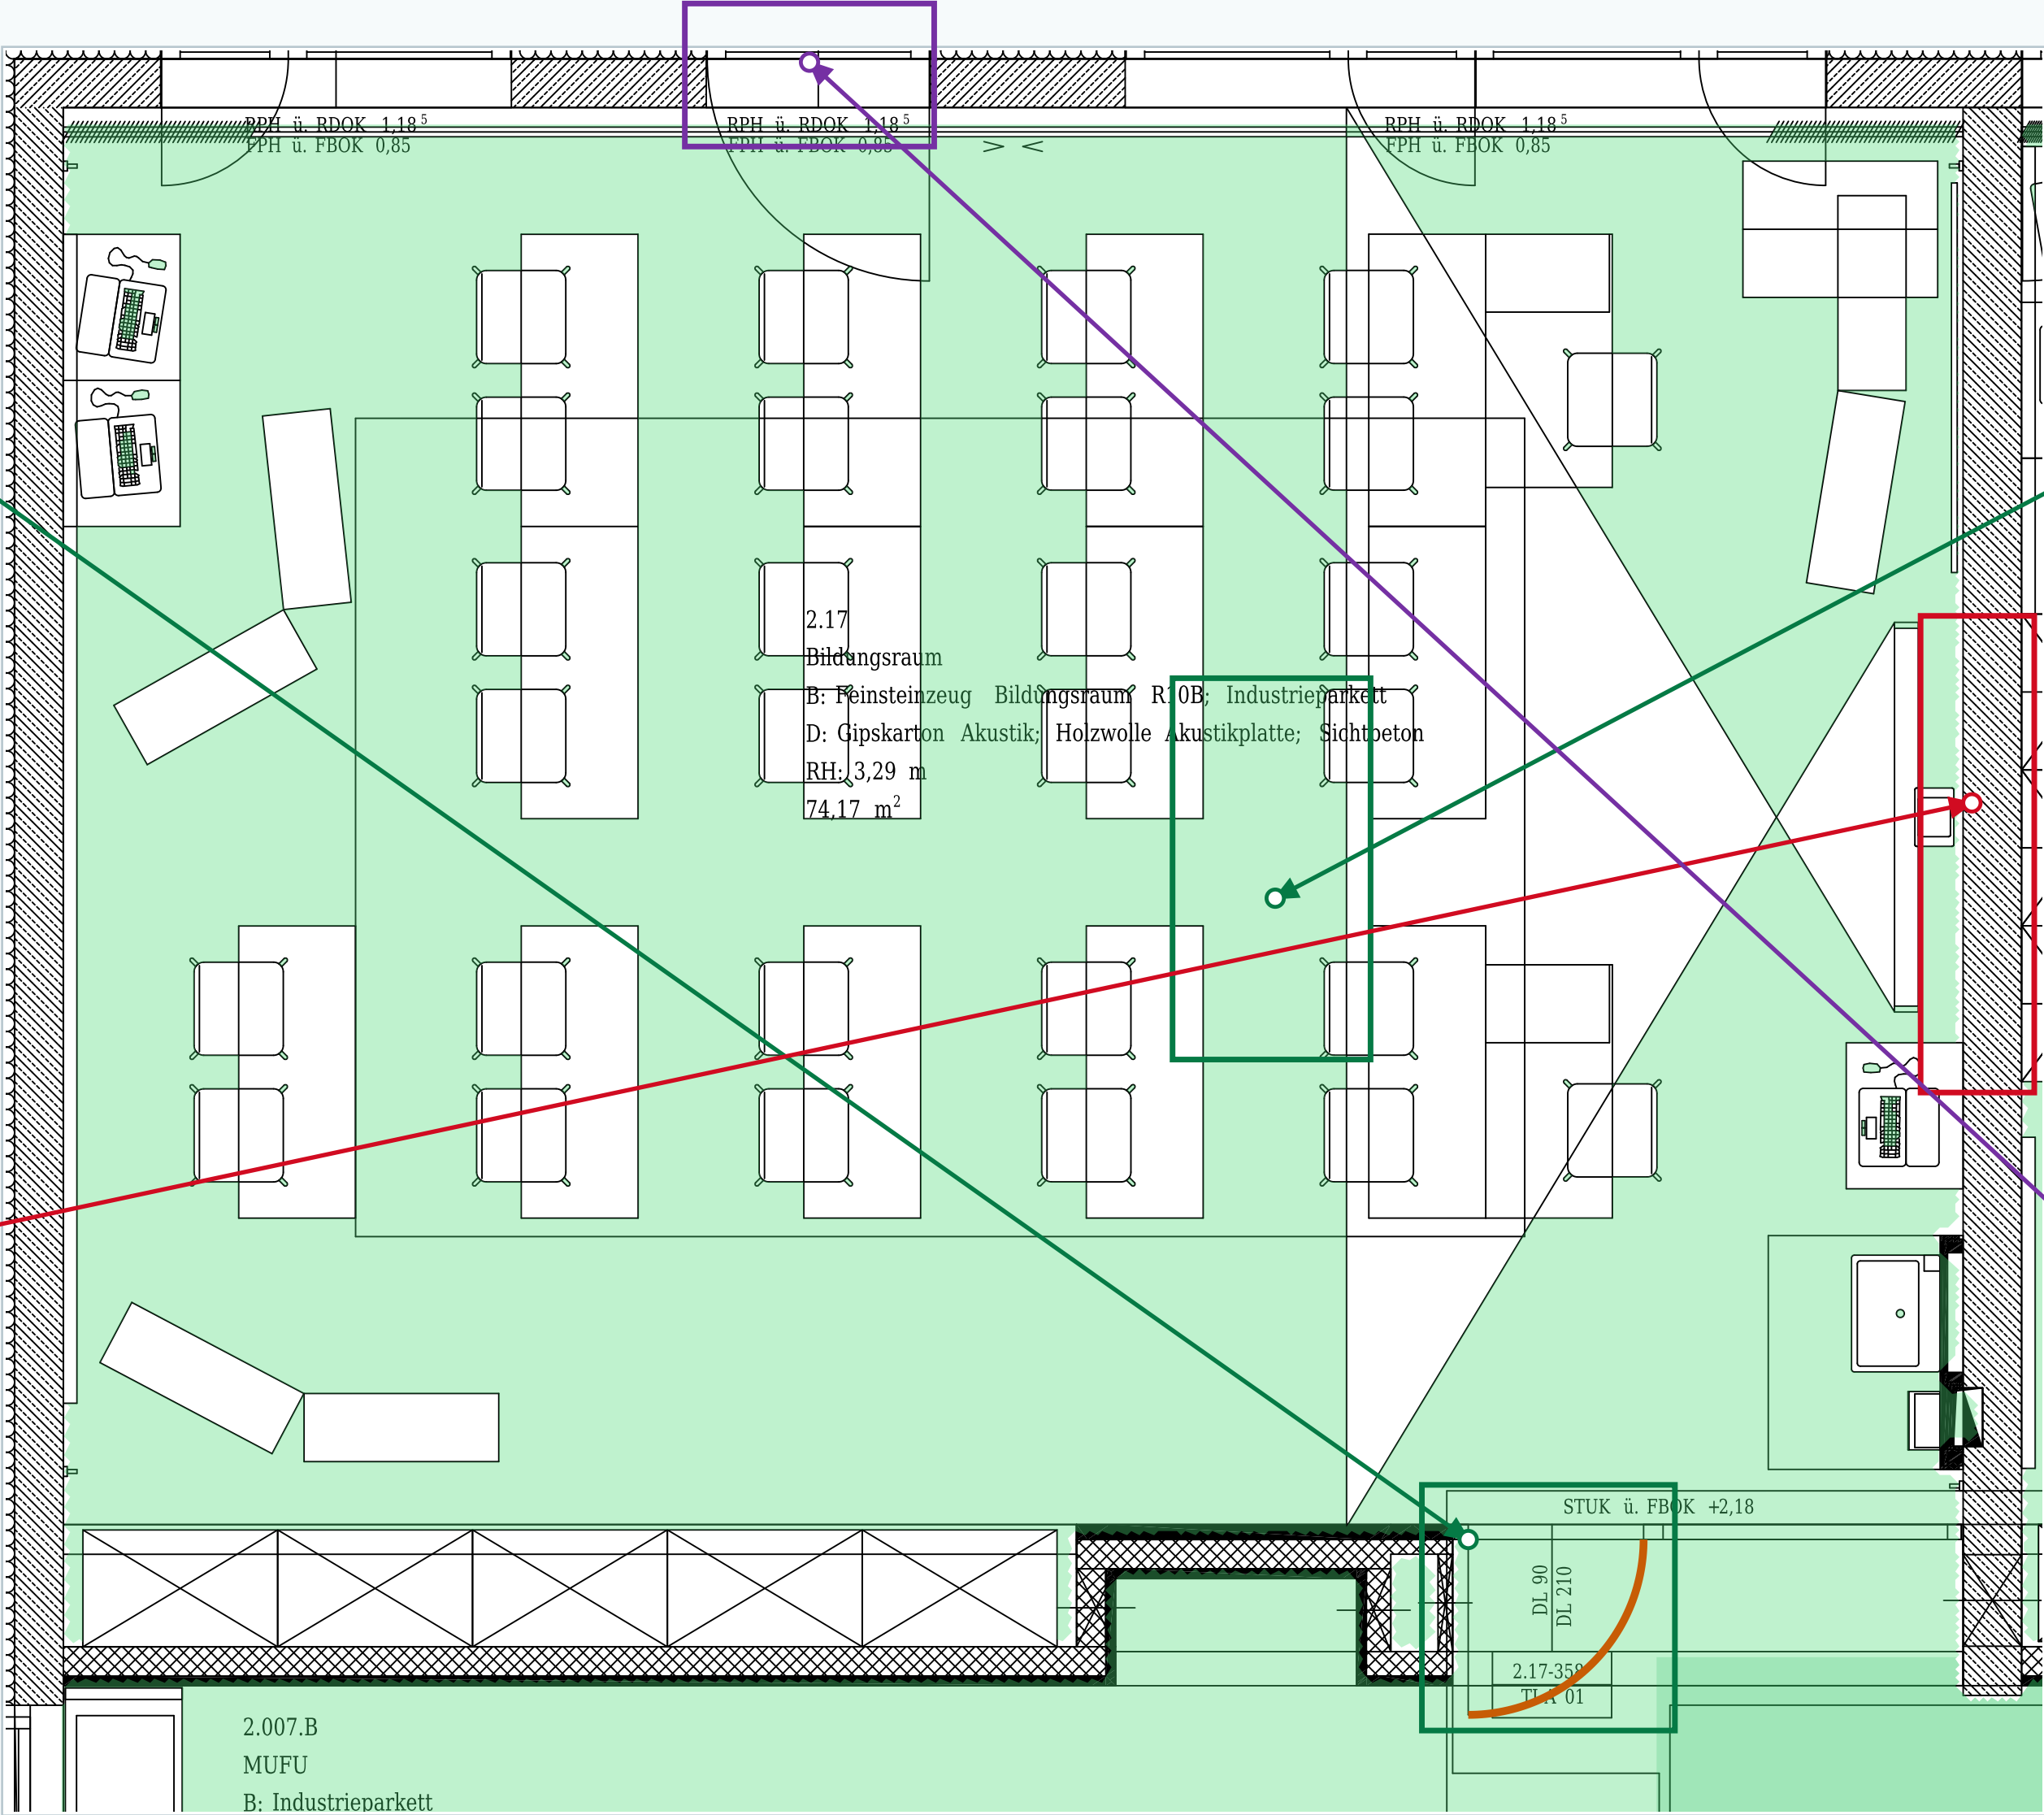

Geschlossener Rahmen + Pfeil: erklärter Bereich. Farblinien: hervorgehobene Merkmale.

G04 | Markierungen am Originalausschnitt

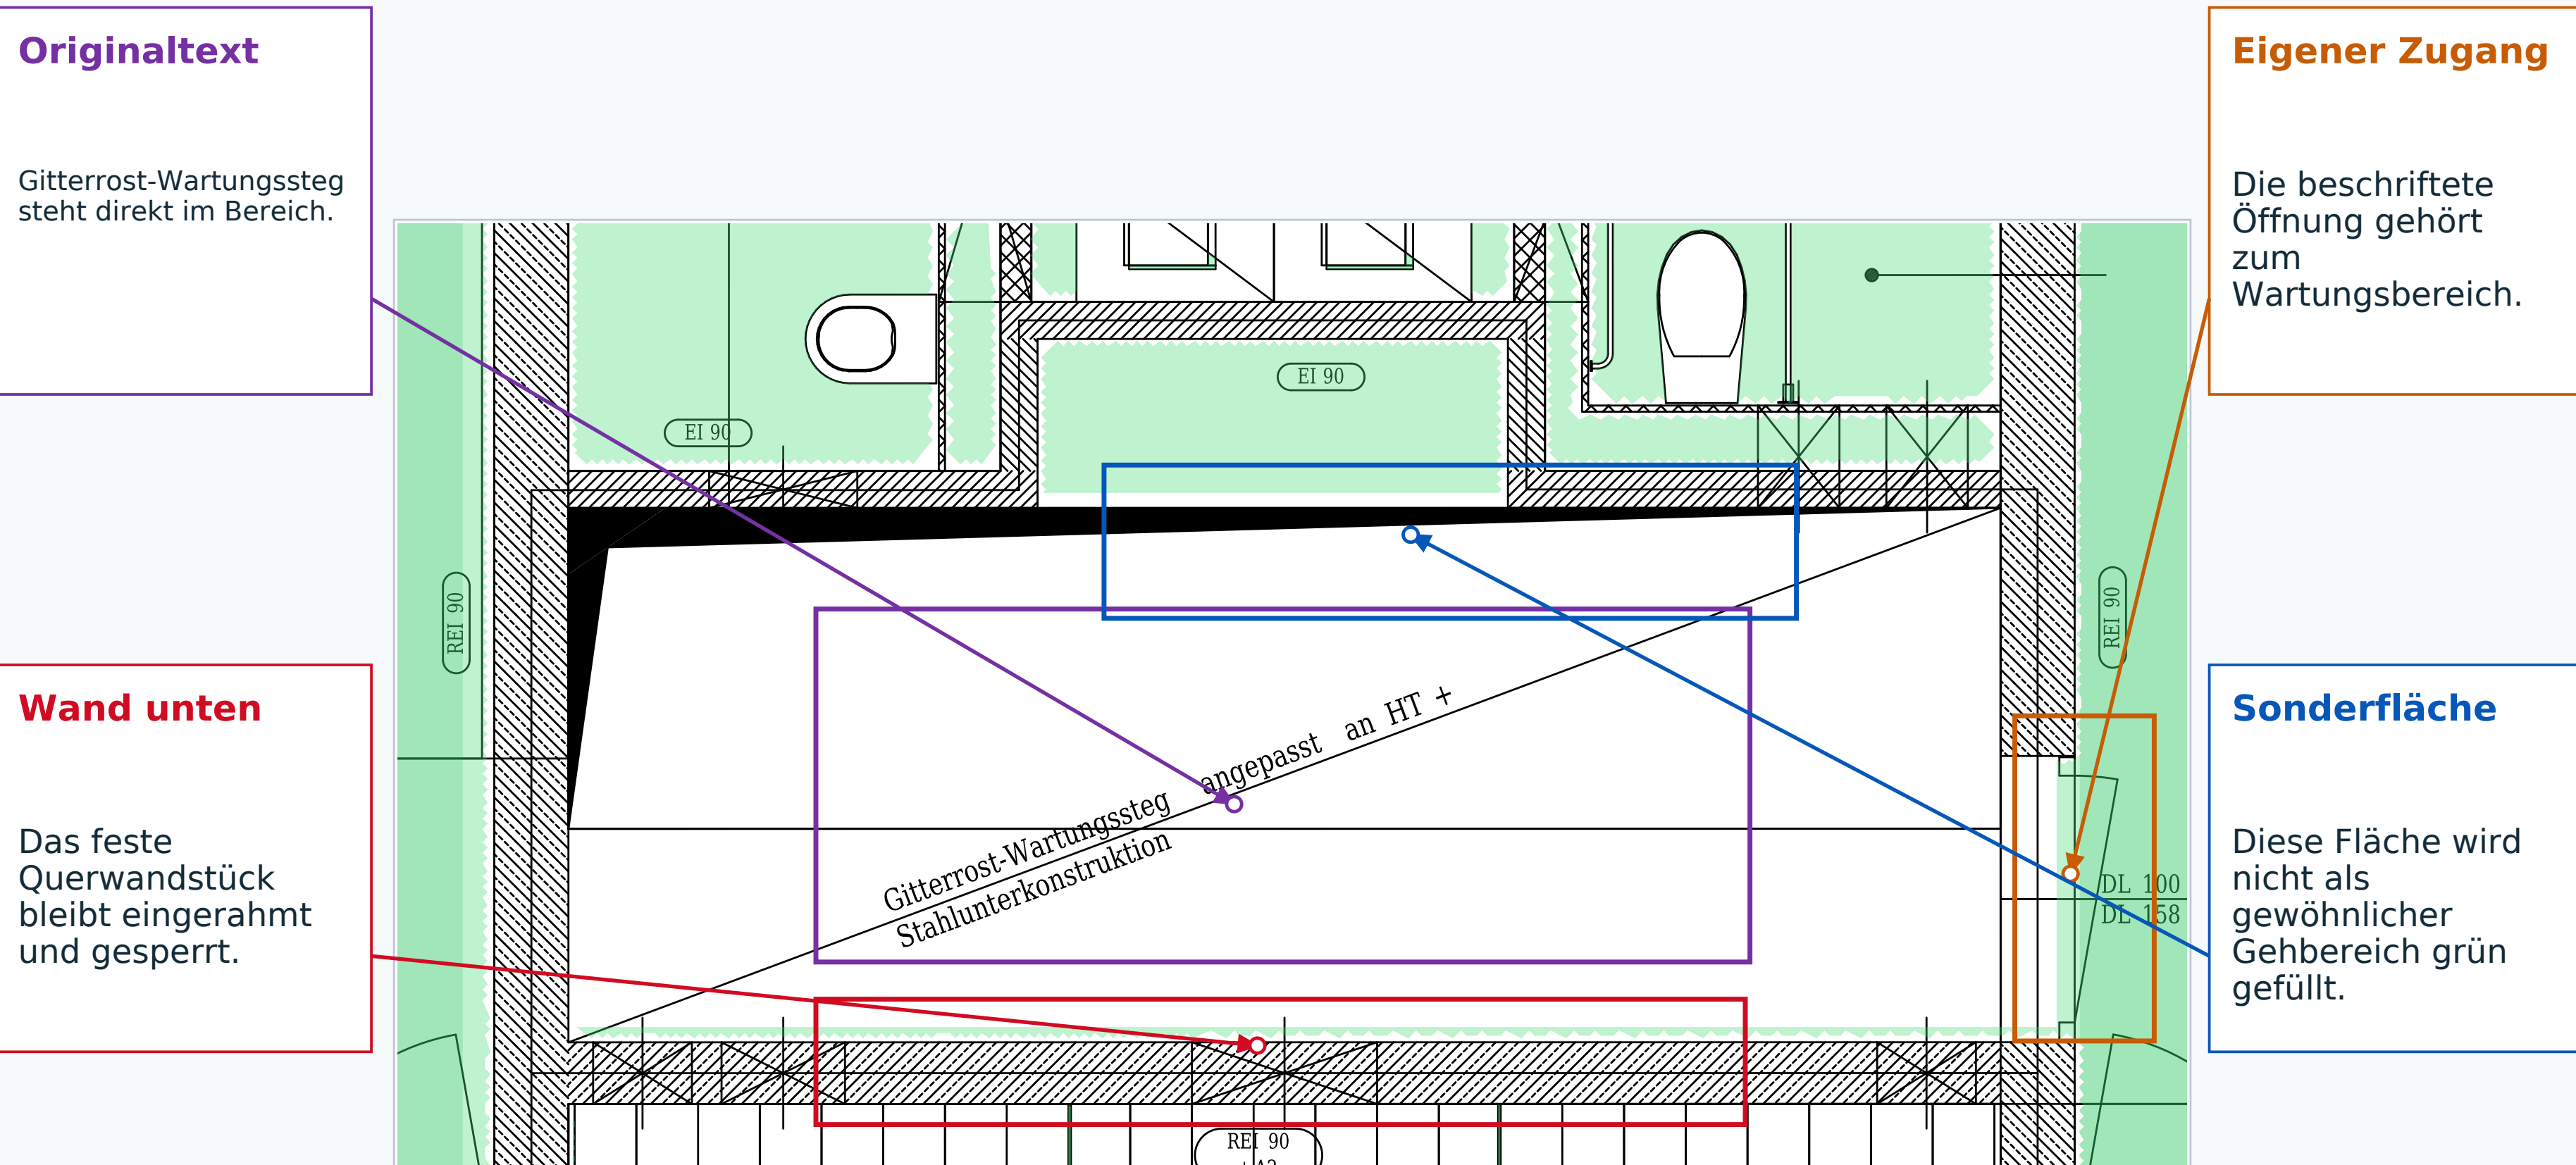

Geschlossener Rahmen + Pfeil: erklärter Bereich. Farblinien: hervorgehobene Merkmale.

G05 | Markierungen am Originalausschnitt

Freiklasse / Boden

Die bezeichnete Außenfläche hat einen erkennbaren Bodenaufbau.

Umwehrter Bereich


Die Absturzsicherung begrenzt die nicht grün gefüllte Fläche.

Stütze aussparen

Die grüne Fläche endet am festen Stützenkörper.

Treppenlauf

Die Treppenfläche ist grün, ihre Originalstufen bleiben schwarz.

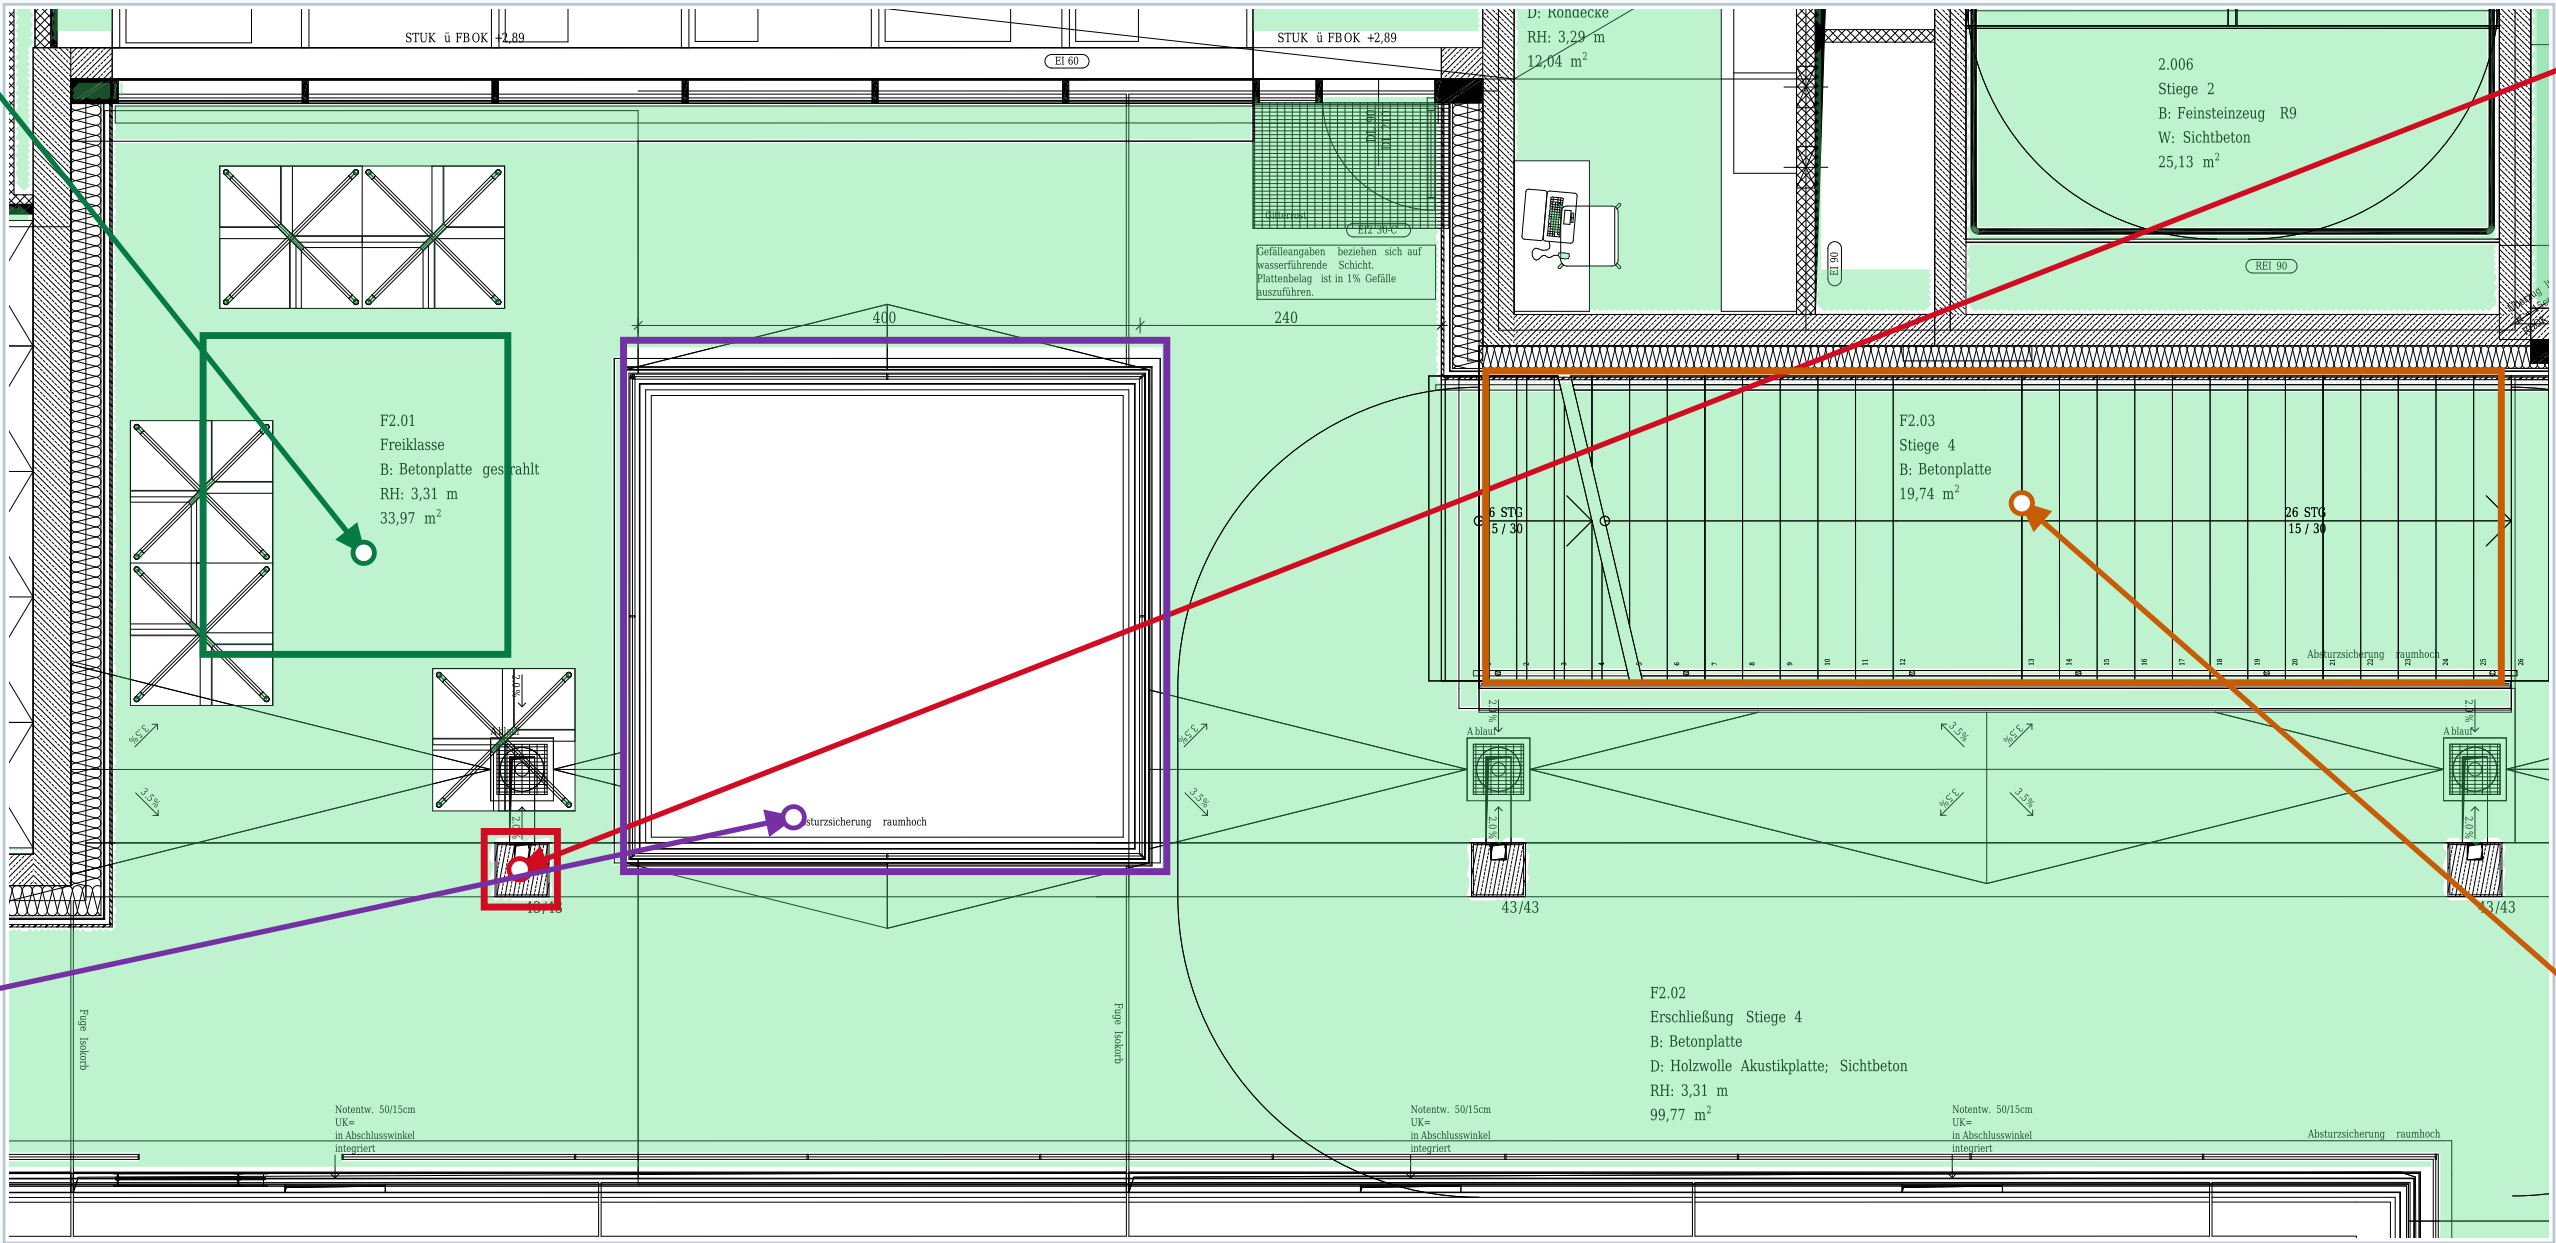

Geschlossener Rahmen + Pfeil: erklärter Bereich. Farblinien: hervorgehobene Merkmale.

S01 | Markierungen am Originalausschnitt

Stufenfolge

Die vielen regelmäßigen Querlinien bilden den Treppenlauf.

Podest


Am Ende der Stufenfolge liegt die zusammenhängende Zwischenfläche.

Laufhinweis

Pfeil, Stufennummern und 13 STG 15/30 gehören zusammen.

Mittlere Grenze

Die beschriftete raumhohe Brüstung trennt die Läufe.

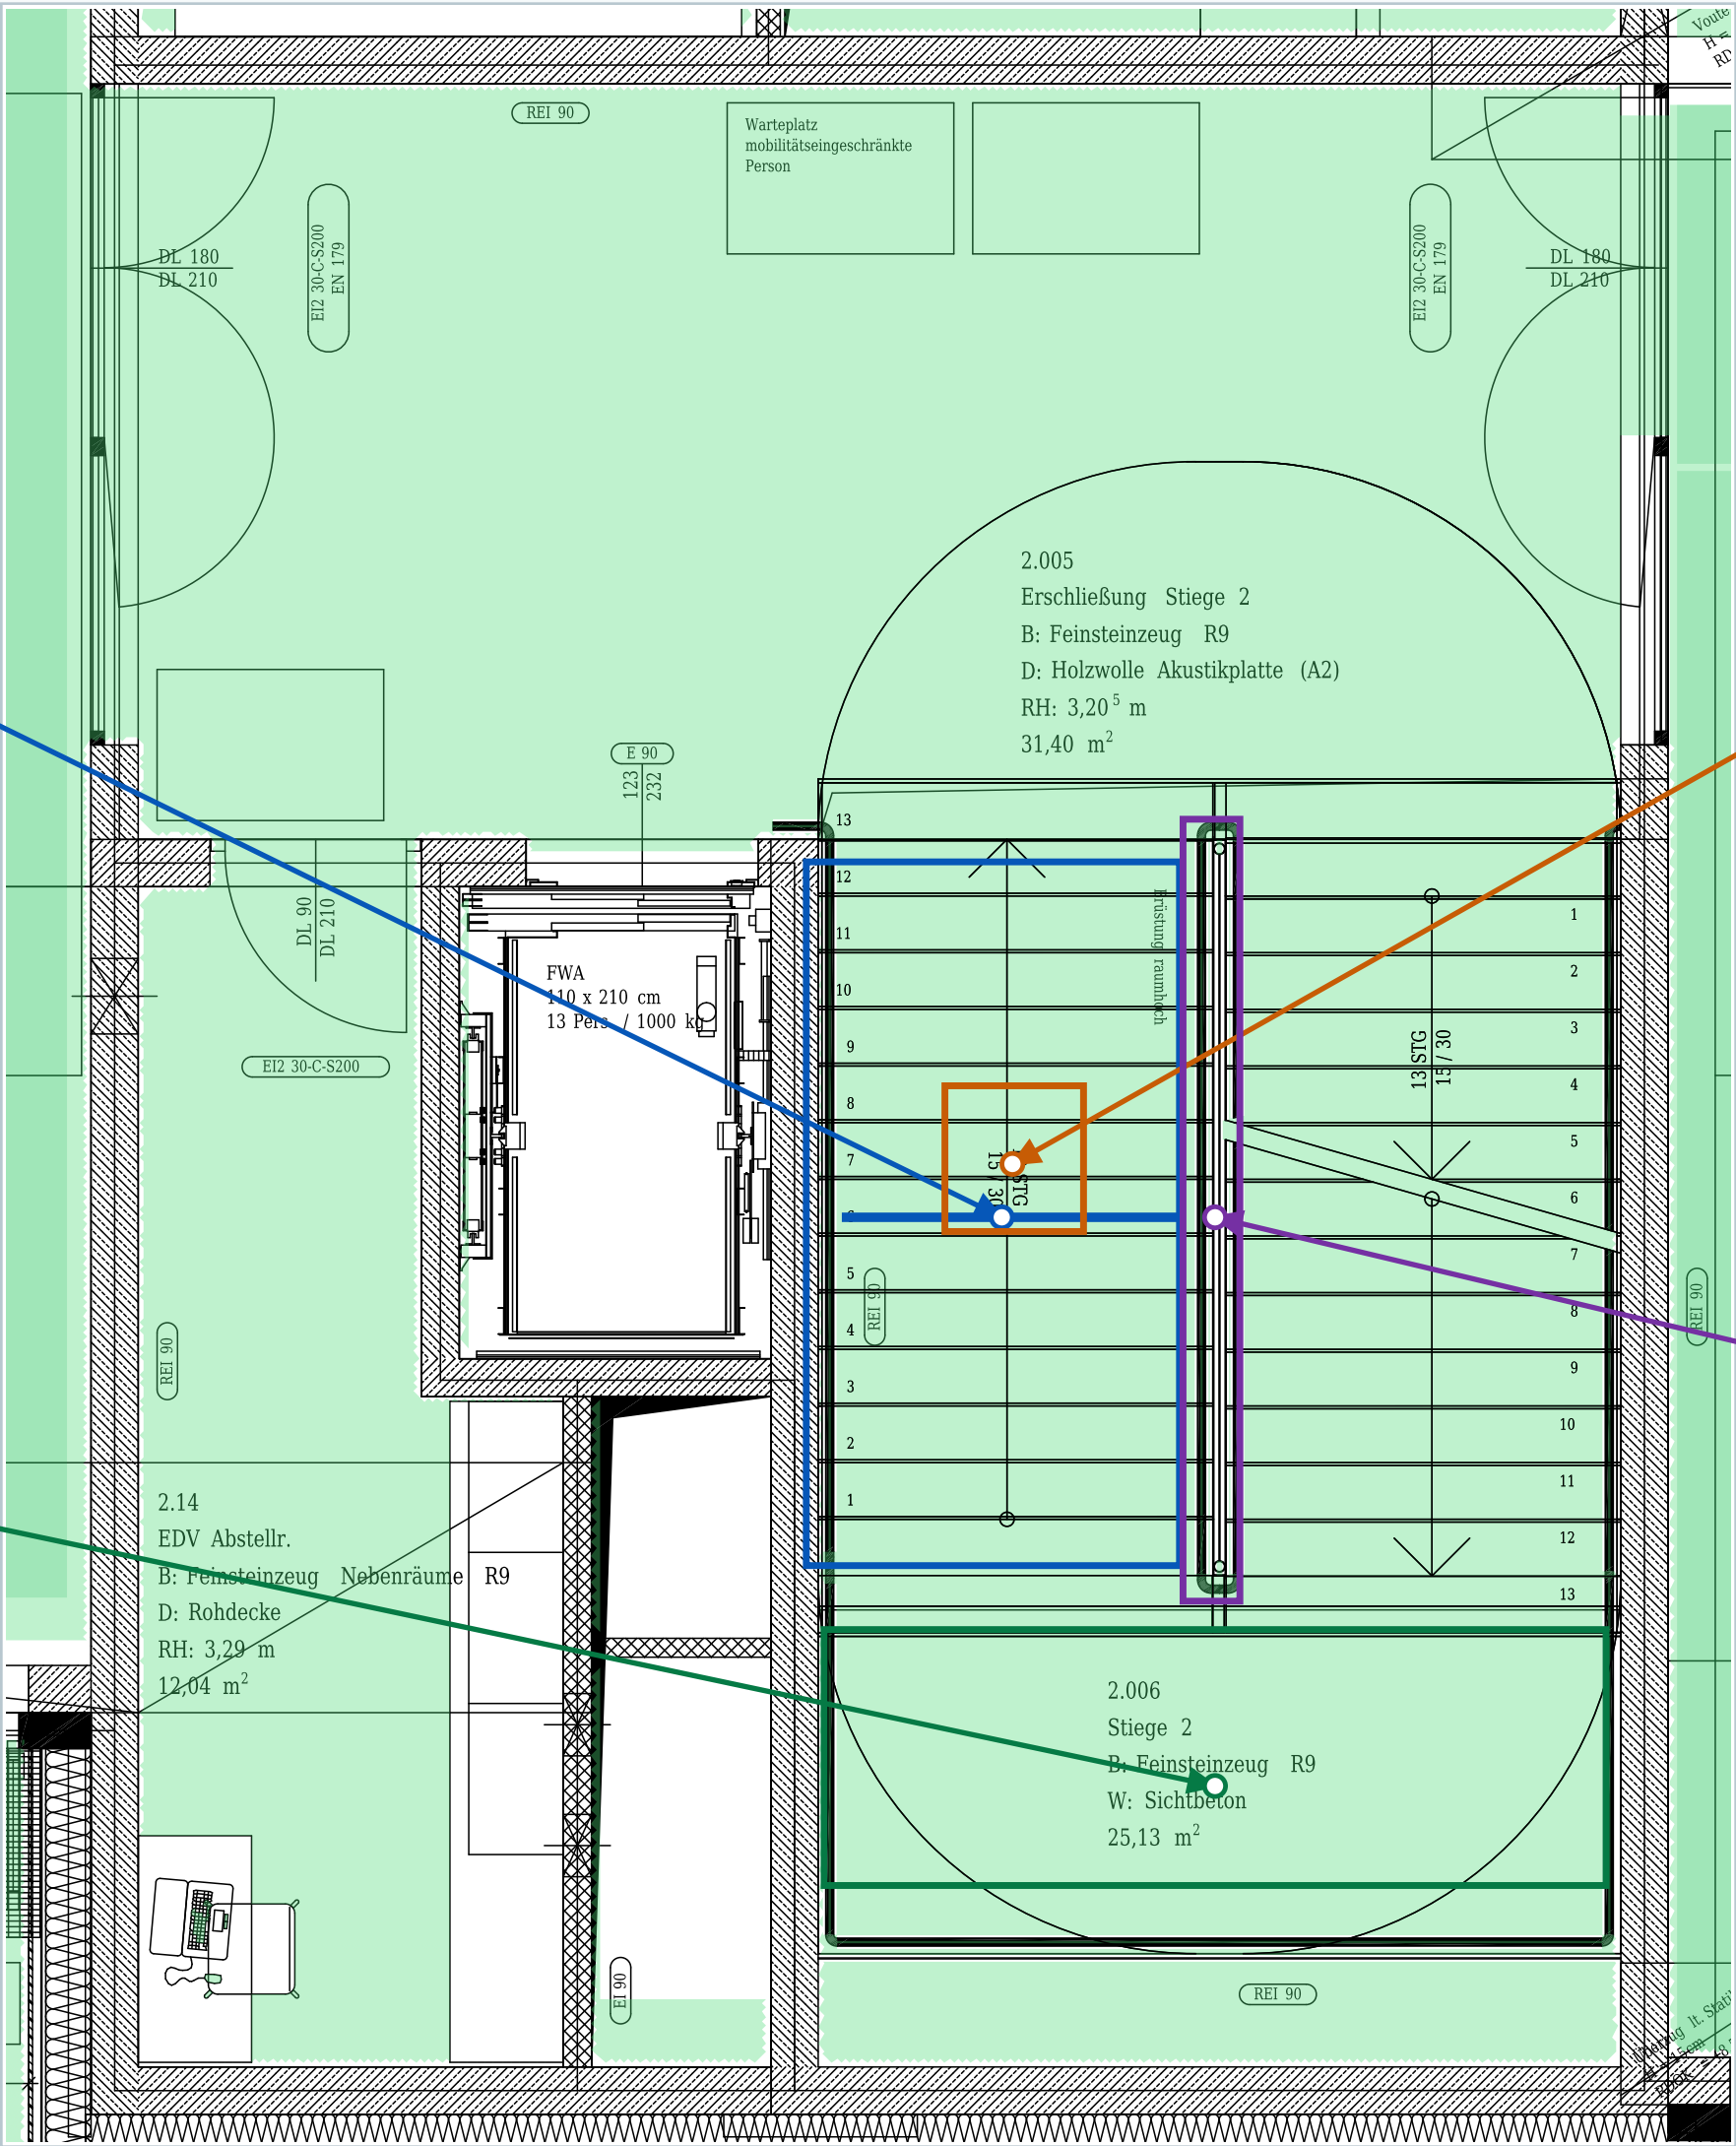

Geschlossener Rahmen + Pfeil: erklärter Bereich. Farblinien: hervorgehobene Merkmale.

S02 | Markierungen am Originalausschnitt

Stufen bleiben schwarz

Die originalen Stufenkanten liegen sichtbar über der grünen Fläche.

Aufzug daneben


Der Schacht rechts ist eine eigene Anlage, keine Fortsetzung des Laufs.

Bruchdarstellung

Die schräge Unterbrechung markiert die Darstellung des Treppenlaufs.

Podestfläche

Die größere Fläche am Laufende ist ein Podest.

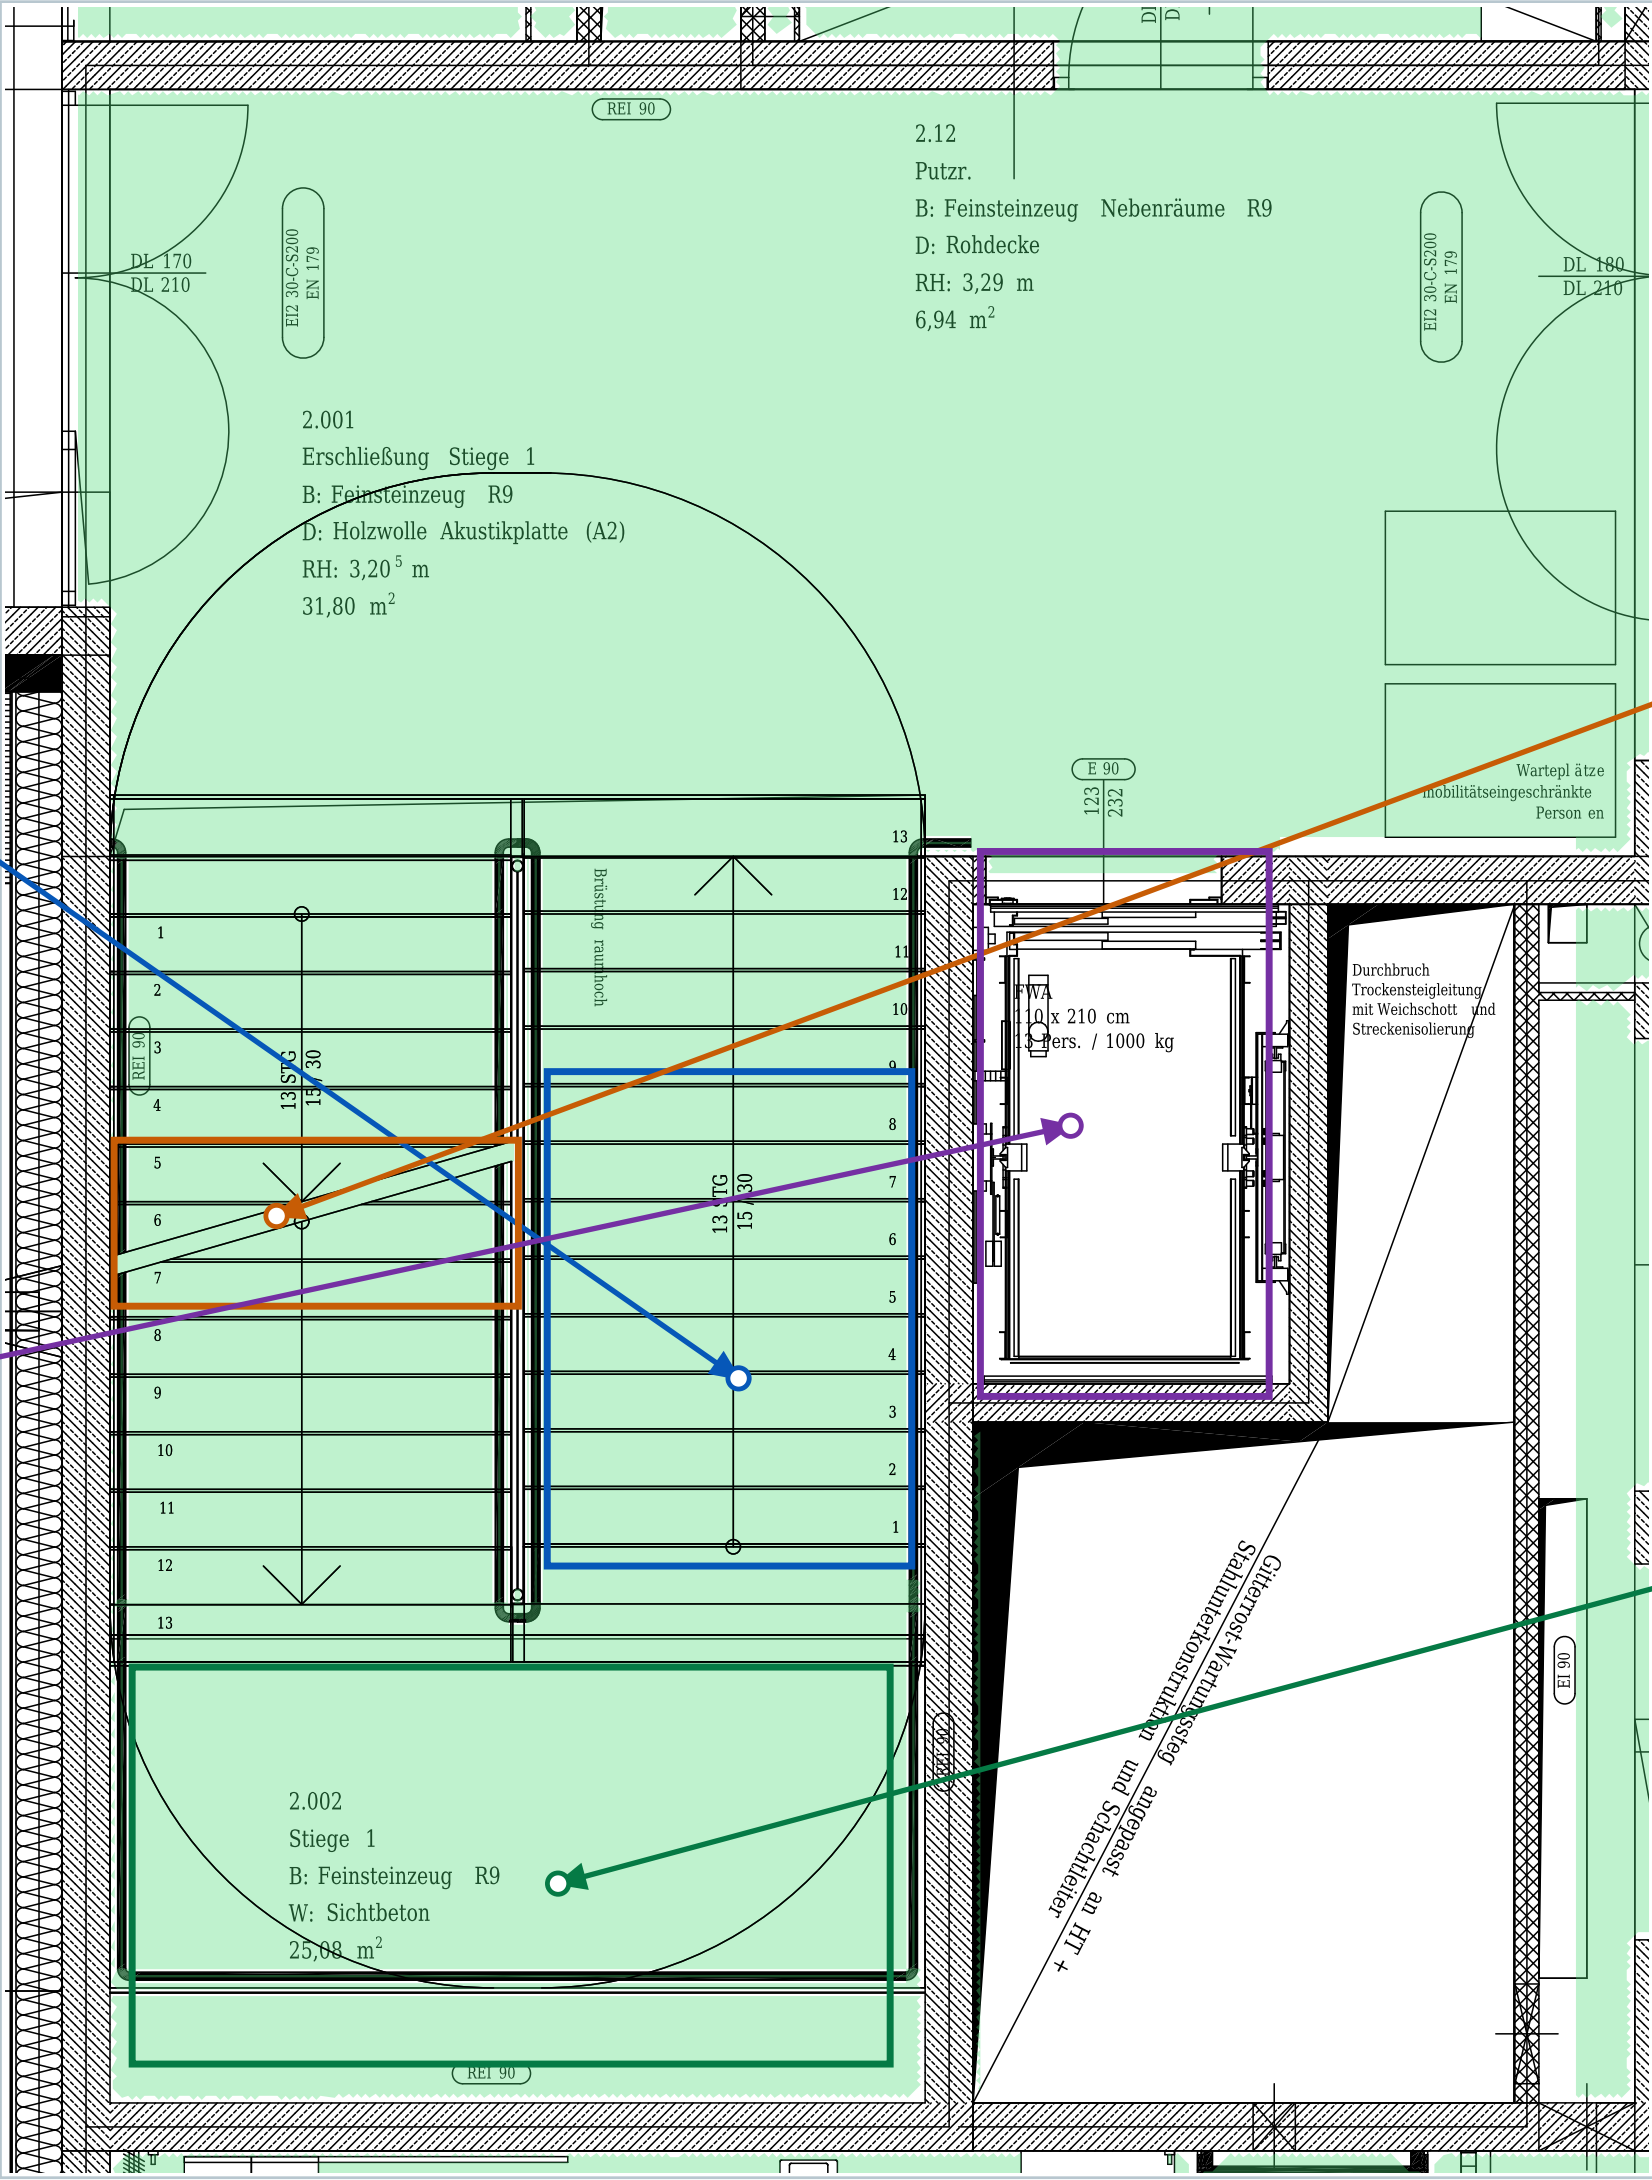

Geschlossener Rahmen + Pfeil: erklärter Bereich. Farblinien: hervorgehobene Merkmale.

S03 | Markierungen am Originalausschnitt

26 STG

Die Originalbeschriftung nennt 26 STG 15/30.

Stufen / Nummern


Die regelmäßigen Querlinien und Nummern laufen über die Treppenfläche.

Bruch im Lauf

Die schräge Bruchdarstellung bleibt schwarz sichtbar.

Seitliche Sicherung

Die raumhohe Absturzsicherung begrenzt den Lauf.

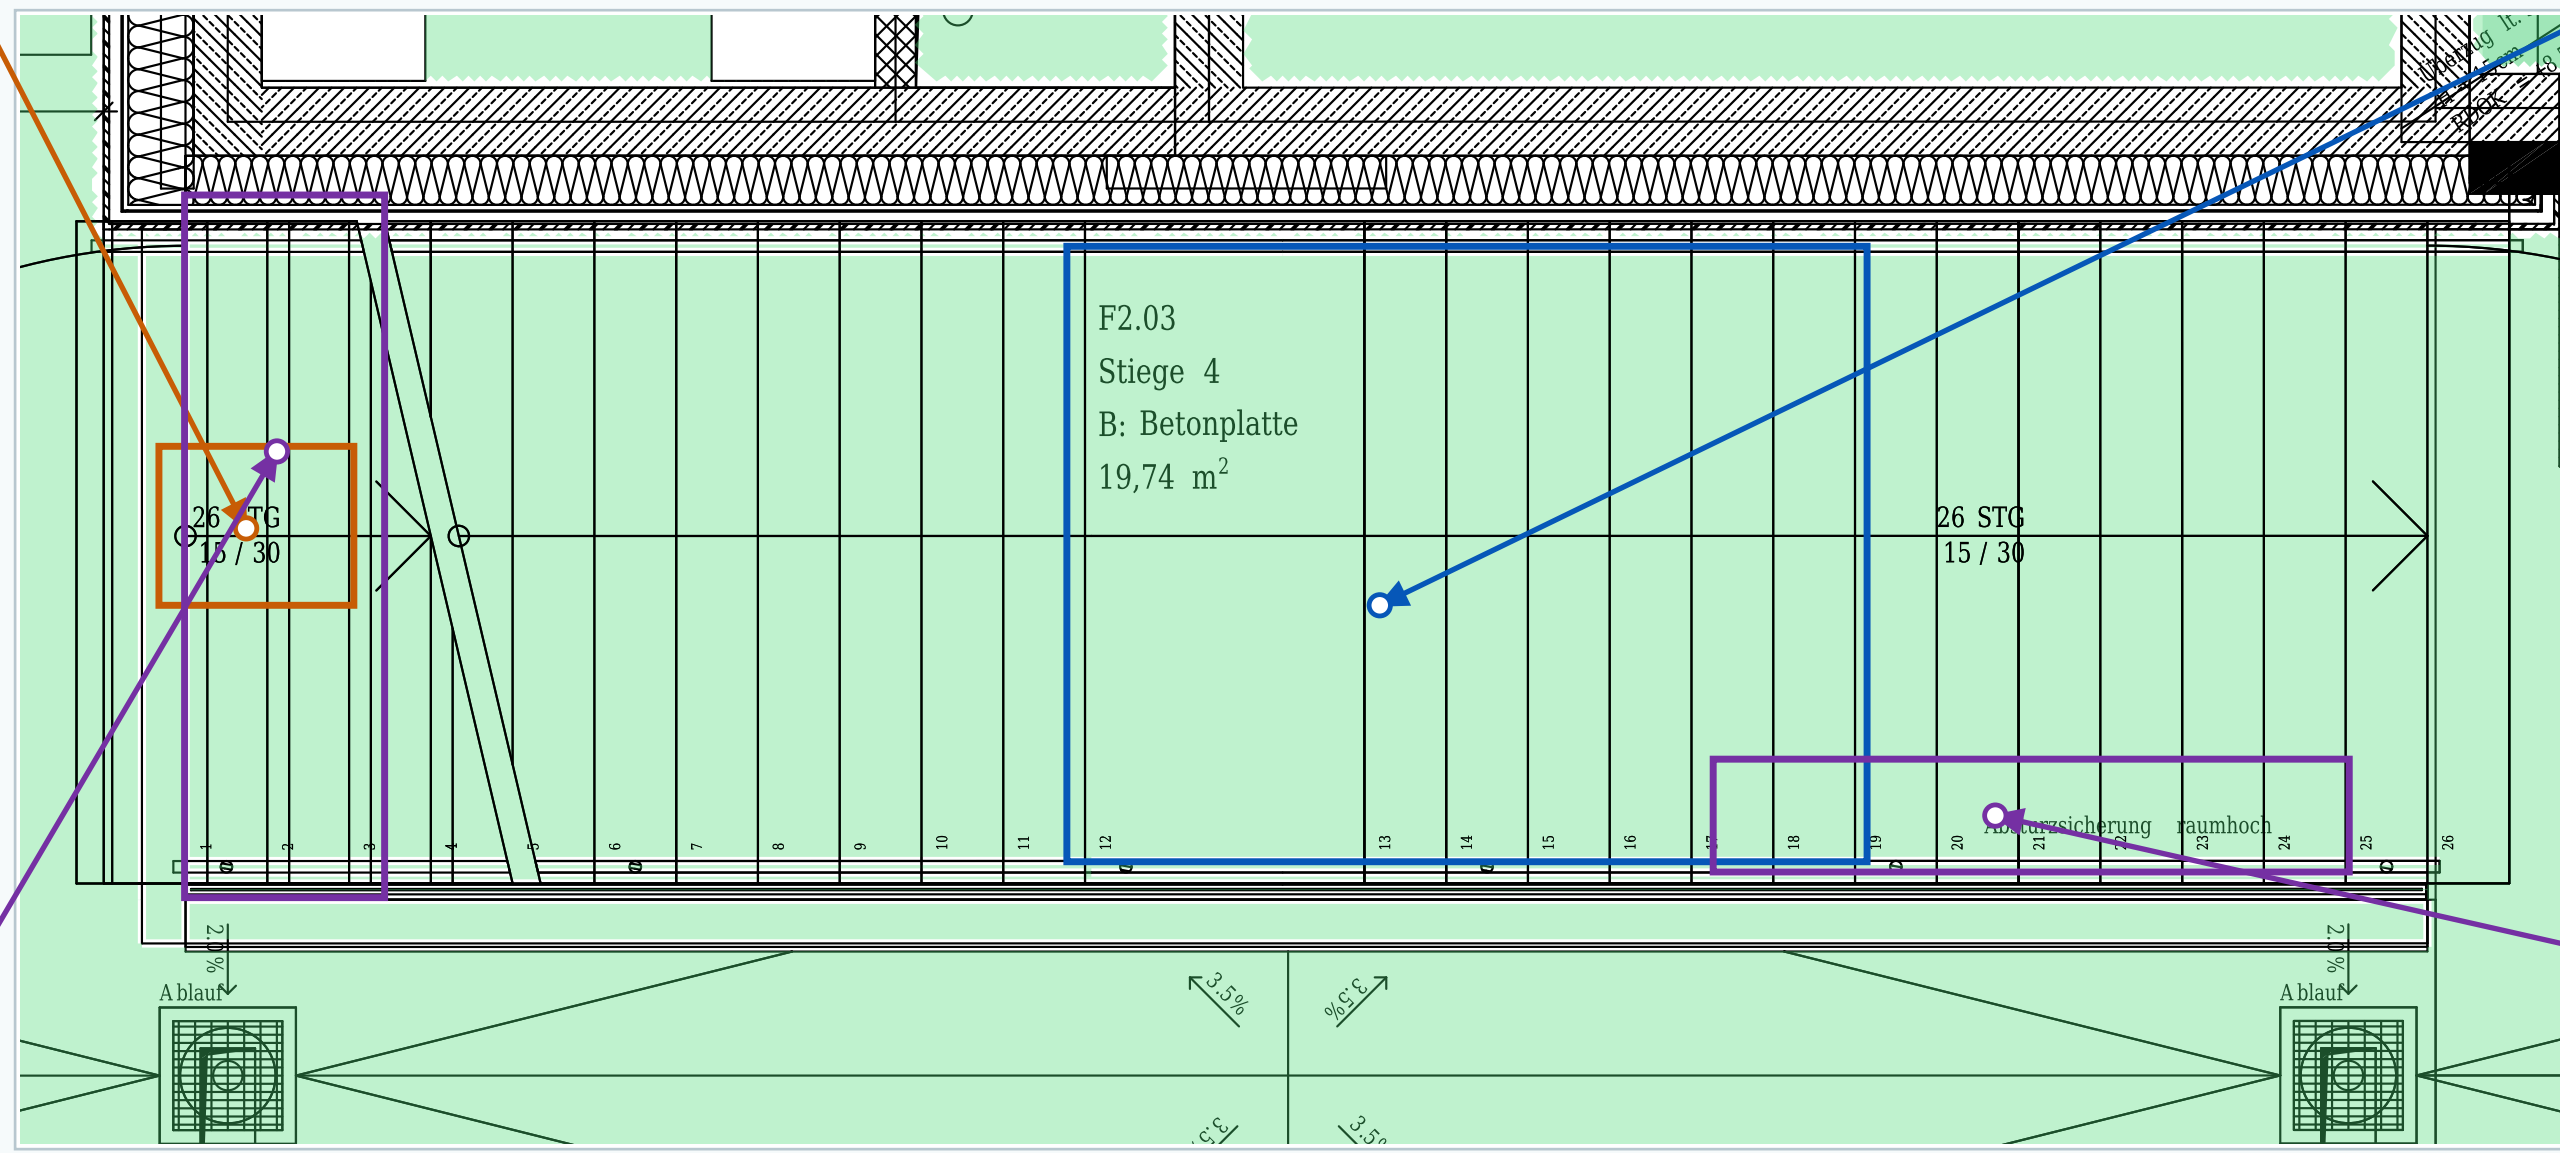

S04 | Markierungen am Originalausschnitt

Treppenbeleg

F2.06 und Stiege 3 stehen innerhalb des Bereichs.

Stufenfolge


Die Originallinien wiederholen sich quer zum Lauf.

Absturzsicherung

Diese Grenze ist als raumhoch bezeichnet.

Vorbereich

F2.05 bezeichnet die zugehörige Erschließung.

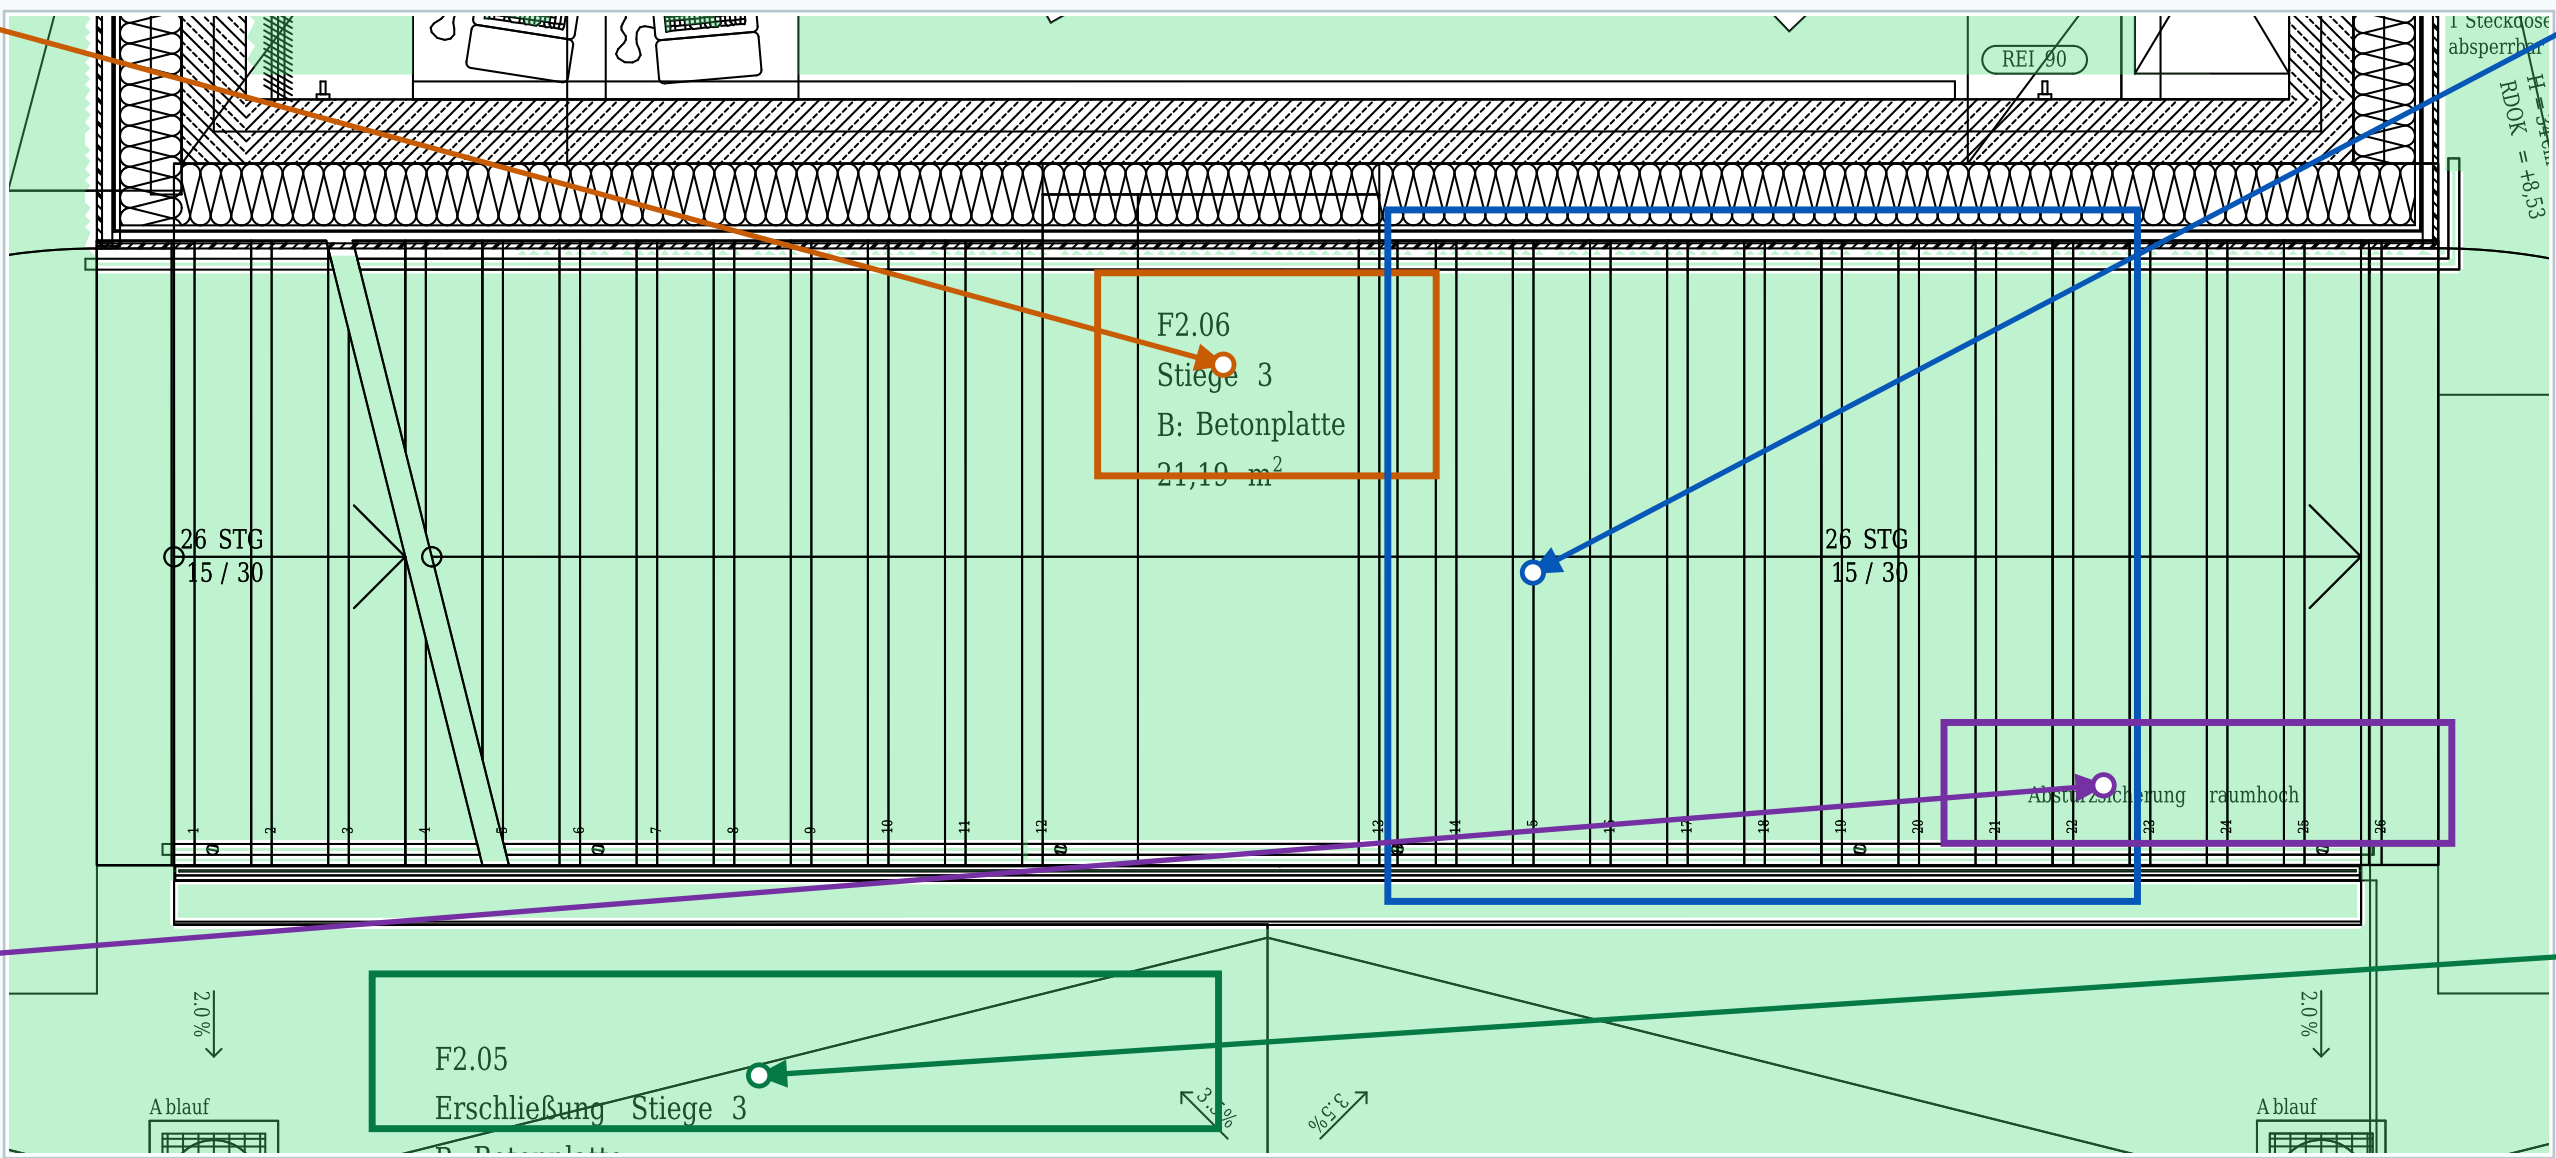

Geschlossener Rahmen + Pfeil: erklärter Bereich. Farblinien: hervorgehobene Merkmale.

S05 | Markierungen am Originalausschnitt

Raumstempel

Der Plan benennt den Raum 2.26 als Garderobe.

Einbauraster


Die kleinen Rechtecke gehören zu den Einbauten.

Keine Stufenbelege

Hier fehlen ein Treppenlauf, STG-Angabe und zusammengehörige Podeste.

Türen zum Raum

Die Seitenzugänge verbinden den Raum mit der Erschließung.

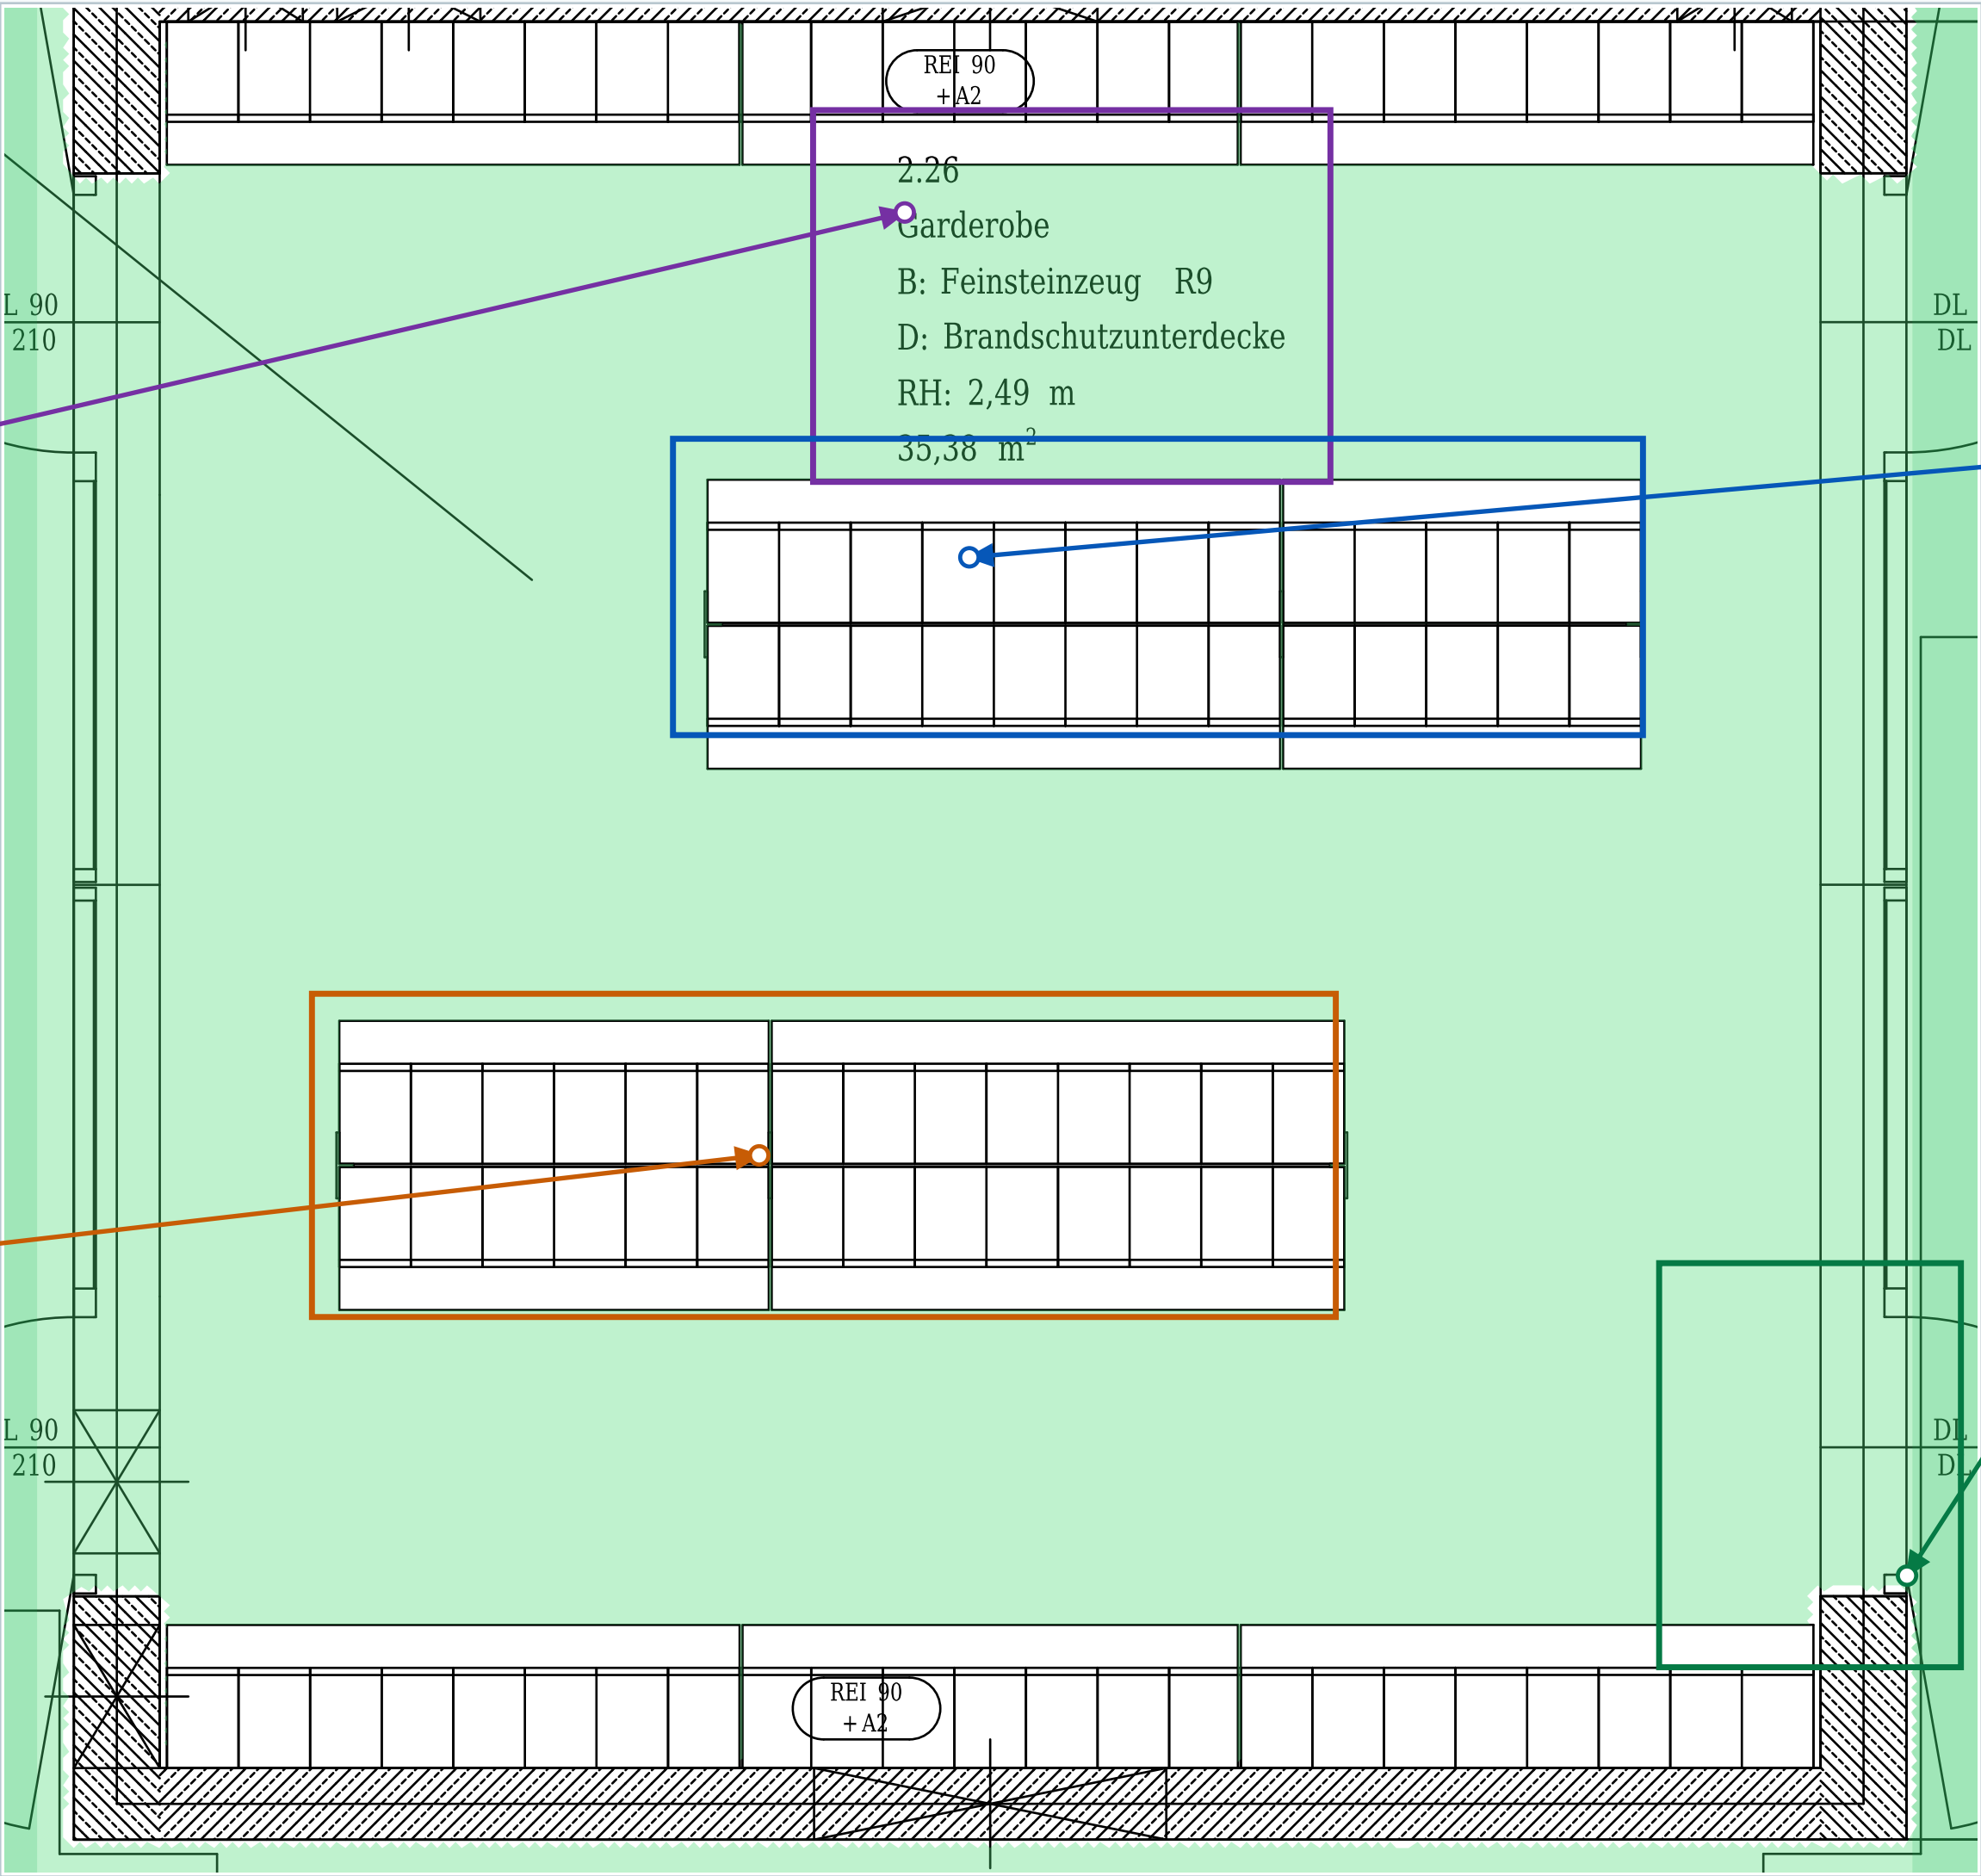

Geschlossener Rahmen + Pfeil: erklärter Bereich. Farblinien: hervorgehobene Merkmale.