



LEGENDE

- STAHLBETON
- BETON
- GIPSKARTONSTÄNDERWAND EI0
- GIPSKARTONSTÄNDERWAND EI30
- GIPSKARTONSTÄNDERWAND EI90
- ZIEGELMAUERWERK
- YTONG
- ALU-GLASKONSTRUKTIONEN
- WÄRMEDÄMMUNG
- BRANDABSCHNITT
- FLW-L FLUCHTWEGSLÄNGE
- TSL LÄNGE TSL
- TRÖCKENSTEGLEITUNG

ABKÜRZUNGEN


- AUDK ... Unterkante abgehängter Decke
- AR ... Abstellraum
- BRE ... Brandrauchentlüftung
- BST ... Brandschutztor
- DBA ... Druckbelüftungsanlage
- DDB ... Deckendurchbruch
- F+H ... Feuerlöscher und Hydrantenkasten
- FDB ... Fußbodendurchbruch
- FOK ... Fußbodenoberkante
- FSTZ ... Feinsteinzeugbelag
- FW ... Feuerwehrlift
- HT ... Haustechnikanlage
- NU ... Notüberlauf
- ROK ... Rohoberkante
- RR ... Regenrohr
- RUH ... Rohunterkante
- STGH ... Stiegenhaus
- UZUK ... Unterzugunterkante
- VR ... Vorraum
- WDB ... Wanddurchbruch

NATURMASZE NEHMEN KOTEN PRÜFEN
±0,00 = +6,90 ü. Wiener Null (ü. WN)

© HNP architects ZT GmbH
DIESES DOKUMENT IST URHEBERRECHTLICH GESCHÜTZT. JEDE WEDE VERWENDUNG ODER BEARBEITUNG BEDARF DERAUSDRÜCKLICHEN ZUSTIMMUNG VON HNP architects

INDEX	DATUM	GEZ.	ÄNDERUNG
A	30.10.2025		VORABZUG-Planstand Nutzwertgutachten
B	20.01.2026		Änderung zur Ausgabe
C	10.03.2026		Änderung zur Ausgabe
D	07.05.2026		Änderung zur Ausgabe

FREIGABE:	BH	ÖBA	ELT	HKLS	TWP	BP	BS
DATUM:							
NAME:							
UNTERSCHR.:							

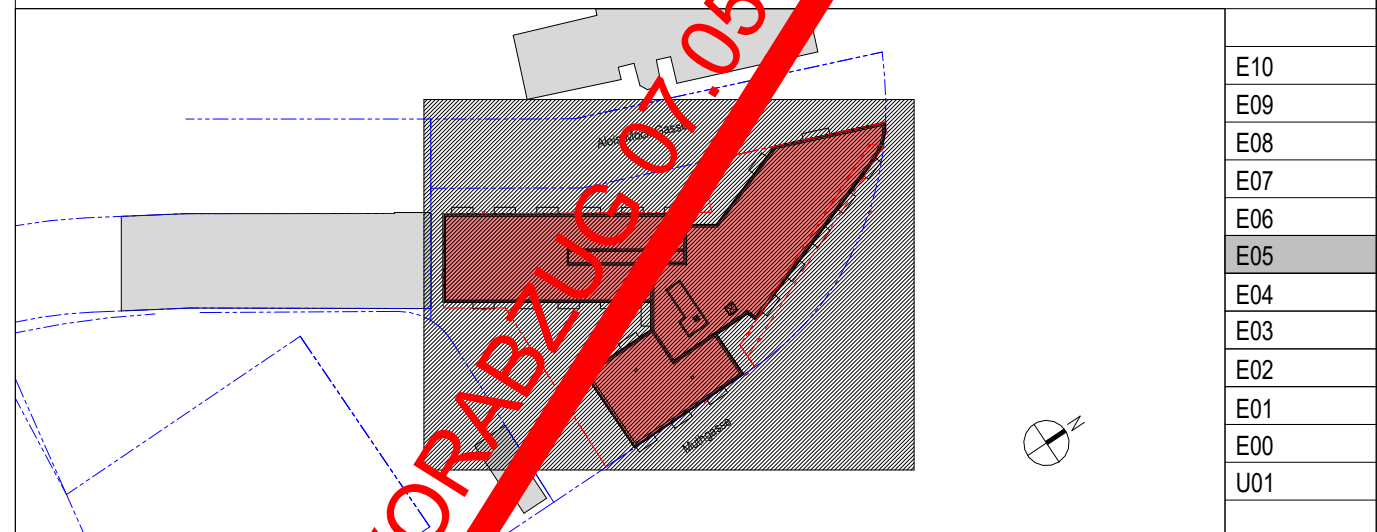

BAUHERR:		at home Immobilien-GmbH Zweigniederlassung Wien Hernalser Gürtel 1, 1170 Wien	
ROHBAU POLIERPLAN Muthgasse 109B, 1190 WIEN			
PLANNUMMER:		PR NR: 4-992-23	
4-992-23		DATUM: 22.04.2024	
HNP AF A GR 05 AB VA D		INDEXDATUM: 07.05.2026	
PLANNUMMER:		PL GR: 1050x650	
HNP ARCHITECTS ZT GMBH A-1190 WIEN - MUTHGASSE 109 +43 1 370 16 16-0 FAX DW6 OFFICE@HNP-ARCHITECTS.COM		GEZ: HNP GEPR: EZ MASSSTAB: 1:100	