



LEGENDE

- STAHLBETON
- BETON
- GIPSKARTONSTÄNDERWAND E10
- GIPSKARTONSTÄNDERWAND E130
- GIPSKARTONSTÄNDERWAND E190
- ZIEGELMAUERWERK
- YTONG
- ALU-GLASKONSTRUKTIONEN
- WÄRMEDÄMMUNG
- BRANDABSCHNITT
- FLW-L FLUCHTWEGSLÄNGE
- TSL LÄNGE TSL
- TRÖCKENSTEIGLEITUNG

ABKÜRZUNGEN

- ADUK ... Unterkannte abgehängter Decke
- AR ... Abstellraum
- BRE ... Brandrauchentlüftung
- BST ... Brandschutztor
- DBA ... Druckbelüftungsanlage
- DDB ... Deckendurchbruch
- F+H ... Feuerlöscher und Hydrantenkasten
- FDB ... Fussbodendurchbruch
- FOK ... Fussbodenoberkante
- FSTZ ... Feinstreuzugbelag
- FW ... Feuerwehrlift
- HT ... Haustechnikanlage
- NU ... Notüberlauf
- ROK ... Rohoberkante
- RR ... Regenrohr
- RUH ... Rohunterkante
- STGH ... Stiegenhaus
- UZUK ... Unterzugunterkante
- VR ... Vorraum
- WDB ... Wanddurchbruch

NATURMASSE NEHMEN KOTEN PRÜFEN
±0,00 =+6,90 ü. Wiener Null (ü. WN)


© HNP architects ZT GmbH
DIESES DOKUMENT IST URHEBERRECHTLICH GESCHÜTZT. JEDE WEITVERWENDUNG ODER BEARBEITUNG BEDARF DERAUSDRÜCKLICHEN ZUSTIMMUNG VON HNP architects

INDEX	DATUM	GEZ.	ÄNDERUNG
A	30.10.2025		Abstimmung erforderlich
B	20.01.2026		VORABZUG-Planstand Nutzwertgutachten
C	10.03.2026		Änderung zur Ausgabe
D	07.05.2026		Änderung zur Ausgabe

FREIGABE:	BH	ÖBA	ELT	HKLS	TWP	BP	BS
DATUM:							
NAME:							
UNTERSCHR.							



home

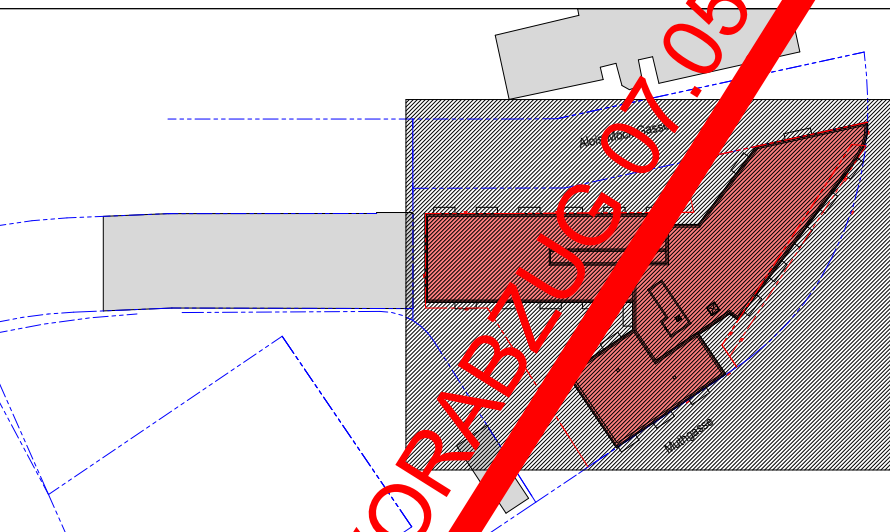

- E10
- E09
- E08
- E07
- E06
- E05
- E04
- E03
- E02
- E01
- E00
- UD1

BAUHERR:

GEWOG Gemeinnützige Wohnungsbau-Ges.m.b.H.
Hernalser Gürtel 1, 1170 Wien

at home Immobilien-GmbH
Zweigniederlassung Wien
Hernalser Gürtel 1, 1170 Wien

ROHBAU POLIERPLAN
Muthgasse 109B, 1190 WIEN

PLANNHALT:
GRUNDRISS E7

PLANNUMMER: 4-992-23

PLANNUMMER: 4-992-23

PROJEKT: HNP AF A GR 07 AB VA D

PR NR: 4-992-23

DATUM: 22.04.2024

INDEXDATUM: 07.05.2026

PL GR: 1050x650

GEZ: HNP

GEPR: EZ

MASSSTAB: 1:100

VORABZUG