Erdgeschoss

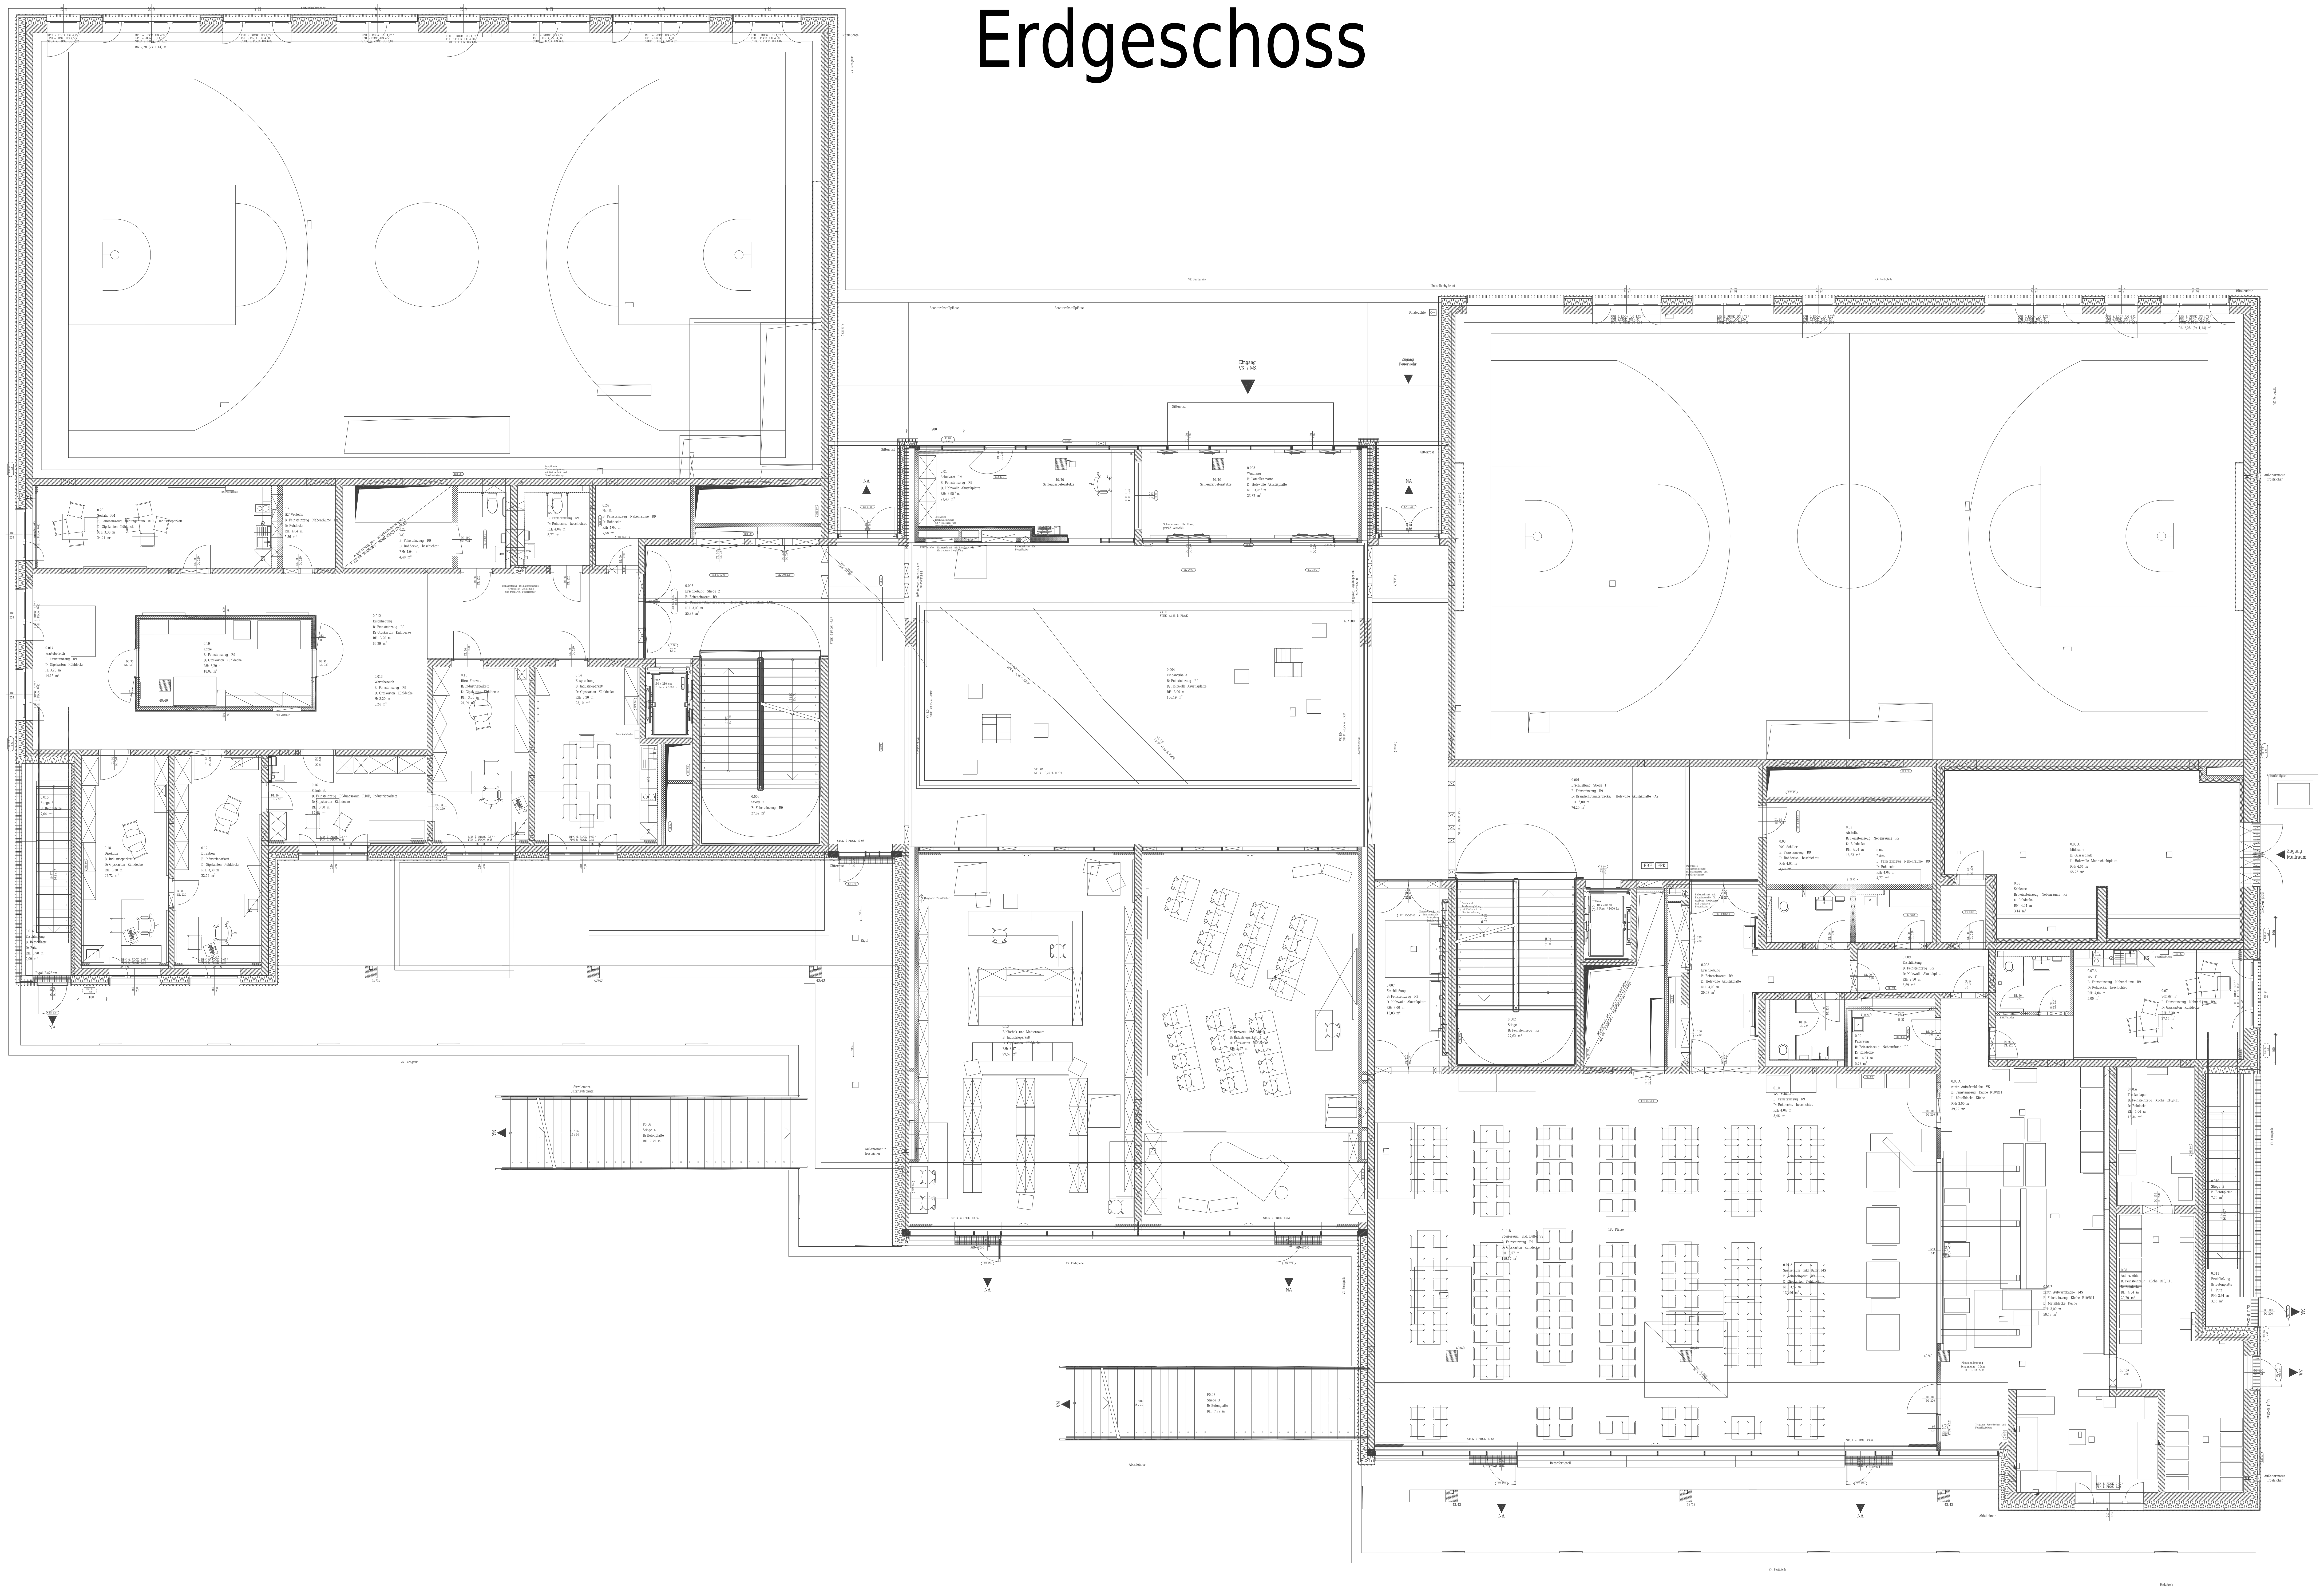
Unterflurhydrant
Blitzleuchte
VK Fertigteile
RPH ü. RDOK UG 4,72
FPH ü.FBOK UG 4,50
STUK ü. FBOK UG 6,82
RA 2,28 (2x 1,14) m²
0.20
Sozialr. FM
B: Feinsteinzeug Bildungsraum R10B; Industrieparkett
D: Gipskarton Kühldecke
RH: 3,30 m
24,21 m²
0.21
IKT Verteiler
B: Feinsteinzeug Nebenräume R9
D: Rohdecke
RH: 4,04 m
5,36 m²
0.22
WC
B: Feinsteinzeug R9
D: Rohdecke, beschichtet
RH: 4,04 m
4,40 m²
0.23
WC
B: Feinsteinzeug R9
D: Rohdecke, beschichtet
RH: 4,04 m
5,77 m²
0.24
Handl.
B: Feinsteinzeug Nebenräume R9
D: Rohdecke
RH: 4,04 m
7,58 m²
0.014
Wartebereich
B: Feinsteinzeug R9
D: Gipskarton Kühldecke
H: 3,20 m
14,15 m²
0.19
Kopie
B: Feinsteinzeug R9
D: Gipskarton Kühldecke
RH: 3,20 m
18,02 m²
0.012
Erschließung
B: Feinsteinzeug R9
D: Gipskarton Kühldecke
RH: 3,20 m
66,29 m²
0.013
Wartebereich
B: Feinsteinzeug R9
D: Gipskarton Kühldecke
H: 3,20 m
6,24 m²
0.15
Büro Freizeit
B: Industrieparkett
D: Gipskarton Kühldecke
RH: 3,30 m
21,09 m²
0.14
Besprechung
B: Industrieparkett
D: Gipskarton Kühldecke
RH: 3,30 m
25,10 m²
0.005
Erschließung Stiege 2
B: Feinsteinzeug R9
D: Brandschutzunterdecke; Holzwolle Akustikplatte (A2)
RH: 3,00 m
55,87 m²
0.006
Stiege 2
B: Feinsteinzeug R9
27,62 m²
FWA
110 x 210 cm
13 Pers. / 1000 kg
0.015
Stiege 6
B: Betonplatte
7,04 m²
0.016
Erschließung
B: Betonplatte
D: Putz
RH: 3,90 m
2,09 m²
Rigol B=25cm
0.18
Direktion
B: Industrieparkett
D: Gipskarton Kühldecke
RH: 3,30 m
22,72 m²
0.17
Direktion
B: Industrieparkett
D: Gipskarton Kühldecke
RH: 3,30 m
22,72 m²
0.16
Schularzt
B: Feinsteinzeug Bildungsraum R10B; Industrieparkett
D: Gipskarton Kühldecke
RH: 3,30 m
17,85 m²
NA
43/43
Rigol
Scooterabstellplätze
Eingang
VS / MS
Zugang
Feuerwehr
Gitterrost
0.01
Schulwart FM
B: Feinsteinzeug R9
D: Holzwolle Akustikplatte
RH: 3,95 m
21,43 m²
40/40
Schleuderbetonstütze
0.003
Windfang
B: Lamellenmatte
D: Holzwolle Akustikplatte
RH: 3,95 m
23,32 m²
Schiebetüren Fluchtweg gemäß Aufzug
0.004
Eingangshalle
B: Feinsteinzeug R9
D: Holzwolle Akustikplatte
RH: 3,00 m
166,19 m²
VK RD
STUK +3,25 ü. RDOK
40/100
0.13
Bibliothek und Medienraum
B: Industrieparkett
D: Gipskarton Kühldecke
RH: 3,57 m
99,57 m²
0.12
Mehrzweck und Musik
B: Industrieparkett
D: Gipskarton Kühldecke
RH: 3,57 m
99,57 m²
STUK ü. FBOK +3,64
Außenarmatur frostsicher
Sitzelement
Unterlaufschutz
F0.06
Stiege 4
B: Betonplatte
RH: 7,79 m
F0.07
Stiege 3
B: Betonplatte
RH: 7,79 m
Abfalleimer
0.007
Erschließung
B: Feinsteinzeug R9
D: Holzwolle Akustikplatte
RH: 3,00 m
15,03 m²
0.001
Erschließung Stiege 1
B: Feinsteinzeug R9
D: Brandschutzunterdecke; Holzwolle Akustikplatte (A2)
RH: 3,00 m
76,20 m²
FBF
FPK
0.002
Stiege 1
B: Feinsteinzeug R9
27,62 m²
0.02
Abstellr.
B: Feinsteinzeug Nebenräume R9
D: Rohdecke
RH: 4,04 m
16,53 m²
0.03
WC Schüler
B: Feinsteinzeug R9
D: Rohdecke, beschichtet
RH: 4,04 m
4,40 m²
0.04
Putzr.
B: Feinsteinzeug Nebenräume R9
D: Rohdecke
RH: 4,04 m
4,77 m²
0.05.A
Müllraum
B: Gussasphalt
D: Holzwolle Mehrschichtplatte
RH: 4,04 m
55,26 m²
0.05
Schleuse
B: Feinsteinzeug Nebenräume R9
D: Rohdecke
RH: 4,04 m
3,14 m²
Zugang
Müllraum
Außenarmatur frostsicher
0.008
Erschließung
B: Feinsteinzeug R9
D: Holzwolle Akustikplatte
RH: 3,00 m
20,08 m²
0.009
Erschließung
B: Feinsteinzeug R9
D: Holzwolle Akustikplatte
RH: 2,50 m
6,89 m²
0.09
Putzraum
B: Feinsteinzeug Nebenräume R9
D: Rohdecke
RH: 4,04 m
5,73 m²
0.07.A
WC P
B: Feinsteinzeug Nebenräume R9
D: Rohdecke, beschichtet
RH: 4,04 m
5,00 m²
0.07
Sozialr. P
B: Feinsteinzeug Nebenräume R9
D: Gipskarton Kühldecke
RH: 3,30 m
27,15 m²
0.10
WC Schülerin
B: Feinsteinzeug R9
D: Rohdecke, beschichtet
RH: 4,04 m
5,46 m²
0.06.A
zentr. Aufwärmküche VS
B: Feinsteinzeug Küche R10/R11
D: Metalldecke Küche
RH: 3,00 m
39,92 m²
0.08.A
Trockenlager
B: Feinsteinzeug Küche R10/R11
D: Rohdecke
RH: 4,04 m
13,34 m²
0.010
Stiege 5
B: Betonplatte
7,70 m²
0.11.B
Speiseraum inkl. Buffet VS
B: Feinsteinzeug R9
D: Gipskarton Kühldecke
RH: 3,57 m
119,17 m²
180 Plätze
0.11.A
Speiseraum inkl. Buffet MS
B: Feinsteinzeug R9
D: Gipskarton Kühldecke
RH: 3,57 m
134,96 m²
0.08
Anl. u. Abh.
B: Feinsteinzeug Küche R10/R11
D: Rohdecke
RH: 4,04 m
29,70 m²
0.06.B
zentr. Aufwärmküche MS
B: Feinsteinzeug Küche R10/R11
D: Metalldecke Küche
RH: 3,00 m
50,43 m²
0.011
Erschließung
B: Betonplatte
D: Putz
RH: 3,91 m
3,56 m²
Flankendämmung
Schaumglas 10cm
Betonfertigteil
Holzdeck

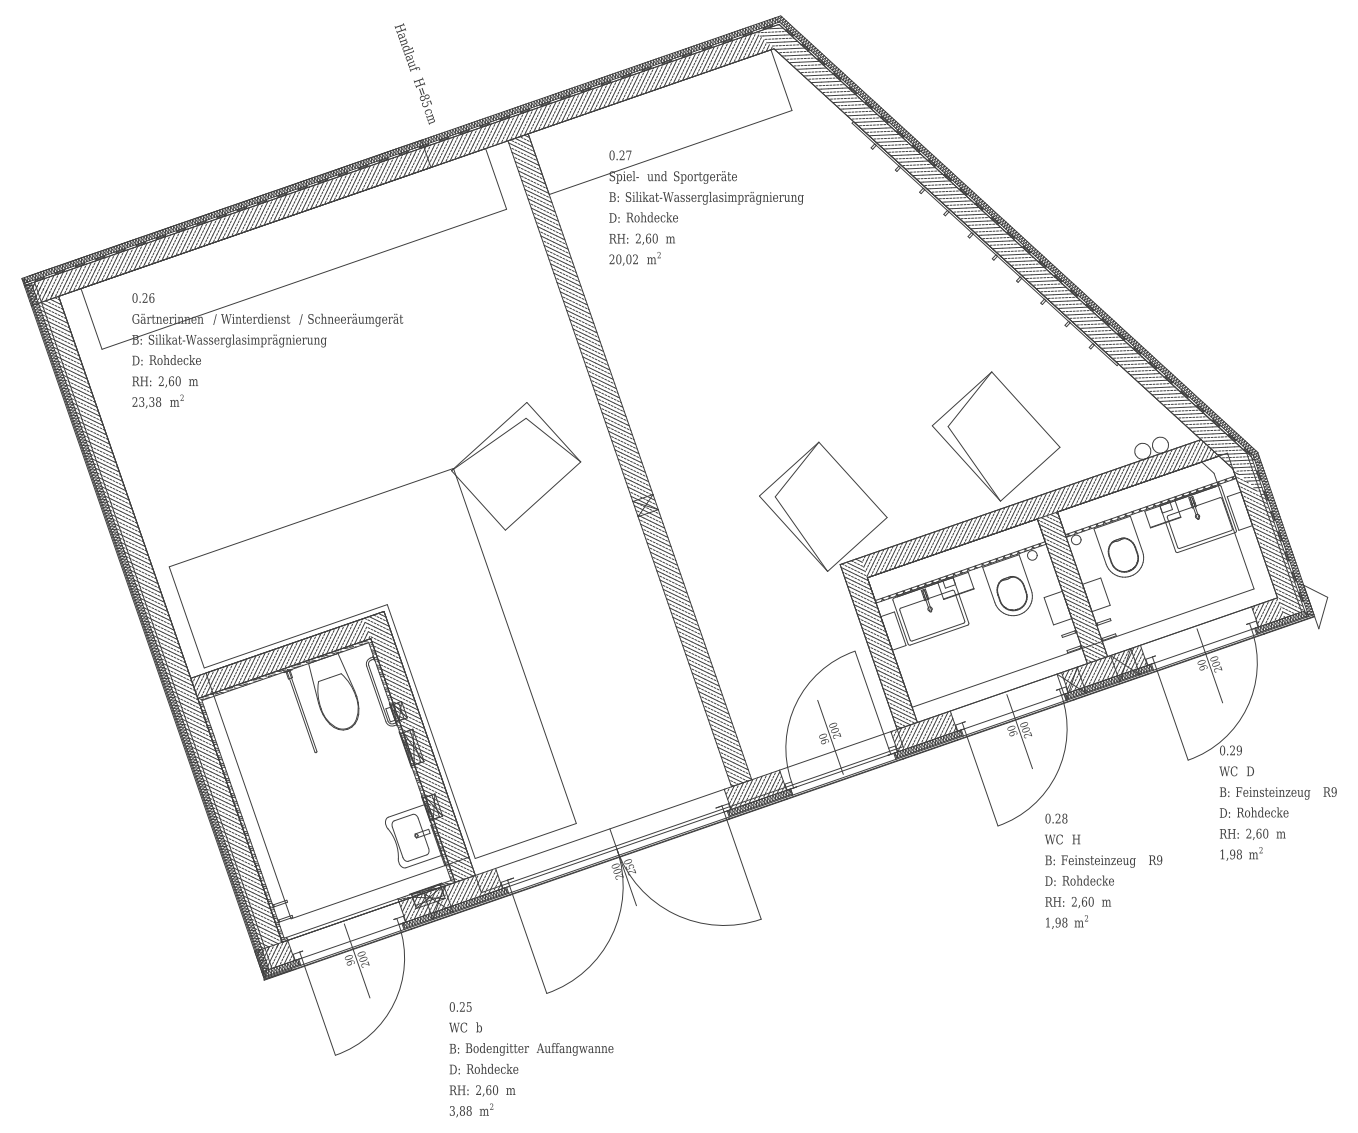
0.27
Spiel- und Sportgeräte
B: Silikat-Wasserglasimprägnierung
D: Rohdecke
RH: 2,60 m
20,02 m²
0.26
Gärtnereimen / Winterdienst / Schneeräumgerät
B: Silikat-Wasserglasimprägnierung
D: Rohdecke
RH: 2,60 m
23,38 m²
0.25
WC b
B: Bodengitter Auffangwanne
D: Rohdecke
RH: 2,60 m
3,88 m²
0.28
WC H
B: Feinsteinzeug R9
D: Rohdecke
RH: 2,60 m
1,98 m²
0.29
WC D
B: Feinsteinzeug R9
D: Rohdecke
RH: 2,60 m
1,98 m²