

EG-01 | Originalausschnitt mit direkt zugeordneten Merkmalen

Außenkante

Rahmen umfasst die volle Wandbreite.

Innenkante


Rahmen zeigt Wand und innere Randlinie.

Wandecke

Rahmen umfasst den Eckanschluss.

Öffnung

Fenster unterbricht das Mauerstück.

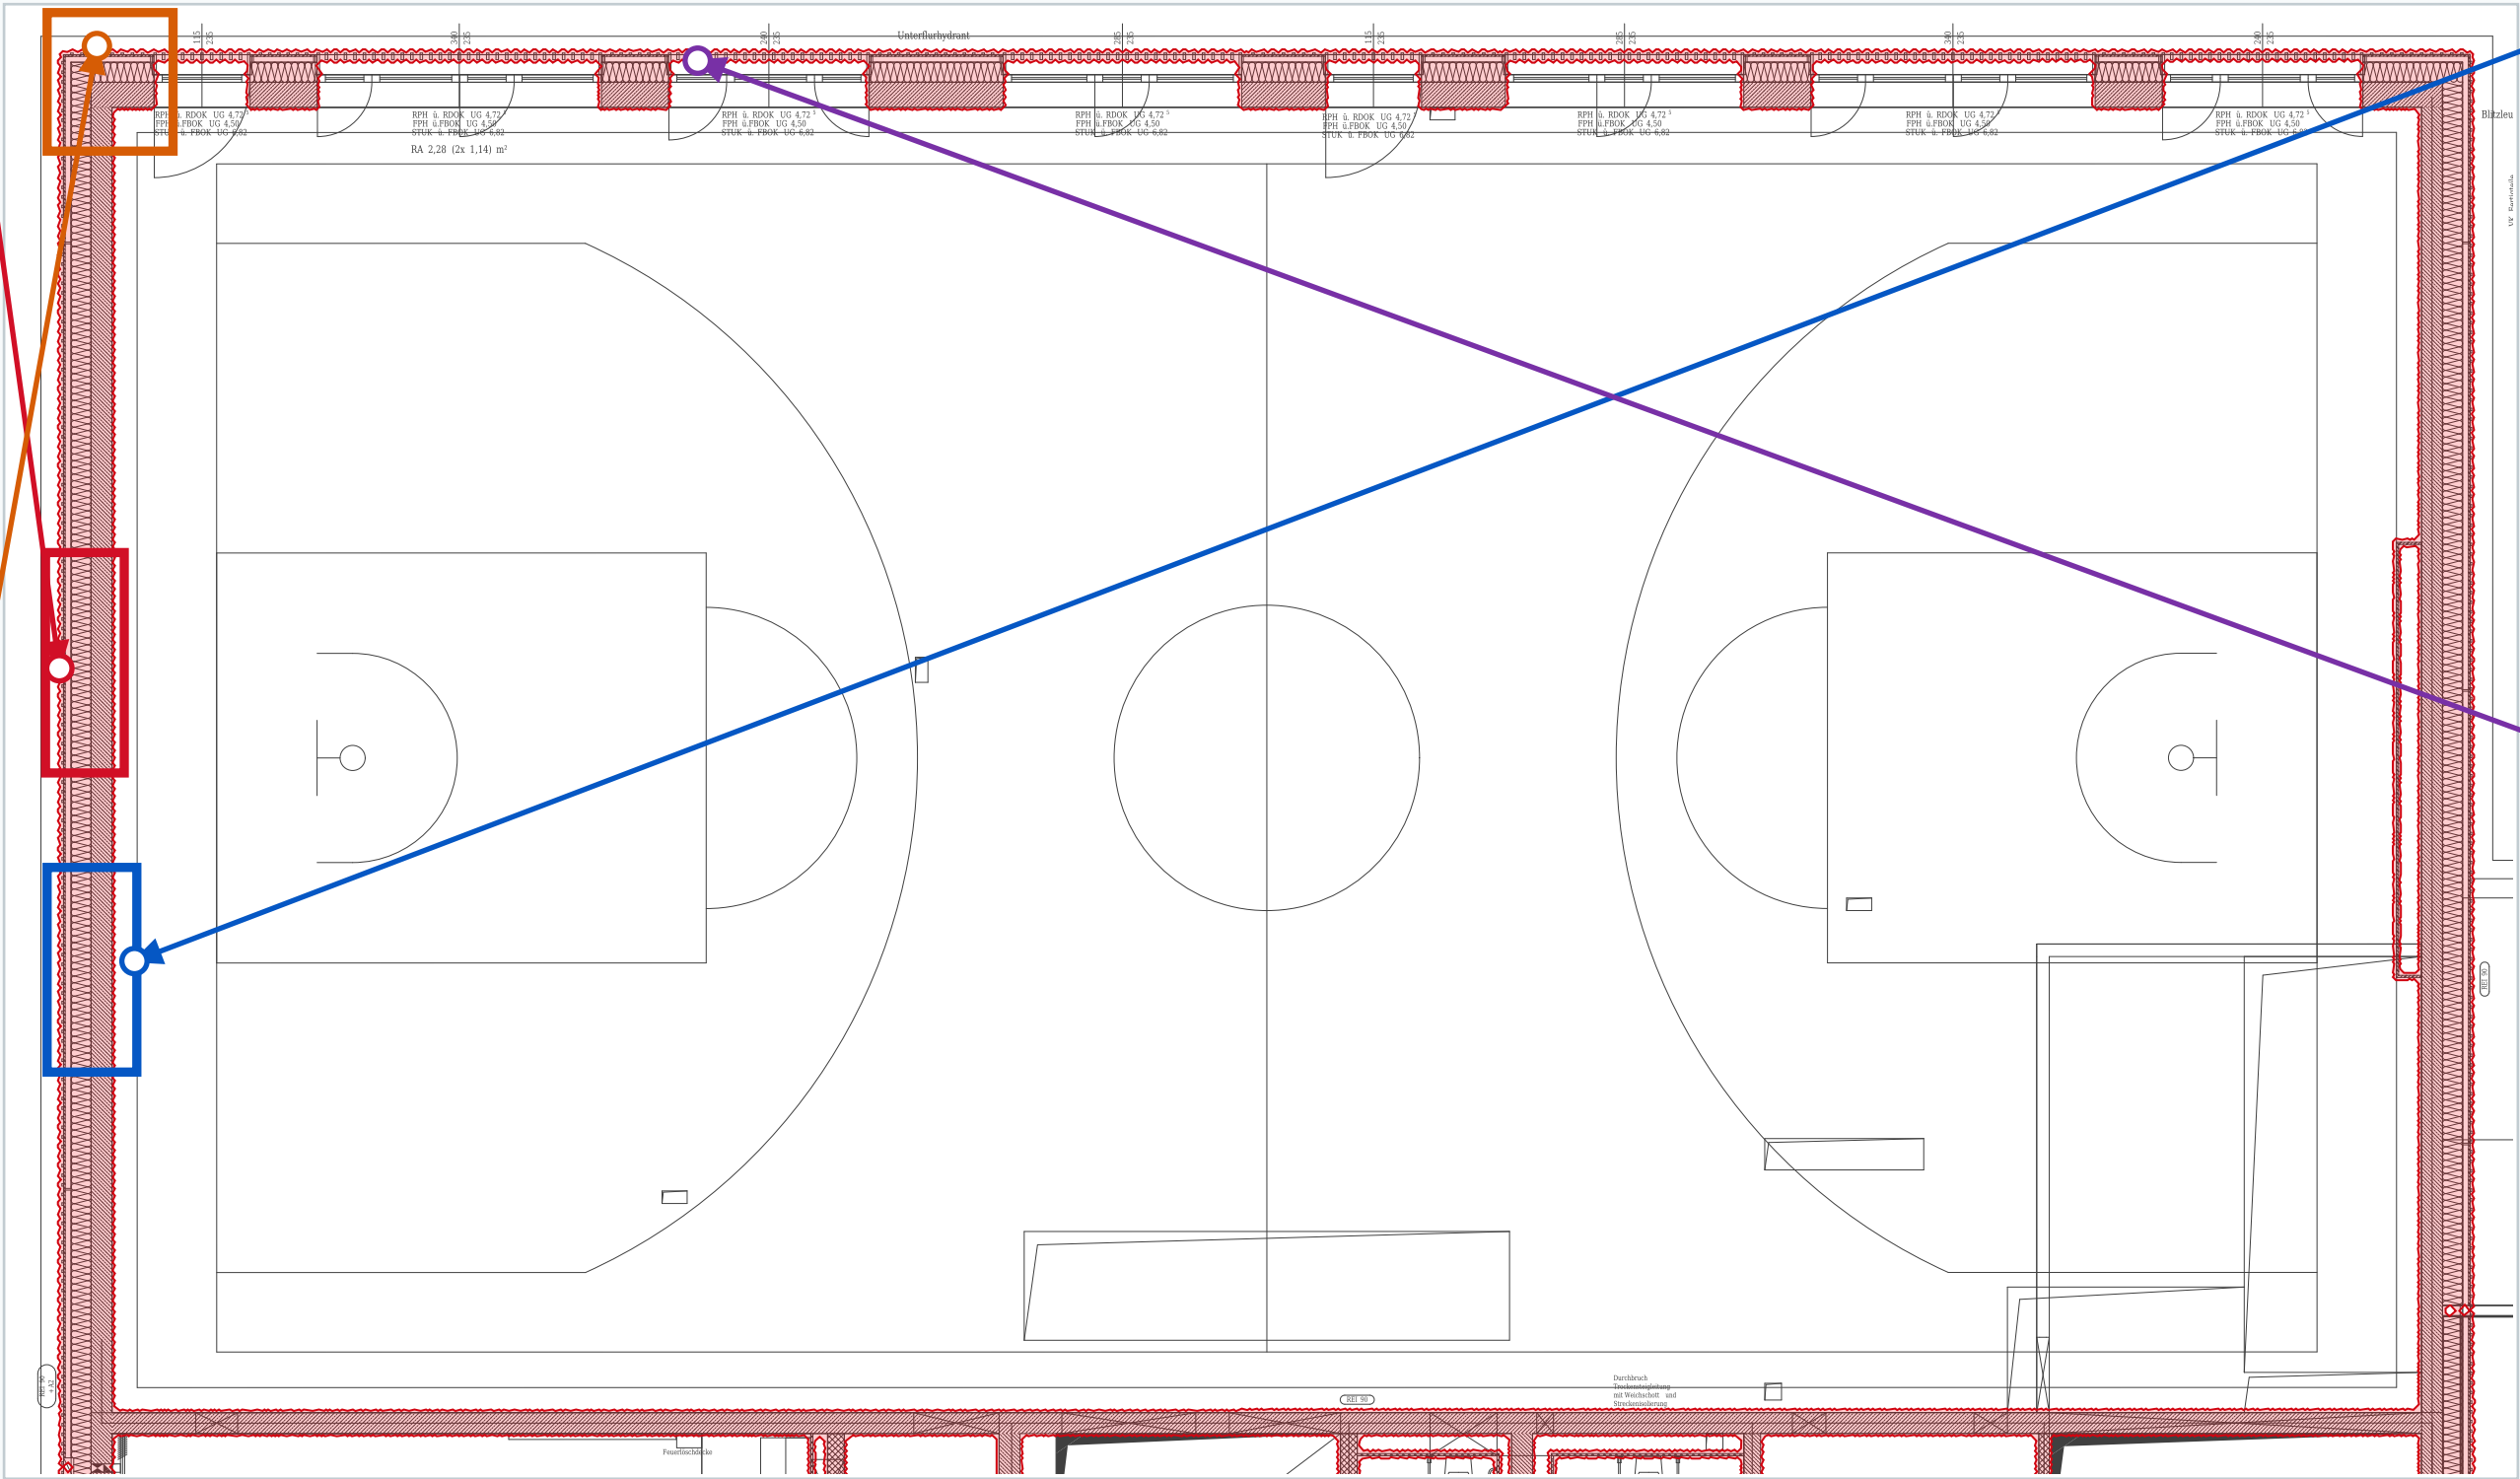

Rahmen: erklärter Bereich. Farblinien: Originalmerkmale. Pfeile: Zuordnung.

EG-02 | Originalausschnitt mit direkt zugeordneten Merkmalen

Außenmauer

Rahmen: massiver Gebäudeabschluss.

Türöffnung


Zwischen den Wandenden bleibt das Portal.

Zwei Wandkanten

Rahmen umfasst beide Kanten und Material.

Raumstempel

Nummer und
Raumtext; keine
bauliche Grenze.

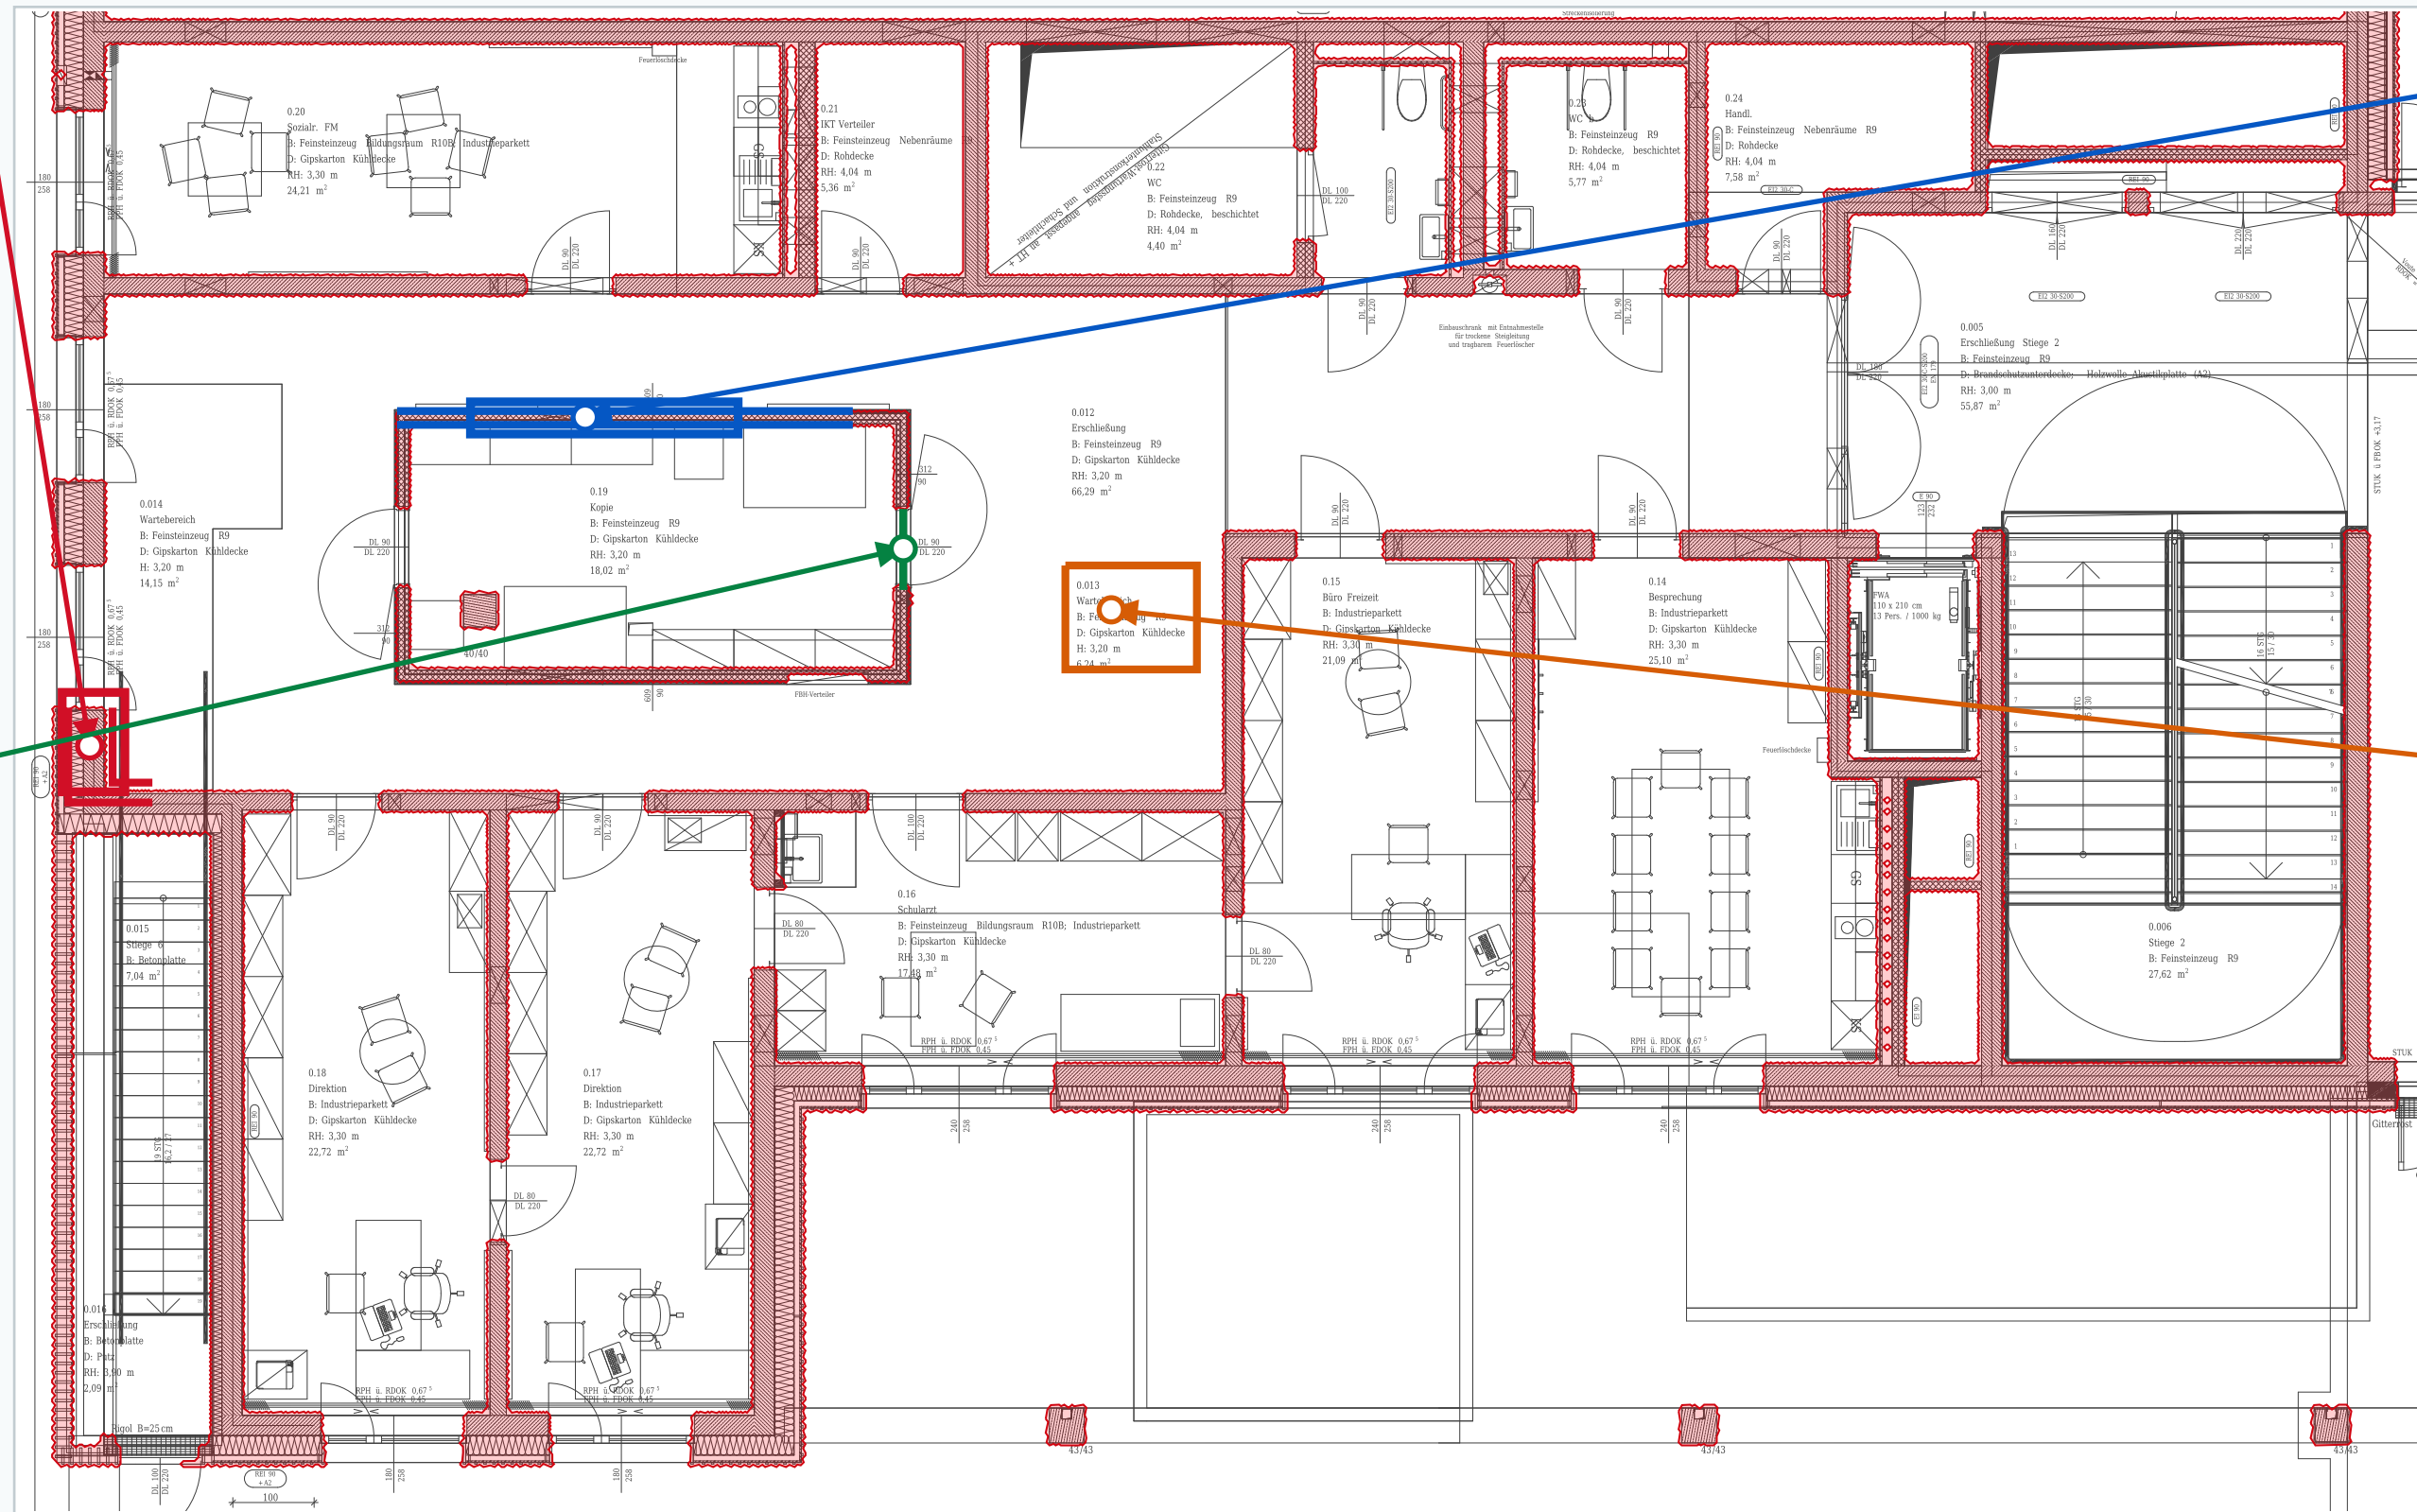

Rahmen: erklärter Bereich. Farblinien: Originalmerkmale. Pfeile: Zuordnung.

EG-03 | Originalausschnitt mit direkt zugeordneten Merkmalen

Außenwand

Rahmen:
Wandkörper
zwischen zwei
Kanten.

Trennwand


Rahmen:
Materialband
zwischen Räumen.

Massive Stütze

Orange umfasst
das schraffierte
Quadrat.

Deckenrand

Violett folgt der
Linie über dem
Boden.

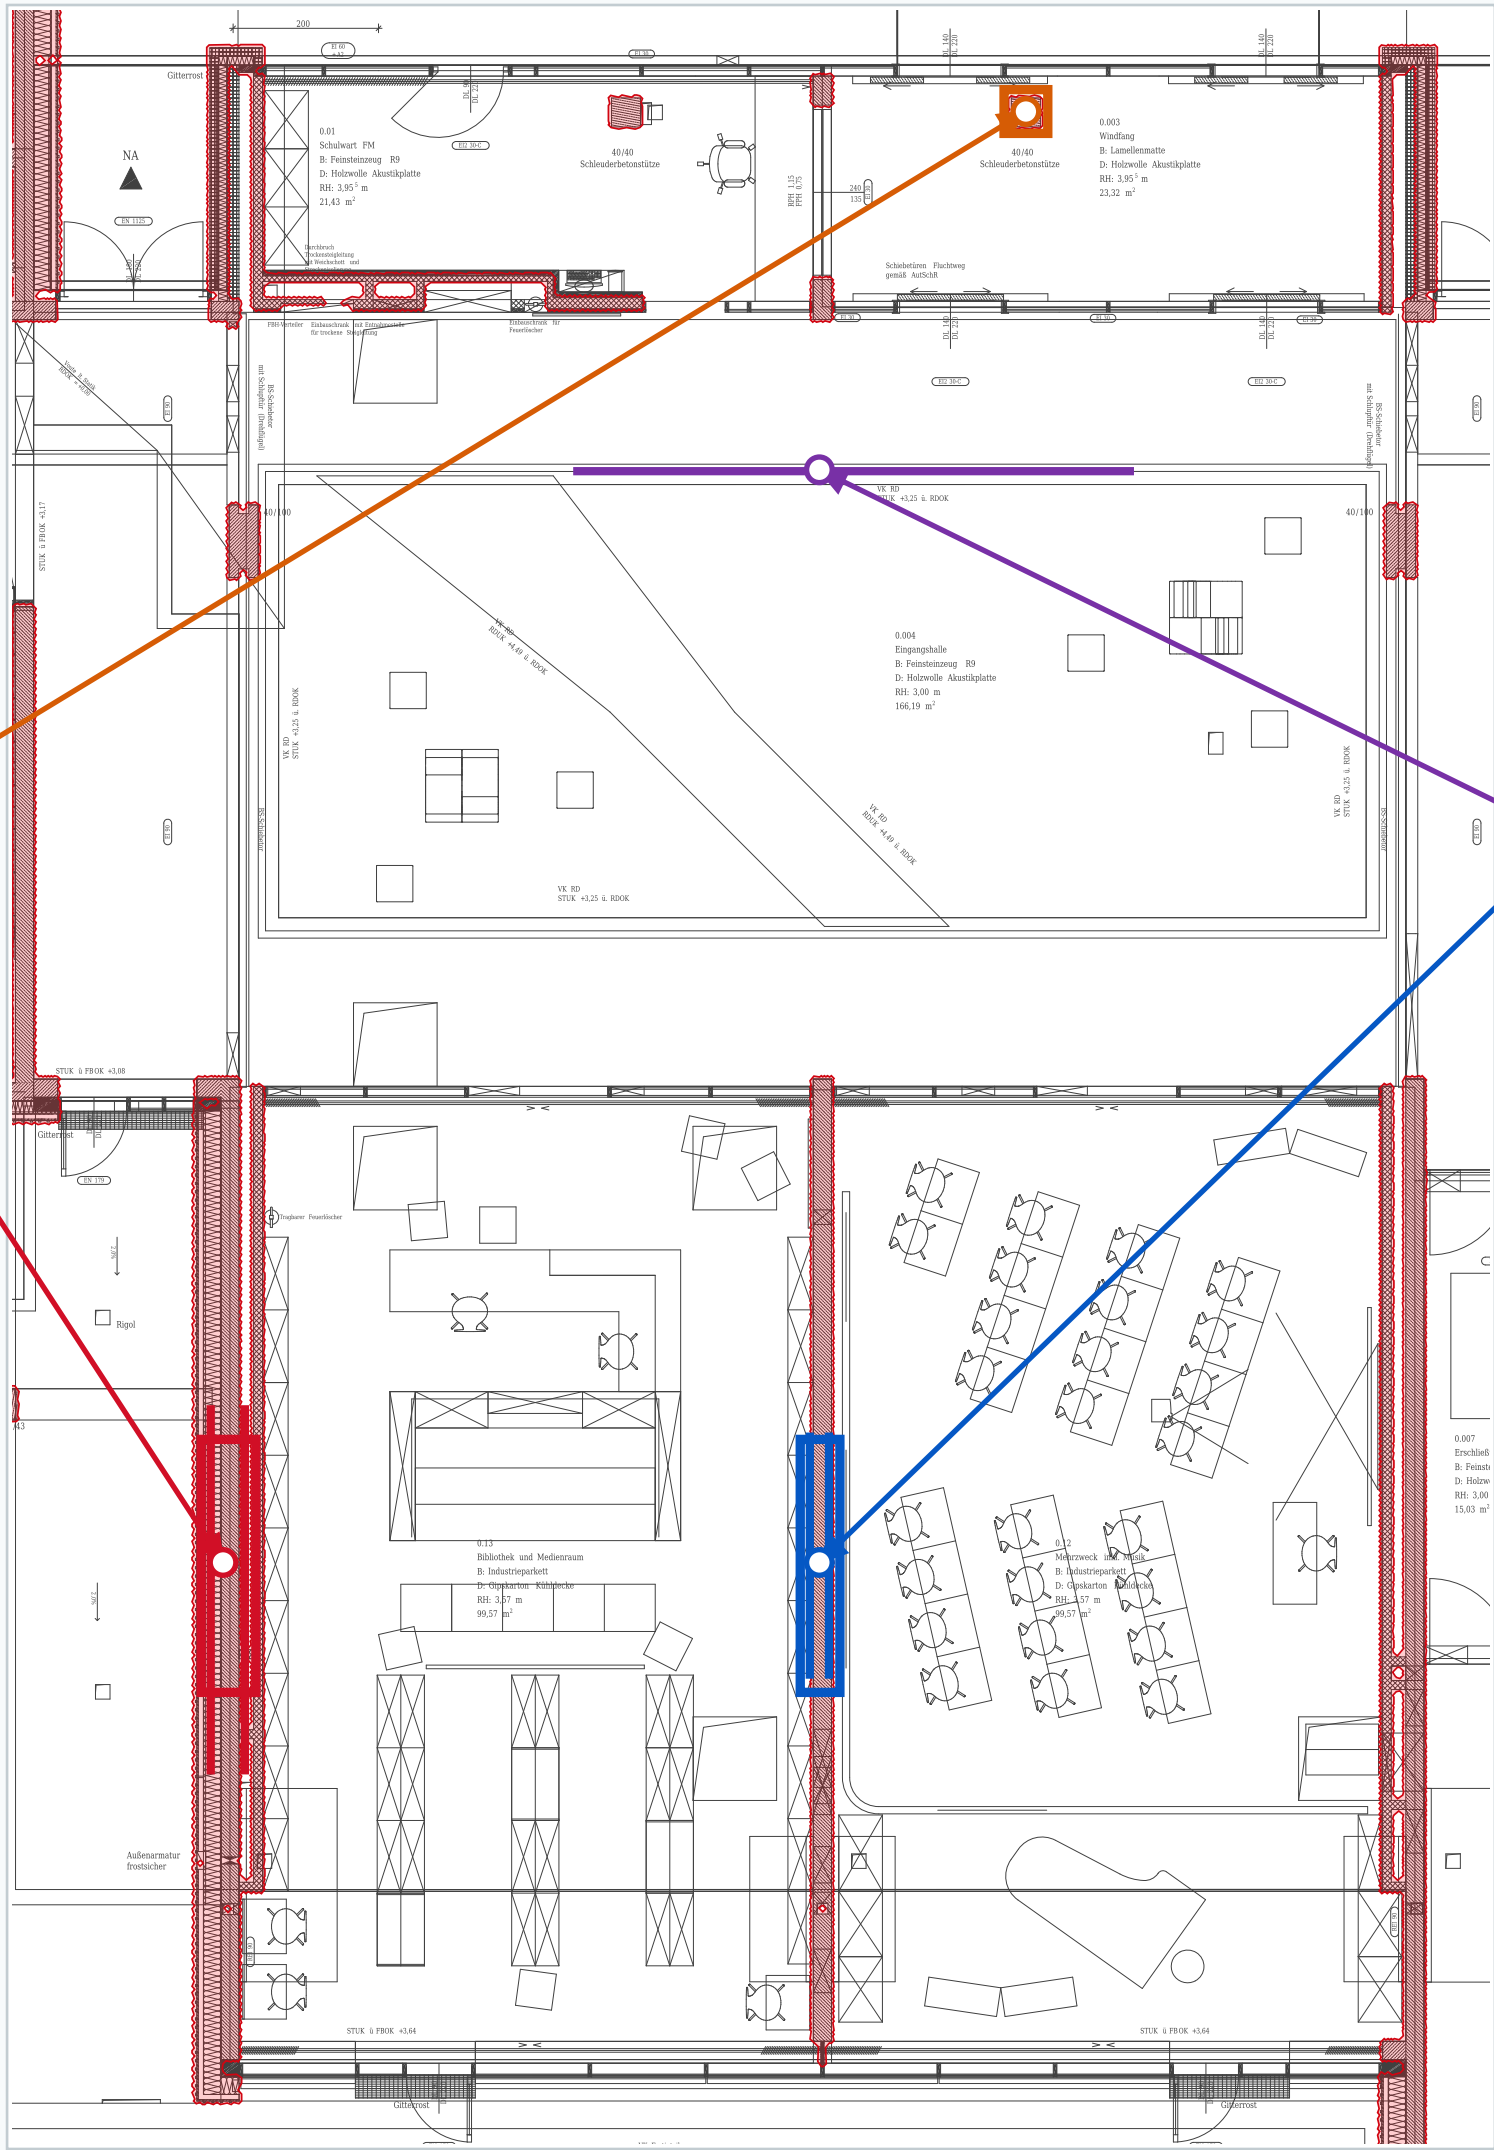

Rahmen: erklärter Bereich. Farblinien: Originalmerkmale. Pfeile: Zuordnung.

EG-04 | Originalausschnitt mit direkt zugeordneten Merkmalen

Hallenwand

Rahmen umfasst den schraffierten Wandkörper.

Schacht


Lift gesondert
lesen; keine
Gehfläche.

Innenwand

Rahmen umfasst
das feste
Wandstück.

Türöffnung

Bogen plus Blatt im
Wanddurchgang.

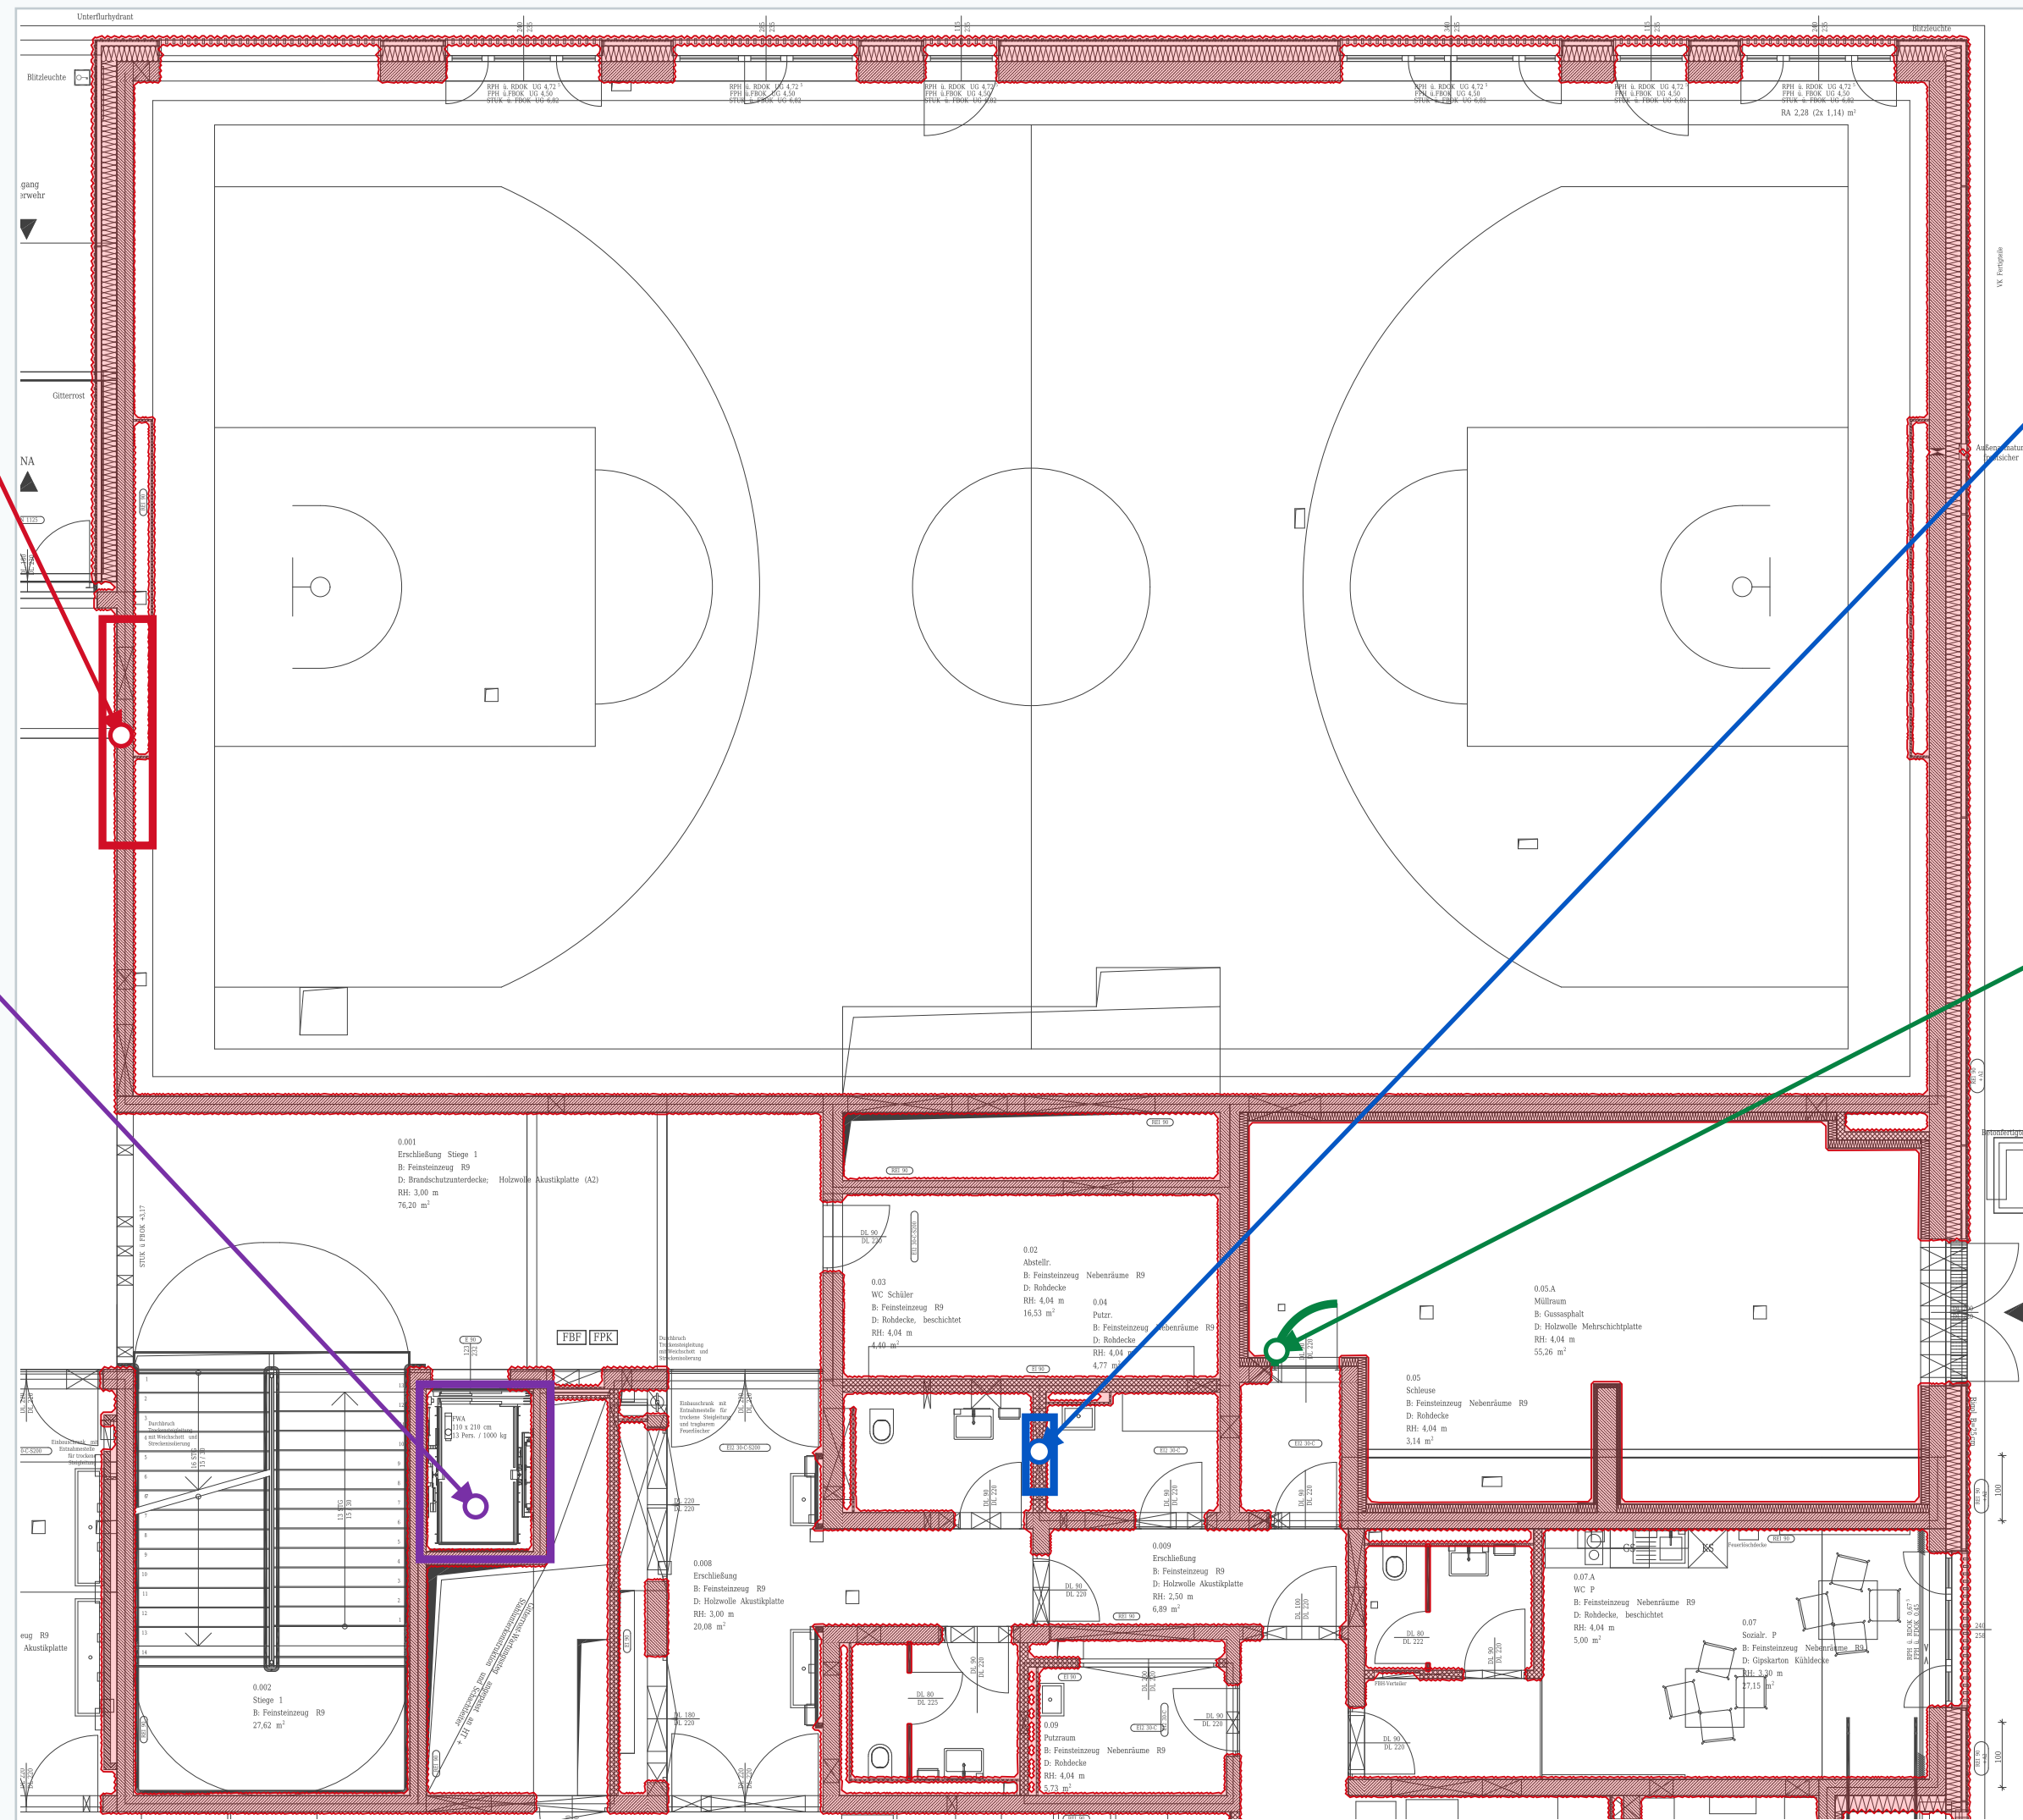

Rahmen: erklärter Bereich. Farblinien: Originalmerkmale. Pfeile: Zuordnung.

EG-05 | Originalausschnitt mit direkt zugeordneten Merkmalen

Breite Außenwand

Rahmen umfasst den ganzen Wandaufbau.

Massives Wandstück


Rahmen liegt um den schraffierten Abschnitt.

Türportal

Blatt und Bogen stehen in der Wandlücke.

Tischreihe

Orange umfasst die gesamte Tischreihe.

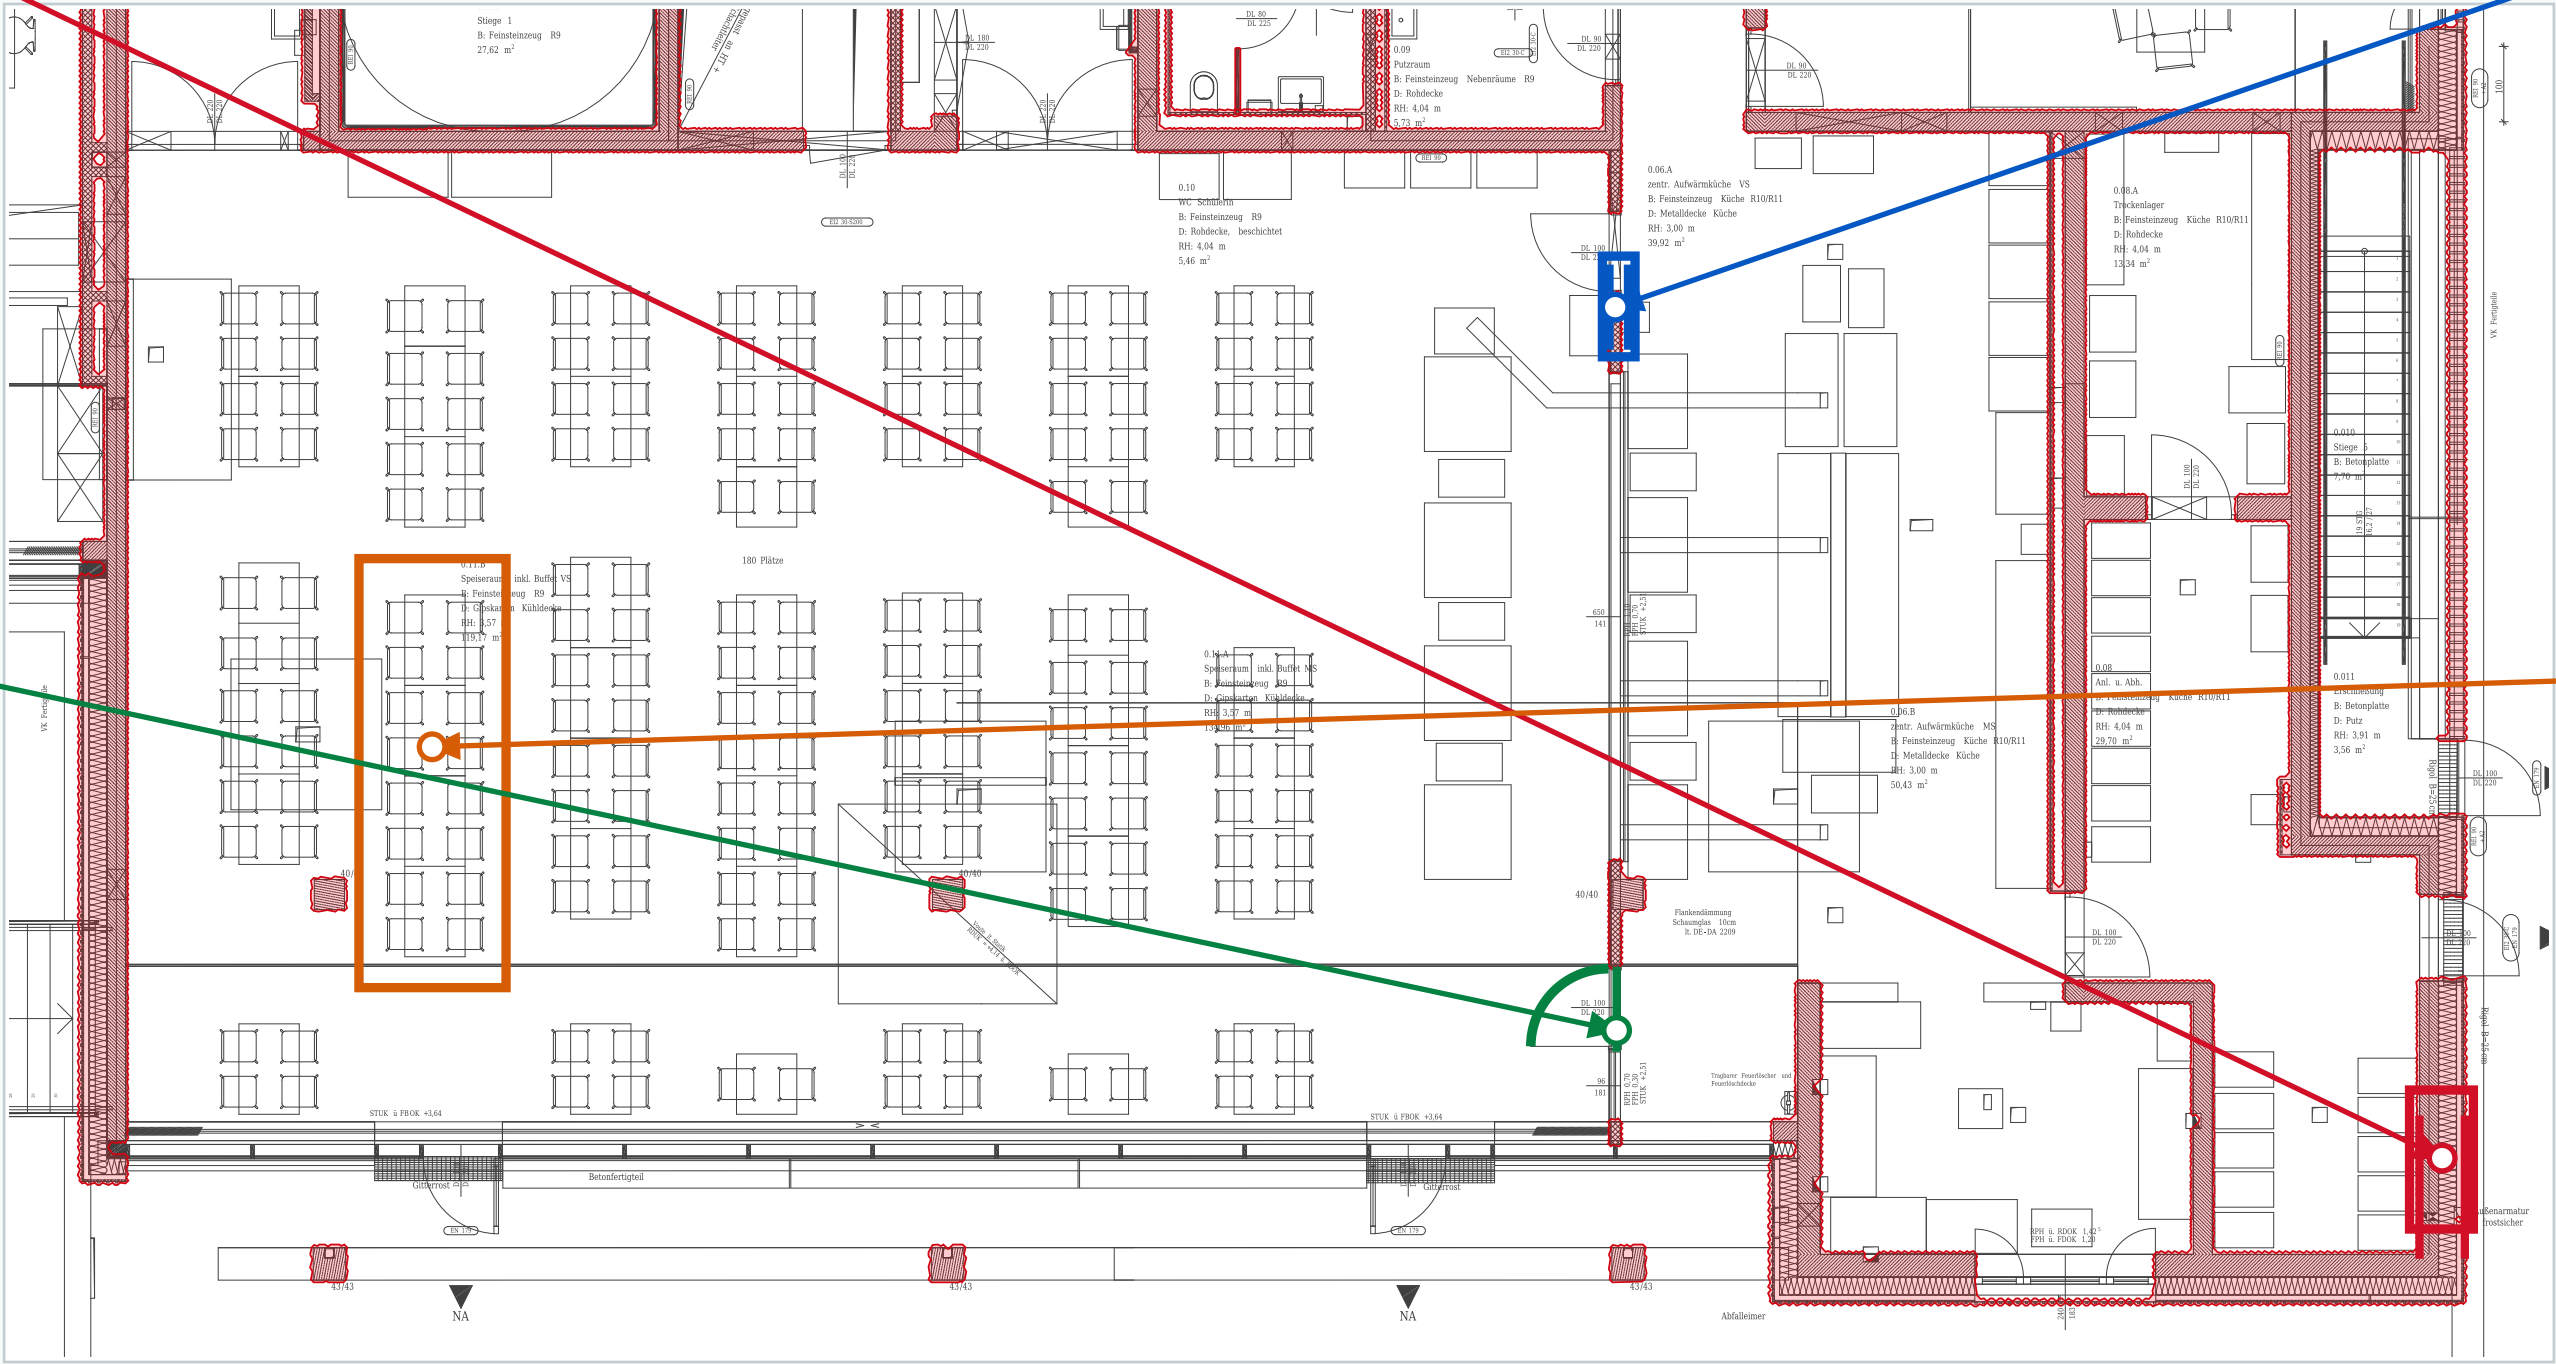

Rahmen: erklärter Bereich. Farblinien: Originalmerkmale. Pfeile: Zuordnung.

EG-06 | Originalausschnitt mit direkt zugeordneten Merkmalen

Schräge Außenwand

Gedrehter Rahmen folgt der Außenwand.

Innenwand


Rahmen umfasst das feste Wandstück.

Möbel

Orange: drei einzelne Gegenstände.

Einbauten

Violett: längliche Möbel an der Wand.

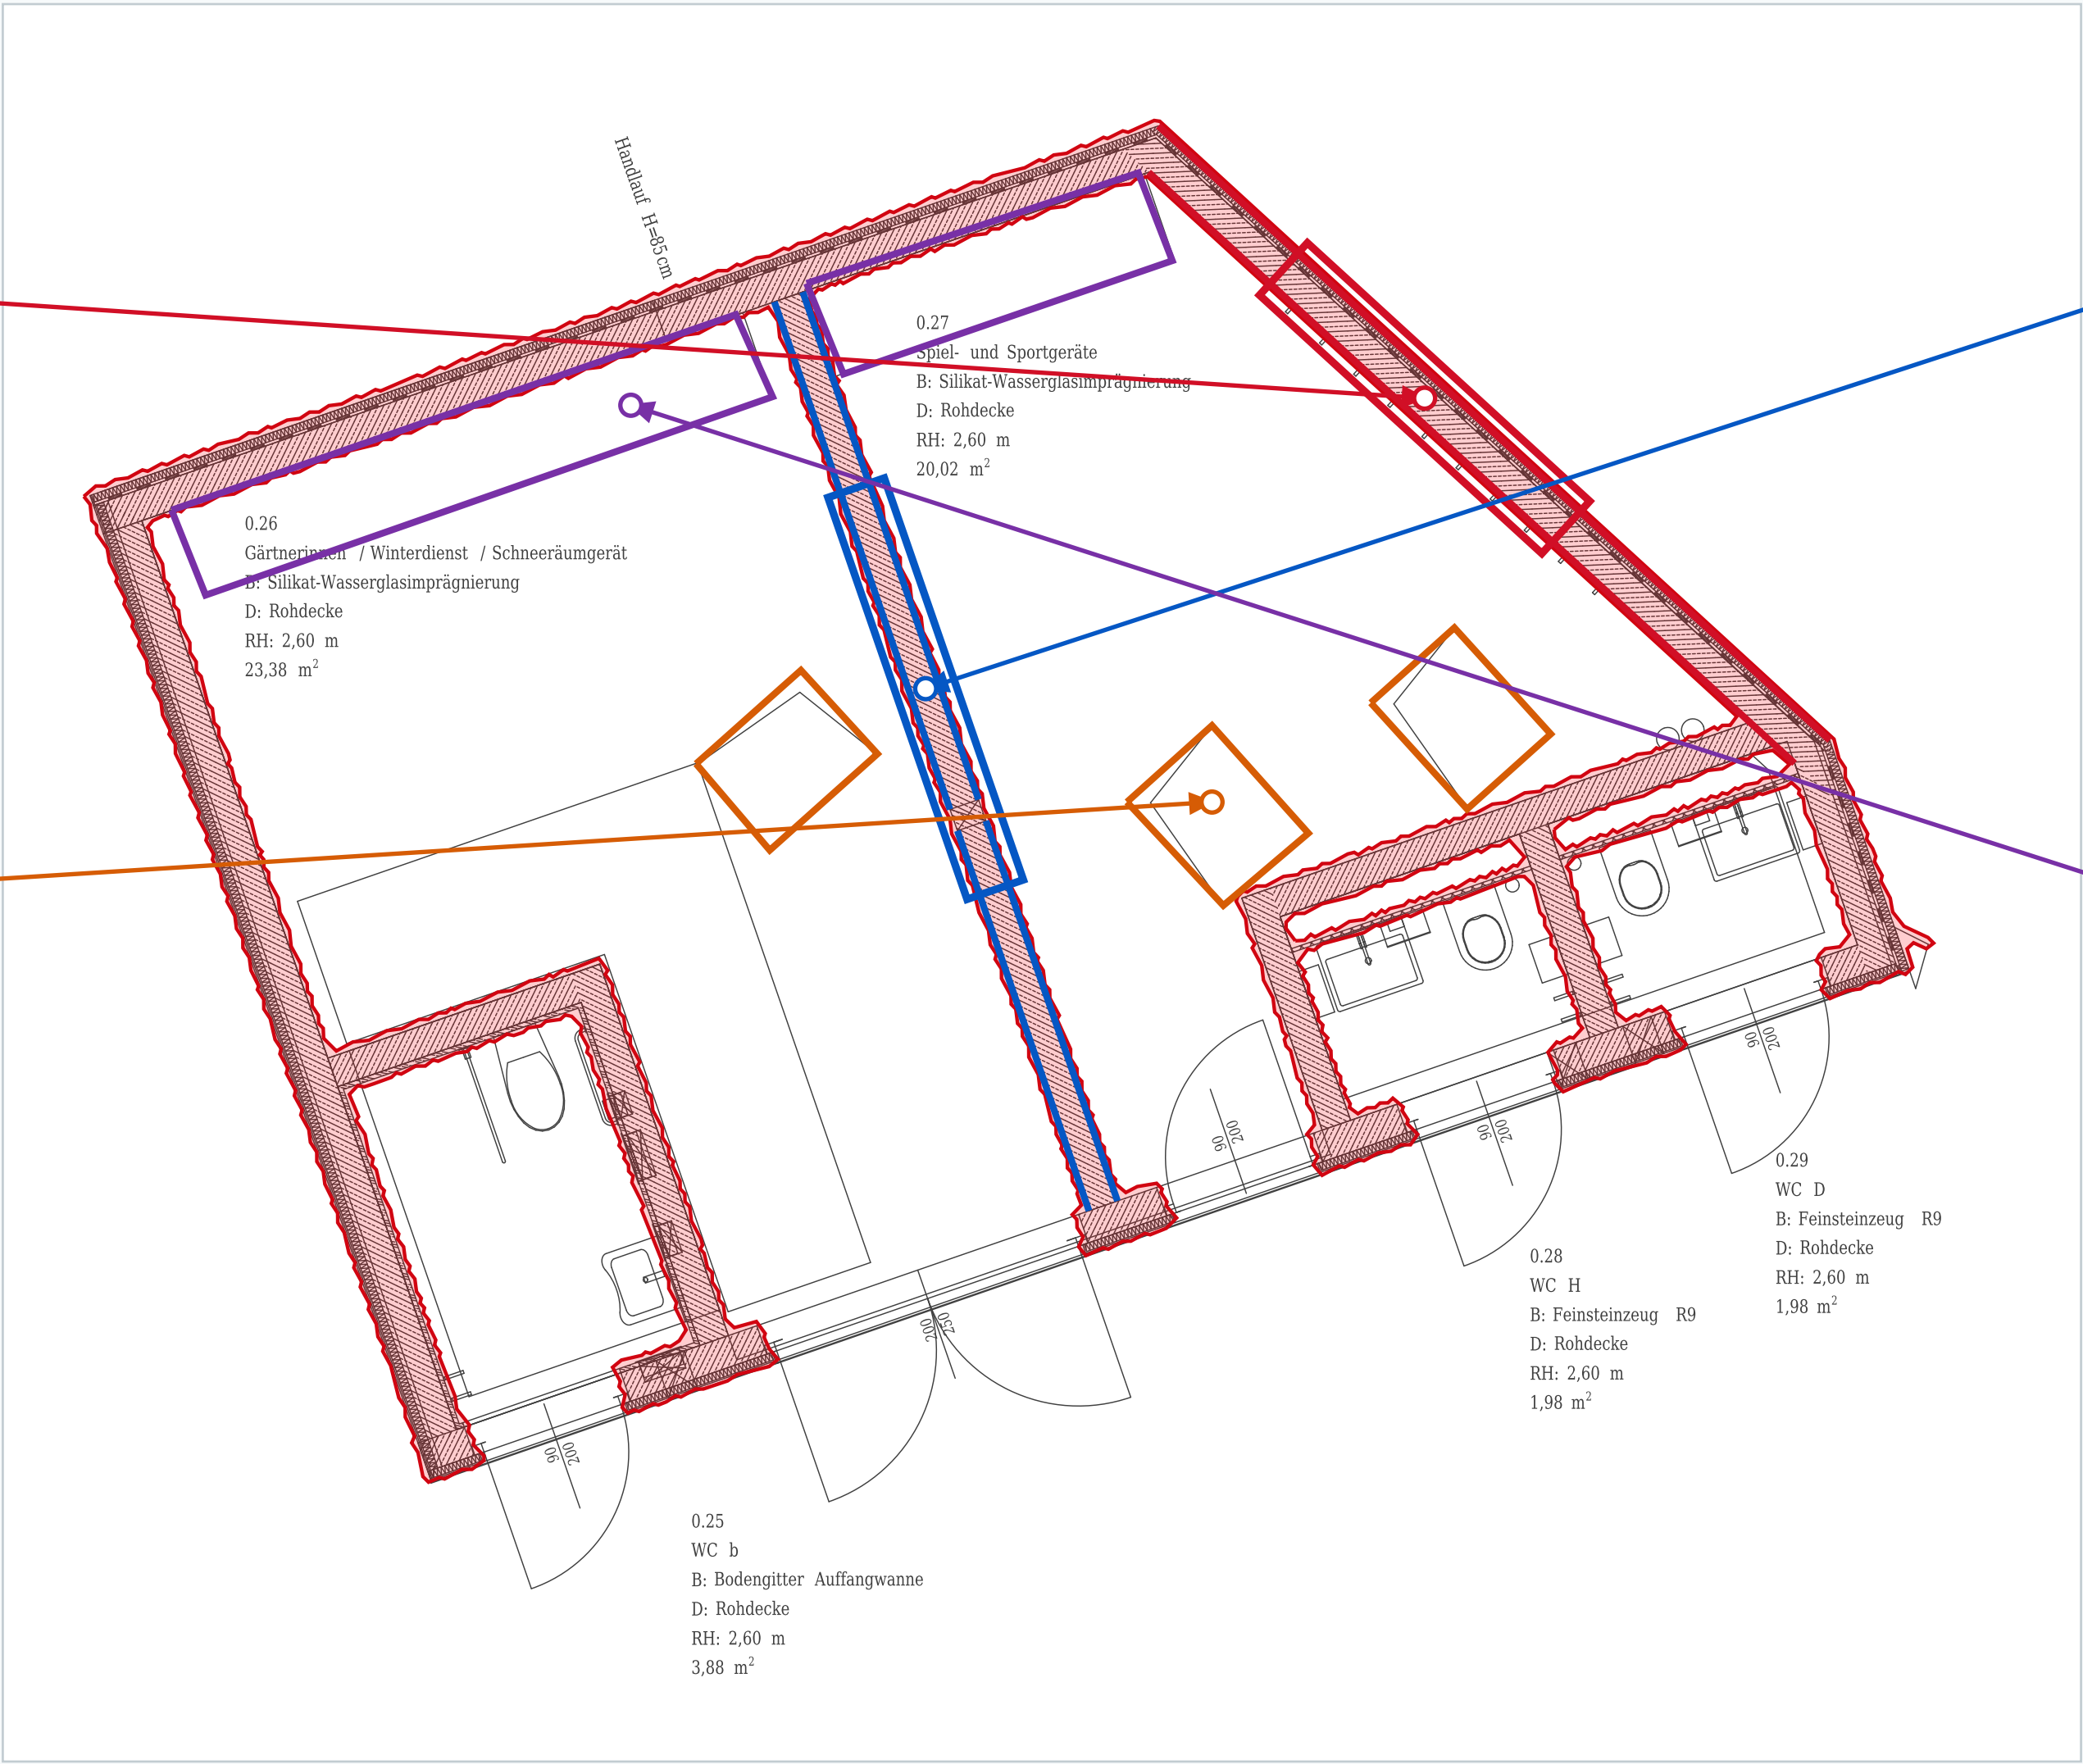

Rahmen: erklärter Bereich. Farblinien: Originalmerkmale. Pfeile: Zuordnung.

EG-07 | Originalausschnitt mit direkt zugeordneten Merkmalen

Wandkern

Rot umfasst die diagonale Schraffur.

Raumseite


Blau folgt der inneren Wandkante.

Dämmlage

Orange umfasst die Schlaufenstruktur.

Türöffnung

Grün liegt zwischen den Wandenden.

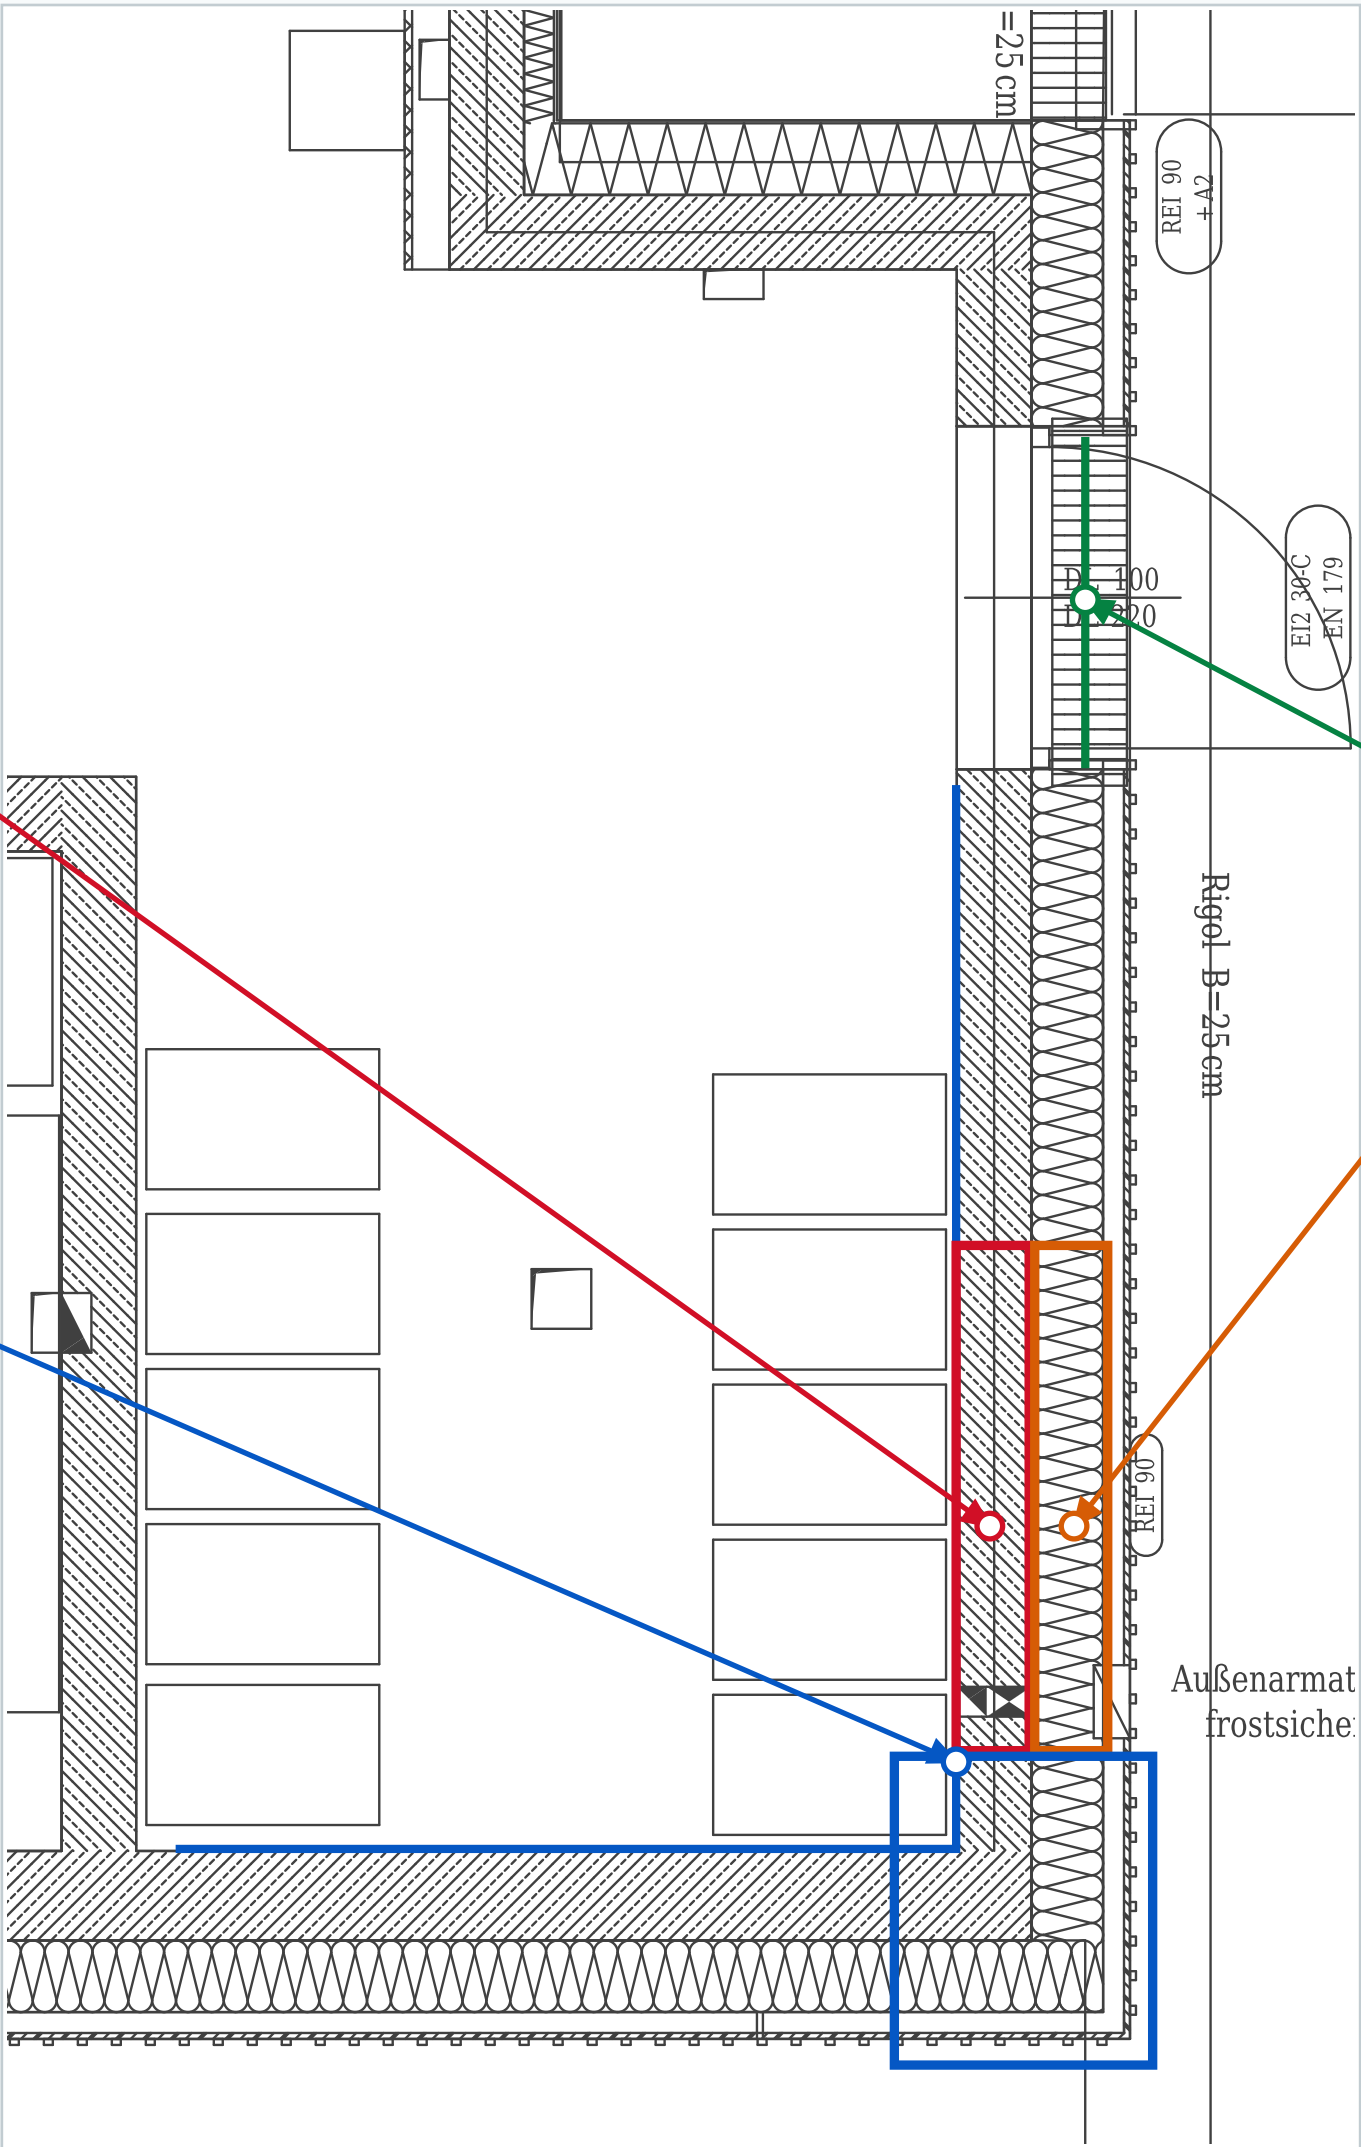

Rahmen: erklärter Bereich. Farblinien: Originalmerkmale. Pfeile: Zuordnung.

EG-08 | Originalausschnitt mit direkt zugeordneten Merkmalen

Dünne
Trennwand

Rahmen zeigt das
untere schmale
Wandstück.

Türblatt


Gerade Linie am
Bandpunkt.

Oberes
Wandstück

Rahmen zeigt das
obere schmale
Wandstück.

Schwenkbogen

Orange folgt dem
Bogen des
Türblatts.

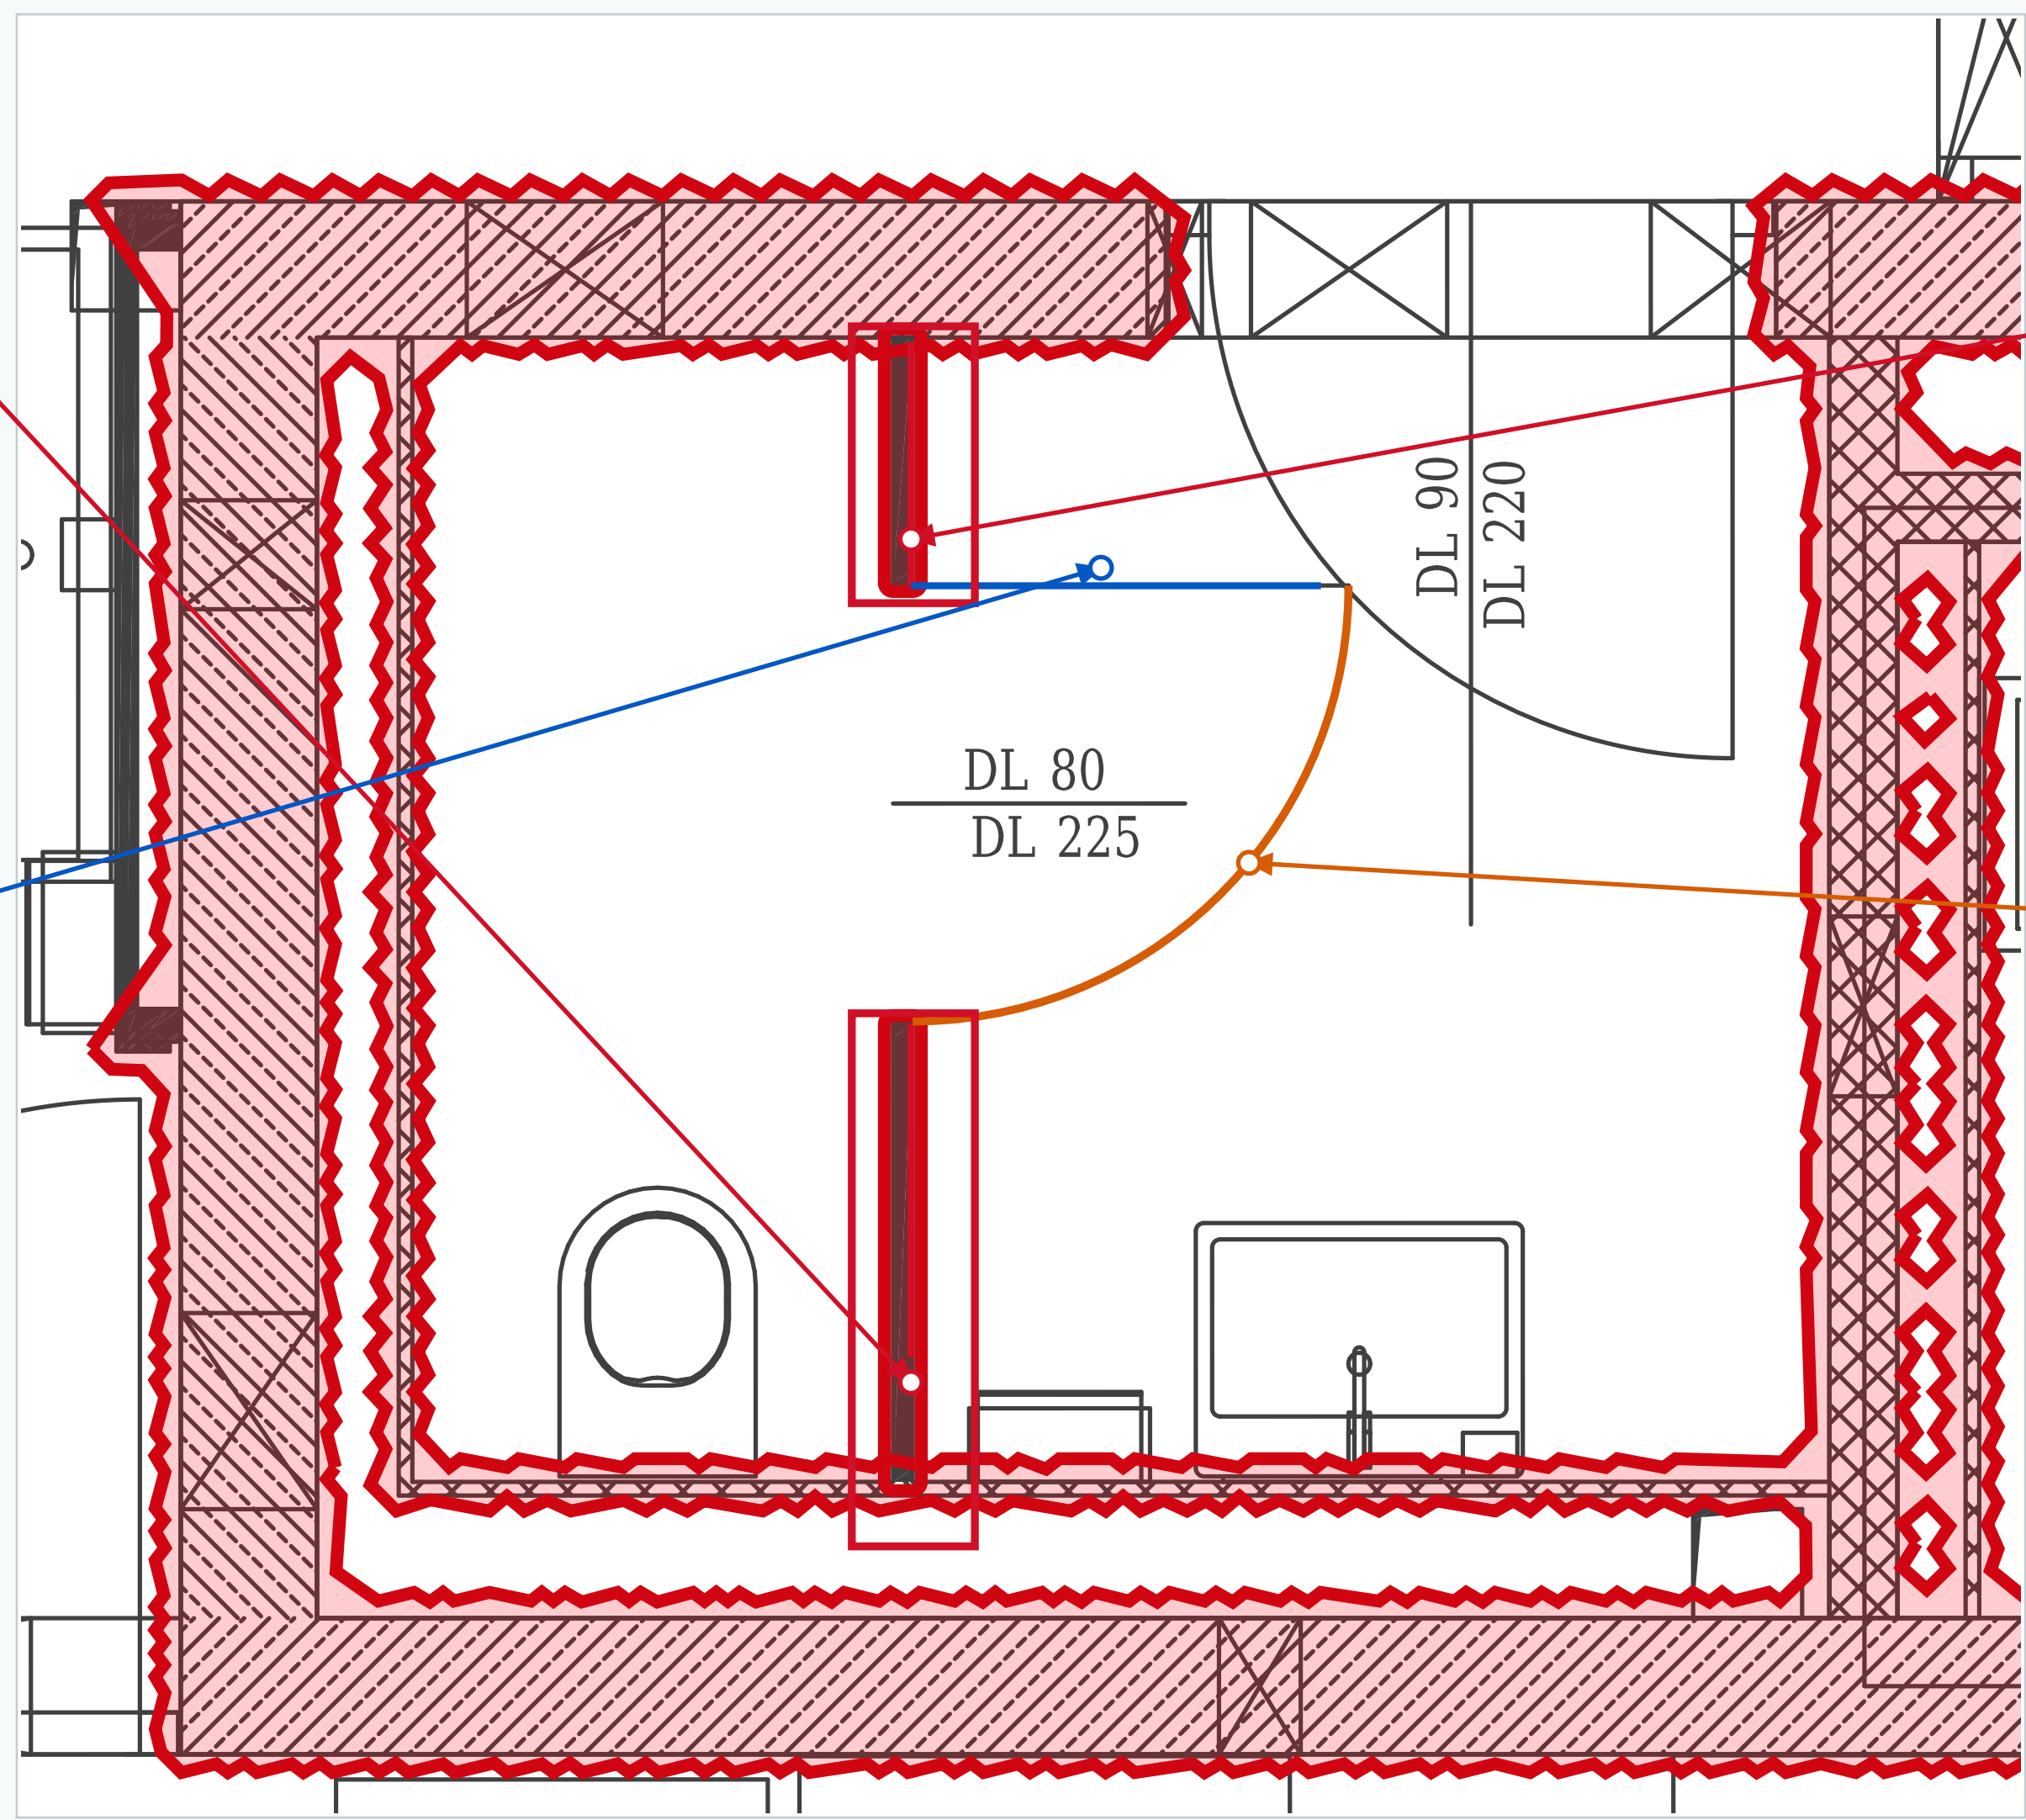

Rahmen: erklärter Bereich. Farblinien: Originalmerkmale. Pfeile: Zuordnung.

EG-09 | Originalausschnitt mit direkt zugeordneten Merkmalen

Türblatt offen

Blaue Gerade steht am Bandpunkt.

Geschlossen

Violett gestrichelt: gedachte Blattlage.

Bandpunkt

Hier dreht das Türblatt.

Öffnungsbogen


Orange Kurve zeigt den Schwenkweg.

Durchgang

Zwischen beiden Laibungen.

DL 90 / 220

Lichte Breite / Höhe laut Beschriftung.

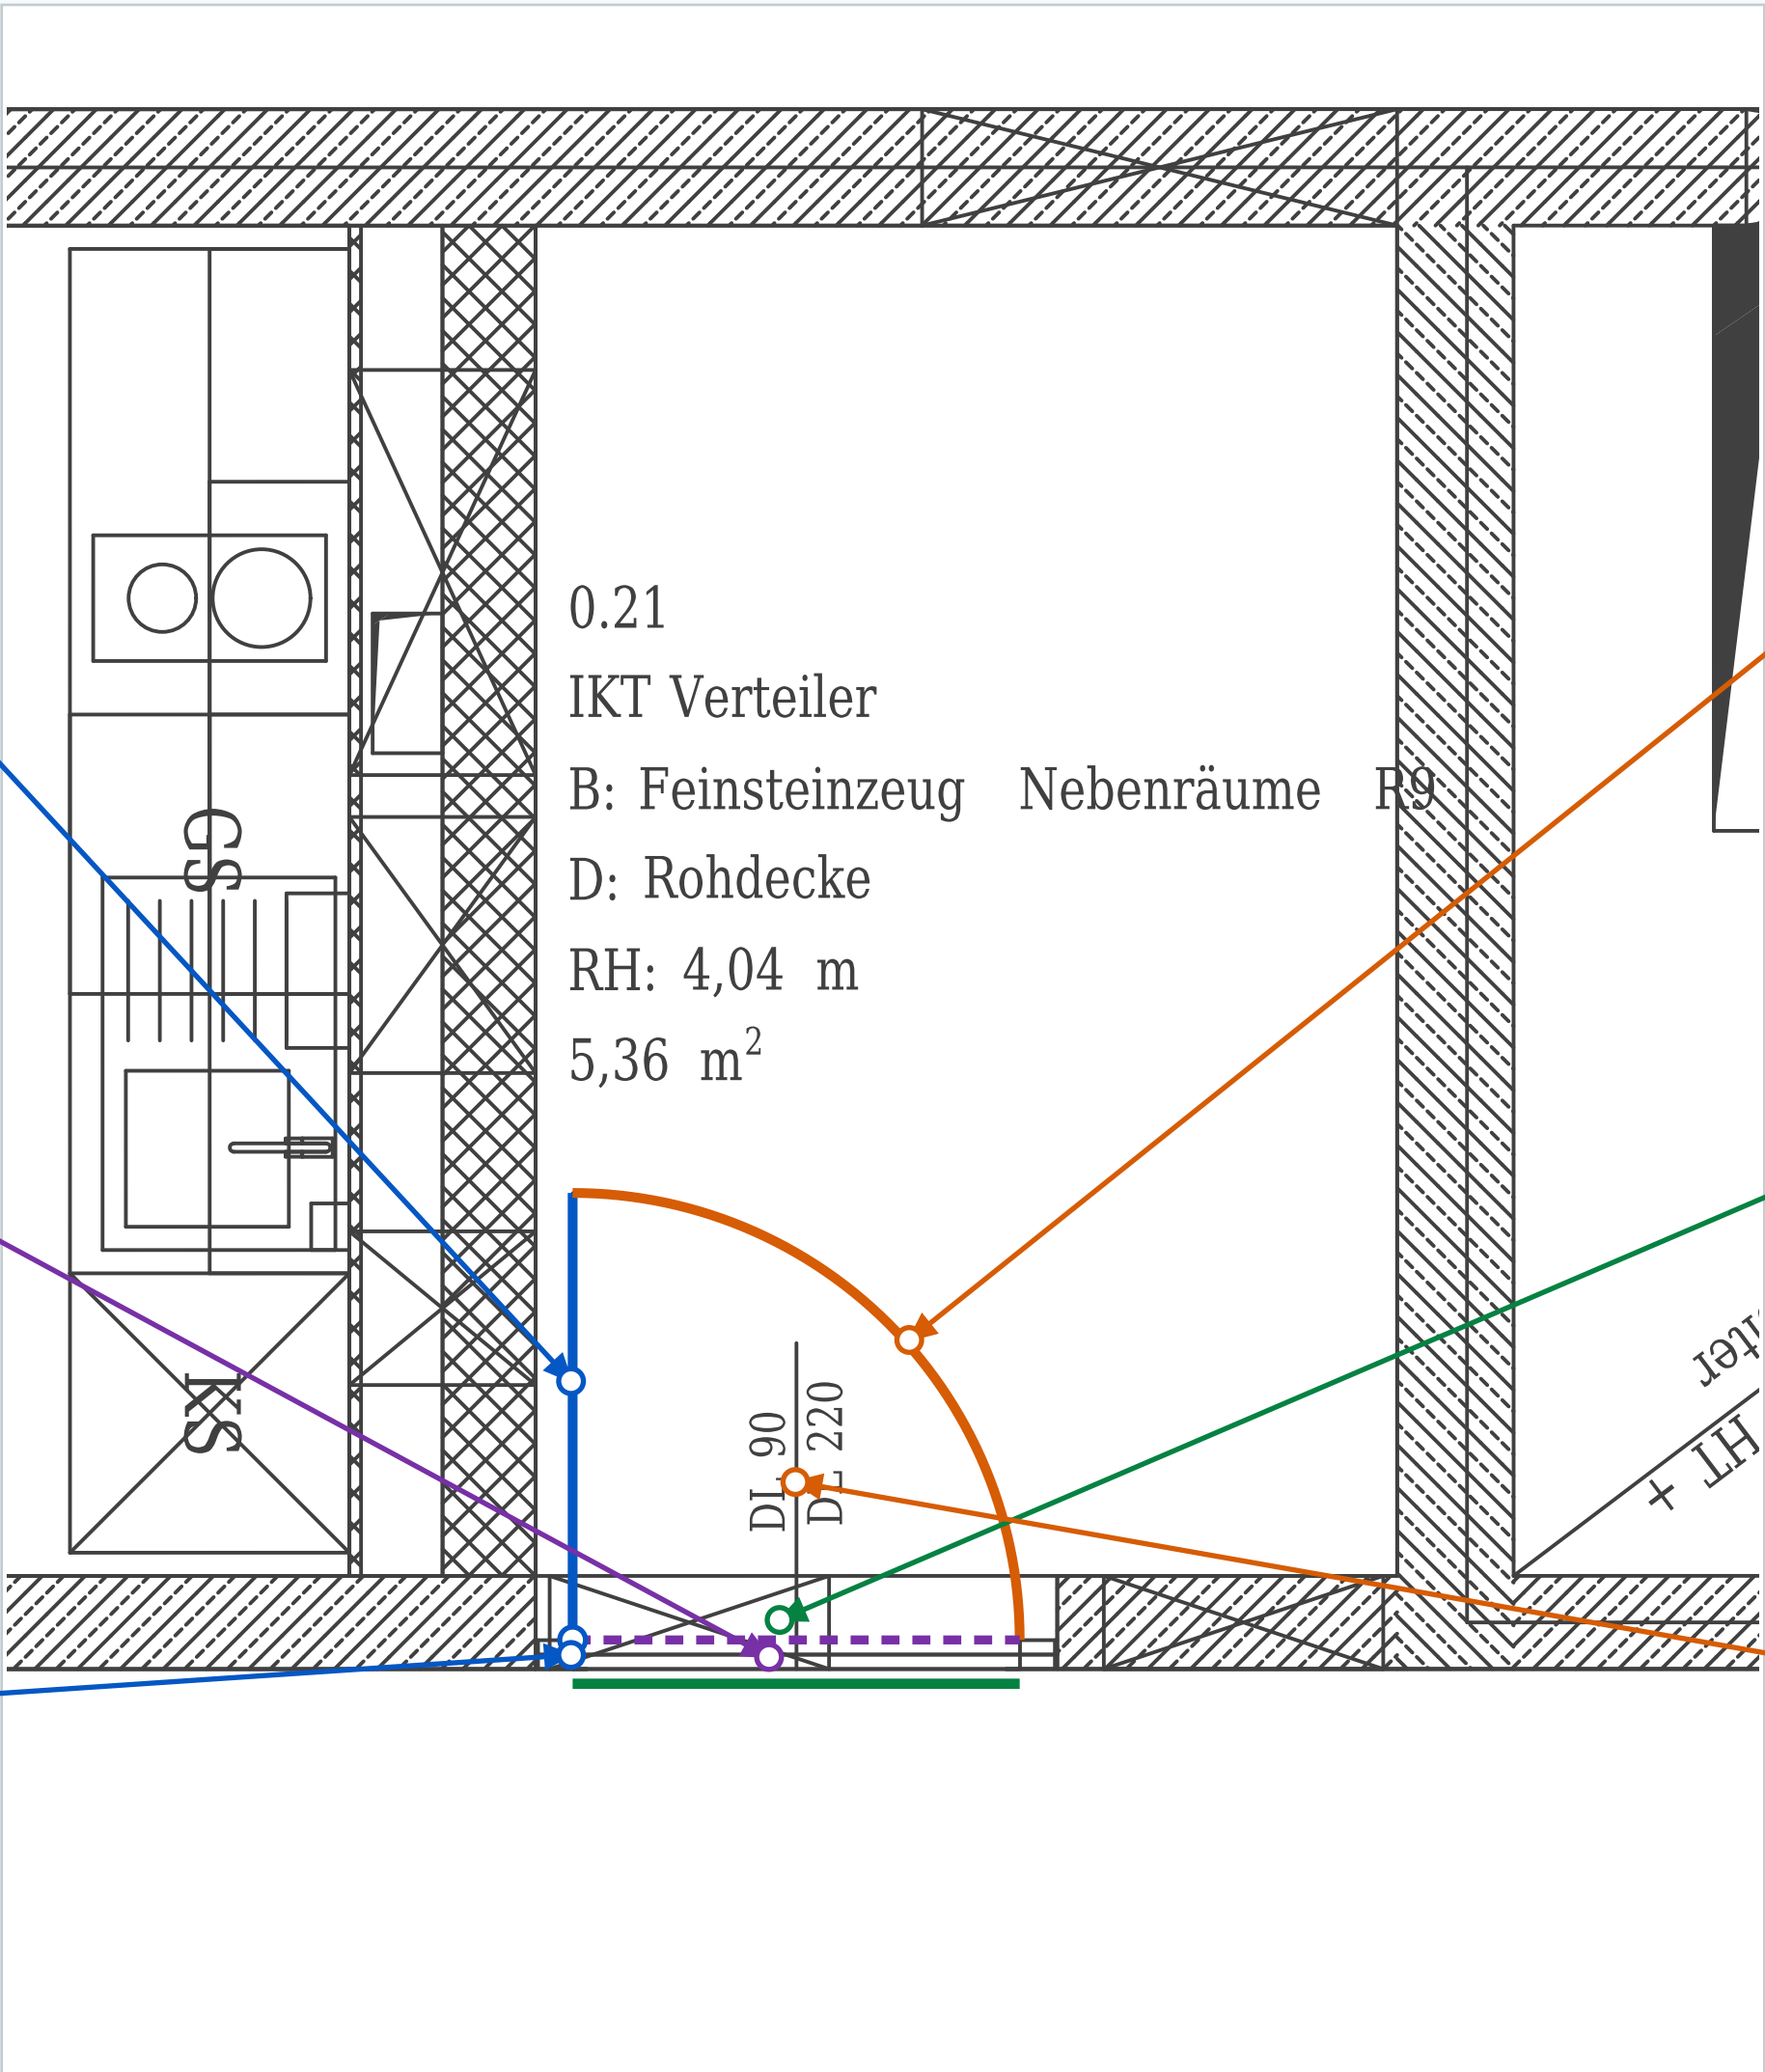

EG-10 | Originalausschnitt mit direkt zugeordneten Merkmalen

Flügel links

Ein gerades Türblatt.

Flügel rechts


Zweites Blatt derselben Tür.

Zwei Bögen

Beide Schwenkbögen sind orange nachgezogen.

Ein Portal

Beide Flügel teilen einen Durchgang.

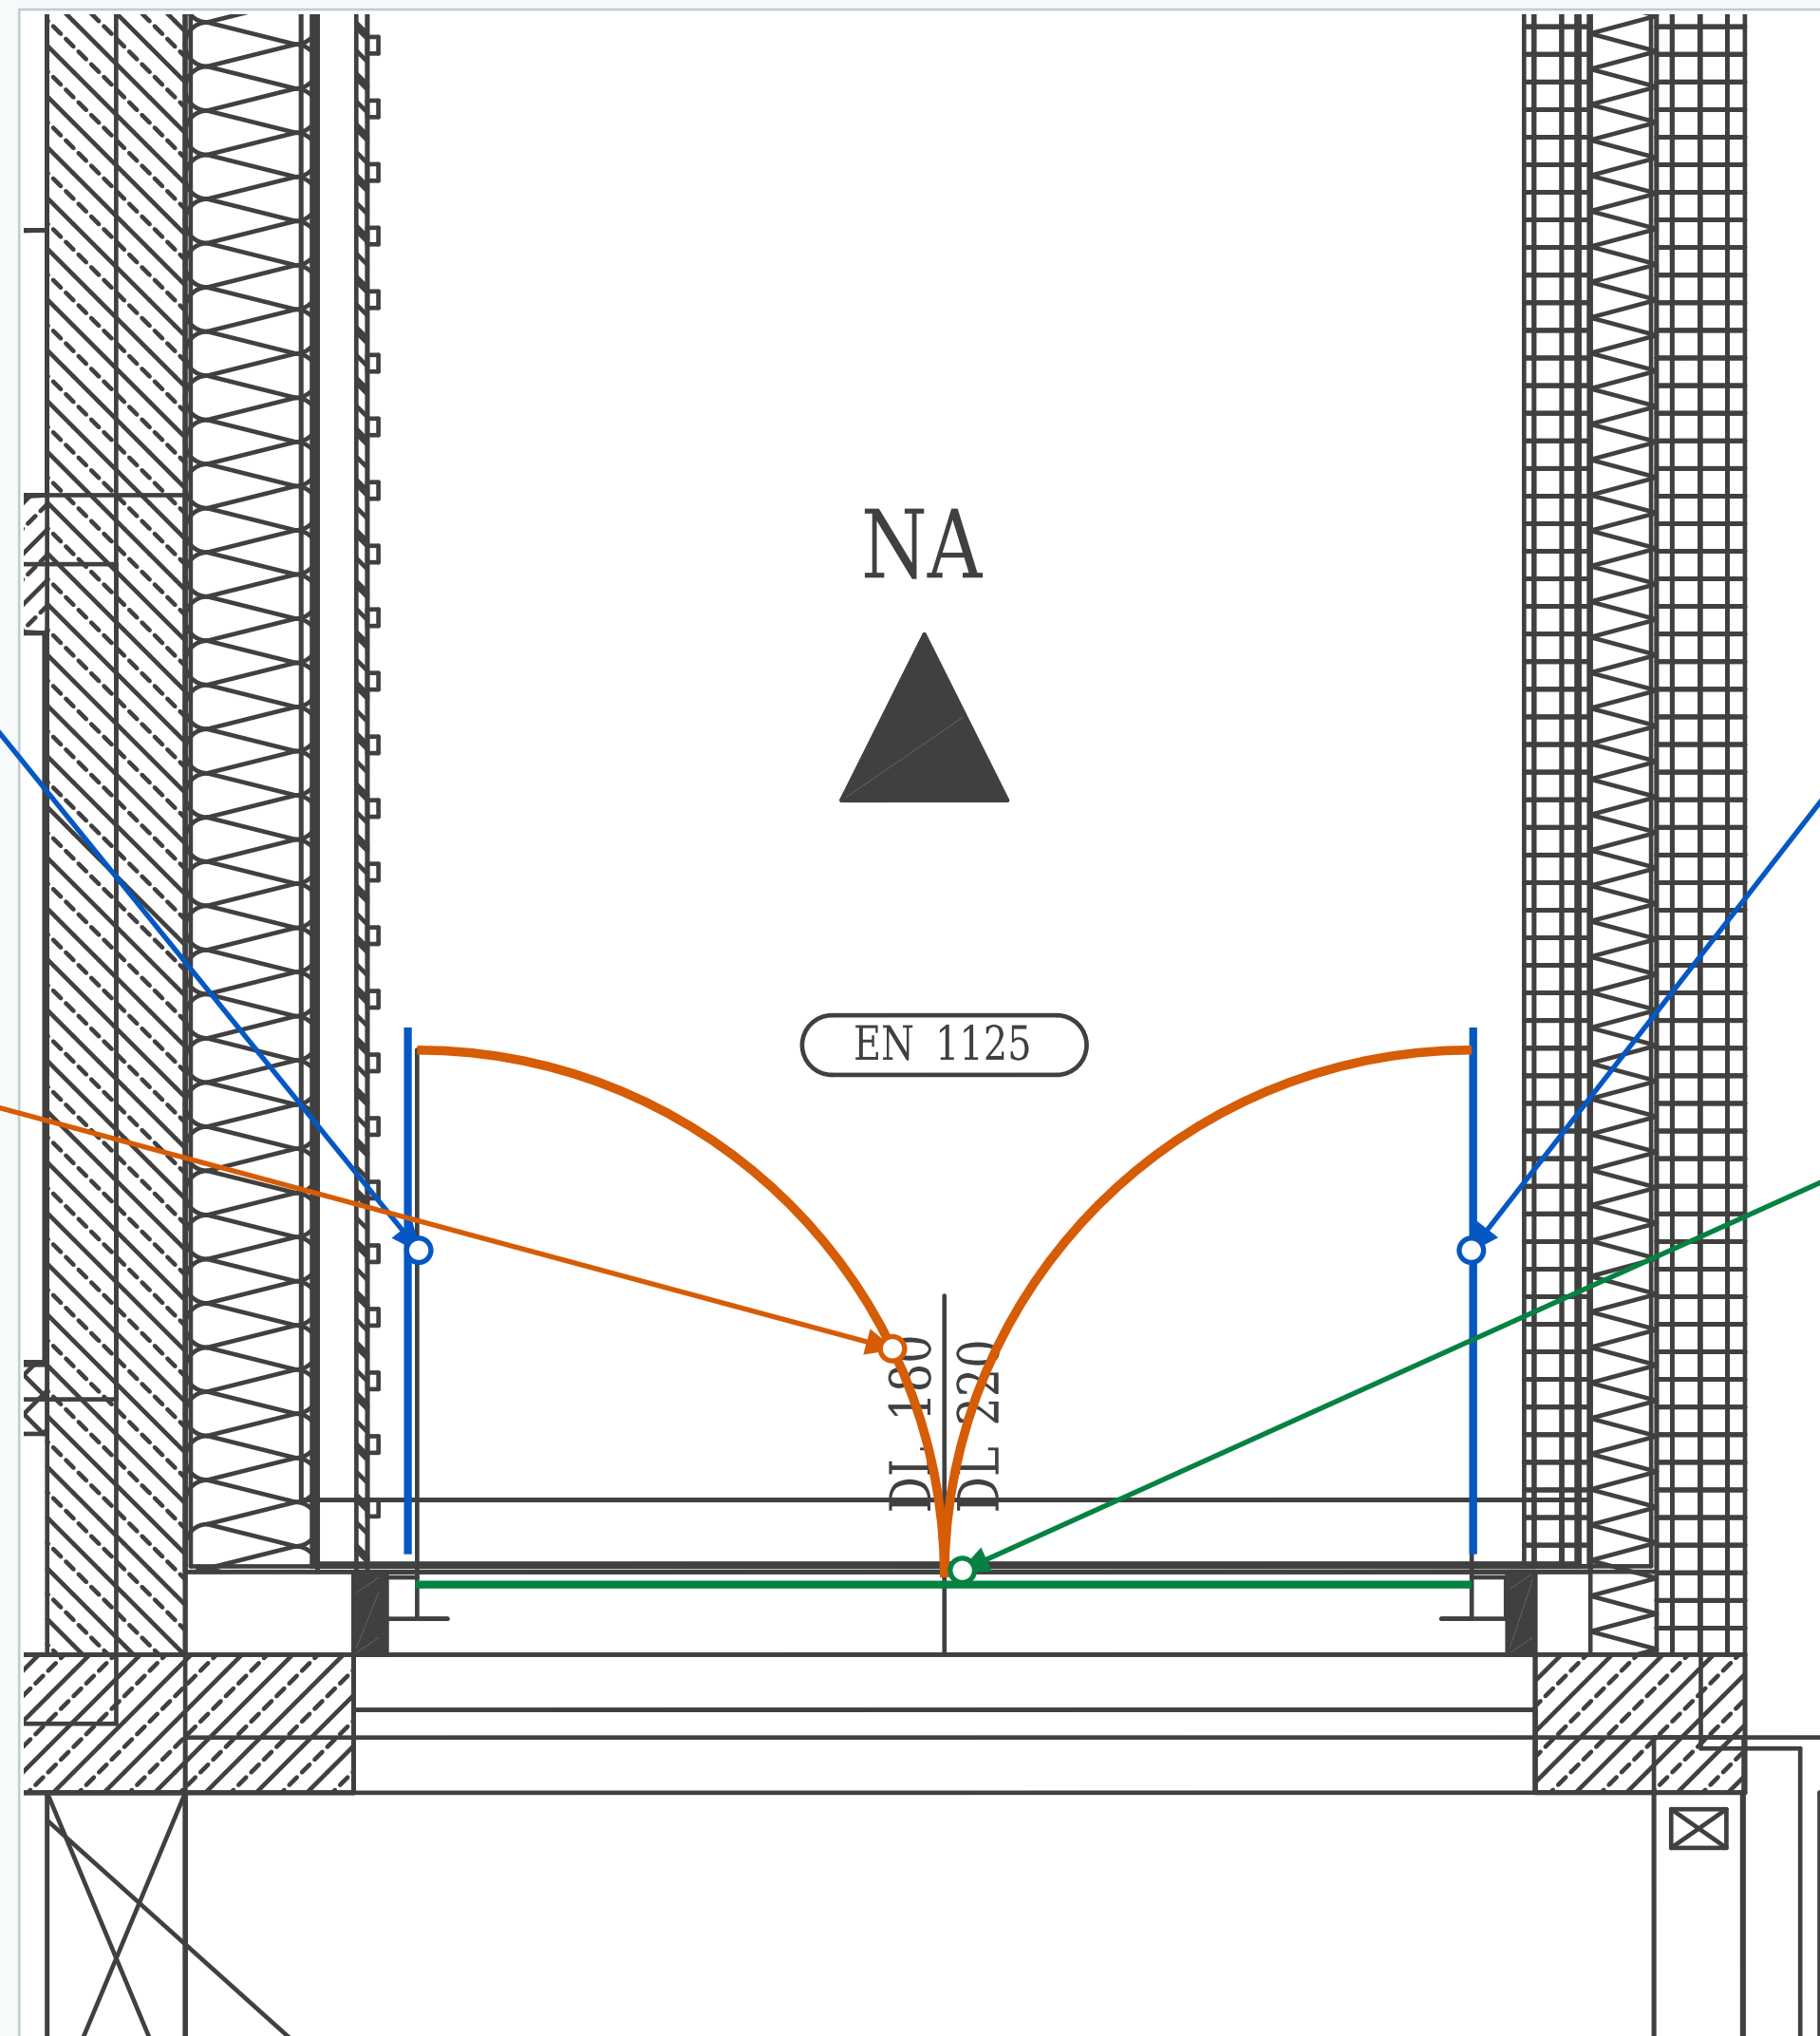

Rahmen: erklärter Bereich. Farblinien: Originalmerkmale. Pfeile: Zuordnung.

EG-11 | Originalausschnitt mit direkt zugeordneten Merkmalen

Schiebeflügel

Kurze parallele
Blattlinien.

Schieberichtung


Kleine Pfeile
parallel zur
Öffnung.

Äußerer Zugang

Zwei Türgruppen
an der Außenfront.

Zur
Eingangshalle

Zwei weitere
Gruppen, ohne
Drehbogen.

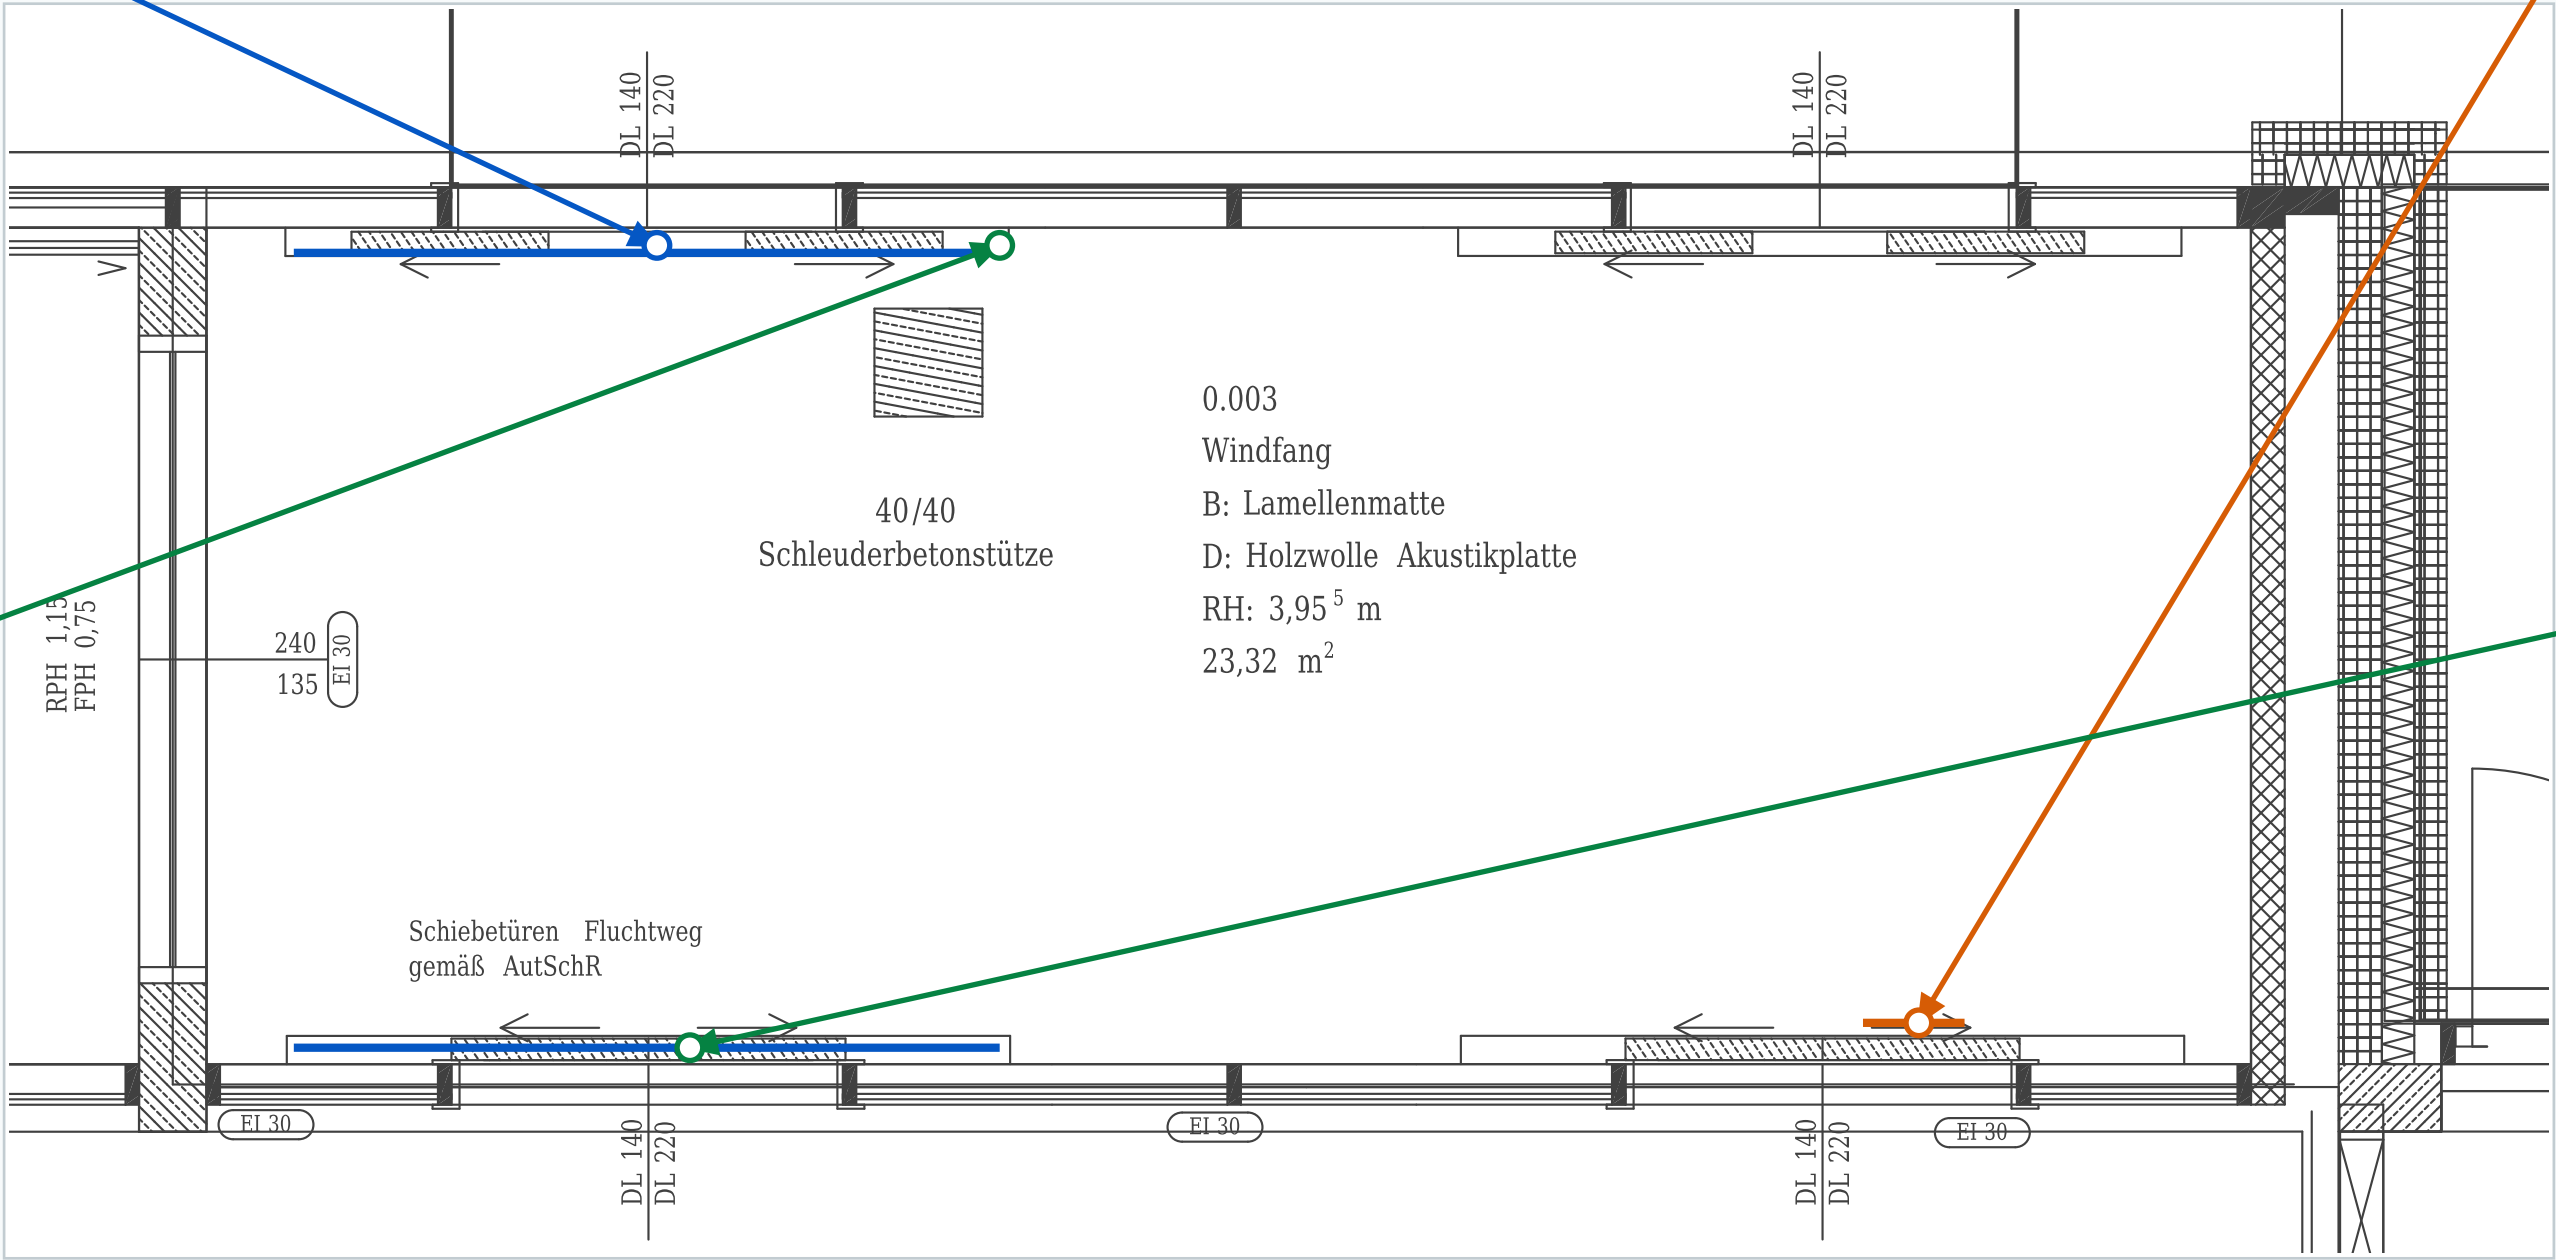

EG-12 | Originalausschnitt mit direkt zugeordneten Merkmalen

Rahmen / Glas

Eng benachbarte
Linien in der
Öffnung.

Öffnungsbogen


Orange: beide
Bögen der
Fensterflügel.

Brüstung

FPH 0,45: Höhe
über Fertigboden.

Mauerstück

Roter Rahmen
umfasst den festen
Wandaufbau.

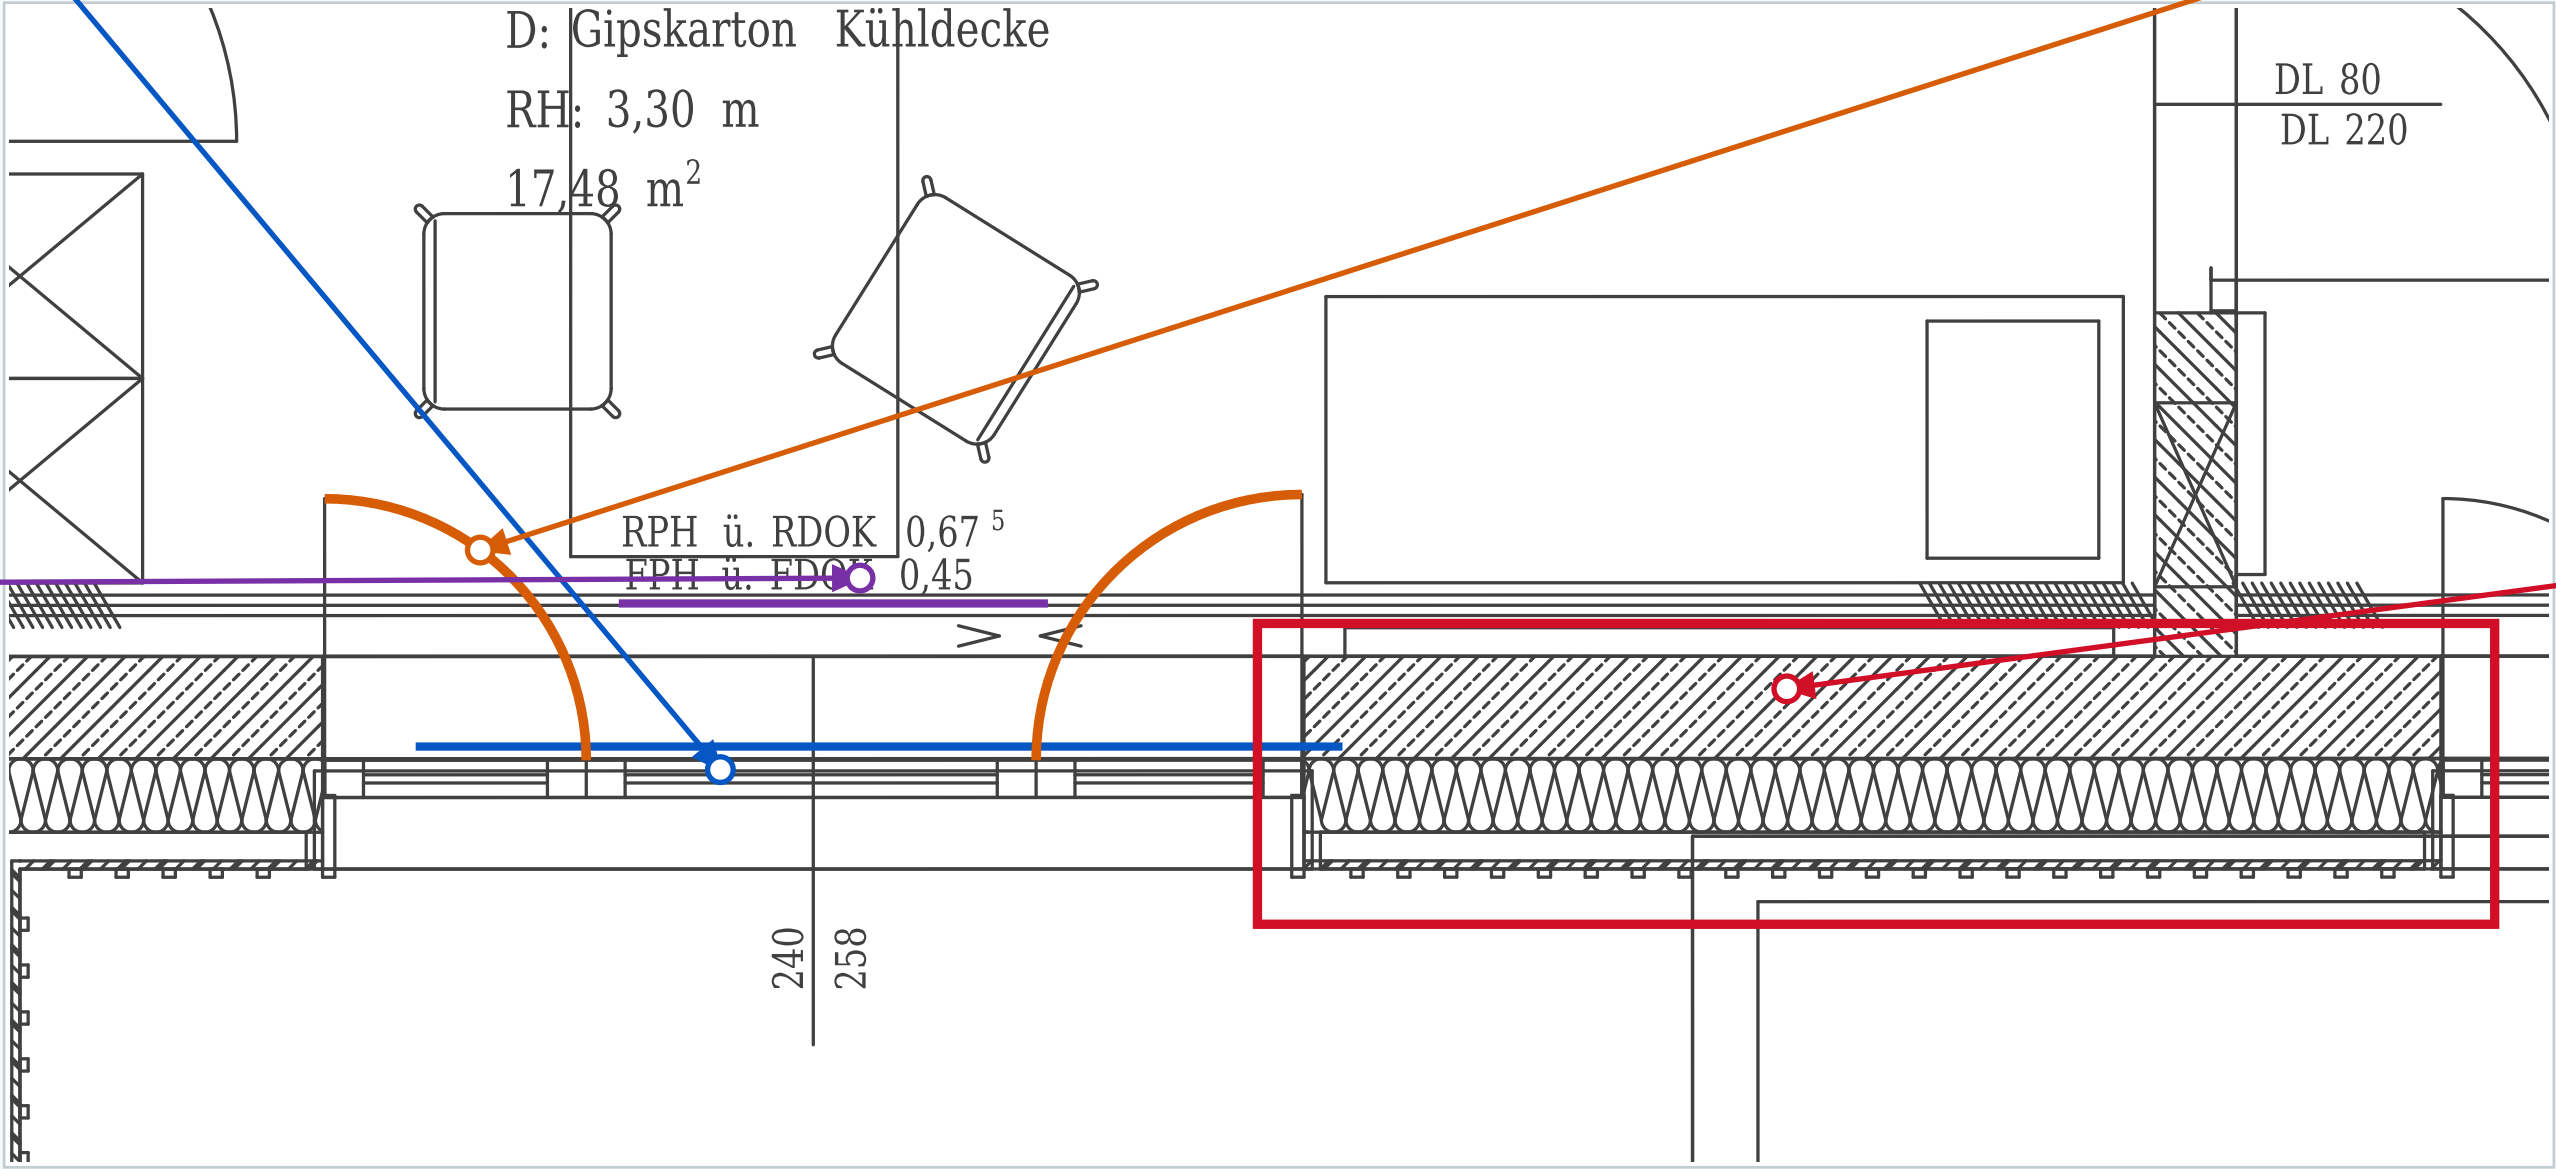

Rahmen: erklärter Bereich. Farblinien: Originalmerkmale. Pfeile: Zuordnung.

EG-13 | Originalausschnitt mit direkt zugeordneten Merkmalen

Fensterrahmen

Rahmenlinien
zwischen
Wandstücken.

Fensterbogen


Orange folgt den
Bögen der
Fensterflügel.

Höhenbezug UG

FPH ü. FBOK UG
4,50 lesen.

Material
dazwischen

Wandpfeiler bleibt
undurchlässig.

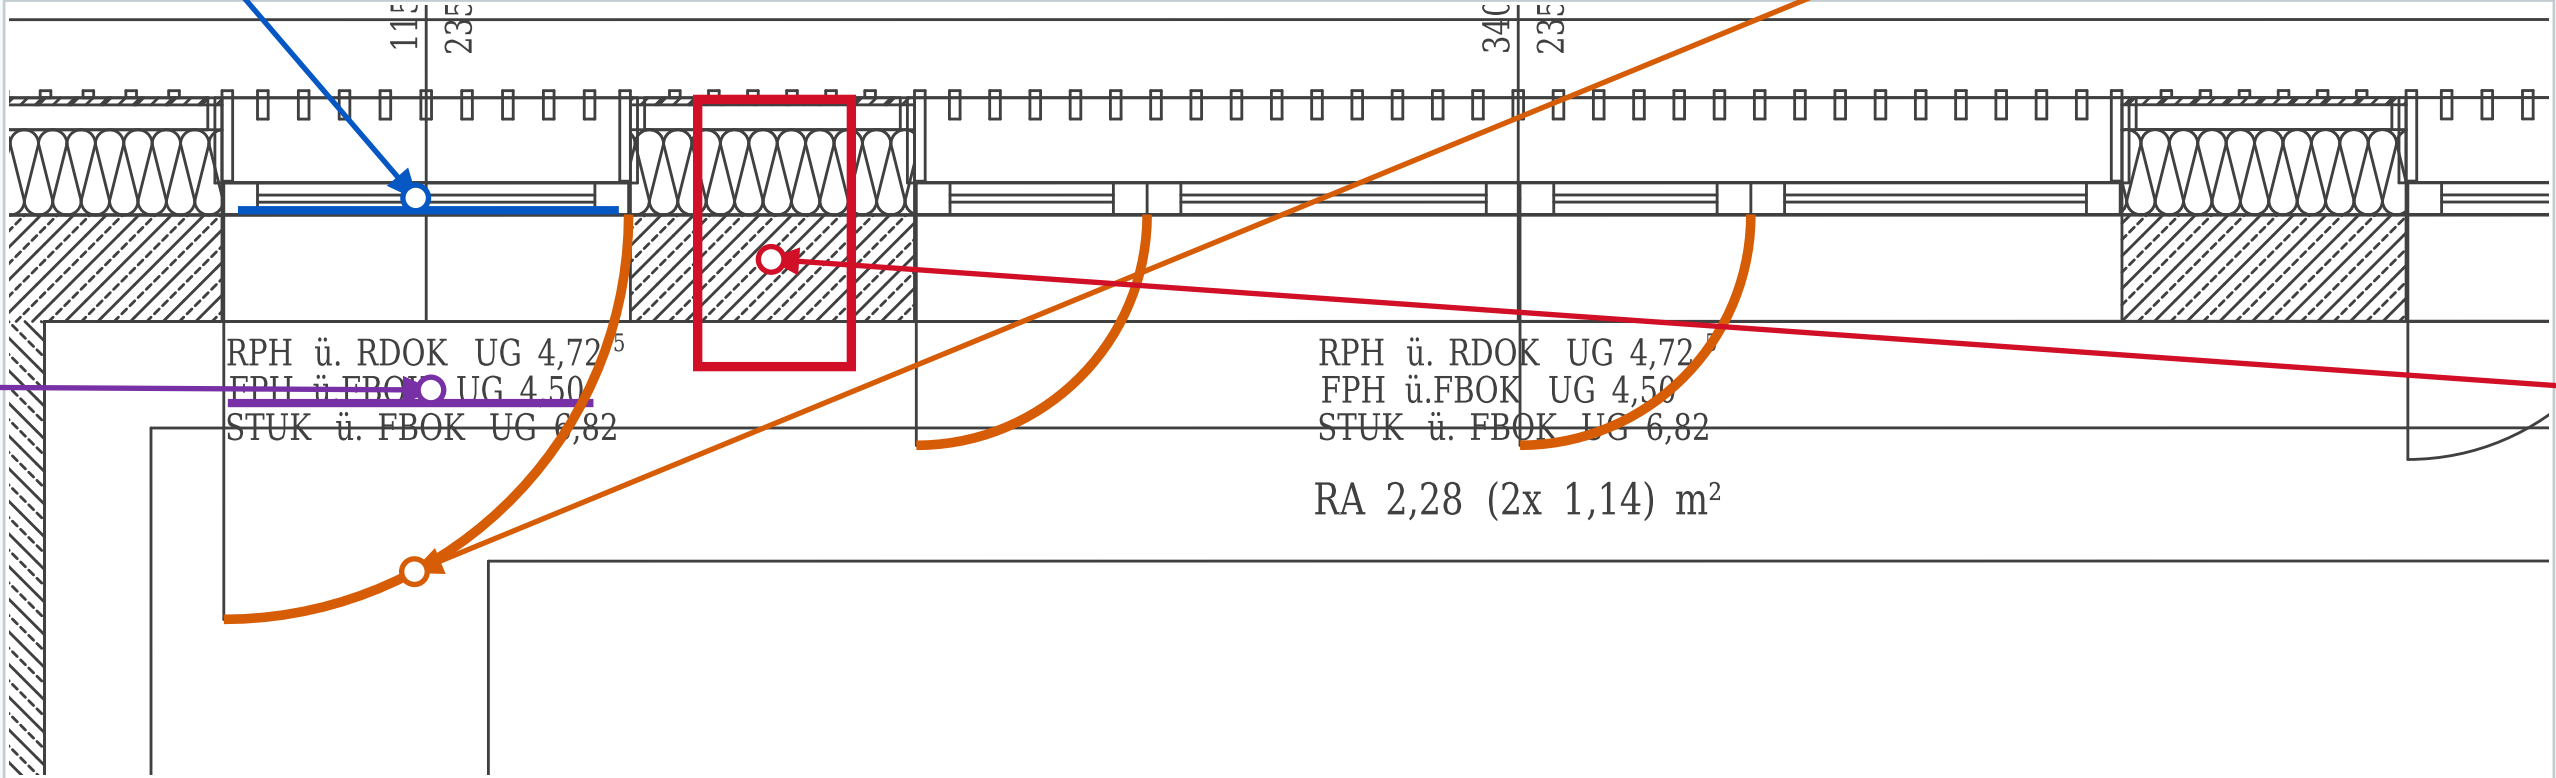

EG-14 | Originalausschnitt mit direkt zugeordneten Merkmalen

Fester Abschluss

Parallele Linien:
keine offene Lücke.

Drehflügel


Bogen und Blatt
oben am Raum.

Mauerstück

Schraffur mit zwei
Randlinien.

Körperprüfung

Durch Glas führt kein normaler Weg.

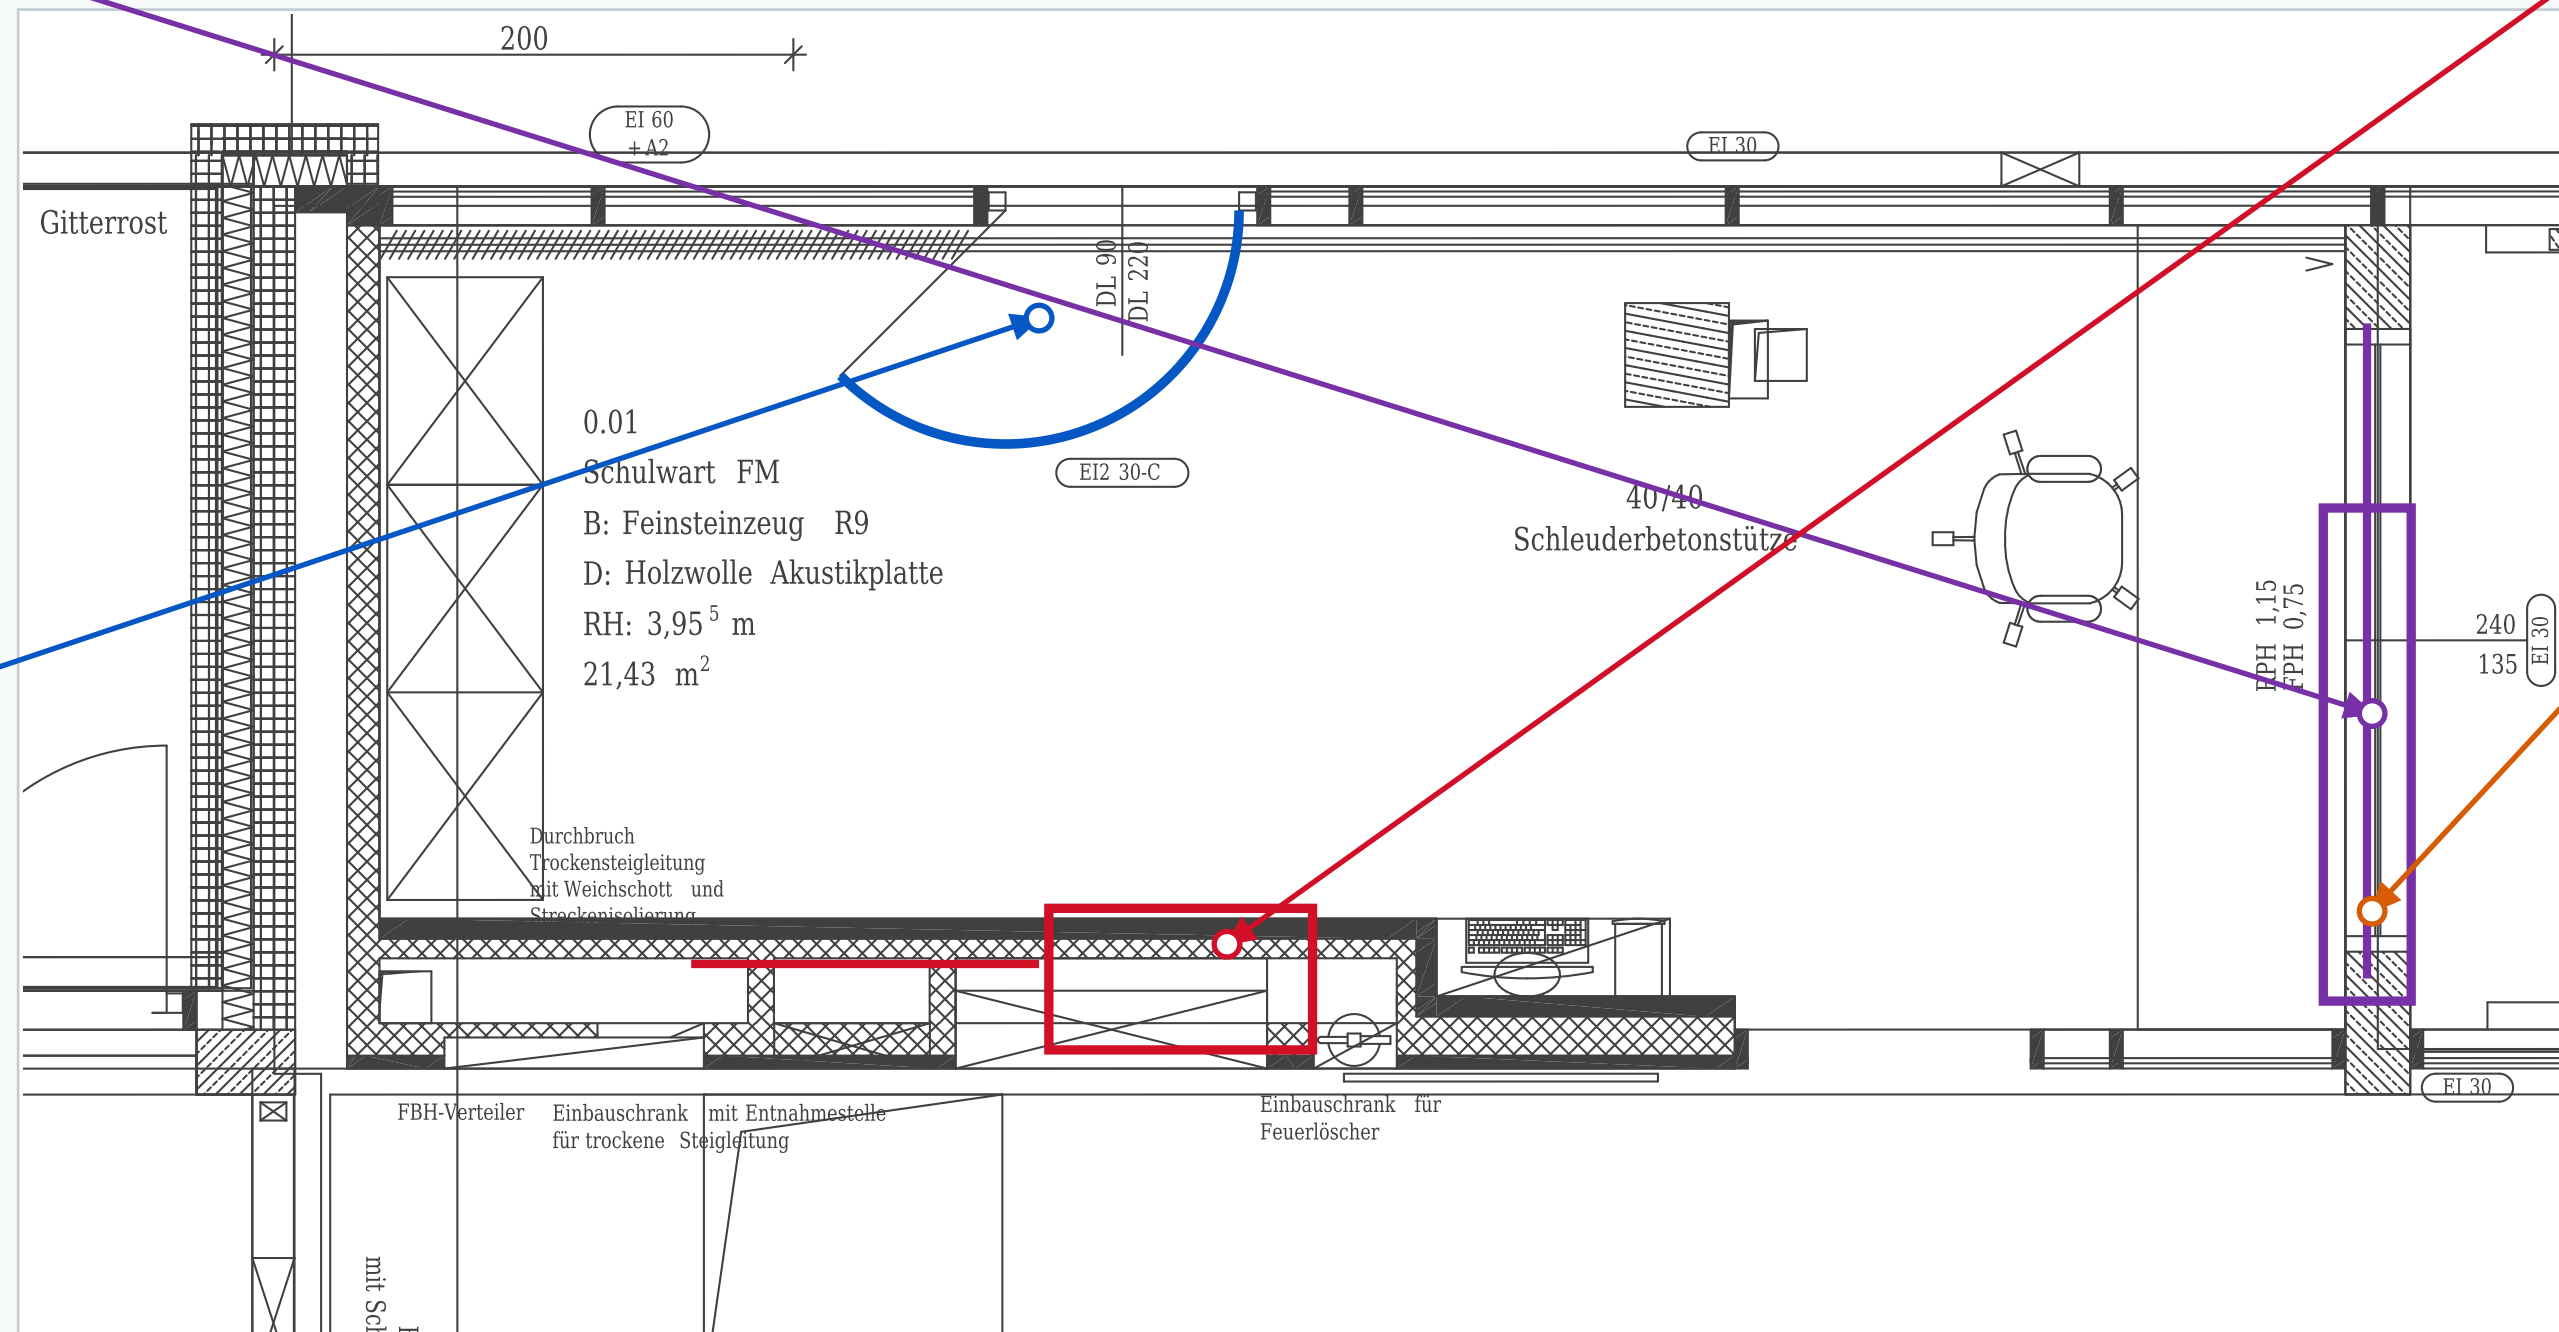

Rahmen: erklärter Bereich. Farblinien: Originalmerkmale. Pfeile: Zuordnung.

EG-15 | Originalausschnitt mit direkt zugeordneten Merkmalen

Gangfläche

Grüner Boden vor dem Kopierraum.

Um den Raum


Der Weg läuft außen am Kopierraum vorbei.

Echte Raumgrenze

Rahmen umfasst die untere Raumwand.

Türöffnung

Öffnung zwischen den Wandenden.

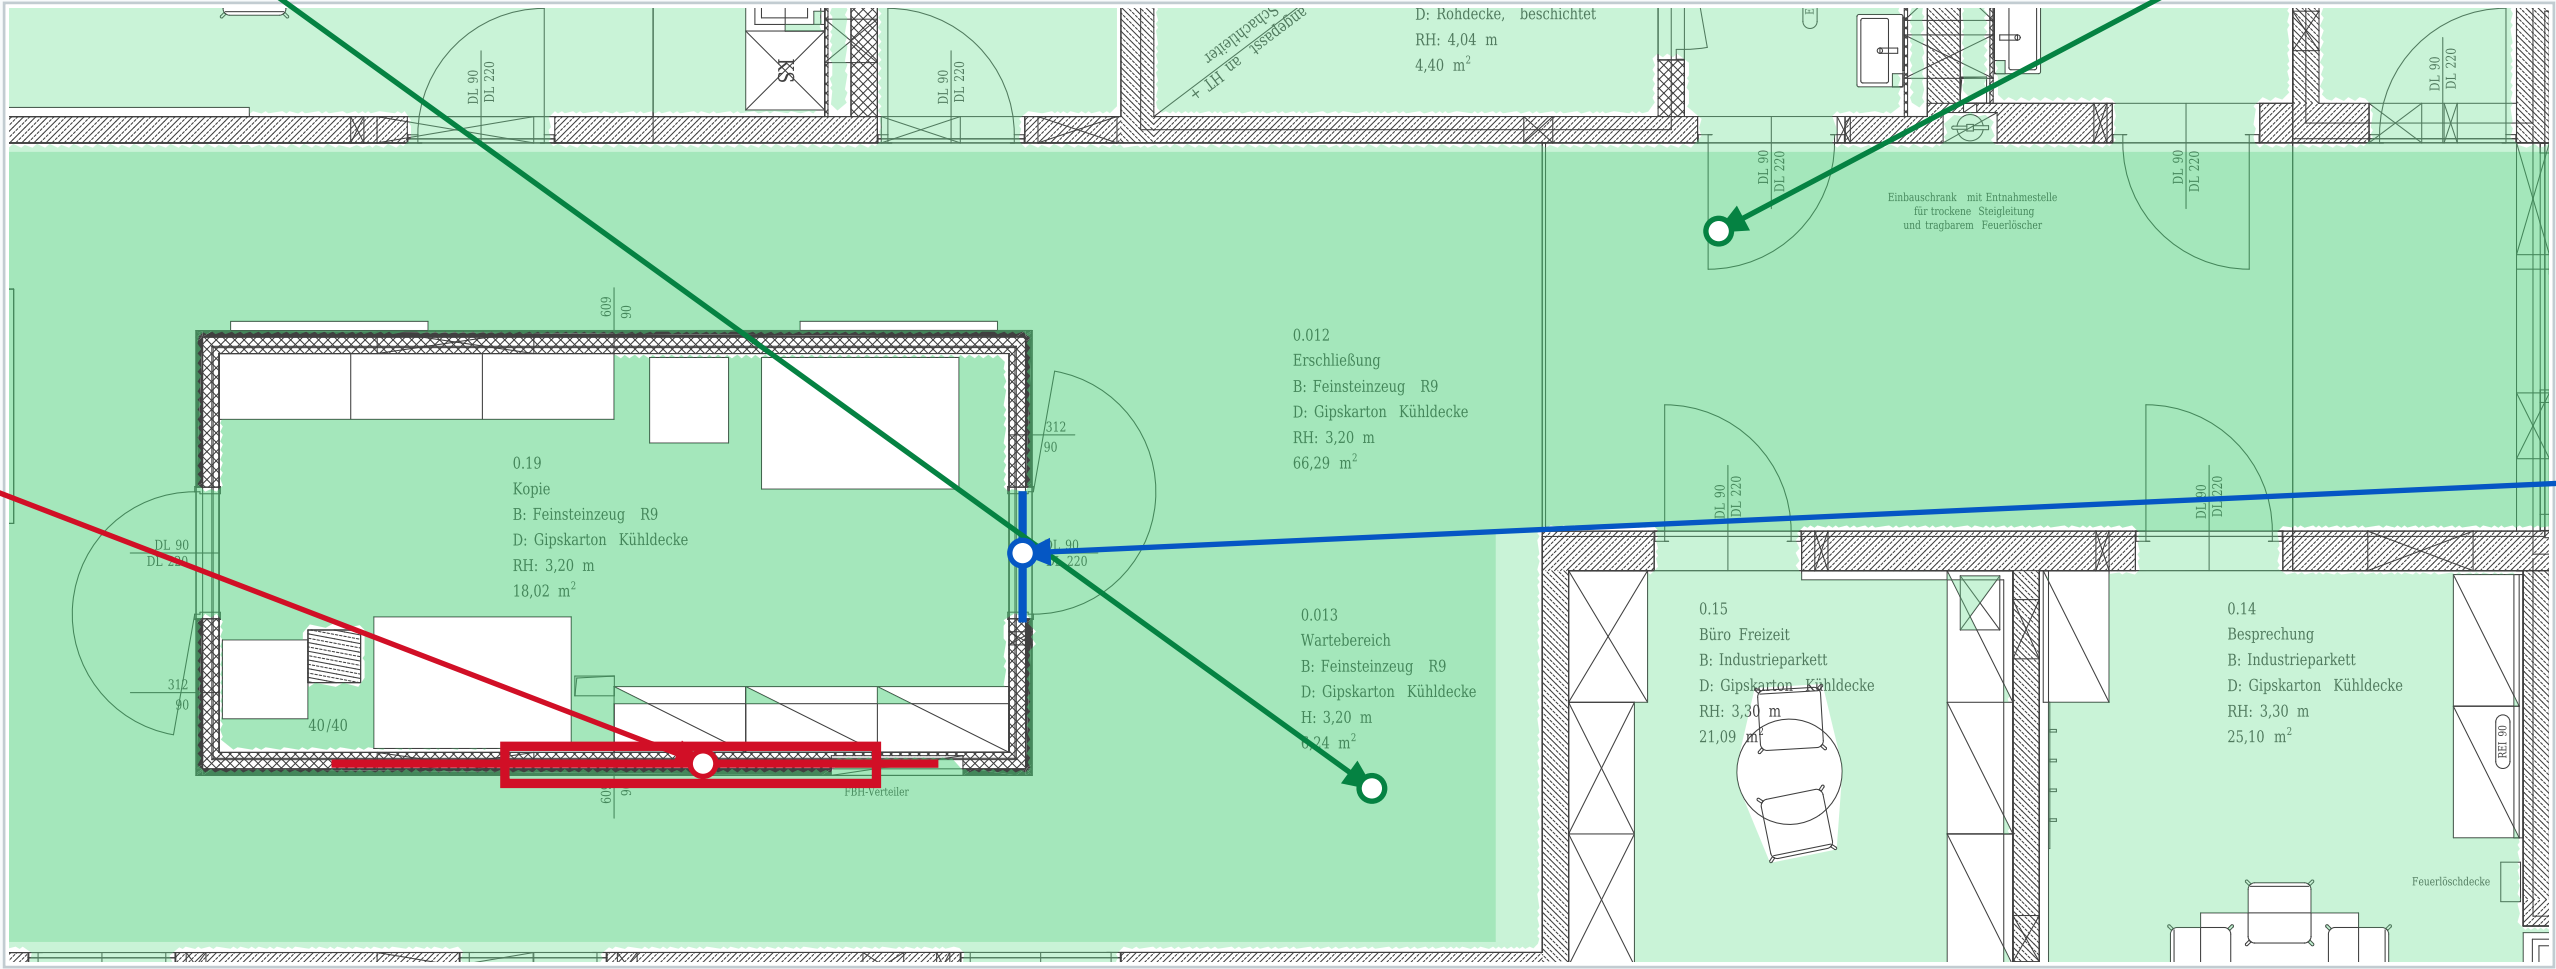


EG-16 | Originalausschnitt mit direkt zugeordneten Merkmalen

Ein Zugang

Hier kommt man
hinein und zurück.

Sackgasse

Zugänglicher
Raum, keine
Durchverbindung.

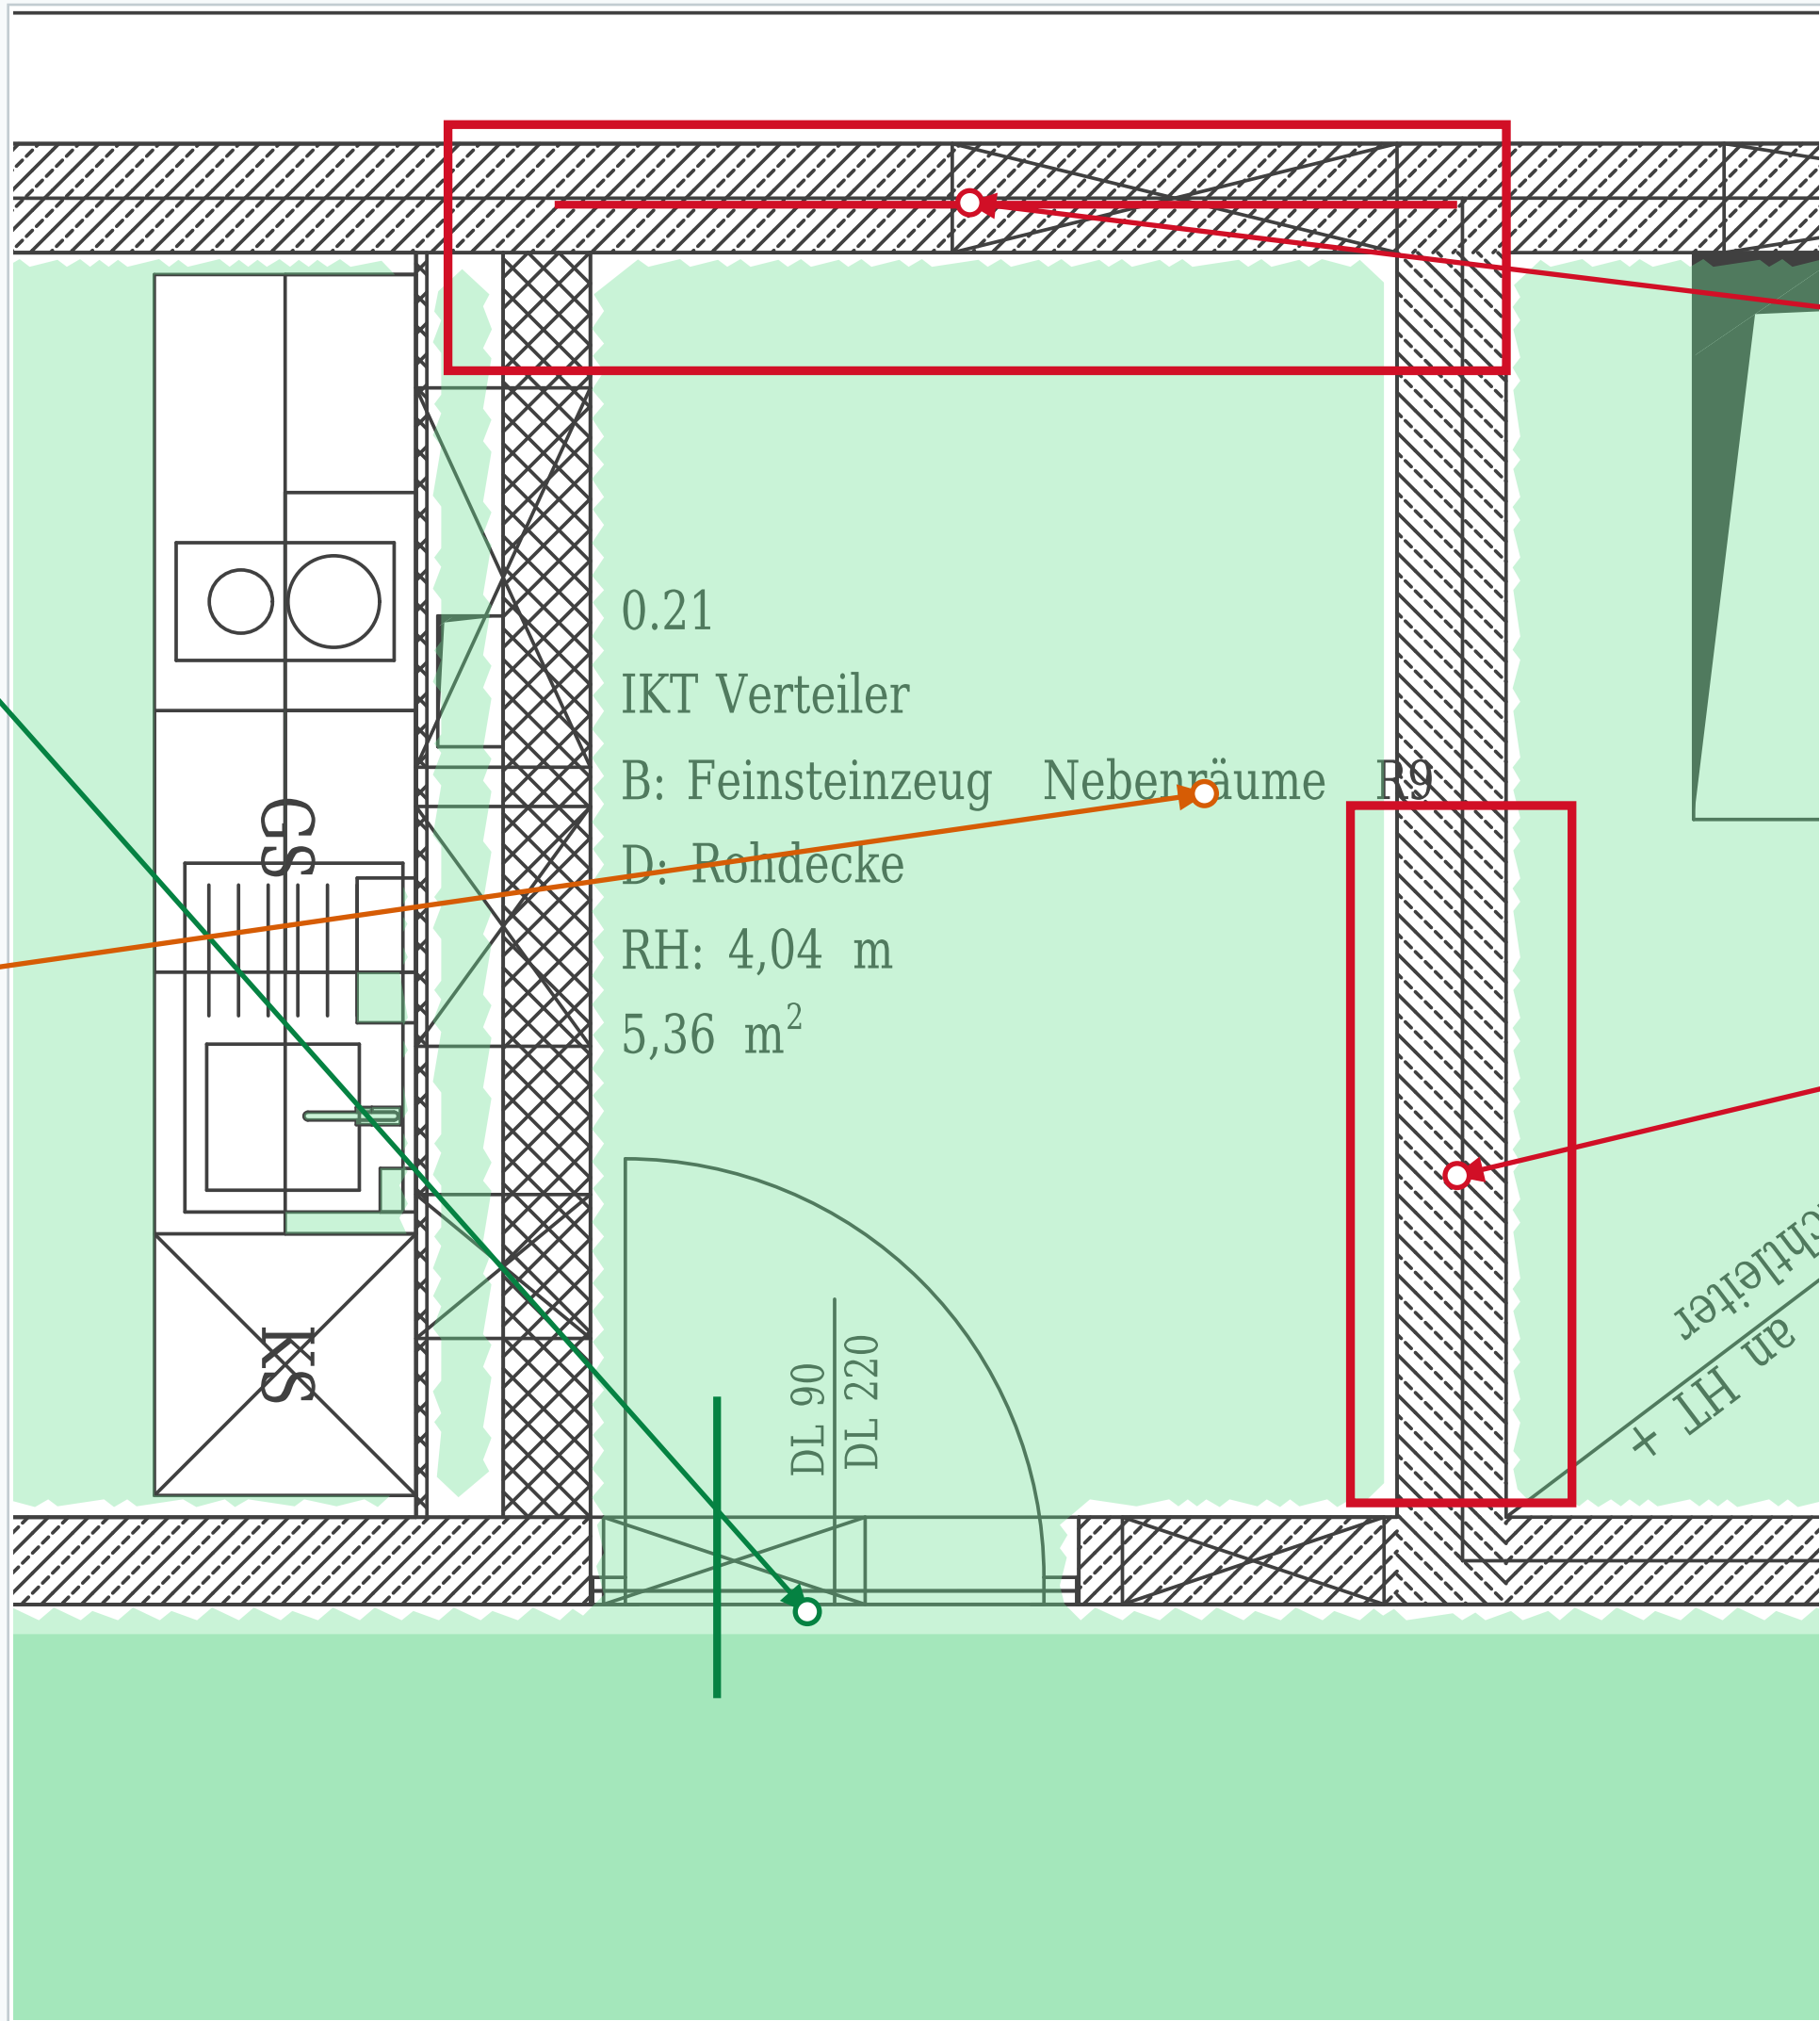

Wandabschluss

Rahmen zeigt den geschlossenen Wandabschluss.

Kein zweites Portal

Rahmen zeigt die geschlossene Seitenwand.

Rahmen: erklärter Bereich. Farblinien: Originalmerkmale. Pfeile: Zuordnung.

EG-17 | Originalausschnitt mit direkt zugeordneten Merkmalen

Deckenrand

Oberer Bauteilrand
laut VK RD / STUK.

Kein Wandkörper


Innenfläche bleibt
Teil der Halle.

Fester Rand

Rahmen zeigt den massiven Hallenrand.

Hallenboden

Verbindung setzt
sich darunter fort.

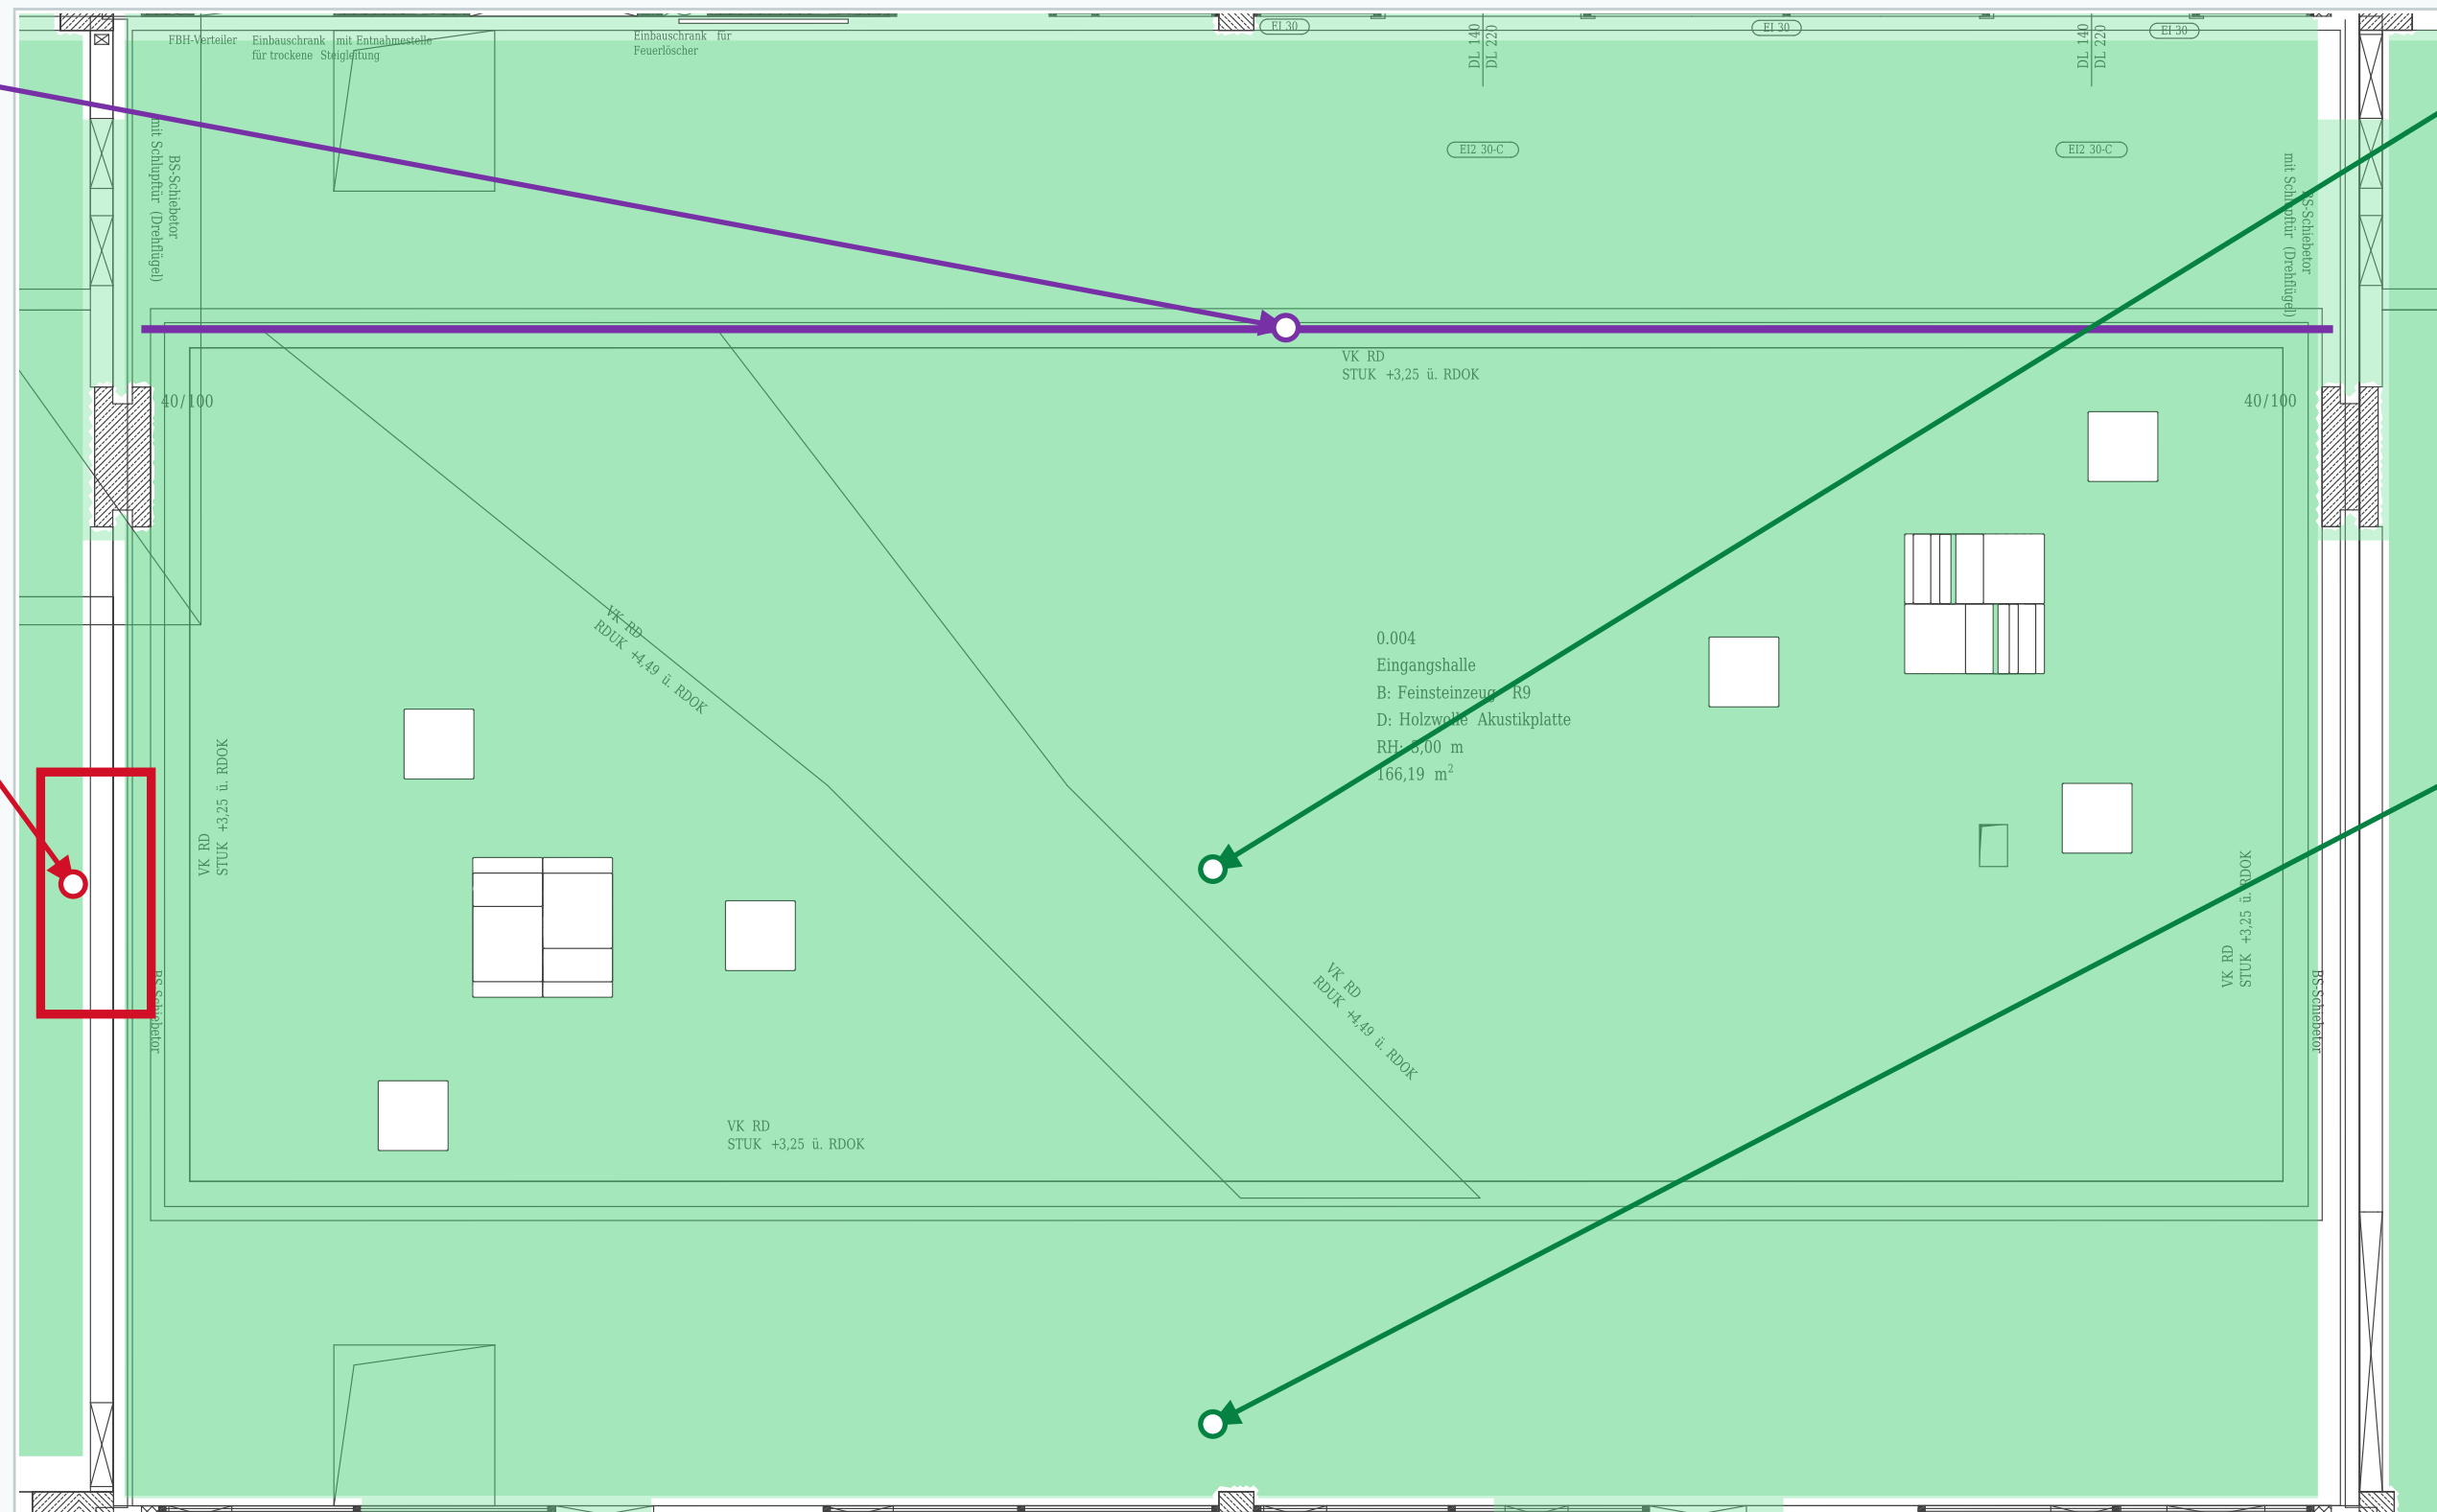

Rahmen: erklärter Bereich. Farblinien: Originalmerkmale. Pfeile: Zuordnung.

EG-18 | Originalausschnitt mit direkt zugeordneten Merkmalen

Technik-Hinweis

Text: Leitung mit Abschottung.

Einbauschrank


Beschriftung und Einbaukontur gehören zusammen.

Wandmaterial

Schraffiertes Band unter dem Raum.


Kein Personenportal

Der Hinweis ist kein Beleg für eine Gethür.

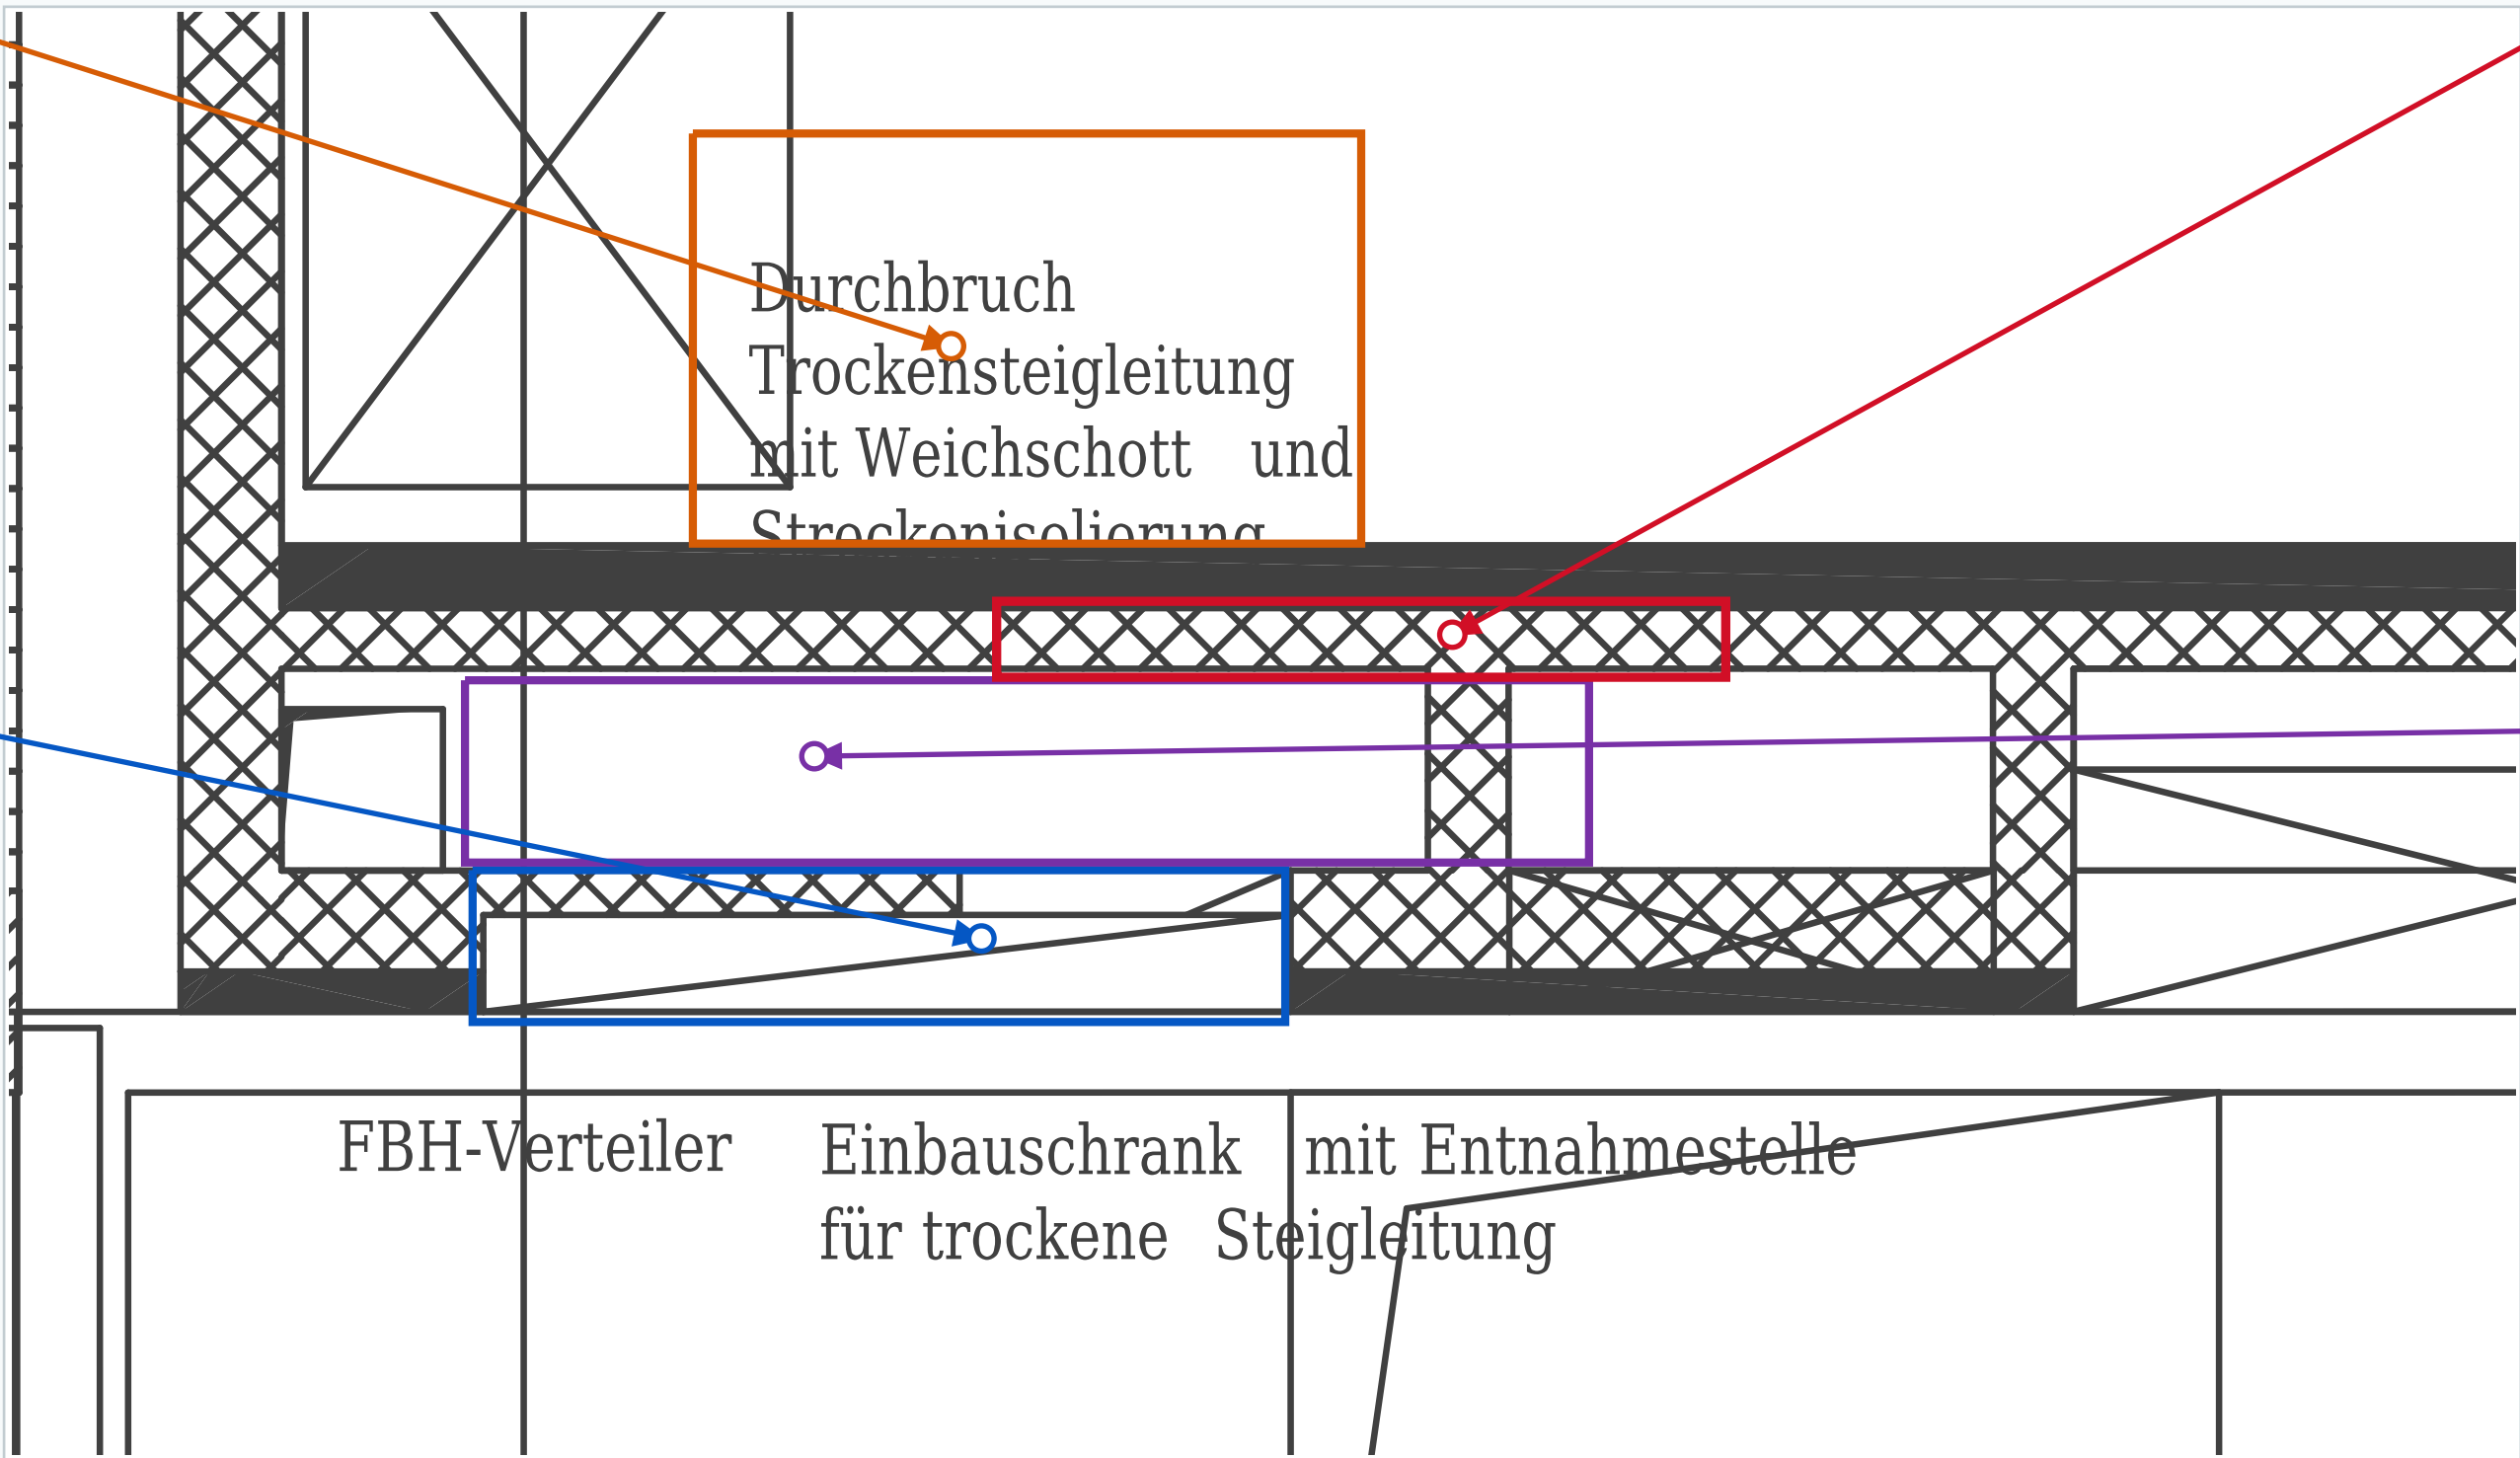

Rahmen: erklärter Bereich. Farblinien: Originalmerkmale. Pfeile: Zuordnung.

EG-19 | Originalausschnitt mit direkt zugeordneten Merkmalen

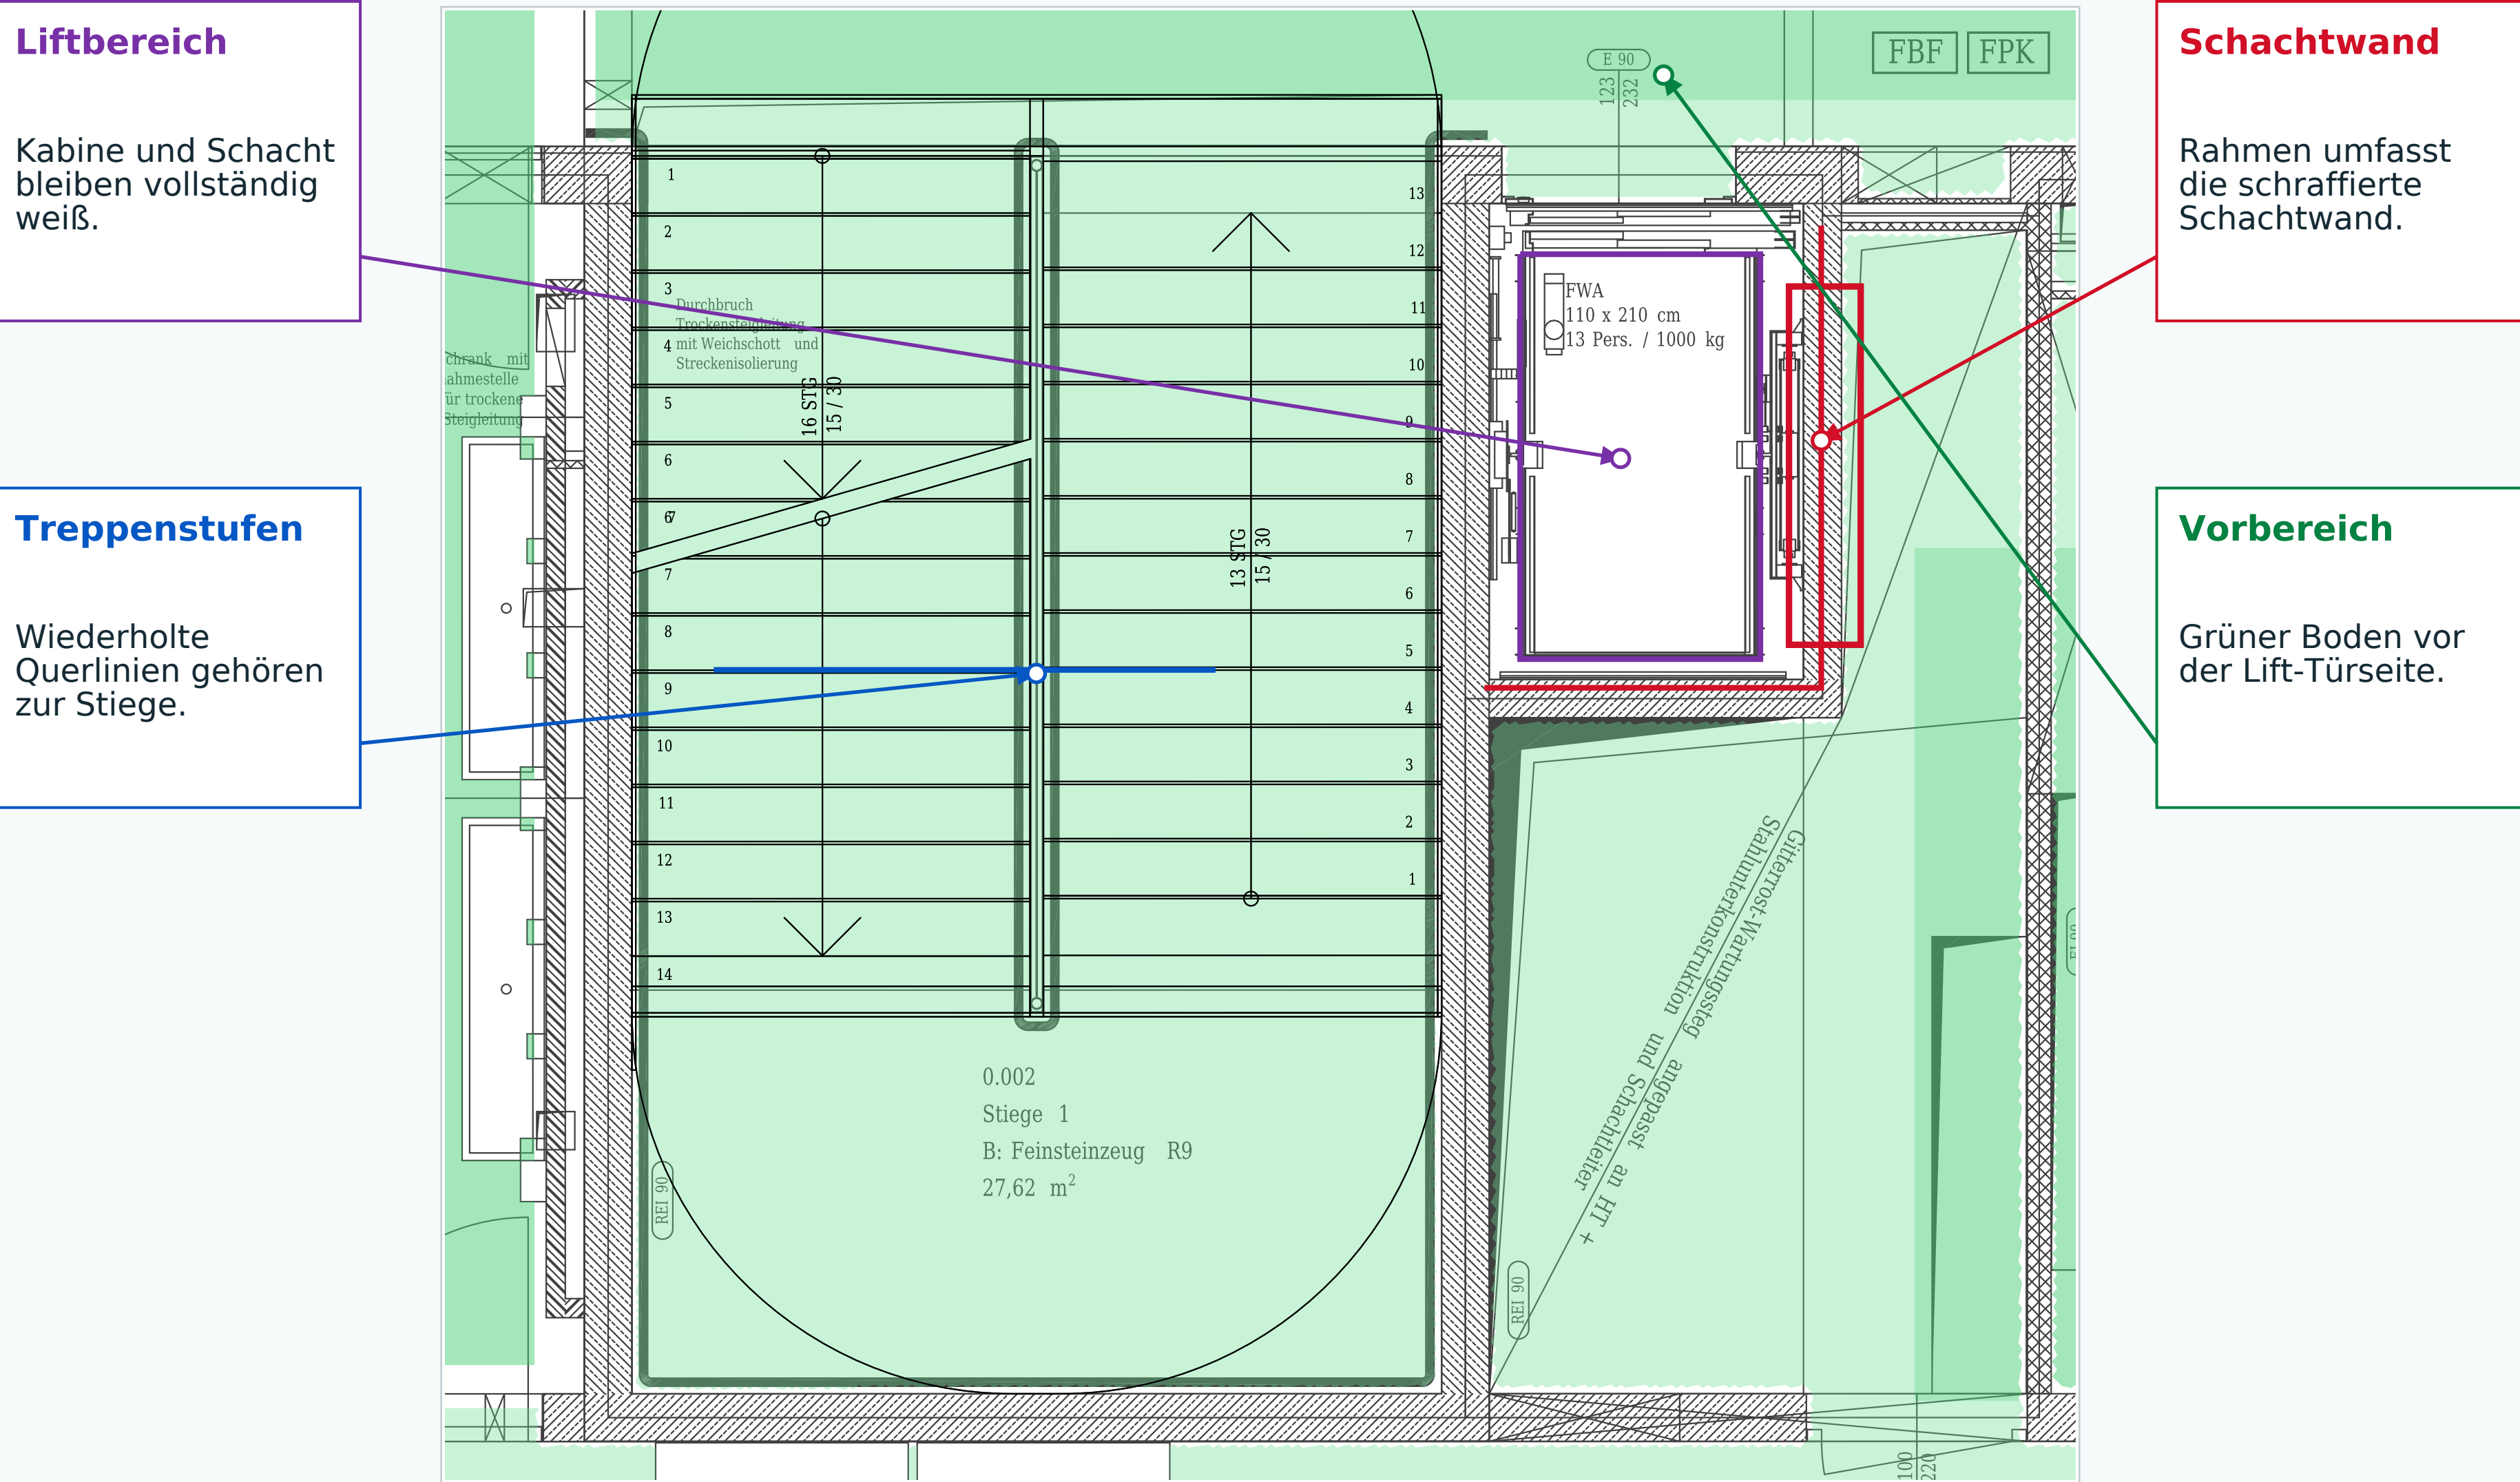

Rahmen: erklärter Bereich. Farblinien: Originalmerkmale. Pfeile: Zuordnung.

EG-29 | Originalausschnitt mit direkt zugeordneten Merkmalen

Kabine

Violett: eigene
Umgrenzung
innerhalb des
Schachts.

Schiebetürlinien

Blau: parallele
Blätter an der
Türseite.

Plantext

Größe und
Lastangabe im
Kabinenbereich.

Schachtwand


Rahmen umfasst
die schraffierte
Schachtwand.

Technik

Orange: Abstand
und Mechanik, kein
Gang.

Vorbereich

Grün: Vorbereich
vor der Türseite.

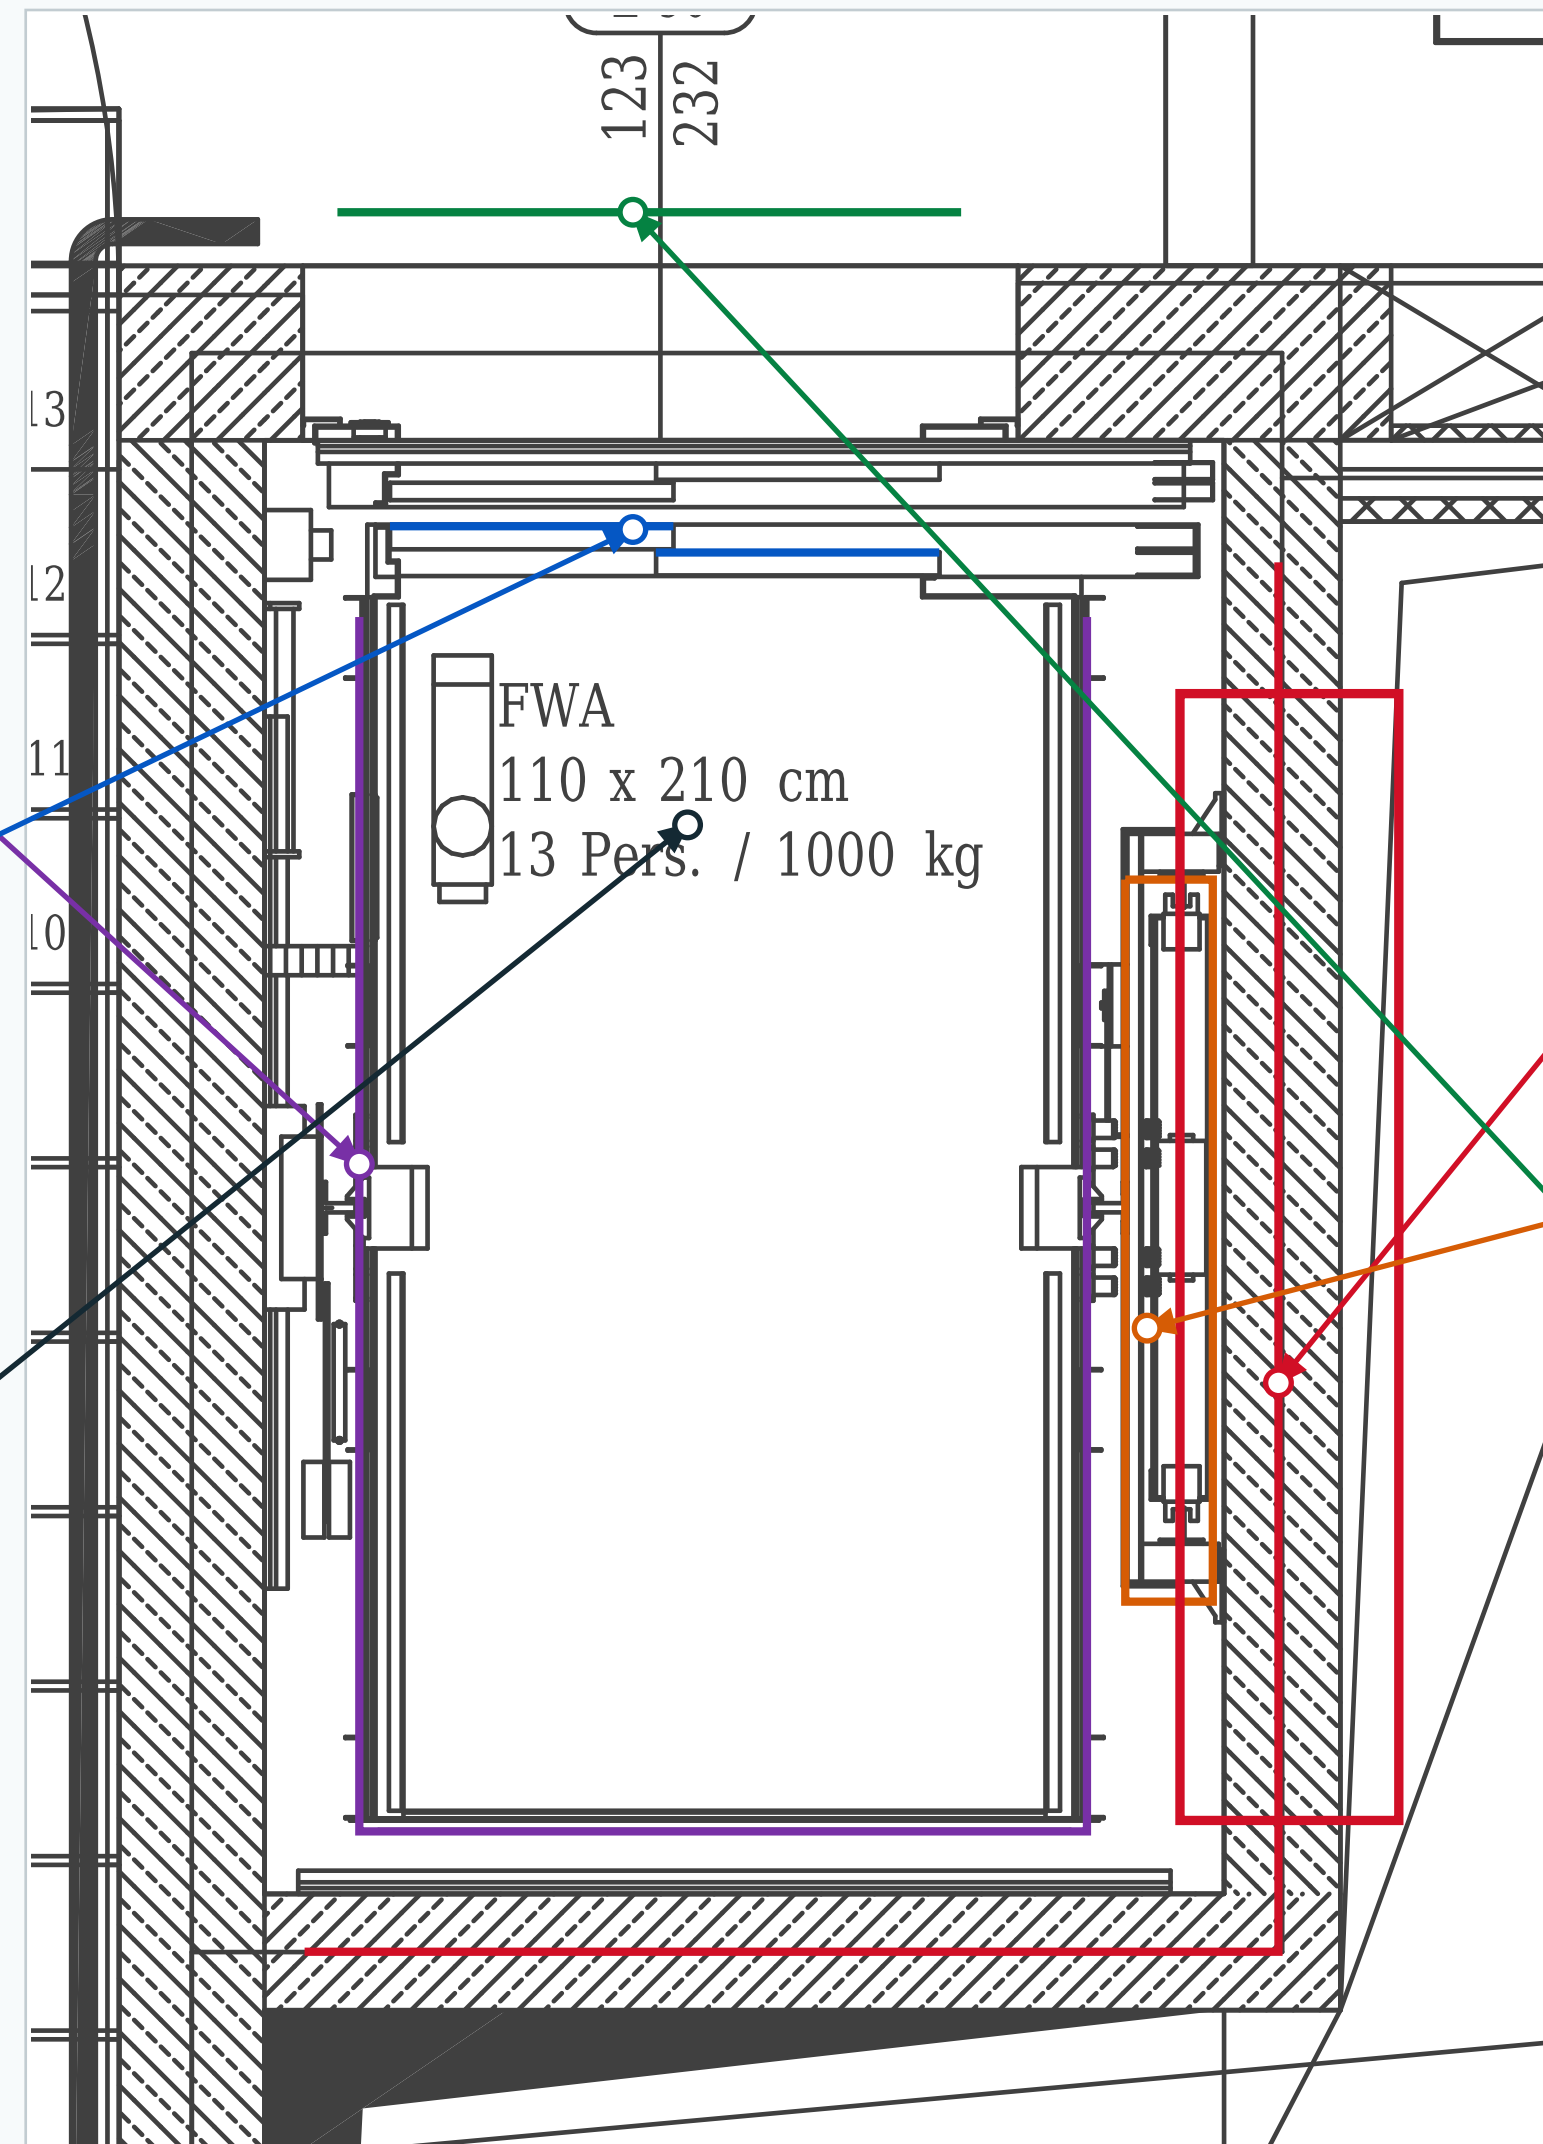

Rahmen: erklärter Bereich. Farblinien: Originalmerkmale. Pfeile: Zuordnung.

EG-20 | Originalausschnitt mit direkt zugeordneten Merkmalen

Stufenkante

Regelmäßige
parallele
Querlinien.

Treppenbruch

Schräge
Unterbrechung;
keine Wand.

Zwei Läufe


In der Mitte bleibt
die Trennung.

Lauflinie / Pfeil

Richtungssymbol
im rechten Lauf.

Podestbereich

Grün mit
erhaltenen
schwarzen Linien.

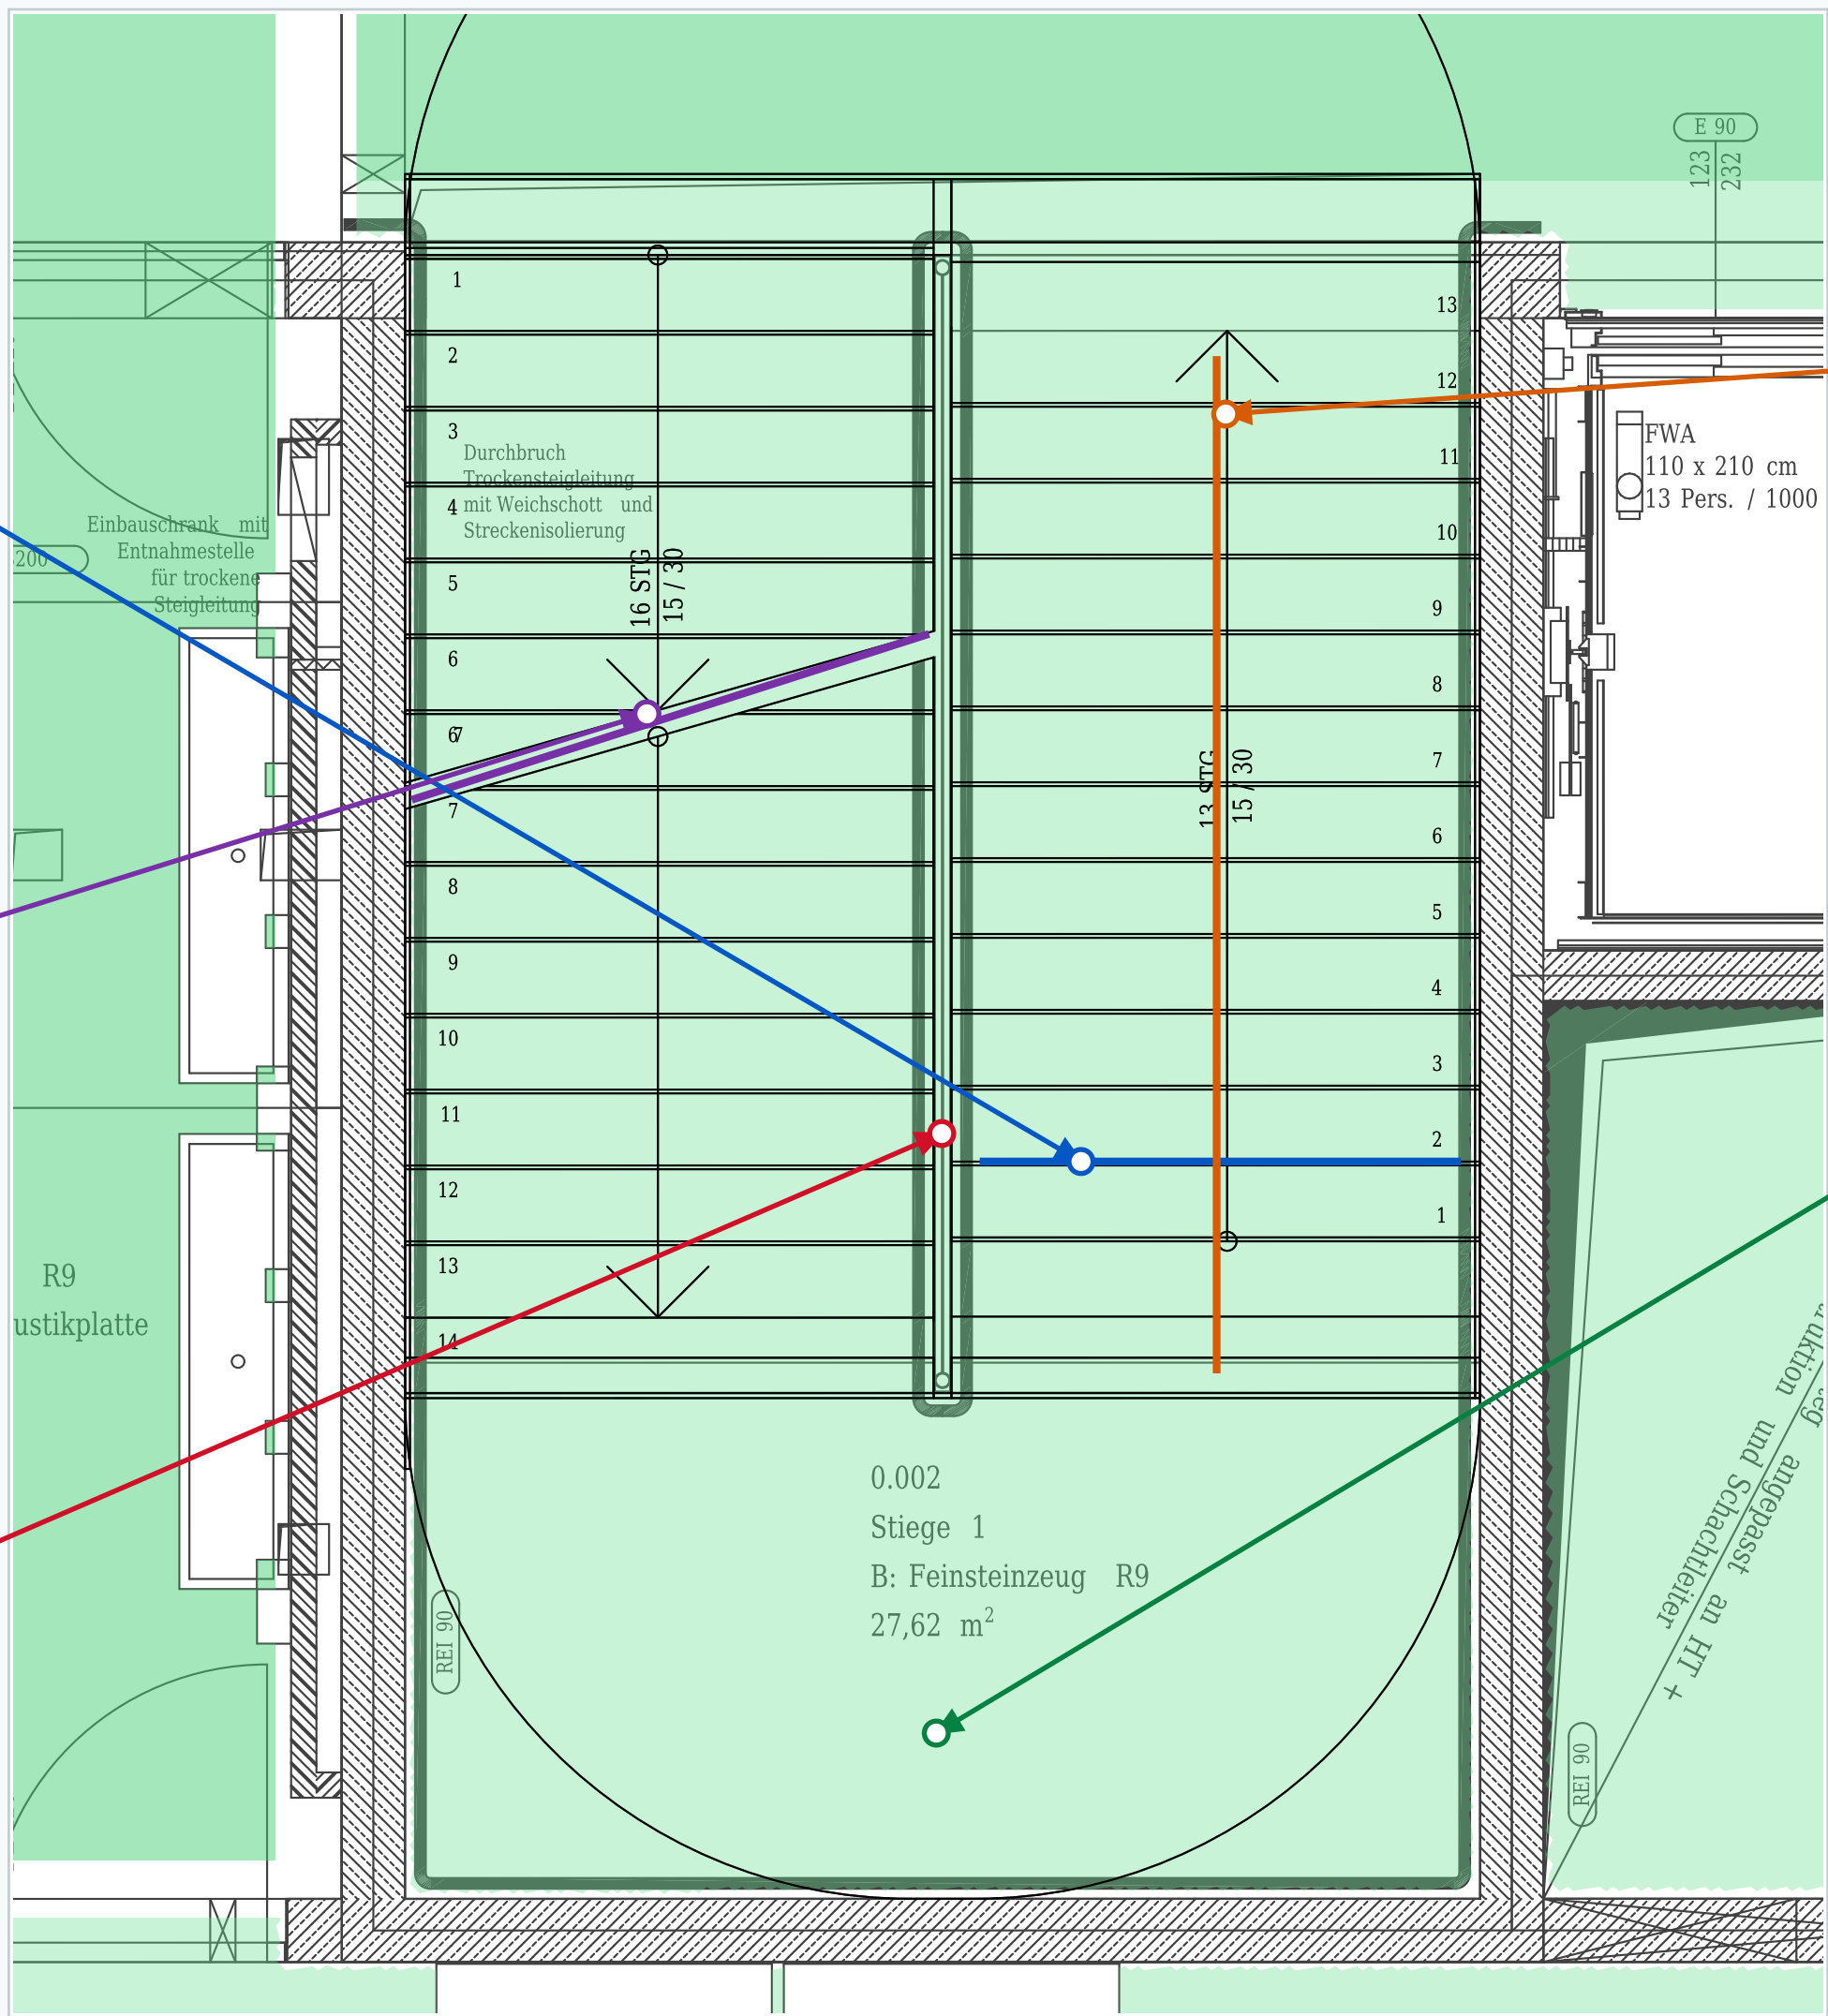

Rahmen: erklärter Bereich. Farblinien: Originalmerkmale. Pfeile: Zuordnung.


EG-21 | Originalausschnitt mit direkt zugeordneten Merkmalen

Stufenfolge

Querlinien werden
fortlaufend
nummeriert.

Bruchlinie

Schräger Strich unterbricht Darstellung.

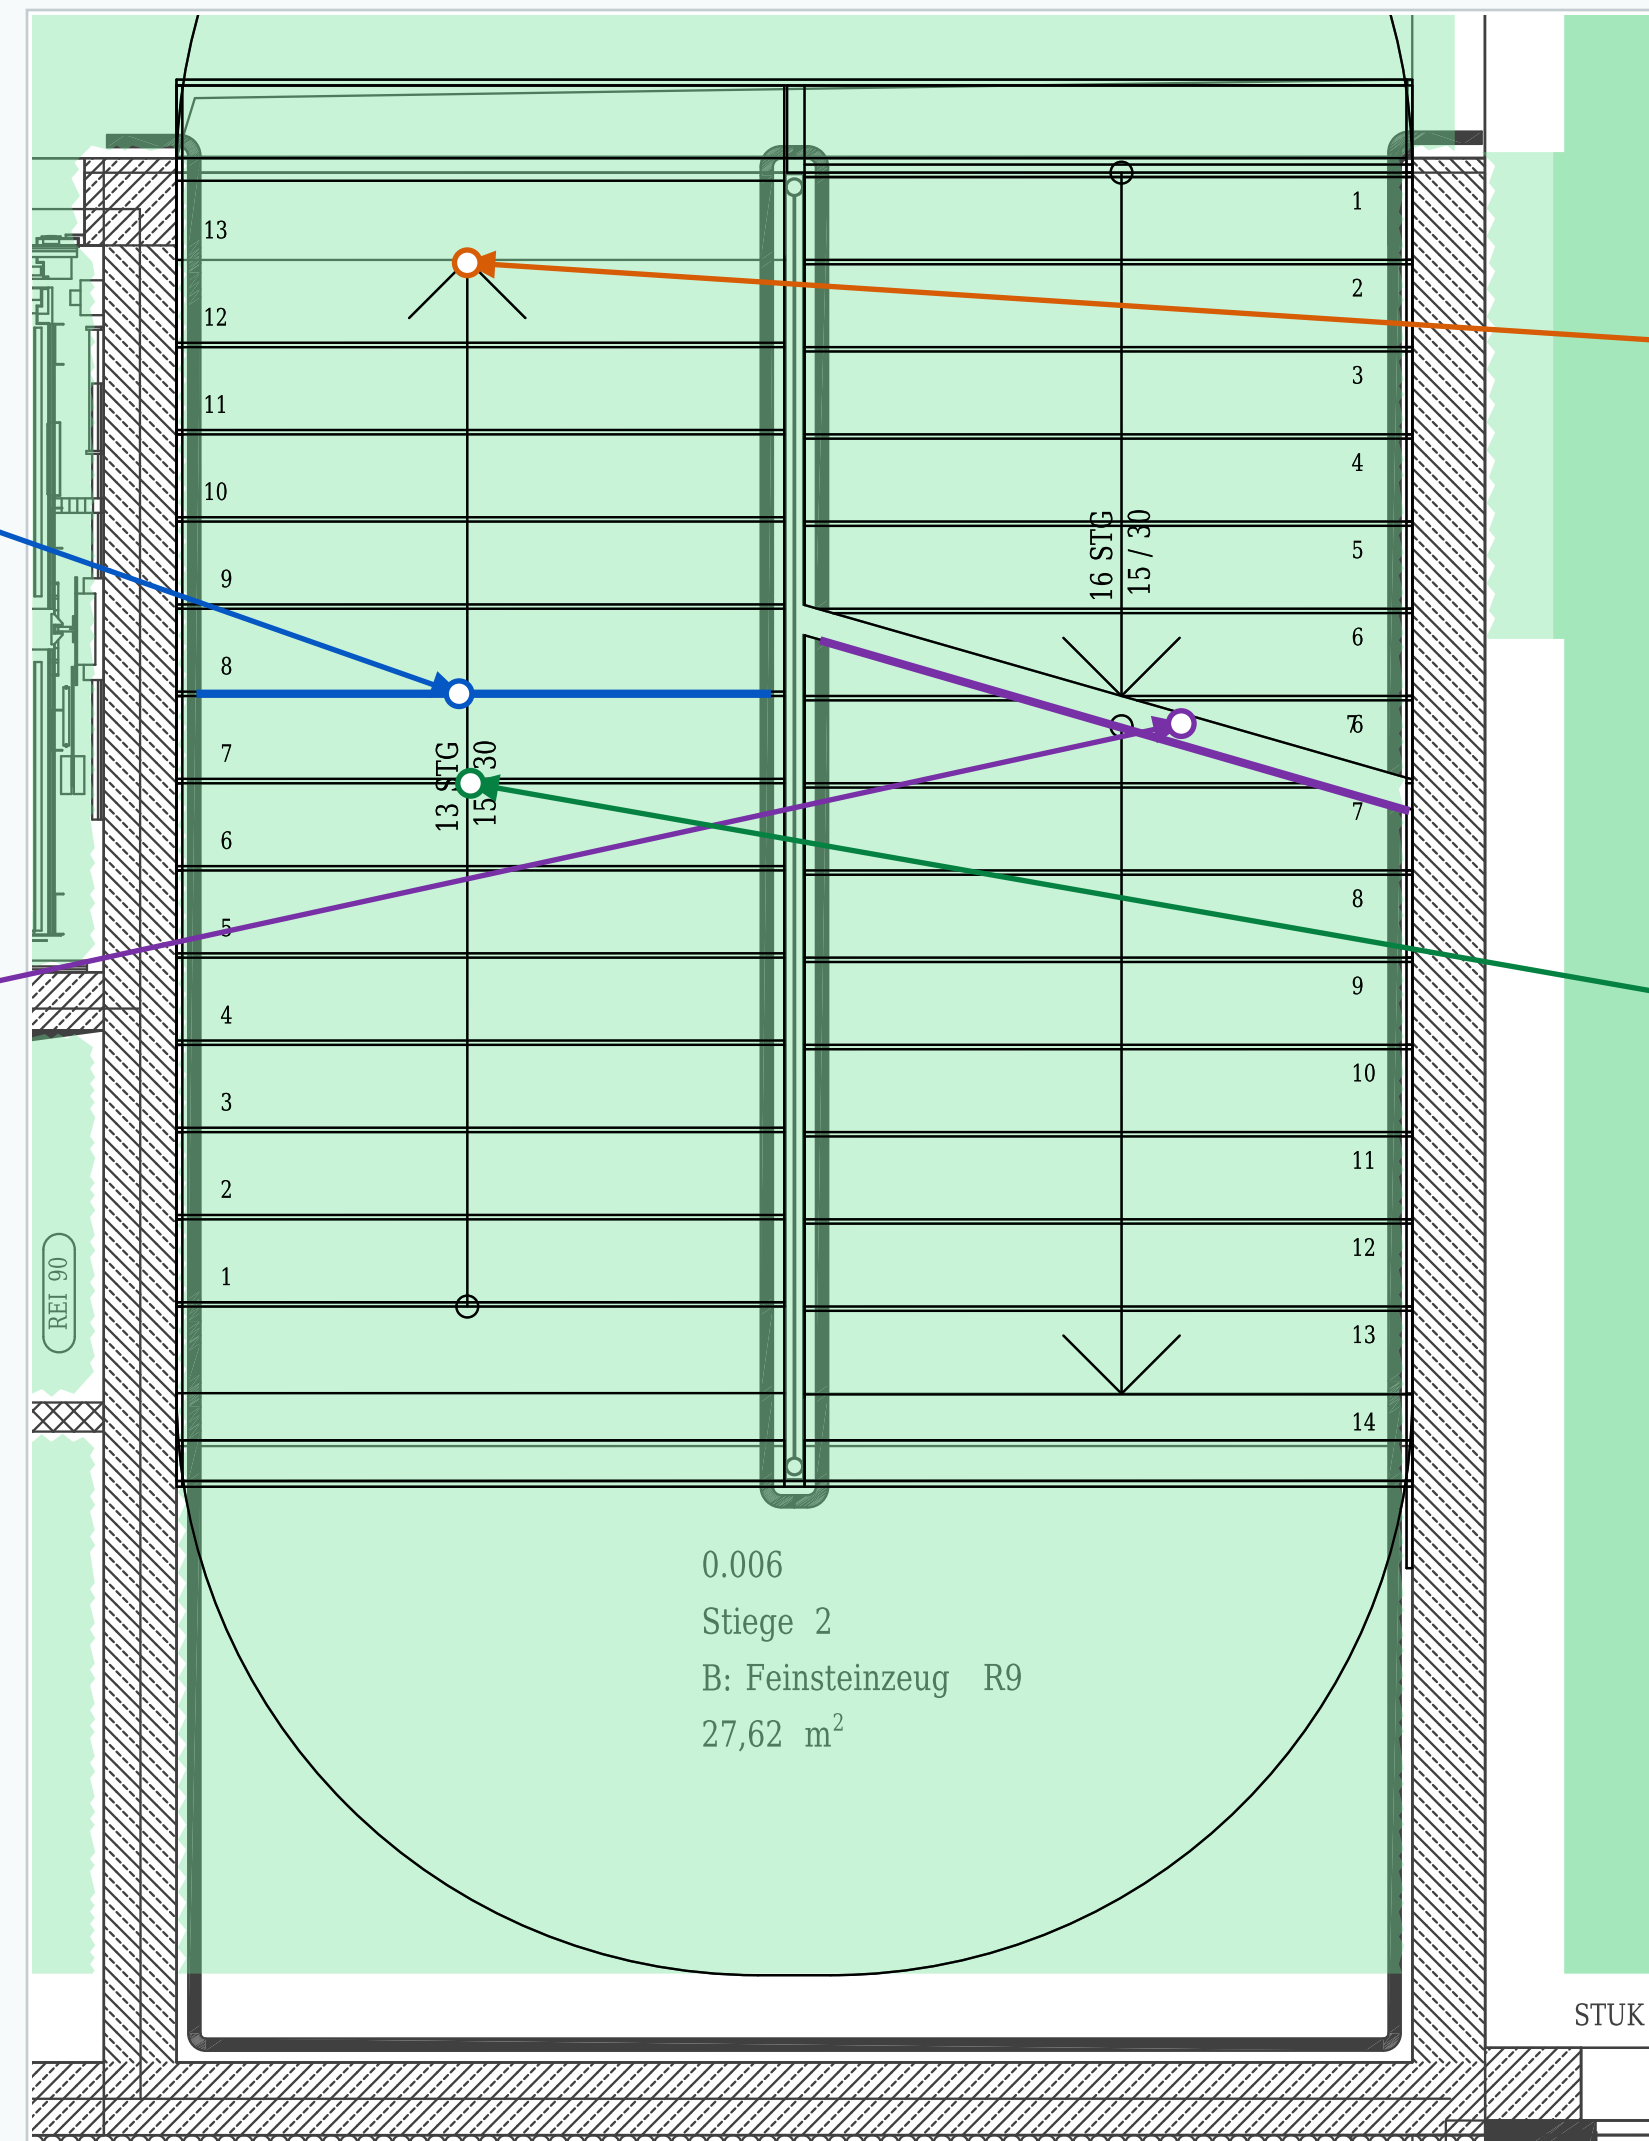

Pfeilsymbol

Richtung aus
Konvention und
Höhen prüfen.

Laufmaß

13 STG 15/30: Steigungen und Auftritt.

Rahmen: erklärter Bereich. Farblinien: Originalmerkmale. Pfeile: Zuordnung.

EG-22 | Originalausschnitt mit direkt zugeordneten Merkmalen

Treppenlauf

Regelmäßige
Querlinien plus
Nummern.

19 STG 16,2/27


19 Steigungen;
Maße gesondert
prüfen.

Laufpfeil

Pfeilspitze unten
auf dem Blatt.

Podest / Zugang

Boden vor der
Außentür.

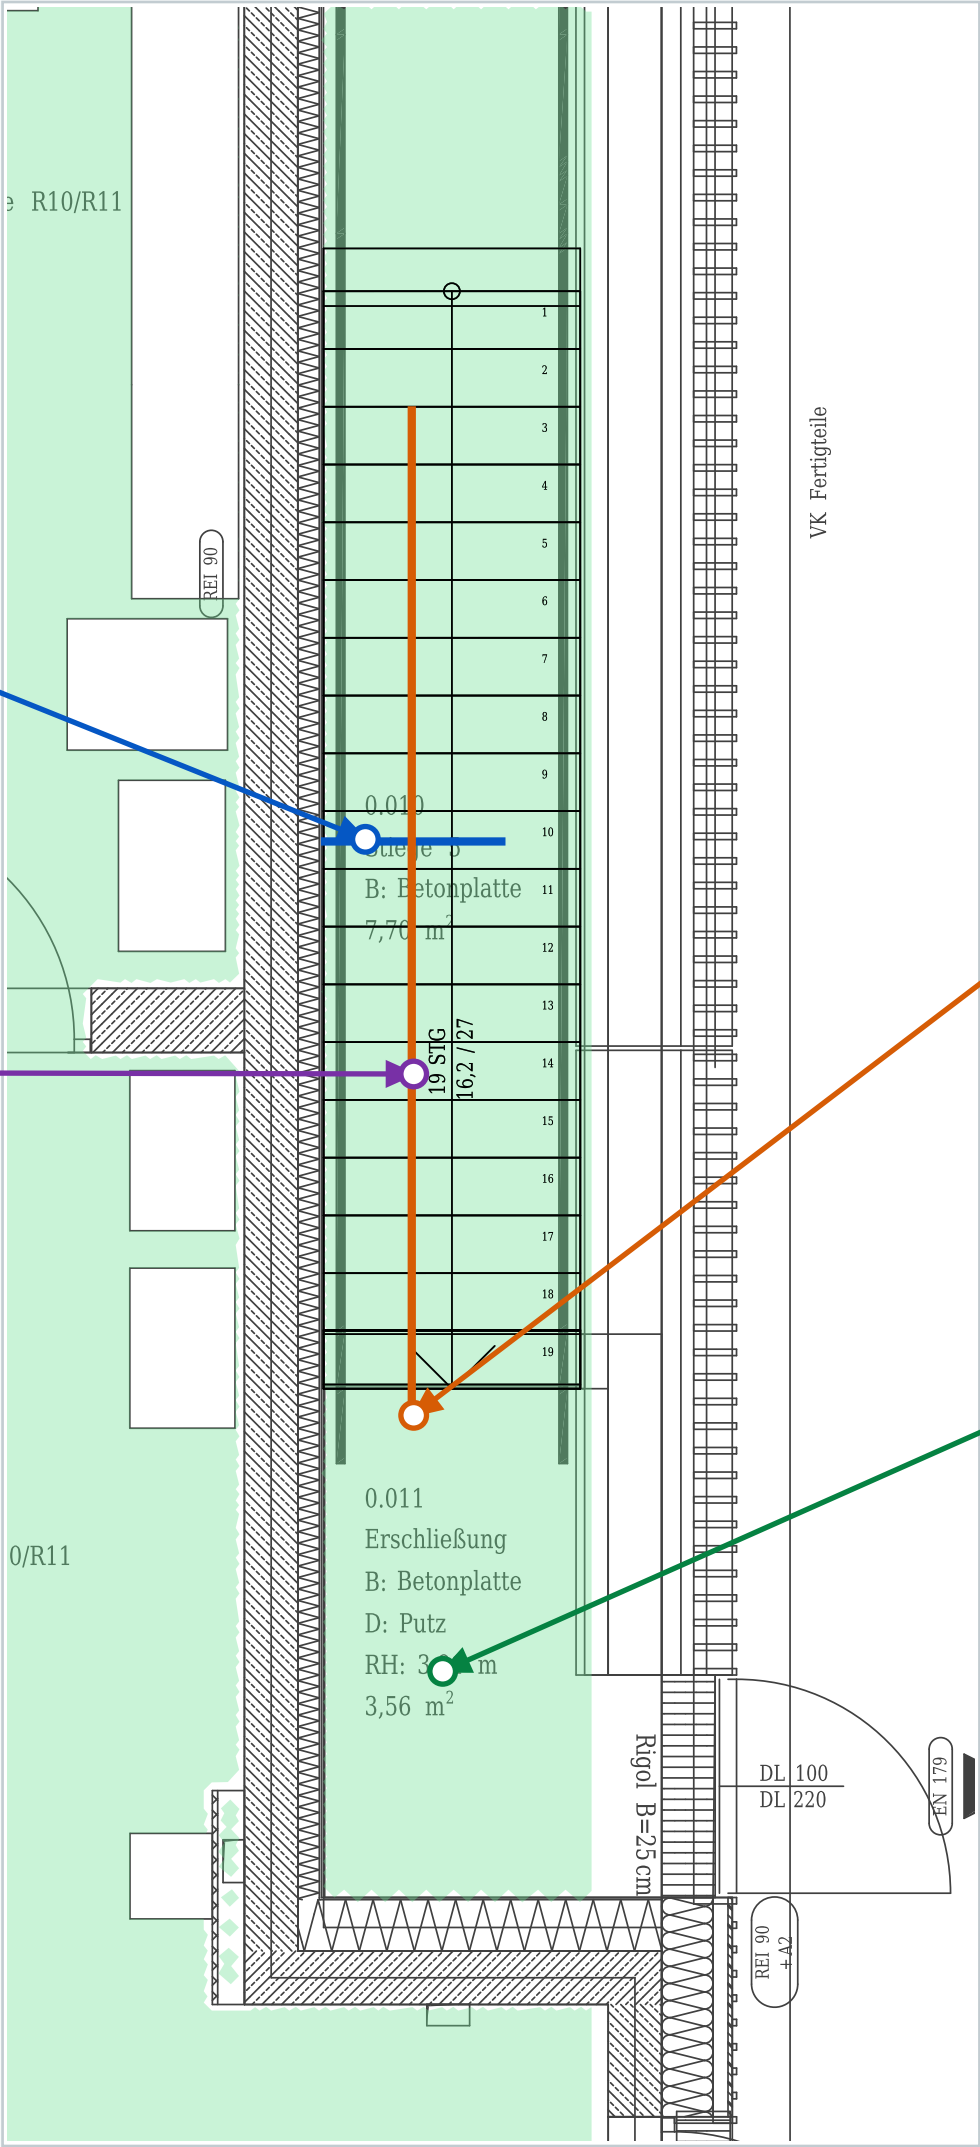

EG-23 | Originalausschnitt mit direkt zugeordneten Merkmalen

Stufen

Wiederholte
schwarze
Querlinien.

Getrennter Lauf


Eigene Anlage
Stiege 6.

Pfeilspitze

Blatt-unten
bedeutet nicht
automatisch ab.

Bodenanschluss

Kleiner Bereich vor
dem Ausgang.

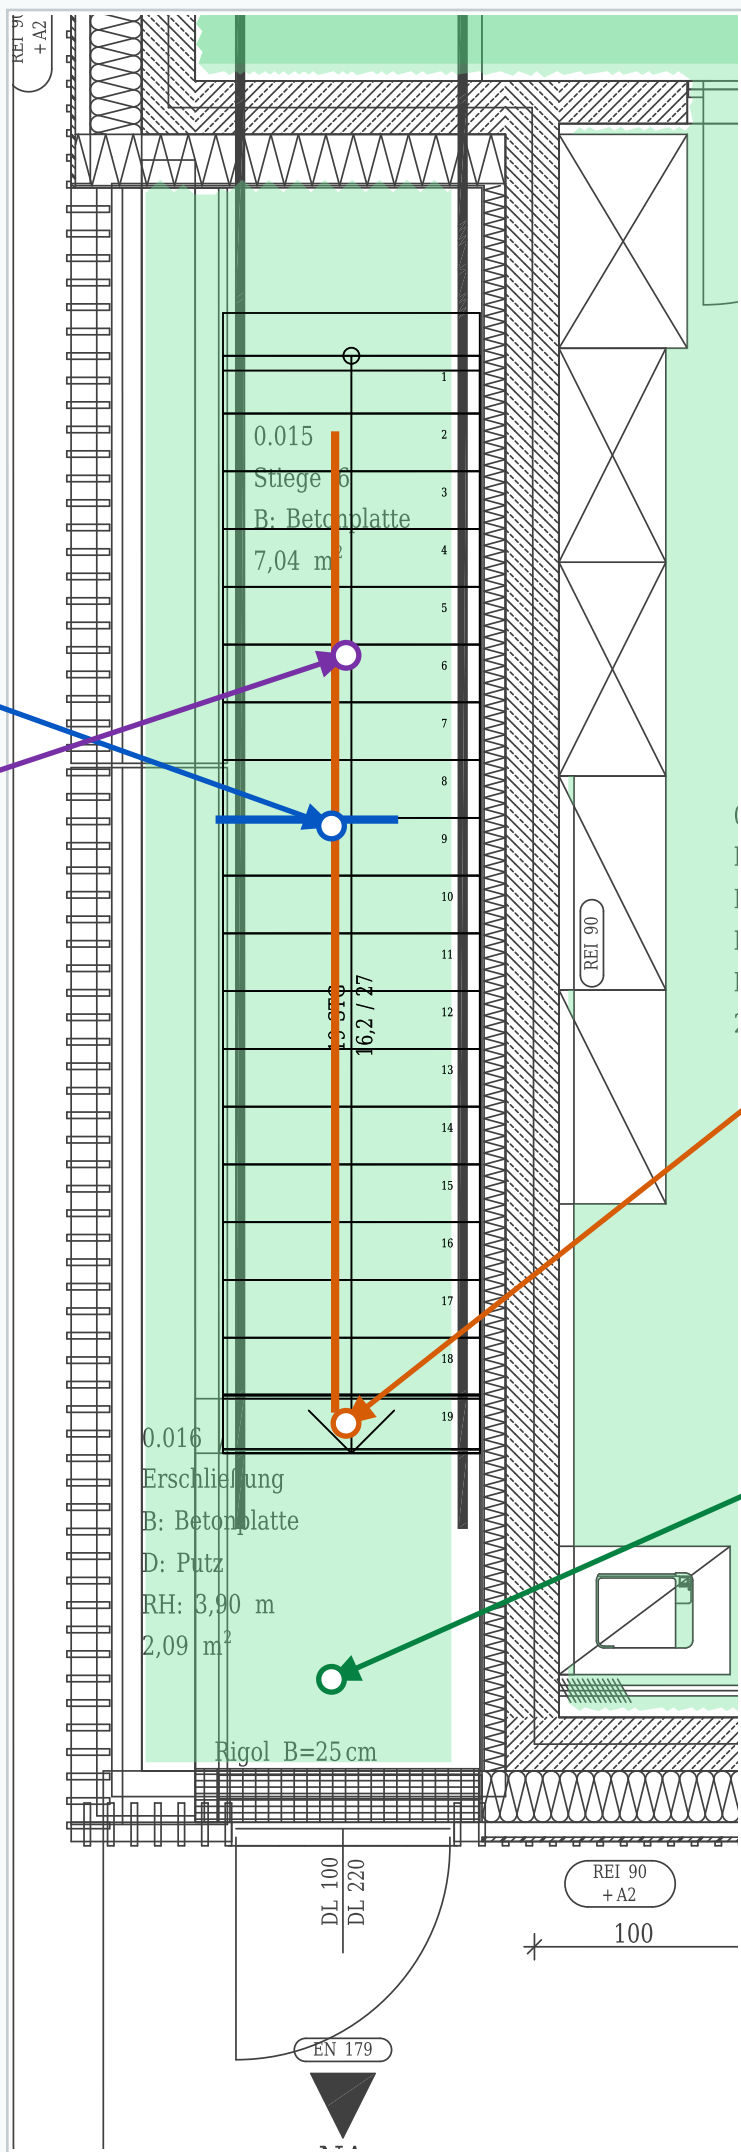

Rahmen: erklärter Bereich. Farblinien: Originalmerkmale. Pfeile: Zuordnung.

EG-24 | Originalausschnitt mit direkt zugeordneten Merkmalen

Querlinien

Außenlauf aus vielen Stufenkanten.

Pfeil


Lauflinie längs durch die Stufen.

Darstellungsbruch

Schräge Linien sind keine Sperrwand.

Unterlaufschutz

Beschrifteten Schutzbereich beachten.

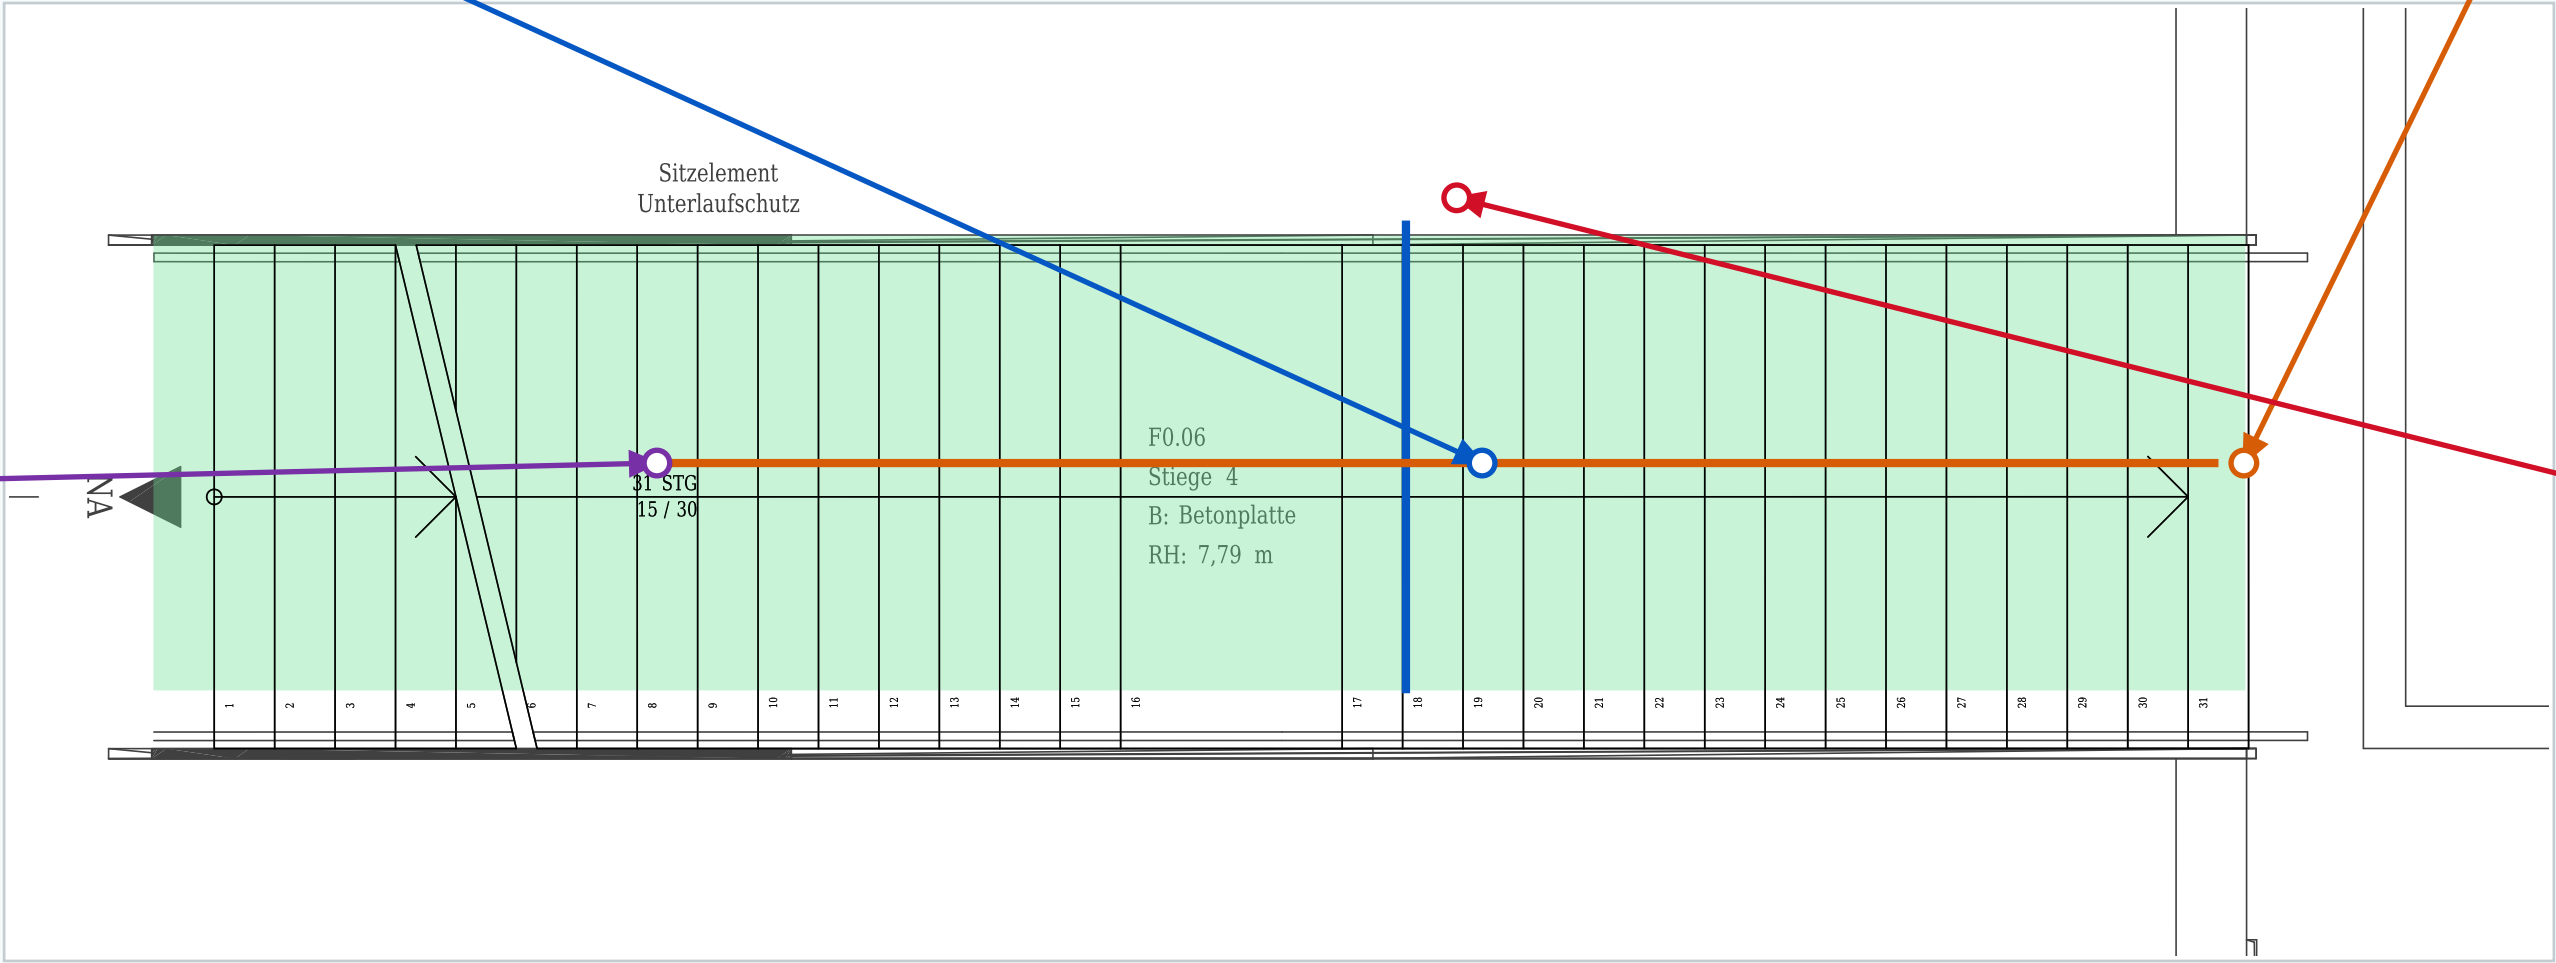

Rahmen: erklärter Bereich. Farblinien: Originalmerkmale. Pfeile: Zuordnung.

EG-25 | Originalausschnitt mit direkt zugeordneten Merkmalen

Stufenkanten

Schwarze Linien bleiben über Grün sichtbar.

Lauflinie


Symbolachse entlang der Treppe.

Bruch

Darstellung wechselt an schrägen Linien.

NA ist lokal

Kennzeichnet hier den Ausgangsbezug.

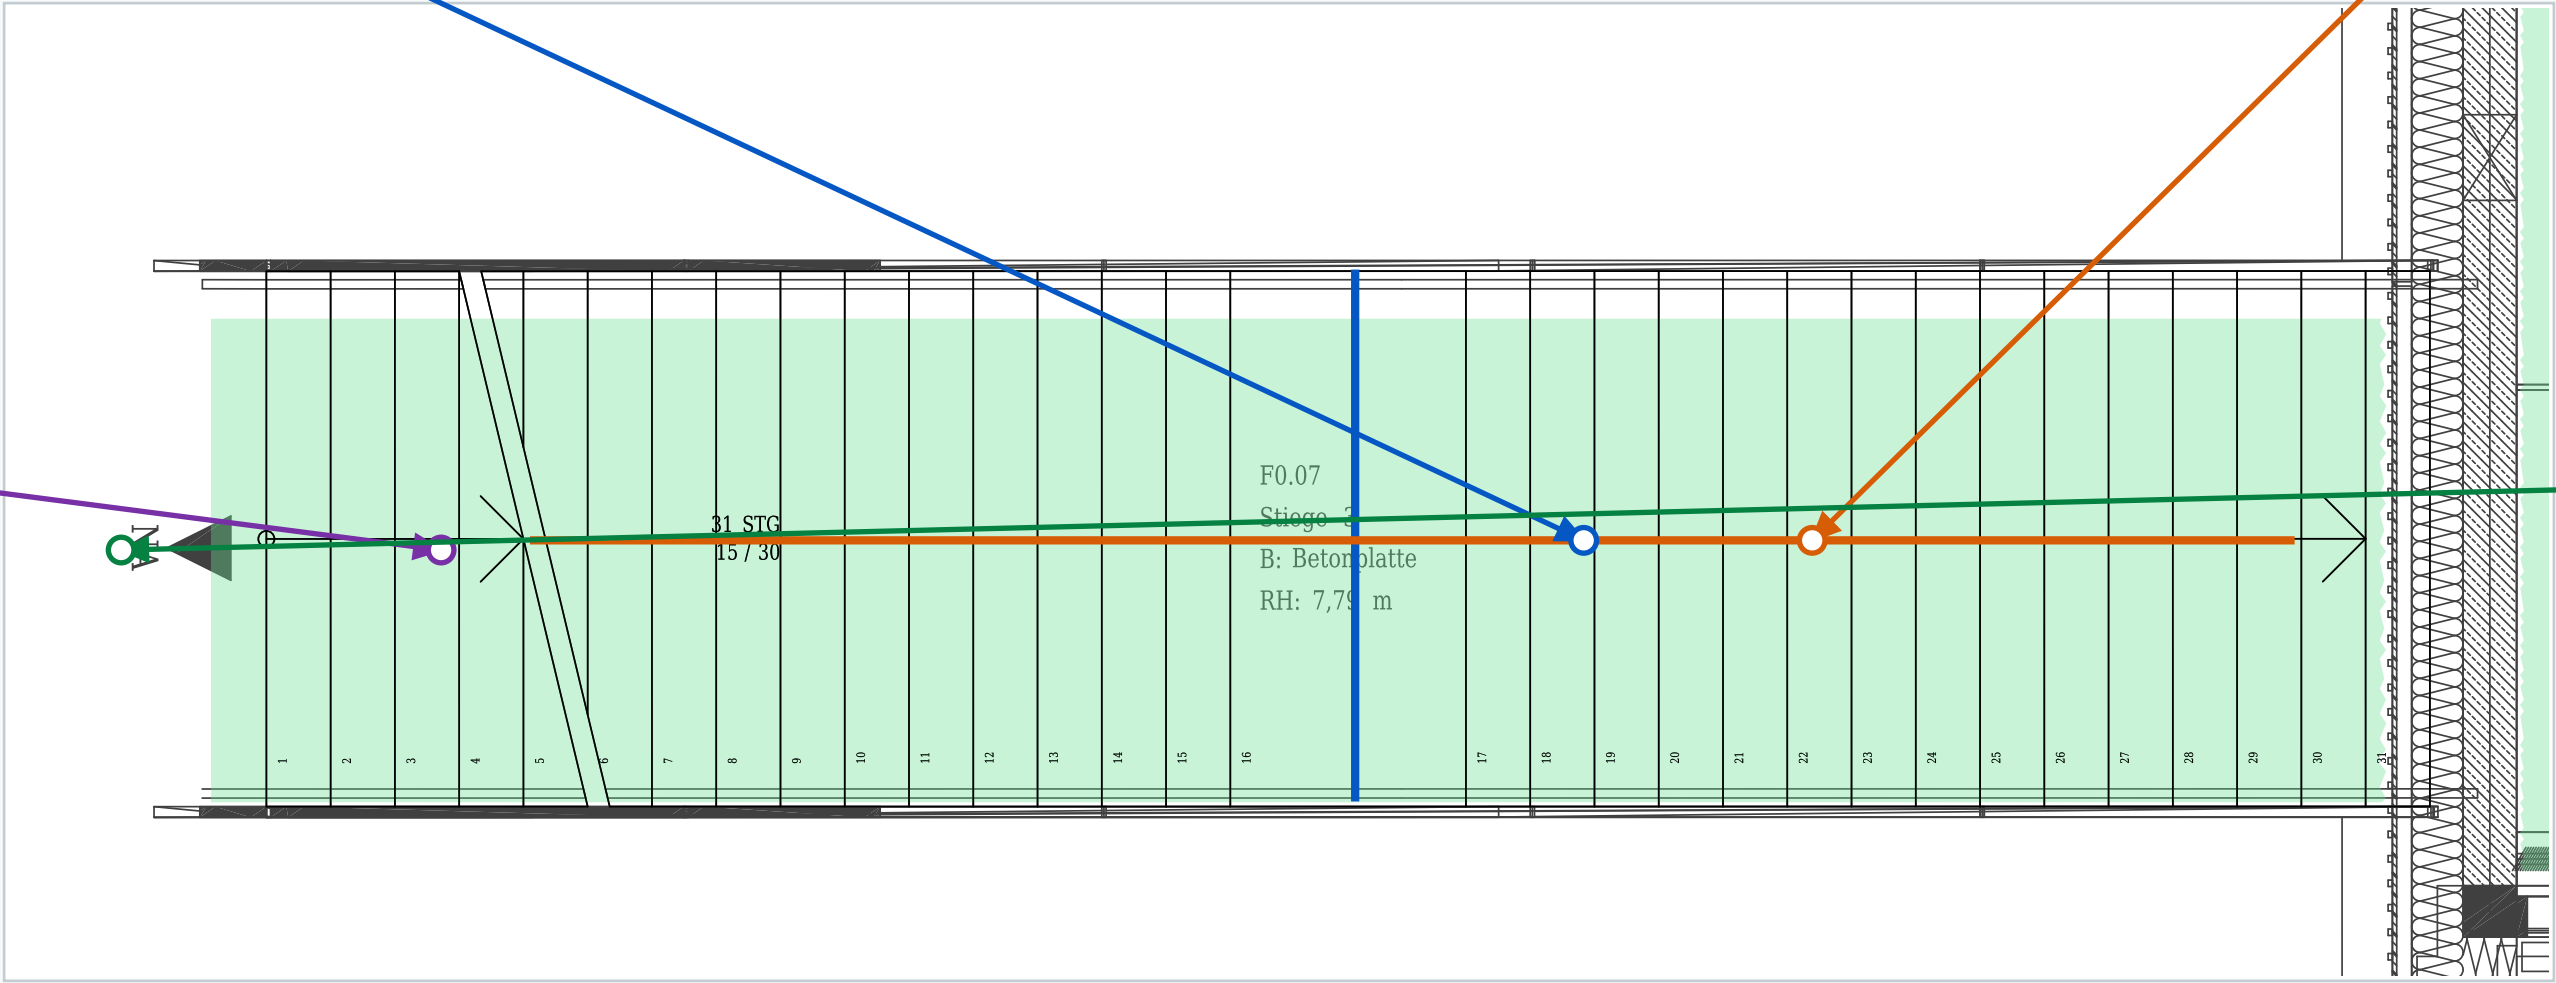

EG-26 | Originalausschnitt mit direkt zugeordneten Merkmalen

Türportal

Außenverbindung
an dieser Öffnung.

NA-Symbol


Kennzeichnung
neben dem
Ausgang.

Fassadenabschluss


Glasfelder daneben
sind keine Türen.

Außenweg offen

Weiterführung
braucht einen
Lageplan.

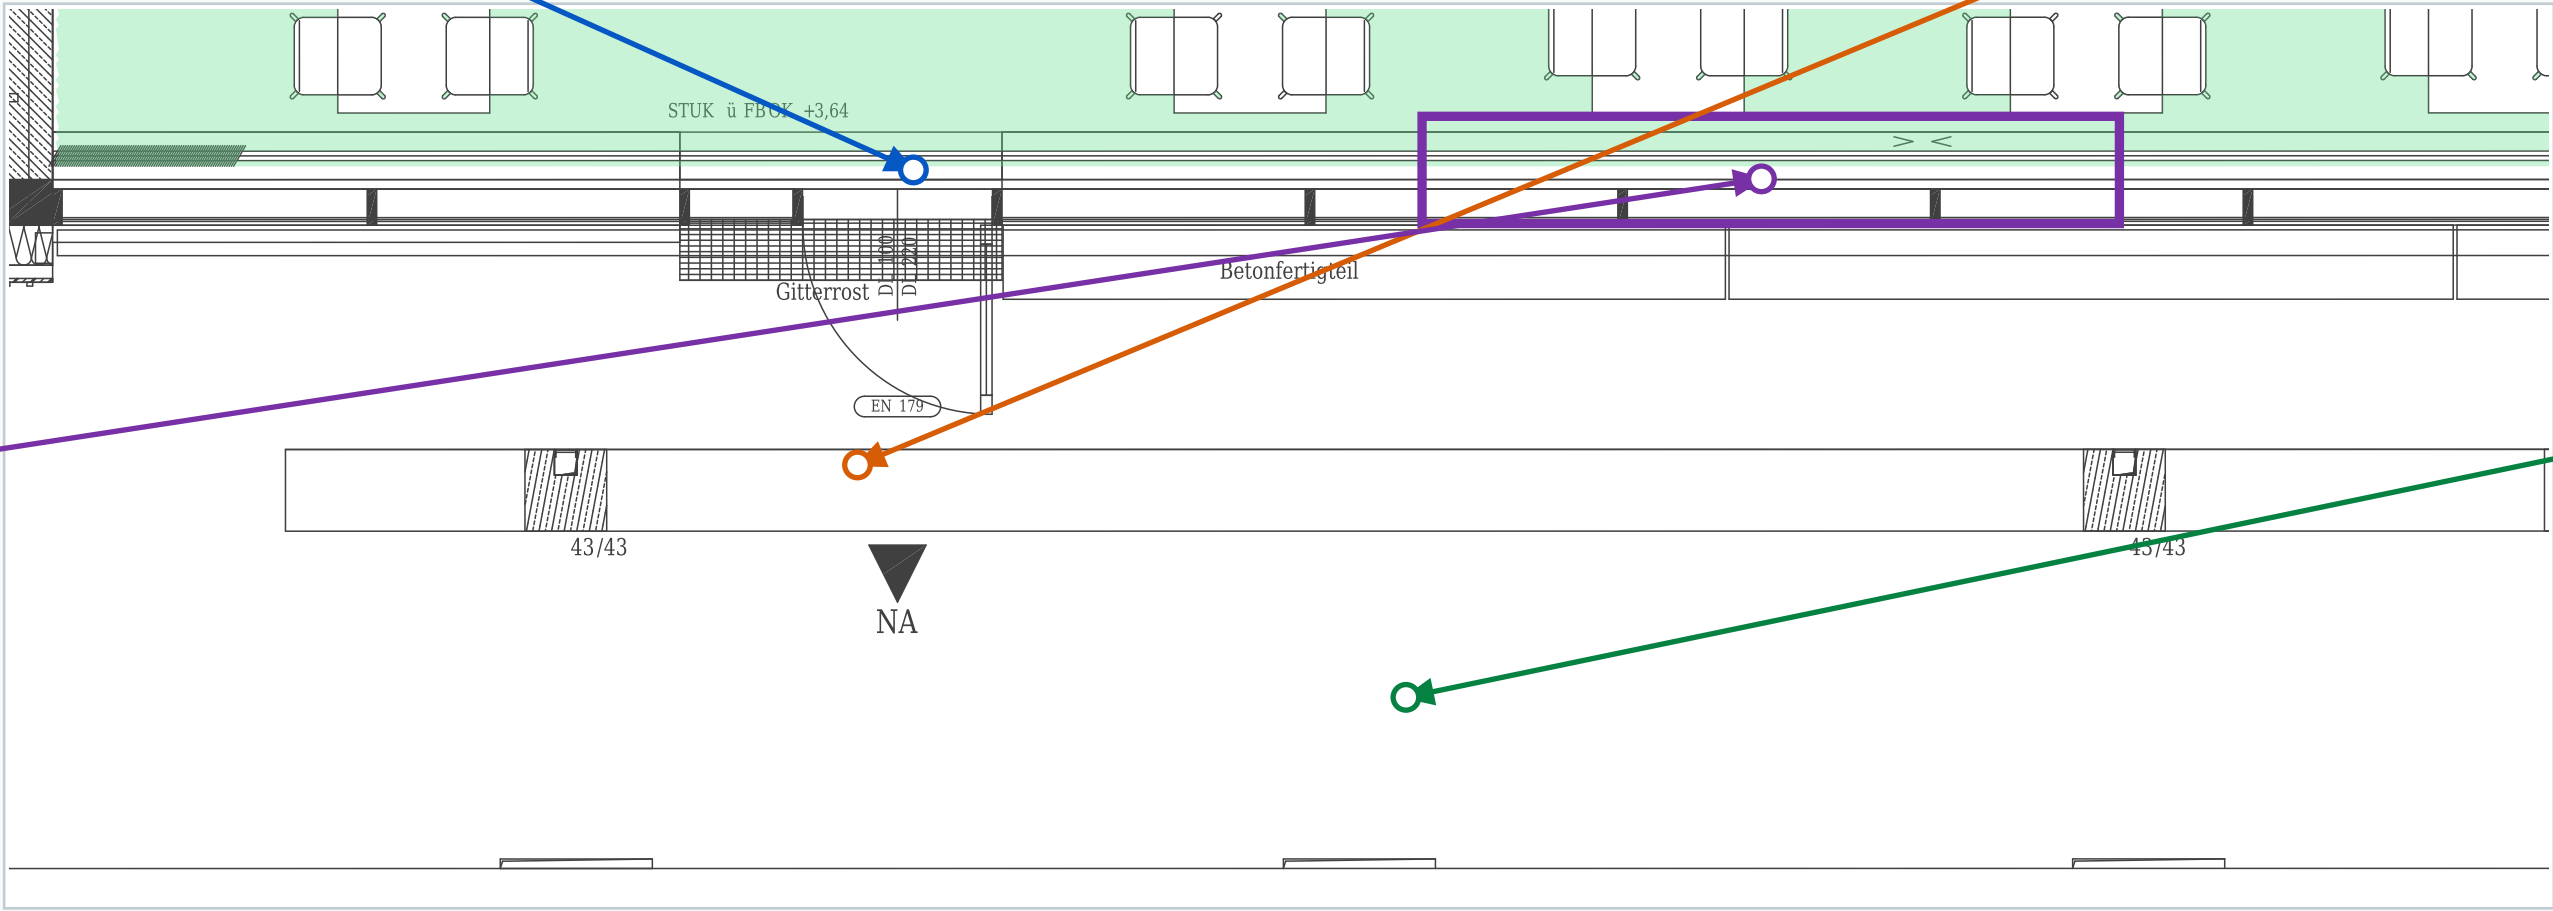

EG-27 | Originalausschnitt mit direkt zugeordneten Merkmalen

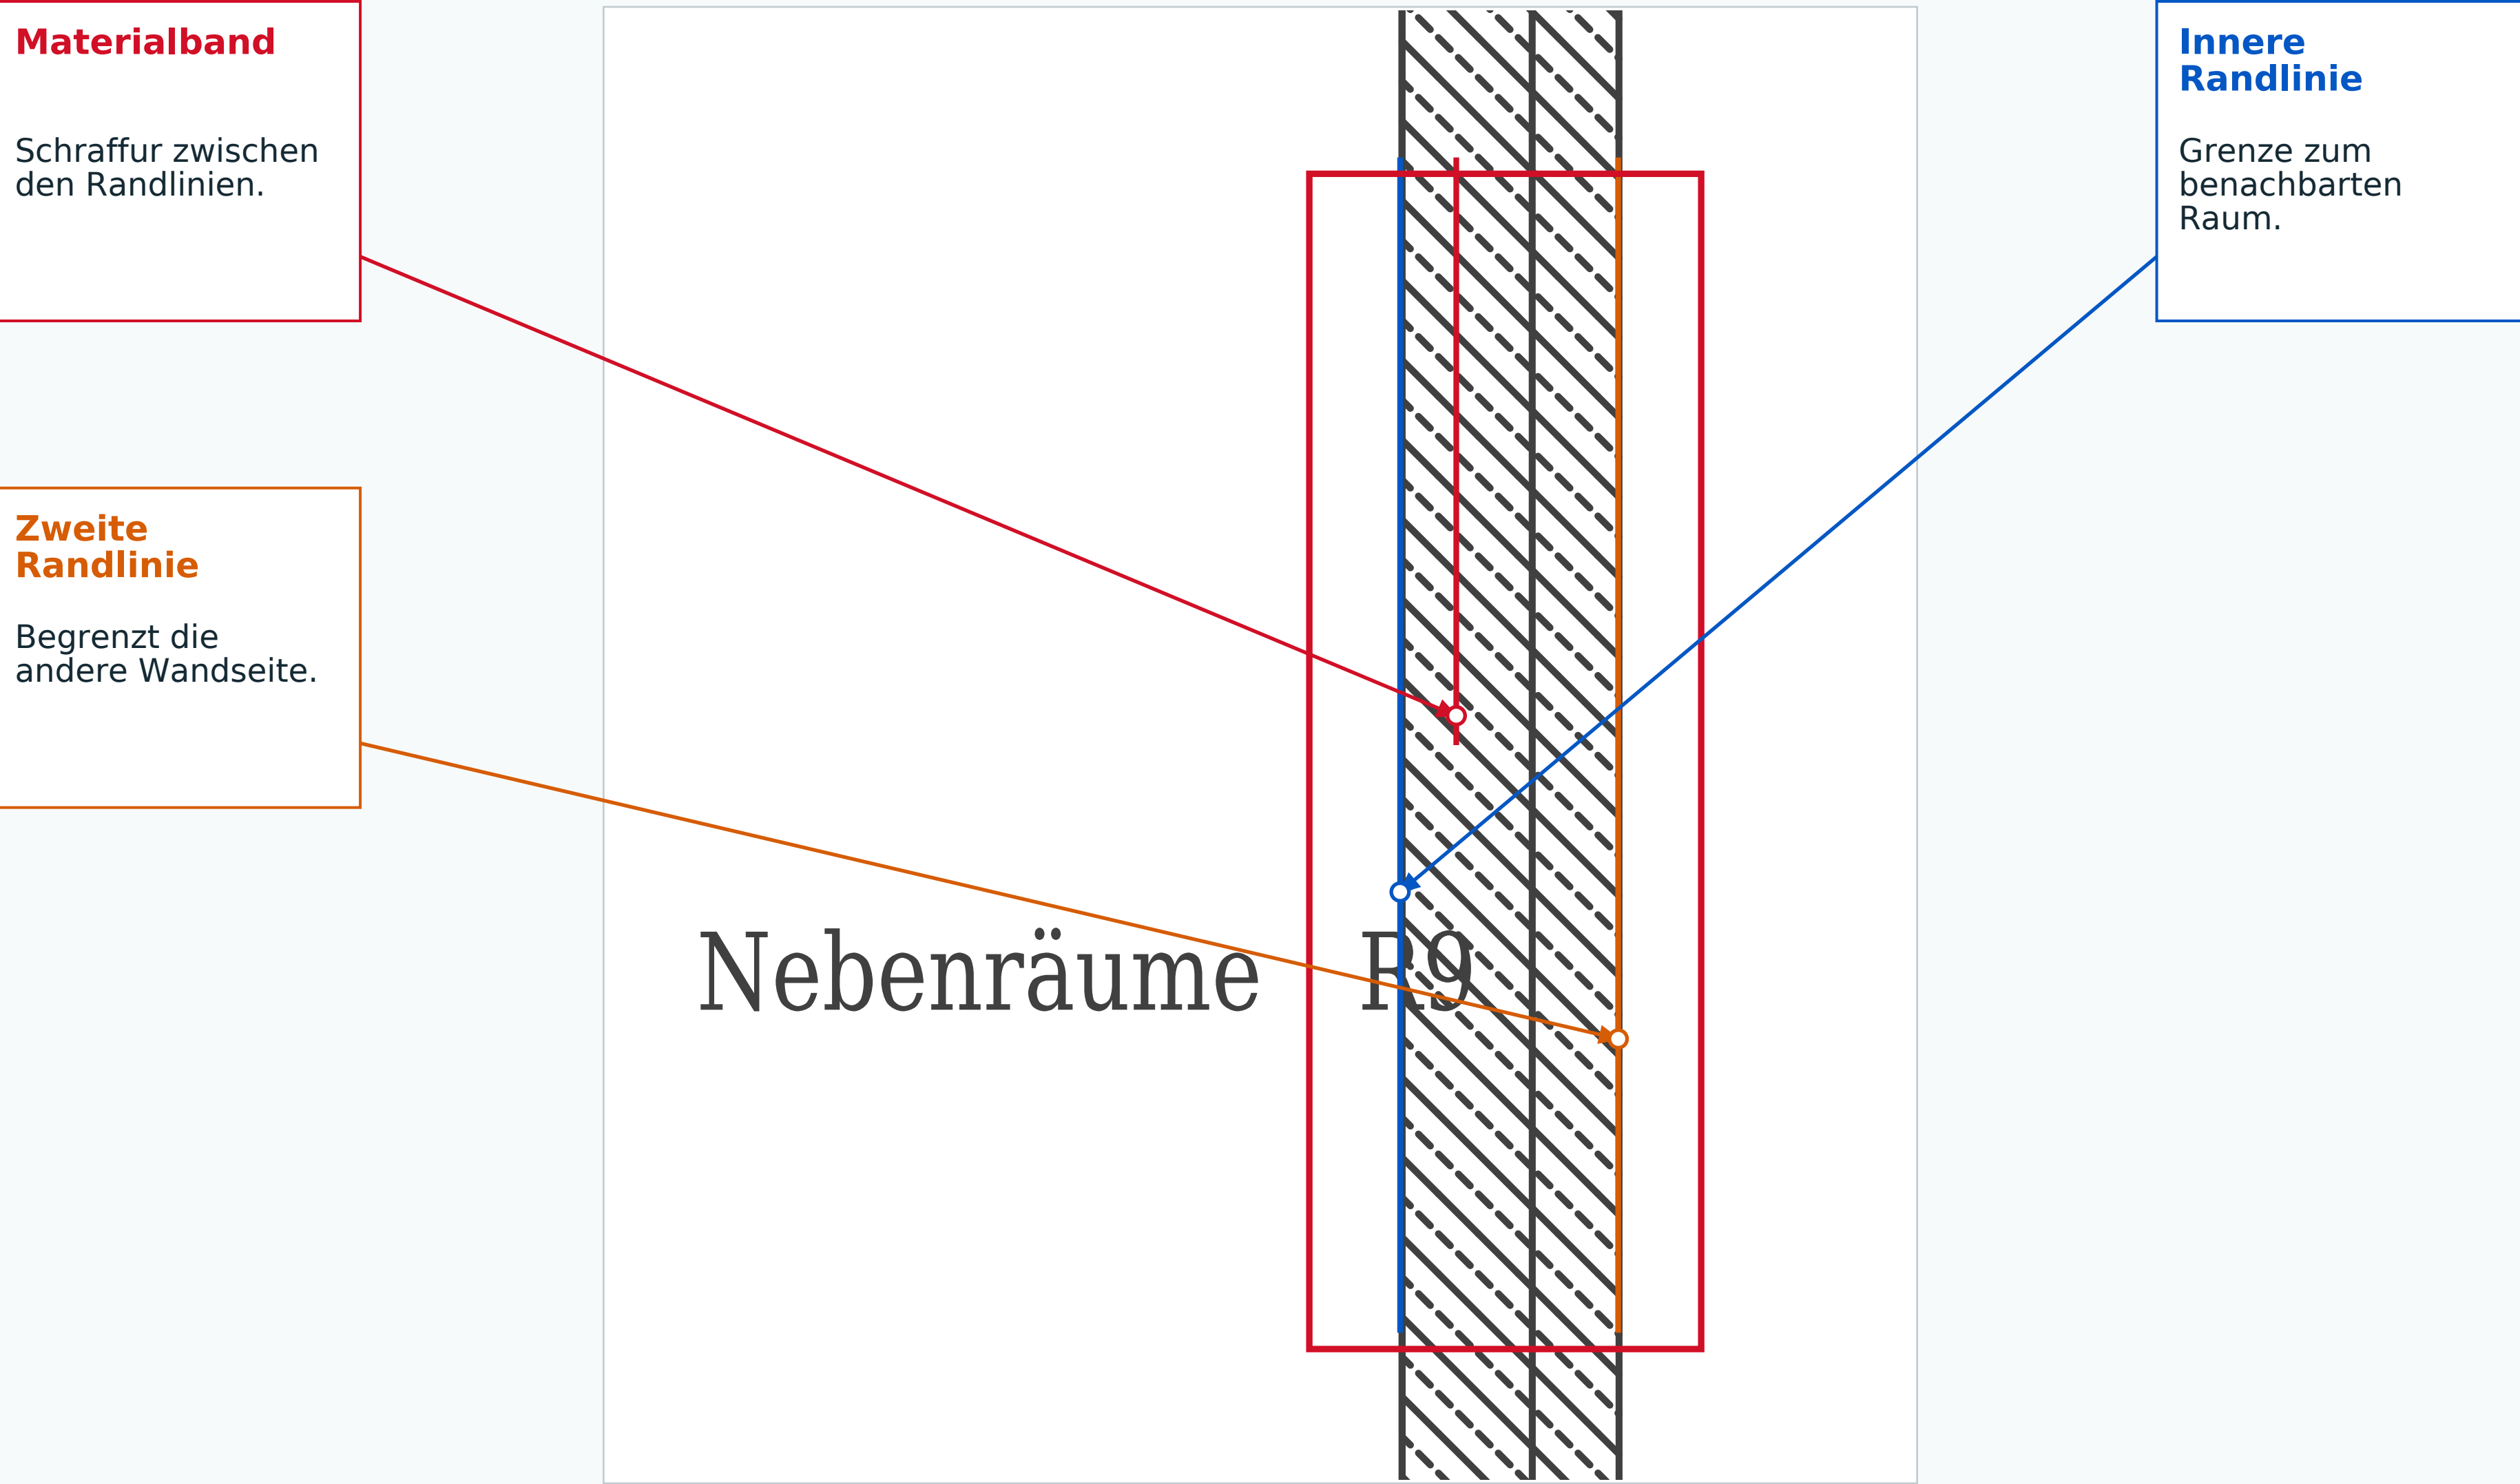

Rahmen: erklärter Bereich. Farblinien: Originalmerkmale. Pfeile: Zuordnung.

EG-28 | Originalausschnitt mit direkt zugeordneten Merkmalen

