Erdgeschoss

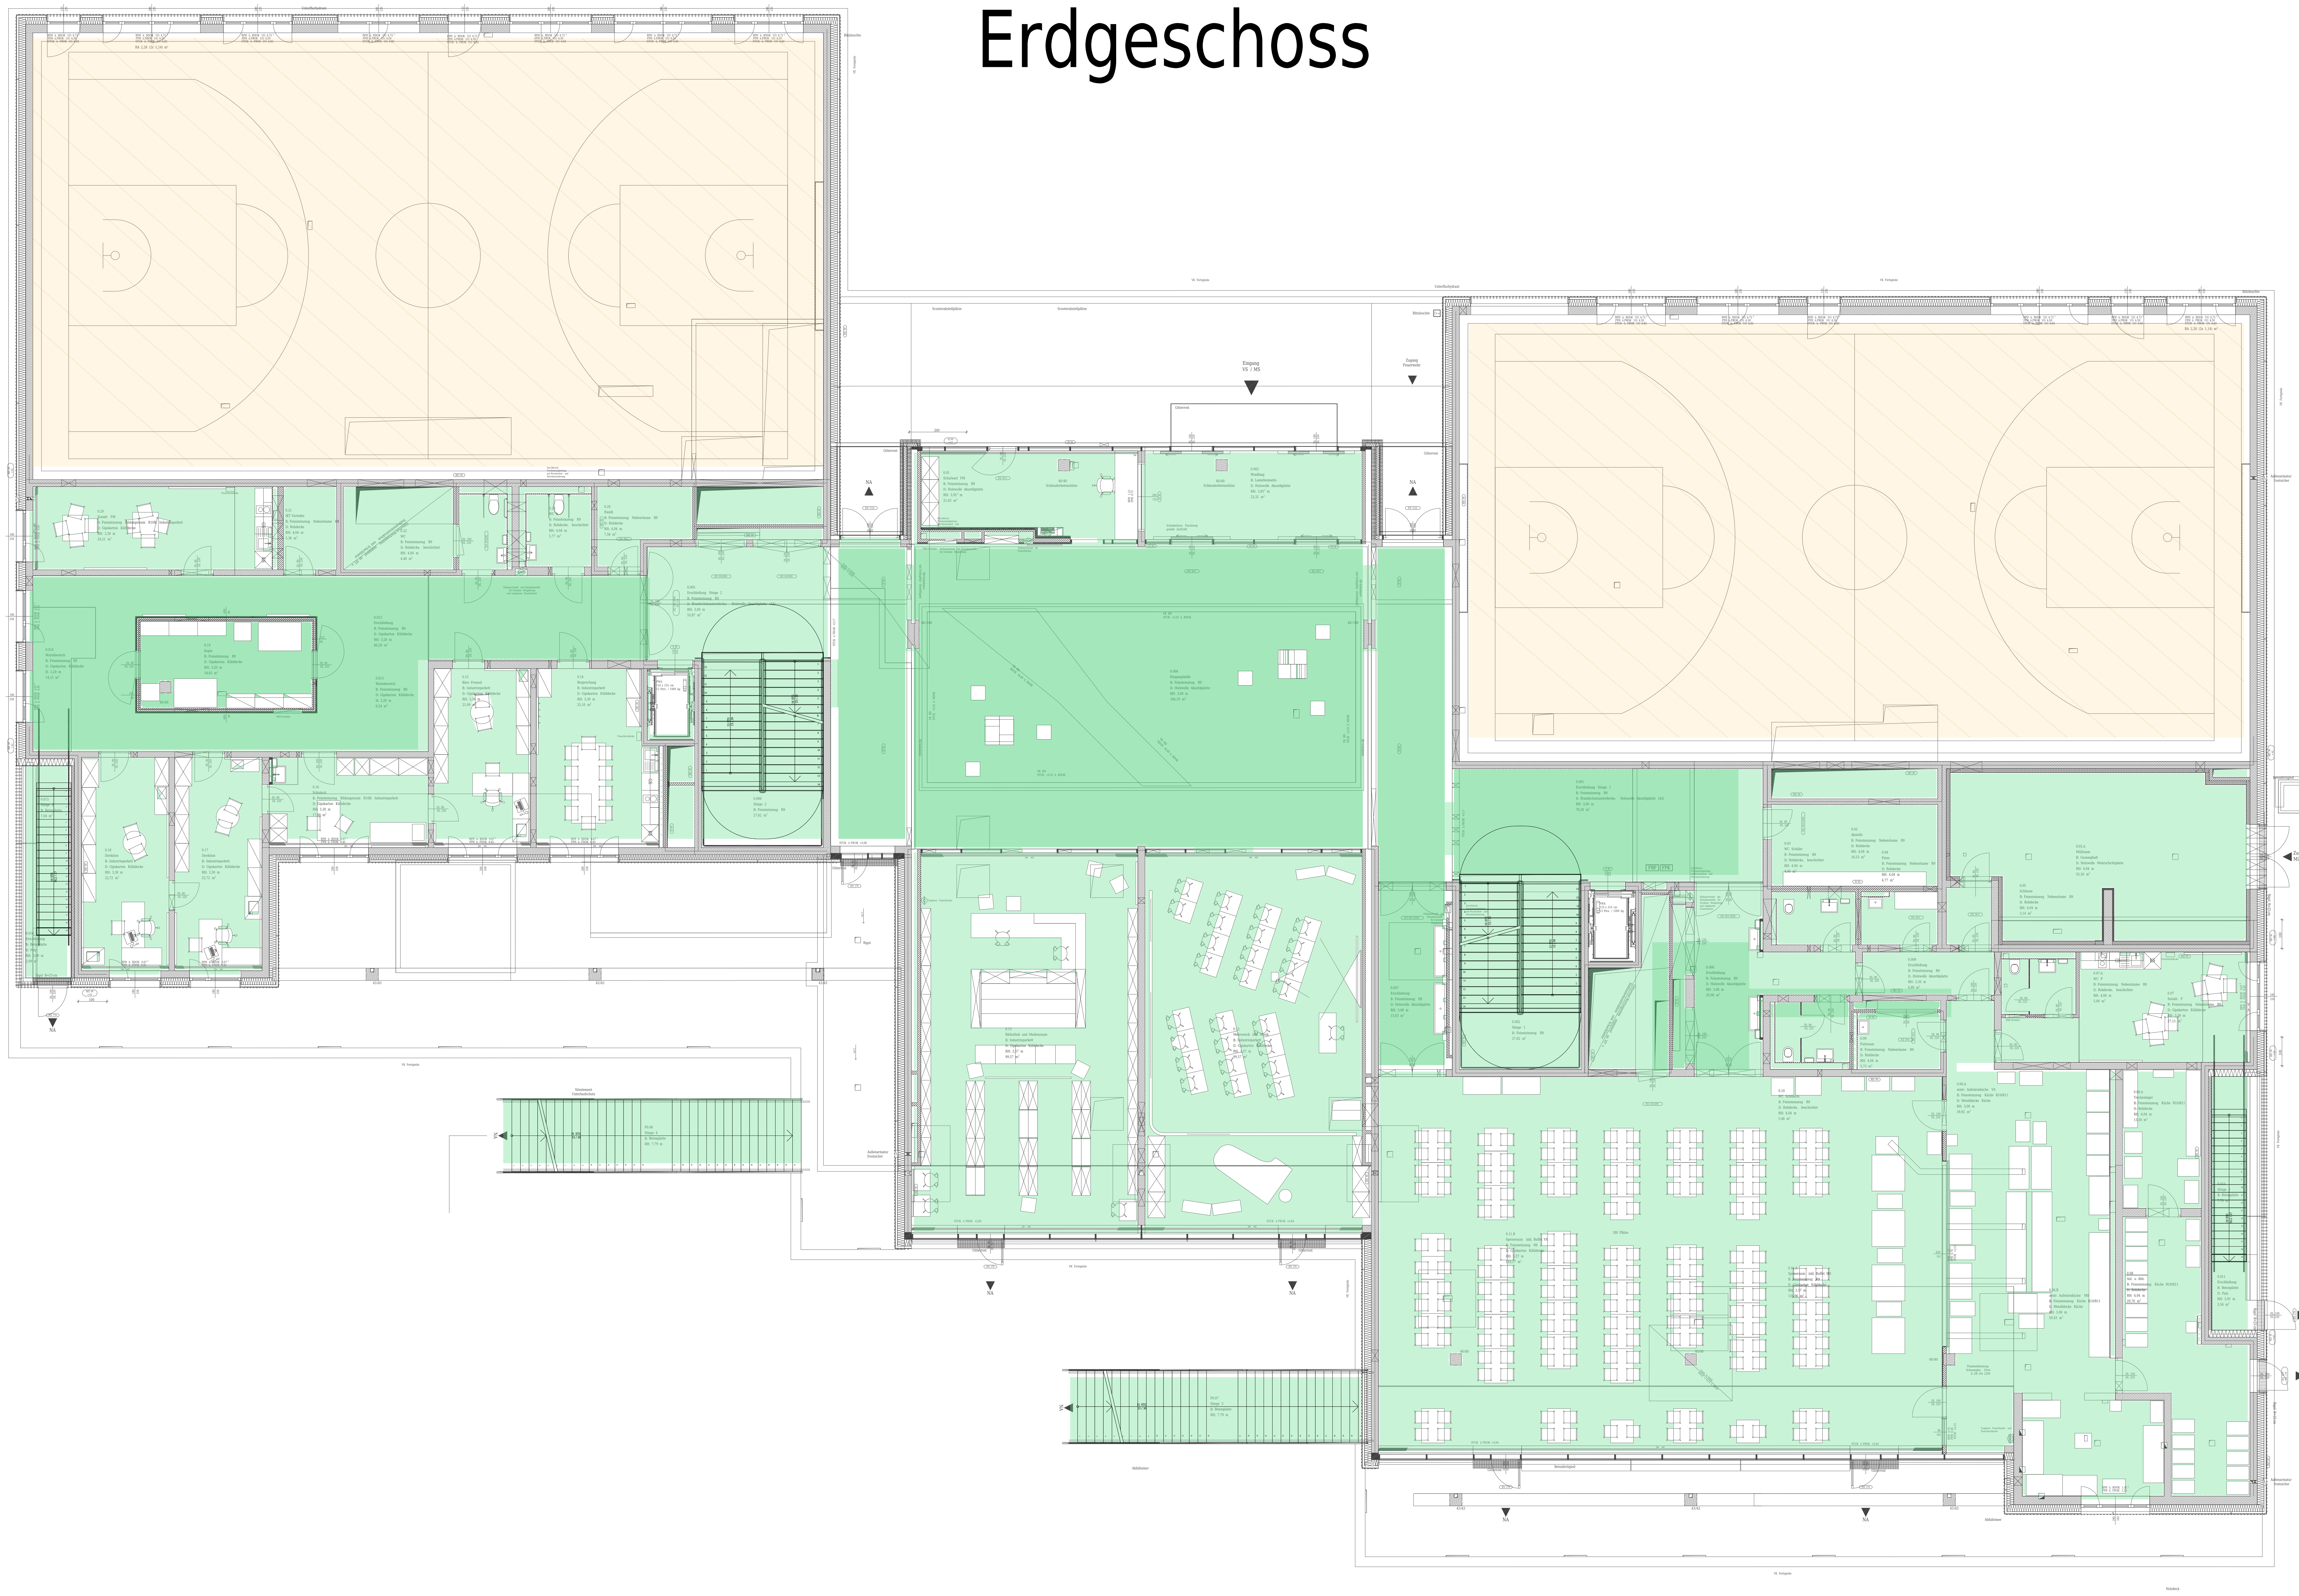
Unterflurhydrant
Blitzleuchte
VK Fertigteile
RA 2,28 (2x 1,14) m²
Scooterabstellplätze
Eingang VS / MS
Zugang Feuerwehr
Gitterrost
NA
0.20 Sozialr. FM B: Feinsteinzeug Bildungsraum R10B; Industrieparkett D: Gipskarton Kühldecke RH: 3,30 m 24,21 m²
0.21 IKT Verteiler B: Feinsteinzeug Nebenräume R9 D: Rohdecke RH: 4,04 m 3,36 m²
0.22 WC B: Feinsteinzeug R9 D: Rohdecke, beschichtet RH: 4,04 m 4,40 m²
0.23 WC B: Feinsteinzeug R9 D: Rohdecke, beschichtet RH: 4,04 m 5,77 m²
0.24 Handl. B: Feinsteinzeug Nebenräume R9 D: Rohdecke RH: 4,04 m 7,58 m²
0.014 Wartebereich B: Feinsteinzeug R9 D: Gipskarton Kühldecke H: 3,20 m 14,15 m²
0.19 Kopie B: Feinsteinzeug R9 D: Gipskarton Kühldecke RH: 3,20 m 18,02 m²
0.012 Erschließung B: Feinsteinzeug R9 D: Gipskarton Kühldecke RH: 3,20 m 66,29 m²
0.013 Wartebereich B: Feinsteinzeug R9 D: Gipskarton Kühldecke H: 3,20 m 6,34 m²
0.15 Büro Freizeit B: Industrieparkett D: Gipskarton Kühldecke RH: 3,30 m 21,09 m²
0.14 Besprechung B: Industrieparkett D: Gipskarton Kühldecke RH: 3,30 m 25,10 m²
0.015 Stiege 4 B: Betonplatte 7,04 m²
0.016 Erschließung B: Betonplatte D: Putz RH: 3,90 m 2,09 m²
0.18 Direktion B: Industrieparkett D: Gipskarton Kühldecke RH: 3,30 m 22,72 m²
0.17 Direktion B: Industrieparkett D: Gipskarton Kühldecke RH: 3,30 m 22,72 m²
0.16 Schularzt B: Feinsteinzeug Bildungsraum R10B; Industrieparkett D: Gipskarton Kühldecke RH: 3,30 m 17,85 m²
0.005 Erschließung Stiege 2 B: Feinsteinzeug R9 D: Brandschutzunterdecke; Holzwolle Akustikplatte (A2) RH: 3,00 m 55,87 m²
0.006 Stiege 2 B: Feinsteinzeug R9 27,62 m²
0.01 Schulwart FM B: Feinsteinzeug R9 D: Holzwolle Akustikplatte RH: 3,95 m 21,43 m²
40/40 Schleuderbetonstütze
0.003 Windfang B: Lamellenmatte D: Holzwolle Akustikplatte RH: 3,95 m 23,32 m²
0.004 Eingangshalle B: Feinsteinzeug R9 D: Holzwolle Akustikplatte RH: 3,00 m 166,19 m²
0.13 Bibliothek und Medienraum B: Industrieparkett D: Gipskarton Kühldecke RH: 3,57 m 99,57 m²
0.12 Mehrzweck inkl. Musik B: Industrieparkett D: Gipskarton Kühldecke RH: 3,57 m 99,57 m²
0.007 Erschließung B: Feinsteinzeug R9 D: Holzwolle Akustikplatte RH: 3,00 m 15,03 m²
0.001 Erschließung Stiege 1 B: Feinsteinzeug R9 D: Brandschutzunterdecke; Holzwolle Akustikplatte (A2) RH: 3,00 m 76,20 m²
0.002 Stiege 1 B: Feinsteinzeug R9 27,62 m²
FWA 110 x 210 cm 13 Pers. / 1000 kg
0.03 WC Schüler B: Feinsteinzeug R9 D: Rohdecke, beschichtet RH: 4,04 m 4,49 m²
0.02 Abstellr. B: Feinsteinzeug Nebenräume R9 D: Rohdecke RH: 4,04 m 16,53 m²
0.04 Putzr. B: Feinsteinzeug Nebenräume R9 D: Rohdecke RH: 4,04 m 4,77 m²
0.05.A Müllraum B: Gussasphalt D: Holzwolle Mehrschichtplatte RH: 4,04 m 55,26 m²
0.05 Schleuse B: Feinsteinzeug Nebenräume R9 D: Rohdecke RH: 4,04 m 3,14 m²
Zugang Müllraum
Außenarmatur frostsicher
0.008 Erschließung B: Feinsteinzeug R9 D: Holzwolle Akustikplatte RH: 3,00 m 20,08 m²
0.009 Erschließung B: Feinsteinzeug R9 D: Holzwolle Akustikplatte RH: 2,50 m 6,89 m²
0.07.A WC P B: Feinsteinzeug Nebenräume R9 D: Rohdecke, beschichtet RH: 4,04 m 5,00 m²
0.07 Sozialr. P B: Feinsteinzeug Nebenräume R9 D: Gipskarton Kühldecke RH: 3,30 m 27,15 m²
0.09 Putzraum B: Feinsteinzeug Nebenräume R9 D: Rohdecke RH: 4,04 m 5,73 m²
0.10 WC Schülerin B: Feinsteinzeug R9 D: Rohdecke, beschichtet RH: 4,04 m 5,46 m²
0.06.A zentr. Aufwärmküche VS B: Feinsteinzeug Küche R10/R11 D: Metalldecke Küche RH: 3,00 m 39,92 m²
0.08.A Trockenlager B: Feinsteinzeug Küche R10/R11 D: Rohdecke RH: 4,04 m 13,34 m²
0.010 Stiege 3 B: Betonplatte 7,79 m²
0.11.B Speiseraum inkl. Buffet VS B: Feinsteinzeug R9 D: Gipskarton Kühldecke RH: 3,57 m 119,17 m²
180 Plätze
0.11.A Speiseraum inkl. Buffet MS B: Feinsteinzeug R9 D: Gipskarton Kühldecke RH: 3,57 m 134,96 m²
Flankendämmung Schaumglas 10cm
0.08 Anl. u. Abh. B: Feinsteinzeug Küche R10/R11 D: Rohdecke RH: 4,04 m 29,70 m²
0.06.B zentr. Aufwärmküche MS B: Feinsteinzeug Küche R10/R11 D: Metalldecke Küche RH: 3,00 m 50,43 m²
0.011 Erschließung B: Betonplatte D: Putz RH: 3,91 m 3,56 m²
Betonfertigteil
43/43
Abfalleimer
Holzdeck
Rigol
Außenarmatur frostsicher
Sitzelement Unterlaufschutz
F0.06 Stiege 4 B: Betonplatte RH: 7,79 m
31 STG 15 / 30
F0.07 Stiege 3 B: Betonplatte RH: 7,79 m

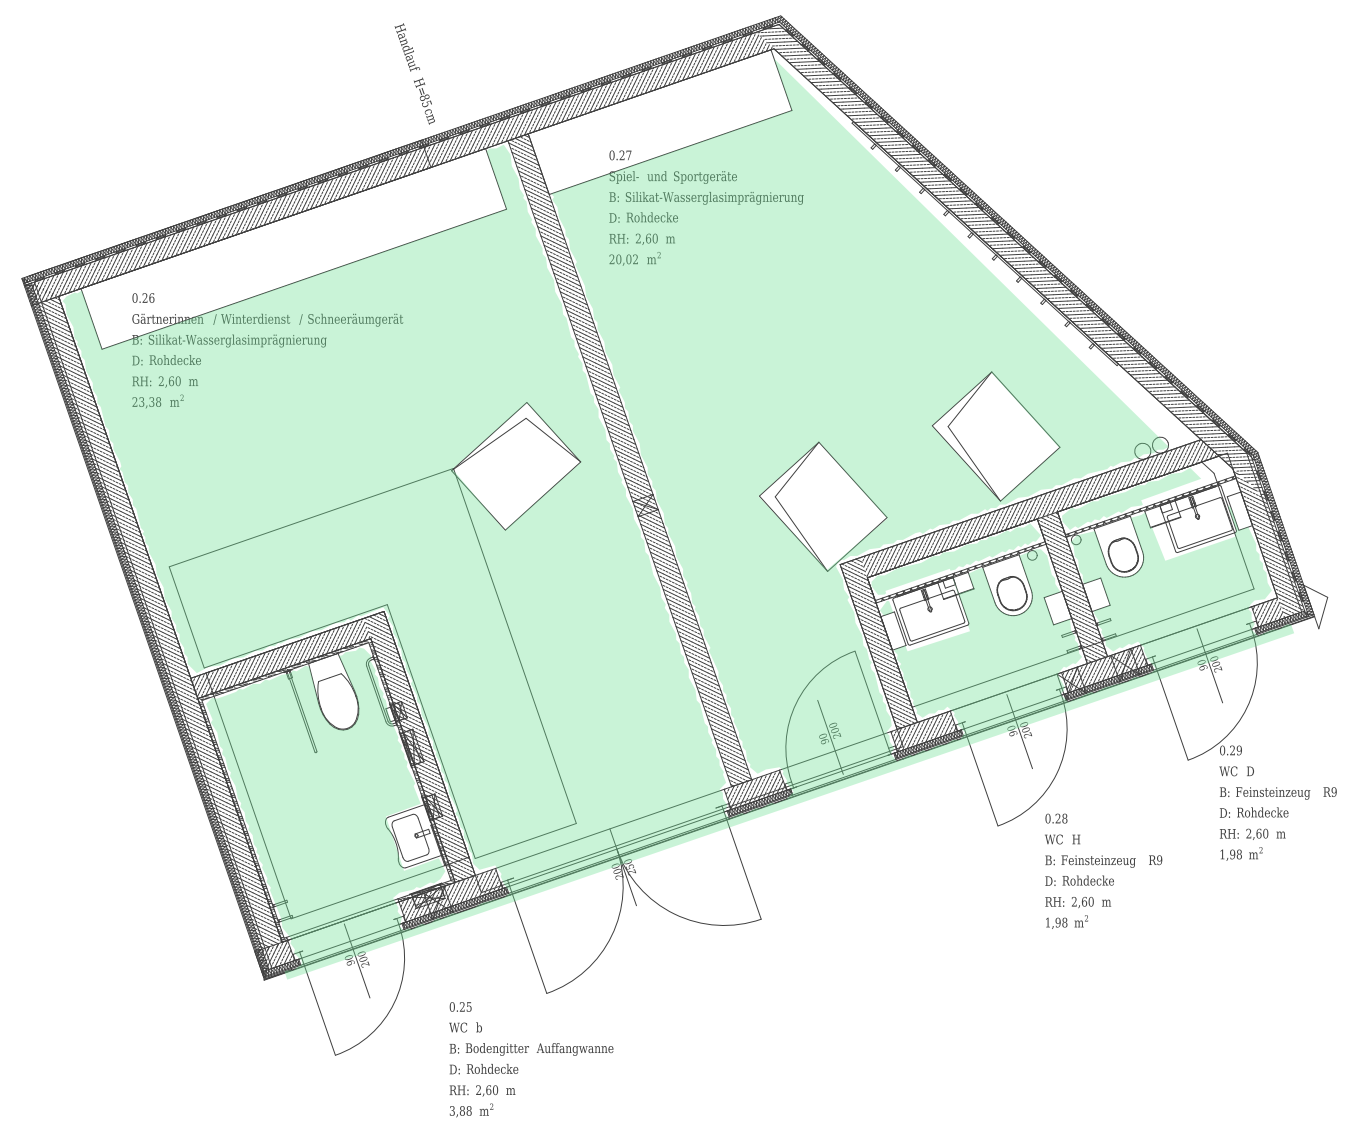
Handlauf H=85cm
0.26 Gärtnerinnen / Winterdienst / Schneeräumgerät B: Silikat-Wasserglasimprägnierung D: Rohdecke RH: 2,60 m 23,38 m²
0.27 Spiel- und Sportgeräte B: Silikat-Wasserglasimprägnierung D: Rohdecke RH: 2,60 m 20,02 m²
0.25 WC b B: Bodengitter Auffangwanne D: Rohdecke RH: 2,60 m 3,88 m²
0.28 WC H B: Feinsteinzeug R9 D: Rohdecke RH: 2,60 m 1,98 m²
0.29 WC D B: Feinsteinzeug R9 D: Rohdecke RH: 2,60 m 1,98 m²