EG: GEHFLÄCHEN IN GRÜN

Grün: aus dem Plan interpretierte Boden- und Treppenbereiche.
Schwarz: Originalkanten und Stufen; Violett: ausgewählte feste Abschlüsse.
Ocker schraffiert: Boden auf EG-Niveau nicht belegt.
Sackgasse bleibt begehbar; am Abschluss führt nur der Rückweg weiter.
Türflächen gelten bei geöffneter Tür. Weiß ist keine automatische Sperre.
Markierte Möbel und Waschbecken sind weiß; Originalkonturen bleiben sichtbar.

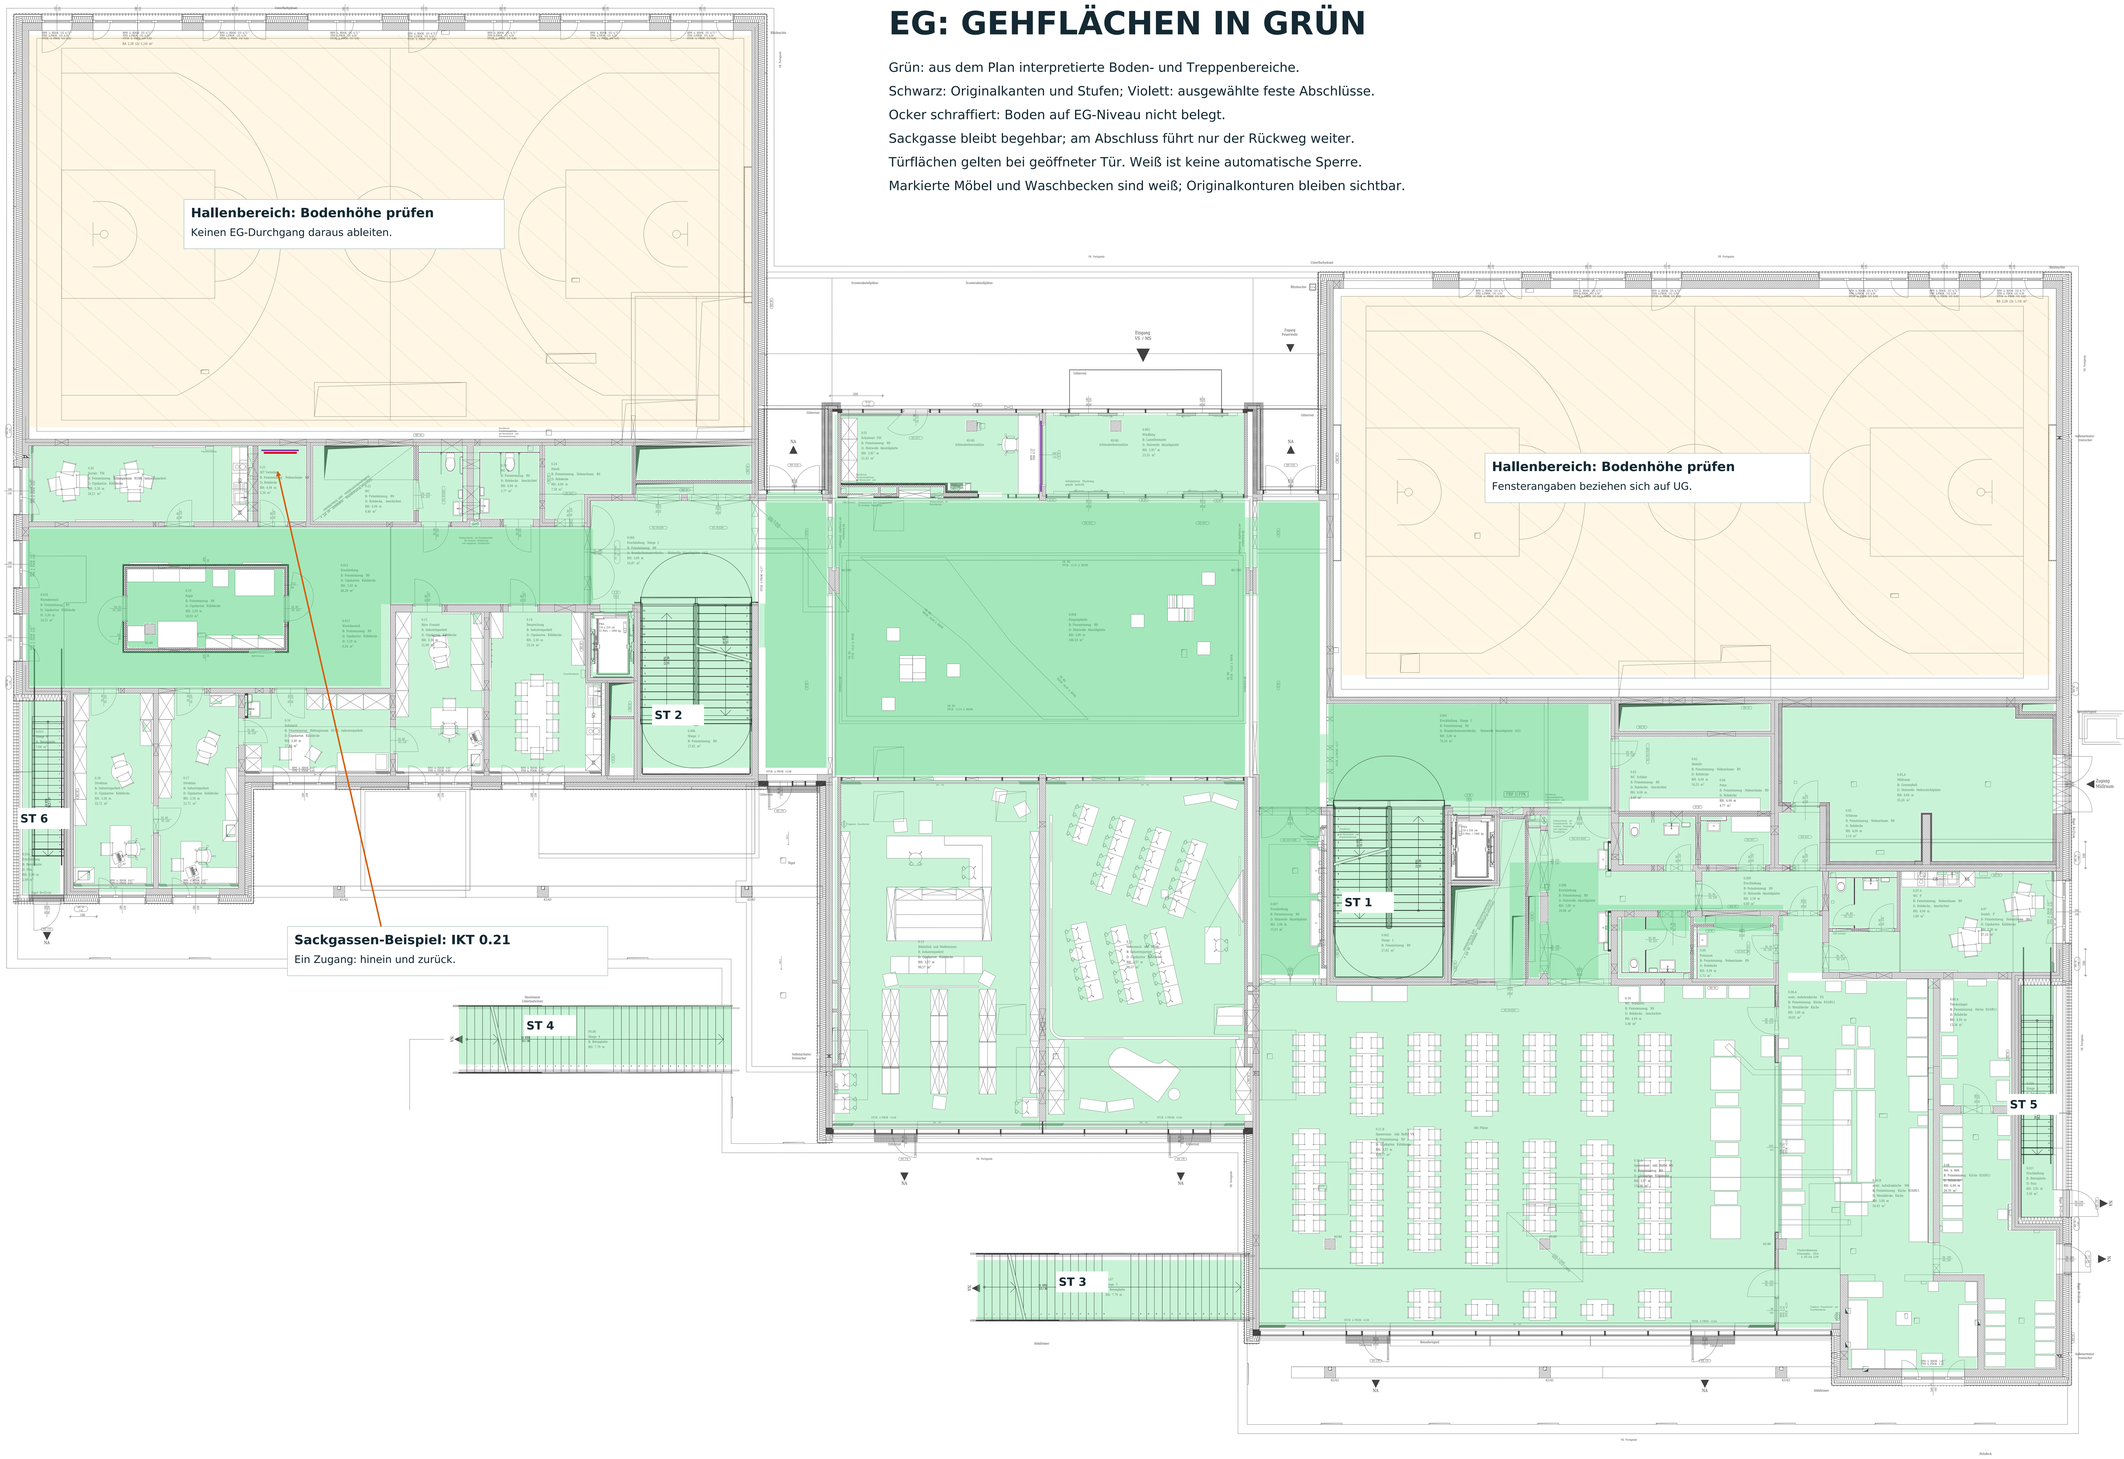

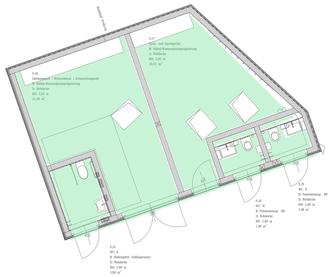

Original: Schule_SH22_EG.pdf | Lernrevision mit Flächen statt Routenlinie
Große Gänge sind flächig grün; Möbel, Wände und Schächte bleiben ablesbar.
Treppen: Zielgeschoss / Auf- und Abstieg erst mit Schnitt und Nachbargeschoss bestätigen.
Dies ist eine Lernzeichnung zum Planlesen, keine geprüfte Weg- oder Fluchtwegfreigabe.