Erdgeschoss

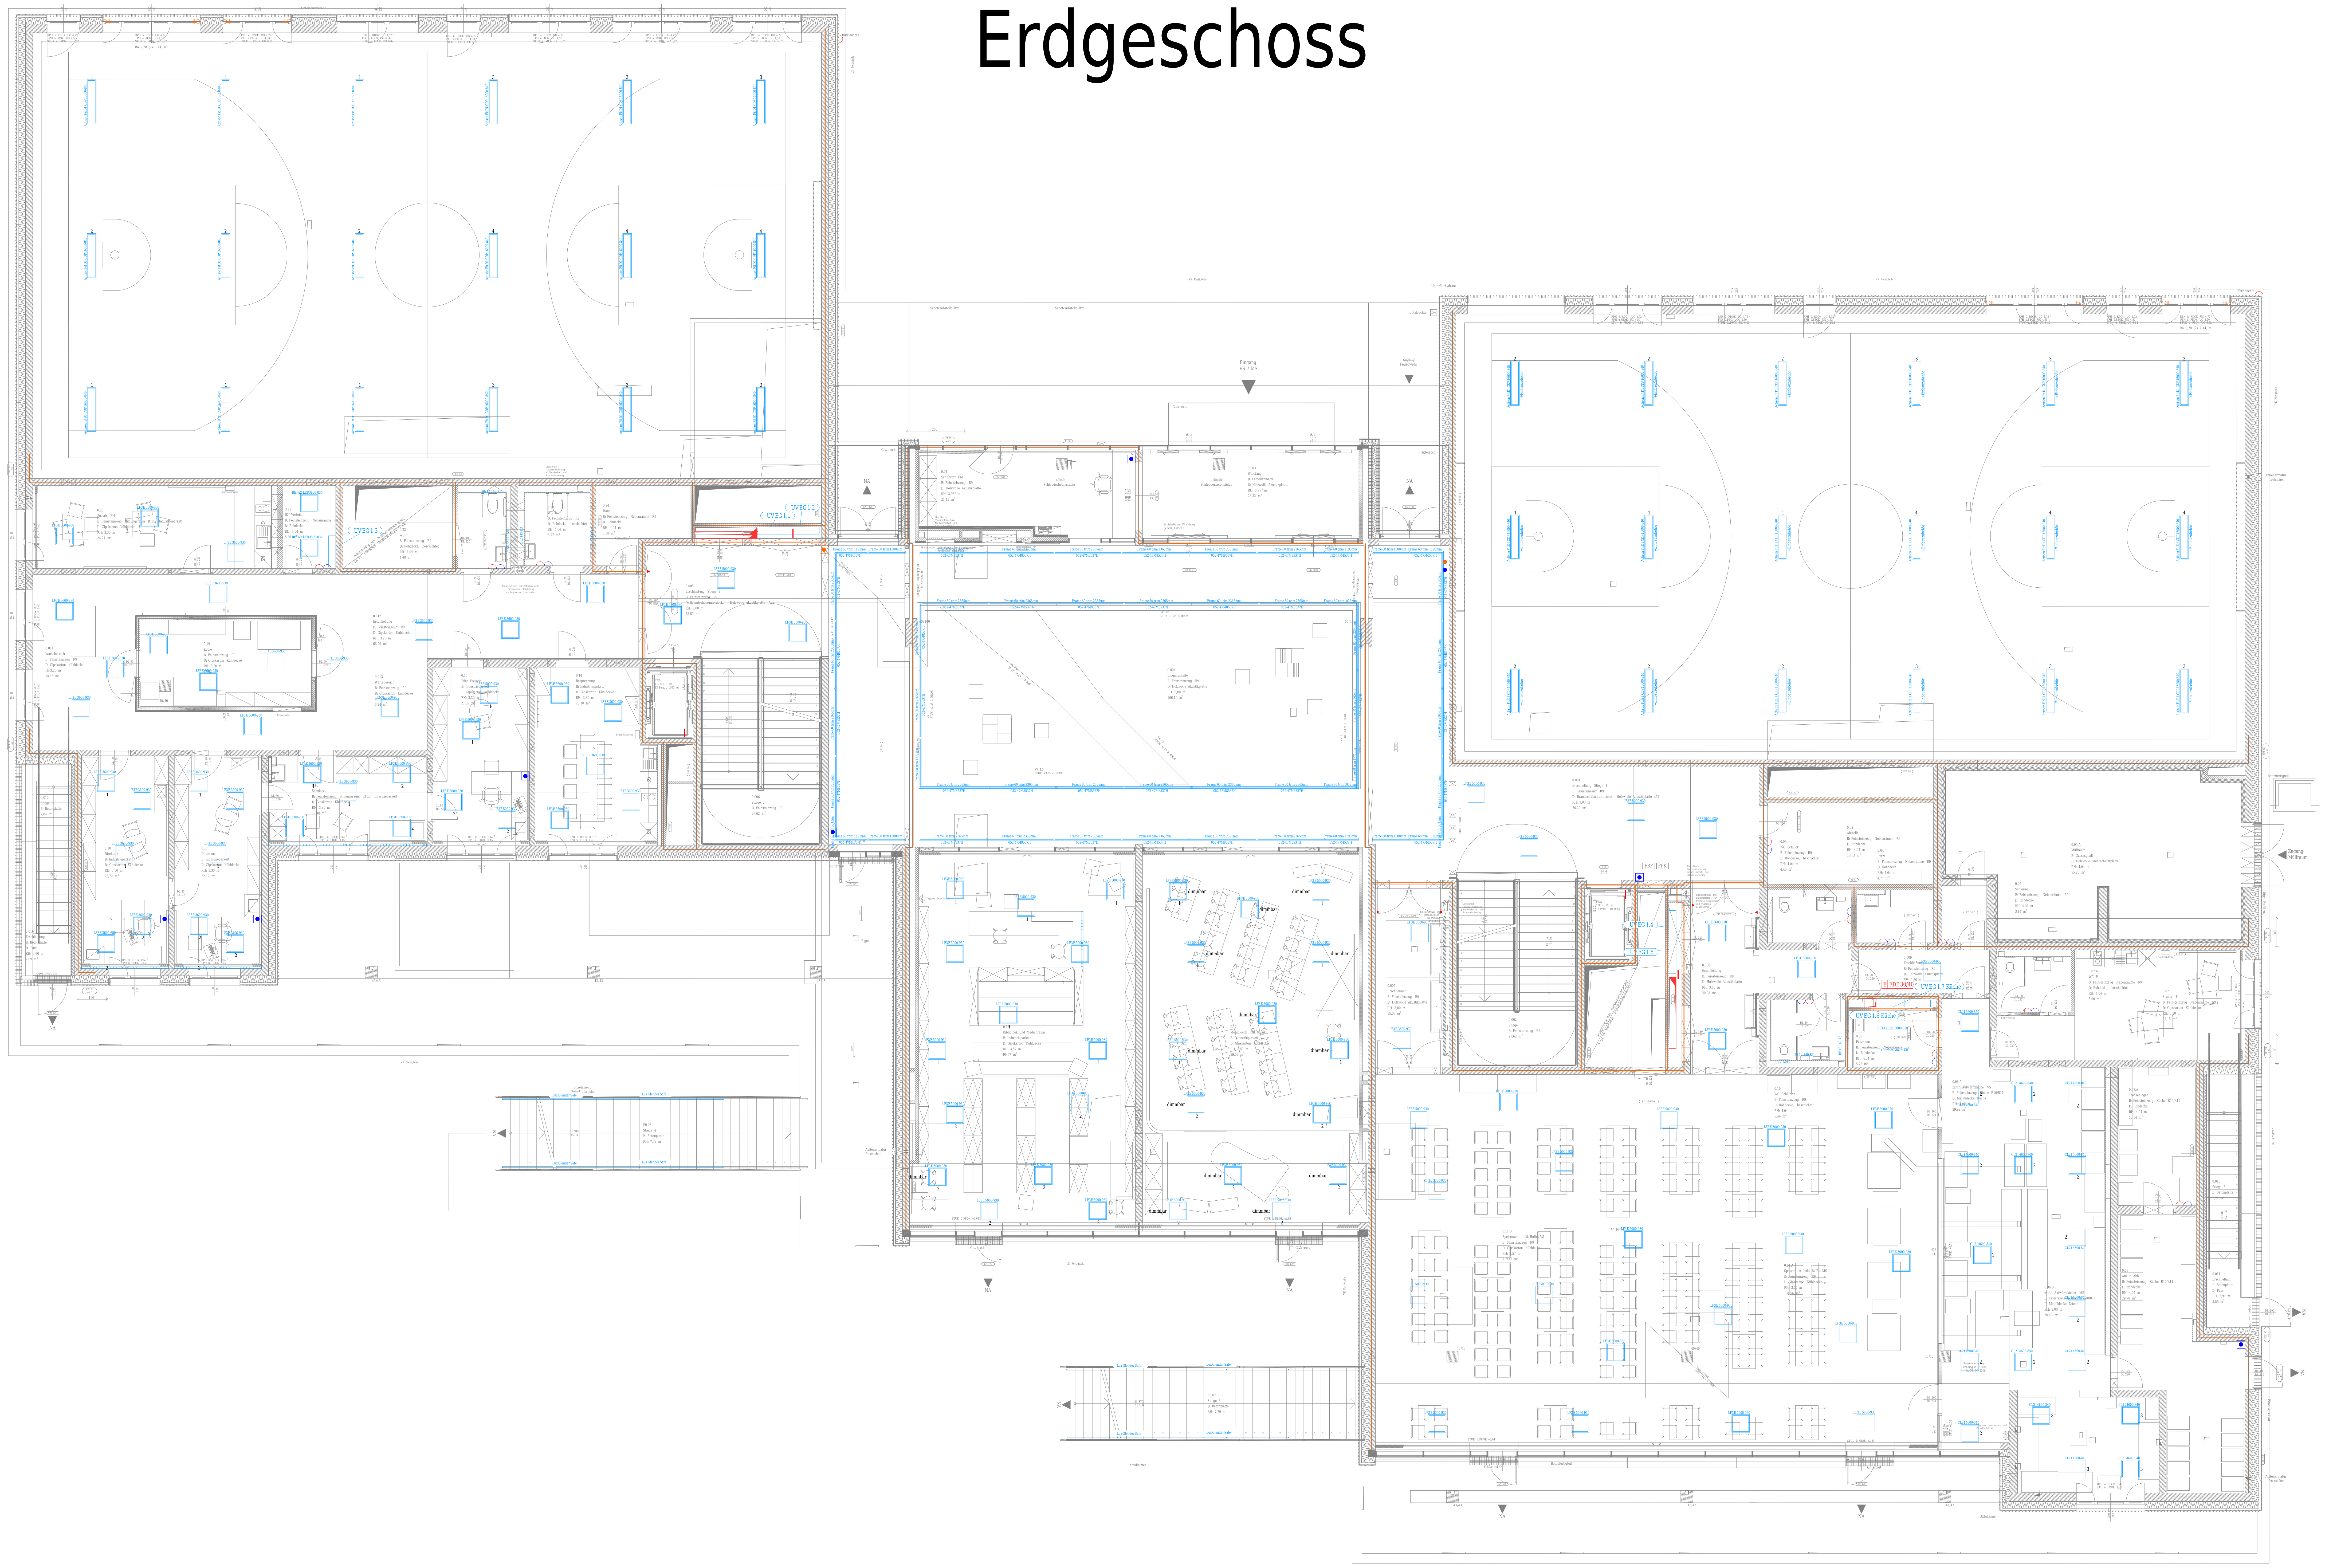
Eingang VS / MS
Zugang Feuerwehr
Zugang Müllraum
NA
Scooterabstellplätze
Gitterrost
VK Fertigteile
Blitzleuchte
Unterflurhydrant
Außenarmatur frostsicher
0.20 Sozialr. FM
0.21 IKT Verteiler
0.22 WC
0.24 Handl.
0.19 Kopie
0.014 Wartebereich
0.012 Erschließung
0.013 Wartebereich
0.15 Büro Freizeit
0.14 Besprechung
0.16 Schularzt
0.18 Direktion
0.17 Direktion
0.015 Stiege 6
0.016 Erschließung
0.005 Erschließung Stiege 2
0.006 Stiege 2
0.01 Schulwart FM
0.003 Windfang
0.004 Eingangshalle
0.11 Bibliothek und Medienraum
0.12 Mehrzweck und Musik
0.007 Erschließung
0.001 Erschließung Stiege 1
0.002 Stiege 1
0.008 Erschließung
0.009 Erschließung
0.02 Abstellr.
0.03 WC Schüler
0.04 Putzr.
0.05.A Müllraum
0.05 Schleuse
0.07.A WC P
0.07 Sozialr. P
0.09 Putzraum
0.10 WC Schüler
0.11.B Speiseraum inkl. Buffet VS
0.11.A Speiseraum inkl. Buffet MS
0.06.A zentr. Aufwärmküche VS
0.06.B zentr. Aufwärmküche MS
0.08.A Trockenlager
0.08 Anl. u. Abf.
0.010 Stiege 5
0.011 Erschließung
F0.06 Stiege 4
F0.07 Stiege 3
Abfalleimer
Holzdeck
UV EG 1.1
UV EG 1.2
UV EG 1.3
UV EG 1.4
UV EG 1.5
UV EG 1.6 Küche
UV EG 1.7 Küche
E FDB30/40
FBF
FPK
LF3E 3600-930
LF3E 5000-930
BETA2 LED3800-830
CL214600-840
Actinea Fit D1 CDP16000-840
Frame 60 trim 2365mm
Lux Glender Safe
dimmbar
43/43
40/40

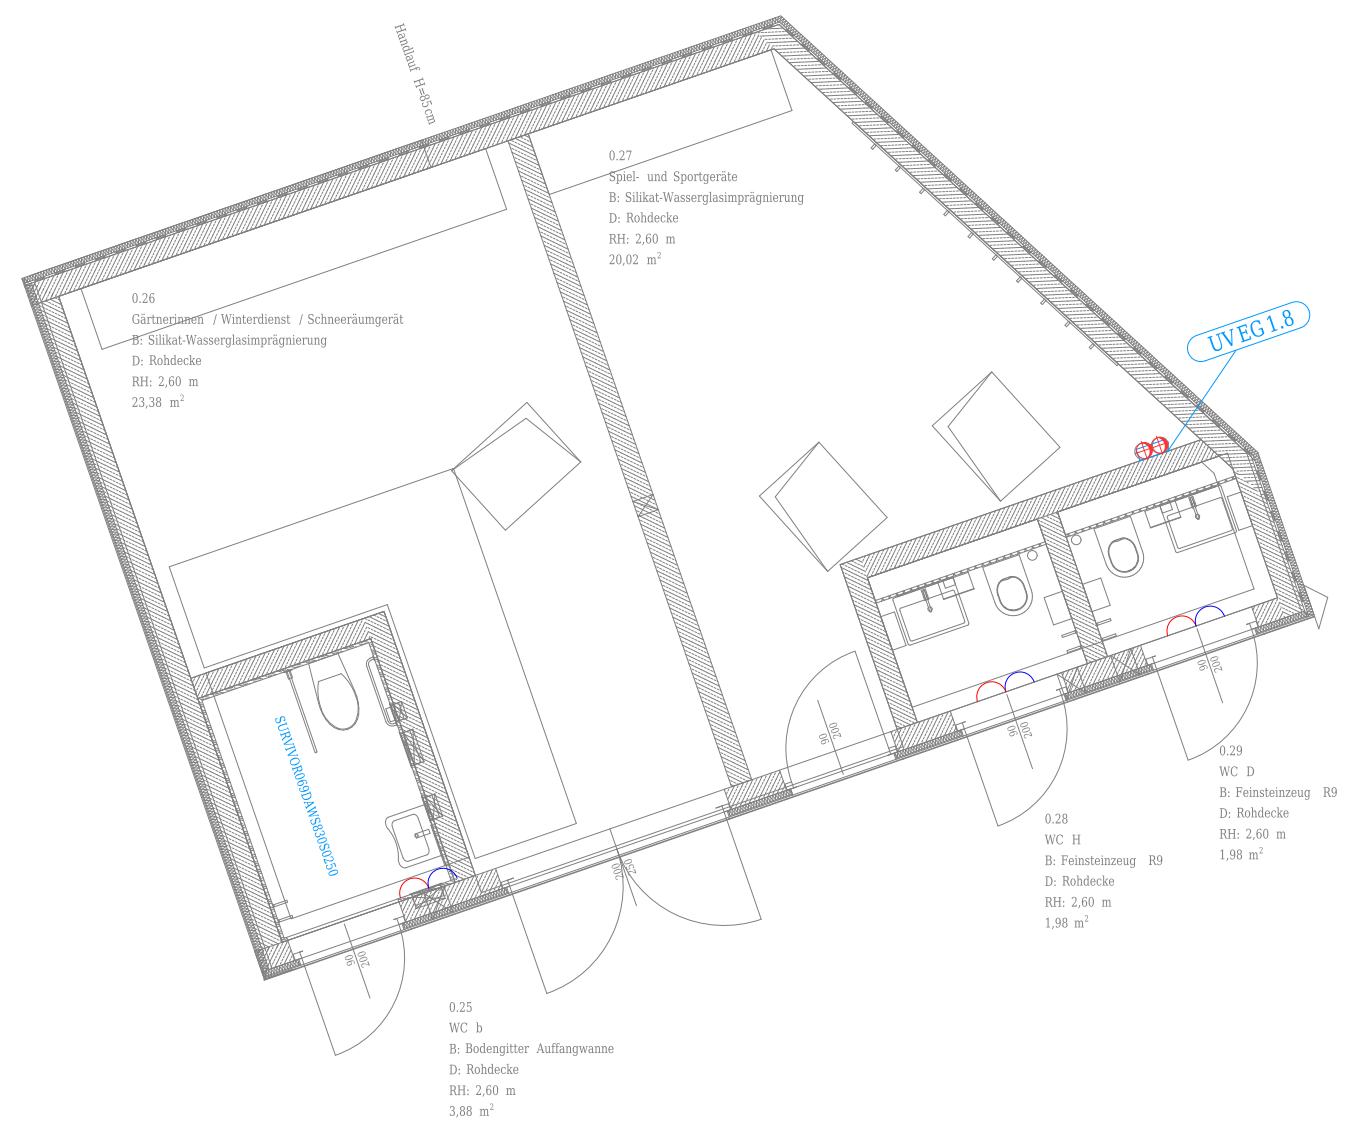
0.26 Gärtnerraum / Winterdienst / Schneeräumgerät
B: Silikat-Wasserglasimprägnierung
D: Rohdecke
RH: 2,60 m
23,38 m²
0.27 Spiel- und Sportgeräte
B: Silikat-Wasserglasimprägnierung
D: Rohdecke
RH: 2,60 m
20,02 m²
UV EG 1.8
0.25 WC b
B: Bodengitter Auffangwanne
D: Rohdecke
RH: 2,60 m
3,88 m²
0.28 WC H
B: Feinsteinzeug R9
D: Rohdecke
RH: 2,60 m
1,98 m²
0.29 WC D
B: Feinsteinzeug R9
D: Rohdecke
RH: 2,60 m
1,98 m²