


1. UNTERGESCHOSS | Geh- und Bodenflächen

Arbeitsfassung zur Raumerkennung - Bodenfläche nach Plan, keine bestätigte Fluchtweg- oder Barrierefreiheitsprüfung.

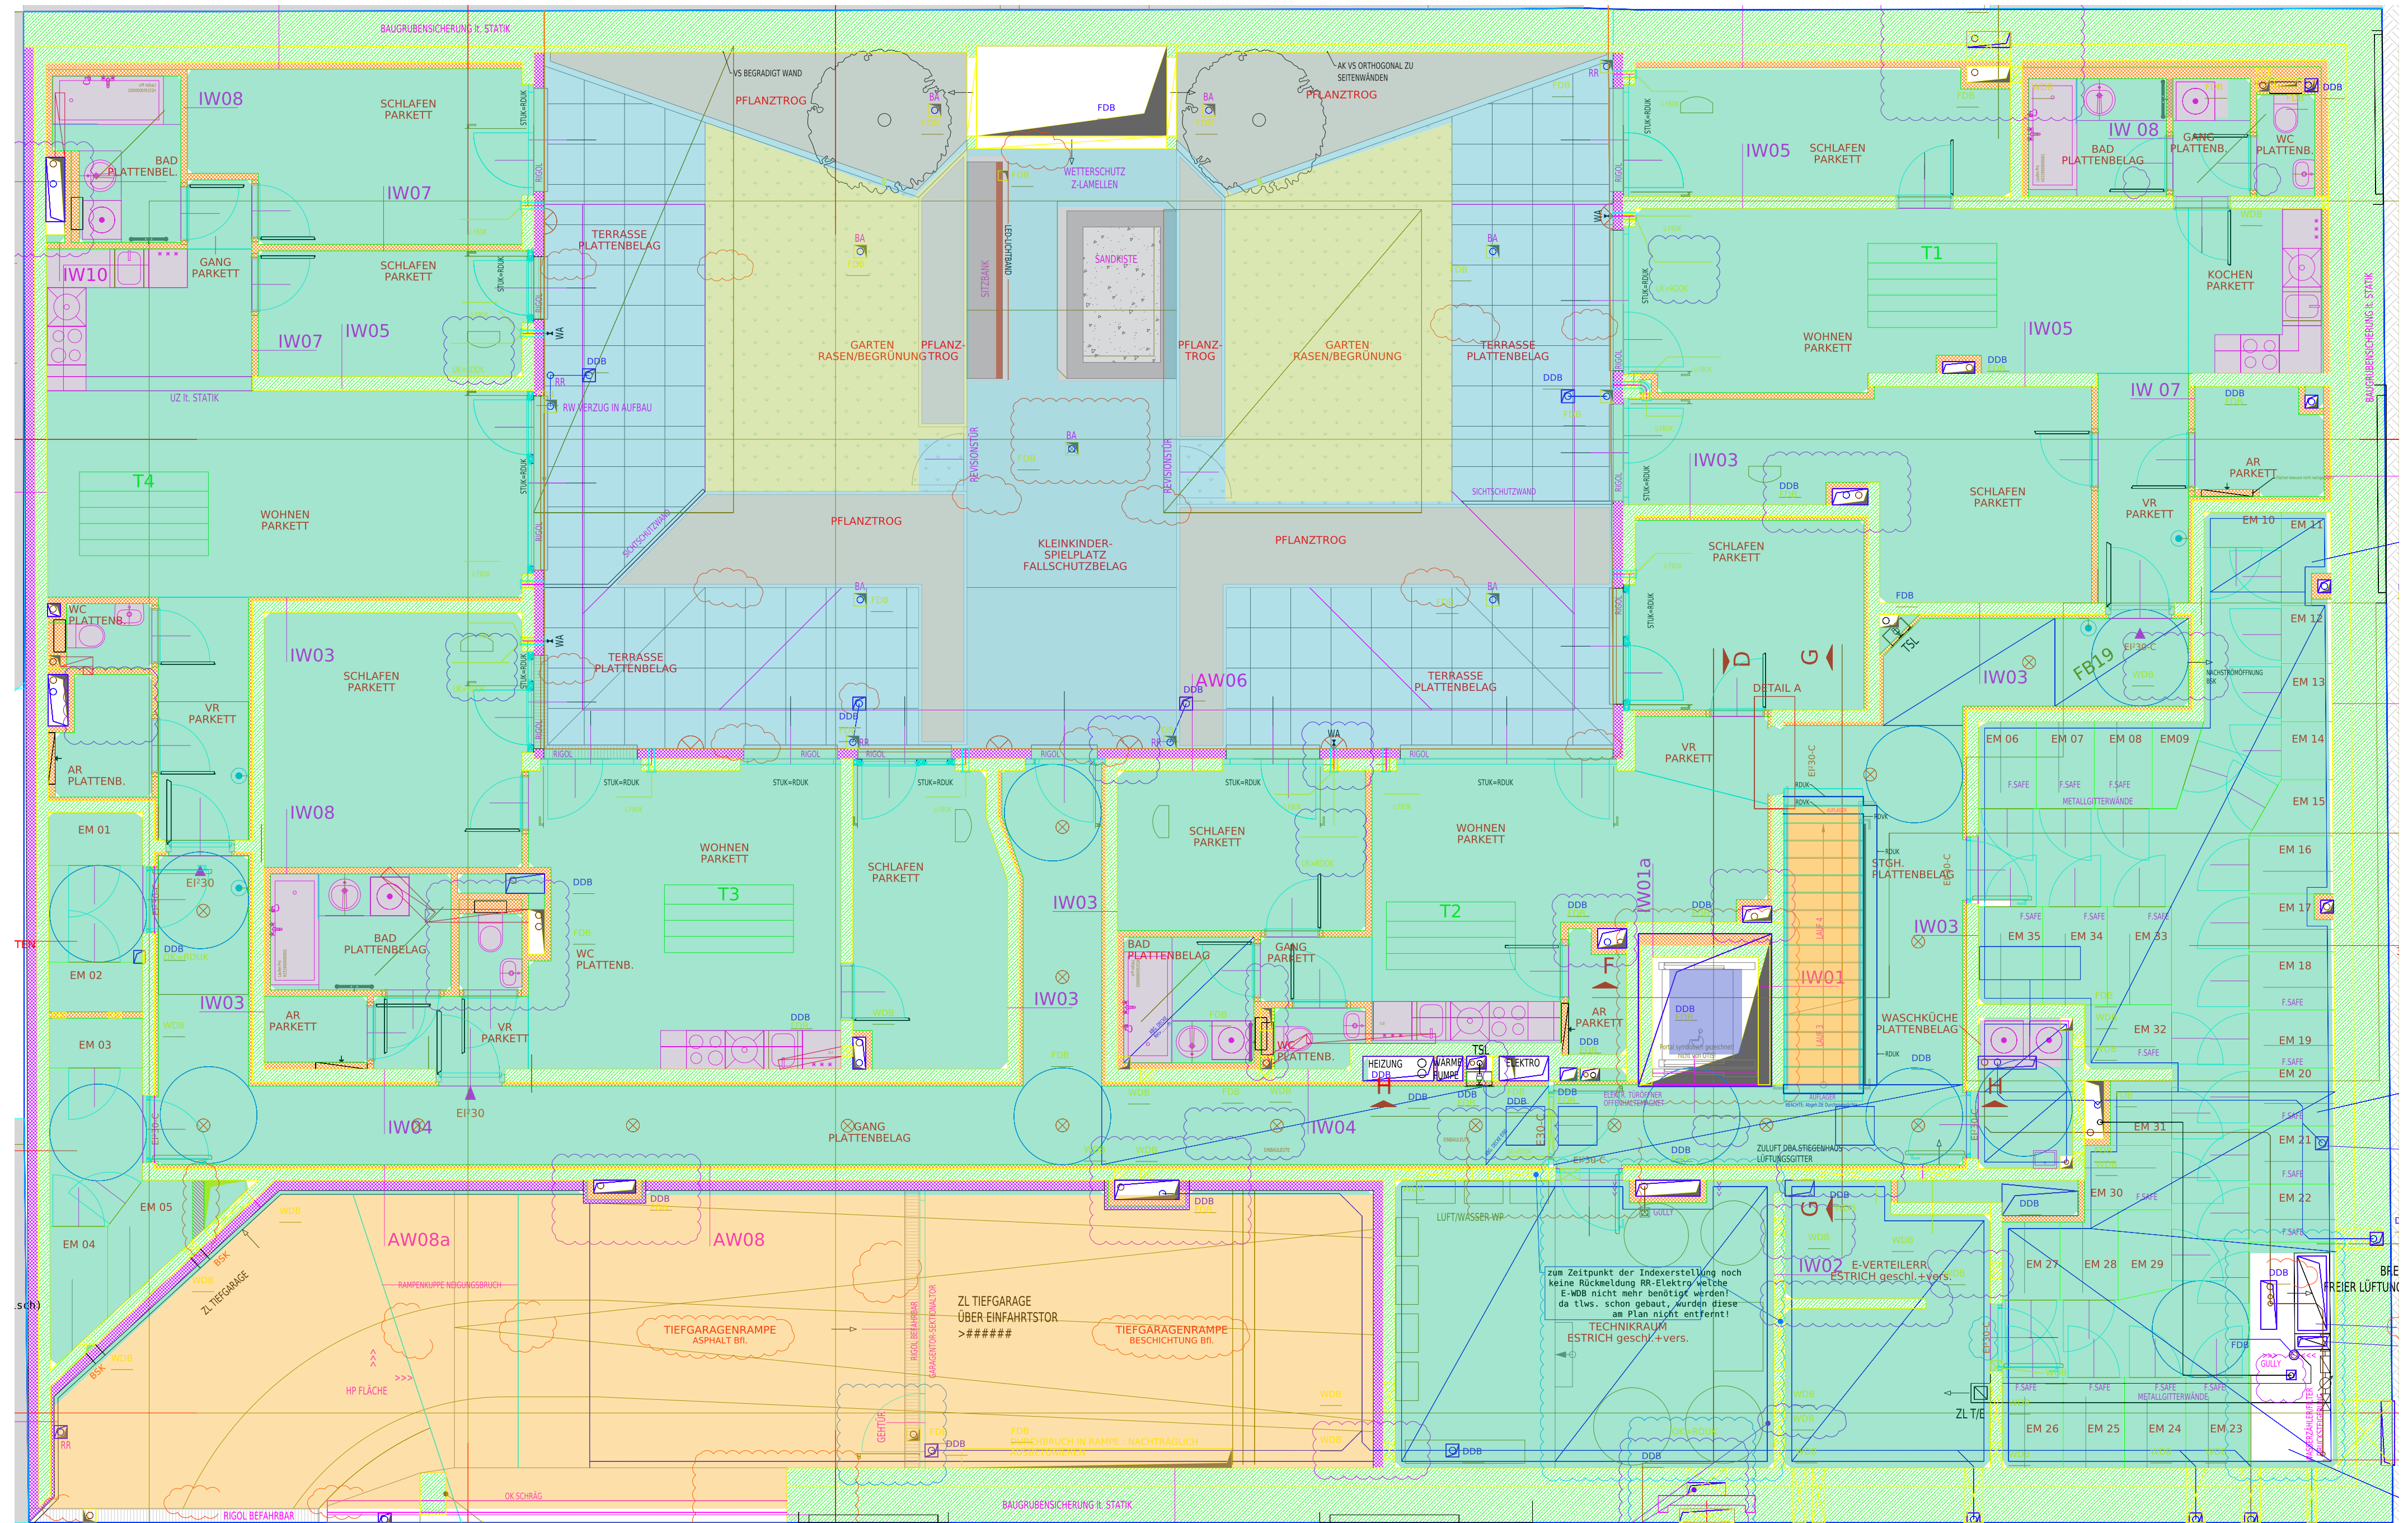

- freier Innenboden
 Terrasse / Spielboden
 Garten
 Treppe / Fahrzeugrampe
 Liftkabine
 feste Ausstattung

Quelle: 1UG_ohne_Masse(1).pdf | Originalgeometrie mit eigenen Lernmarkierungen | 24.09.2026 | Details und offene Deutungen im Lernbuch

1. UNTERGESCHOSS | Bauteile direkt markiert

Arbeitsfassung zur Raumerkennung - Bodenfläche nach Plan, keine bestätigte Fluchtweg- oder Barrierefreiheitsprüfung.

