

Grundriss lesen lernen - 2. Dachgeschoss

Ein Erklärplan für Menschen, die noch nie einen Bauplan gesehen haben


Links siehst du das **2. Dachgeschoss** des Wohnhauses an der Ecke **Aichholzgasse / Pöhlgasse**. Ein Dachgeschoss ist ein Stockwerk **im Dach** – ganz oben im Haus. Darum sieht es anders aus als die Stockwerke darunter: Es ist kleiner und hat große **Terrassen** im Freien.

So ist das Heft aufgebaut:

- A. **Grundlagen:** Was ist ein Grundriss? Was ist ein Dachgeschoss? Die Sprache der Linien.
- B. **Schicht für Schicht:** Ein Stück Plan wird Farbe für Farbe aufgebaut.
- C. **Überblick:** Wo ist was? Welche Wohnungen gibt es?
- D. **Bauteile:** Wände, Türen, Fenster, Glas – Gesamtplan und Nahaufnahmen.
- E. **Gehen:** Innenräume, Terrassen, ein Weg durch die Wohnung T64.
- F. **Das Dach:** Dachschräge, Dachflächenfenster, Rinnen, Flachdach.
- G. **Kern:** Stiegenhaus, Aufzug, Schächte.
- H. **Schrift, Zeichen, Anfängerfehler, Lexikon, Vergleich, Fragen, Quiz, Checkliste.**

Jede Nahaufnahme hat unten rechts eine **Lagekarte** mit rotem Kästchen: So weißt du immer, wo im Haus du bist.

Wichtig: Die Farben sind Lernmarkierungen. Sie wurden aus der Geometrie des Original-PDFs abgeleitet und an vielen Stellen geprüft, sind aber keine millimetergenaue Planung. Terrassenflächen wurden teils als Rechtecke entlang ihrer Beschriftung und Ränder angenähert. Wo der Plan etwas nicht eindeutig sagt, steht das dabei.

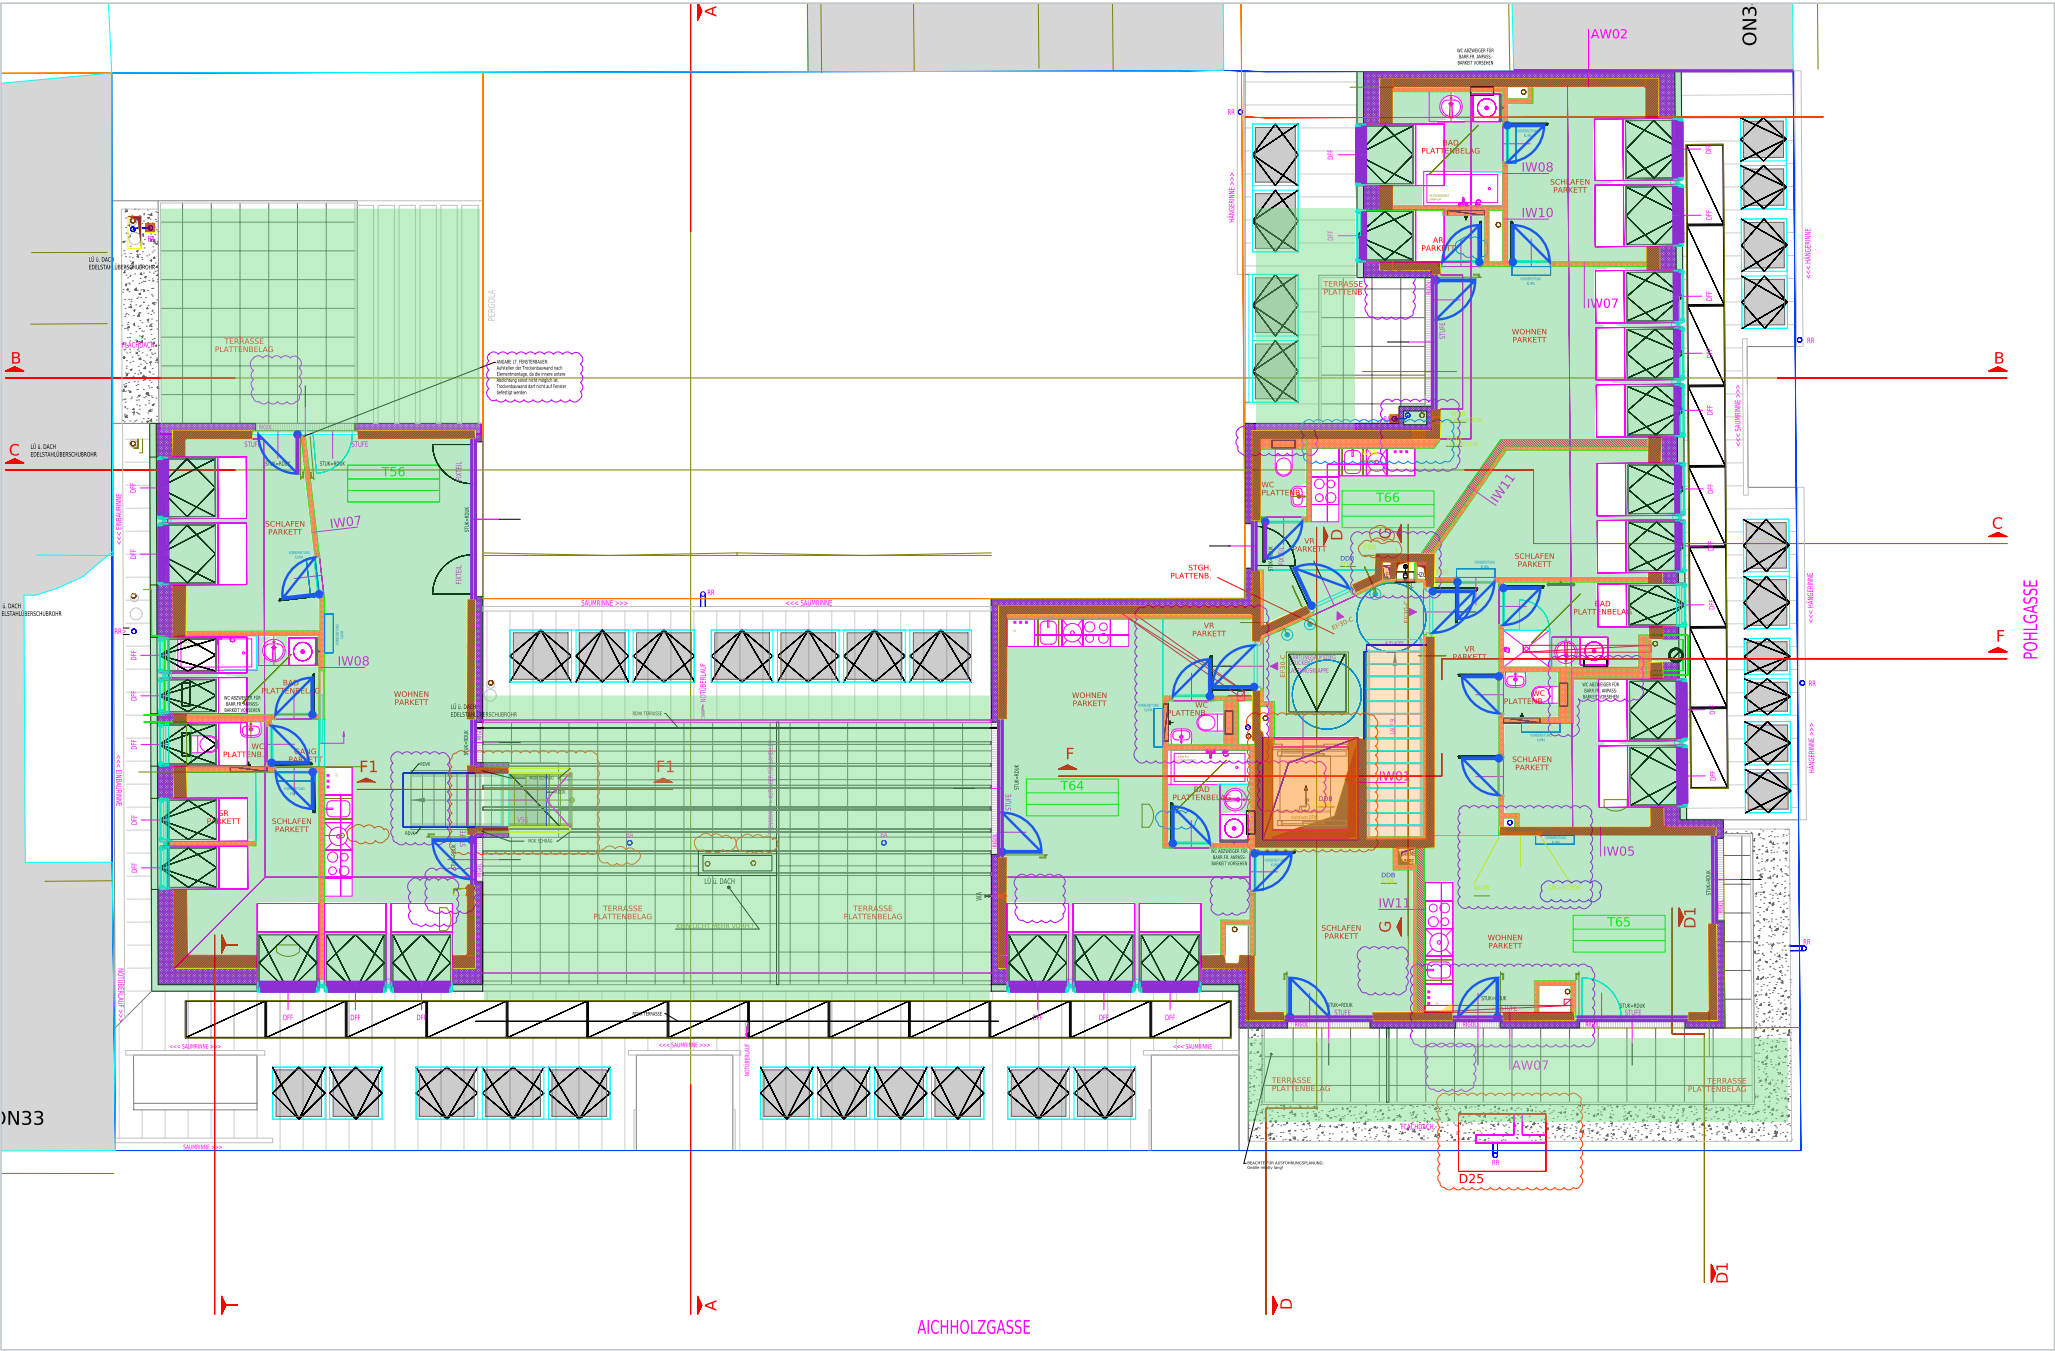

So liest du dieses Heft: Farben und Zeichen

Jede Farbe bedeutet im ganzen Heft **immer dasselbe**. Die Farben sind **durchsichtig** – darunter siehst du immer das Original. Merkhilfe wie bei einer Ampel: **Rot = Stopp** (Material, kein Durchgang), **Grün = Los** (hier kann ich gehen), **Blau = Durchgang** (hier wechsle ich den Raum).

- DUNKELROT - dicke Wand**
Feste, massive Wand. Im Plan: gelbe Umrandung, innen grüne Schrägstriche.
- HELLROT - dünne Wand**
Schmalere Wand in der Wohnung. Im Plan: grüne Umrandung, orange Gitterstriche.
- ROSA - Dämmschicht**
Schicht gegen Kälte an der Außenwand. Im Plan: violette Gittermuster.
- BLAU - Tür**
Viertelkreis = Weg des Türblatts, dicke Linie = Türblatt, Punkt = Scharnier.
- GRÜN - innen begehbar**
Fußboden in der Wohnung, im Gang, im Stiegenhausvorplatz.
- HELLGRÜN - Terrasse/Balkon**
Boden im Freien. Im Dachgeschoss sind das große Terrassen.
- GELB - Öffnung in der Außenwand**
Lücke in einer gemauerten Außenwand für Fenster oder Glastür.
- VIOLETT - Glaslinien**
Dünne hellblaue Originallinien an der Außenseite: Glasfronten, Fenster.
- ORANGE - Hindernisse & Einbauten**
Küche, WC, Waschbecken, Kästen, Schächte, Aufzug, Treppe.
- TÜRKIS - Schrift und Planzeichen**
Rahmen um Texte, Nummern und Symbole.


Die Hilfszeichen

- 1

Nummer: verbindet die Stelle im Plan mit dem Text rechts.
- Rahmen: umschließt das Bauteil, das gerade erklärt wird.
- Pfeil mit Punkt: der Punkt sitzt genau auf dem gemeinten Element.
- Gestrichelt violett: gedachte Lage (z. B. geschlossene Tür).
- Türkiser Kreis: hier steht ein Text oder Symbol.
- Rotes Kästchen in der Lagekarte: dein Ausschnitt.

Und was bedeutet „weiß“?


Weiß heißt nur: **hier ist nichts eingefärbt**. Im Dachgeschoss ist vieles weiß, weil dort **Dach** ist – also Fläche, auf der man normalerweise nicht geht (Flachdach, Dachschräge von außen, Rinnen).

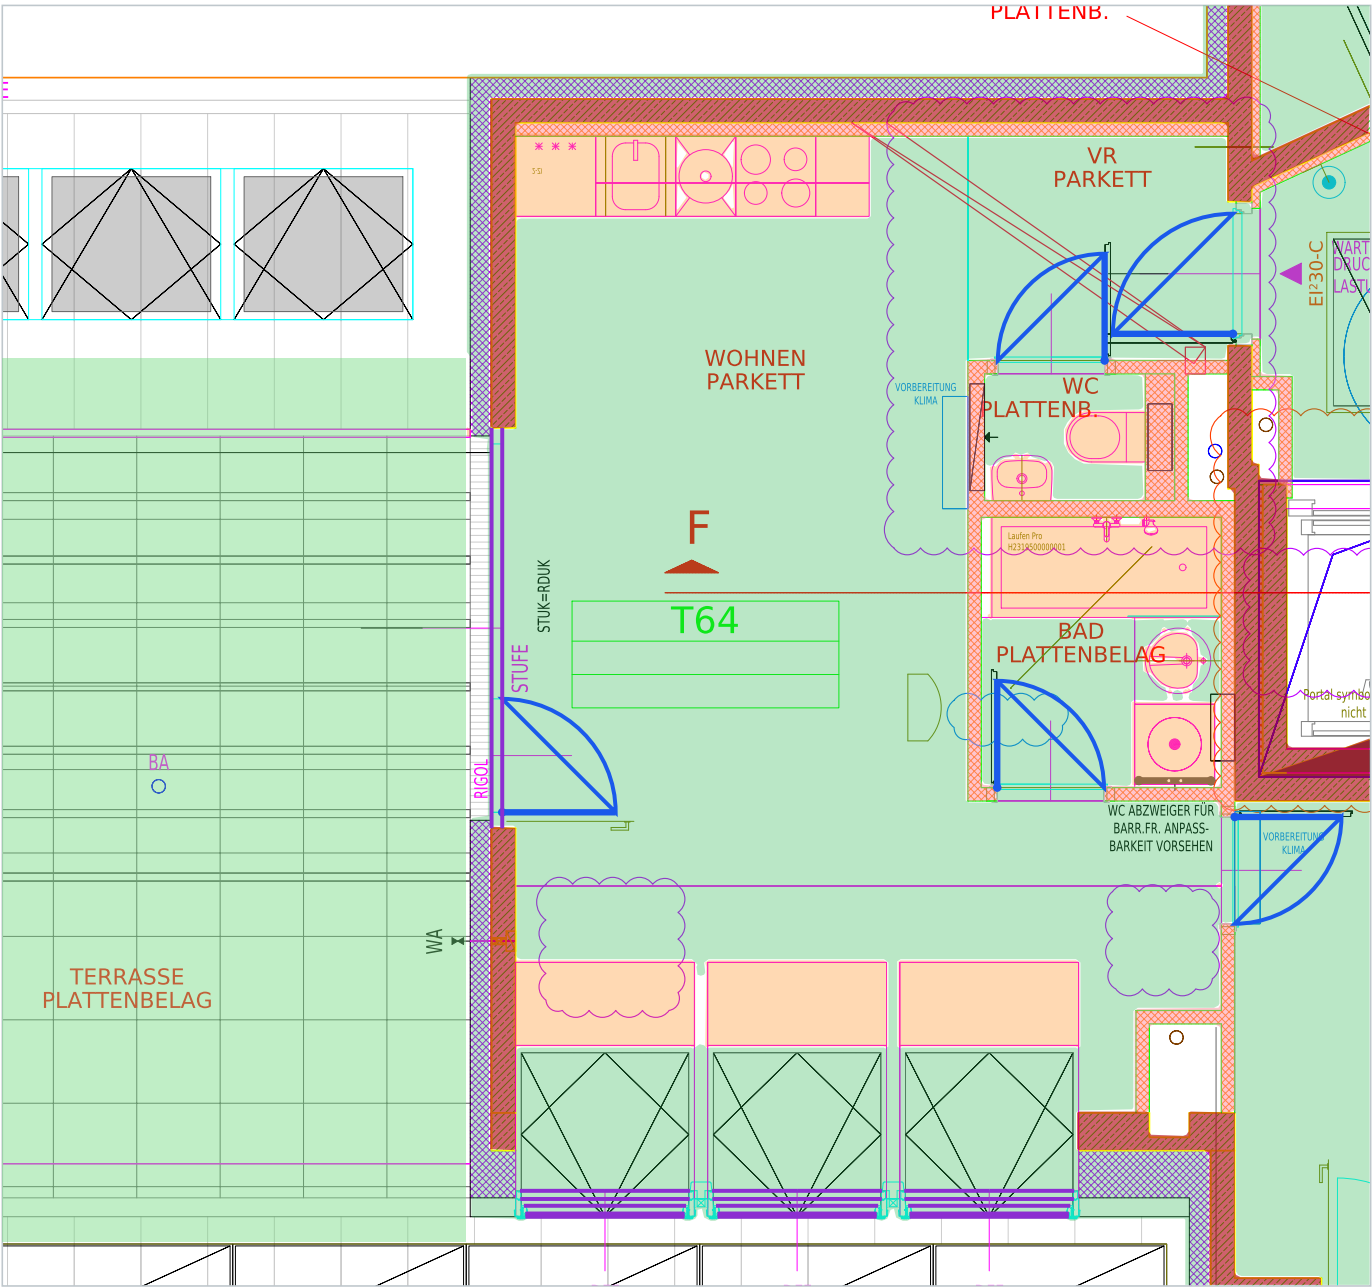

Beispiel: die Wohnung T64 mit allen Farben

Rote Wände umschließen die Räume, **grüner Boden** füllt sie, **blaue Türbögen** verbinden sie, **violett** sind die Glaslinien, **orange** die Einbauten, **hellgrün** die Terrasse. Diese Wohnung begleitet dich durch das Heft.

Was ist ein Grundriss - und was ist ein Dachgeschoss?

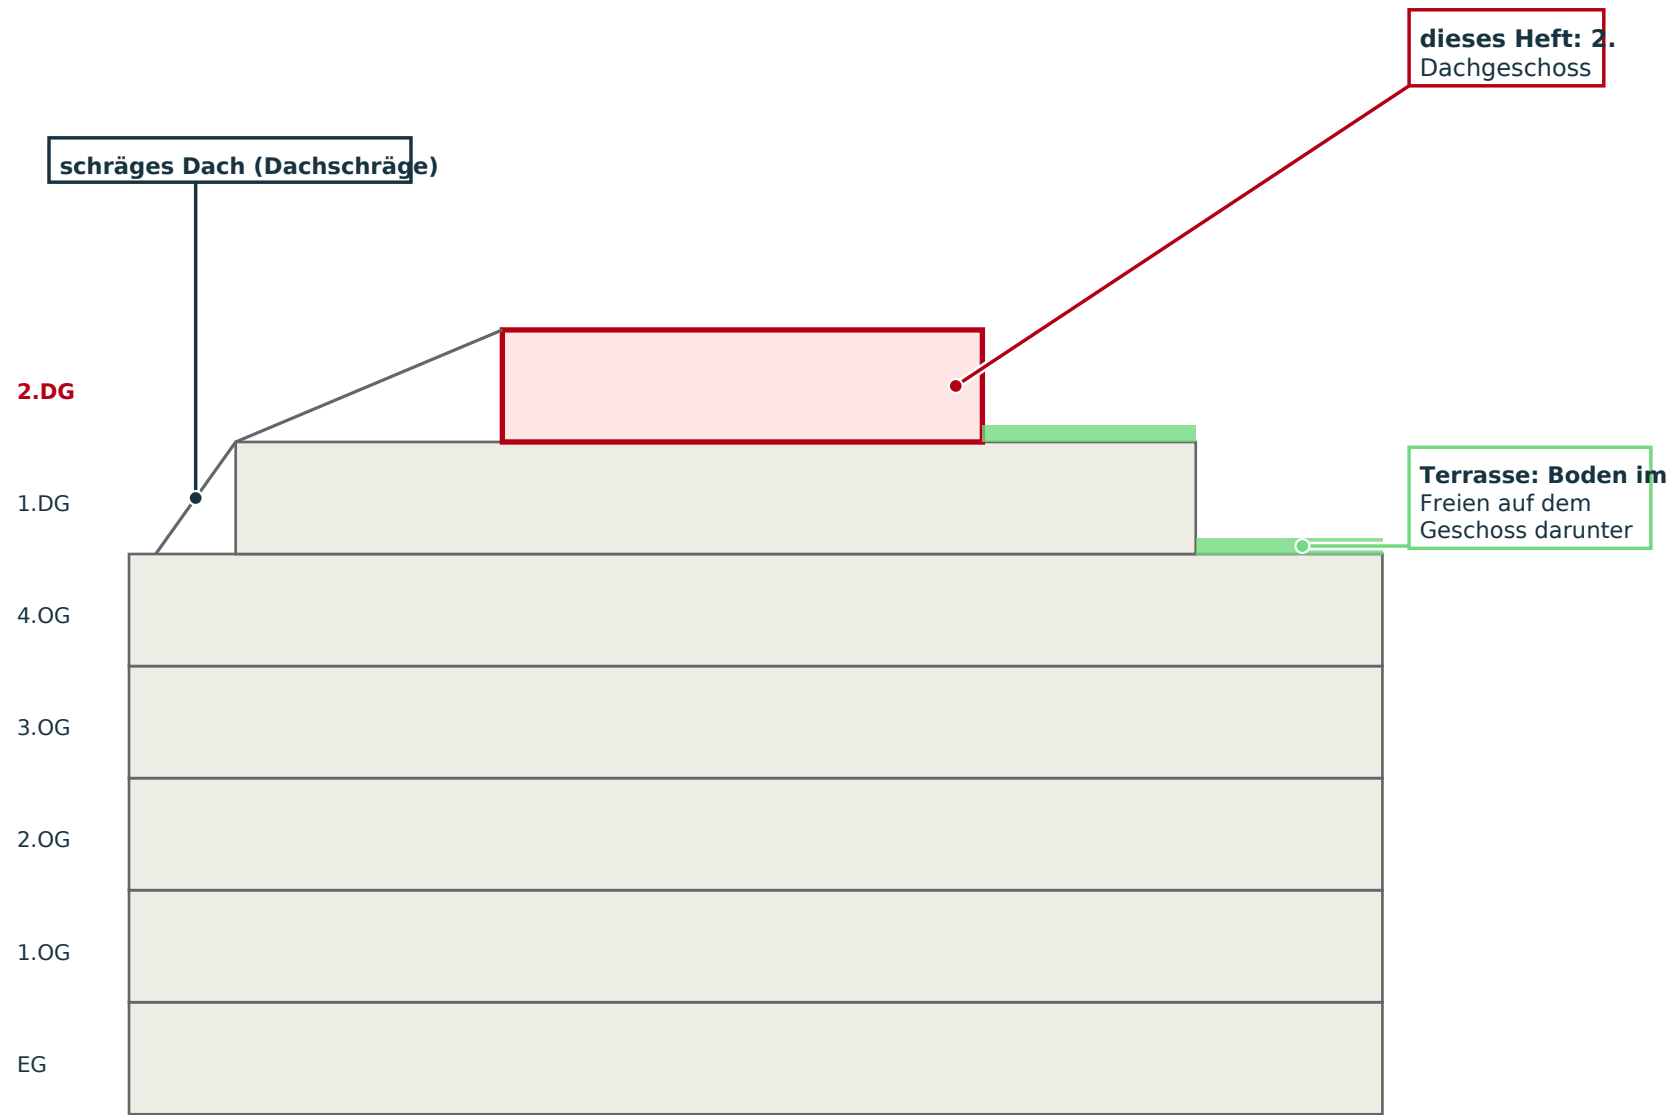

Seitenansicht (Schema): Das Haus wird oben schmaler.

Drei Dinge, die Anfänger im Dachgeschoss verwechseln

- 1. Terrasse ist nicht Zimmer.** Eine Terrasse ist Boden im Freien – mit Platten belegt, aber ohne Dach darüber. Man erreicht sie nur durch eine Tür.
- 2. Dach ist nicht Terrasse.** Neben den Terrassen liegen Dachflächen (Flachdach, Kies, Rinnen). Auf ihnen geht man normalerweise nicht – sie sind hier weiß.
- 3. Viele Linien gehören zum Dach, nicht zum Raum.** Rinnen, Dachfenster, Dachkanten und Hinweise sind keine Wände. Die Seite „Typische Anfängerfehler“ zeigt die wichtigsten.

Die Seitenansicht auf dieser Seite ist ein vereinfachtes Lernschema. Die genaue Form des Daches steht in Schnitten und Ansichten, nicht im Grundriss.

Grundriss = Blick von oben in ein aufgeschnittenes Haus

Stell dir vor, du schneidest das Haus mit einem riesigen Messer **waagrecht** durch – ungefähr in Hüfthöhe des Stockwerks. Den oberen Teil hebst du weg und schaust senkrecht hinunter. Was du siehst, ist der **Grundriss**: Wände als dicke Streifen, Türen als Lücken mit Bogen, Fenster als dünne Linien, dazwischen der Boden.

Was ist ein Dachgeschoss (DG)?


Über den normalen Stockwerken (Erdgeschoss, 1. bis 4. Obergeschoss) liegen hier noch **zwei Dachgeschosse**. Sie stecken im Dach. Darum:

- Sie sind **kleiner** als die Stockwerke darunter – die Außenwände springen nach innen („Rücksprung“).
- Dort, wo das Stockwerk darunter größer ist, entsteht oben eine **Terrasse** im Freien.
- Manche Räume liegen unter einer **Dachschräge**: Die Decke ist dort schief und wird zum Rand hin niedriger.
- Man sieht viele **Dachteile** im Plan: Rinnen, Flachdächer, Dachfenster.

Das **2. Dachgeschoss** ist das obere, oberste der beiden Dachgeschosse.


Die Sprache der Linien: acht Dinge, die du immer wieder siehst

1. Dicke Wand

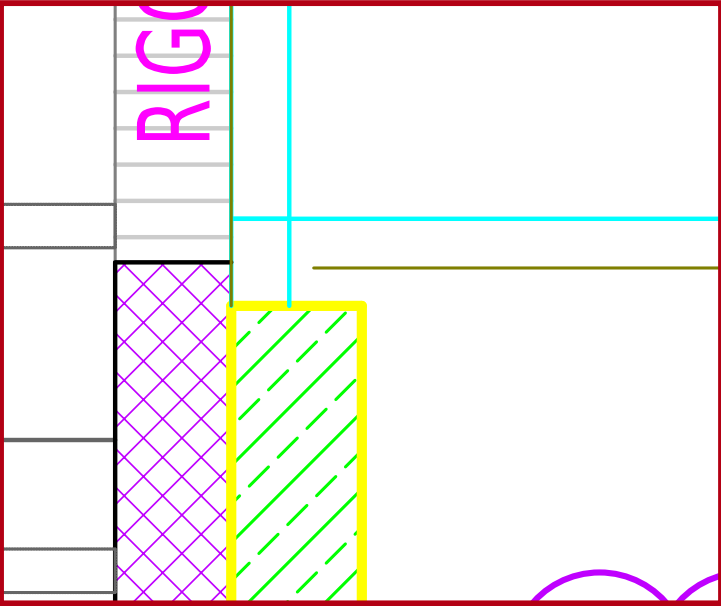


Gelbe Außenlinie, innen grüne Schrägstriche: zwei Kanten mit Material dazwischen.

2. Dünne Wand

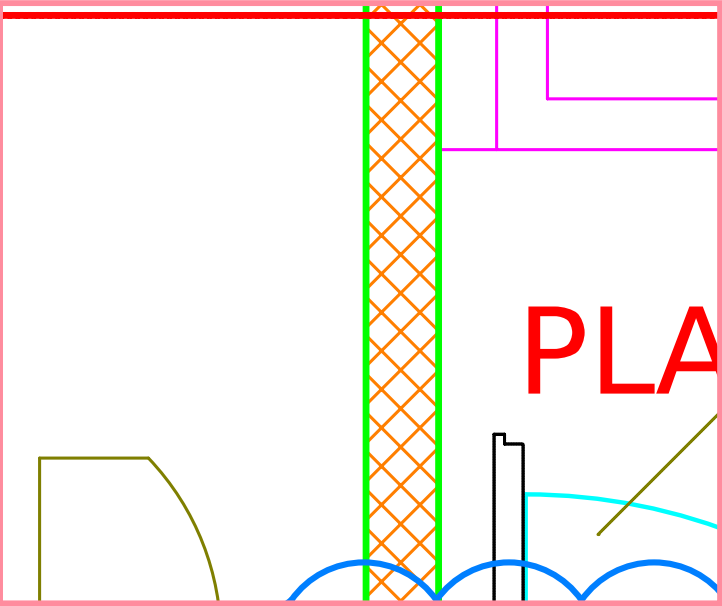


Grüne Außenlinie, orange Gitterstriche. Schmäler, aber genauso eine Wand.

3. Tür

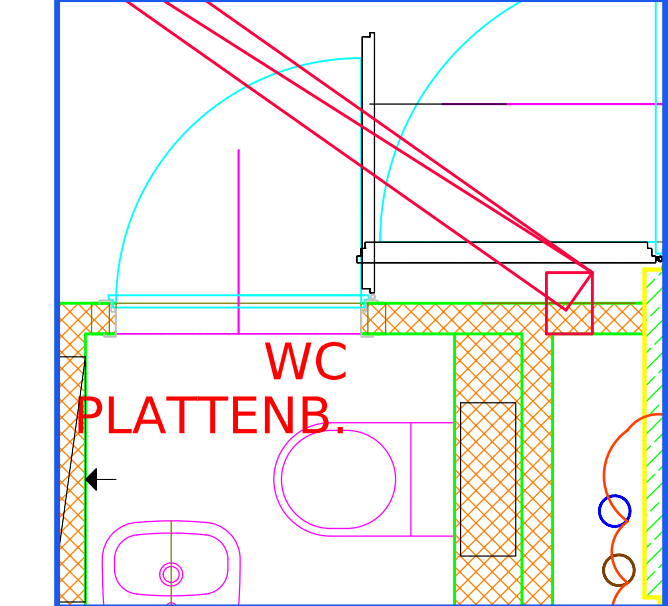


Lücke in der Wand + gerade Linie (Türblatt) + Viertelkreis (Weg der Türkante).

4. Tür nach draußen

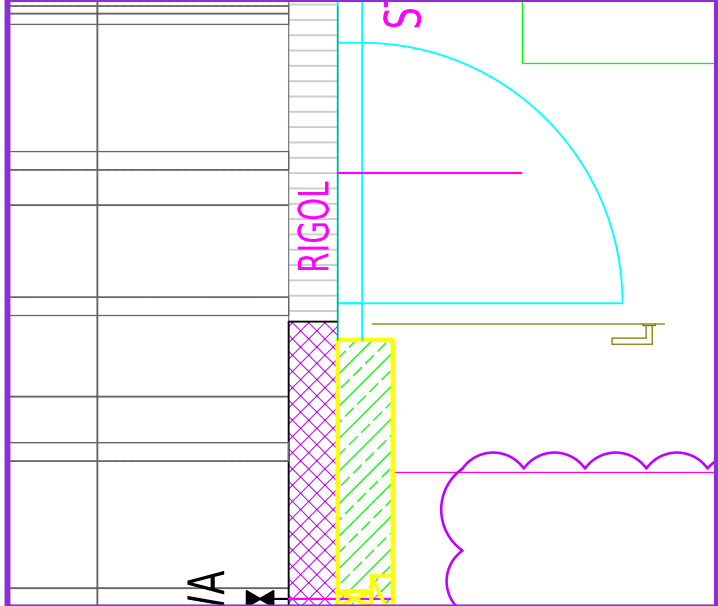


Glastür zur Terrasse: Türbogen in einer Front aus dünnen hellblauen Linien.

5. Terrasse

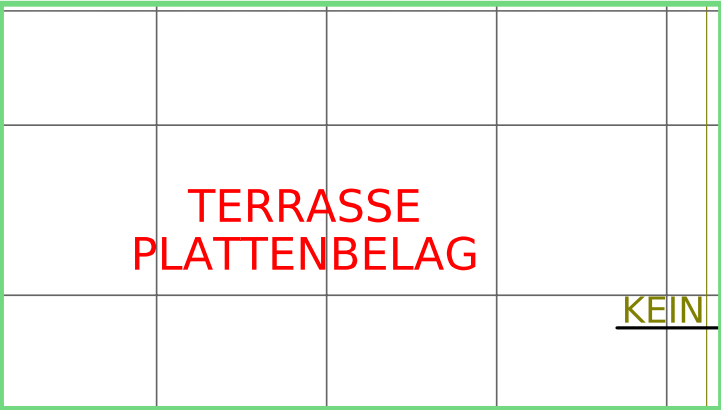

Beschriftung TERRASSE PLATTENBELAG, oft ein Gitter aus Plattenfugen.

6. Dachrand / Rinne

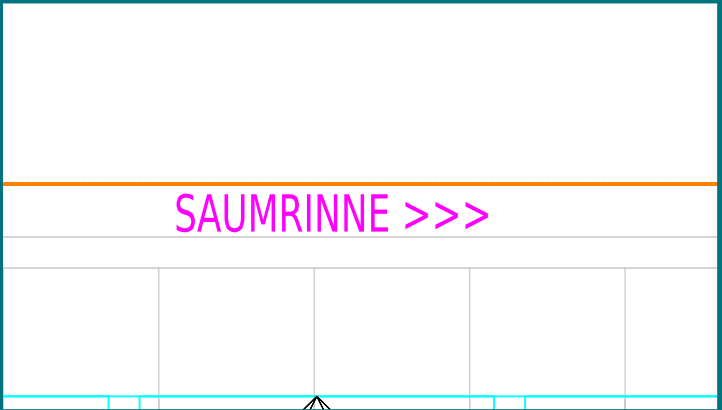


Magenta Text SAUMRINNE mit Pfeilen: Regenrinne am Dachrand – kein Weg.

7. Raumstempel



Rote Schrift: Raumname oben, Bodenbelag unten.

8. Aufzug

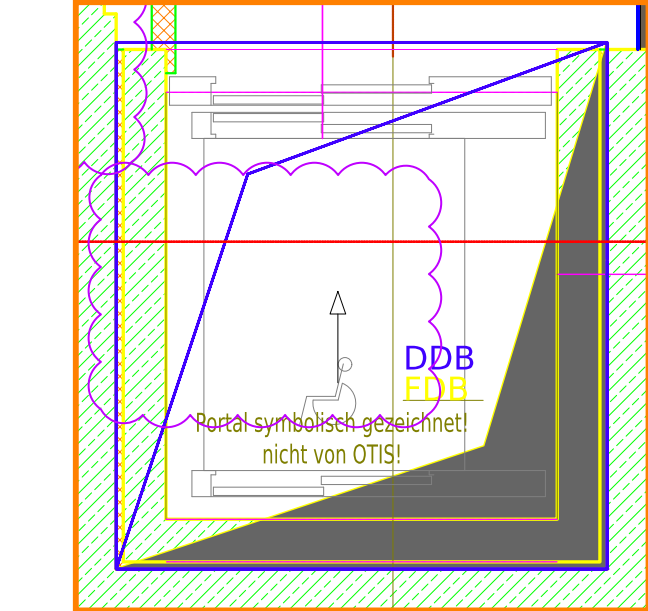

Dicker Schacht mit Kabinen-Rechteck, dunkler Fläche und Rollstuhlsymbol.

[illegible]

Architectural floor plan of a residential unit (T64) showing various rooms and their finishes. The plan includes a kitchen (Küche), living area (Wohnen), bathroom (Bad), and terrace (Terrasse). Rooms are labeled with their respective floor coverings: 'VR PARKETT' (hardwood), 'WOHNEN PARKETT' (hardwood), 'WC PLATTENB.' (tiles), 'BAD PLATTENBELAG' (tiles), and 'TERRASSE PLATTENBELAG' (tiles). The plan also shows a staircase (STUFE) and a fire escape (F). The unit is identified as 'T64'.

[illegible]

The floor plan shows a residential unit with the following features:


- Rooms and Areas:**
 - WOHNEN PARKETT:** Living area with a fireplace (F) and a large window.
 - VR PARKETT:** Veranda area with a glass door.
 - WC PLATTENB:** Toilet with a toilet and sink.
 - BAD PLATTENBELAG:** Bathroom with a bathtub, toilet, and sink.
 - TERRASSE PLATTENBELAG:** Terrace area with a glass door.
- Furniture and Fixtures:**
 - Stuhl-Box:** A box for a chair, located near the living area.
 - WC Abzweiger für Baro-Fix:** A branch for a baro-fix, located near the bathroom.
 - WC Abzweiger für Anpass-Barkett:** A branch for an adaptation barkett, located near the bathroom.
- Construction Details:**
 - Plattenb.:** Plattenbau (slab construction) indicated by a red line.
5



6

Wo ist was? Die große Übersicht

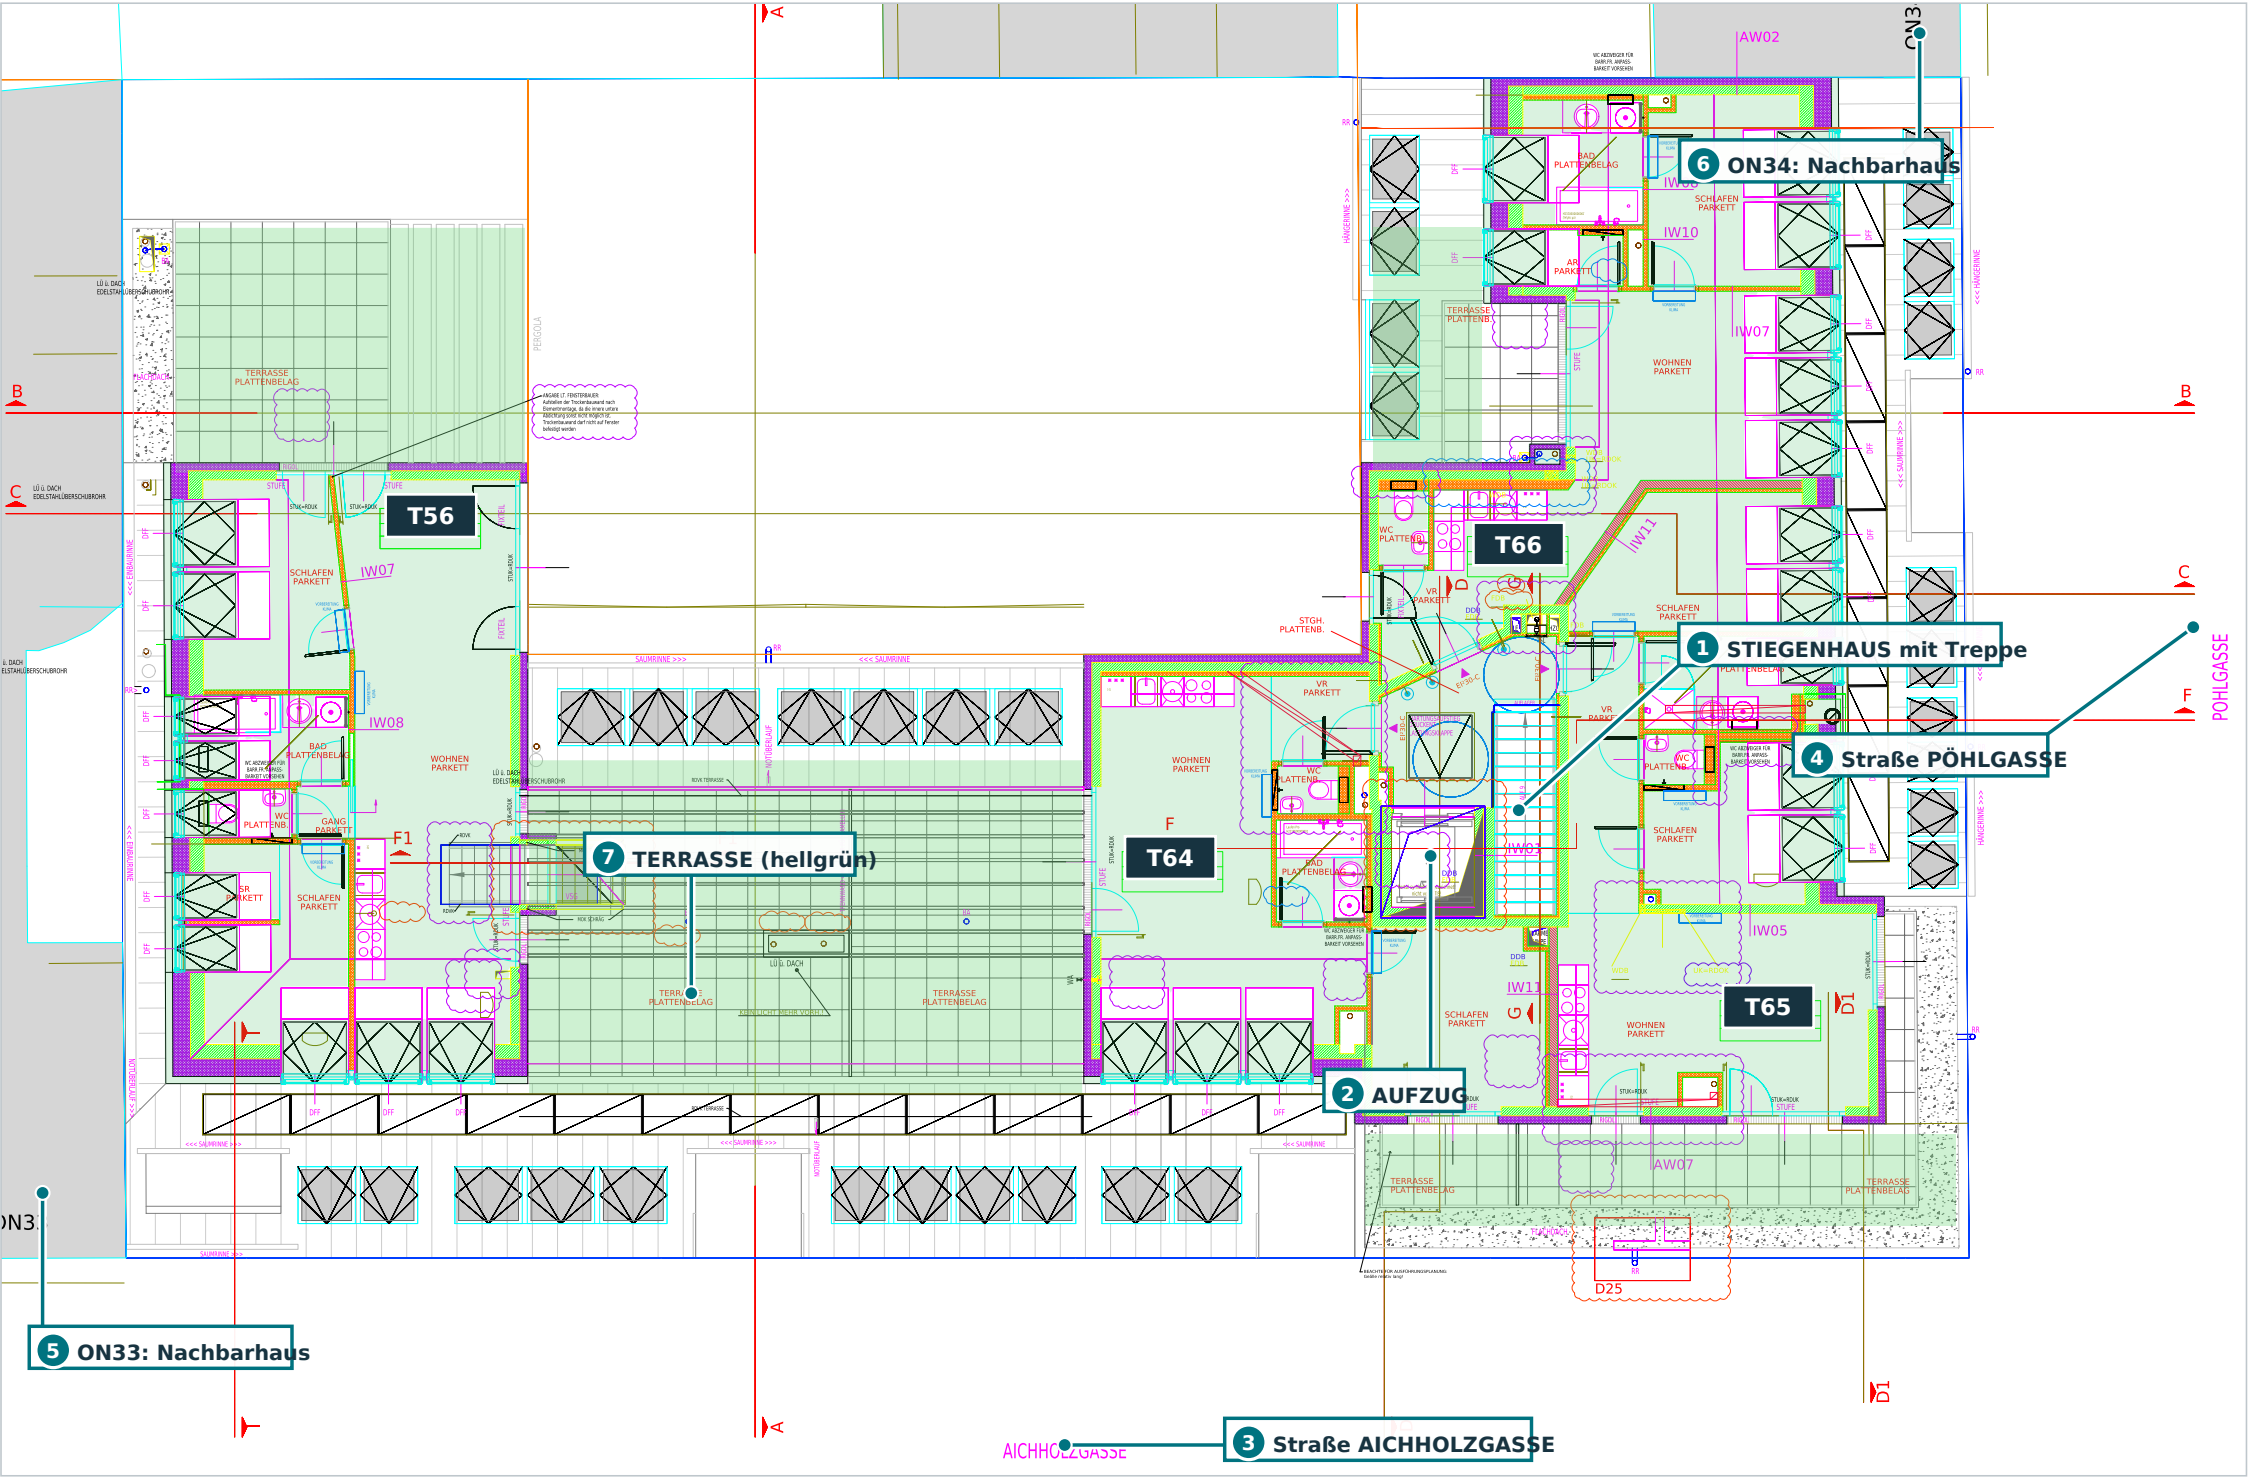

Das 2. Dachgeschoss von oben

Auf diesem Stockwerk stehen 4 Wohnungsnummern: T56, T64, T65, T66. „T“ heißt **Top** = Wohnungsnummer. Im Plan stehen sie in grüner Schrift in einem kleinen Kasten.

T56 steht in **beiden** Dachgeschossen. Das deutet auf eine Wohnung über zwei Ebenen (**Maisonette**) hin. Eine Verbindungstreppe ist im Grundriss aber nicht eindeutig zu erkennen – das muss ein Schnitt bestätigen.


Die Wohnungen erreicht man über das **Stiegenhaus** (1) und den **Aufzug** (2) in der Mitte.

Die **Straßen** (3, 4) stehen außen am Plan. Die **grauen Flächen** (5, 6) sind Nachbarhäuser.

Die **hellgrünen Flächen** (7) sind Terrassen und Balkone. Sie sind im Dachgeschoss besonders groß, weil das Haus hier schmaler wird.

Weiß zwischen und um die Wohnungen: **Dach** oder offener Hof – dort ist auf diesem Stockwerk kein Raum.

Alle Wände im Überblick - rot

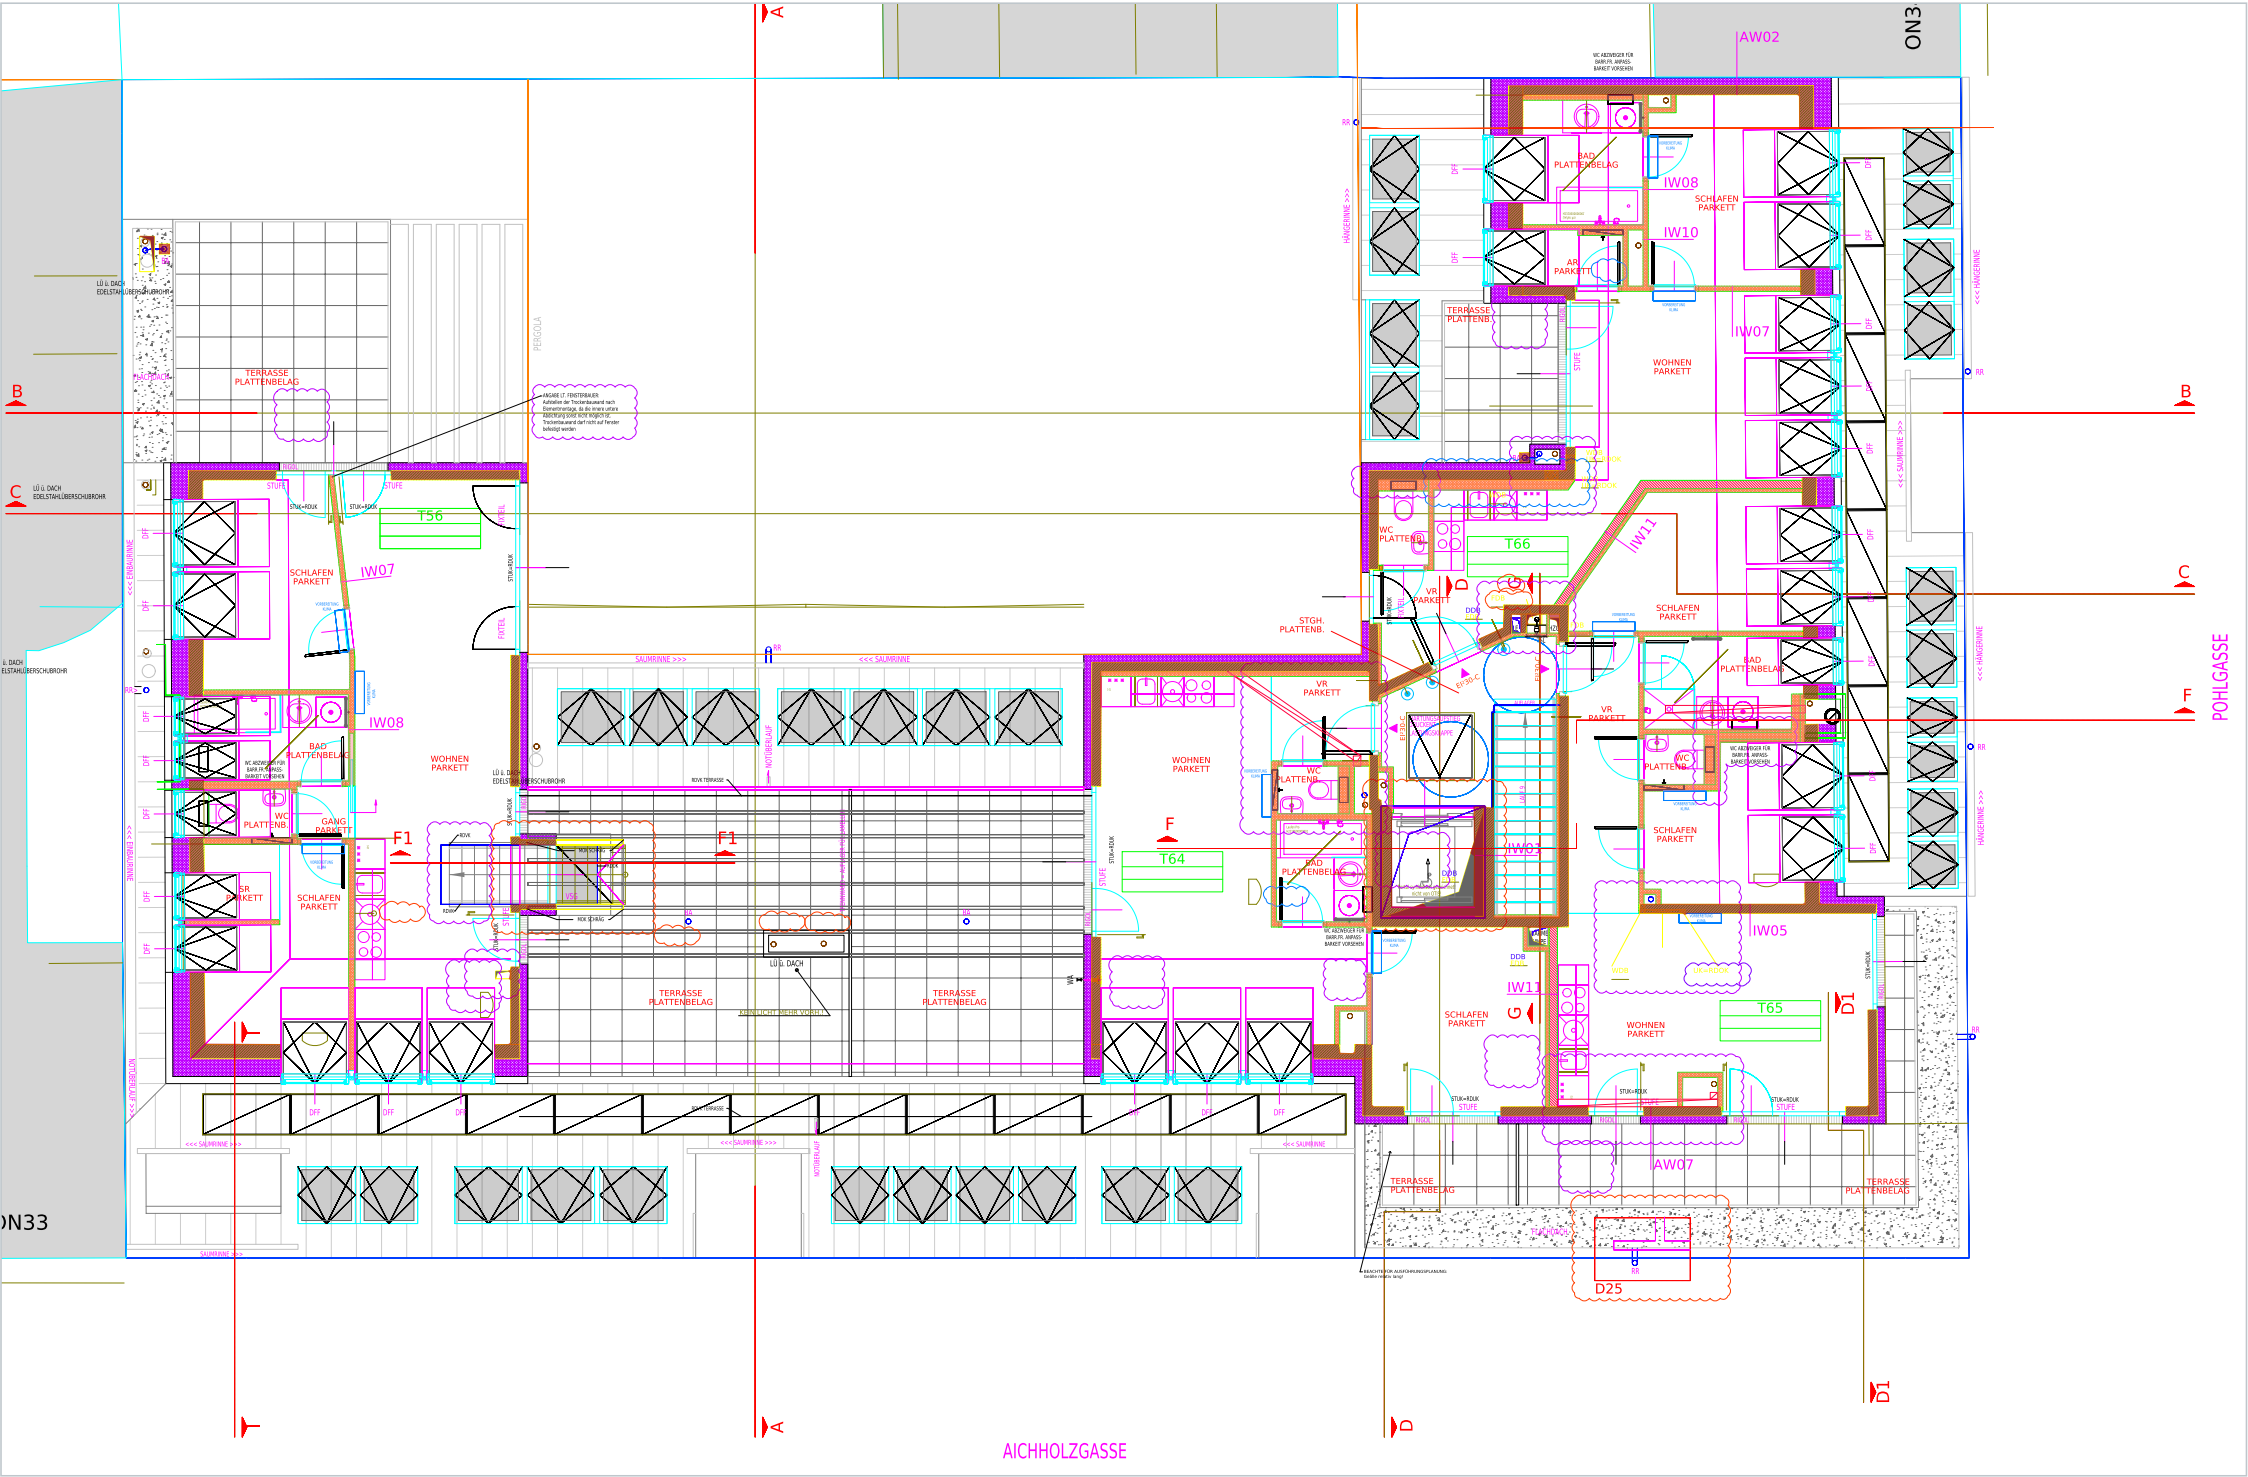

Was ist eine Wand?

Ein fester, senkrechter Bauteil, der zwei Bereiche **trennt**. Man kann **nicht** durch sie hindurchgehen.

Wie sieht sie im Grundriss aus?

Als **Streifen**: zwei parallele Linien (die Wandseiten), dazwischen ein Muster (Schraffur = „hier ist Material“).

Woran erkenne ich die Wände hier?

Dunkelrot = gelbe Umrandung + grüne Schrägstriche: dicke Wände (Wohnungstrennwände, Stiegenhaus, Außenwände).

Hellrot = grüne Umrandung + orange Gitterstriche: dünne Wände in den Wohnungen.

Besonderheit Dachgeschoss


Viele Außenseiten sind hier **keine gemauerten Wände**, sondern große **Glasfronten** zu den Terrassen oder die **Dachschräge**. Darum ist das Rot außen oft unterbrochen. Glas findest du auf der Seite „Fenster und Glas“.

Übung

Such eine Wohnung und folge ihrer roten Umrandung. Wo hört Rot auf? Dort ist eine Tür oder Glas.

Ob eine Wand tragend ist, steht nicht im Plan.

Dicke und dünne Wände in der Wohnung T64

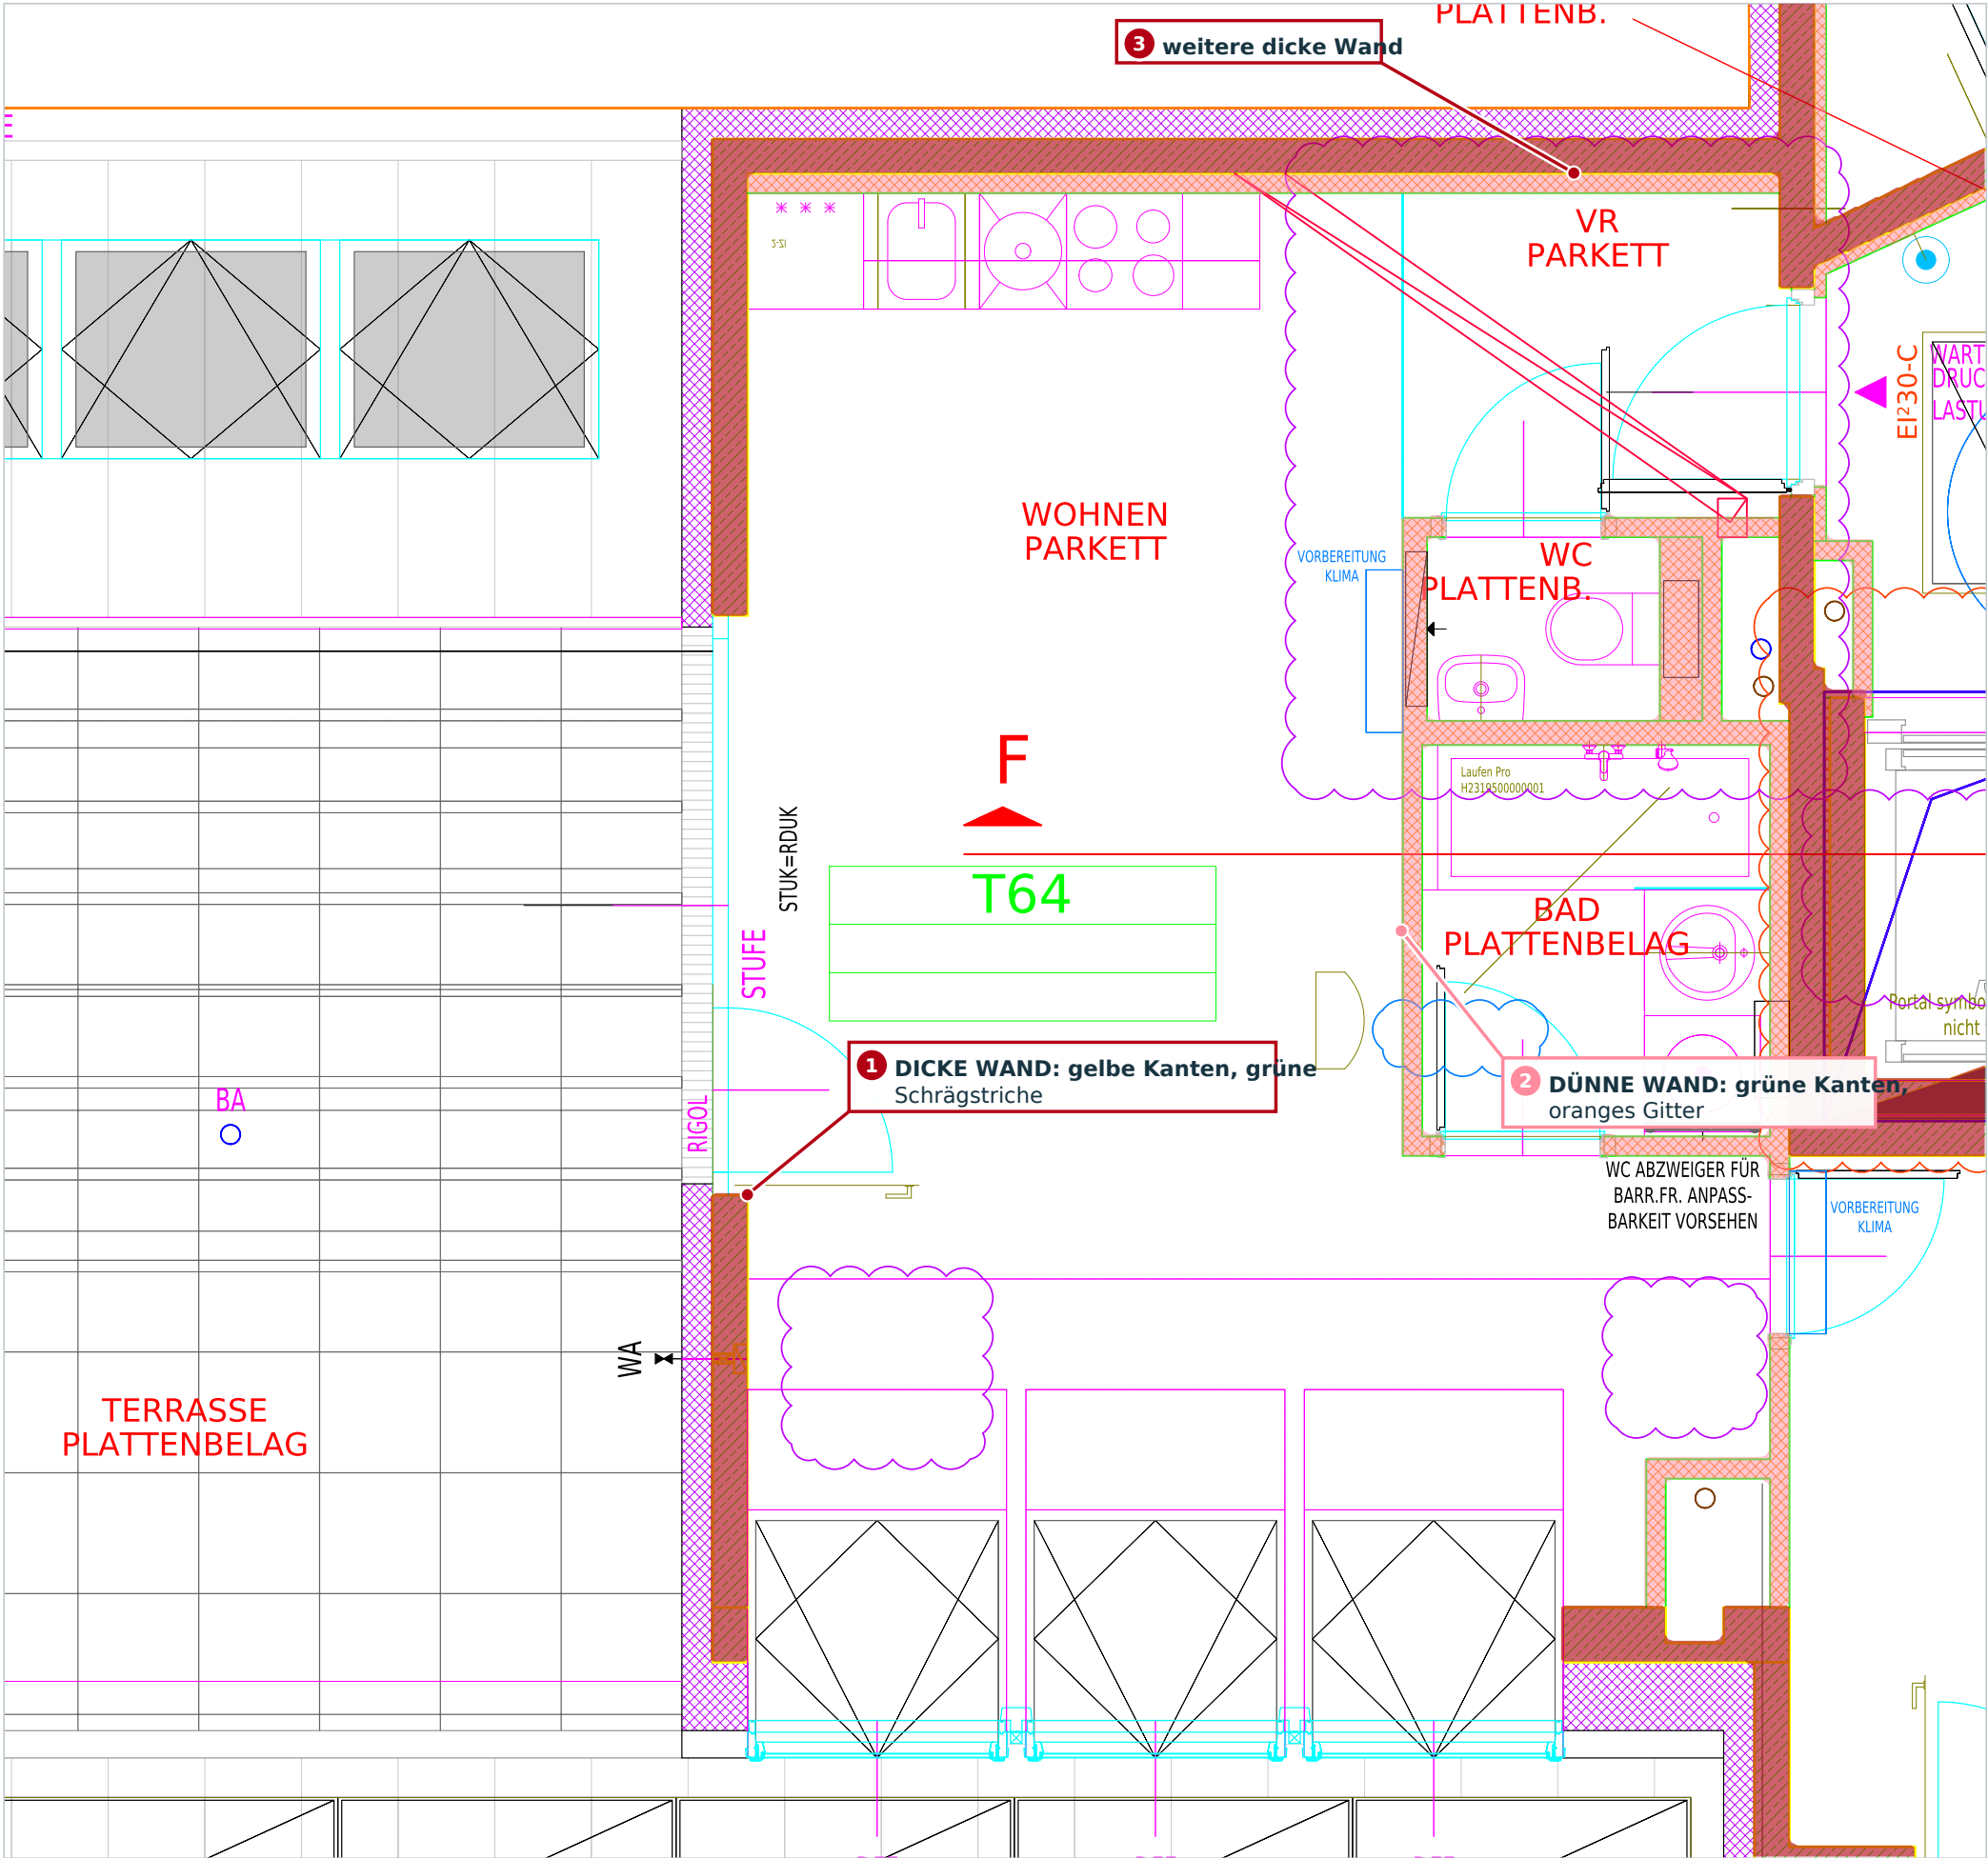


Zwei Arten, beide sind Wände
Egal ob dick oder dünn – durch keine Wand kann man gehen.

Dicke Wand (dunkelrot)
Was: eine massive Wand. **Wie:** breiter Streifen, gelbe Außenlinie, grüne Schrägstriche. Sie trennt meist Wohnungen voneinander oder vom Stiegenhaus.

Dünne Wand (hellrot)
Was: eine schmalere Trennwand. **Wie:** grüne Außenlinie, orange Gitterstriche. Sie trennt meist Räume innerhalb einer Wohnung, z. B. Bad und WC.


Der Drei-Punkte-Trick
1. Zwei parallele Linien? 2. Muster dazwischen? 3. Schließt der Streifen an andere Wände an? Nur wenn alles „ja“ ist, ist es eine Wand.

Die Kürzel wie IW03 oder AW07 nennen den Wandtyp. Die genaue Bauart steht in einem Wandkatalog, der nicht beiliegt.

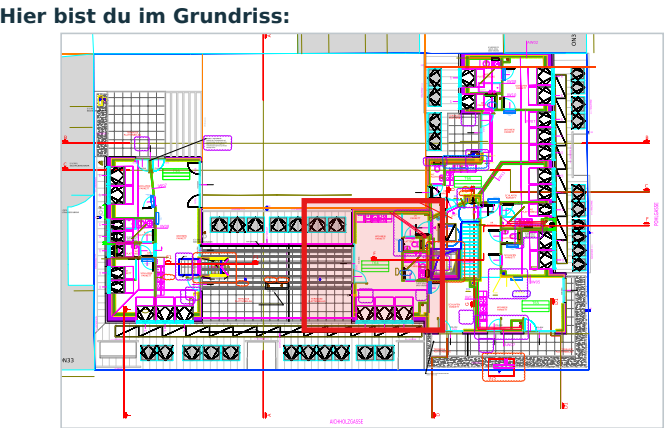

TÜREN 1/4

Alle Türen im Überblick (24 Türblätter)

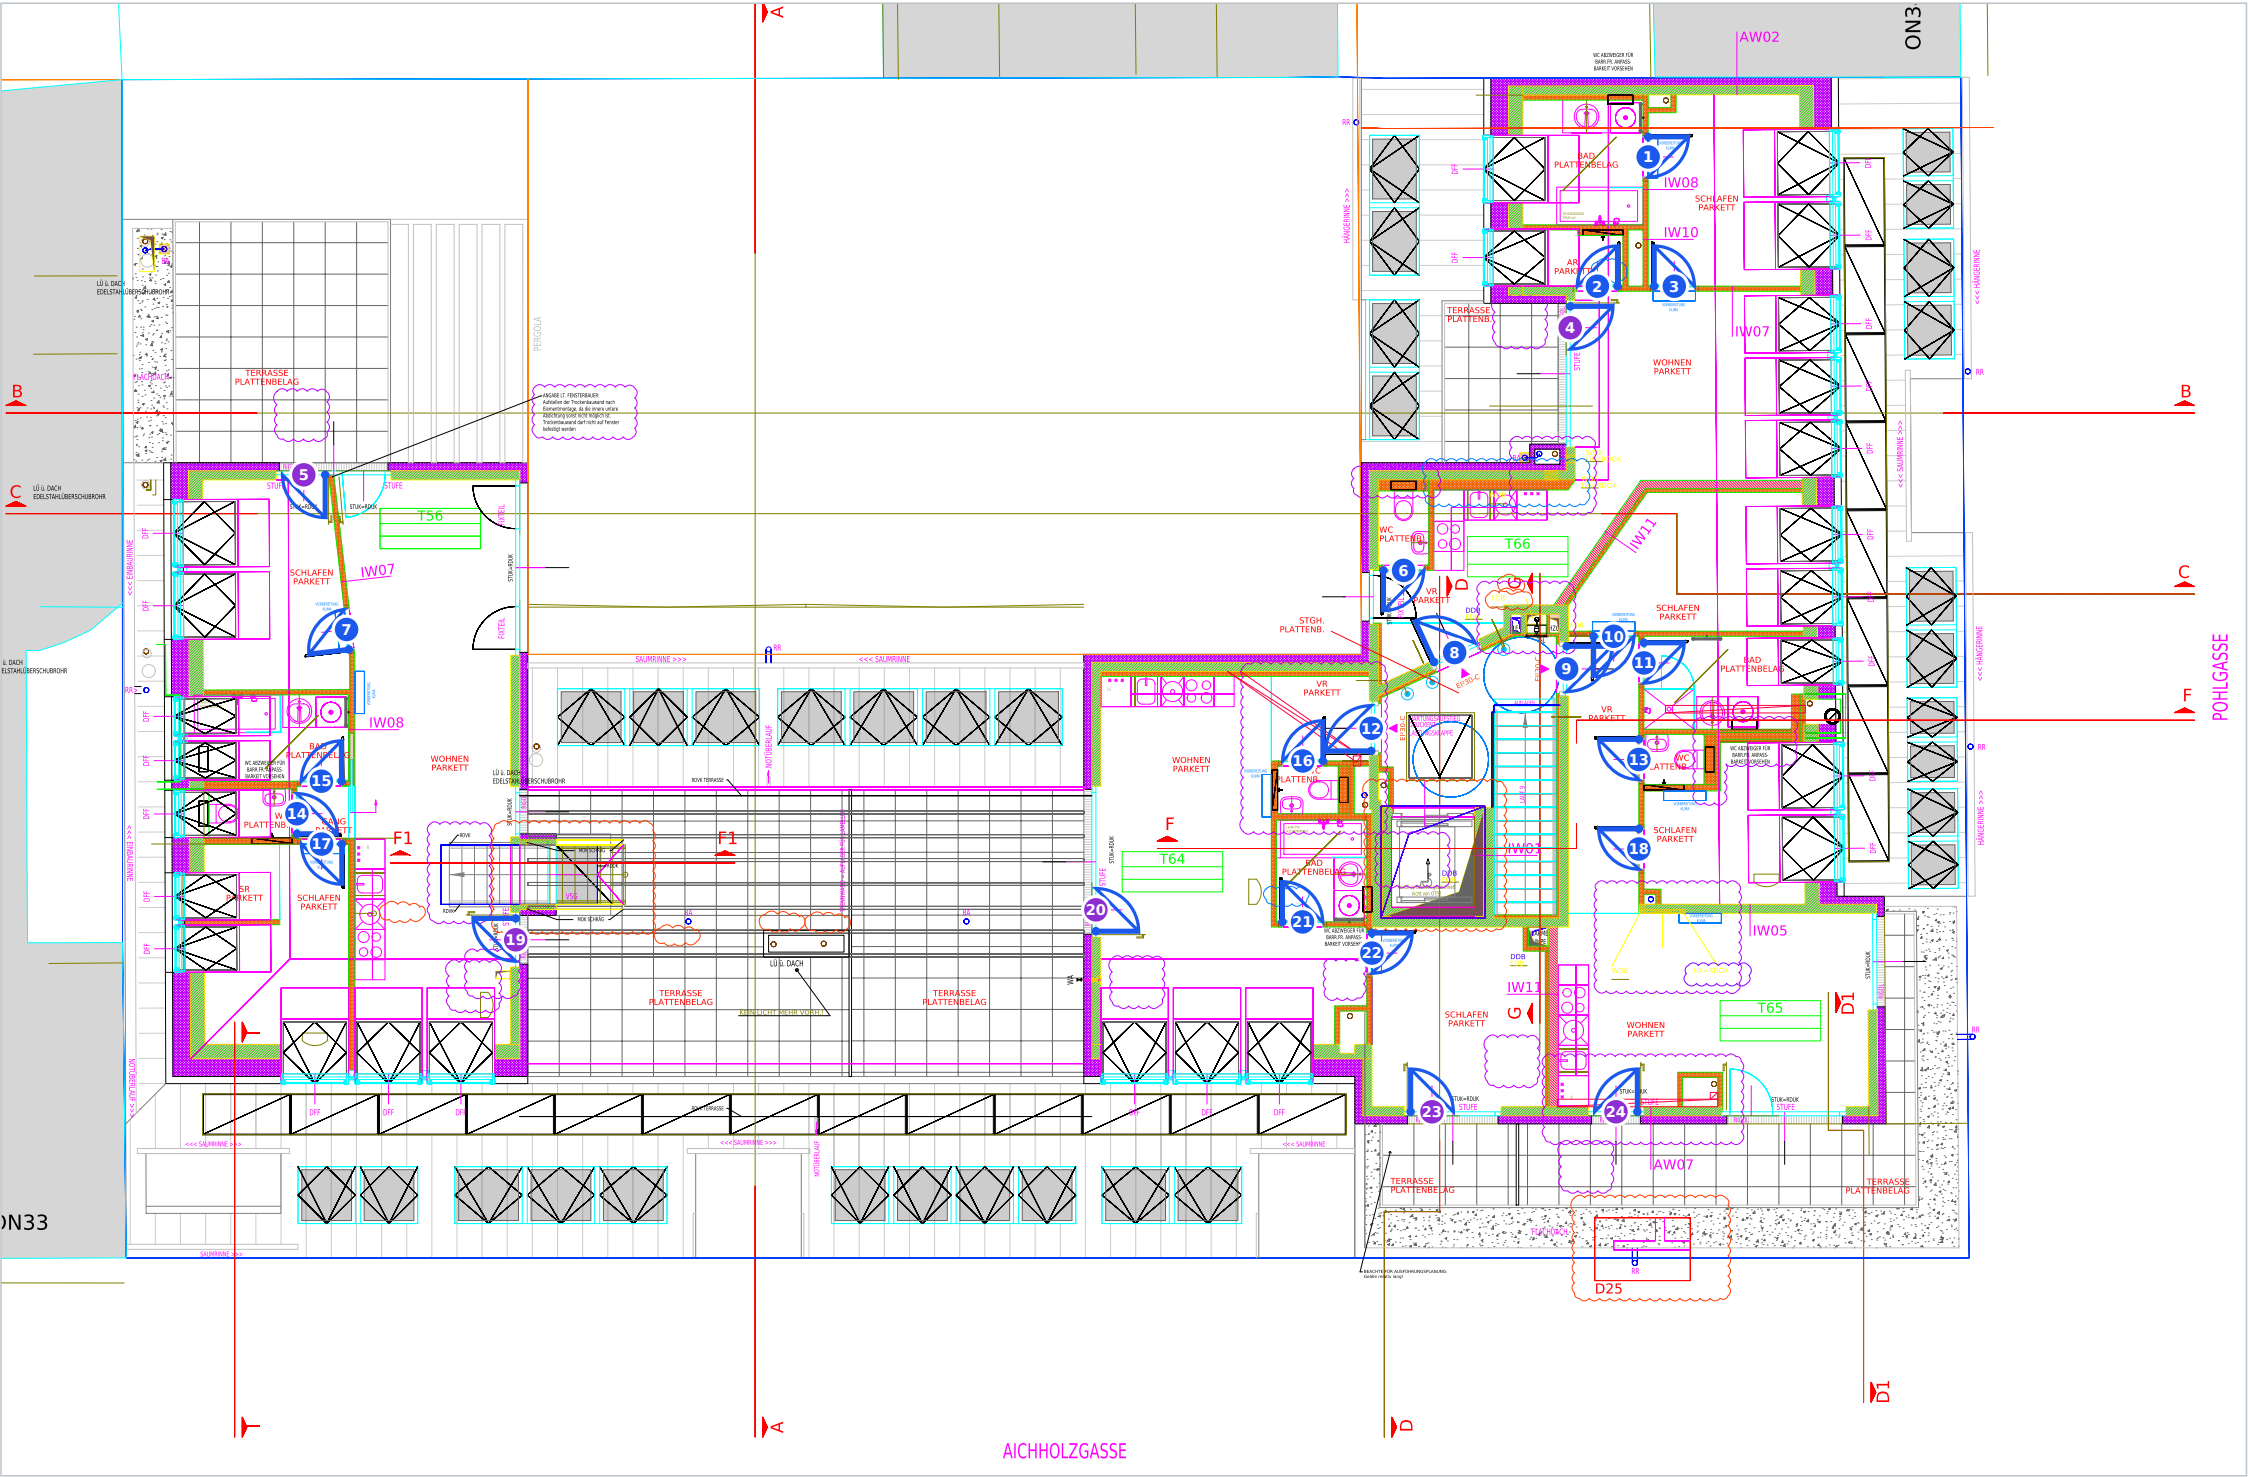

Was ist eine Tür?
Eine **bewegliche Platte** in einer Lücke der Wand. Offen kann man durchgehen, geschlossen nicht.


Wie sieht sie im Grundriss aus?
1. **Lücke** in der Wand, 2. **gerade Linie** = Türblatt (immer offen gezeichnet), 3. **Viertelkreis** = Weg der Türkante.

Was zeigt diese Seite?
24 Türblätter. **Blaue Nummer:** Tür innen. **Violette Nummer** (6 Stück): Tür nach draußen, meist auf eine Terrasse.

Übung
Such die Tür Nr. 12: Das ist der Eingang der Wohnung T64. Such dann Tür Nr. 20: Hier geht es auf die Terrasse.

Die Türen wurden aus den Bogenlinien erkannt. Schiebetüren ohne Bogen werden so nicht gefunden; Türen in Glasfronten können fehlen. Der Plan zeigt nicht, ob Türen offen oder versperrt sind.

Eine Drehtür Stück für Stück lesen (Tür Nr. 16)

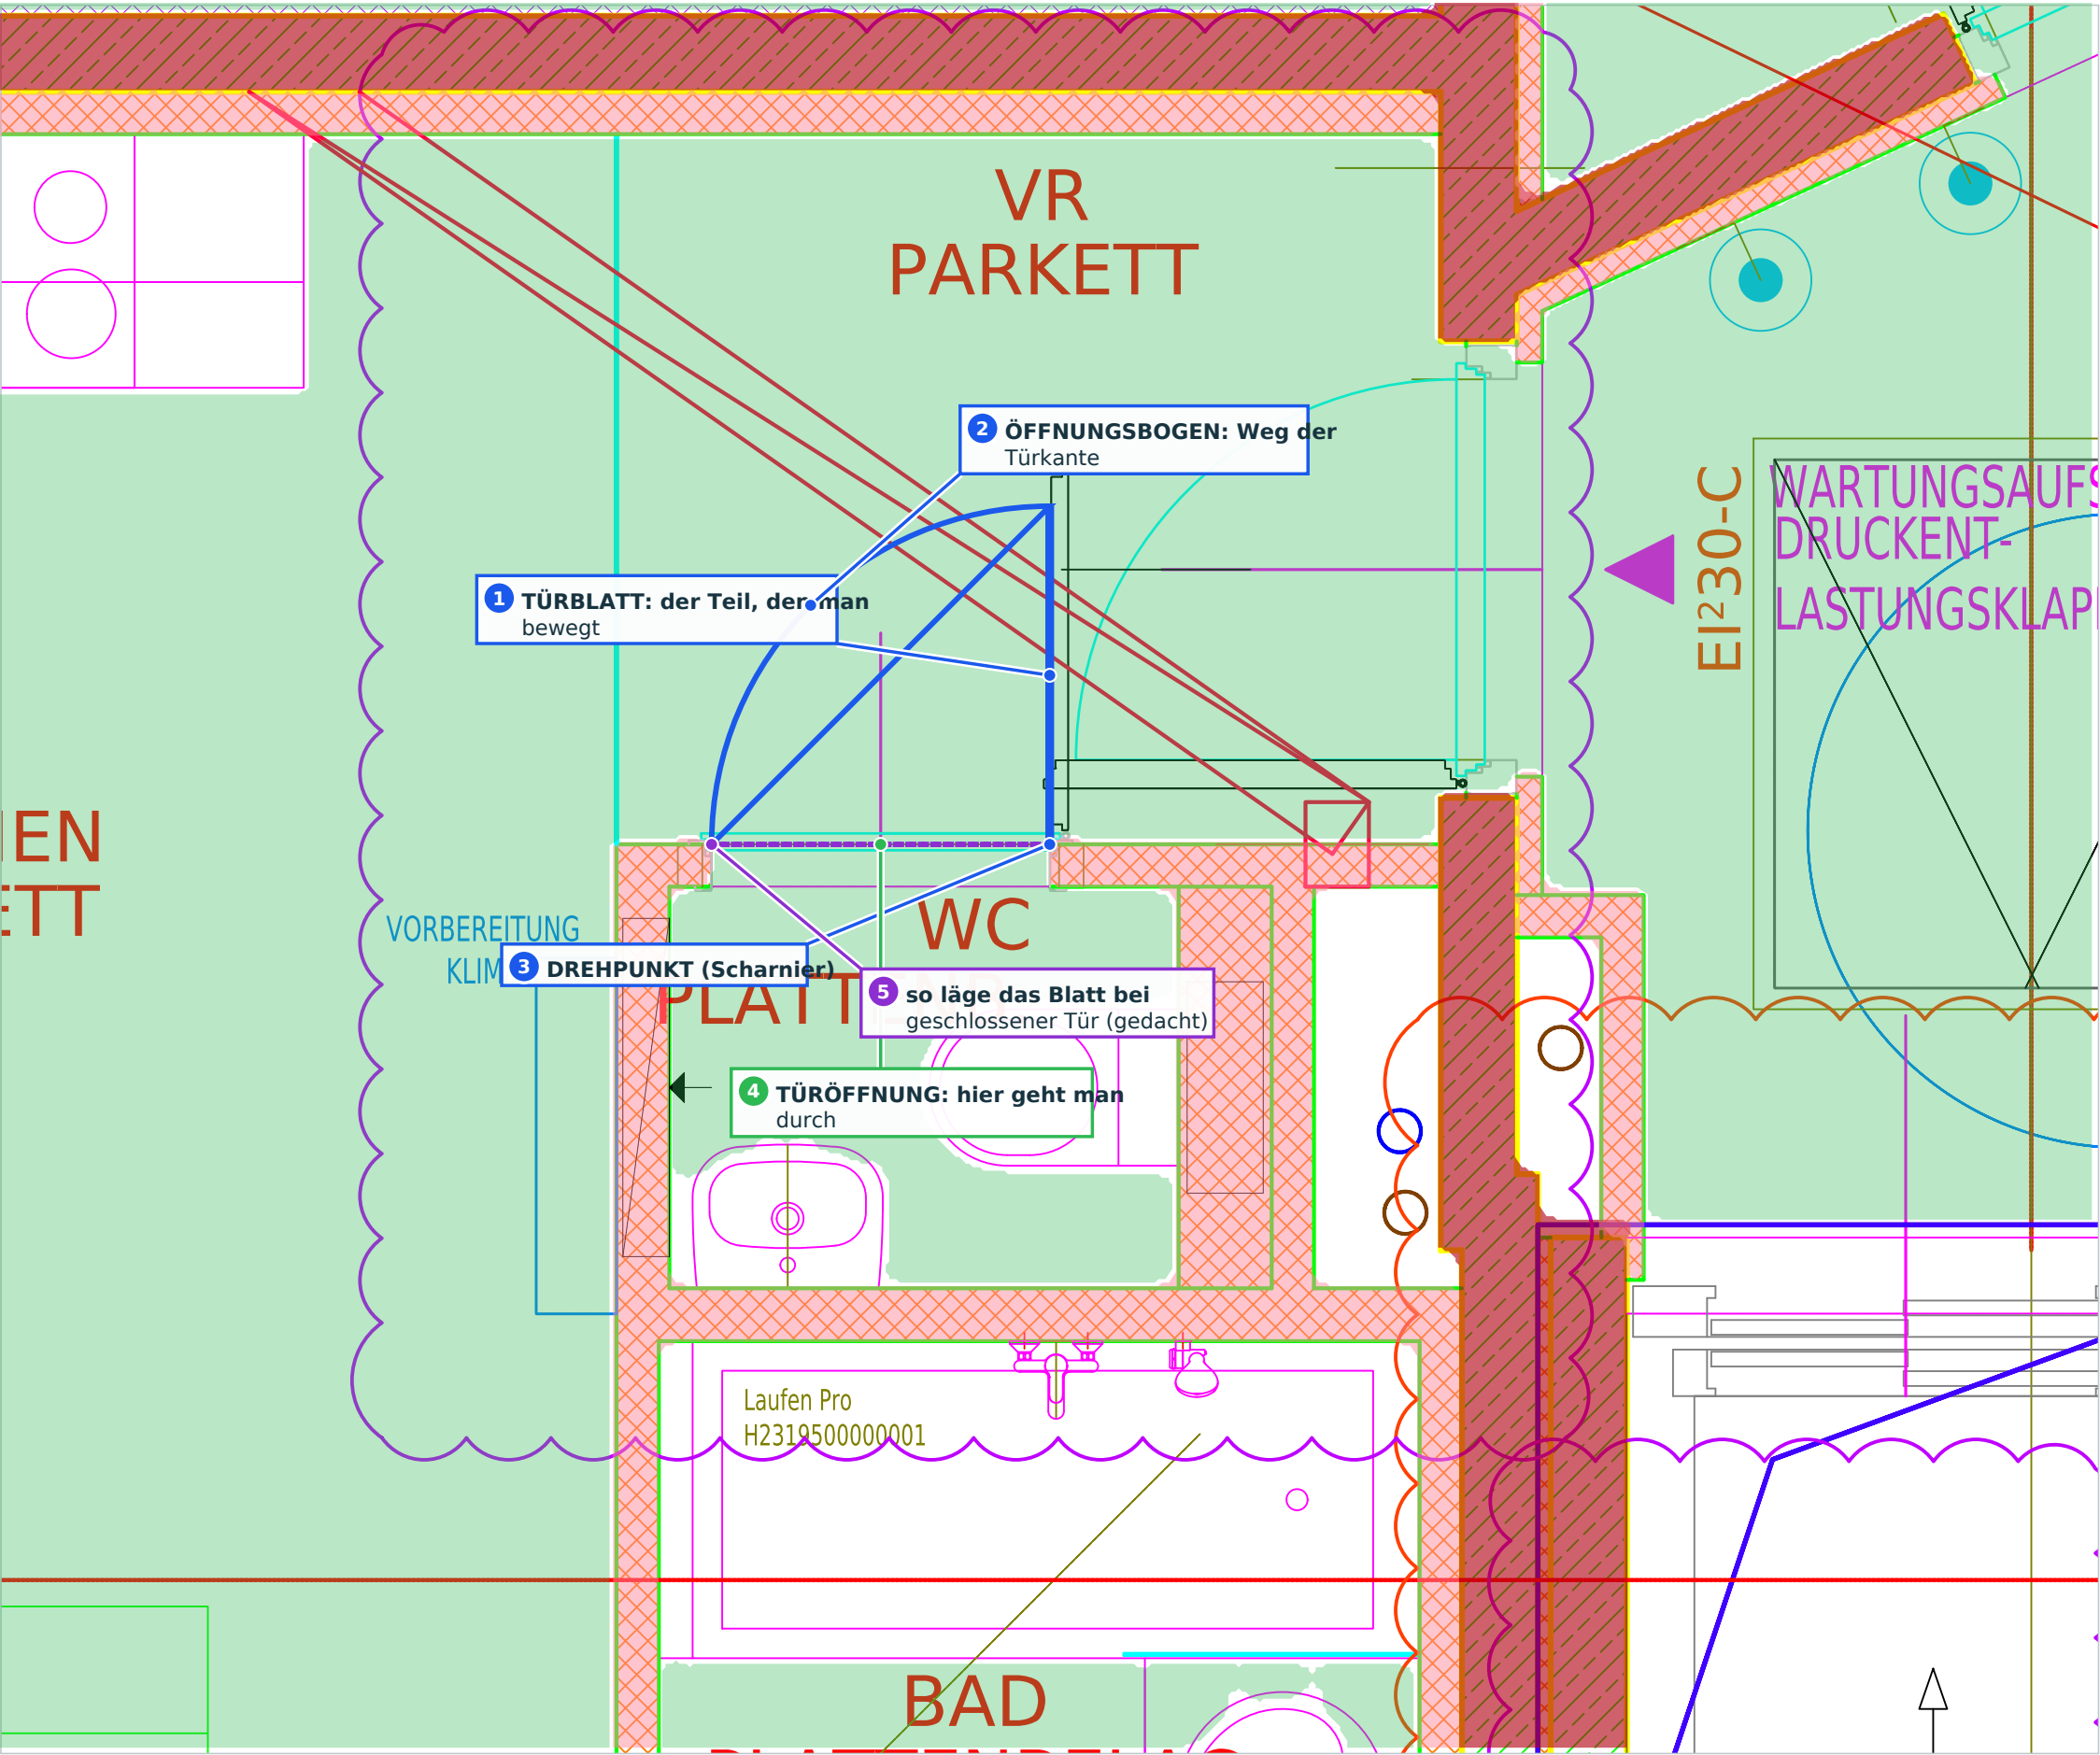

Was ist das?

Eine **Drehtür** in der Wohnung T64 – man drückt die Klinke, die Tür dreht sich um eine Seite.


Wie sieht sie im Plan aus?

- (4) Die Wand ist unterbrochen: die Lücke.
- (1) Das Türblatt ist eine gerade Linie, immer **offen** gezeichnet.
- (3) Am Drehpunkt hängt die Tür in den Scharnieren.
- (2) Der Viertelkreis zeigt, wie weit die Tür in den Raum schwenkt. Dort muss Platz bleiben.
- (5) Gestrichelt: die geschlossene Lage. Steht so nicht im Original.


In welche Richtung geht sie auf?

Immer zur Seite, auf der der **Bogen** liegt.

Hier bist du im Grundriss:

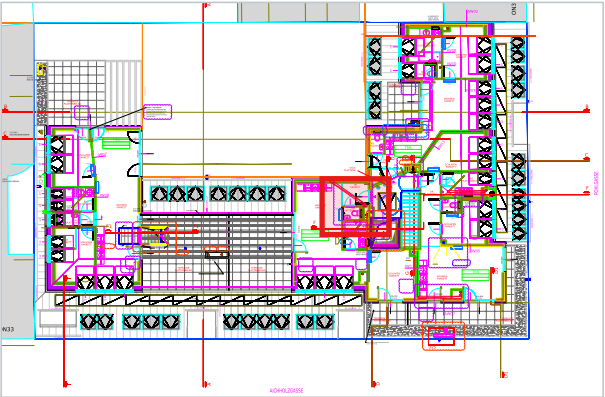

Die Wohnungseingangstür von T64

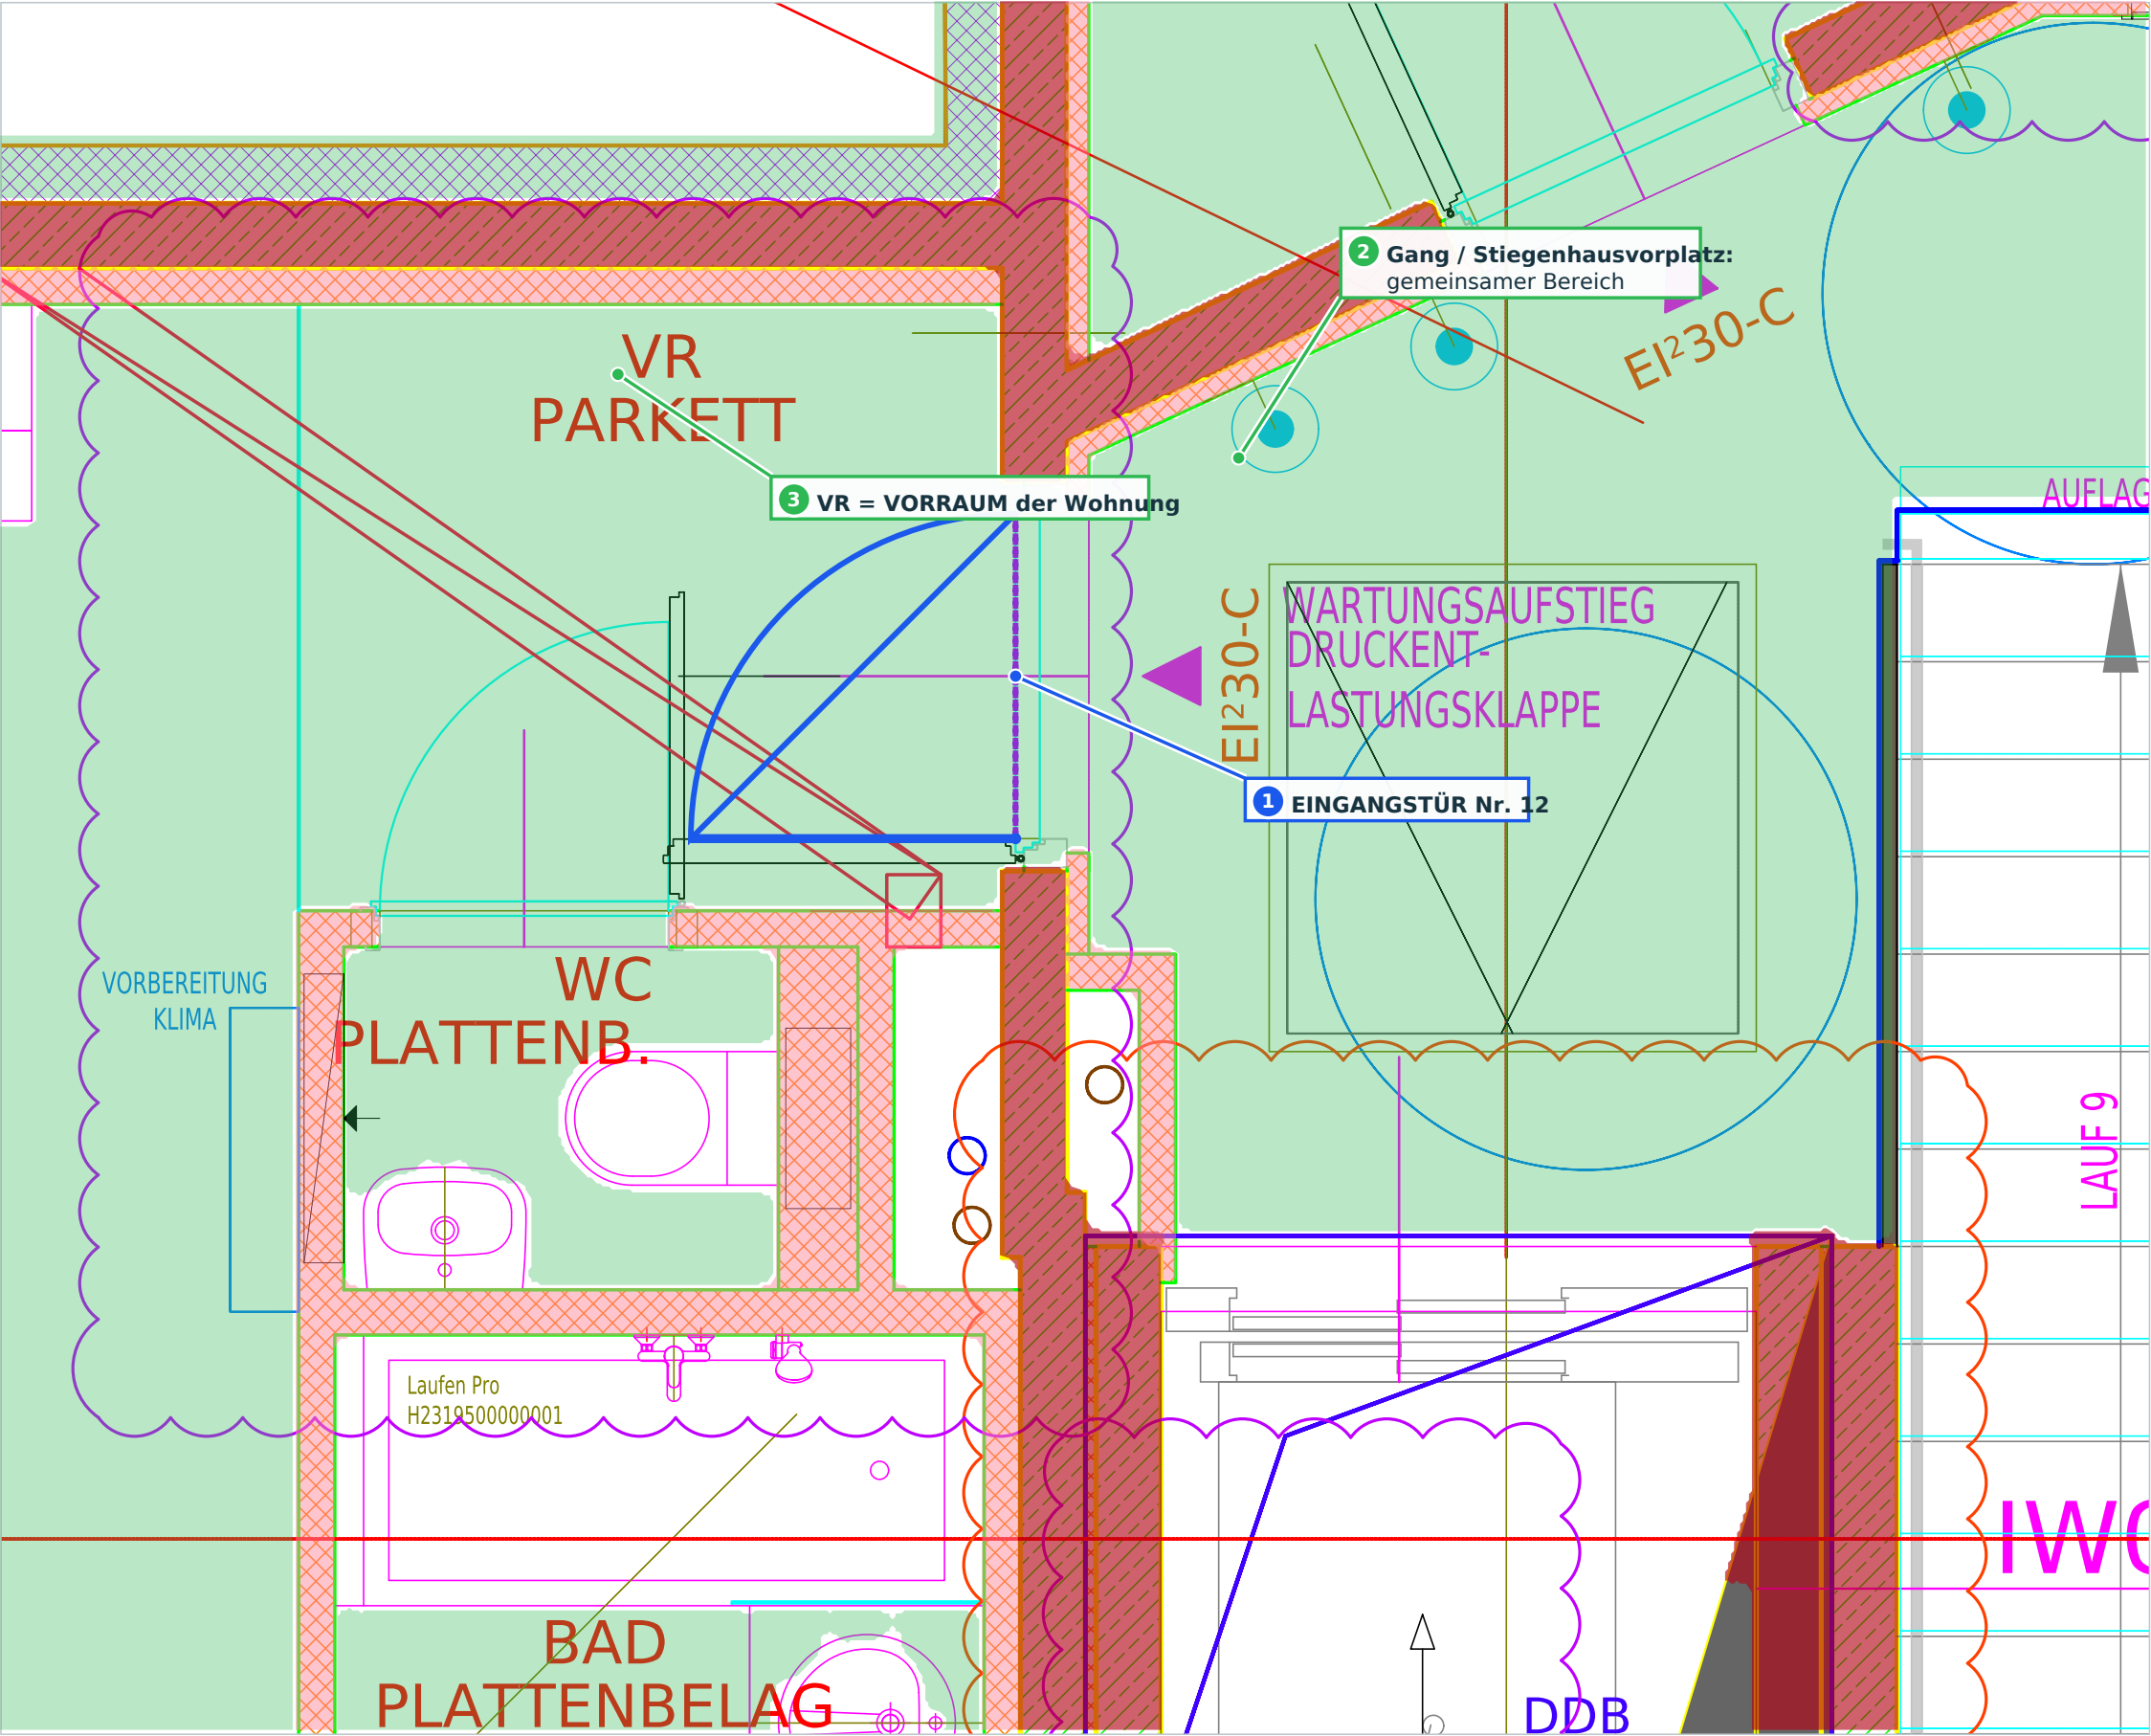

Was ist das?

Die Tür zwischen dem **gemeinsamen Bereich** (2), den alle Bewohner benutzen, und dem **Vorraum** (3) der Wohnung T64.

Woran erkenne ich sie?


Sie sitzt in einer **dicken Wand** zwischen Allgemeinbereich und Wohnung. Wie jede Tür: Lücke, Türblatt, Bogen (1).

Was bedeutet „EI230“ daneben?


An Wohnungseingangstüren steht meist eine Angabe wie **EI230**: eine Brandschutzklasse. Die Tür soll ein Feuer **30 Minuten** aushalten. Mit **-C** schließt sie zusätzlich **von selbst**.

Ob der Bogen hier in die Wohnung oder nach außen zeigt, siehst du direkt im Ausschnitt: Die Tür geht immer zur Seite des Bogens auf.

Hier bist du im Grundriss:

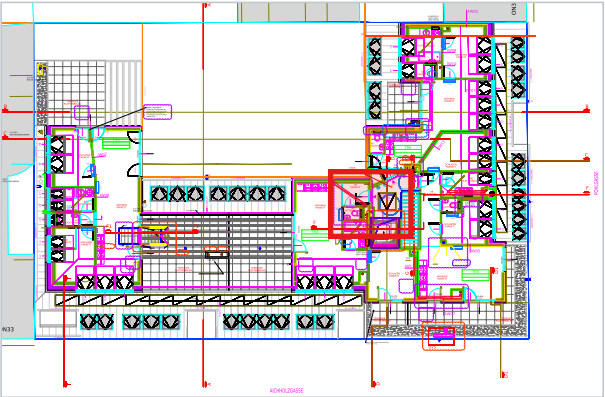

Die Tür nach draußen: auf die Terrasse

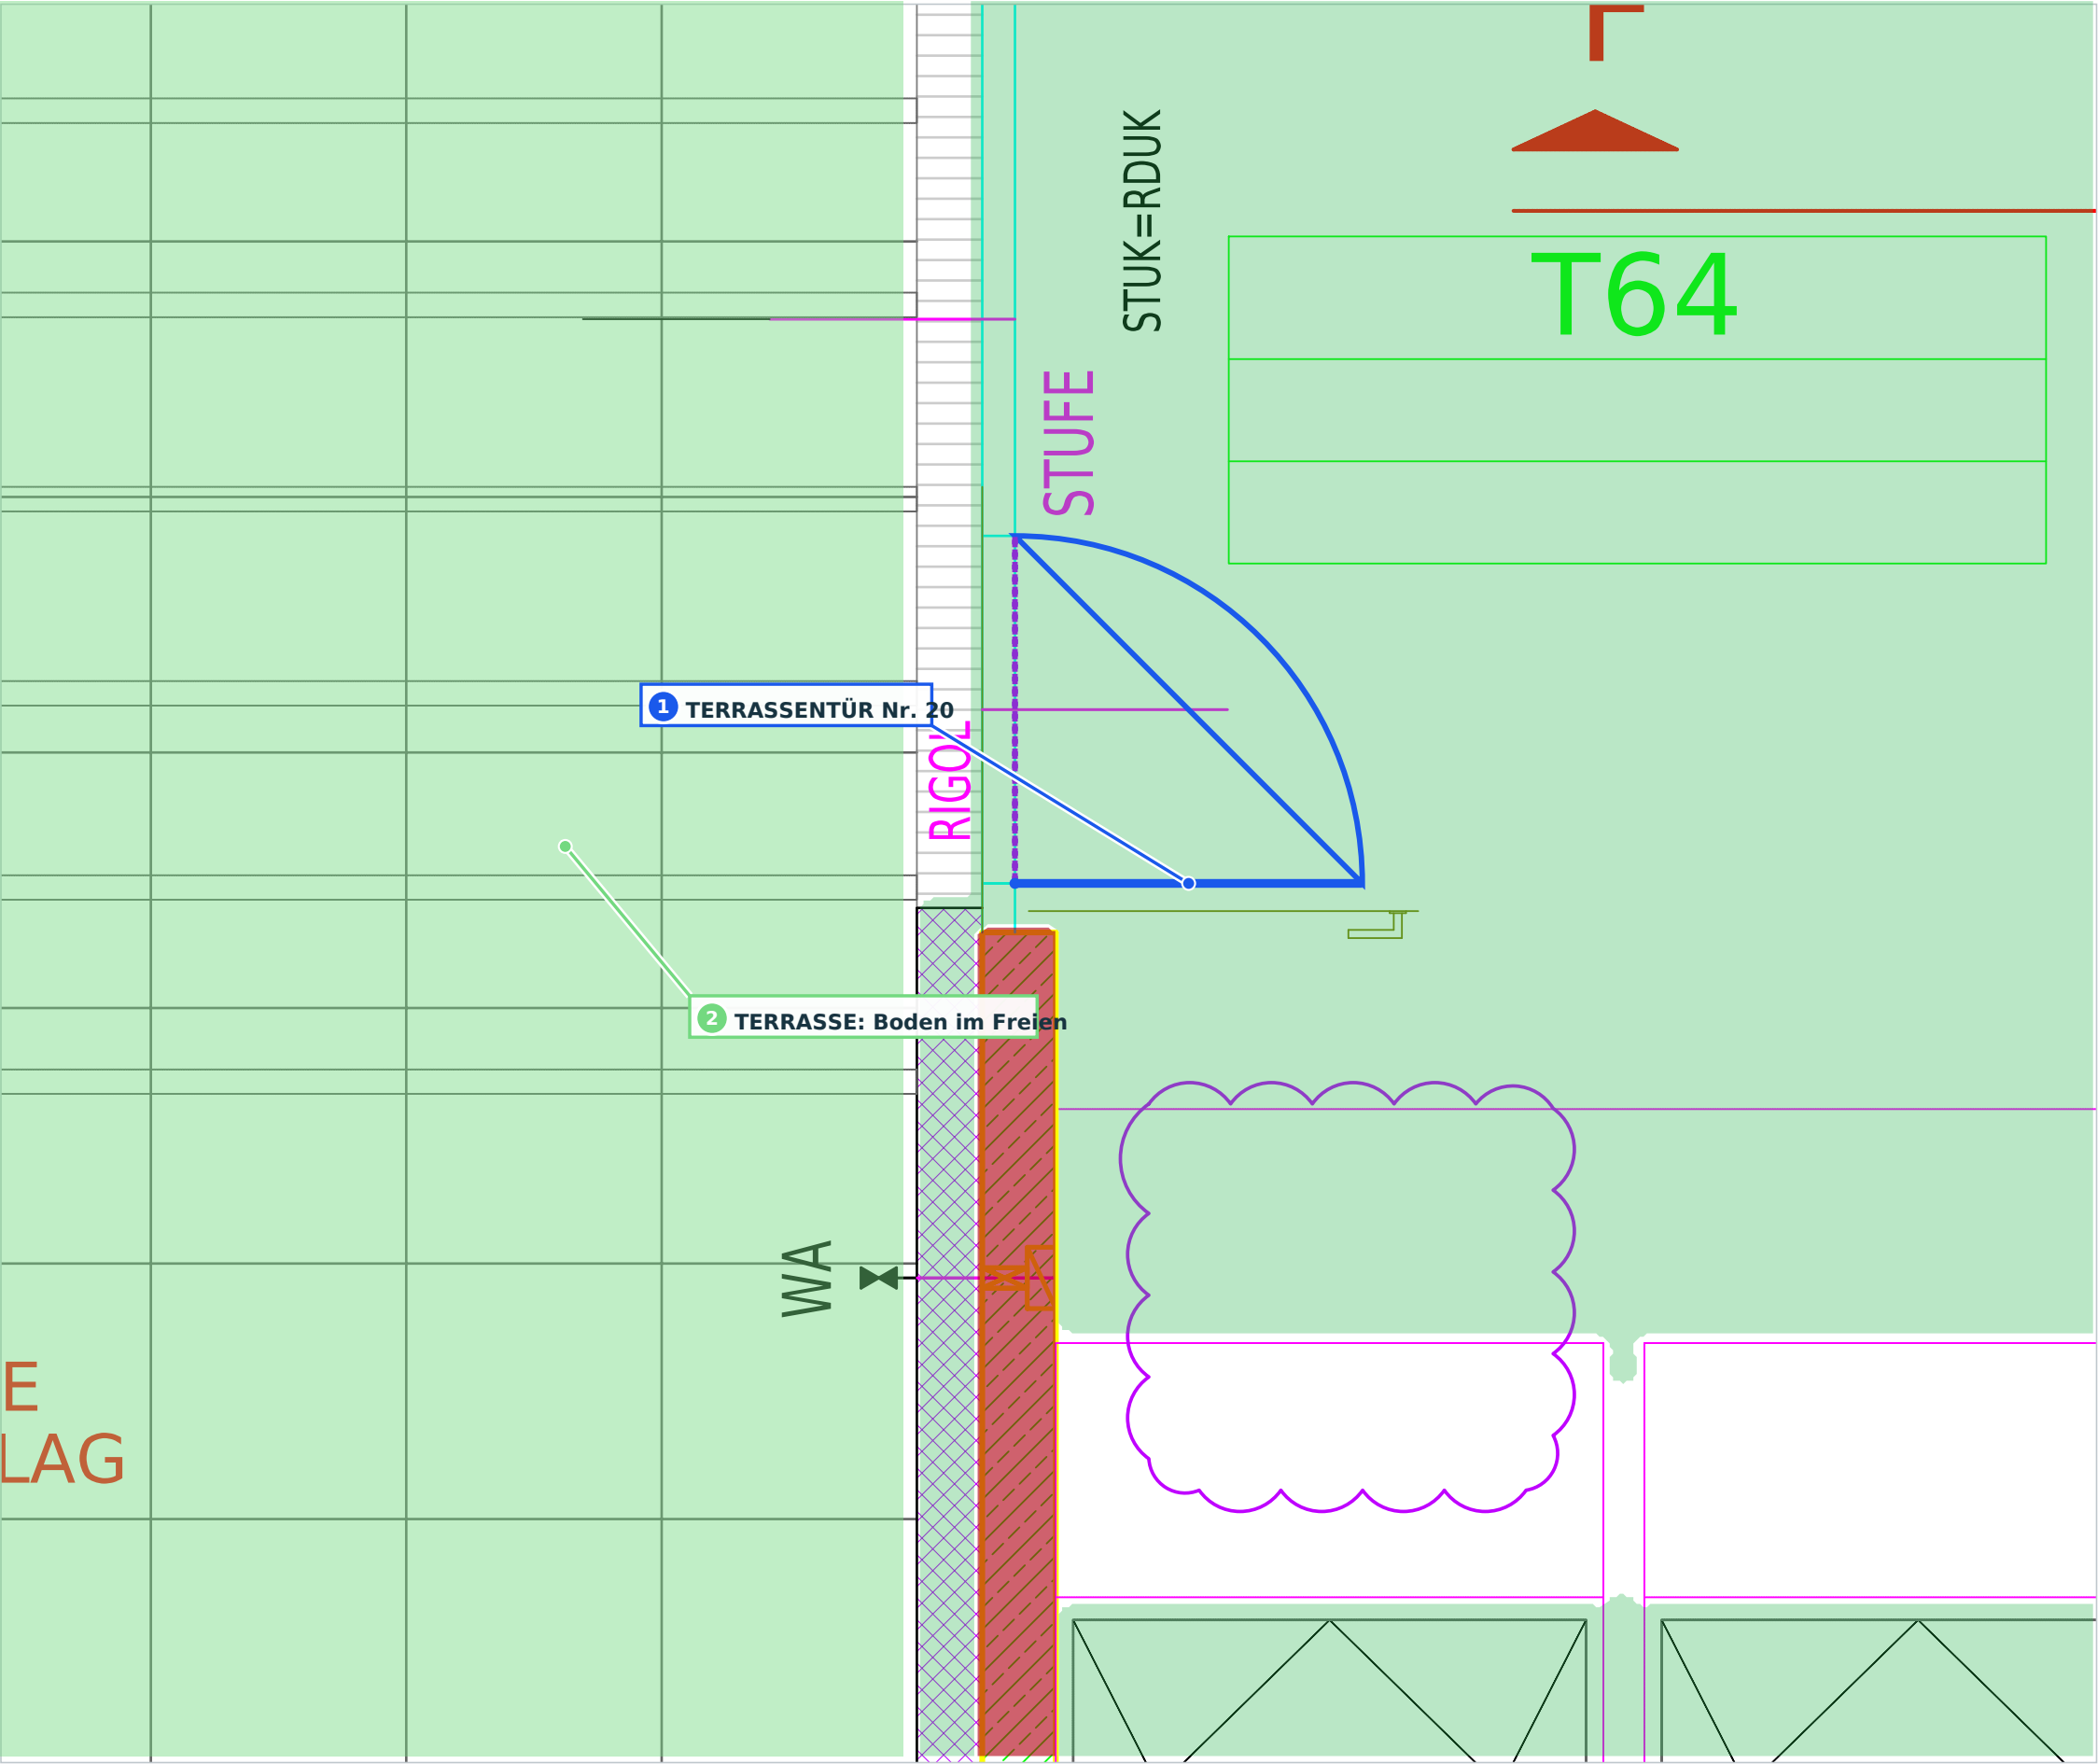

Was ist das?

Eine Tür in der Außenwand oder Glasfront, durch die man aus der Wohnung **ins Freie** kommt – hier auf eine **Terrasse**.

Woran erkenne ich sie?

Ein **Türbogen** an der Grenze zwischen Grün (innen) und Hellgrün (draußen). Rund um die Tür sind oft nur dünne hellblaue Linien: Dort ist die Wand eine **Glasfront**.


Tür oder festes Glas?

Nur wo ein **Bogen** gezeichnet ist, geht etwas auf. Dünne Linien **ohne** Bogen sind festes Glas (oft mit „FIXTEIL“ beschriftet).


Worauf muss man achten?

Vor Terrassentüren steht oft das Wort **RIGOL** (Rinne gegen Regenwasser) oder **STUFE** (Höhenunterschied). Wie hoch eine Stufe ist, steht im Grundriss nicht.

Hier bist du im Grundriss:

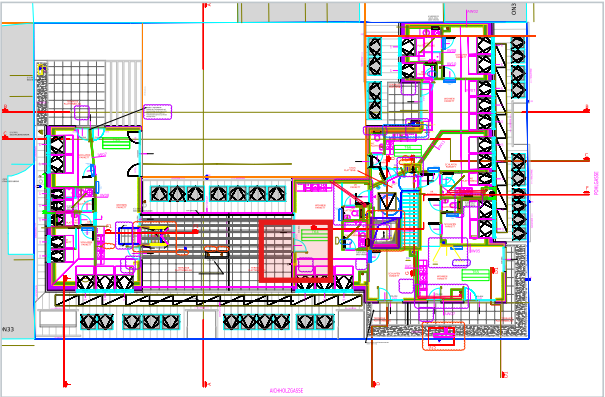

Glaslinien und Öffnungen an der Außenseite

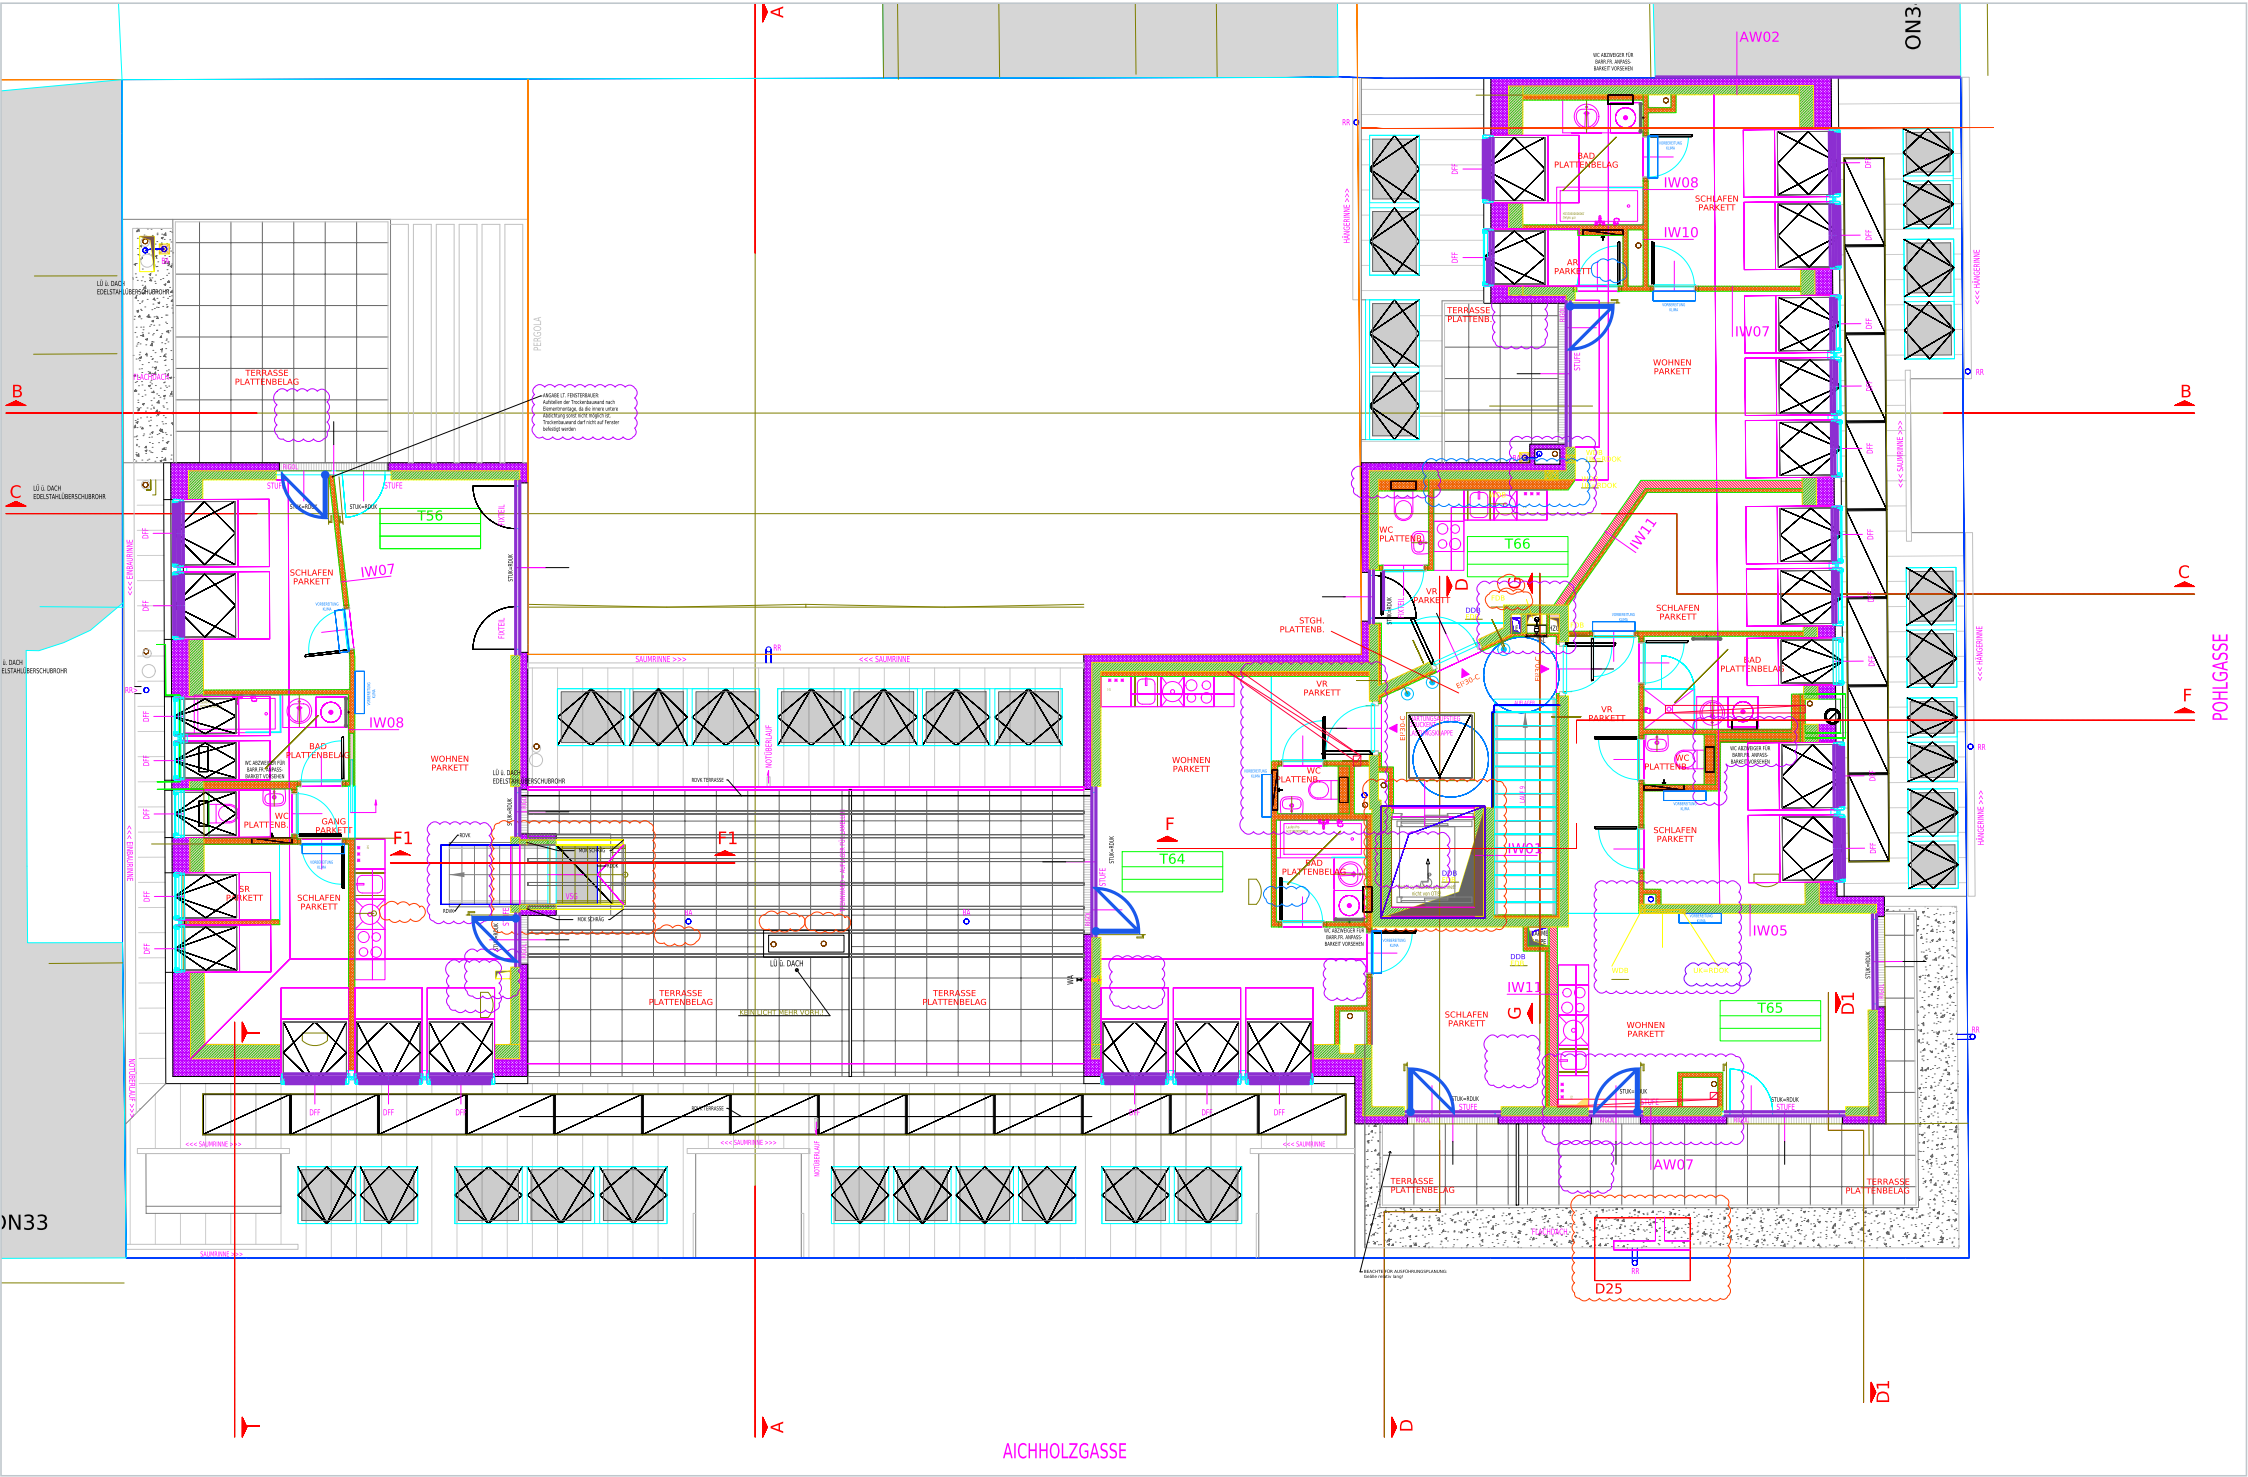

Was ist ein Fenster?

Eine Öffnung in der Außenwand, in der eine **Glasscheibe** in einem **Rahmen** sitzt. Licht kommt herein, **durchgehen kann man nicht**.

Wie sieht es im Grundriss aus?

Die dicke, gemusterte Wand hört auf. Stattdessen laufen **mehrere sehr dünne hellblaue Linien** parallel: außen und innen der Rahmen, in der Mitte das Glas.

Was zeigt diese Seite?

Violett: 235 hellblaue Originallinien, die direkt an der Außenseite der Innenräume liegen – das sind die Glasfronten und Fenster.

Gelb: die wenigen Stellen, an denen eine gemauerte Außenwand für ein Fenster unterbrochen ist.


Blau: Türen nach draußen.

Besonderheit Dachgeschoss

Hier gibt es kaum „Loch in der Mauer“-Fenster. Die Wohnungen öffnen sich mit großen **Glasfronten** zu den Terrassen. Dazu kommen **Dachflächenfenster (DFF)** in der Dachschräge – siehe Seite „Das Dach im Plan“.

Die violetten Linien wurden automatisch ausgewählt. Einzelne Linien können zu Rahmen oder Fensterbänken gehören statt zur Scheibe.

Innen grün, draußen hellgrün

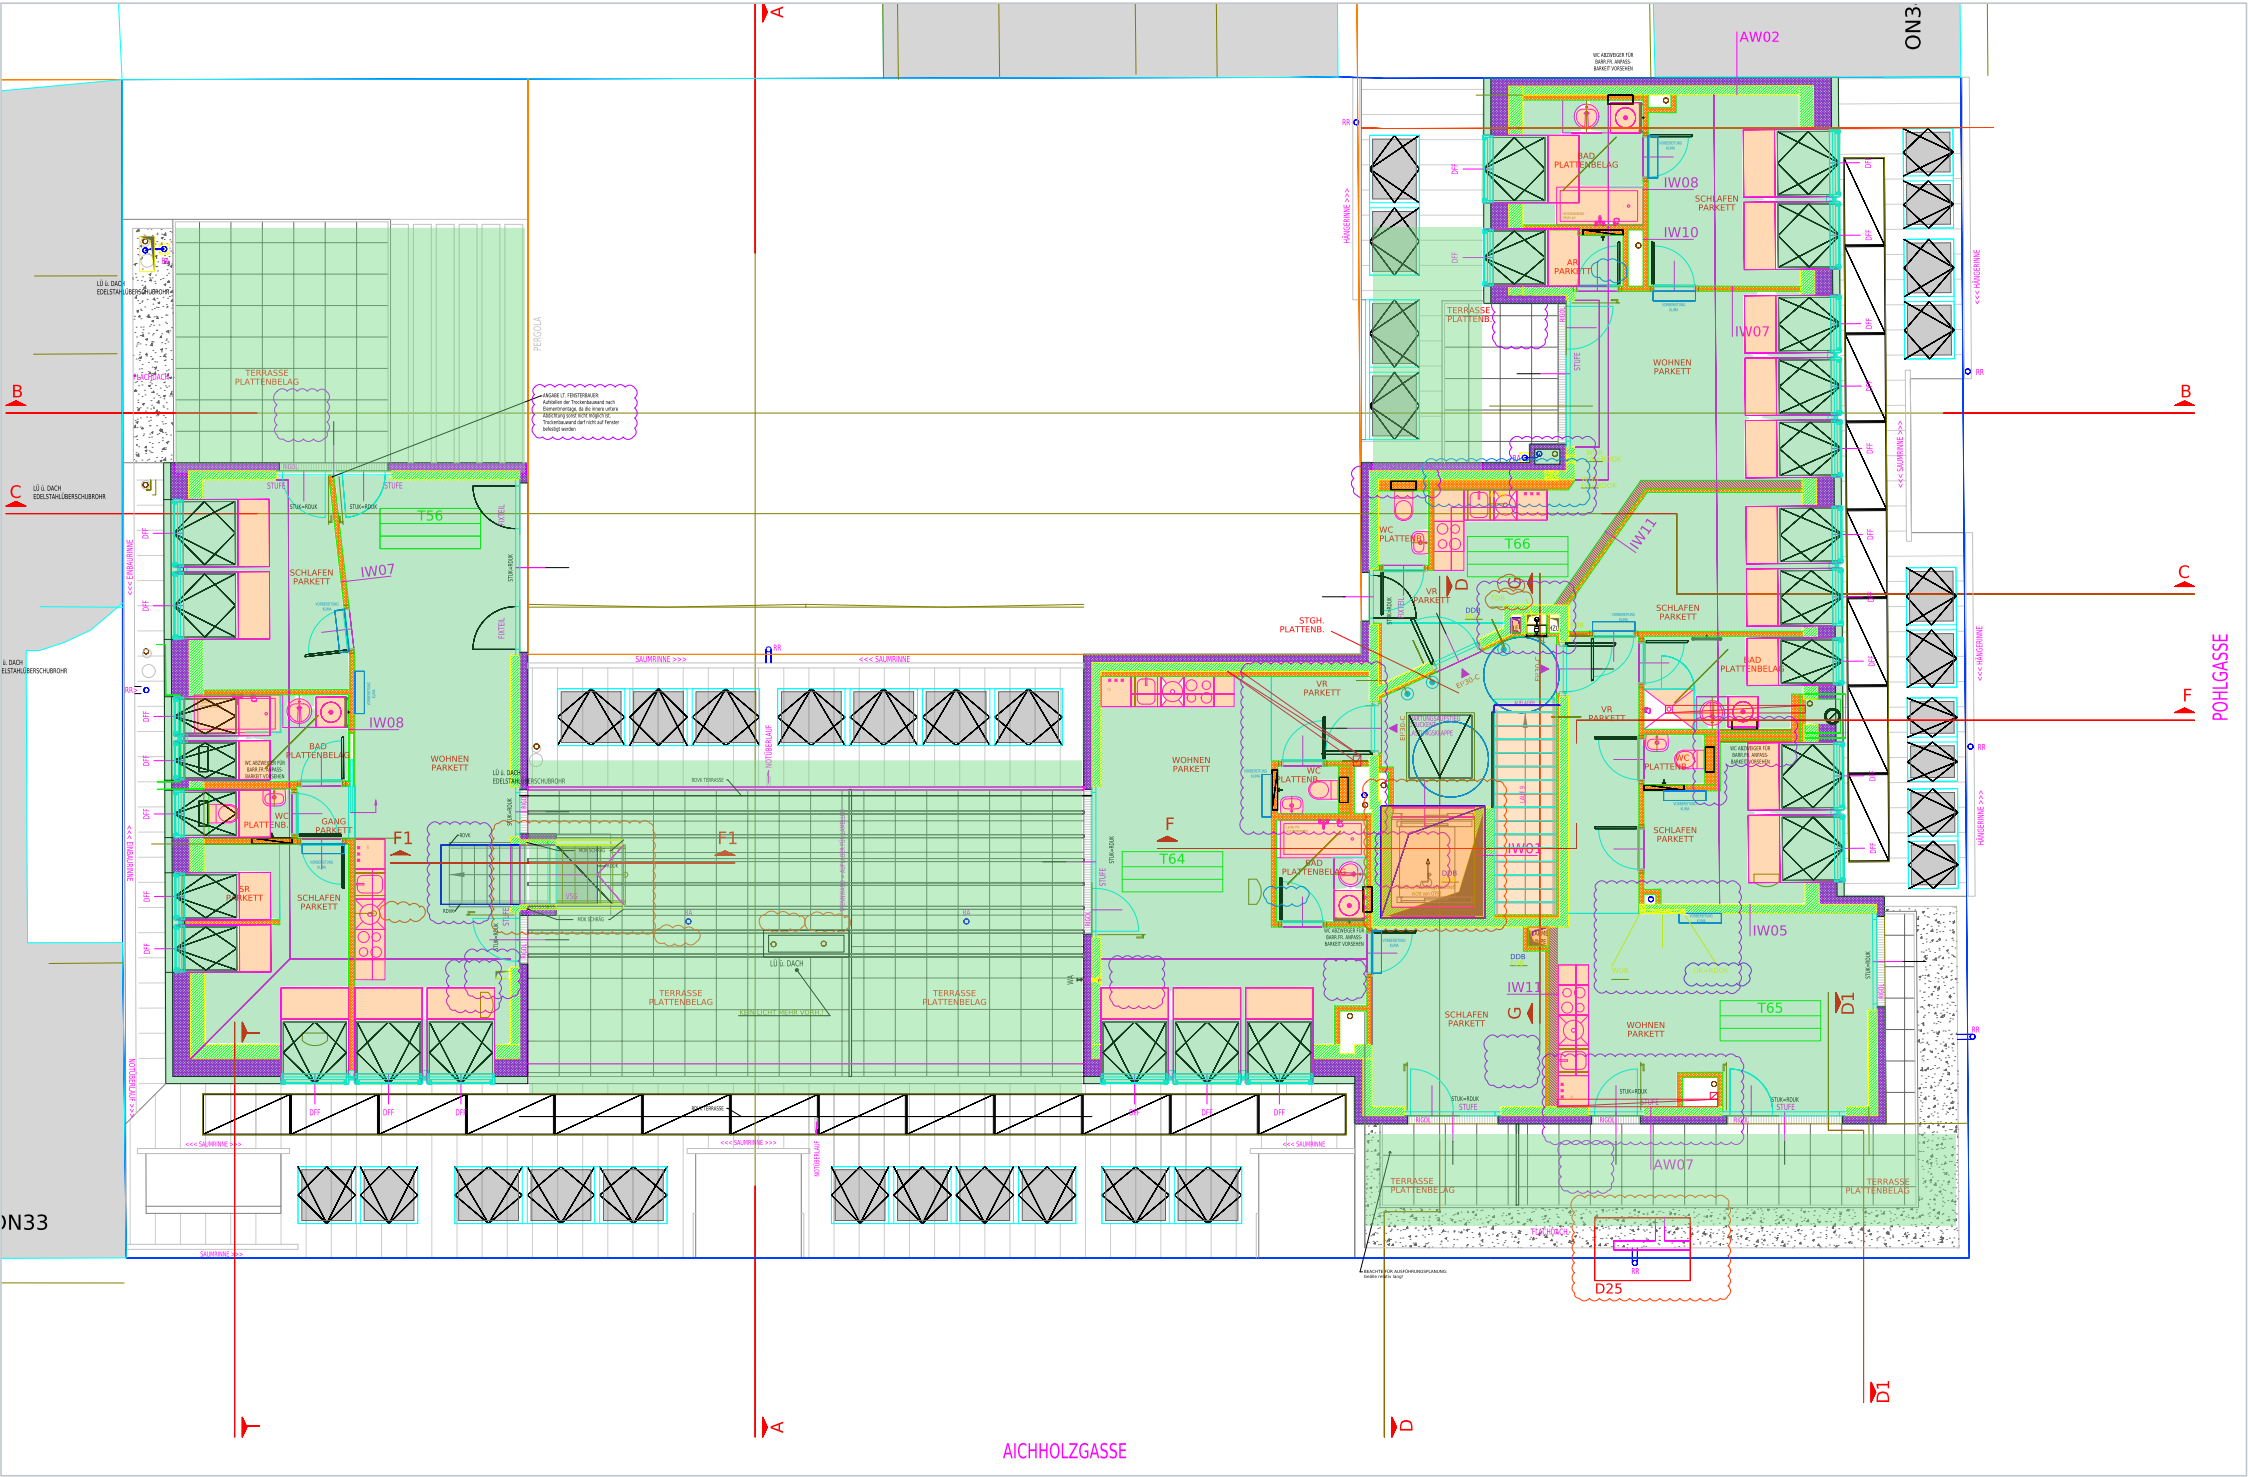

Die wichtigste Frage

Grün: Innenboden – hier kann ich gehen, mit Dach über mir.
Hellgrün: Terrassen und Balkone – hier kann ich im **Freien** gehen.

Was ist NICHT grün?

Wände (weiß ausgespart), **Einbauten** (orange: Küche, WC, Waschbecken, Kästen), **Aufzug und Schächte** (kräftig orange: kein Boden), die **Treppe** (blass orange), und das **Dach** (weiß: Flachdach, Rinnen, Dachschrägen von außen).

Innen und draußen verbinden


Zwischen Grün und Hellgrün liegt immer eine **Glasfront mit Tür**. Nur durch die Tür kommt man hinaus.

Terrassen im Dachgeschoss

Die hellgrüne Fläche ist in diesem Geschoss sehr groß. Dort, wo das Stockwerk darunter breiter ist, liegt oben die Terrasse – auf der Decke des unteren Geschosses.

Terrassen wurden aus ihrer Beschriftung und ihren Rändern angenähert. Grün sagt nichts über Barrierefreiheit oder Fluchtwege.

Die Terrasse: begehbar, aber draußen

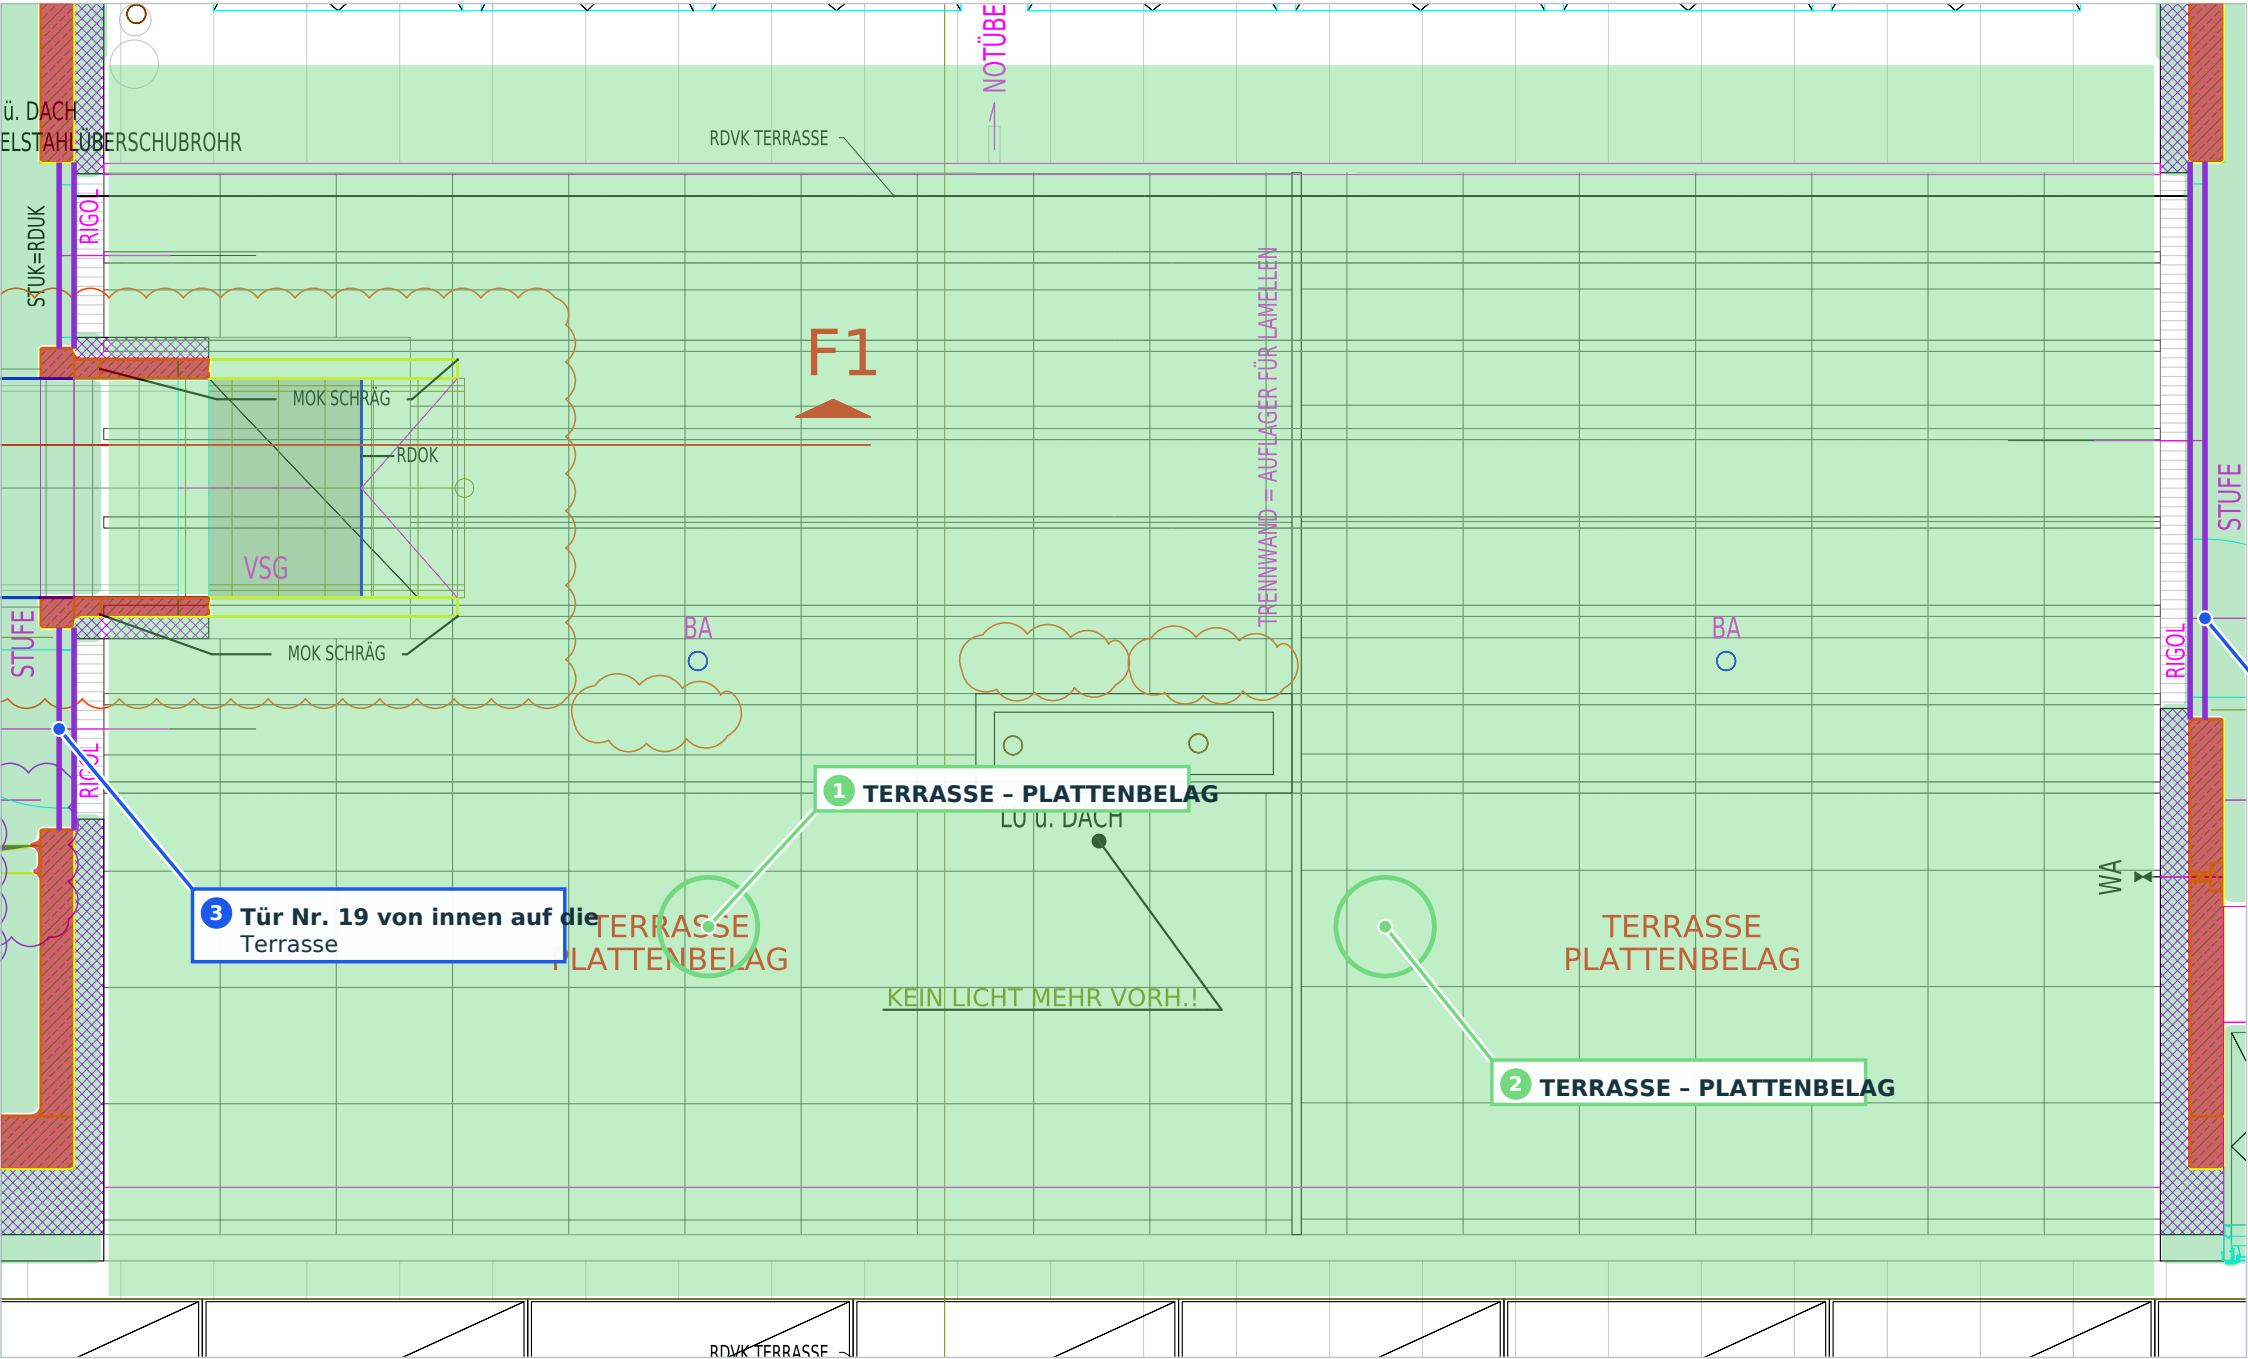

Was ist eine Terrasse?

Eine ebene Fläche **im Freien**, mit Platten belegt, auf der man stehen, sitzen und gehen kann. Im Dachgeschoss liegt sie **auf dem Dach des Stockwerks darunter**.

Woran erkenne ich sie im Plan?


- Die Beschriftung **TERRASSE PLATTENBELAG** (oder BALKON PLATTENBELAG).
- Oft ein **Gitter aus dünnen Linien** – das sind die Fugen zwischen den Platten, keine Wände.
- Sie liegt **außerhalb** der roten Wände und der Glasfronten.
- Man erreicht sie nur durch eine **Tür** aus einer Wohnung.

Wie unterscheide ich Terrasse und Dach?


Terrasse: Plattenbelag, Beschriftung TERRASSE, Tür dorthin.
Dach: Texte wie FLACHDACH, SAUMRINNE, DFF, Kies-Punkte – und **keine Tür** führt hin.

Wo genau die Terrasse endet (Geländer, Brüstung, Kante), ist im Grundriss nicht immer eindeutig. Hellgrün ist hier eine Annäherung.

Hier bist du im Grundriss:

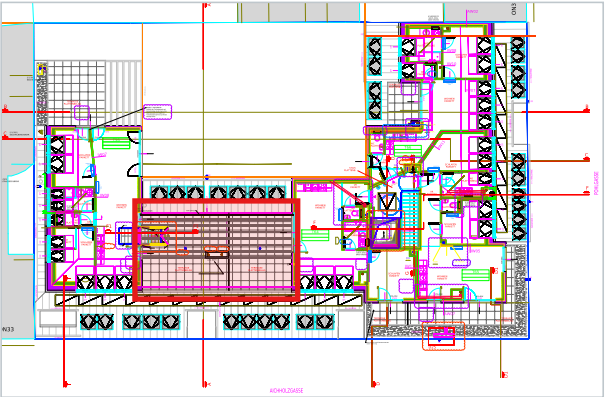

Dachschräge, Dachfenster, Rinnen: was im Dachgeschoss dazukommt

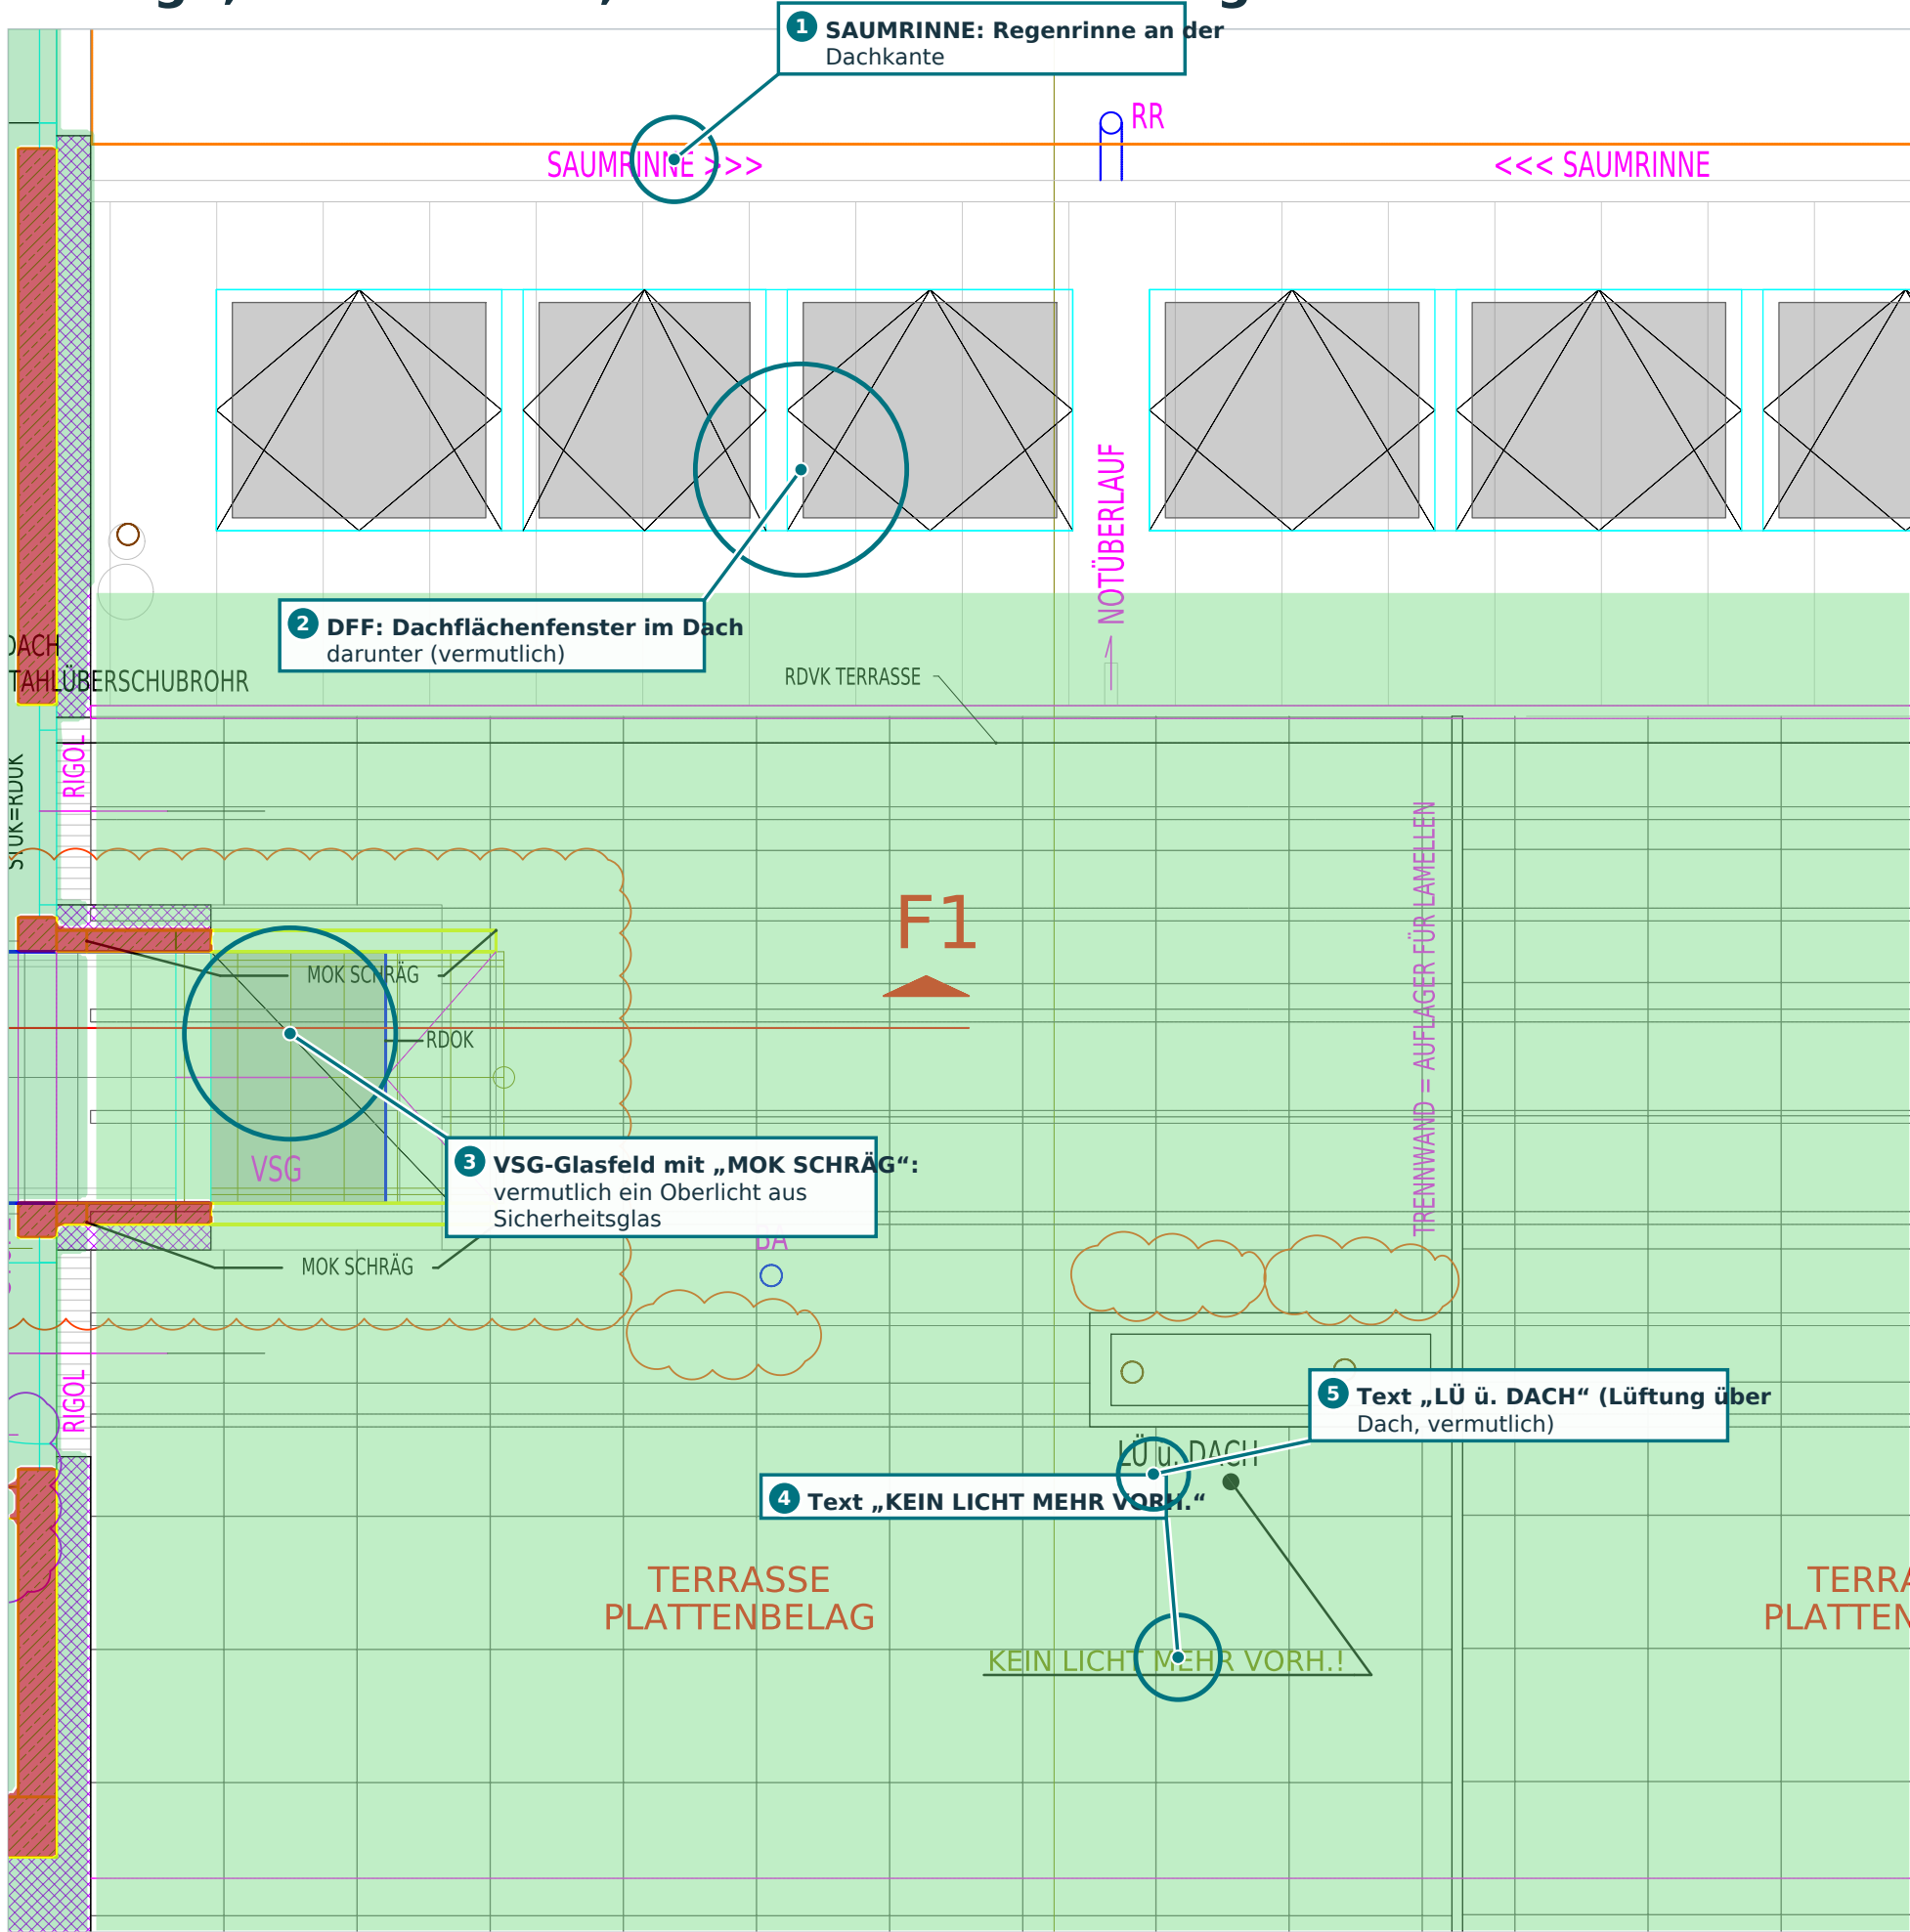

Warum sind hier so viele neue Zeichen?

Ein Dachgeschoss liegt im **Dach**. Darum zeigt der Plan zusätzlich Teile des Daches, die in den Stockwerken darunter nicht vorkommen.

Die wichtigsten Dach-Wörter

DFF – Dachflächenfenster: ein Fenster, das schräg in der Dachfläche liegt. Man kann nicht hindurchgehen.

SAUMRINNE / HÄNGERINNE – Regenrinnen an der Dachkante. Die Pfeile >>> zeigen die Richtung, in die das Wasser fließt.


FLACHDACH – ein flacher Dachteil. Er ist kein Wohnraum und keine Terrasse.

Dachschräge – ein Bereich, in dem die Decke schief ist. Im Plan oft als gemustertes Band mit Fenstern am Rand eines Raums. Der Boden darunter gehört zum Raum, aber man kann dort nicht überall aufrecht stehen.

NOTÜBERLAUF – eine Öffnung, durch die Regenwasser abfließt, wenn die normale Entwässerung verstopft ist.

Wie hoch der Raum unter der Dachschräge ist, zeigt der Grundriss nicht. Die Deutung einzelner Zeichen ist bei fehlender Legende als „vermutlich“ markiert.

Hier bist du im Grundriss:

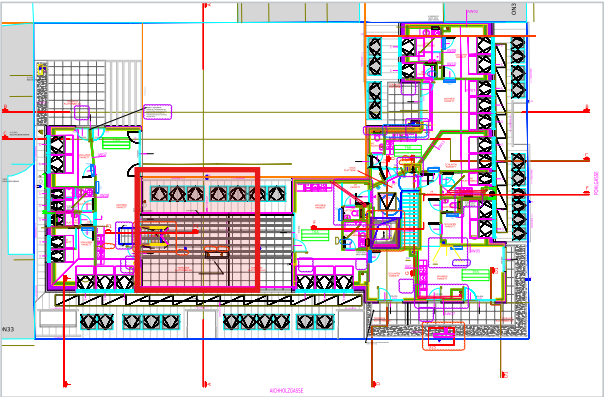

1. Starte im **Stiegenhaus** (orange, in der Mitte).
2. Geh auf dem grünen Boden zu einer **Wohnungseingangstür**.
3. Durch den **Vorraum** in die Zimmer.
4. Such eine **blaue Tür** an der Grenze zu Hellgrün – dahinter ist die **Terrasse**.

Rot trennt. **Blau** verbindet. **Grün** trägt dich drinnen, **Hellgrün** draußen. **Violett** lässt Licht durch. **Orange** steht im Weg. **Weiß** ist oft Dach.





1 – Start im gemeinsamen Bereich vor der Wohnung.

2 – Die **Eingangstür** in der dicken Wand.

3 – Der Vorraum.


4-5 – Weiter auf Grün durch die Wohnung, um orange Einbauten herum.

6 – Die Tür nach draußen (blauer Bogen in der Glasfront).

7 – Du stehst auf der **Terrasse**. Weiter geht es nicht: zurück nur durch dieselbe Tür.

Die Linie zeigt die Reihenfolge, nicht den exakten Gehweg.
Lernbeispiel, kein geprüfter Flucht- oder Rettungsweg.

Räume erkennen: die Wohnung T64

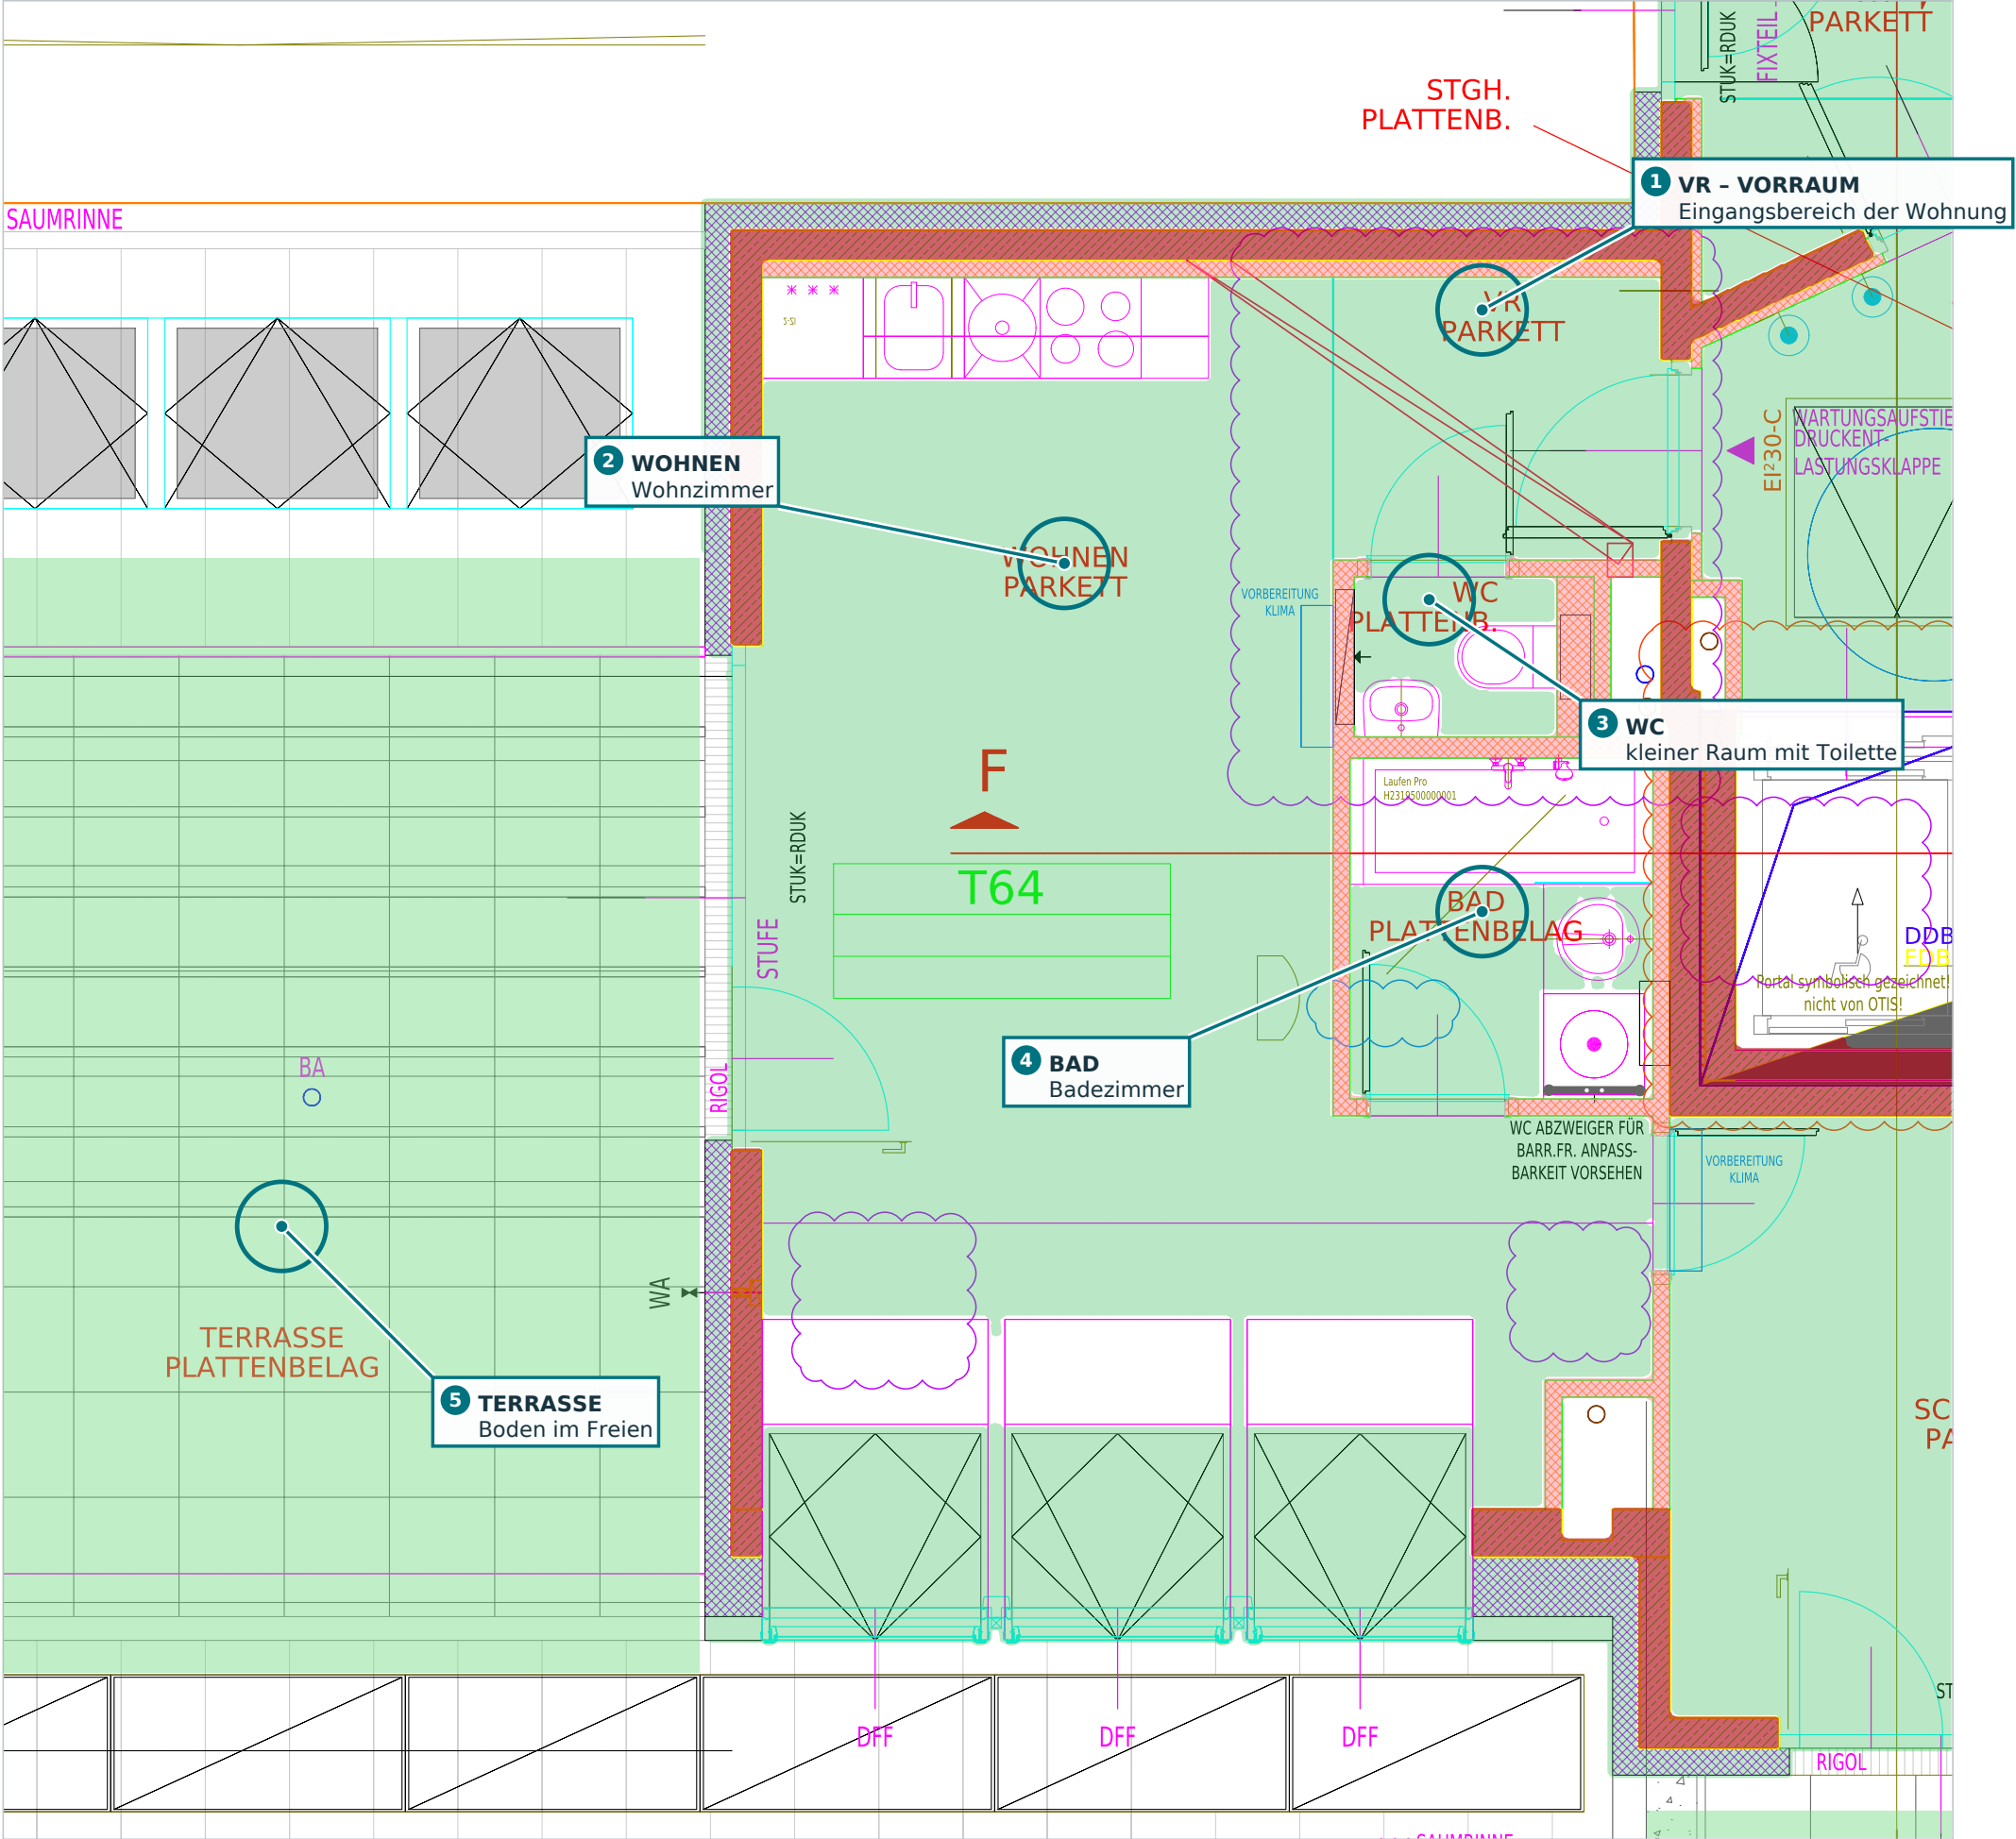


Was ist ein Raum?
Ein Stück Boden, rundherum von **Wänden oder Glas** umschlossen. Hinein kommt man durch **Türen**.

Woher weiß ich, wie ein Raum heißt?
Am **Raumstempel** in roter Schrift: oben der Name, darunter der Bodenbelag. **PARKETT** = Holzboden, **PLATTENBELAG** = Fliesen oder Platten.


Wichtige Raumnamen
VR Vorraum · **WC** Toilette · **BAD** Badezimmer · **AR** Abstellraum · **SR** vermutlich Schrankraum · **WOHNEN** Wohnzimmer (oft mit Küche) · **SCHLAFEN** Schlafzimmer · **GANG** Flur.

Im Dachgeschoss beachten
Ein Raum kann an einer Seite unter der **Dachschräge** liegen. Der Boden gehört trotzdem zum Raum – nur die Decke ist dort niedriger.

Die Raumnamen stammen aus den Raumstempeln. Flächen in m² stehen in diesem Plan nicht.

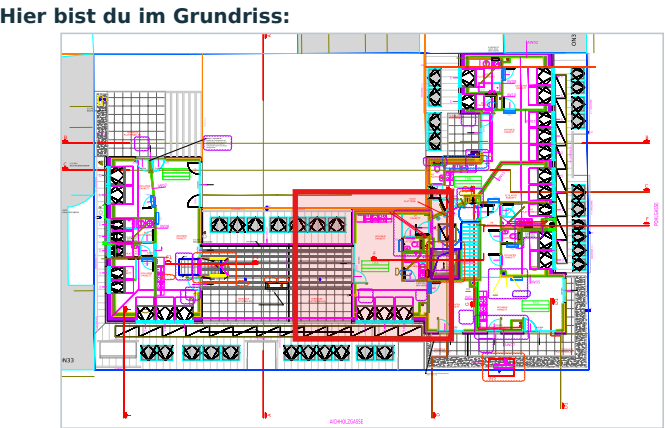

Was dünn gezeichnet ist, steht am Boden: Einbauten in T64

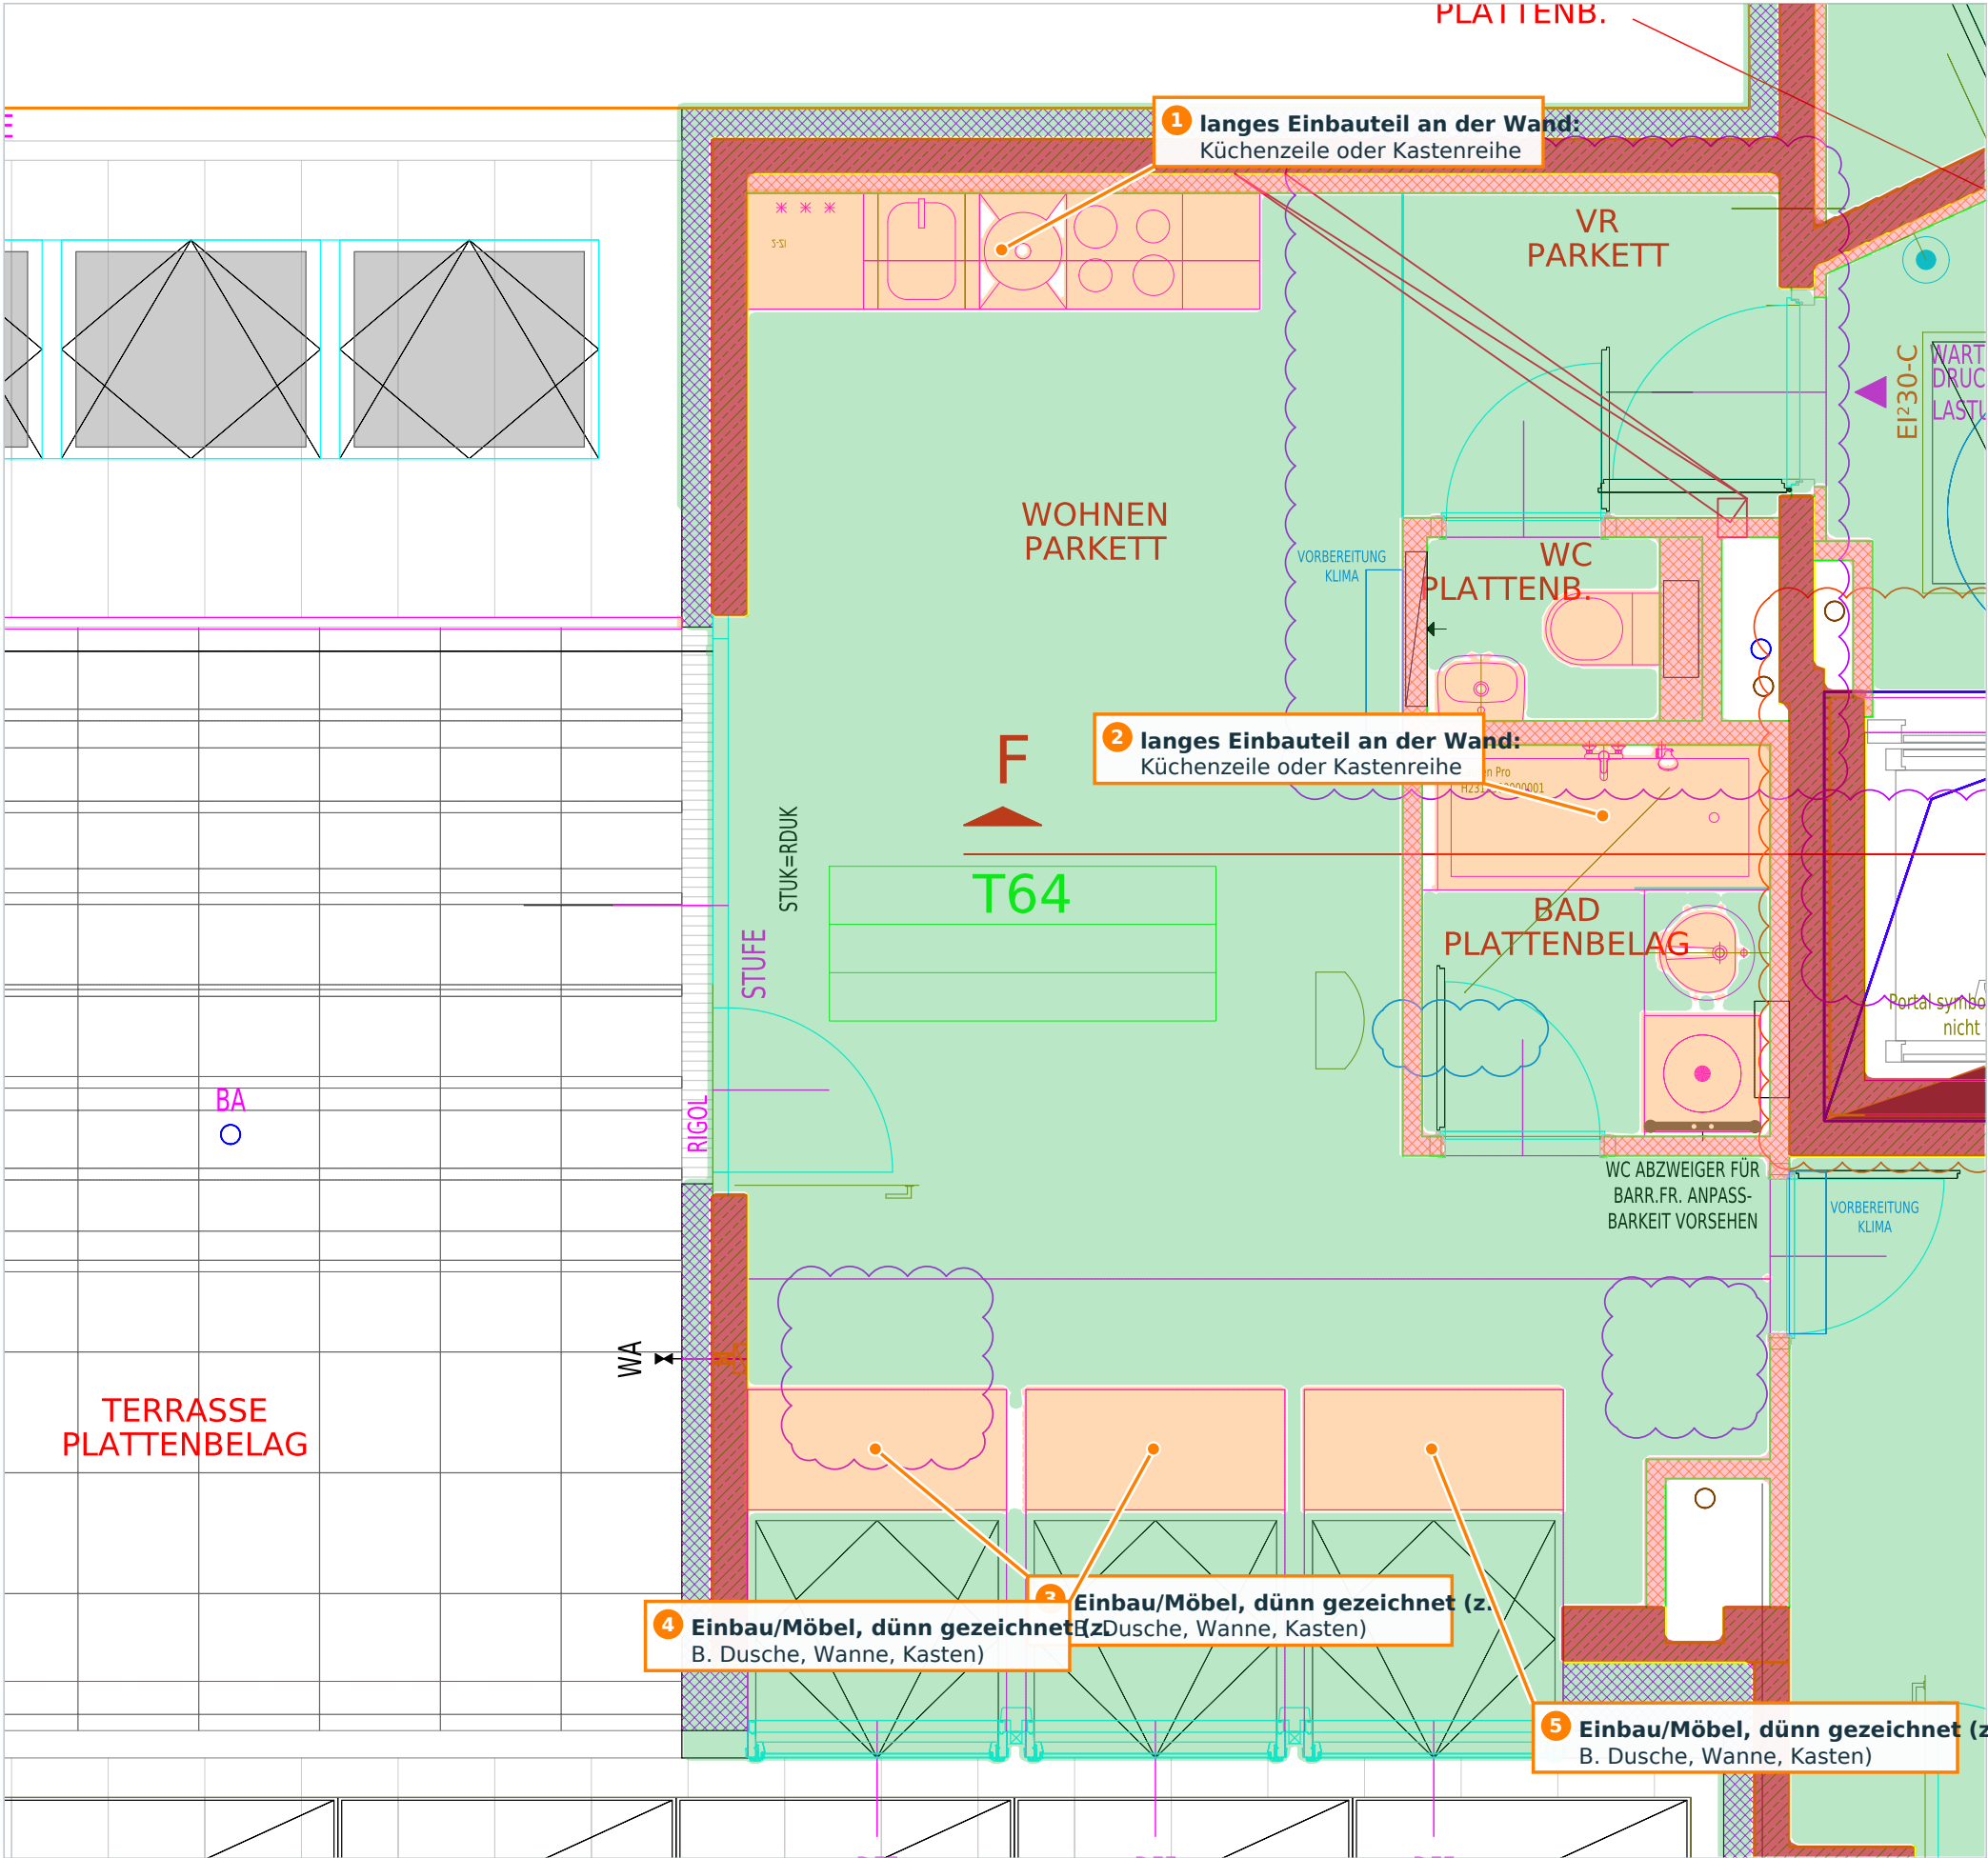

Was sind Einbauten?

Dinge, die fest im Raum stehen: WC, Waschbecken, Dusche, Wanne, Küchenzeile, eingebaute Kästen. Sie sind **keine Wände**, stehen aber im Weg.

Wie sehen sie im Plan aus?

Mit **dünnen magenta Linien**, weil sie unterhalb der Schnitthöhe stehen – man sieht sie „von oben drauf“.


- **Oval** im abgerundeten Rechteck = WC.
- **Kreis im Rechteck** = Waschbecken.
- **Rechteck mit vier Kreisen** = Herd.
- **Rechteck mit Kreuz (X)** = Kasten / Schrank.
- **Langer schmaler Streifen** an der Wand = Küchenzeile oder Kastenreihe.

Was bedeutet das für das Gehen?


Orange = hier steht etwas. Man geht **davor** auf dem grünen Boden. Einbauten teilen einen Raum aber nicht in zwei Räume.

Die Beschriftung der Nummern wurde nach Form und Größe gewählt. Bei kleinen Symbolen ist nicht jedes Teil sicher bestimmbar.

Hier bist du im Grundriss:

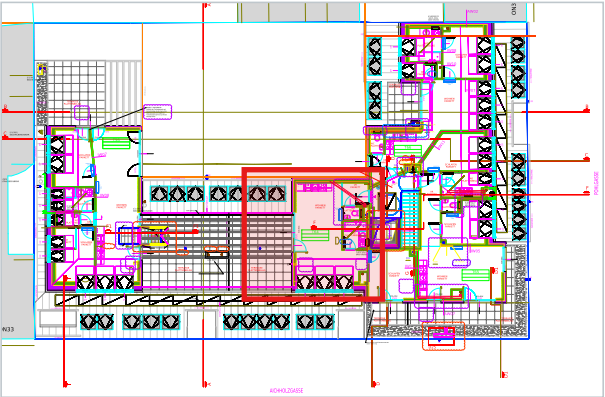

Der Kern des Hauses: Treppe, Aufzug und Schächte

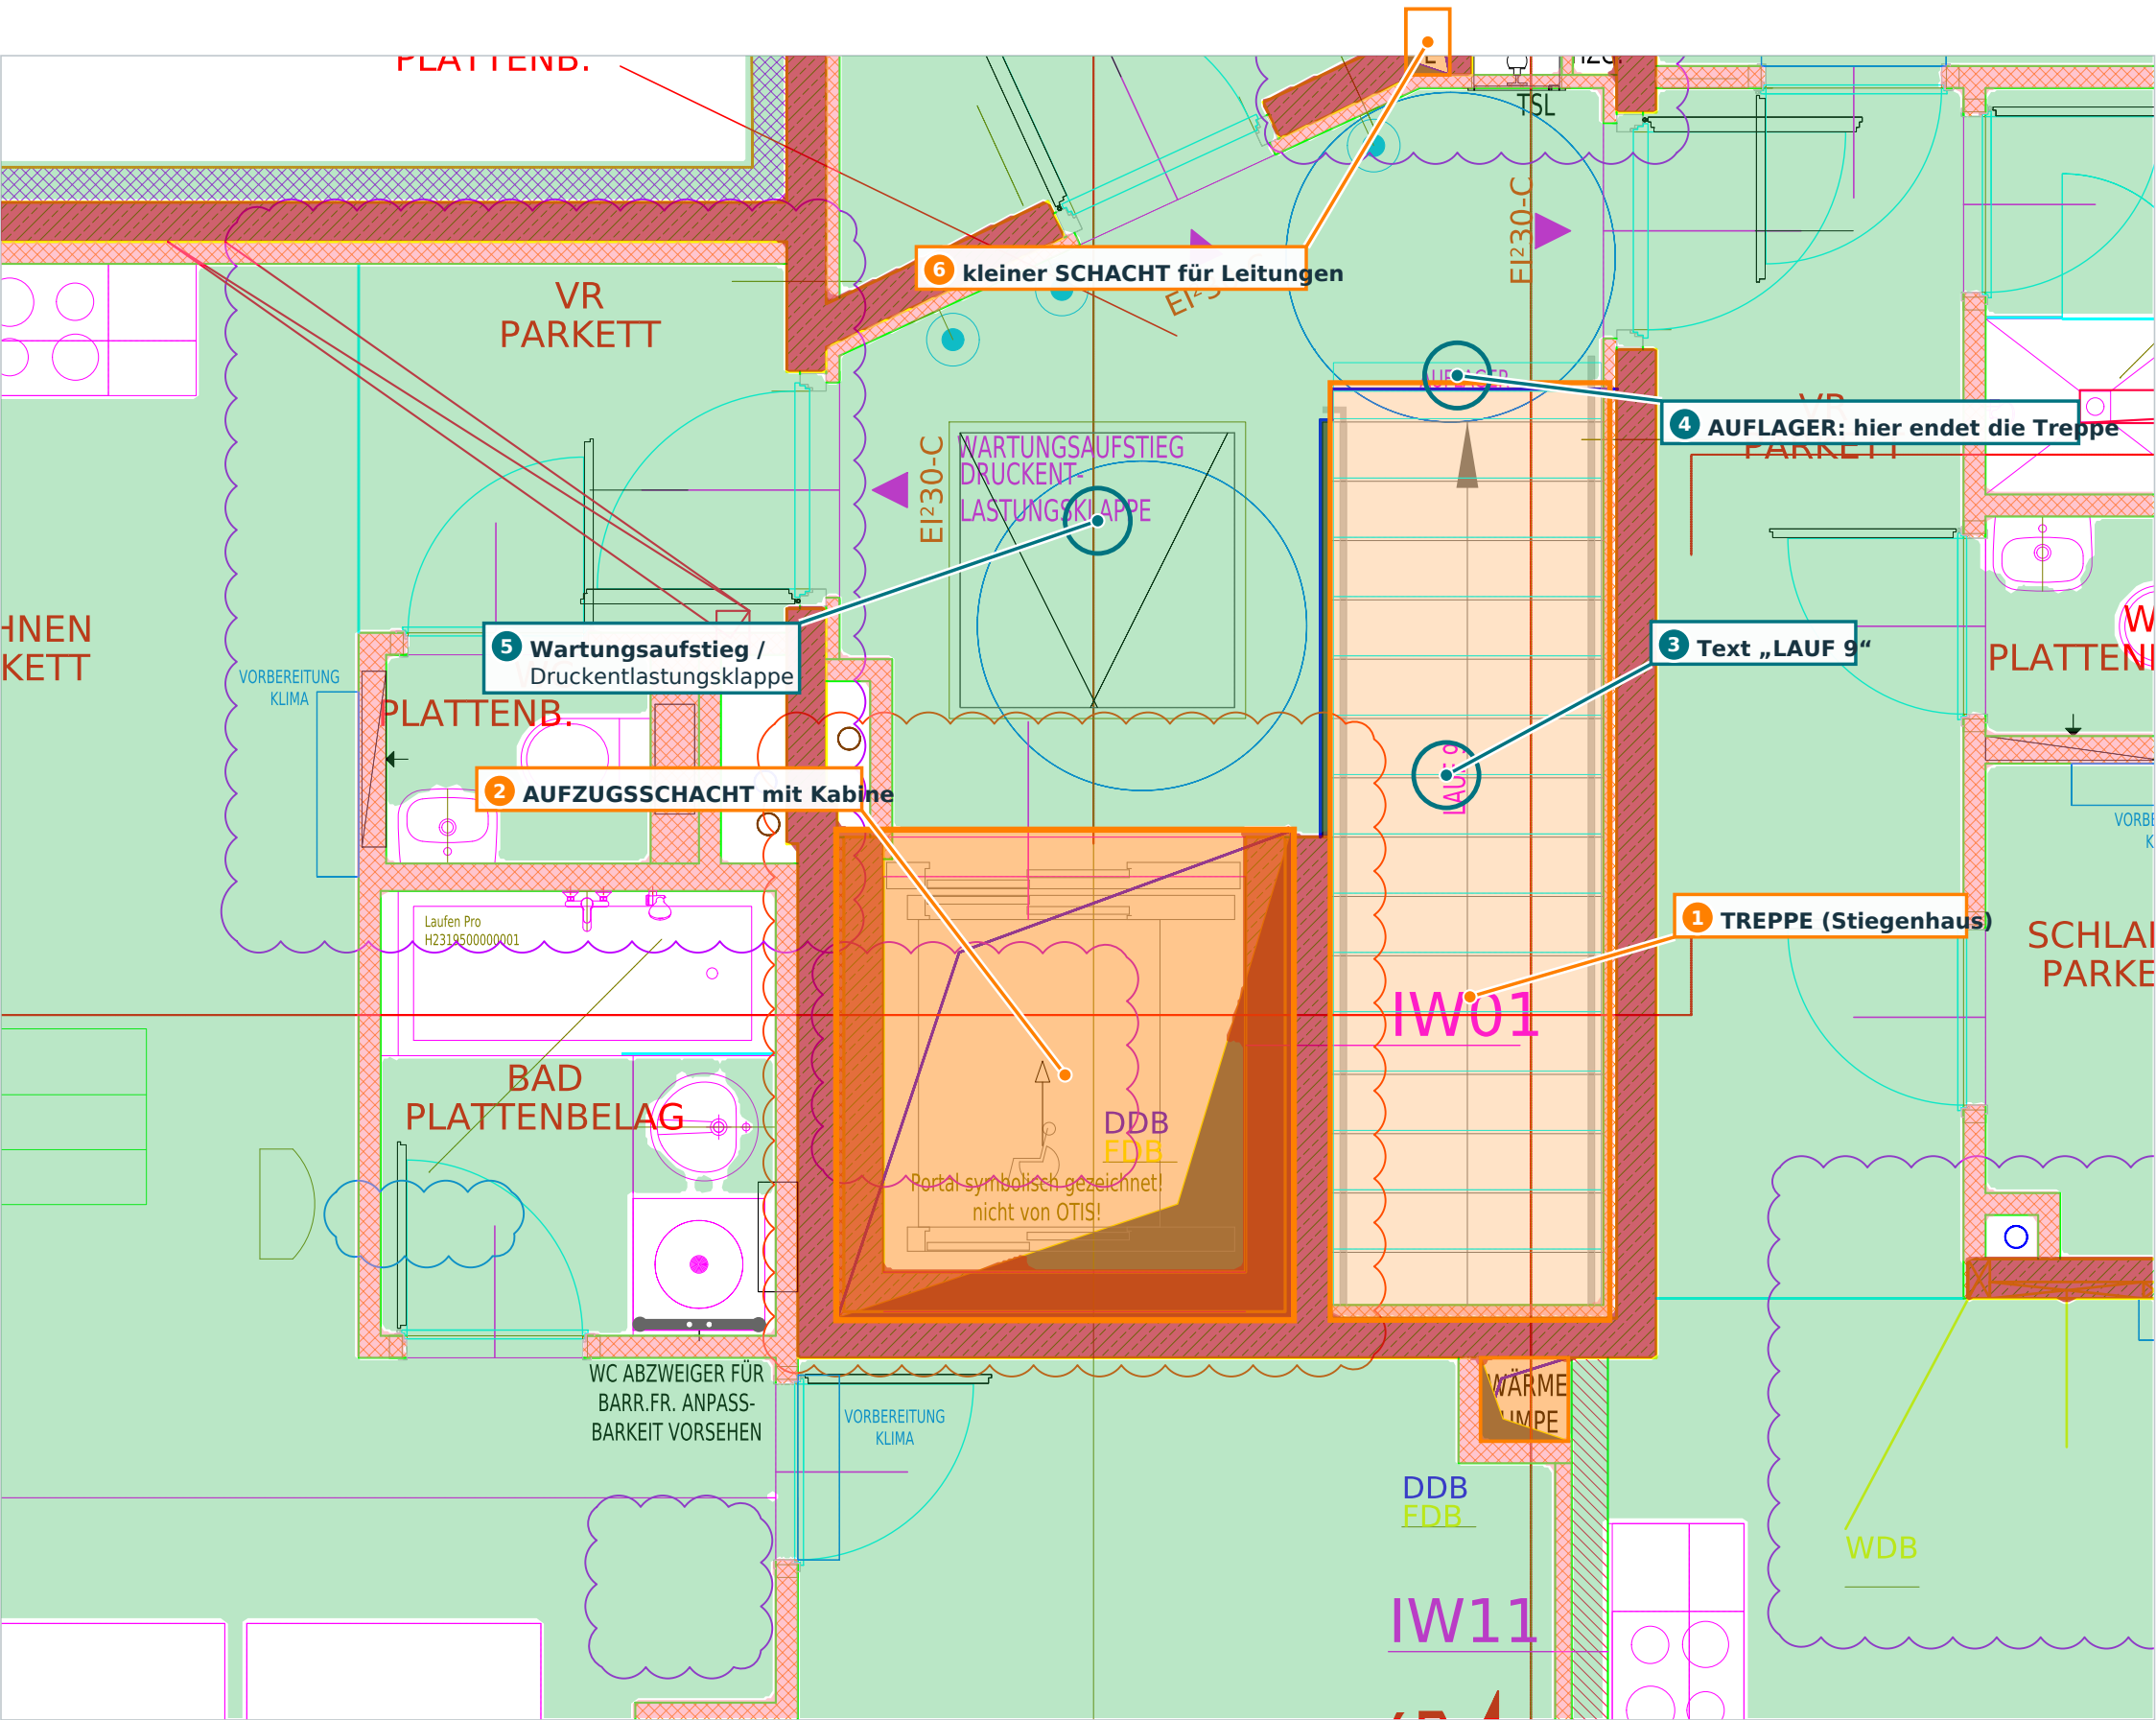

Treppe

Was: Stufen, über die man in ein anderes Stockwerk kommt. **Normalerweise** zeigt ein Grundriss viele parallele Querlinien – jede ist eine Stufenkante. **Besonderheit hier:** Im 2. DG sind die **Stufen wirklich gezeichnet!** Du siehst viele parallele Querlinien (jede eine Stufenkante), einen **Pfeil** in Laufrichtung und oben das Wort **AUFLAGER:** Dort liegt der Lauf auf der Decke auf – das 2. DG ist das oberste Geschoss, die Treppe endet hier.

Daneben steht „**Wartungsaufstieg / Druckentlastungsklappe**“: ein Zugang für Wartungsarbeiten und eine Klappe, die sich bei Rauch oder Überdruck öffnen kann. Das ist kein Weg für Bewohner.


Aufzug

Ein fast quadratischer Schacht mit dicken Wänden, darin ein Rechteck (Kabine), eine dunkle Fläche und ein Rollstuhlsymbol. Eine Notiz sagt, dass das Tor nur symbolisch gezeichnet ist.

Schächte

Kleine Kästchen mit Schräglinie, beschriftet mit DDB/FDB: Durchbrüche für Leitungen durch die Decken. **Kein Boden.** Welche Stockwerke die Treppe genau verbindet, bestätigt erst ein Schnitt.

Hier bist du im Grundriss:

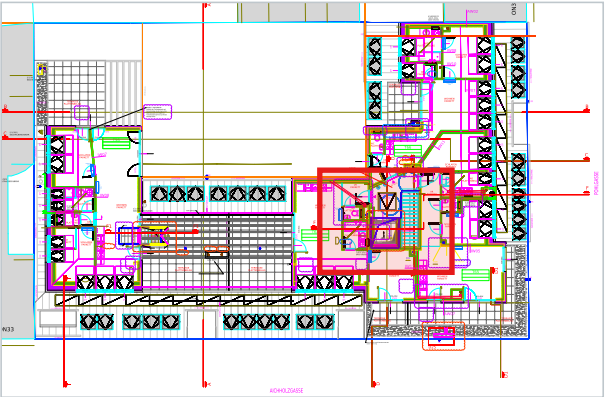


Typische Anfängerfehler: sieht aus wie Wand oder Raum - ist es aber nicht

1. Plattenfugen




Sieht aus wie: viele kleine Räume.
Ist: das Fugenbild des Terrassenbelags – eine Fläche.

2. Saumrinne

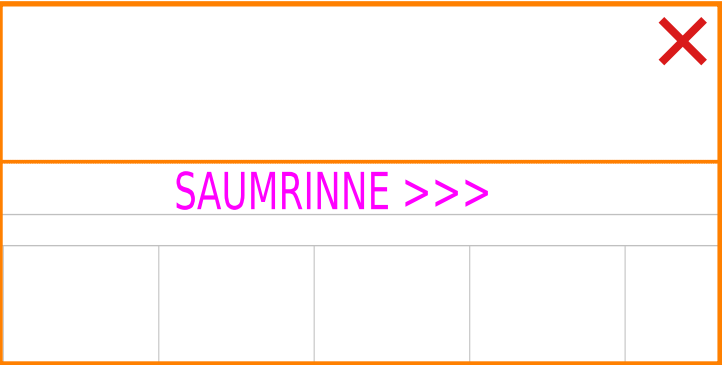


Sieht aus wie: eine lange Wandkante.
Ist: die Regenrinne am Dachrand, mit Fließpfeilen.

3. Türbogen

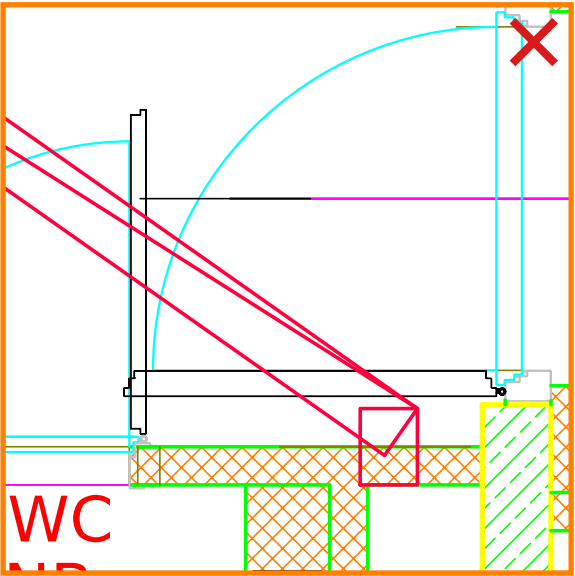


Sieht aus wie: eine gebogene Wand.
Ist: nur der Weg der Türkante – dort ist Platz.

4. Glasfeld (VSG)

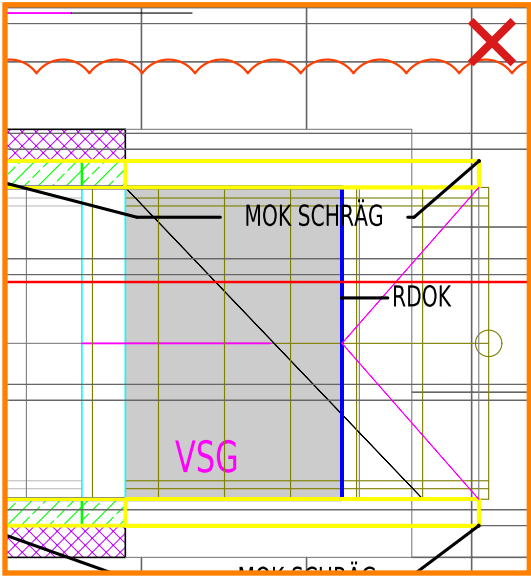


Sieht aus wie: ein kleiner Raum oder Schacht.
Ist: vermutlich ein Oberlicht aus Glas im Terrassenbereich – nicht begehbar.

5. Nummernkasten

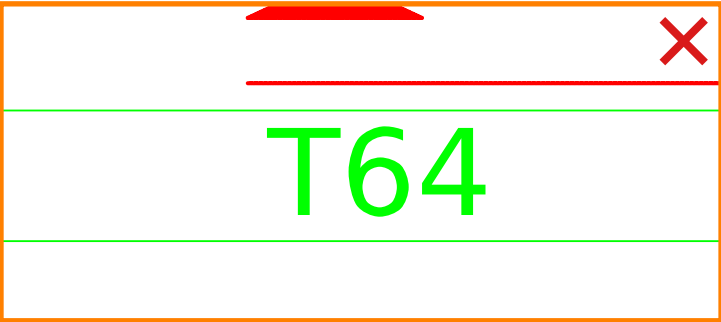


Sieht aus wie: ein kleines Zimmer.
Ist: der Kasten der Wohnungsnummer T64 – Schrift.

6. Treppenbereich

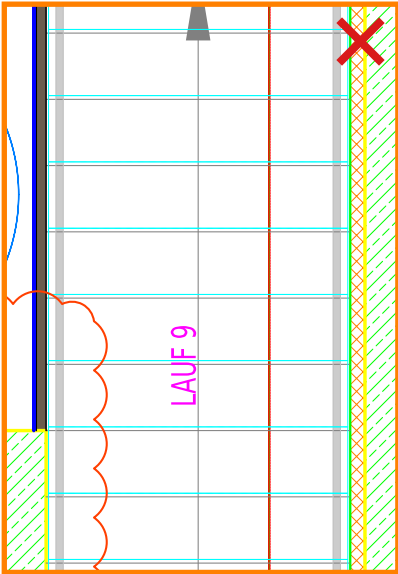


Sieht aus wie: ein schmaler Raum.
Ist: die Treppe bzw. die Deckenöffnung dafür – kein ebener Boden.

7. Aufzugsschacht

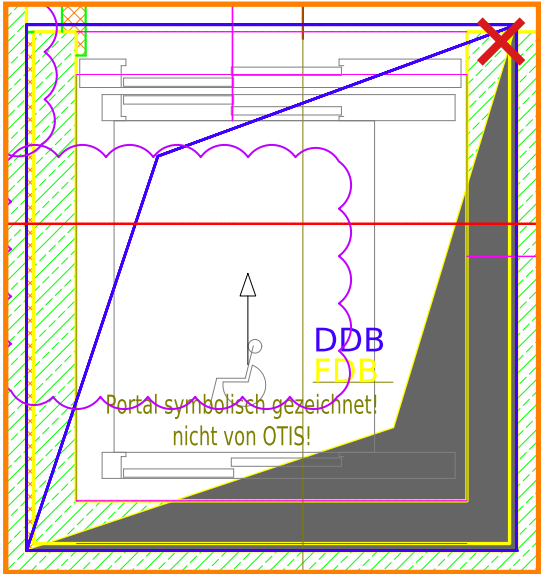

Sieht aus wie: ein kleiner Raum.
Ist: ein senkrechter Schacht mit Kabine – kein Zimmer.

8. So sieht die echte Wand aus

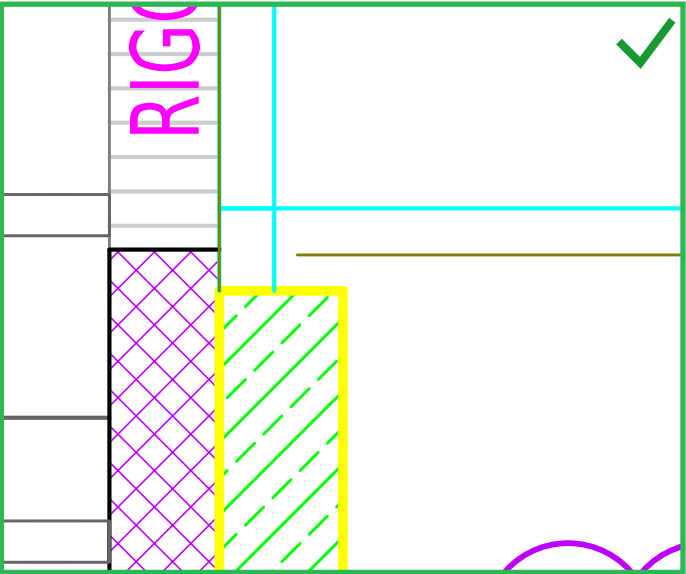

Zum Vergleich: zwei Kanten + Muster dazwischen + Anschluss an andere Wände.

Die goldene Regel: Eine Wand hat IMMER zwei parallele Kanten mit Muster dazwischen. Fehlt eines davon, ist es sehr wahrscheinlich keine Wand.


Alle wichtigen Abkürzungen und Wörter in diesem Plan

Im Plan steht	Bedeutung in einfachen Worten	Wie sicher?
VR, AR, SR	Vorraum, Abstellraum, Schrankraum (SR vermutlich)	sicher / vermutlich
WC, BAD, WOHNEN, SCHLAFEN, GANG	Toilette, Badezimmer, Wohnzimmer, Schlafzimmer, Flur	sicher
STGH.	Stiegenhaus	sicher
LAUF ...	Treppenlauf mit Nummer	sicher
AUFLAGER	Stelle, an der der Treppenlauf aufliegt	sicher
PARKETT / PLATTENBELAG	Holzboden / Fliesen oder Platten	sicher
TERRASSE, BALKON	begehbare Flächen im Freien	sicher
T...	Top = Wohnungsnummer	sicher
IW..., AW...	Innenwand- / Außenwand-Typ	sicher (Aufbau nicht im Plan)
EI³30, EI²30-C	Brandschutz 30 Min.; C = selbstschließend	sicher (Norm)
DFF	Dachflächenfenster	sehr wahrscheinlich
SAUMRINNE, HÄNGERINNE	Regenrinnen am Dachrand	sicher
FLACHDACH	flacher Dachteil, kein Raum	sicher
NOTÜBERLAUF	Notablauf für Regenwasser	sicher
STUFE	Höhenunterschied, meist an Terrassentüren	sicher
RIGOL	Rinne vor Türen nach draußen	sicher
FIXTEIL	festes Glas, geht nicht auf	sicher
STUK=RDUK	Sturzunterkante = Rohdeckenunterkante	sehr wahrscheinlich
RDOK, RDVK, RDUK	Rohdecken-Oberkante/-Vorderkante/-Unterkante	wahrscheinlich
MOK SCHRÄG	schräg verlaufende Oberkante (z. B. Mauer-/Aufkantung)	unsicher
VSG	Verbundsicherheitsglas	sicher (übliche Abkürzung)
LÜ ü. DACH	Lüftung über Dach	wahrscheinlich
DDB / FDB	Decken- / Fußbodendurchbruch für Leitungen	wahrscheinlich
RR	Regenrohr	wahrscheinlich
BA	nicht erklärt	unsicher
WA	nicht erklärt (evtl. Wasseranschluss)	unsicher
DETAIL A, D25, D1	Verweise auf Detailzeichnungen/-markierungen	sicher / unsicher
A, B, C, D, F, F1, G	Schnittlinien und Schnittmarken	sicher
ON33, ON34	Nachbargebäude/-grundstücke	wahrscheinlich
Wartungsaufstieg, Druckentlastungsklappe	Zugang für Wartung; Klappe, die bei Rauch/Überdruck öffnet	sicher (Wortlaut)


Nicht jedes Wort kommt in beiden Dachgeschossen vor.

Vergleich: 1. Dachgeschoss und 2. Dachgeschoss

1. Dachgeschoss (aus dem anderen Lernheft)

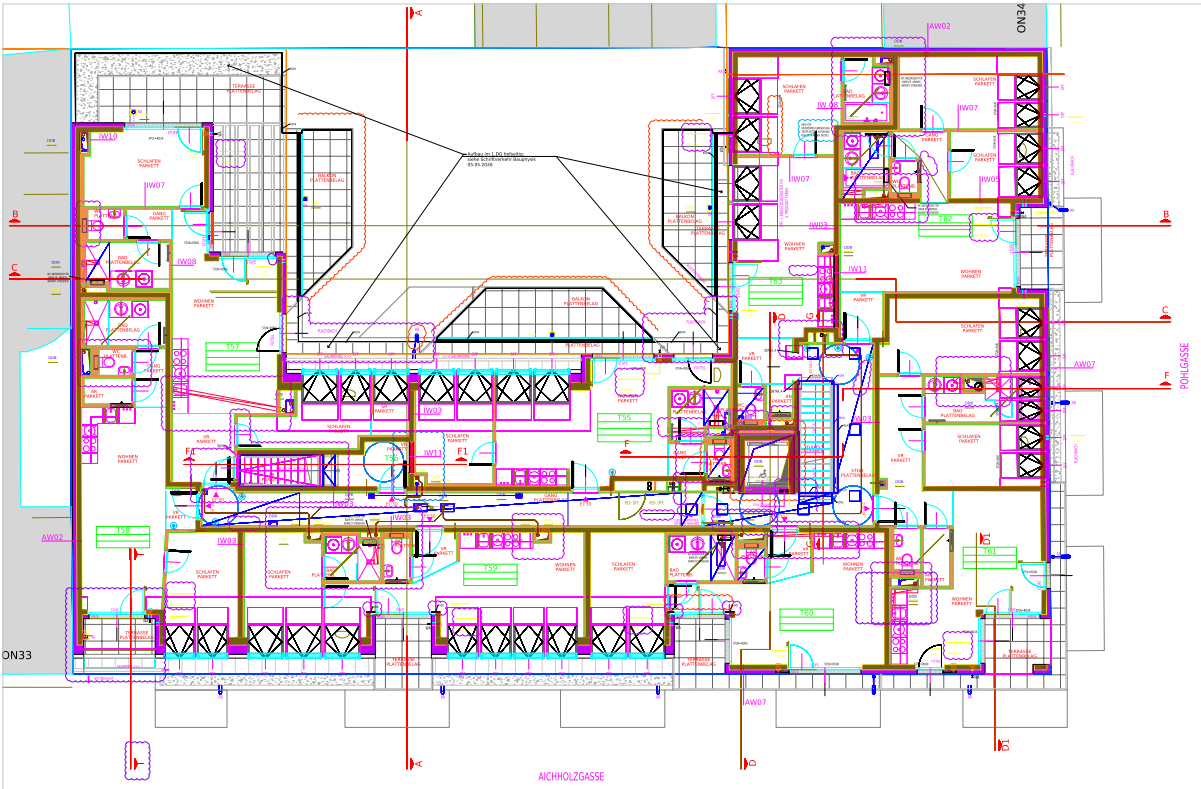

2. Dachgeschoss (Wände rot, Terrassen hellgrün)

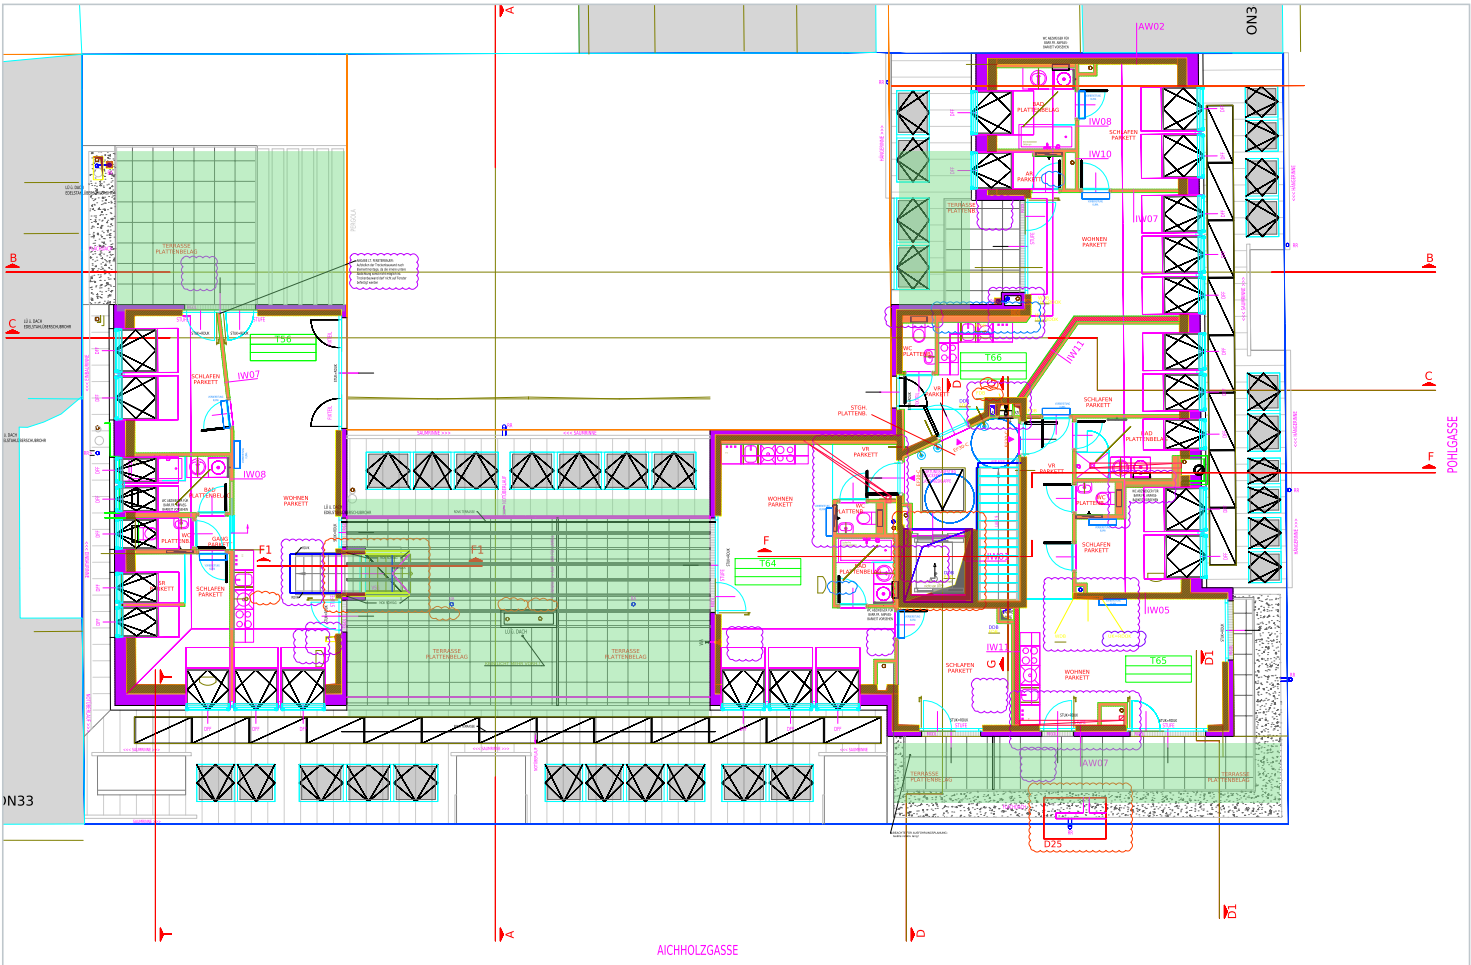

Warum vergleichen?

Stockwerke liegen übereinander. Stiegenhaus, Aufzug und Schächte müssen genau übereinander liegen. Wer zwei Geschosse vergleicht, versteht das Haus als Ganzes – und warum das Dachgeschoss Terrassen hat.

Gleich geblieben: Stiegenhaus und Aufzug liegen genau übereinander. Das Stiegenhaus endet hier: Die Treppe hat oben ein **AUFLAGER**, einen weiteren Lauf nach oben gibt es nicht.

Anders: Das 2. DG ist **viel kleiner**: nur noch 4 Wohnungsnummern (T56, T64, T65, T66). Der Rest ist Terrasse oder Dach des 1. DG – dort siehst du die **Dachflächenfenster** des Geschosses darunter von oben.

T56 steht in beiden Dachgeschossen – vermutlich eine Wohnung über zwei Ebenen (nicht sicher).

Die beiden Abbildungen sind einzeln eingepasst (unterschiedliche Blattgrößen) und nicht exakt deckungsgleich.

Fragen, die Anfänger im Dachgeschoss wirklich stellen

„Warum ist das Dachgeschoss kleiner als die anderen Stockwerke?“

Weil das Haus oben schmaler wird (Rücksprünge, Dachschrägen). So bekommt es mehr Licht und die Nachbarhäuser werden weniger verschattet. Die gewonnenen Flächen werden zu Terrassen.

„Darf ich auf das Flachdach gehen?“

Normalerweise nicht – es ist kein Aufenthaltsbereich. Nur die als TERRASSE beschriftete Fläche mit Tür dorthin ist zum Begehen gedacht.

„Was ist das Gitter auf der Terrasse?“

Die Fugen zwischen den Bodenplatten. Das Gitter zeigt den Belag, keine Wände.

„Wie hoch ist der Raum unter der Dachschräge?“

Das zeigt der Grundriss nicht. Dafür braucht man einen Schnitt.

„Kann ich durch ein Dachflächenfenster hinaus?“

Nein. Ein Dachflächenfenster lässt Licht und Luft herein – es ist kein Ausgang.

„Wo läuft das Regenwasser hin?“

In die Rinnen (SAUMRINNE, HÄNGERINNE) und über Regenrohre (RR) hinunter. Die Pfeile an den Rinnen zeigen die Fließrichtung.

„Warum ist Weiß hier so häufig?“

Weil um die Wohnungen herum Dach ist. Weiß heißt: nicht eingefärbt – hier kein Raum und keine Terrasse.

„Welche Wand darf man herausreißen?“

Das sagt kein Grundriss. Ob eine Wand trägt, steht im Tragwerksplan.

„Was ist eine Maisonette?“

Eine Wohnung über zwei Stockwerke, verbunden mit einer eigenen Treppe. Die gleiche Wohnungsnummer in zwei Geschossen ist ein Hinweis darauf.

Was dieser Plan NICHT verrät

Ein guter Planleser weiß auch, **was fehlt**:

1. Maße

„ohne Masse“: keine Maßketten, keine Flächen.

2. Eine Legende

Farben, Muster und manche Kürzel sind nicht erklärt. Die Deutungen im Heft sind nach Sicherheit gekennzeichnet.

3. Höhen und Dachform

Wie steil das Dach ist und wie hoch Räume unter der Schräge sind, zeigt nur ein Schnitt.

4. Tragende Wände und Material

Stehen im Tragwerksplan bzw. im Wandkatalog.

5. Terrassenränder

Wo genau Geländer und Brüstungen stehen, ist im Grundriss nicht immer eindeutig. Hellgrün ist eine Annäherung.

6. Verbindungen zwischen den Dachgeschossen

Ob T56 wirklich eine Maisonette mit eigener Treppe ist, lässt sich aus den Grundrissen allein nicht sicher sagen.

7. Einige Zeichen

„BA“, „WA“, „TSL“, „D1“, rote Schrägbalken und manche Linien sind ohne Legende nicht eindeutig. Sie sind markiert, aber nicht gedeutet.

8. Der wirkliche Zustand

Der Plan zeigt, wie gebaut werden **soll**.

9. Fluchtwege und Barrierefreiheit

Grün ist Boden – keine geprüfte Freigabe.


10. Wie die Farben entstanden sind

Wände, Türbögen und Innenböden wurden aus der Vektorgeometrie des Original-PDFs abgeleitet und mit dem Original verglichen.

Terrassen: von ihrer Beschriftung aus, teils als Rechteck angenähert. Glaslinien: hellblaue Linien direkt an der Außenseite der Innenräume. Kleine Abweichungen an Kanten sind möglich.

Merke: Was der Plan nicht eindeutig zeigt, heißt „steht nicht im Plan“ – nicht raten.

Tür · dicke Wand · dünne Wand · Tür nach draußen · Terrasse ·
Aufzug · Treppe · Raumstempel · Regenrinne · Dach-Zeichen

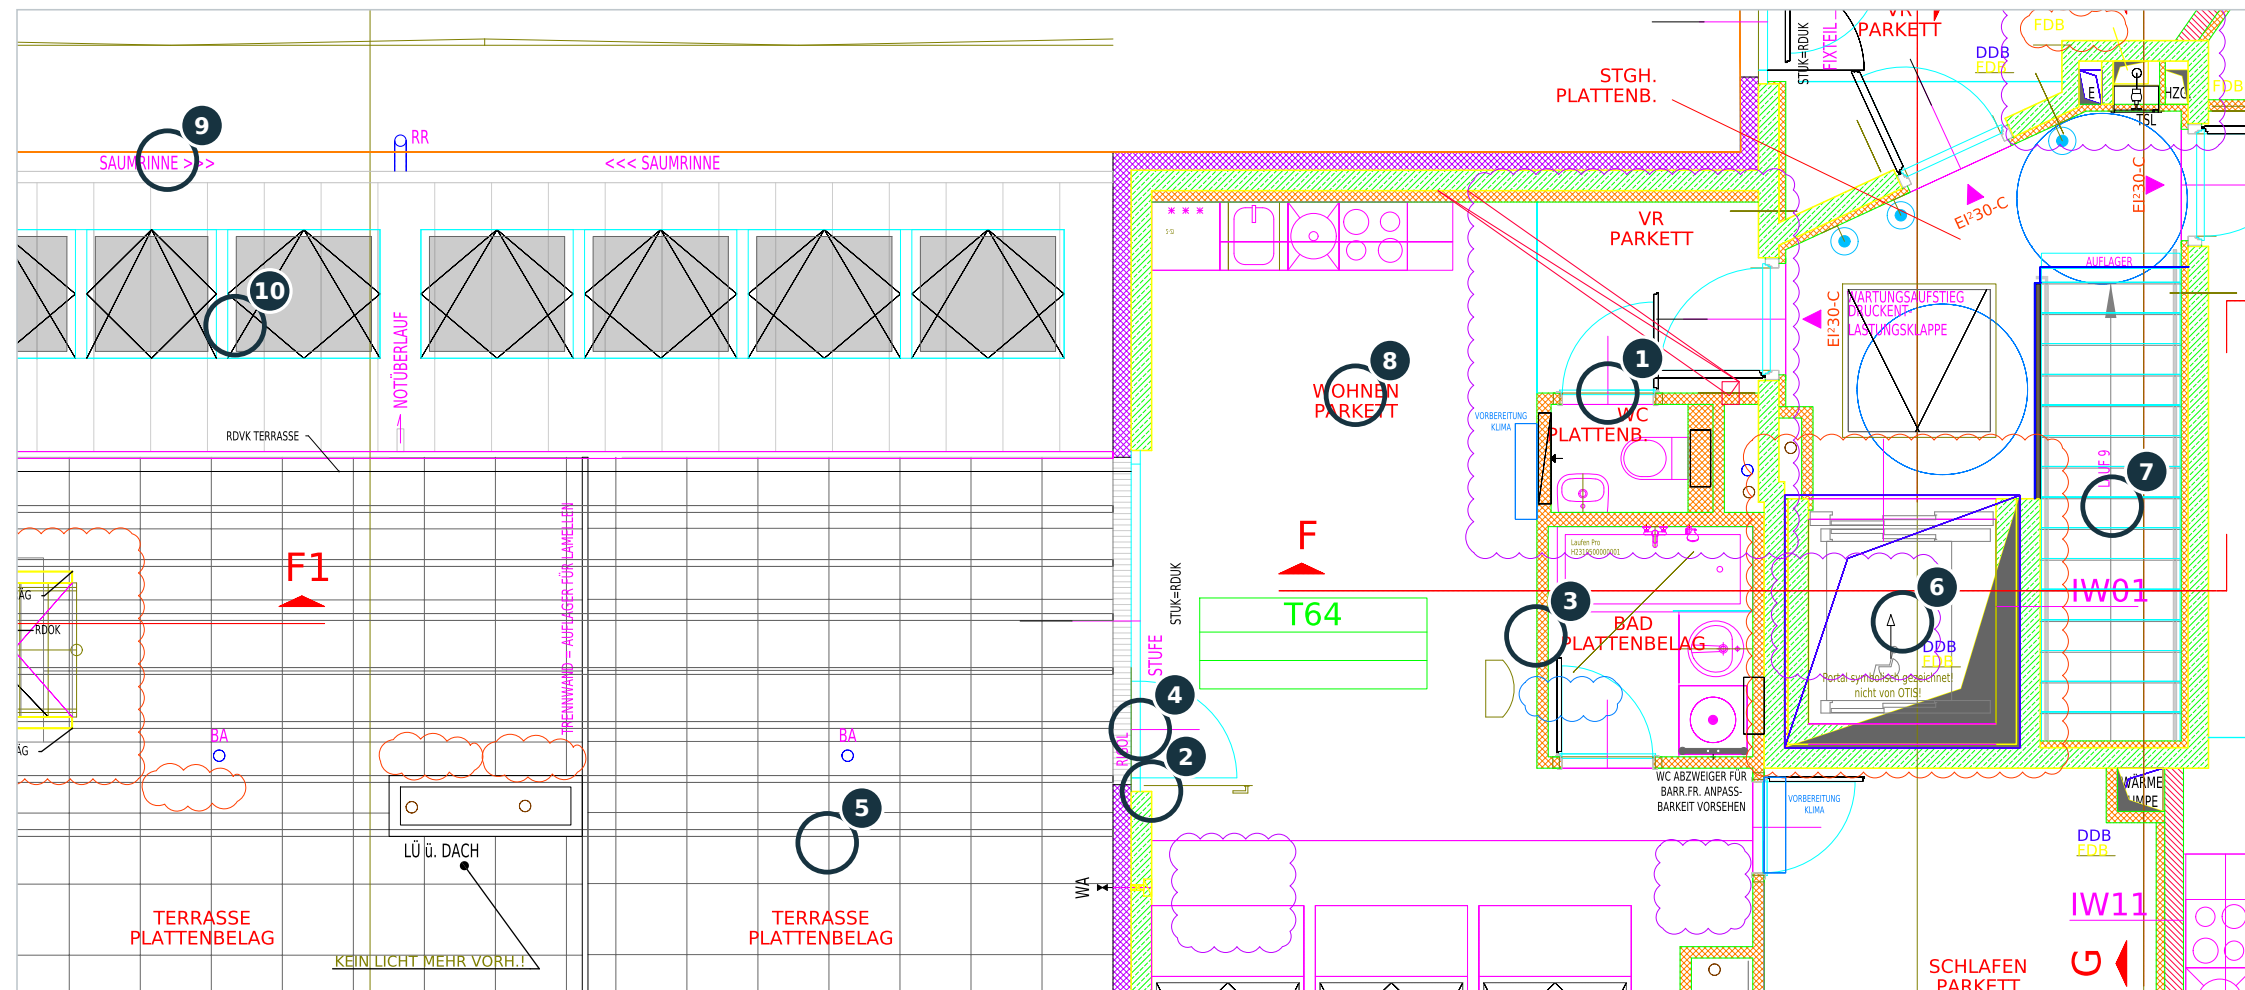



- RIVOPLAN | Lernheft Grundriss lesen | 2. Dachgeschoss (2DG ohne Masse.pdf) | Lernmarkierungen, keine geprüfte Planung

Checkliste: So liest du jeden Grundriss – auch im Dach

Schritt 1 – Überblick

Plantitel (hier: „2. DACHGESCHOSS“). Welches Stockwerk? Wo sind Straßen und Nachbarn?

Schritt 2 – Innen und draußen trennen

Wo sind rote Wände und Glasfronten? Alles darin ist innen. Davor: Terrasse oder Dach.

Schritt 3 – Wände verfolgen

Streifen mit zwei Kanten und Muster. Dicke trennen Wohnungen, dünne trennen Zimmer.

Schritt 4 – Türen suchen

Lücke + Türblatt + Viertelkreis. Der Bogen zeigt, wohin sie aufgeht.

Schritt 5 – Glas erkennen

Dünne parallele Linien ohne Muster. Mit Bogen = Glastür, ohne Bogen = festes Glas.

Schritt 6 – Dach-Zeichen erkennen

DFF, Rinnen, Flachdach, Dachschräge: gehören zum Dach, nicht zum Raum.

Schritt 7 – Räume benennen

Raumstempel: Name oben, Belag unten.

Schritt 8 – Kern finden

Treppe, Aufzug, Schächte – sie liegen in allen Geschossen übereinander.

Schritt 9 – Wohnungen abgrenzen

Durch eine Eingangstür hinein – alles, was man ohne Rückweg erreicht, ist eine Wohnung.

Schritt 10 – Weg gehen

Vom Stiegenhaus zur Wohnung, durch Türen in die Räume, durch die Terrassentür hinaus.

Schritt 11 – Grenzen kennen

Höhen, Dachform, Material, Tragwerk stehen in anderen Plänen. Unklares als „unklar“ markieren.

Der Abschlusstest

Nimm die Seite „Der Originalplan – unverändert“ und zeige ohne Farben: Wo hat die Wohnung **T56** ihre Eingangstür, ihre Räume und ihren Zugang ins Freie? Wenn du das kannst: Gratulation – du liest auch Dachgeschoss-Pläne.