


Einen Grundriss lesen – ganz von vorne

2. Obergeschoss · Wohnhaus Aichholzgasse / Pohlpassse · Lernbuch mit farbigen Markierungen direkt im Originalplan

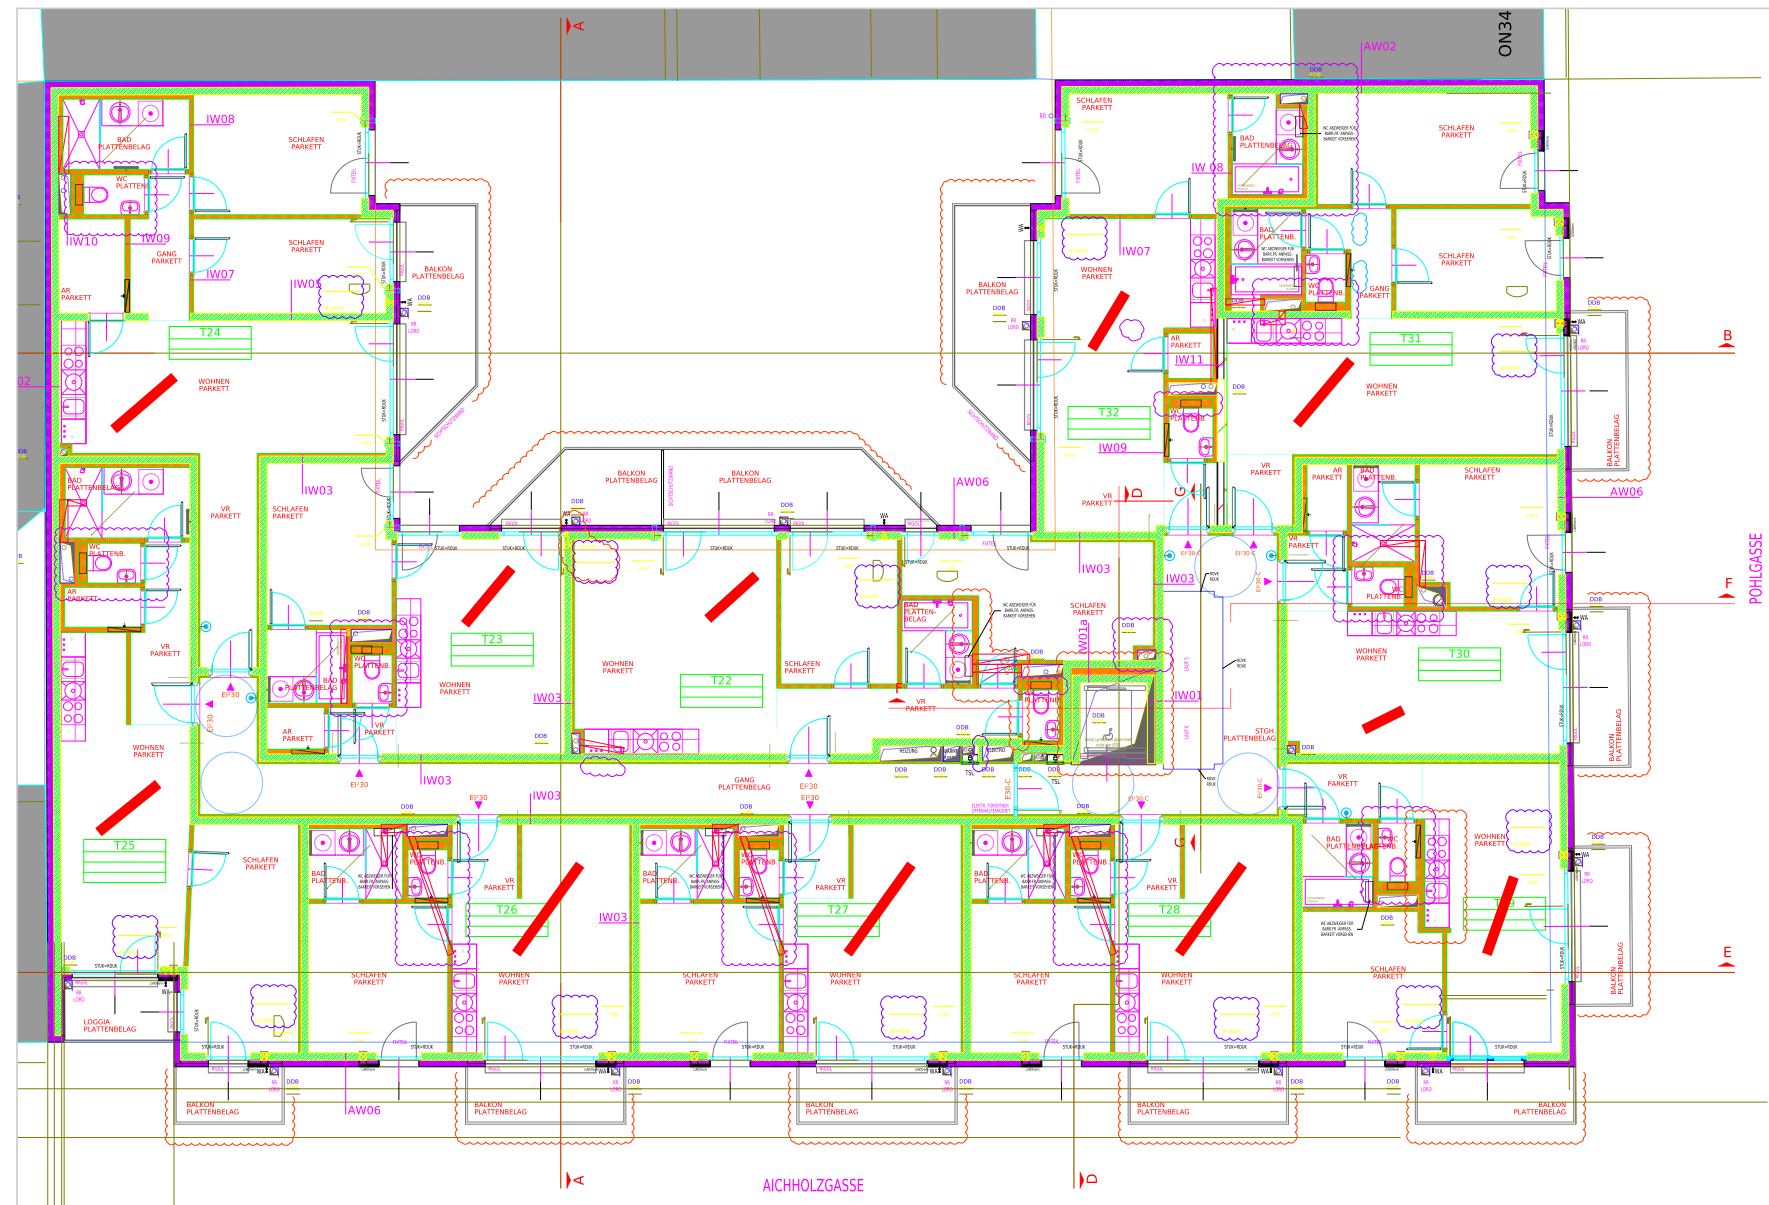

Für wen ist dieses Buch?

Für jemanden, der **noch nie** einen Bauplan gesehen hat. Du musst nichts wissen. Jedes Wort wird erklärt, bevor es benutzt wird.

Was lernst du?

Am Ende kannst du **genau diesen Plan** anschauen und sagen:

- wo eine **Wand** ist,
- wo eine **Tür** ist, welcher Teil das **Türblatt** ist und was der **Bogen** bedeutet,
- wo ein **Fenster** ist, wo sein **Rahmen** und wo das **Glas** ist,
- wo ein Mensch **gehen** kann und wo nicht,
- was **Treppe**, **Lift**, **Bad**, **Küche** und **Loggia** sind.

Wie ist das Buch gebaut?

Wir fangen beim Allereinfachsten an („Was ist überhaupt ein Grundriss?“) und werden Seite für Seite genauer. Fast jede Seite zeigt links ein Stück **dieses** Plans, stark vergrößert. Farbige Flächen, Pfeile und Nummern zeigen genau auf die Stelle, um die es geht. Rechts steht die Erklärung.

Das Bild links ist der Originalplan (Datei 2OG_ohne_Masse.pdf). Es ist dasselbe Haus wie im Lernbuch zum 1. Obergeschoss. Dieses Buch ist aber vollständig und kann ohne das andere gelesen werden. Die Wohnungen heißen hier T22 bis T32, und statt Loggien haben die meisten Wohnungen einen Balkon.

00 | So benutzt du dieses Buch

Erst schauen, dann lesen, dann selbst im Plan wiederfinden.

1 · Immer zuerst auf das Bild schauen

Links siehst du einen Ausschnitt aus dem Plan. Er ist meistens **grau** gezeichnet, damit die farbigen Markierungen gut auffallen. Die grauen Linien sind genau die Linien des Originalplans.

2 · Dann den Pfeilen folgen

Jeder Pfeil beginnt bei einem kleinen Kästchen mit Text und endet **genau** auf der Linie, um die es geht. Die Nummern im Bild (① ② ③ ...) gehören zu den gleichen Nummern im Text rechts.

3 · Dann rechts lesen

Rechts steht jedes Mal in derselben Reihenfolge:

- **Was ist das?** – in ganz einfachen Worten.
- **Wie sieht es im Plan aus?**
- **Woran erkenne ich es?**
- **Wo ist es auf diesem Plan?**
- **Was bedeutet es?**
- **Womit könnte ich es verwechseln?**

Die Zahl vor jedem Titel (01, 02, ...) ist die **Kapitelnummer**. Steht im Text „(Kapitel 12)“, findest du dort mehr dazu.

4 · Ehrlich bleiben

Manches zeigt ein Grundriss nicht sicher, zum Beispiel wie hoch ein Fenster ist. Dann steht das auch so da. Wir erfinden nichts dazu.

Die Lernfarben

 **Rot** – Wand. Hier ist festes Mauerwerk oder Beton. Man kann nicht hindurch.

 **Blau** – Tür, vor allem das Türblatt (der Teil, den man auf- und zumacht).

 **Violett** – Öffnungsbogen: zeigt, wohin sich eine Tür oder ein Fensterflügel bewegt.

 **Gelb** – Fenster bzw. Fensterrahmen.

 **Hellblau** – Glas (Glasscheibe).

 **Grün** – Boden, auf dem ein Mensch stehen und gehen kann.

 **Türkis** – Treppe: dort geht es nach oben oder unten.

 **Orange** – Öffnung in der Wand, Hindernis (Einrichtung, Schacht), Lift – und Achtung: sieht aus wie etwas anderes, ist es aber nicht.


 **Grau** – der Originalplan selbst (unverändert, nur ohne Farbe).

MERKSATZ


Die Farben in diesem Buch sind **Lernfarben**. Sie wurden nachträglich darübergerlegt. Sie sind nicht Teil des Originalplans.

01 | Was ist überhaupt ein Grundriss?


Ein Grundriss ist eine Zeichnung eines Stockwerks – so, als würde man von oben hineinschauen.

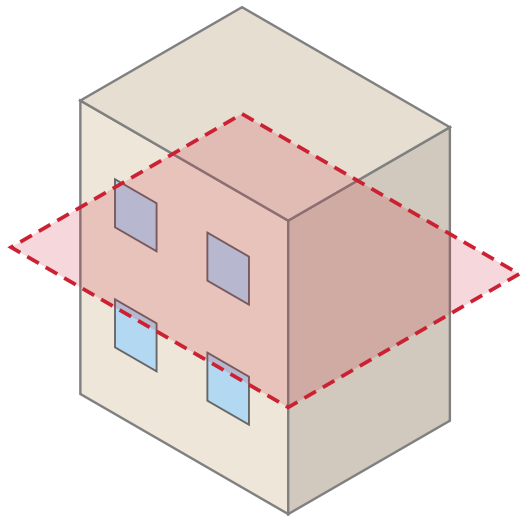

1 Ein Haus. Die rote Ebene zeigt, wo wir es in Gedanken **waagrecht durchschneiden** – etwa in Brusthöhe.

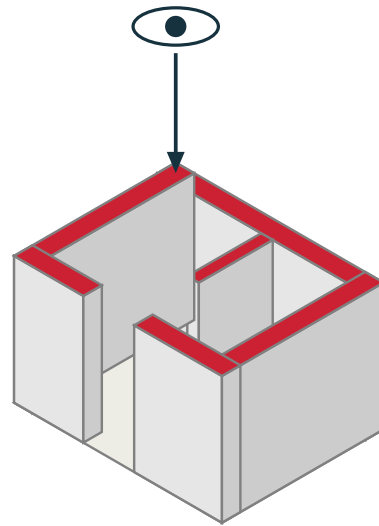

2 Den oberen Teil heben wir weg und schauen **senkrecht von oben** hinein. Die durchgeschnittenen Wände sieht man als dicke Streifen (hier rot).

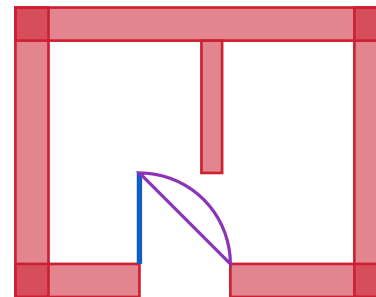

3 Was wir von oben sehen, wird auf Papier gezeichnet. **Das ist ein Grundriss.** Die Lücke unten mit dem Bogen ist eine Tür.

Stell dir vor ...

... du hast ein Spielzeughaus. Du schneidest es mit einem großen Messer waagrecht durch, ungefähr in der Höhe deiner Brust. Den oberen Teil hebst du ab. Jetzt schaust du von oben in das Haus hinein.

Du siehst: die **Wände** (dort, wo das Messer durchgeschnitten hat), die **Lücken** in den Wänden (Türen und Fenster) und alles, was **auf dem Boden** steht (Möbel, Badewanne, Küche).

Genau das zeichnet ein Architekt. Diese Zeichnung heißt **Grundriss**.

Was ist das?

Ein **Grundriss** ist eine Zeichnung. Sie zeigt ein Stockwerk eines Gebäudes **von oben**.

Was heißt „Stockwerk“ oder „Geschoss“?

Ein Haus hat mehrere Ebenen übereinander: Erdgeschoss (ganz unten, auf Höhe der Straße), darüber das 2. Obergeschoss, darüber das 2. Obergeschoss und so weiter. Jede Ebene nennt man **Geschoss** oder Stockwerk.

Unser Plan

Unser Plan zeigt das **2. Obergeschoss**, also das zweite Stockwerk über dem Erdgeschoss. Das steht auch unten rechts auf dem Plan: „2. OBERGESCHOSS“.


Wichtig

Ein Grundriss ist **flach**. Er zeigt, wie lang und wie breit etwas ist – aber nicht, wie **hoch** es ist. Ob ein Fenster bis zum Boden geht, sieht man darin meistens nicht.

02 | Was bedeutet „von oben gesehen“?

Von oben sehen Dinge anders aus als von der Seite. Das muss man einmal verstehen.

Von der Seite (so kennst du Dinge)

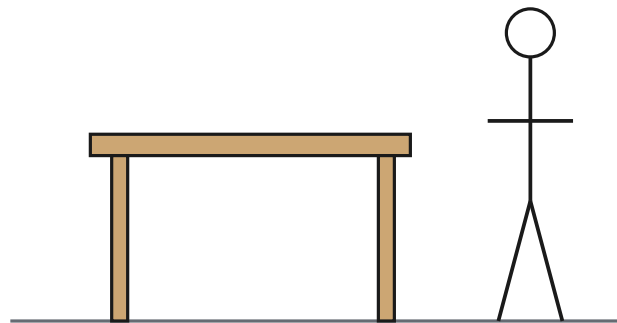

Tisch mit Beinen, daneben ein Mensch.

Von oben (so zeigt es ein Grundriss)



Vom Tisch bleibt nur die Platte (ein Rechteck).
Vom Menschen sieht man Schultern und Kopf
(zwei Kreise).

Warum ist das wichtig?

Im echten Leben siehst du Dinge fast immer **von der Seite**: eine Tür als großes Rechteck mit Klinke, einen Tisch mit vier Beinen.

Im Grundriss schaust du **von oben**. Dann sieht alles anders aus:


- ein Tisch → nur noch die Tischplatte (ein Rechteck),
- eine Wand → ein langer Streifen,
- eine Tür → ein dünner Strich und ein Viertelkreis,
- ein Waschbecken → ein Rechteck mit einem runden Loch.

Hier im Plan

Unten links siehst du ein echtes Stück aus unserem Plan: das **Bad** der Wohnung T26. Von oben sieht man die Waschmaschine, das Waschbecken und die Dusche nur als flache Formen.

Merke dir

Wenn du eine Form nicht verstehst, frage dich: *Wie sähe dieser Gegenstand aus, wenn ich von der Decke auf ihn hinunterschaue?*

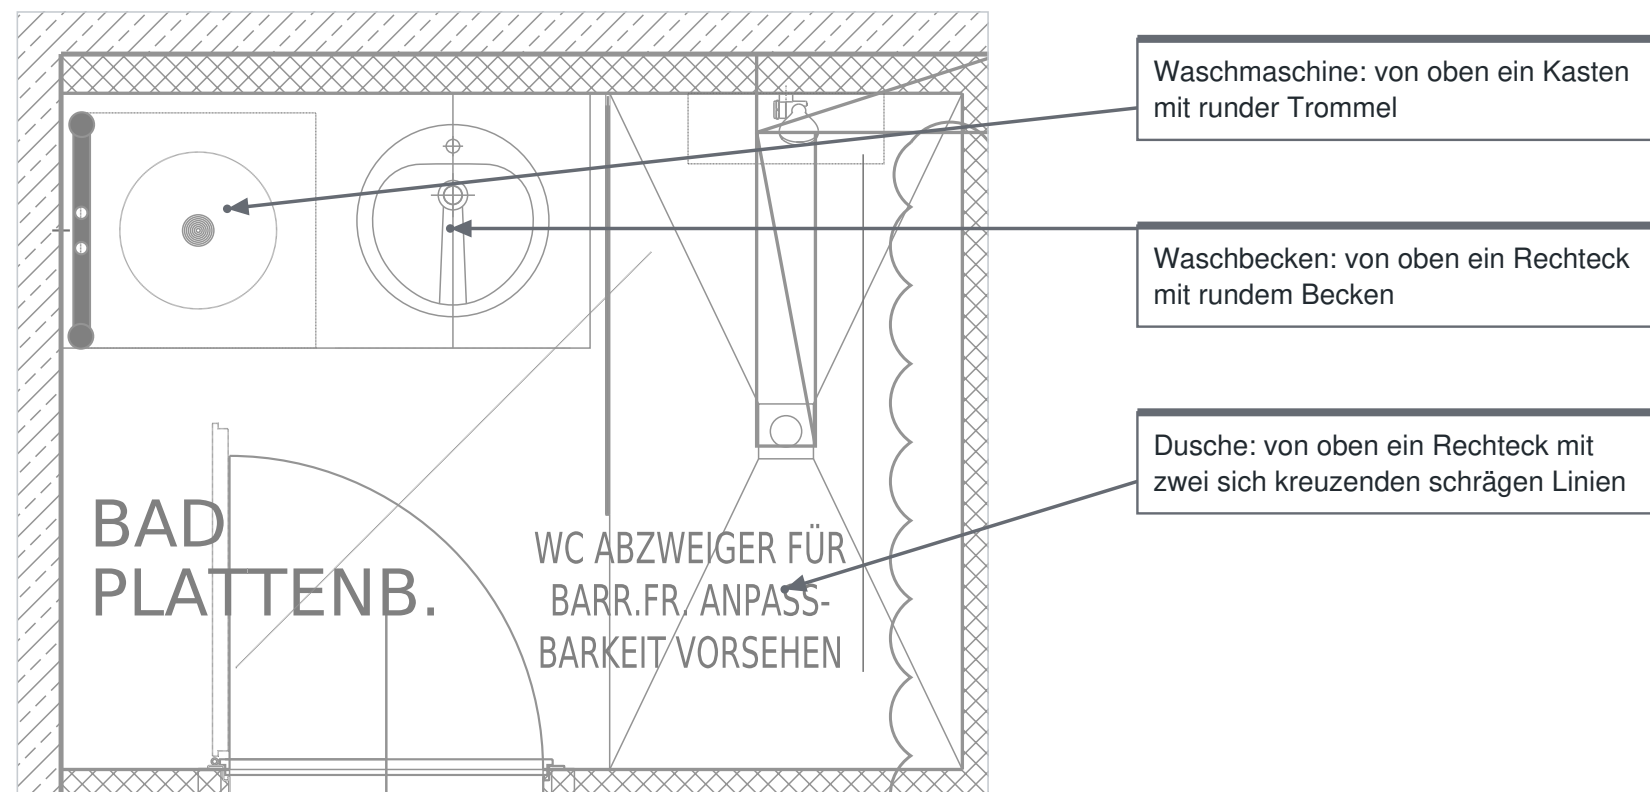


MERKSATZ

Im Grundriss siehst du immer nur die **Umrisse von oben**. Ein Tisch ist ein Rechteck, eine Wand ist ein Streifen, eine Tür ist ein Strich mit einem Bogen.

03 | Der ganze Plan – so wie er ist

Das ist der Originalplan ohne jede Veränderung. Keine Sorge: Er sieht am Anfang wie ein Durcheinander aus.

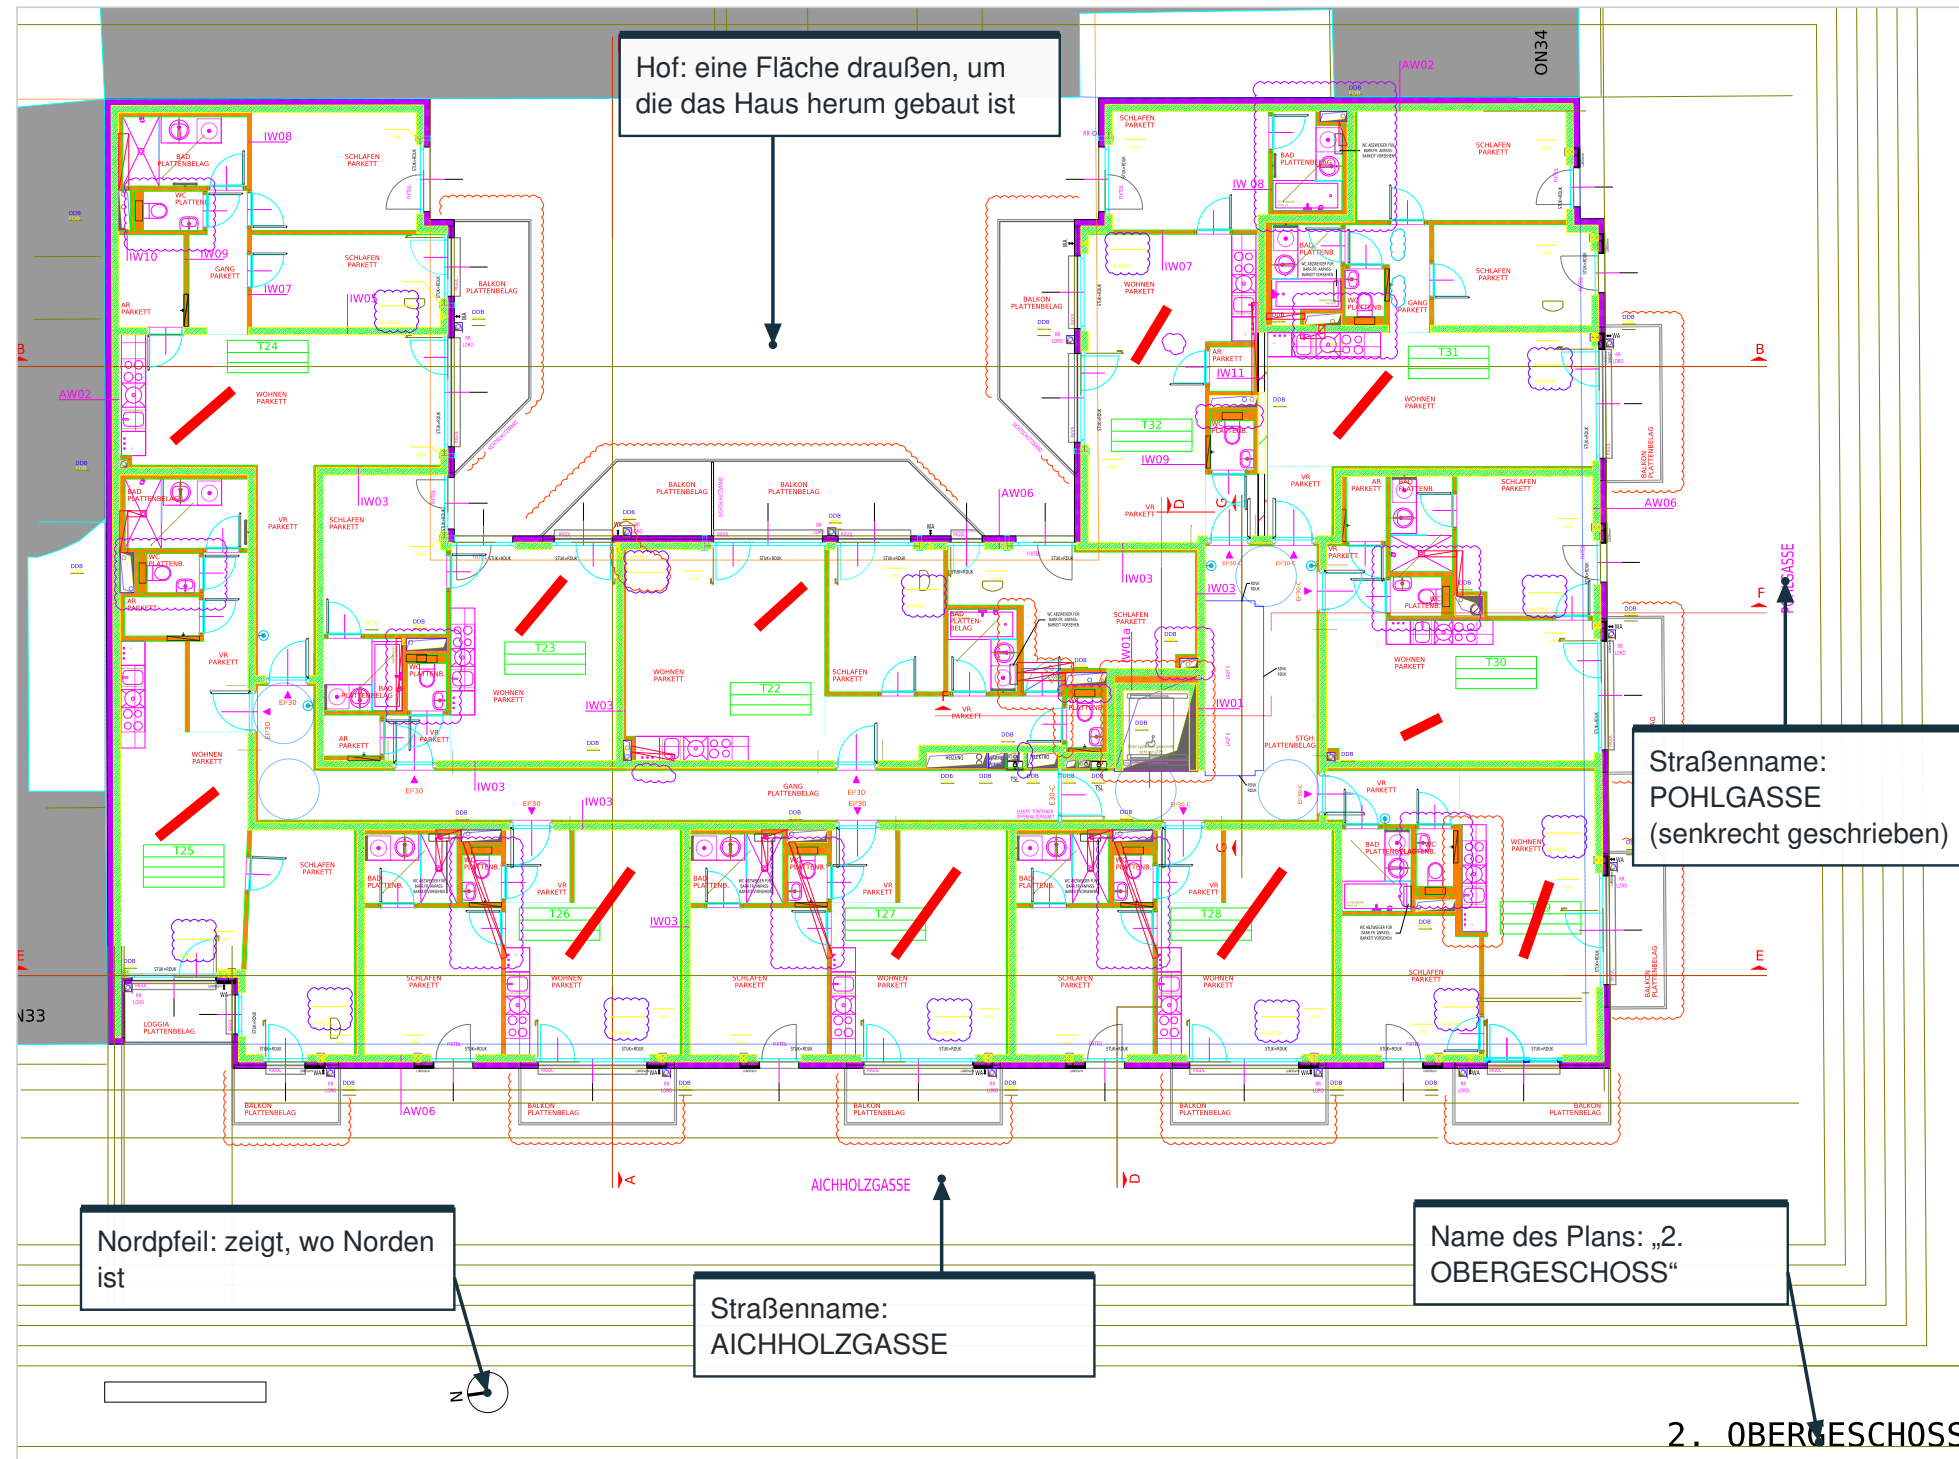

Was siehst du?

Ein großes Blatt voller farbiger Linien. Das ist normal. Ein Architekturplan wird am Computer gezeichnet, und der Computer gibt jeder Art von Linie eine eigene Farbe.

Zuerst nur grob orientieren

- **Der dünne Rahmen** um alles ist der Rand des Zeichenblatts.
- **Unten rechts** steht, was der Plan zeigt: „2. OBERGESCHOSS“.
- **Unten links** ist ein kleiner Kreis mit einem Pfeil und dem Buchstaben N: der **Nordpfeil**. Er zeigt die Himmelsrichtung Norden. Hier zeigt der Strich nach links (leicht schräg): Norden ist also links.
- **AICHHOLZGASSE** (unten) und **POHLASSE** (rechts) sind die Straßen, an denen das Haus steht.
- Die **große helle Fläche oben in der Mitte** ist ein **Hof**: Dort ist kein Haus, sondern draußen.
- **Grau hinterlegte Flächen** oben und links liegen außerhalb unseres Hauses (Nachbarbereiche).

Wichtig


Die Farben im Originalplan sagen noch **nicht** „das ist eine Wand“ oder „das ist eine Tür“. Ab der nächsten Seite legen wir unsere eigenen, einfachen Lernfarben darüber.

MERKSATZ

Ein Plan hat viele Farben und Zeichen. Wir lernen sie **einzel**n und der Reihe nach – nicht alle auf einmal.

04 | Orientierung: Was ist wo in diesem Geschoss?

Bevor wir ins Detail gehen: eine grobe Landkarte des ganzen Stockwerks.

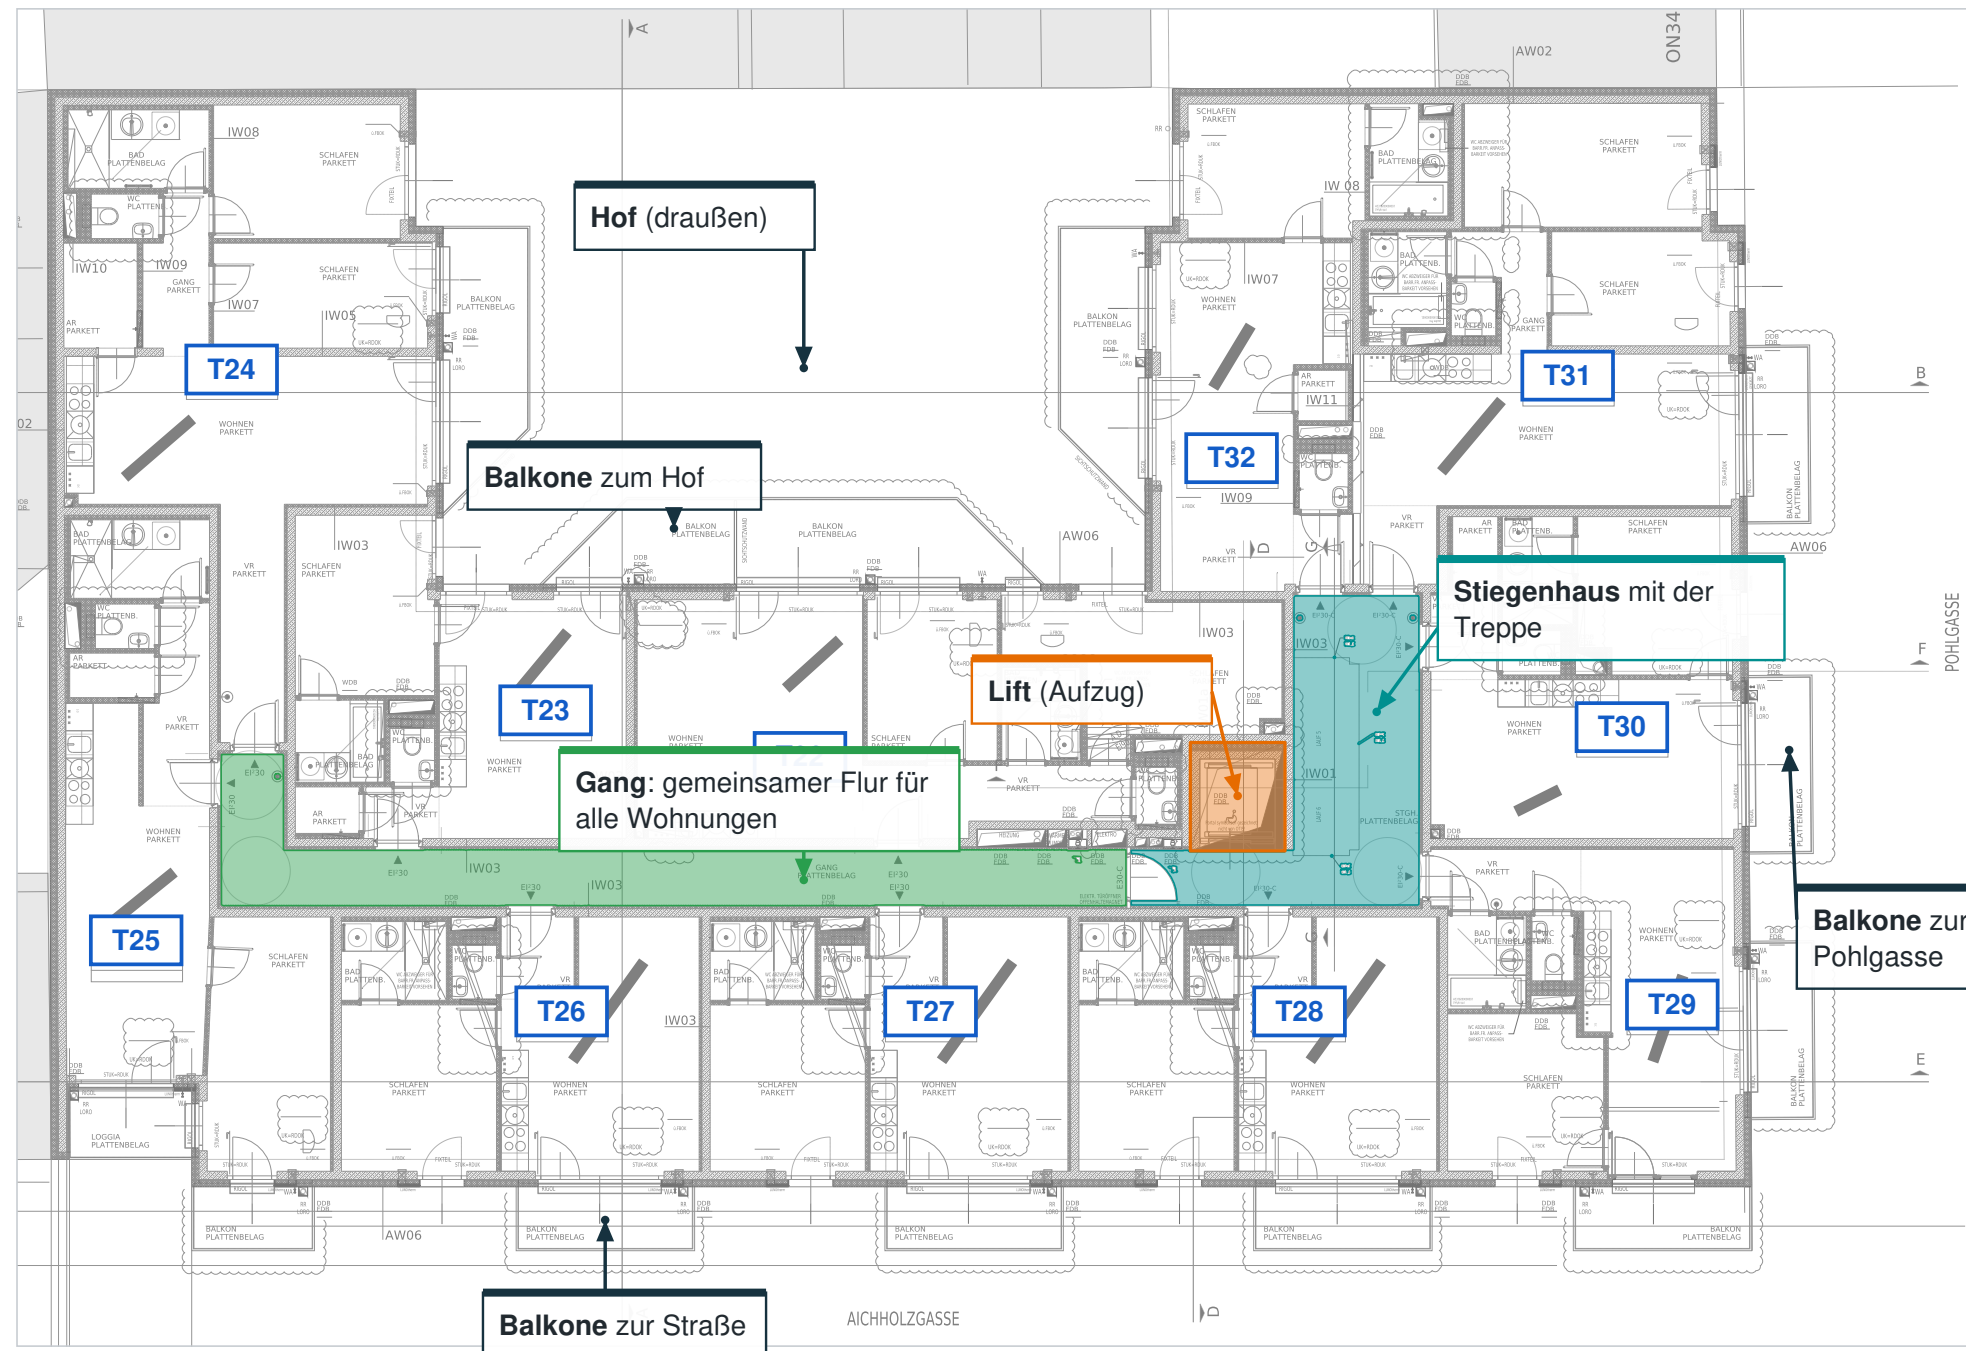

Die Wohnungen

In jeder Wohnung steht ein grünes Kästchen mit einer Nummer, zum Beispiel **T26**. In Österreich nennt man eine Wohnungsnummer oft „Top“ – daher das **T**. Im Bild sind die Nummern blau umrandet.

Es gibt 11 Wohnungen: **T22 bis T32**. Die Nummer von **T29** (rechts unten) ist im Original teilweise von einem roten Balken verdeckt; man liest „T?9“, und aus der Reihenfolge ergibt sich T29.

Der Gang (grün)

Ein langer Flur verbindet alle Wohnungen mit dem Stiegenhaus. Er gehört niemandem allein, alle benutzen ihn.

Stiegenhaus (türkis) und Lift (orange)

Dort kommt man in die anderen Stockwerke: zu Fuß über die Treppe oder mit dem Lift.

Hof und Balkone

Oben in der Mitte ist das Haus offen: ein Hof. Dort hängen einige Balkone. Weitere Balkone hängen **außen vor** der Hauswand: unten zur Aichholzgasse und rechts zur Pohl gas.

Unsere Lernwohnung


Die meisten Beispiele in diesem Buch stammen aus der Wohnung **T26** (unten, links von der Mitte). Sie ist klein und hat fast alles, was es zu lernen gibt: Eingangstür, Vorraum, WC, Bad, Schlafzimmer, Wohnzimmer mit Küche, ein Fenster, eine große Glasfront mit Balkontür und einen Balkon.

MERKSATZ

Das Geschoss besteht aus **11 Wohnungen** (T22 bis T32), einem gemeinsamen **Gang**, einem **Stiegenhaus** mit Treppe und einem **Lift**.

05 | Was stellen die vielen Linien dar?

Ein Plan besteht aus Linien, Mustern, Bögen und Schrift. Jede Art hat eine andere Aufgabe.

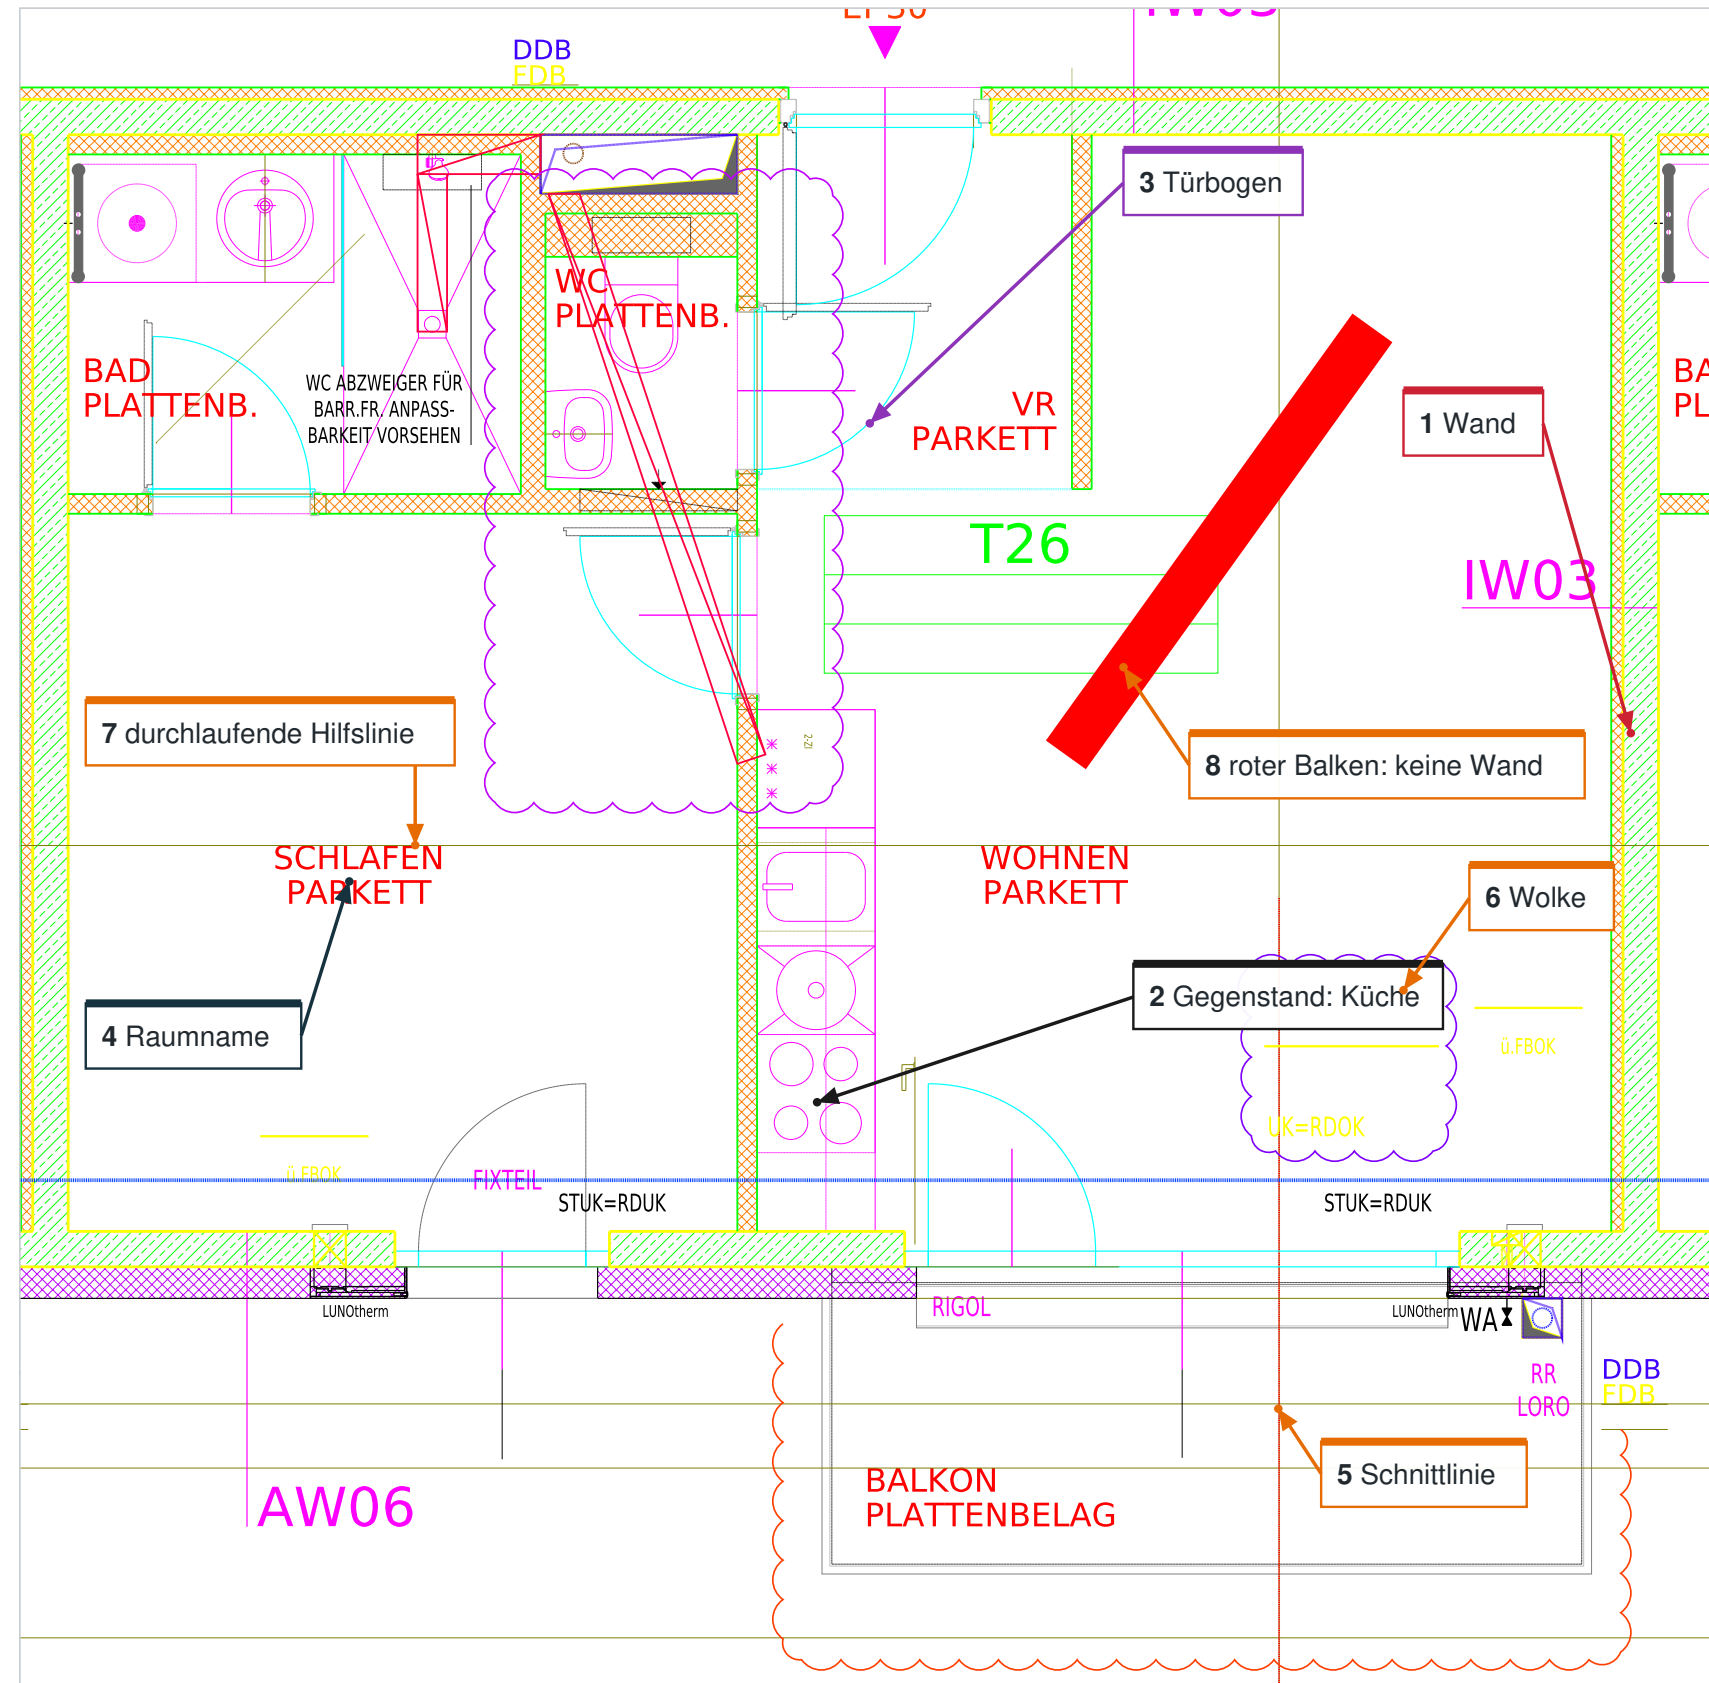

Links siehst du die Wohnung T26 in den **Originalfarben**. Die Farben kommen vom Zeichenprogramm. Wichtig ist nicht die Farbe, sondern die **Form** der Linie.

1 · Breite Streifen mit Muster

Zwei lange Linien mit einem Muster aus Strichen dazwischen: das ist fast immer eine **Wand**.

2 · Dünne Linien, die kleine Formen bilden

Rechtecke, Kreise, kleine Kästchen: **Gegenstände**, die im Raum stehen (Küche, Waschbecken, WC).

3 · Viertelkreise

Ein Bogen wie ein Stück Tortenrand zeigt, **wie sich eine Tür bewegt**. Er ist keine Wand – der Bogen ist nur die Spur, die die Türkante in der Luft macht.

4 · Schrift

Wörter wie SCHLAFEN oder WOHNEN sind **Beschriftungen**. Sie stehen im Plan, aber nicht im echten Haus.


5, 6, 7, 8 · Hilfszeichen

Lange gerade Linien quer durch das Haus, „Wolken“ aus kleinen Bögen und ähnliche Zeichen sind **Hinweise für die Planer**. Auch der dicke rote Schrägbalken (**8**) ist kein Bauteil (Kapitel 12). Man erkennt sie daran, dass sie **durch Wände und Räume hindurchlaufen**. Eine echte Wand würde das nie tun.

MERKSATZ Nicht jede Linie ist eine Wand. Frag bei jeder Linie: **Ist das ein Bauteil, ein Gegenstand, eine Bewegung oder nur eine Beschriftung?**

06 | Die Schrift im Plan lesen

Wörter und Abkürzungen verraten, was ein Raum ist und woraus sein Boden besteht.

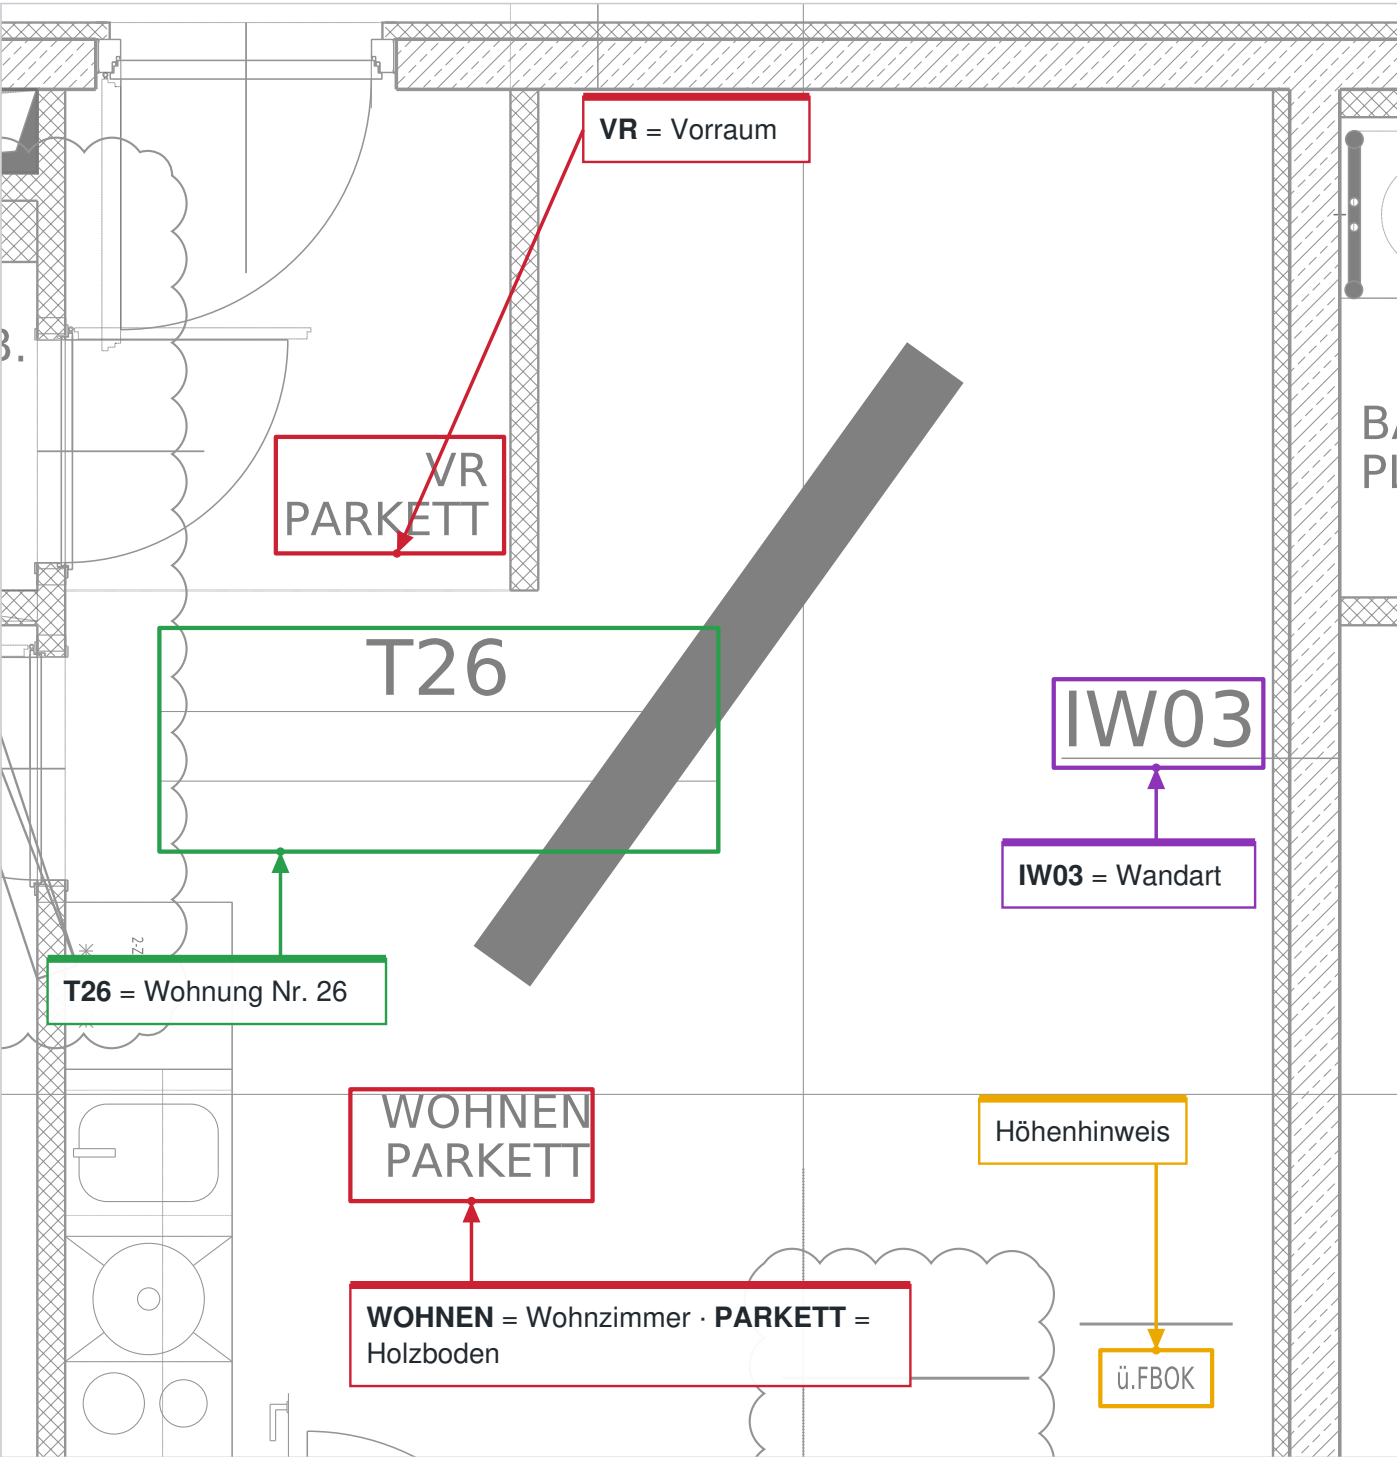

Die Raumnamen in diesem Plan

WOHNEN	Wohnzimmer
SCHLAFEN	Schlafzimmer
VR	Vorraum – gleich hinter der Wohnungstür
GANG	Flur (in der Wohnung oder der gemeinsame Gang)
BAD	Badezimmer
WC	Toilette
AR	Abstellraum (kleiner Raum zum Verstauen)
STGH.	Stiegenhaus – dort ist die Treppe
LOGGIA	eine Art Balkon, der in das Haus hineingeschoben ist (im 2. OG nur bei T25)
BALKON	Plattform draußen vor der Wand

Die Bodenarten (untere Zeile)

PARKETT	Holzboden
PLATTENBELAG, PLATTENB., PLATTENBEL.	Boden aus Fliesen oder Platten (alle drei meinen dasselbe, nur verschieden abgekürzt)

Weitere Beschriftungen


T22 ... T32	Nummer der Wohnung („Top“)
IW03, AW02 ...	Kürzel für eine Wandart. IW steht üblicherweise für Innenwand, AW für Außenwand. Was genau dahintersteckt, steht auf einer anderen Liste, die wir nicht haben.
FBOK, RDOK, RDUK, STUK	Höhenangaben für die Bauleute. Für das Lesen des Grundrisses brauchst du sie nicht.

MERKSATZ

Ein Raumname besteht meist aus **zwei Zeilen**: oben **wofür** der Raum ist, unten **welcher Boden** darin liegt.

07 | Unsere Lernwohnung T26

Diese kleine Wohnung schauen wir uns jetzt ganz genau an.

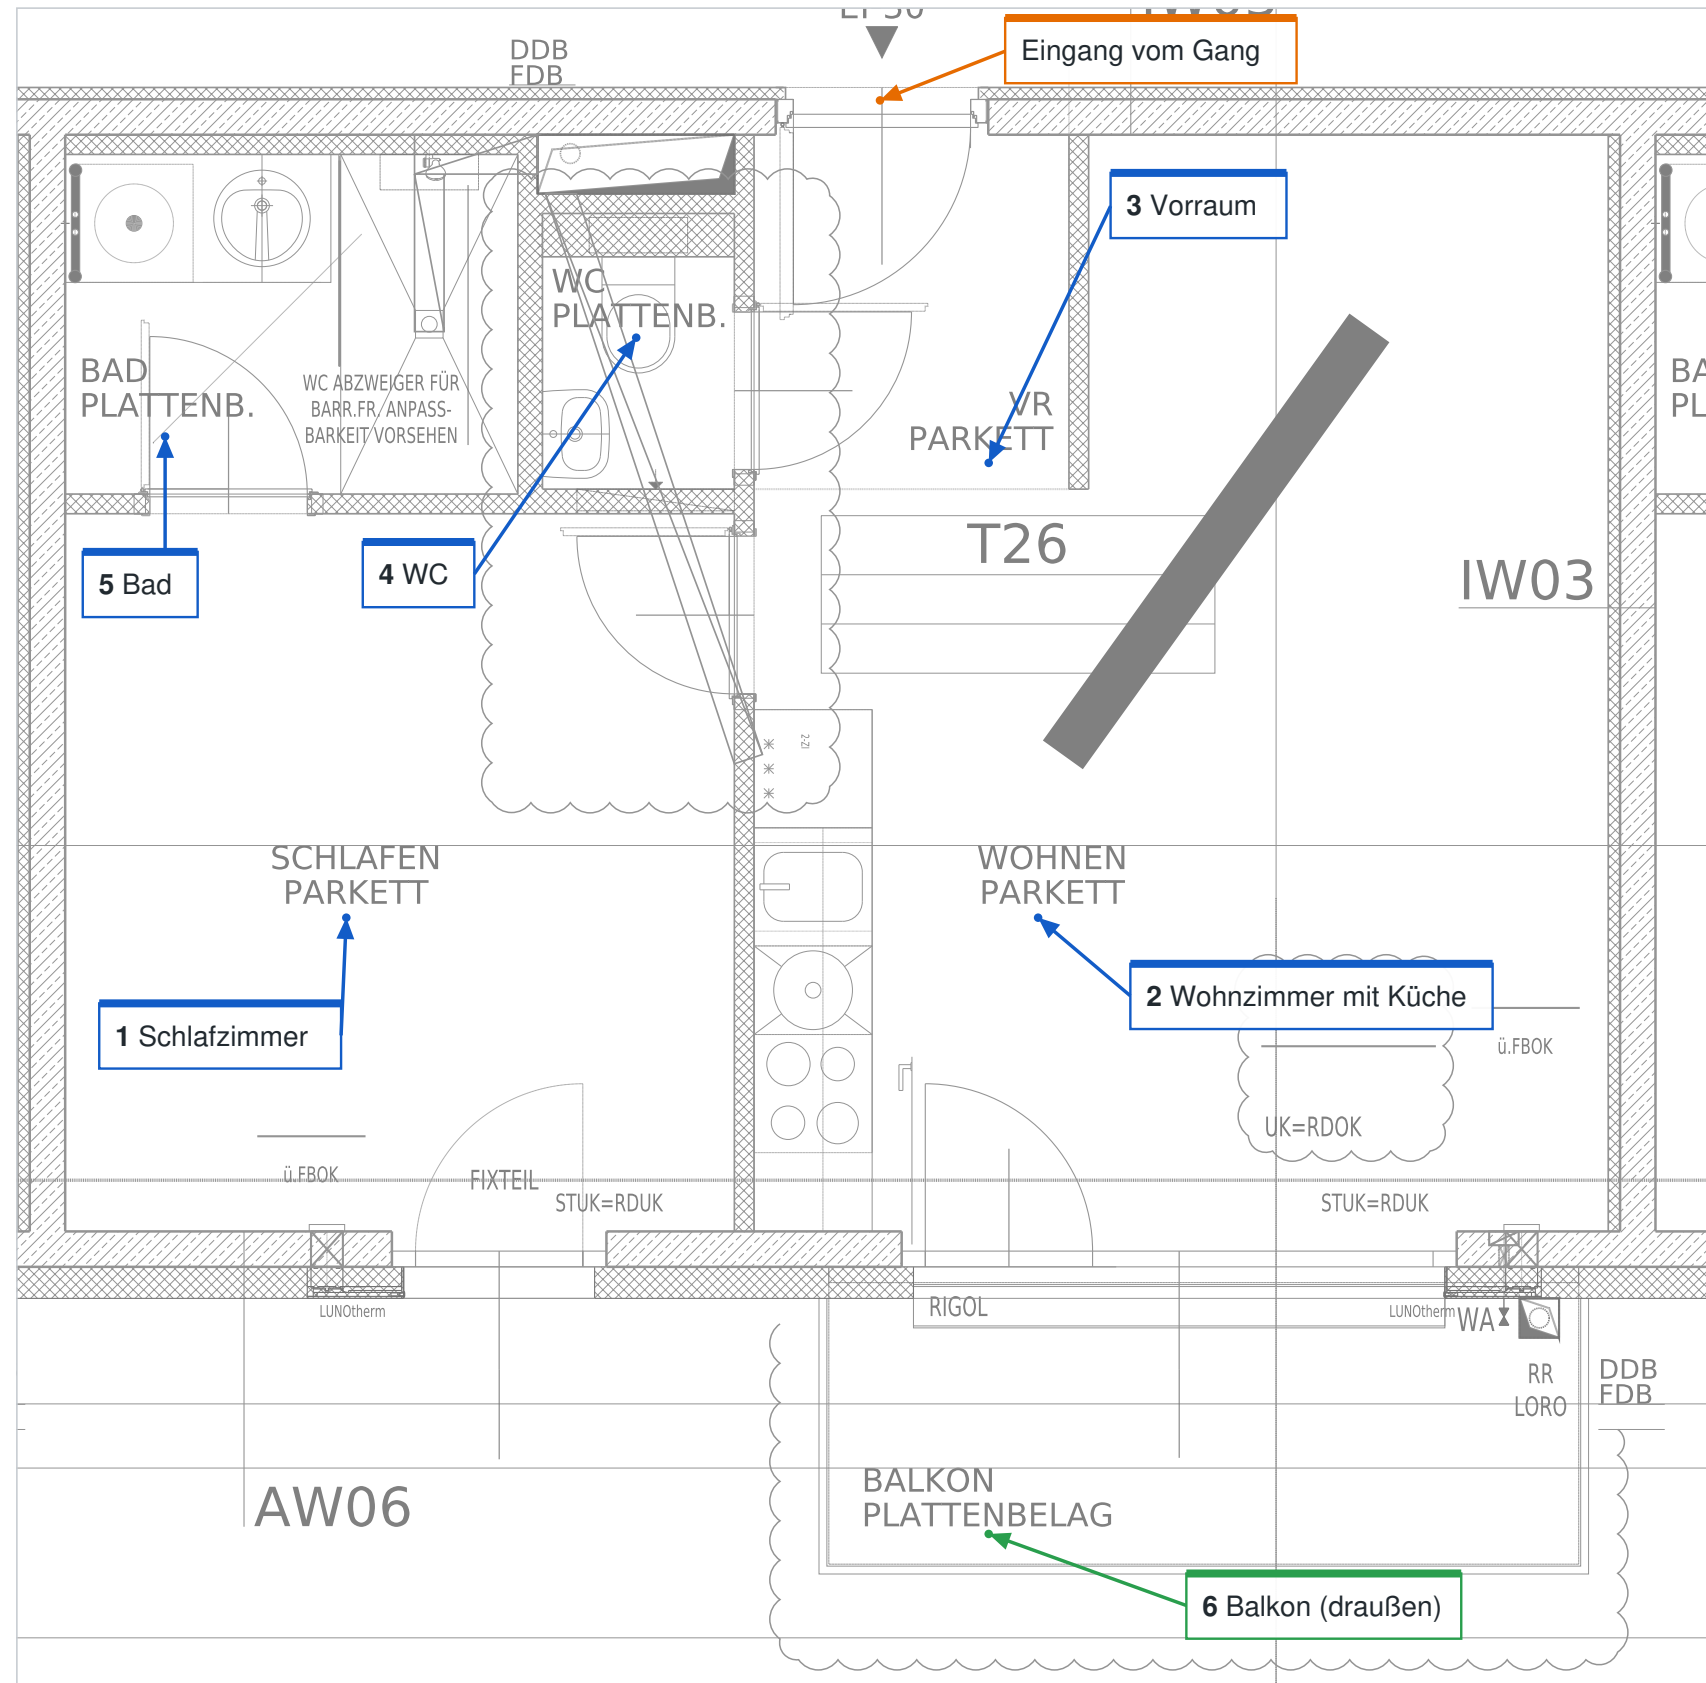

Was ist ein Raum?

Ein **Raum** ist ein Stück Fläche, das rundherum von Wänden begrenzt ist – wie ein Zimmer. Durch eine **Tür** oder eine offene Stelle kommt man hinein.

Die Räume von T26

- 1 Schlafzimmer (SCHLAFEN)** – links unten, groß.
- 2 Wohnzimmer (WOHNEN)** – rechts, groß. An seiner linken Wand steht die Küche. Unten hat es eine breite Glasfront zum Balkon.
- 3 Vorraum (VR)** – gleich hinter der Wohnungstür.
- 4 WC** – eine kleine Toilette.
- 5 Bad** – links oben, mit Dusche und Waschbecken.
- 6 Balkon** – ganz unten, **vor** der Hauswand. Er ist draußen.

So kommt man hinein

Oben (orange Pfeil) ist der gemeinsame Gang. Von dort führt die Wohnungstür in den Vorraum. Vom Vorraum geht man weiter ins WC, ins Schlafzimmer und – ohne Tür – ins Wohnzimmer. Vom Wohnzimmer führt eine Glastür auf den Balkon.



Oben im Bild sieht man noch ein Stück des gemeinsamen Gangs, links und rechts Teile der Nachbarwohnungen T25 und T27. Der dicke rote Schrägbalken im Wohnzimmer ist kein Bauteil (Kapitel 12).

MERKSATZ

Ein Raum ist ein Bereich, der von Wänden umschlossen ist. Man betritt ihn durch eine Tür oder eine Öffnung.

08 | Was ist eine Wand?

Die Wand ist das Wichtigste im Grundriss. Sie teilt das Haus in Räume.

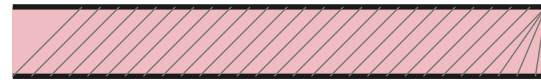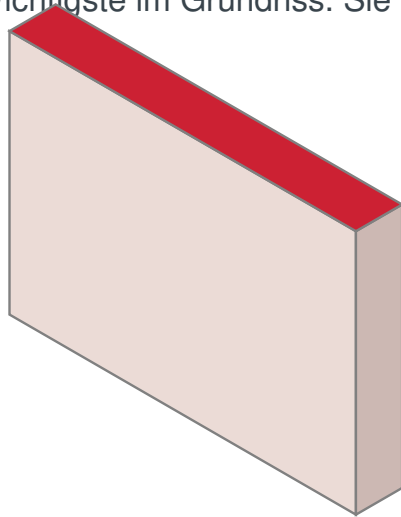

Dieselbe Wand im Grundriss: **zwei lange Linien** (die beiden Seiten der Wand) und dazwischen oft ein **Muster aus schrägen Strichen**. Dieses Muster heißt **Schraffur**.

Eine echte Wand: lang, hoch – und **dick**. Oben siehst du die Schnittfläche (rot).

Stell dir vor ...

... du stehst in deinem Zimmer. Links, rechts, vorne und hinten sind Wände. Sie sind hart, du kannst nicht durch sie hindurchgehen. Hinter einer Wand liegt ein anderes Zimmer – oder draußen.

Wenn wir das Haus in Gedanken durchschneiden (Kapitel 01), schneiden wir auch durch jede Wand. Von oben sieht man dann die **Schnittfläche** der Wand: einen langen Streifen. Er ist so breit, wie die Wand dick ist.

Was ist das?

Eine **Wand** ist ein festes, hohes Bauteil aus Beton, Ziegeln oder Platten. Sie trennt einen Raum vom nächsten oder das Innere des Hauses von draußen.

Wie sieht sie im Plan aus?

- **zwei lange parallele Linien** – das sind die beiden Seiten der Wand;
- **dazwischen** meistens ein **Muster** aus schrägen Strichen oder Kreuzen (die Schraffur);
- manchmal ist die Fläche dazwischen auch einfarbig oder leer.

Warum manchmal mehrere Linien?

Eine Wand kann aus mehreren **Schichten** bestehen – zum Beispiel innen Beton und außen eine Wärmedämmung (eine Schicht, die das Haus warm hält). Jede Schicht bekommt eigene Linien und ein eigenes Muster. Alle Schichten zusammen sind **eine** Wand.

Was bedeutet das für mich?


Wo eine Wand ist, kann niemand gehen. Menschen kommen nur dort von einem Raum in den anderen, wo die Wand **unterbrochen** ist – an einer Tür oder Öffnung.

MERKSATZ

Eine Wand hat immer **zwei Seiten**. Im Grundriss siehst du deshalb **zwei Linien** und die Fläche dazwischen. Beides zusammen ist die Wand.

09 | Wände in der Wohnung T26 erkennen

Alle Wände sind hier rot eingefärbt. Folge den Pfeilen.

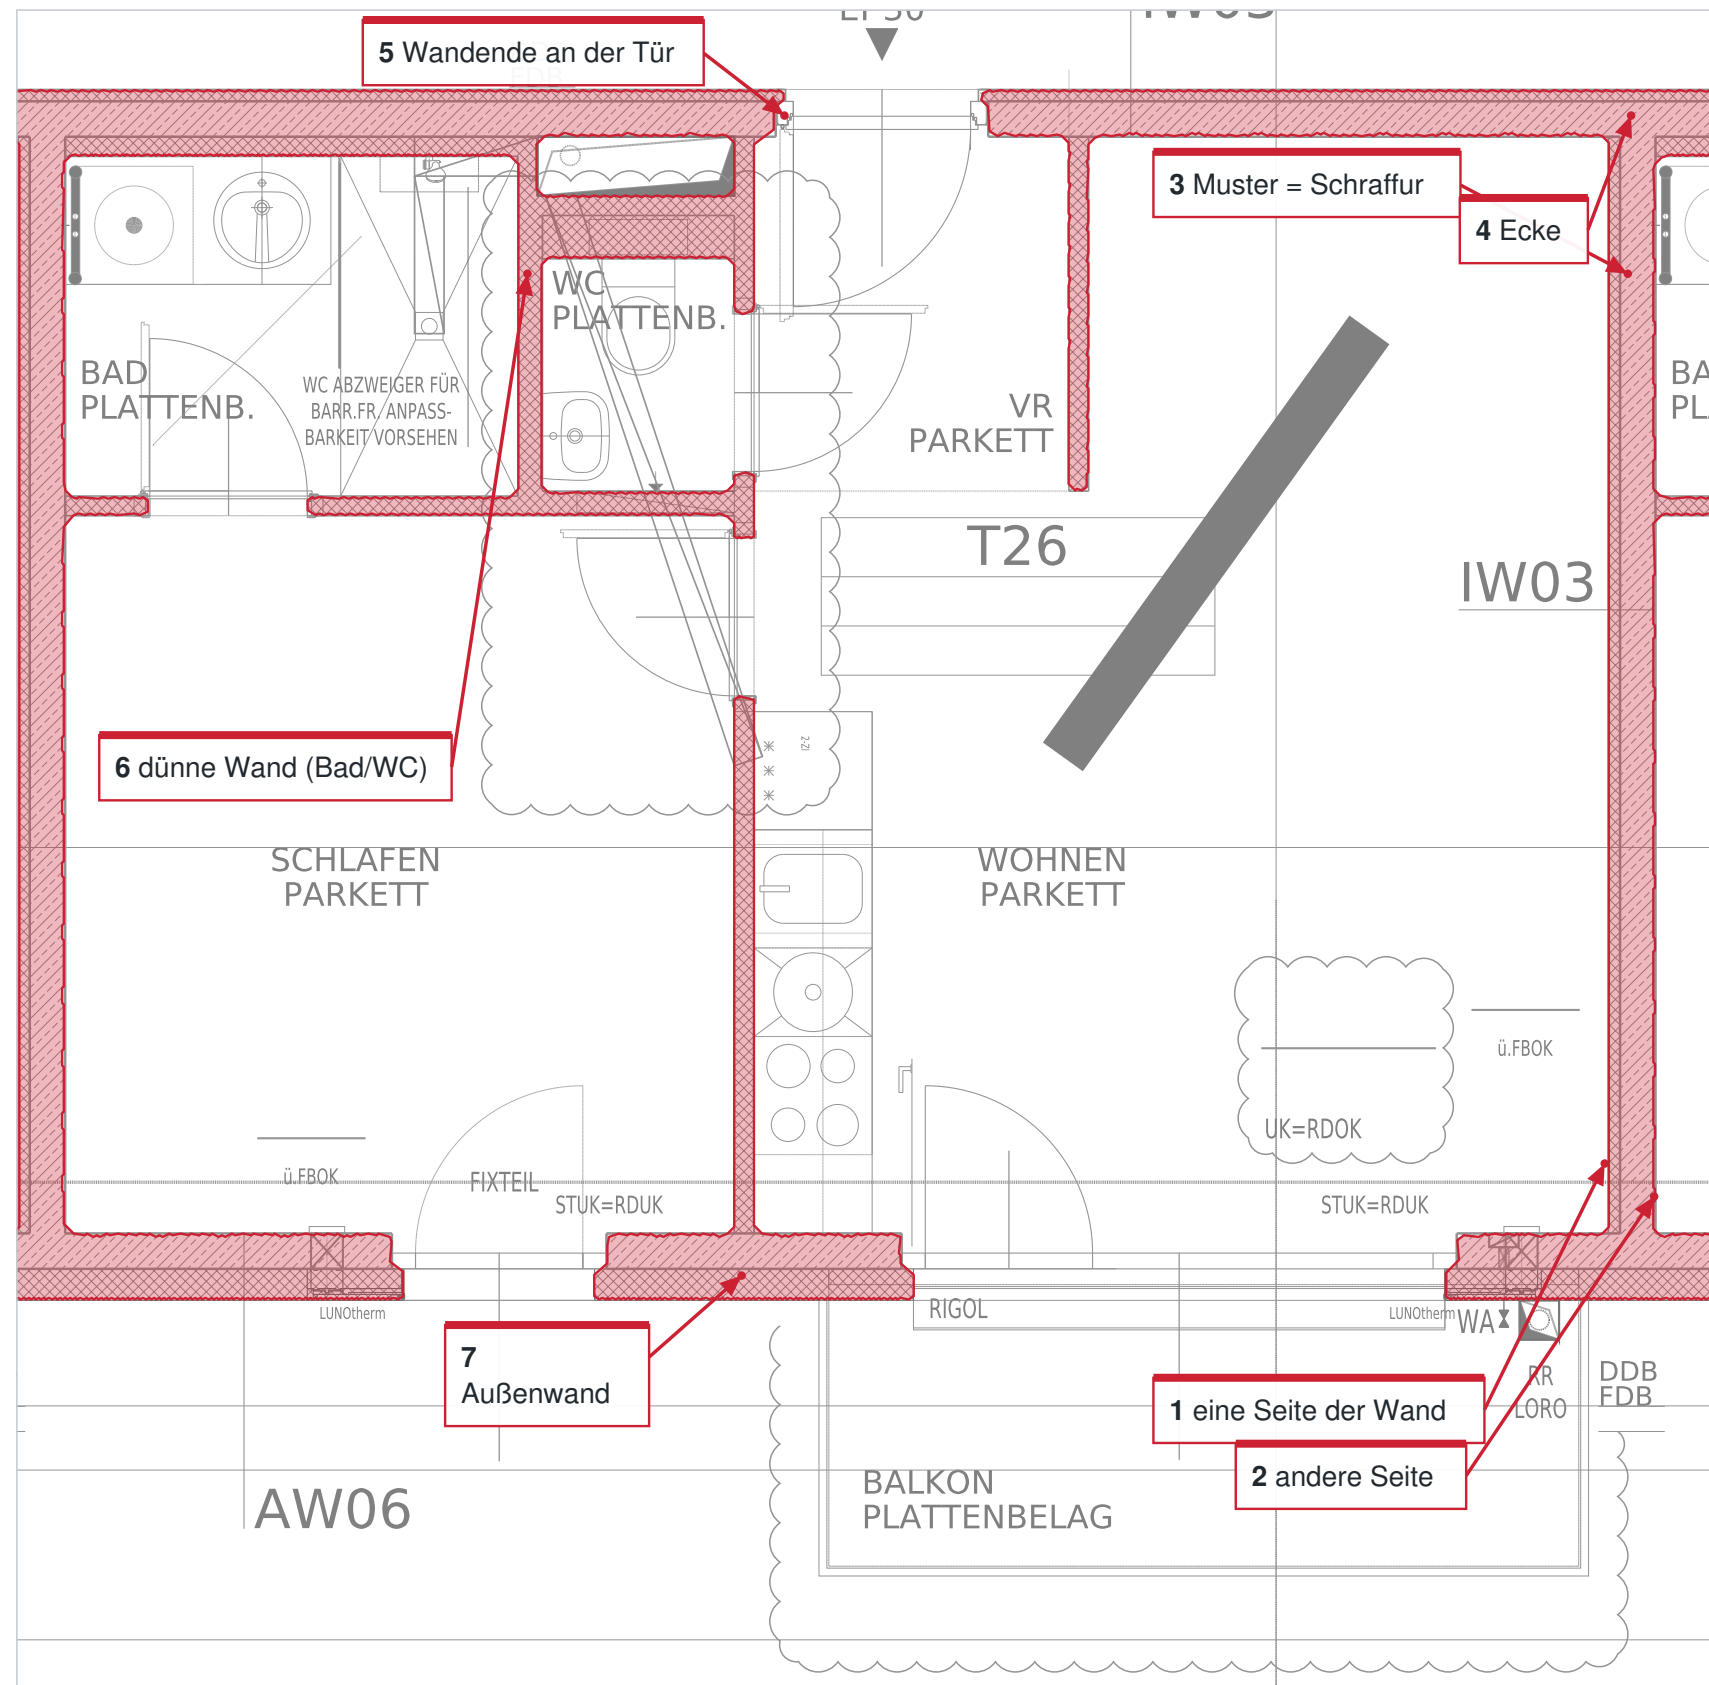

Was siehst du?

Alles, was **rot** ist, ist Wand. Die grauen Linien darunter sind das Original.

Woran erkenne ich eine Wand? (Punkte 1–3)

Schau auf die senkrechte Wand ganz rechts (zur Nachbarwohnung). Sie hat eine **linke Seite (1)** und eine **rechte Seite (2)**. Beide Linien laufen parallel, also immer im gleichen Abstand nebeneinander. Die Fläche dazwischen ist mit schrägen Strichen gefüllt (**3**). Das Muster heißt **Schraffur** und bedeutet: hier ist festes Material.

Wie läuft eine Wand weiter? (Punkt 4)

Wände knicken an **Ecken** ab. Die Markierung folgt dem Streifen um die Ecke herum.

Wo hört eine Wand auf? (Punkt 5)

Eine Wand endet, wo eine Tür oder Öffnung beginnt. Die kurze Querlinie am Ende heißt **Wandende** (die Fachleute sagen **Laibung** zur Innenseite der Öffnung).

Dicke und dünne Wände (Punkte 6 und 7)


Die Wand zwischen Bad und WC (**6**) ist dünn, die Außenwand (**7**) ist dick. **Beide** sind Wände. Auch eine dünne Wand kann man nicht durchqueren.

MERKSATZ

Eine Wand erkennst du an **zwei parallelen Linien mit Muster dazwischen**, die ohne Lücke weiterlaufen – bis zu einer Ecke, einer anderen Wand oder einer Tür.

10 | Nicht jede Wand ist gleich

Außenwand, Wohnungstrennwand und Zimmerwand haben unterschiedliche Dicken und Muster.

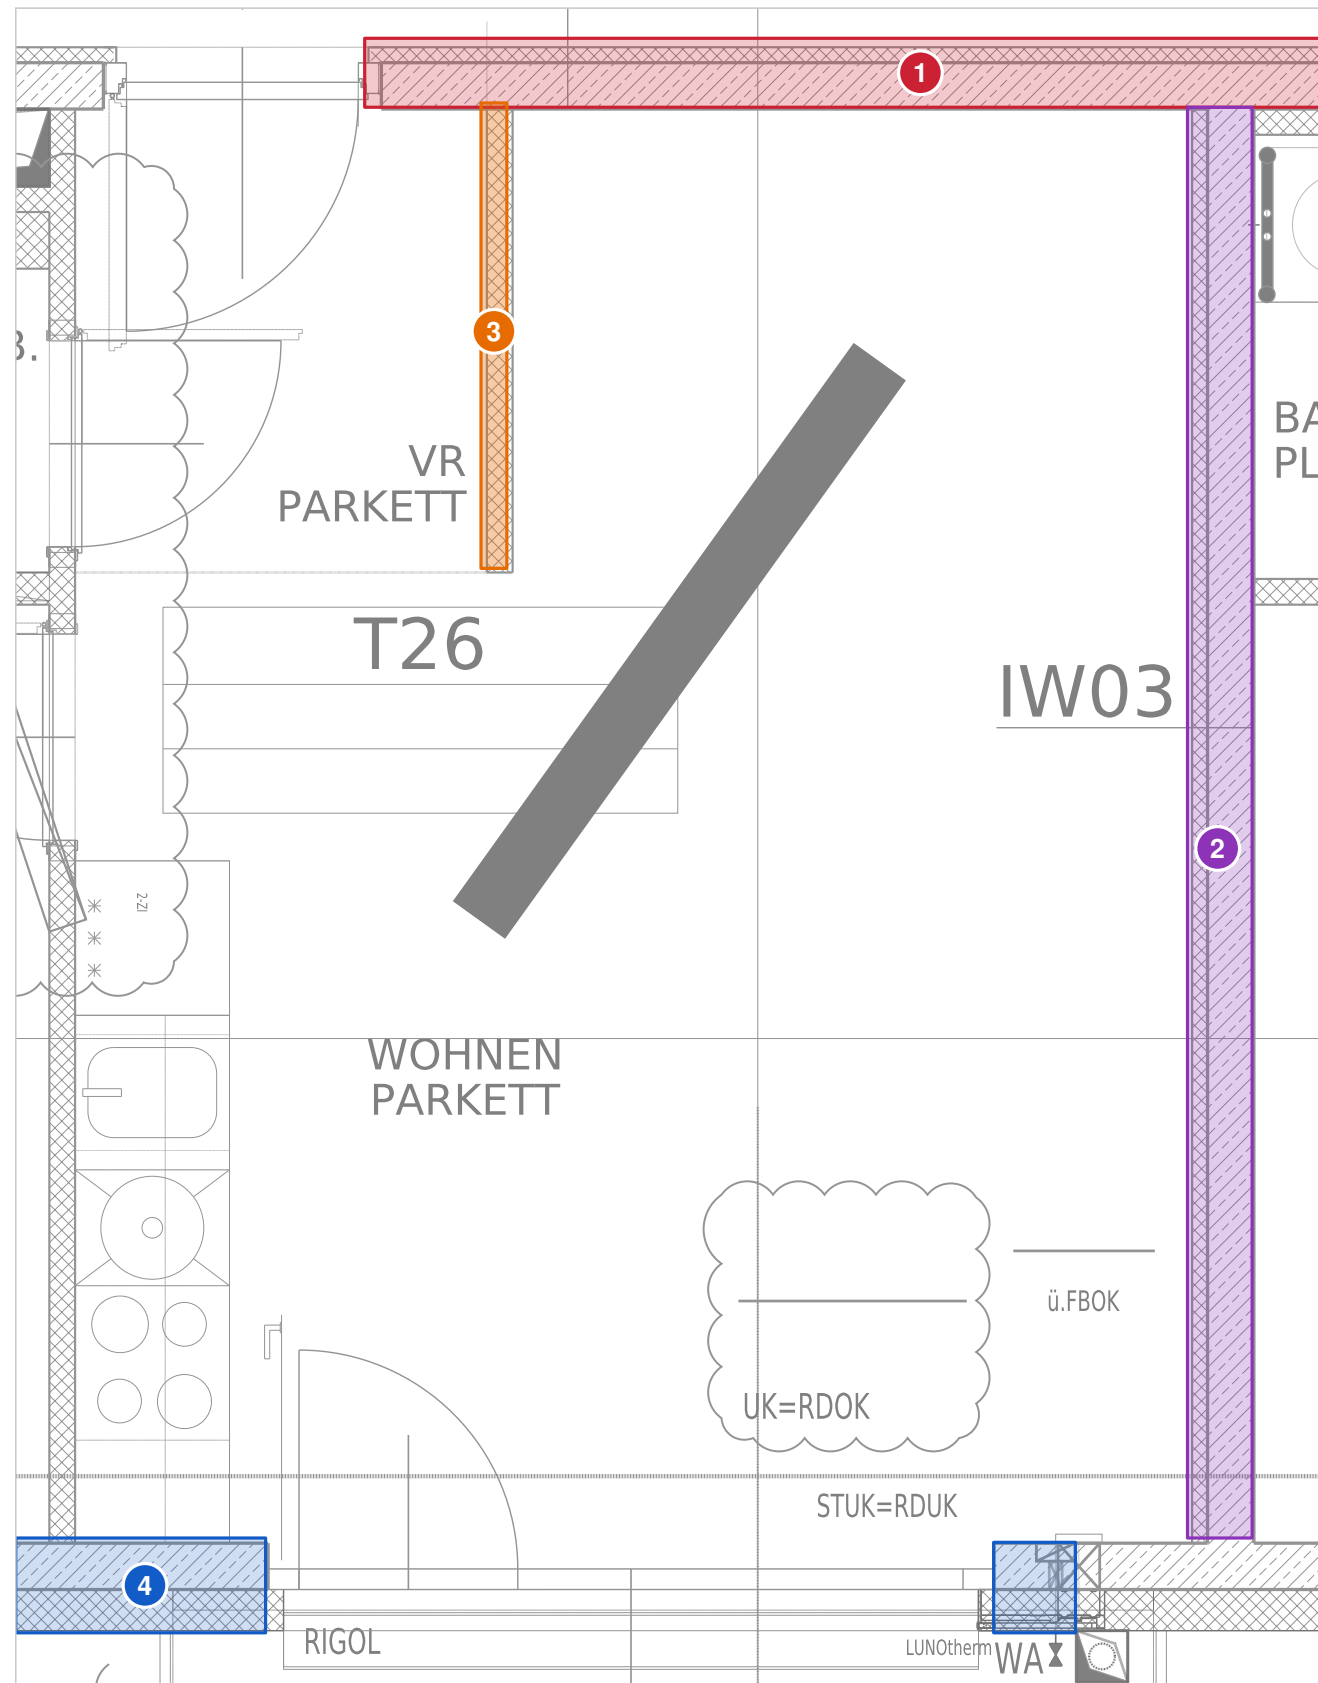

1 · Wand zum Gang (rot umrandet)

Oben trennt eine dicke Wand die Wohnung vom gemeinsamen Gang. Sie hat zwei Schichten: ein Streifen mit schrägen, gestrichelten Linien und ein Streifen mit kleinen Kreuzen. Zwei Muster = zwei Schichten = trotzdem **eine** Wand.

2 · Wohnungstrennwand (violett umrandet)

Rechts trennt eine dicke Wand die Wohnung T26 von der Nachbarwohnung T27. Solche Wände sind dick, damit man den Nachbarn nicht hört. Das Kürzel **IW03** daneben benennt diese Wandart.

3 · Zimmerwand (orange umrandet)

Zwischen Vorraum und Wohnzimmer steht eine **dünne** Wand. Sie ist nur mit einem Kreuzmuster gefüllt.

4 · Außenwand (blau umrandet)

Unten liegt die Wand zur Straße. Sie hat innen einen Streifen mit schrägen Strichen und außen einen Streifen mit Kreuzen. Die äußere Schicht ist sehr wahrscheinlich die **Wärmedämmung**: eine Schicht, die Kälte draußen hält. Im Wohnzimmer ist diese Außenwand nur noch ein kurzes Stück (rechts unten) – der Rest ist eine Glasfront (Kapitel 19).

Ehrlich gesagt

Der Plan schreibt nirgends hin, aus welchem Material jedes Muster ist. Dafür gibt es bei Architekten eine eigene Liste. Für uns reicht: **Muster zwischen zwei Linien = Wand**.

MERKSATZ

Muster und Dicke verraten die **Art** der Wand. Für die Frage „kann ich hier durch?“ ist die Antwort aber immer dieselbe: **nein**.

11 | Alle Wände im ganzen Geschoss

So sieht das Stockwerk aus, wenn man nur die Wände einfärbt.



Was siehst du?

Nur die Wände sind kräftig rot. Man erkennt sofort die **Form des Hauses**: eine Art großes „U“ mit dem Hof oben in der Mitte.

Wie liest man das?

- Die **äußerste rote Linie** rundherum ist die Außenwand. Außerhalb davon ist draußen.
- Die langen roten Streifen in der Mitte begleiten den **Gang**.
- Die kurzen Streifen dazwischen trennen die Wohnungen und die Zimmer.
- Überall, wo das rote Netz eine **Lücke** hat, kommt man von einem Raum in den nächsten – oder es ist ein Fenster.

Probier es selbst

Such dir eine Wohnung aus und fahre mit dem Finger ihre roten Wände entlang. Wo musst du „springen“? Genau dort sind ihre Türen und Fenster.


Die rote Fläche wurde aus den Mustern (Schraffuren) des Originalplans berechnet und dann mit den Linien des Plans verglichen.

MERKSATZ

Die roten Wände bilden ein Netz. Jede **Lücke** im Netz ist eine Tür, ein Durchgang oder ein Fenster.

12 | Vorsicht: Das sieht aus wie eine Wand – ist aber keine

Im Plan gibt es lange Linien und sogar einen dicken roten Balken, die gar nichts Festes bedeuten.

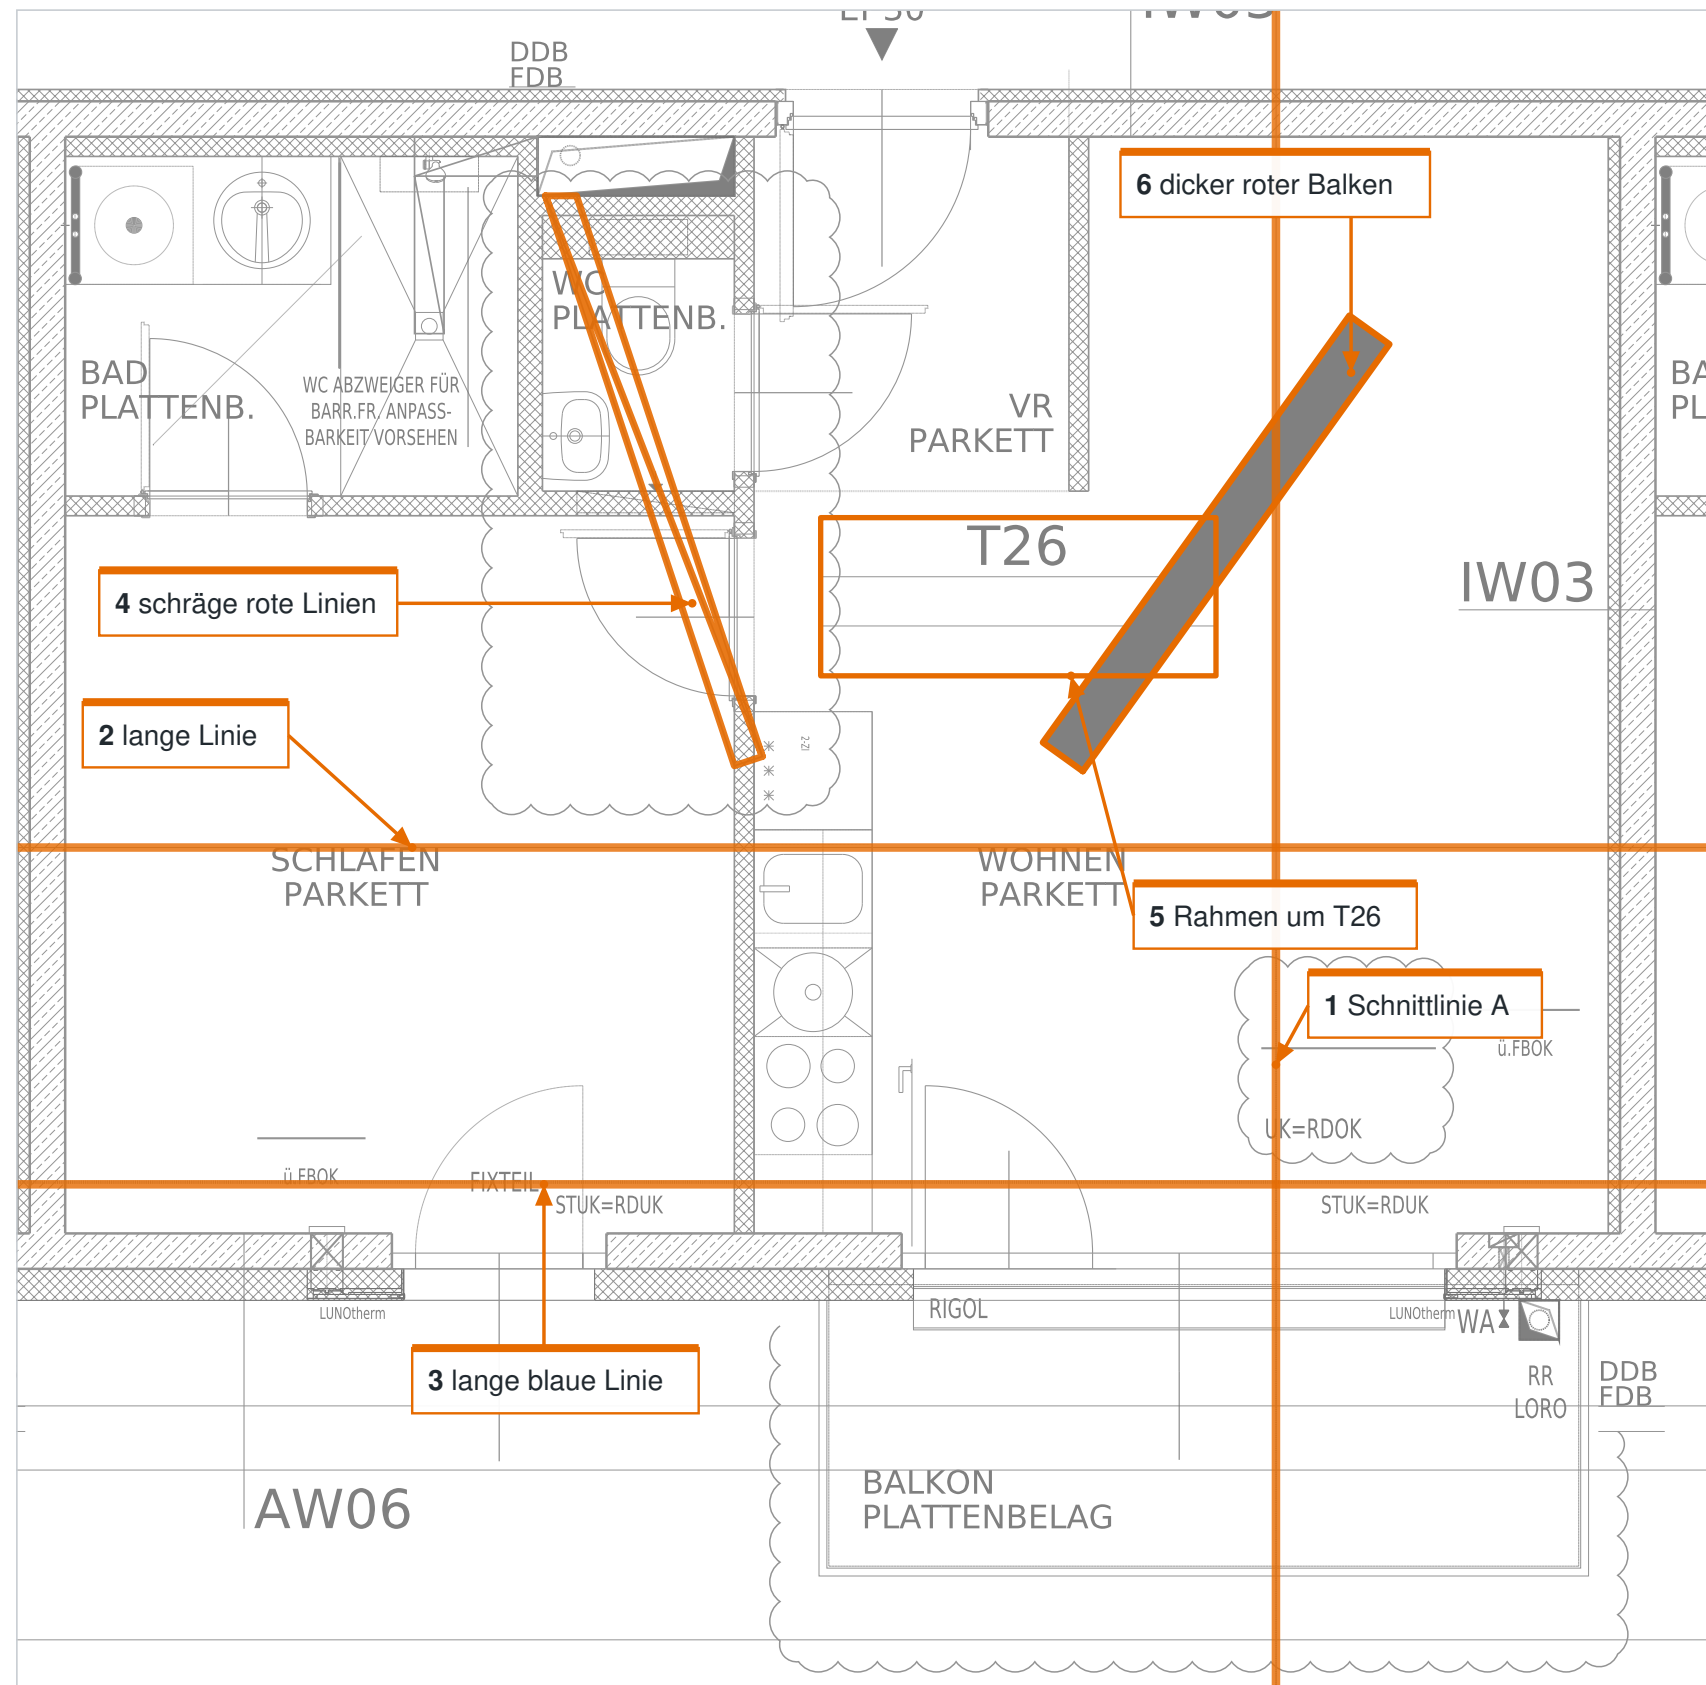

Warum ist das wichtig?

Wer nur auf „lange gerade Linie“ oder „dicker Strich“ achtet, würde hier sechs falsche Wände sehen. Keine dieser Linien ist ein Bauteil, auf das man stoßen würde.

Woran erkenne ich, dass es keine Wand ist?

- **Sie läuft durch Wände hindurch.** Eine Wand kann nicht durch eine andere Wand laufen (1, 2, 3, 4).
- **Sie ist nur eine einzige Linie** – ohne zweite Seite und ohne Muster dazwischen (1, 2, 3).
- **Sie läuft schräg durch Zimmer**, ohne Anfang an einer Wand (4).
- **Sie umrahmt Schrift** (5).
- **Sie steht schräg frei im Raum**, berührt keine Wand und hat kein Wandmuster (6).

Was sind diese Linien dann?

1 ist eine **Schnittlinie**: Sie zeigt, wo eine andere Zeichnung (ein „Schnitt“) das Haus von der Seite zeigt. **2** und **3** laufen durch alle Wohnungen und sind **Hilfslinien** der Planer. Ihre genaue Bedeutung steht nicht im Plan. **4** beginnt an einem Schacht (einem Kanal für Rohre) und ist vermutlich eine **Leitung**; beschriftet ist sie nicht. **5** ist nur der Rahmen um die Wohnungsnummer. **6**, der dicke rote Balken, steht in mehreren Wohnzimmern dieses Plans. Er ist nicht beschriftet; seine Bedeutung kennen wir nicht.

Sicher ist bei allen sechs: Man kann dort ganz normal gehen. Sie sind keine Hindernisse am Boden.

MERKSATZ

Eine echte Wand **hört an Ecken, Türen und anderen Wänden auf**. Eine Linie, die einfach durch Räume und Wände hindurchläuft, ist **keine** Wand.


13 | Was ist eine Öffnung?

Eine Öffnung ist eine Stelle, an der die Wand unterbrochen ist.



Hier fehlt ein Stück Wand: **eine
Öffnung.**

Durch eine Öffnung kann man je nach Art **hindurchgehen** (Tür, Durchgang) oder nur **hindurchschauen** (Fenster).

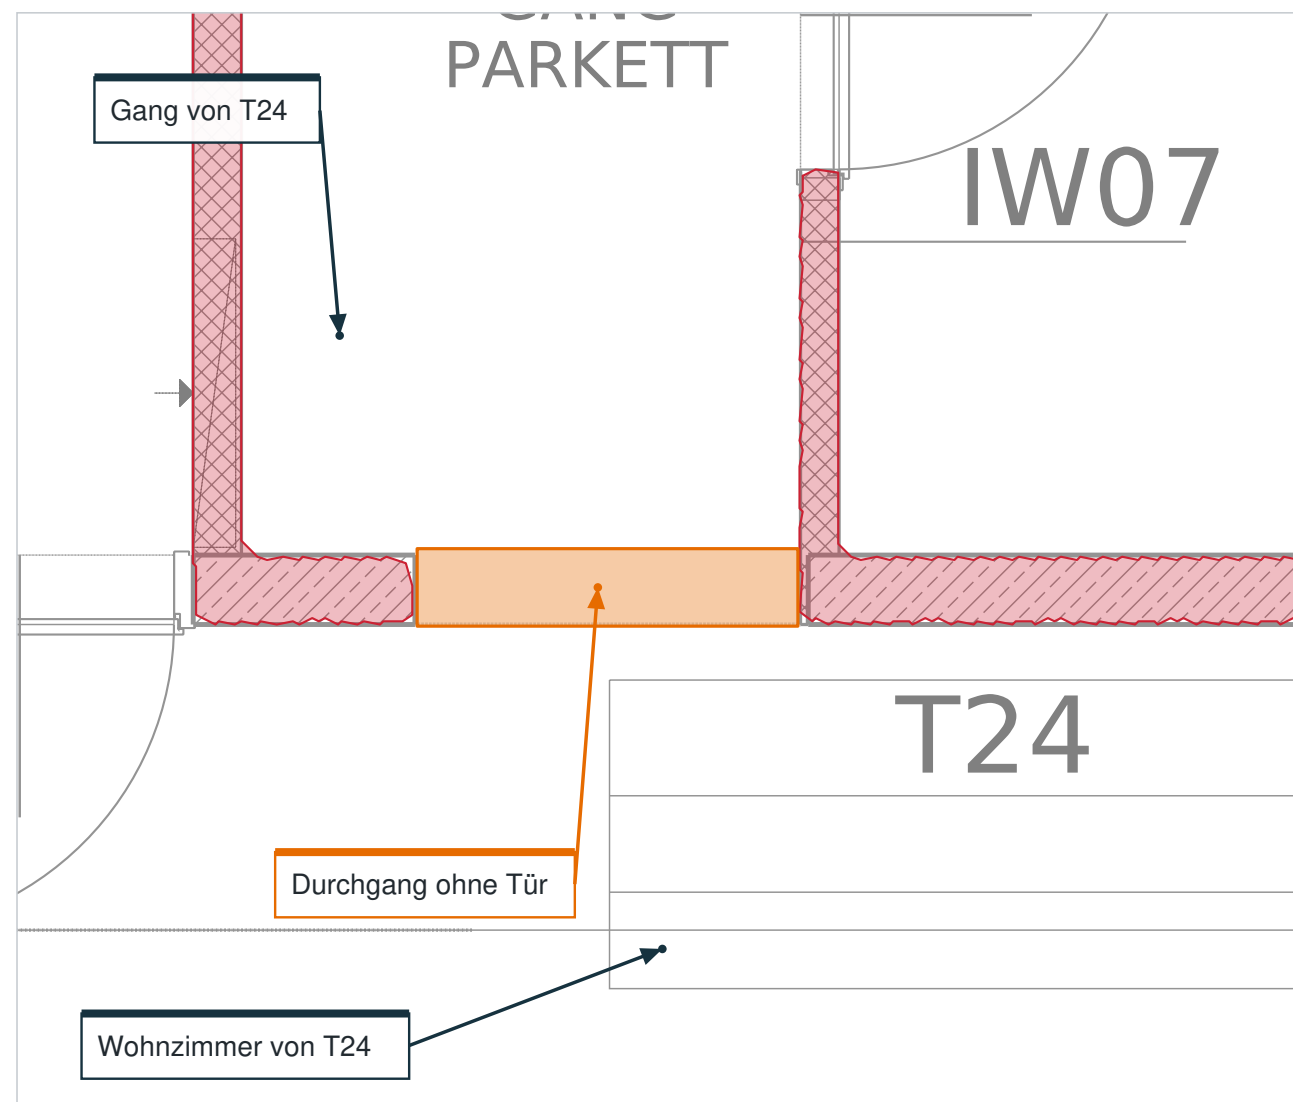

Was ist das?

Eine **Öffnung** ist ein Loch in einer Wand – eine Stelle, an der die Wand einfach aufhört und ein Stück weiter wieder anfängt.

Welche Arten gibt es?

- **Durchgang:** eine Öffnung ohne Tür. Man geht einfach hindurch.
- **Tür:** eine Öffnung, in der ein Türblatt sitzt, das man auf- und zumachen kann.
- **Fenster:** eine Öffnung mit Glas. Man kann hindurchschauen, aber normalerweise nicht hindurchgehen.

Hier im Plan (unten links)

Das Beispiel stammt aus der Wohnung **T24** (oben links im Haus). Zwischen dem schmalen Gang dieser Wohnung und ihrem Wohnzimmer hört die rote Wand auf. Die Lücke (orange) hat **kein Türblatt und keinen Bogen**. Das ist ein **Durchgang**: Man geht einfach hinüber.

Woran erkenne ich eine Öffnung?


Folge einer Wand mit dem Finger. Wenn der Streifen plötzlich aufhört und nach einer Lücke wieder anfängt, hast du eine Öffnung gefunden. Dann schaust du, was **in** der Lücke gezeichnet ist: nichts (Durchgang), ein Strich mit Bogen (Tür) oder feine Doppellinien (Fenster).

Merksatz **Offnung** = Lücke in der Wand. **Durchgang** = Öffnung, durch die man gehen kann. Eine **Tür** ist ein Durchgang, den man mit einem Türblatt schließen kann.


14 | Was ist eine Tür – und wie wird sie gezeichnet?

Eine Tür besteht im Grundriss aus drei Teilen: Öffnung, Türblatt und Bogen.

Raum B (oben) – hier hinein öffnet diese Tür

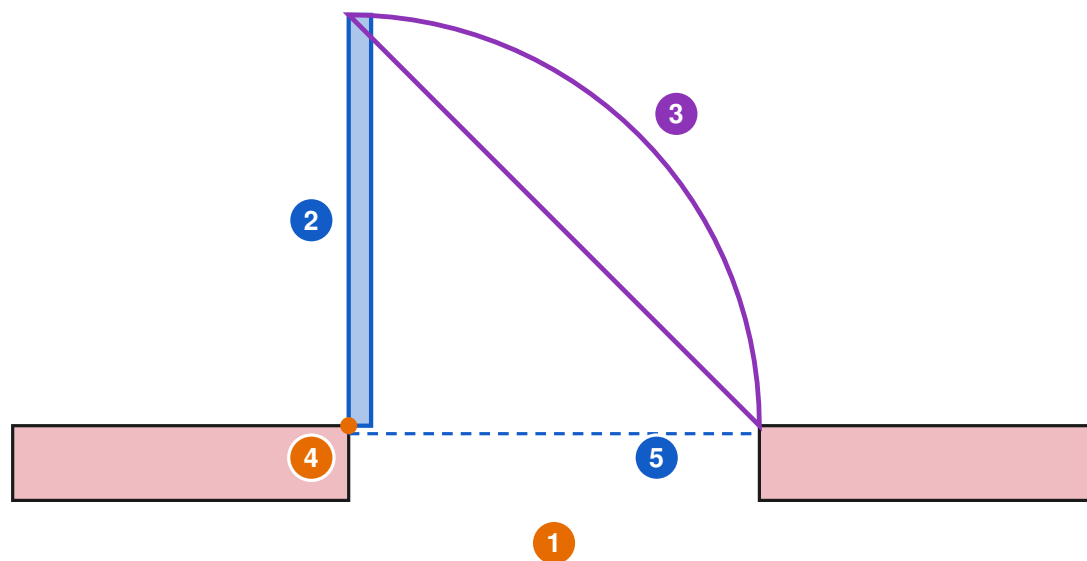

Raum A (unten)

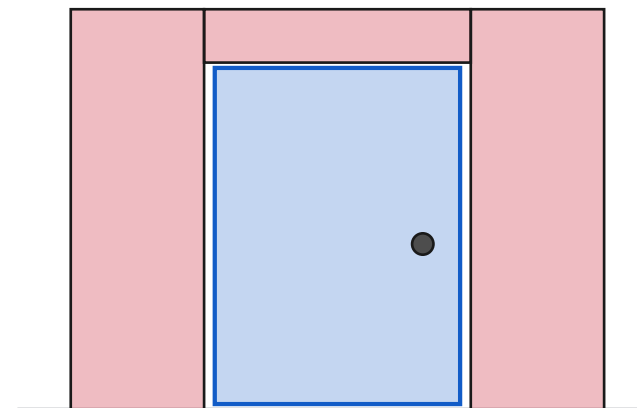

Dieselbe Tür von vorne: die Wand (rot) hat ein Loch, darin sitzt das **Türblatt** (blau) mit der Klinke.

- | | |
|----------------------|---|
| 1 Öffnung | Die Lücke in der Wand. Hier ist die Wand unterbrochen. |
| 2 Türblatt | Der Teil der Tür, den man auf- und zumacht – die „Platte“ mit der Klinke. Im Plan wird es offen gezeichnet: als gerader, schmaler Strich, der quer von der Wand absteht. |
| 3 Bogen | Ein Viertelkreis. Er zeigt den Weg, den die äußere Kante des Türblatts beim Öffnen durch die Luft nimmt. Er ist kein Gegenstand . |
| 4 Drehpunkt | Die Stelle, an der das Türblatt an der Wand befestigt ist (dort sind die Scharniere). Die Fachleute sagen Anschlag . |
| 5 Geschlossen | So liegt das Türblatt, wenn die Tür zu ist: genau in der Öffnung. Das wird im Plan meist nicht gezeichnet – hier gestrichelt zur Erklärung. |

Was ist das?

Eine **Tür** ist eine Stelle, an der man von einem Raum in einen anderen gehen kann – und die man schließen kann.

Warum sieht sie im Plan so seltsam aus?

Weil wir von oben schauen (Kapitel 02). Von oben ist ein Türblatt nur so dick wie ein Brett – also ein schmaler Strich. Damit man sieht, **dass** die Tür aufgeht und **wohin**, zeichnet man sie **offen** (im rechten Winkel zur Wand) und dazu den Bogen.

Woran erkenne ich eine Tür?

Suche **alle drei** Hinweise:

- Die Wand hat eine **Lücke**.
- An einer Seite der Lücke steht ein **gerader Strich** von der Wand ab.
- Ein **Viertelkreis** verbindet das freie Ende dieses Strichs mit der anderen Seite der Lücke.


Womit kann ich es verwechseln?

Ein Bogen allein kann auch zu einem Fensterflügel gehören (Kapitel 19). Ein Strich allein kann eine Möbelkante sein. Erst wenn Lücke, Strich und Bogen zusammenpassen, ist es sicher eine Tür.

MERKSATZ Tür = **Öffnung** in der Wand + **Türblatt** (gerader Strich) + **Bogen** (Viertelkreis). Erst alle drei zusammen sind ein sicheres Zeichen für eine Tür.

15 | Eine echte Tür im Plan: WC und Schlafzimmer

Zwei Türen im Vorraum von T26, stark vergrößert. Jeder Teil ist farbig markiert.

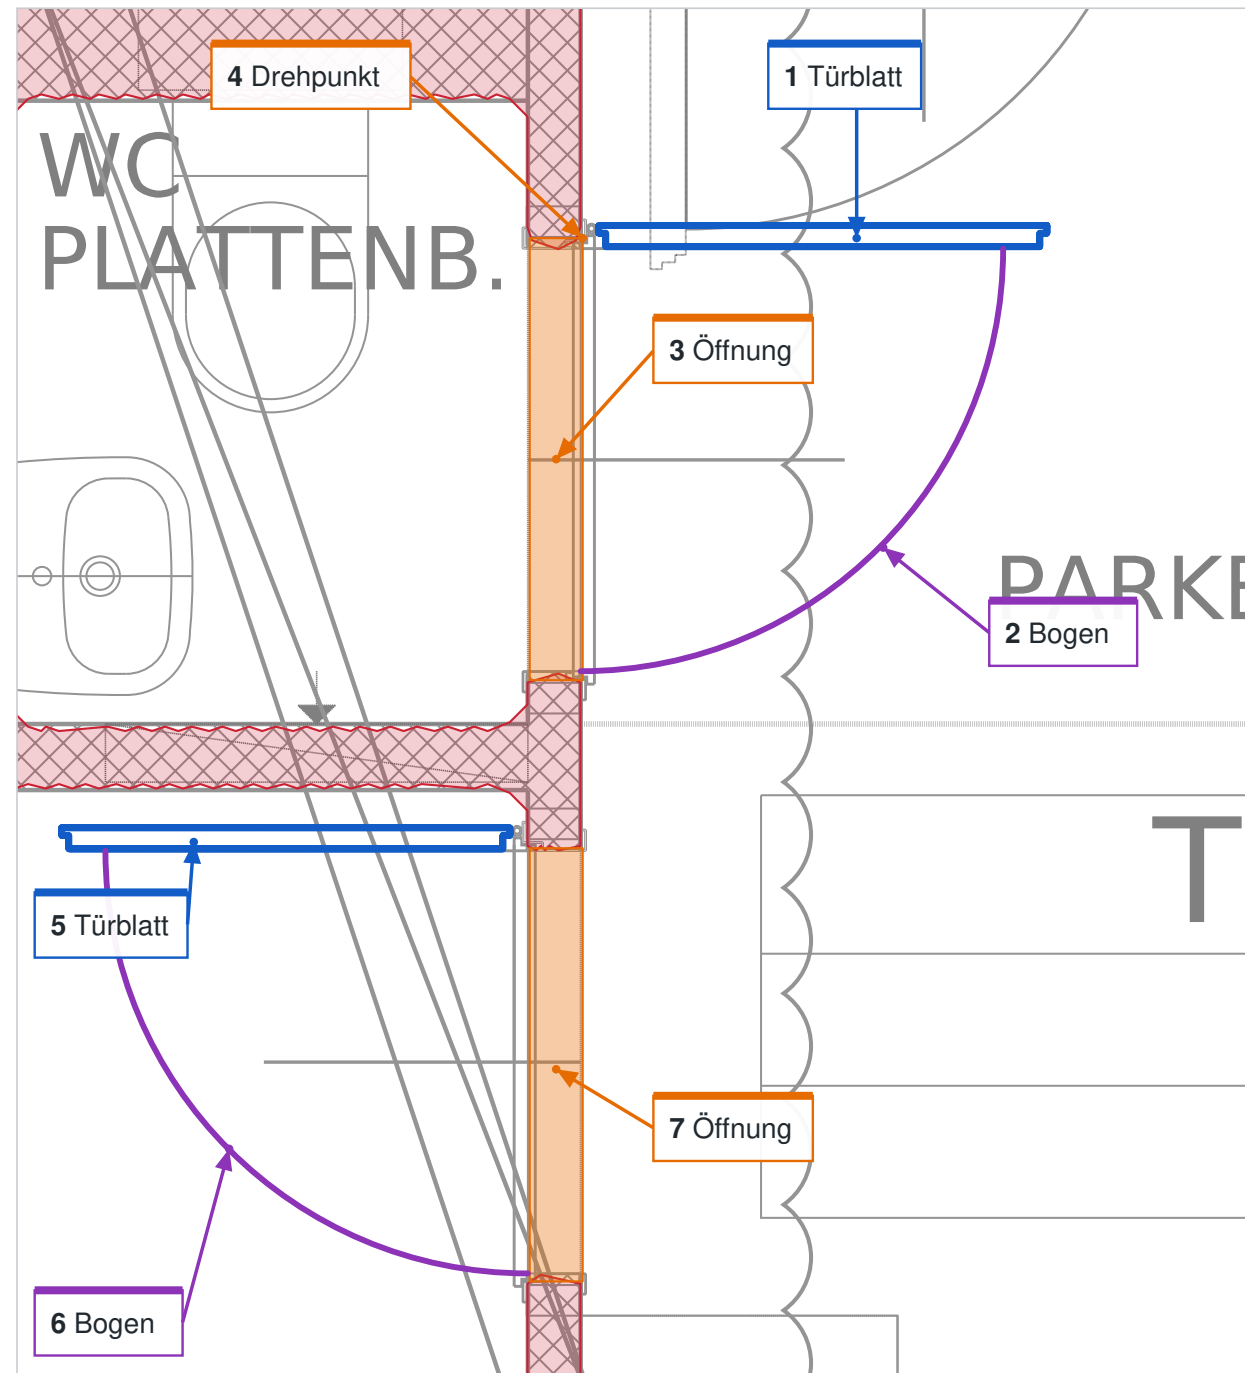

Die WC-Tür (oben, Nummern 1–4)

Wo? In der Wand zwischen WC (links) und Vorraum (rechts).

1 Türblatt: der waagrechte blaue Strich oben. Er steht von der Wand ab und ragt nach rechts in den Vorraum. Das ist die geöffnete Tür, von oben gesehen.

2 Bogen: der violette Viertelkreis. Er beginnt am freien Ende des Türblatts und endet unten an der Wand. So bewegt sich die Türkante beim Schließen.

3 Öffnung: Die rote Wand ist hier unterbrochen (orange). Genau so lang wie das Türblatt.

4 Drehpunkt: Hier ist das Türblatt an der Wand befestigt.

Die Schlafzimmertür (unten, Nummern 5–7)

Etwas weiter unten ist in **derselben** Wand noch eine Tür. Sie sieht fast gleich aus – nur ragt ihr Türblatt **nach links**, ins Schlafzimmer.

Was bedeutet das?

Aus dem Vorraum kommt man durch die obere Tür ins WC und durch die untere Tür ins Schlafzimmer.

Nicht verwechseln


- Der Bogen ist **keine Wand** und kein Teppich – man kann über diese Fläche ganz normal gehen.
- Die schrägen roten Linien daneben gehören **nicht** zur Tür (Kapitel 12).

MERKSATZ

Das Türblatt (blau) steht **quer zur Wand**. Der Bogen (violett) läuft vom freien Ende des Türblatts zurück zur Wand. Die Lücke (orange) ist die Öffnung.

16 | In welche Richtung geht eine Tür auf?

Der Bogen verrät, in welchen Raum die Tür hineinschwenkt.

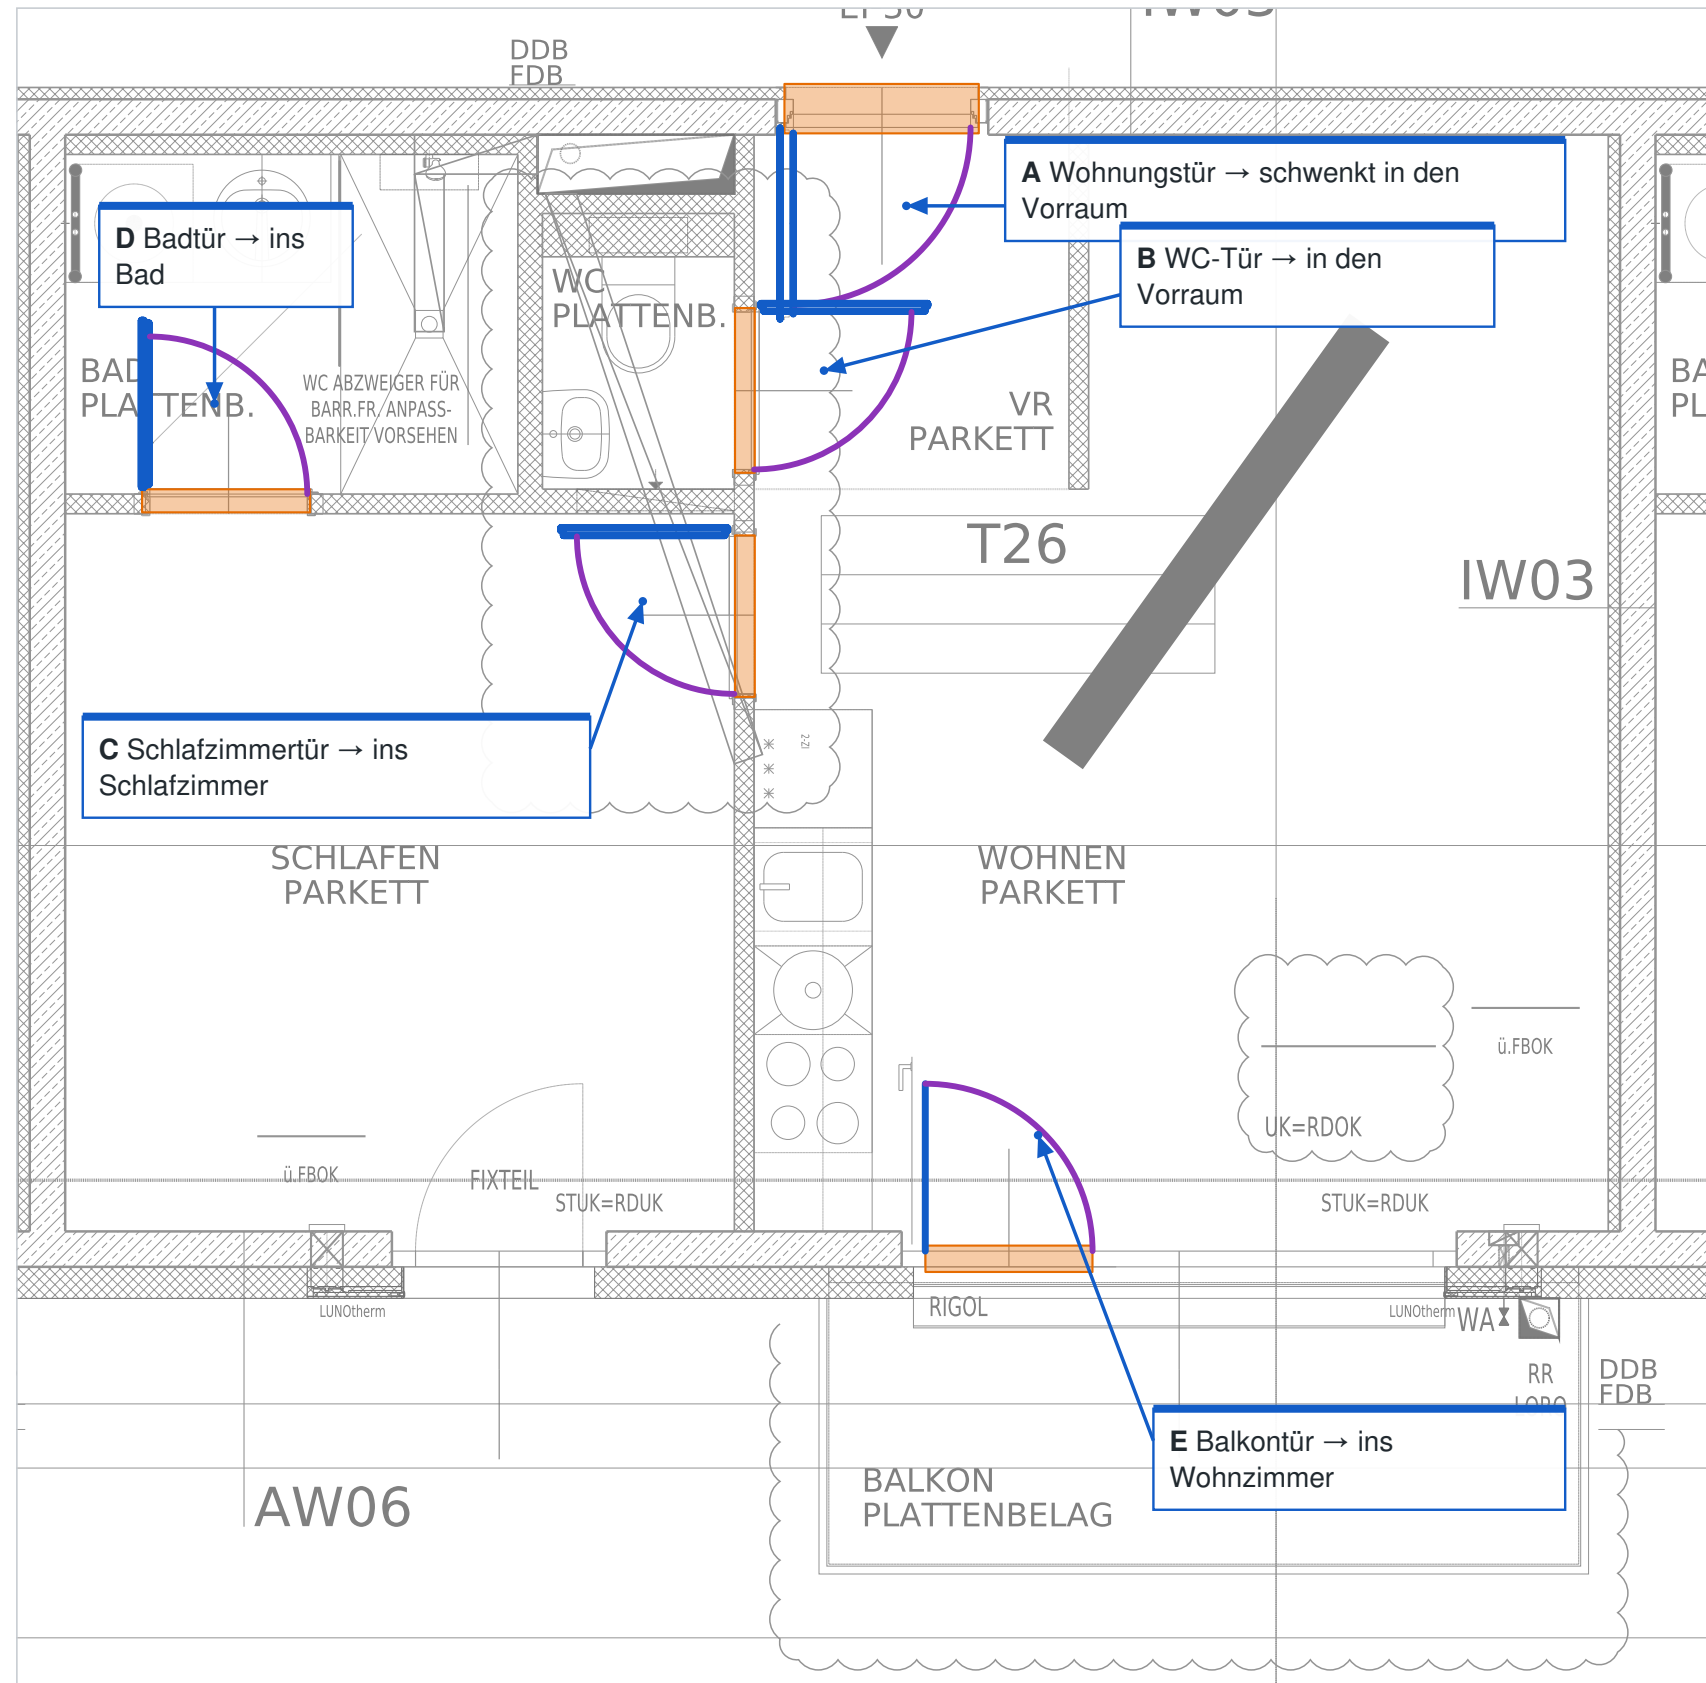

Die Regel

Schau, auf welcher Seite der Wand der **Bogen** liegt. In diesen Raum hinein geht die Tür auf. Auf der anderen Seite ist nur die Lücke zu sehen.

Alle Türen von T26

- A Wohnungstür** (oben): Der Bogen liegt im Vorraum. Man drückt die Tür vom Gang aus nach innen auf.
- B WC-Tür**: Der Bogen liegt im Vorraum, nicht im WC. Die Tür geht also **nach außen** auf. Bei kleinen WCs ist das üblich, damit innen Platz bleibt.
- C Schlafzimmertür**: Der Bogen liegt im Schlafzimmer.
- D Badtür**: Das Bad erreicht man vom Schlafzimmer aus. Der Bogen liegt im Bad.
- E Tür zum Balkon**: Sie sitzt in der Glasfront unten und schwenkt ins Wohnzimmer. Draußen liegt der Balkon.

Wo ist der Drehpunkt?

Immer dort, wo Türblatt und Bogen **nicht** zusammentreffen, also an dem Ende des Türblatts, das an der Wand sitzt.

Wozu ist das gut?


Wer den Plan liest, weiß sofort: Vor der WC-Tür im Vorraum muss Platz bleiben, sonst stößt die Tür an.

MERKSATZ

Die Tür schwenkt in den Raum, **in dem der Bogen liegt**. Dort muss man Platz lassen – dort darf nichts im Weg stehen.

17 | Die Wohnungstür von T26

Die Tür zwischen dem gemeinsamen Gang und der Wohnung hat einige Besonderheiten.

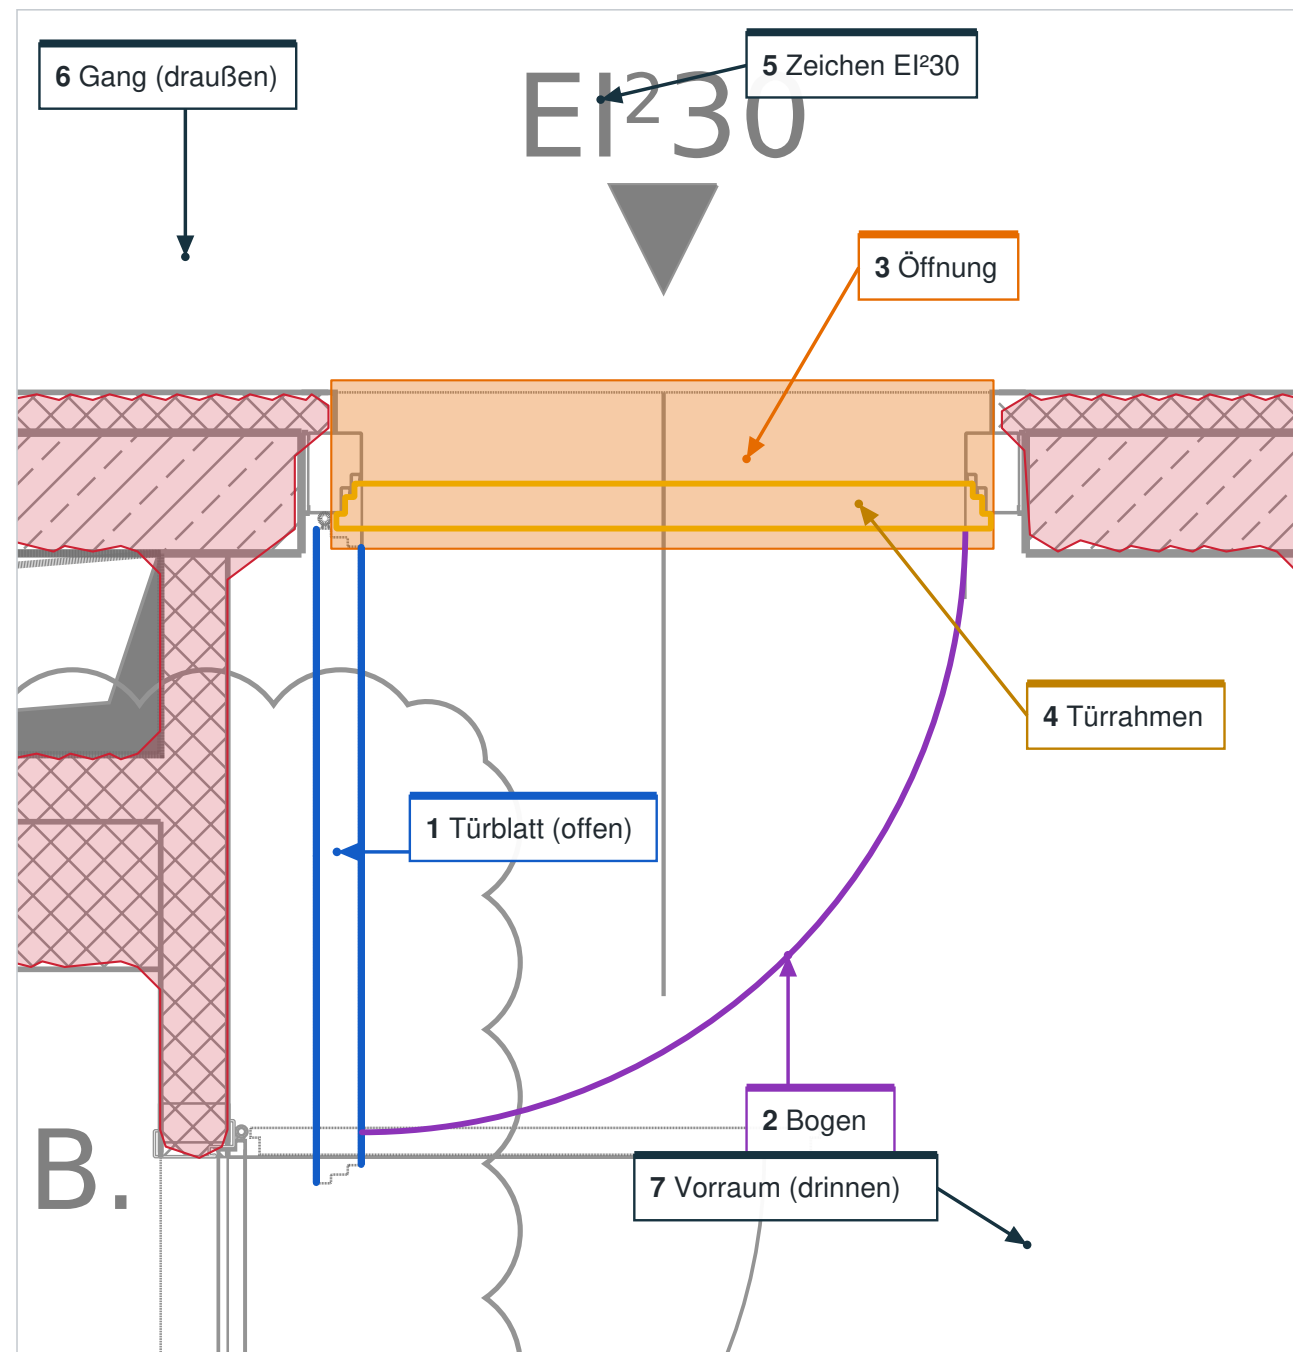

Was ist das?

Die **Wohnungstür** (auch Eingangstür) ist die Tür, durch die man die Wohnung betritt. Sie liegt in der Wand zwischen dem gemeinsamen Gang und dem Vorraum.

Die Teile

1 Türblatt: Es steht senkrecht und ist doppelt gezeichnet (zwei Linien), weil diese Tür dicker ist als eine Zimmertür. **2 Bogen:** zeigt, dass die Tür in den Vorraum hinein aufgeht. **3 Öffnung:** die Lücke in der dicken Gangwand. **4 Türrahmen:** die feine Doppellinie in der Öffnung. Der Rahmen ist fest in die Wand eingebaut; in ihm hängt das Türblatt. Die Fachleute sagen **Zarge**.

5 · Das Zeichen EI²30

Über der Tür steht **EI²30** mit einem kleinen Dreieck, das auf die Tür zeigt. Das ist eine Kennzeichnung für den **Brandschutz**: Die Tür soll im Brandfall Feuer und Hitze eine bestimmte Zeit lang aufhalten (die Zahl 30 steht üblicherweise für 30 Minuten). An manchen Türen steht **EI²30-C**; das C bedeutet üblicherweise, dass die Tür von selbst zufällt.

Woran erkenne ich eine Wohnungstür?

- Sie verbindet den **gemeinsamen Gang** (6) mit dem **Vorraum** (7) einer Wohnung.
- Sie sitzt in einer **dicken** Wand.
- Oft steht eine Brandschutz-Kennzeichnung dabei.


MERKSATZ

Die Wohnungstür erkennst du daran, dass sie **vom gemeinsamen Gang** in die Wohnung führt. Das Zeichen **EI²30** mit dem Dreieck kennzeichnet eine Brandschutztür.


18 | Was ist ein Fenster?

Ein Fenster ist eine Öffnung in der Wand, die mit Glas verschlossen ist.

Von oben (Grundriss)

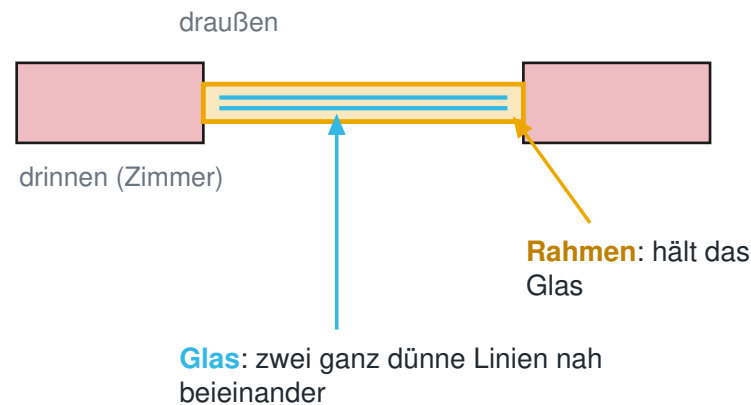

Von der Seite (Schnitt durch die Wand)

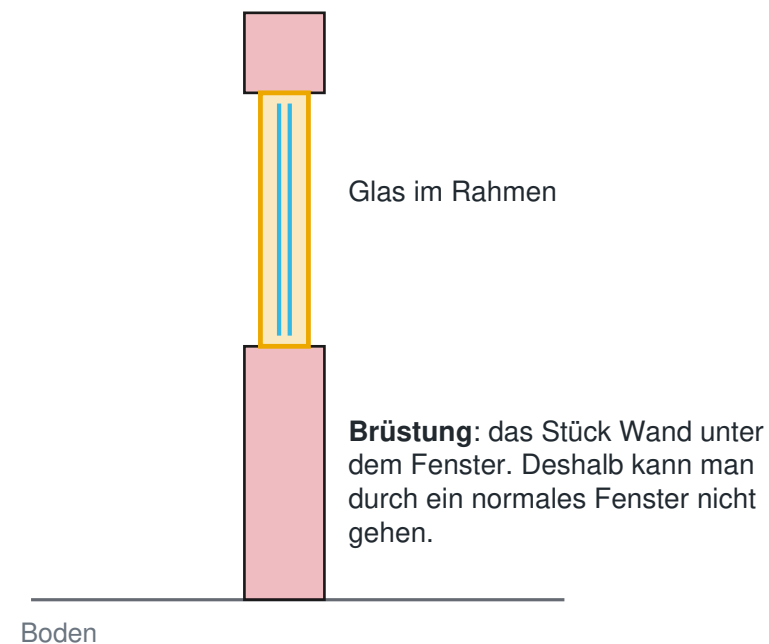

Was ist das?

Ein **Fenster** ist eine Öffnung in einer Wand – meistens in einer Außenwand –, in der eine Glasscheibe sitzt. Durch das Glas kommt Licht herein, und man kann hinausschauen.

Wie sieht es im Plan aus?

- Die Wand hat eine **Lücke** (wie bei einer Tür).
- In der Lücke liegen **feine, parallele Linien** dicht nebeneinander. Das ist der Rahmen mit dem Glas.
- Kann ein Teil geöffnet werden, zeichnet man seinen **Flügel** offen, mit einem Bogen – genau wie bei einer Tür.

Tür oder Fenster?

Bei einer Tür ist die Lücke **leer**, wenn die Tür offen ist. Bei einem Fenster liegen **Glaslinien quer in der Lücke**. Diese Linien versperren den Weg.

Was der Grundriss nicht zeigt

Wie **hoch** die Brüstung ist, sieht man von oben nicht (Kapitel 01). Ob ein Glaselement eine Fenstertür ist, erkennt man im Grundriss nur an Hinweisen – zum Beispiel daran, dass **dahinter ein Balkon** liegt (Kapitel 19).


Die Teile eines Fensters

- | | |
|-------------------|---|
| Rahmen | Das feste Gestell aus Holz, Kunststoff oder Metall, das in der Wandöffnung sitzt und das Glas hält. |
| Glas | Die durchsichtige Scheibe. Man sagt auch Verglasung – das bedeutet einfach „das Glas“. |
| Flügel | Der Teil eines Fensters, den man öffnen kann. Er dreht sich wie eine kleine Tür. |
| Fixteil | Ein Teil, den man nicht öffnen kann („fix“ = fest). |
| Brüstung | Das Stück Wand unter einem Fenster. Wegen der Brüstung kann man nicht einfach hinausgehen. |
| Fenstertür | Ein Glaselement, das bis zum Boden reicht und durch das man hinausgehen kann – zum Beispiel auf einen Balkon. Man sagt dann auch Balkontür . |

MERKSATZ Fenster = **Öffnung** in der Wand + **Rahmen** + **Glas**. Durch ein Fenster kommt Licht herein – hindurchgehen kann man normalerweise nicht.

19 | Fenster und Glasfront von T26

Links das Fenster des Schlafzimmers, rechts die große Glasfront des Wohnzimmers mit der Balkontür.

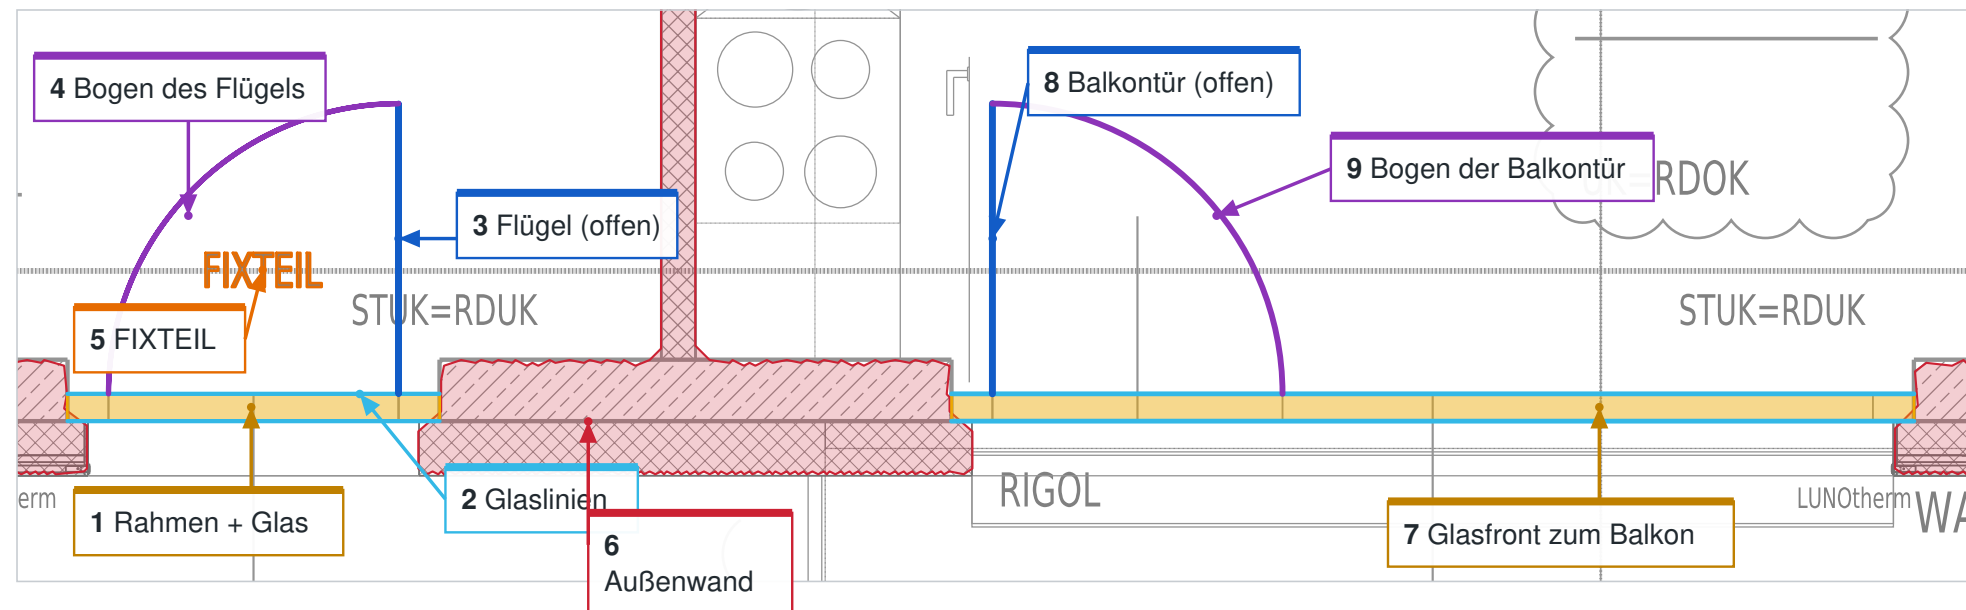

Wo? Unten in der Außenwand von T26. Das Bild ist ein schmaler Streifen: oben sind die Zimmer, unten ist draußen. Links das Schlafzimmer, in der Mitte die Küche, rechts das Wohnzimmer. Ganz unten beginnt der Balkon.

Die Lücken: Die rote Außenwand hört zweimal auf. Links ist die Lücke schmal (ein Fenster), rechts ist sie sehr breit: Dort besteht fast die ganze Wand des Wohnzimmers aus Glas.

Das Fenster im Schlafzimmer (1–5)

1 Rahmen und Glas (gelb): In der Lücke liegen zwei feine Linien sehr nah beieinander. Dort sitzt das Fenster. Rahmen und Glas sind in diesem Plan zusammen als schmales Band gezeichnet. **2 Glaslinien** (hellblau): Sie laufen quer durch die ganze Lücke – die Öffnung ist mit Glas verschlossen. **3 Flügel** (blau) und **4 Bogen** (violett): Ein Teil lässt sich öffnen und schwenkt ins Zimmer. **5 FIXTEIL**: Ein Teil ist fest. Welcher genau, zeigt der Grundriss nicht.

Die Glasfront im Wohnzimmer (7–9)

7: Im Wohnzimmer ist die Außenwand fast auf ganzer Breite durch ein Glaselement ersetzt – eine **Glasfront**. Auch hier: zwei feine Linien quer durch die Lücke.

8, 9: Links in der Glasfront ist ein Flügel offen gezeichnet, mit einem Bogen. Hier ist er im Original **genauso gezeichnet wie die Türen** der Wohnung, und **dahinter liegt der Balkon**. Deshalb ist das eine **Balkontür**: Durch sie geht man hinaus.

Der übrige Teil der Glasfront zeigt keinen Flügel und keinen Bogen. Dort ist das Glas also vermutlich fest.

Ehrlich gesagt


Beim Schlafzimmerfenster liegt draußen kein Balkon. Ob es bis zum Boden reicht, zeigt der Grundriss nicht – ein Weg nach draußen ist es jedenfalls nicht.

MERKSATZ

Ein Fenster erkennst du an der **Lücke in der Außenwand** und den **feinen Doppellinien quer darin** (gelb). Liegt dahinter ein Balkon und hat das Glas einen Türbogen, ist es eine **Balkontür**.

20 | Glas erkennen

Glas ist durchsichtig – im Plan aber ist es eine feste Grenze.

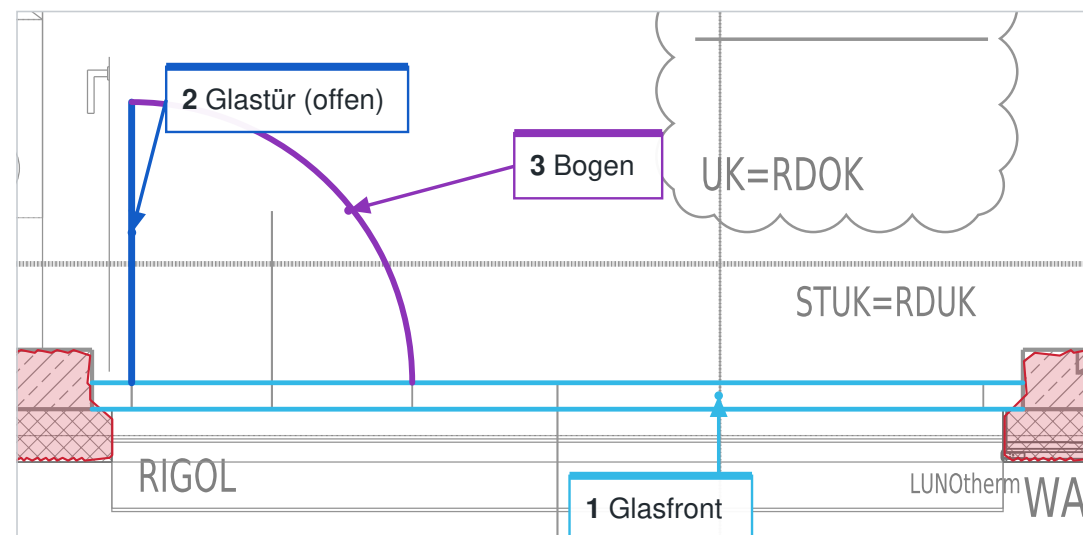

Was ist Glas?

Glas ist ein hartes, **durchsichtiges** Material. Fenster, Glastüren und manche Duschwände bestehen daraus. Das Wort **Verglasung** bedeutet einfach: „Stelle, an der Glas eingebaut ist“.

Wie sieht Glas im Plan aus?

Eine Glasscheibe ist nur wenige Millimeter dick. Von oben ist sie deshalb nur eine **sehr dünne Linie**. Oft wird das Glas zusammen mit seinem Rahmen als **feine Doppellinie** gezeichnet.

Woran erkenne ich Glas?

- sehr feine Linie(n), **ohne Muster** dazwischen (eine Wand hätte ein Muster),
- sitzt in einer Lücke der Wand oder bildet selbst eine dünne Trennwand,
- oft steht ein Hinweis dabei, etwa **FIXTEIL**.

Glas ist eine Grenze

Auch wenn man hindurchsehen kann: Wo Glas ist, kommt man **nicht** durch. Hindurch geht man nur dort, wo eine Tür in der Glaswand sitzt (erkennbar am Bogen).

Nicht verwechseln

Eine einzelne dünne Linie kann auch eine Möbelkante oder eine Hilfslinie sein. Glas erkennst du an der **Lage**: in einer Wandöffnung oder als Trennung zwischen zwei Bereichen.

Links: die Glasfront des Wohnzimmers von T26 (unten in der Wohnung). Die Außenwand ist hier durch Glas ersetzt (1): zwei feine Linien ganz nah beieinander. Links darin sitzt eine **Glastür** (2), mit der man auf den Balkon hinausgeht. Ihr Bogen (3) liegt im Wohnzimmer.

Rechts: das Bad von T26. Zwischen Waschbecken und Dusche steht eine einzelne dünne Linie (4). So werden Duschwände gezeichnet, die oft aus Glas sind. Der Plan schreibt das Material nicht dazu.

MERKSATZ

Glas zeichnet man als **ganz dünne Linie** oder **feine Doppellinie**. Durch Glas sieht man hindurch, aber man kann **nicht** hindurchgehen – nur dort, wo eine Tür darin sitzt.

The diagram illustrates the construction of a balcony with the following components and labels:

- 1 Boden des Balkons (begehrbar)**: The balcony floor surface, shown as a green layer.
- 2 Glasfront**: The glass railing or front edge of the balcony.
- 3 Balkontür**: The balcony door, shown as a blue vertical element.
- 4 RIGOL = Wasserrinne**: A drainage channel (grate) located beneath the floor surface.
- 5 Rand mit Geländer / Brüstung**: The edge of the balcony with a railing or balustrade.
- 6 Außenwand**: The exterior wall of the building, shown as a red hatched area.
- 7 RR = Regenrohr**: A rain pipe or downspout, shown as a vertical pipe with a circular outlet.
- 8 Wolke**: A cloud, shown as a white area at the bottom left.

Additional labels and materials shown in the diagram include:

- BALKON PLATTENBELAG**: Balcony slab surface covering.
- RIGOL**: Drainage channel.
- UK=RDOK**: Thermal insulation layer.
- STUK=RDUK**: Plaster or render layer.
- LUNOtherm**: Thermal insulation material.
- WAX**: Wax or waterproofing material.
- RR LORO**: Rain pipe with a specific outlet type.
- DDB FDB**: Drainage and floor construction details.
- ü.FBOK**: Upper floor construction.

Ein Balkon hängt **vor** der Hauswand. Eine **Loggia** liegt **in** der Hauslinie und hat Wände an den Seiten. Im 2. Obergeschoss hat nur die Wohnung **T25** (links unten) eine Loggia.

23 / 39

The floor plan shows a 65m² apartment with the following rooms and features:

- 6 Gang: begehbar** (Entrance hallway)
- 4 auch unter dem Türbogen ist Boden** (Floor also under the door arch)
- VR PARKETT** (Living room parquet)
- T26** (Living room area)
- IW03** (Living room area)
- WOHNEN PARKETT** (Living room parquet)
- 2 weiß: Küche – dort steht man nicht** (White kitchen – one does not stand there)
- UK=RDOK** (Kitchen unit)
- STUK=RDOK** (Kitchen unit)
- RIGOL** (Drainage)
- LUNOtherm** (Thermal insulation)
- RR LORO** (Door lock)
- DDB FDB** (Double door frame)
- BALKON PLATTENBELAG** (Balcony slab covering)
- 5 Balkon: draußen, aber begehbar** (Balcony: outside, but accessible)
- AW06** (Balcony area)
- SCHLAFEN PARKETT** (Bedroom parquet)
- 1 freier Boden im Schlafzimmer** (Free floor in the bedroom)
- ü.FBOK** (Floor board)
- FIXTEIL** (Fixed part)
- STUK=RDOK** (Kitchen unit)
- WC PLATTENB.** (Toilet slab)
- WC ABZWEIGER FÜR BARR.FR. ANPASS-BARKEIT VORSEHEN** (Toilet branch for barrier-free adaptation)
- BAD PLATTENB.** (Bathroom slab)
- DDB FDB** (Double door frame)

... du bist ganz klein und läufst auf dem Plan herum. Überall, wo du stehen kannst, ohne gegen etwas zu stoßen, ist es **grün**. Das nennt man **begehbare Fläche**: die Fläche, auf der man gehen kann.

- der freie Boden in allen Zimmern (1),
- die Fläche, über die eine Tür schwenkt (4) – der Bogen ist ja kein Gegenstand,
- der Balkon (5), obwohl er draußen liegt,
- der gemeinsame Gang (6).

- **Wände** (rot) – dort ist festes Material.
- **Einrichtung** (weiß gelassen): Küchenzeile (2), Dusche und Waschbecken (3), WC-Schale. Auf einer Küchenarbeitsplatte oder in einem Waschbecken läuft niemand herum.


Zwei grüne Flächen sind verbunden, wenn zwischen ihnen eine **Tür** oder ein **Durchgang** liegt. So kannst du vom Gang über den Vorraum und das Wohnzimmer bis auf den Balkon gehen.

Die grüne Fläche wurde aus den Linien des Plans berechnet: freie Stellen zwischen Wänden, Einrichtung und Glas.

Begehrbar heißt: Dort ist freier Boden. Wände, Möbel, Küche, Dusche und Waschbecken gehören **nicht** dazu.

23 | Was ist nicht begehbar?

Orange sind alle Dinge, die im Raum stehen und im Weg sind.

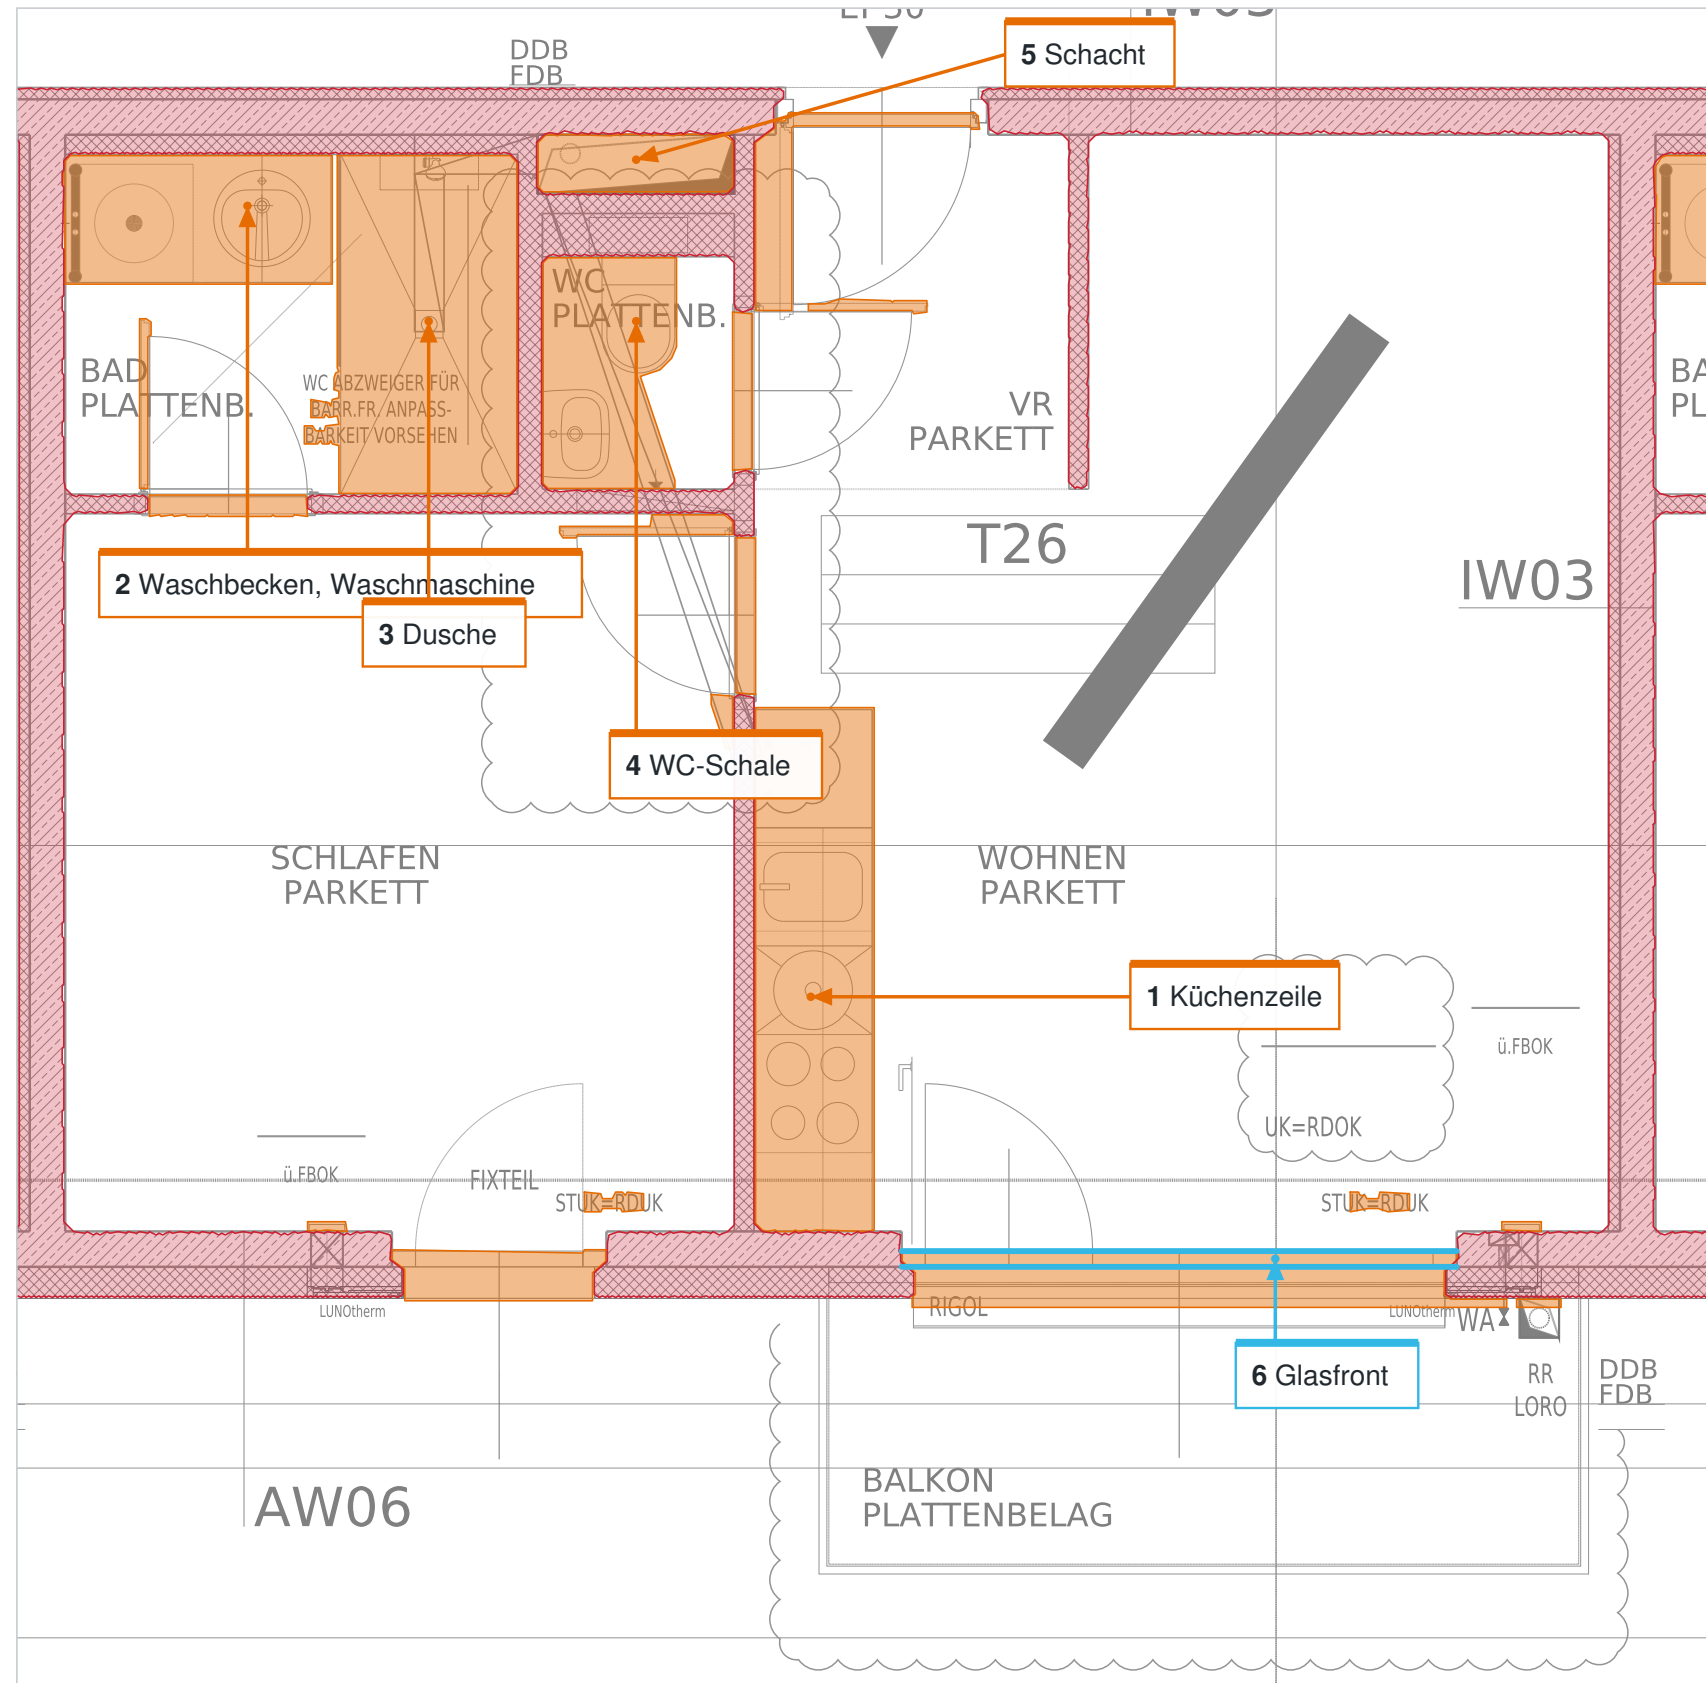

Warum ist das wichtig?

Wer wissen will, wo man gehen kann, muss auch wissen, **wo man nicht gehen kann**. Das sind nicht nur Wände.

Die Hindernisse in T26

- 1 Küchenzeile:** eine lange Reihe aus Schränken mit Arbeitsplatte, Herd und Spüle.
- 2 Waschbecken** und **Waschmaschine** im Bad.
- 3 Dusche.** In einer Dusche kann man zwar stehen – aber sie ist kein Weg, um irgendwohin zu gehen.
- 4 WC-Schale** (die Toilette) und das kleine Handwaschbecken im WC.
- 5 Schacht:** ein senkrechter Kanal in der Wand, in dem Rohre und Leitungen durch alle Stockwerke laufen. Er ist ummauert und von außen nicht betretbar.
- 6 Glasfront:** man sieht hindurch, geht aber nicht hindurch – nur durch die Balkontür darin.

Woran erkenne ich Einrichtung?

Einrichtung wird mit **dünnen Linien** gezeichnet und bildet **kleine, geschlossene Formen**: Rechtecke, Kreise, Ovale. Wände dagegen sind breite Streifen mit Muster.


Orange wurde berechnet: alles innerhalb des Hauses, das weder Wand noch freier Boden ist.

MERKSATZ

Nicht begehbar ist alles, was **fest im Raum steht**: Wände, Küche, Bad- und WC-Einrichtung, Schächte. Glas ist auch eine Grenze.

24 | Bad und WC: Was ist was?

Von oben gesehen haben Waschbecken, Dusche und Toilette typische Formen.

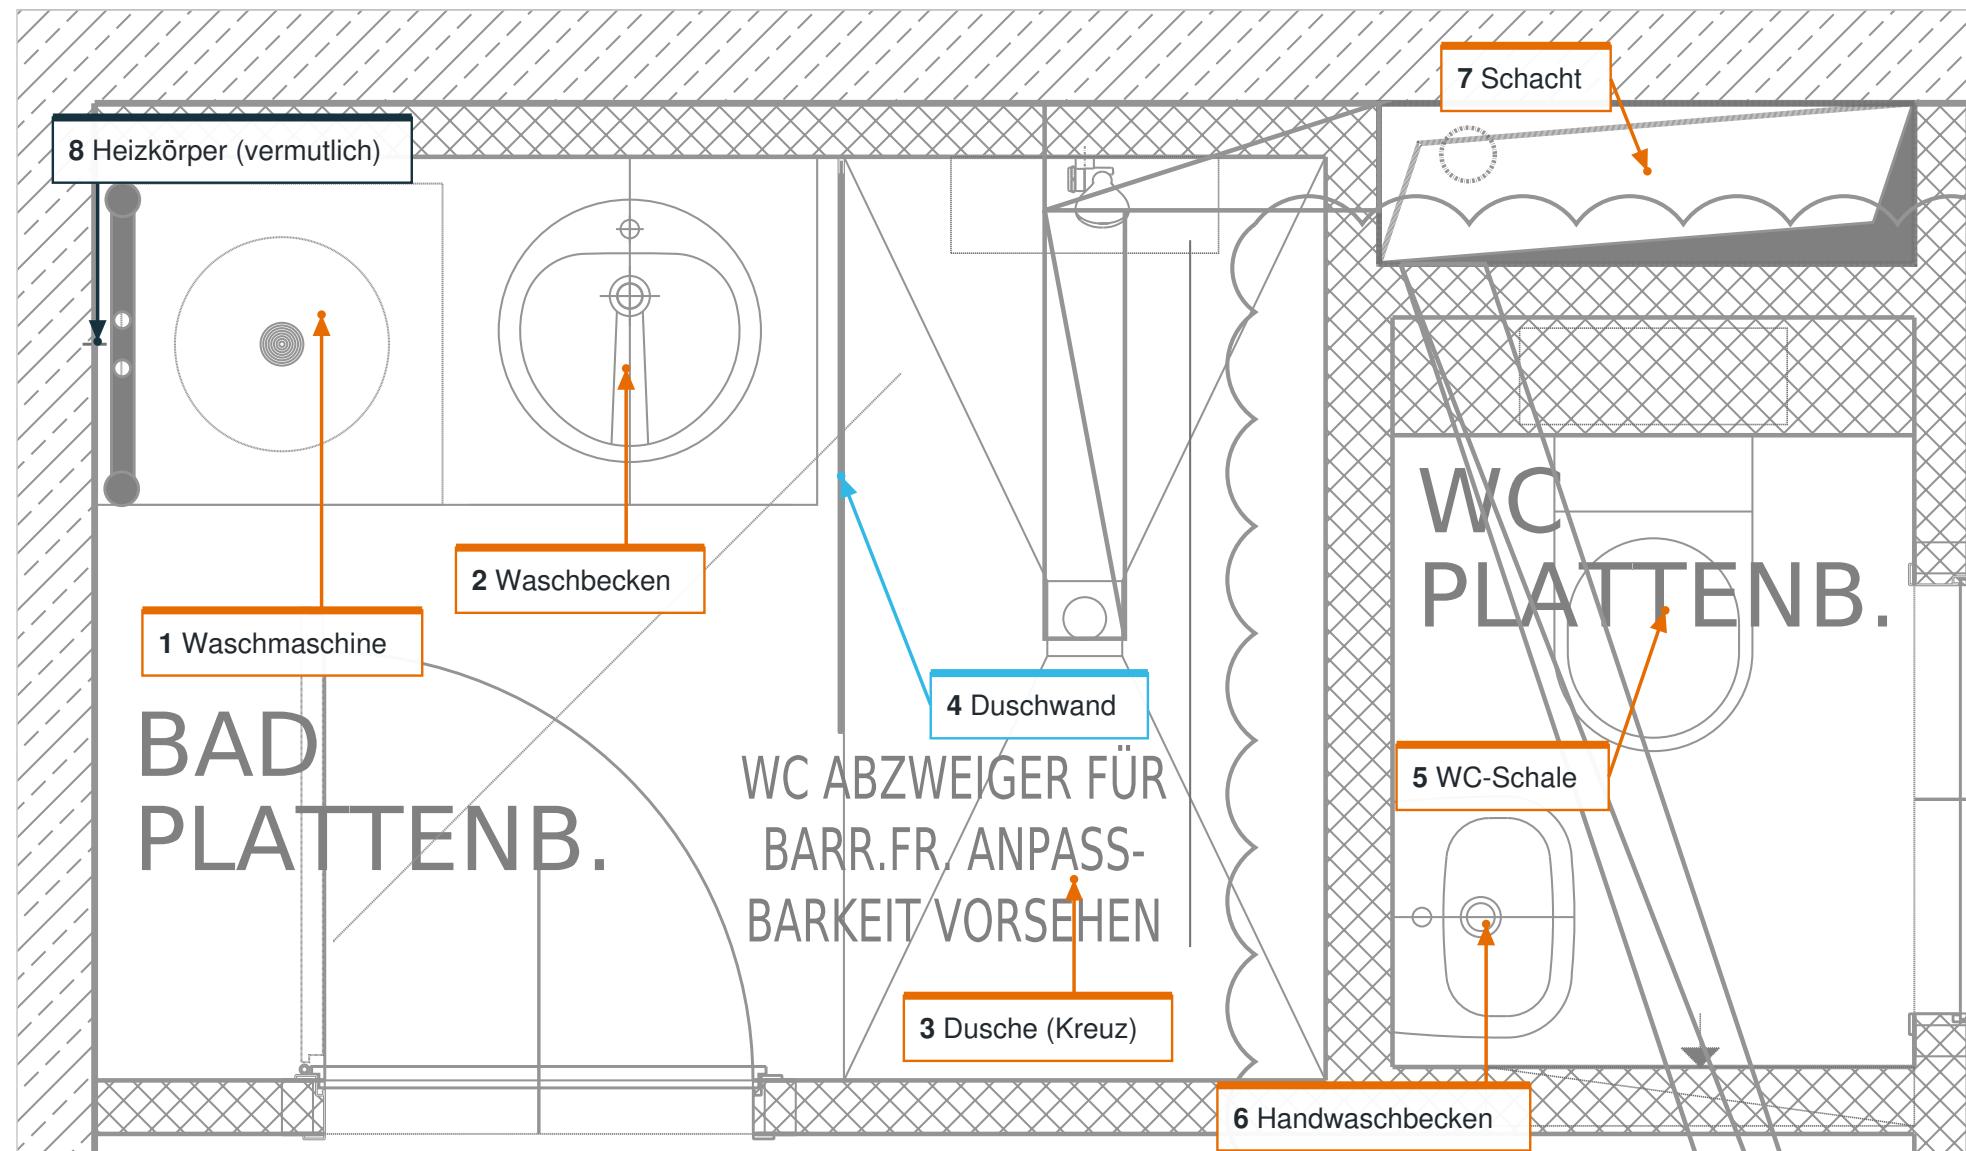

Das Bad (links)

1 Waschmaschine: ein Quadrat mit einem großen Kreis (der Trommel). **2 Waschbecken:** ein Rechteck mit einem runden Becken und einem kleinen Kreis für den Abfluss. **3 Dusche:** ein Rechteck mit zwei schrägen Linien, die sich kreuzen. So zeichnet man eine Duschfläche. **4 Duschwand:** die einzelne dünne Linie zwischen Waschbecken und Dusche – sie hält das Wasser in der Dusche.

8: Der dunkle Balken an der linken Wand ist vermutlich ein Heizkörper (zum Beispiel für Handtücher). Der Plan beschriftet ihn nicht.

Das WC (rechts)

5 WC-Schale: ein Oval – die Toilette von oben. **6 Handwaschbecken:** ein kleines Becken. **7 Schacht:** der Kasten mit dem dunklen Dreieck oben ist ein Schacht für die Rohre.

Der Hinweis in der Mitte

„WC ABZWEIGER FÜR BARR.FR. ANPASSBARKEIT VORSEHEN“ ist eine Notiz für die Bauleute: Man soll einen Rohranschluss vorbereiten, damit man das Bad später **barrierefrei** umbauen kann (so, dass es auch mit Rollstuhl benutzbar ist). Die Notiz ist **kein Gegenstand**.


Nicht verwechseln

Ein Kreis im Plan ist nicht automatisch ein Waschbecken. Erst die Umgebung (Raum BAD, Lage an der Wand, Abfluss) macht die Deutung sicher.

MERKSATZ Sanitärgegenstände (Waschbecken, Dusche, WC) erkennst du an ihren **runden oder ovalen Formen** in kleinen Räumen mit dem Boden **PLATTENBELAG**.

25 | Die Küche erkennen

Die Küche von T26 steht als lange Zeile an der linken Wand des Wohnzimmers.

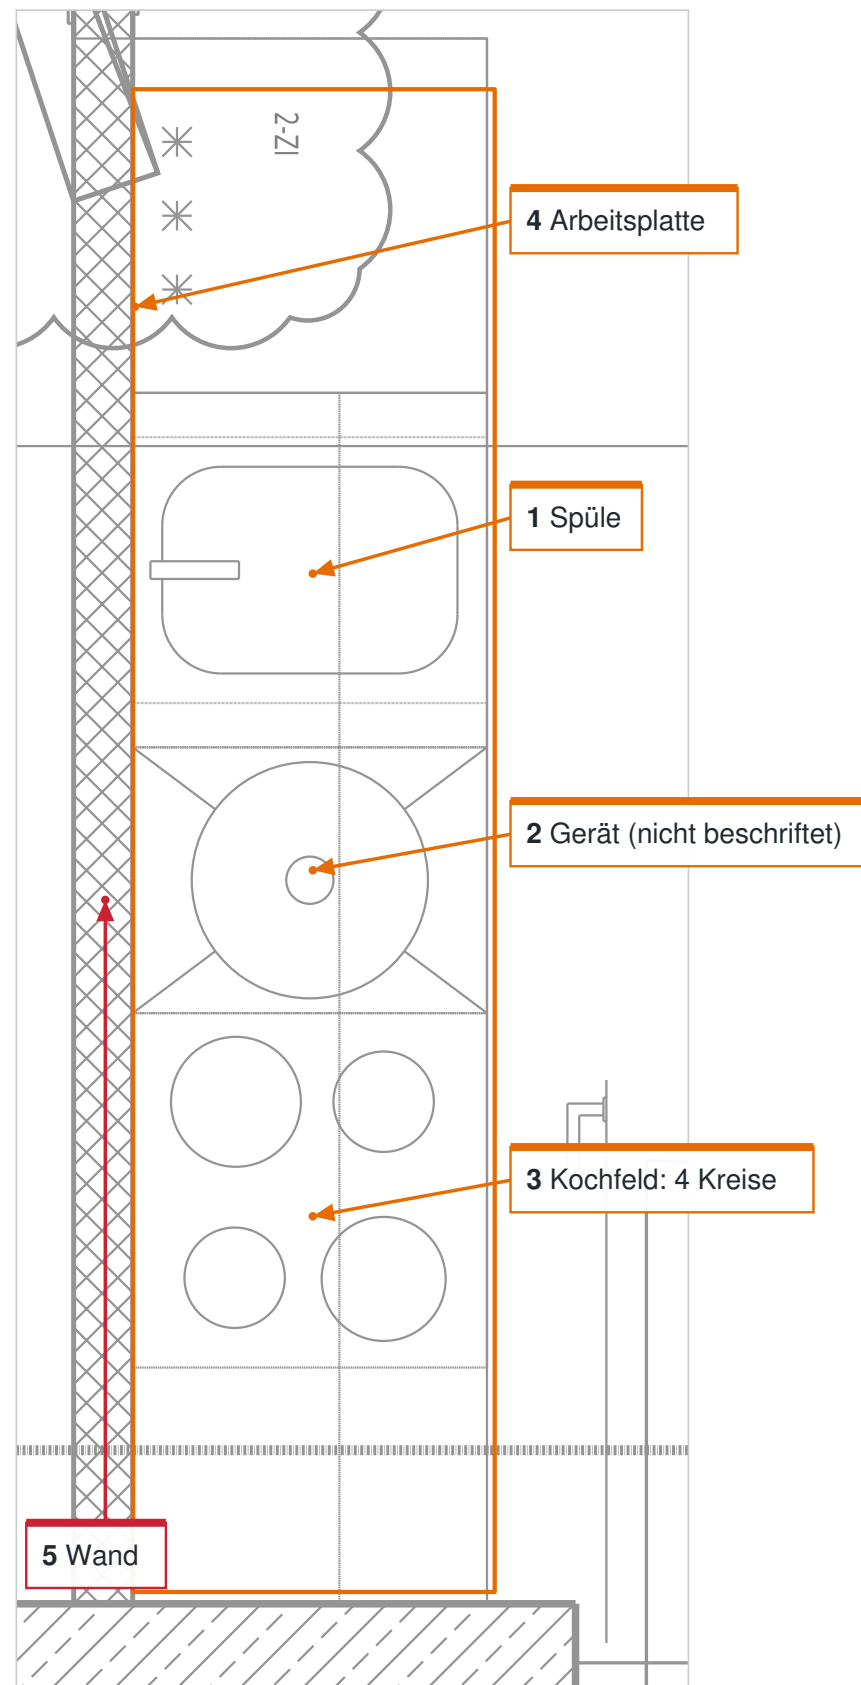

Was ist das?

Eine **Küchenzeile** ist eine Reihe von Küchenschränken, die nebeneinander an einer Wand stehen. Oben drauf liegt die **Arbeitsplatte** (4), auf der man Essen vorbereitet. In die Arbeitsplatte sind Spüle und Herd eingebaut.

Die Teile – von oben gesehen

- **1 Spüle:** ein Rechteck mit abgerundetem Becken. Dort wäscht man ab.
- **2 Gerät:** ein Quadrat mit Kreuz und Kreis. Das ist ein eingebautes Gerät, zum Beispiel ein Geschirrspüler oder ein Backofen. Welches genau, steht nicht im Plan.
- **3 Kochfeld:** vier Kreise. Jeder Kreis ist eine Herdplatte.

Wo ist das?

Im Wohnzimmer von T26, direkt an der Wand zum Schlafzimmer (5). Die Küche hat keinen eigenen Raum – Wohnen und Kochen teilen sich einen Raum. Deshalb steht im Plan nur „WOHNEN“.

Nicht verwechseln

Die Küchenzeile ist **keine Wand**: Sie hat dünne Linien und kein Wandmuster, und sie steht **vor** der Wand. Aber sie ist ein Hindernis: Dort kann man nicht gehen.

MERKSATZ

Eine Küche erkennst du an einer **langen, schmalen Zeile** entlang einer Wand, mit **Herdplatten** (vier Kreise) und einer **Spüle** (Becken).

26 | Was ist eine Verkehrsfläche?

Verkehrsflächen sind die Flächen, die man zum Hin- und Hergehen braucht.



Was ist das?

Das Wort **Verkehrsfläche** klingt nach Straße – gemeint ist aber einfach die Fläche, auf der Menschen **unterwegs** sind. Man hält sich dort nicht lange auf, man geht hindurch.

Hier im Plan

- **1 Gang** (kräftig grün): der lange Flur. Alle Wohnungstüren gehen von ihm ab.
- **2 Stiegenhaus** (türkis): verbindet den Gang mit der Treppe und dem Lift.
- **3 Vorraum** (blau): Auch in einer Wohnung gibt es Verkehrsfläche – den Vorraum, von dem aus man in die Zimmer kommt. Hier ist nur der Vorraum von T26 eingefärbt; jede Wohnung hat einen.

Hellgrün ist der übrige begehbare Boden: Zimmer, Bäder, die Loggia von T25 und die Balkone.

Woran erkenne ich eine Verkehrsfläche?

- am Namen: GANG, VR (Vorraum), STGH. (Stiegenhaus);
- an der Form: lang und schmal;
- an den vielen Türen, die von ihr abgehen.

Warum ist das wichtig?


Über die Verkehrsflächen kommt man im Notfall aus dem Haus hinaus. Deshalb schaut man sie besonders genau an.

MERKSATZ

Verkehrsfläche = Fläche, auf der sich Menschen **von einem Ort zum anderen bewegen**: Gang, Stiegenhaus, Vorraum. Sie verbindet die Räume miteinander.

27 | Der gemeinsame Gang

Ein Stück des Gangs vor den Wohnungen T26 und T27.

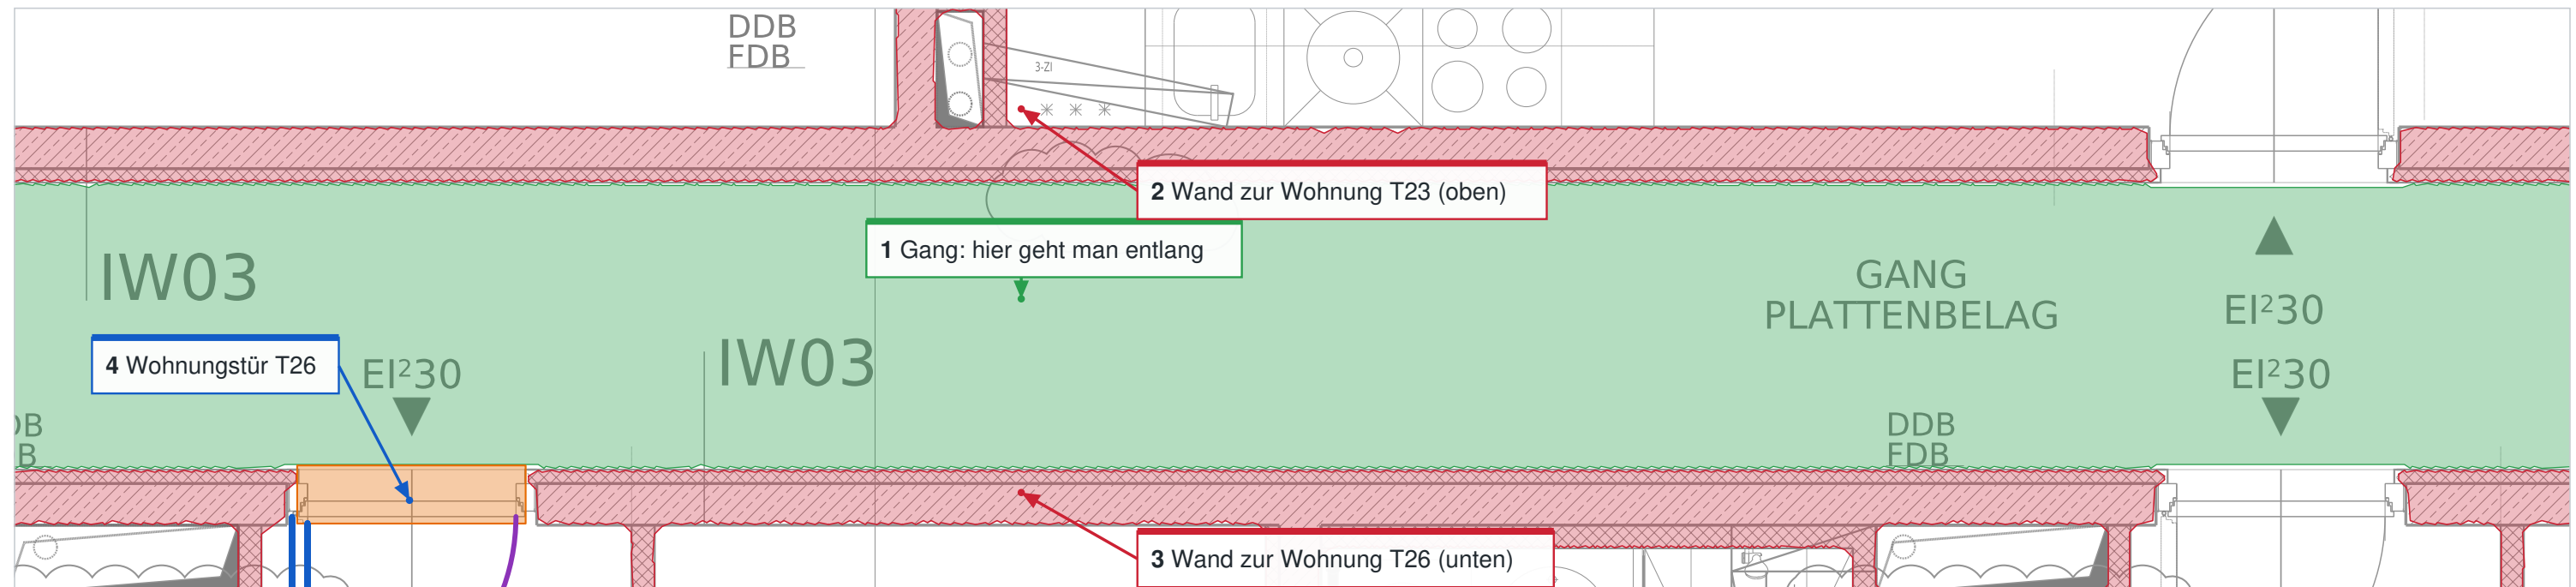

Was siehst du? Einen waagrechten Streifen (grün), oben und unten begrenzt von dicken Wänden (rot). Das ist der Gang.

Wo sind die Türen? Wo die untere Wand eine Lücke hat, geht es in eine Wohnung. Links ist die Wohnungstür von T26 (blau).

Nicht verwechseln: Die Wörter IW03, DDB und FDB und die Wolken im Gang sind Beschriftungen. Sie stehen nicht im Weg.


Merke: Der Gang ist wie eine Straße im Haus. Von ihm gehen die „Hauseingänge“ der einzelnen Wohnungen ab, und an seinem Ende liegt das Stiegenhaus.

MERKSATZ

Der Gang ist eine lange, begehbare Fläche zwischen zwei Wänden. Die Lücken in seinen Wänden sind die **Wohnungstüren**.

28 | Balkone zum Hof

Auch zum Hof hin hängen zwei Balkone. Sie sind draußen – und trotzdem begehbar.

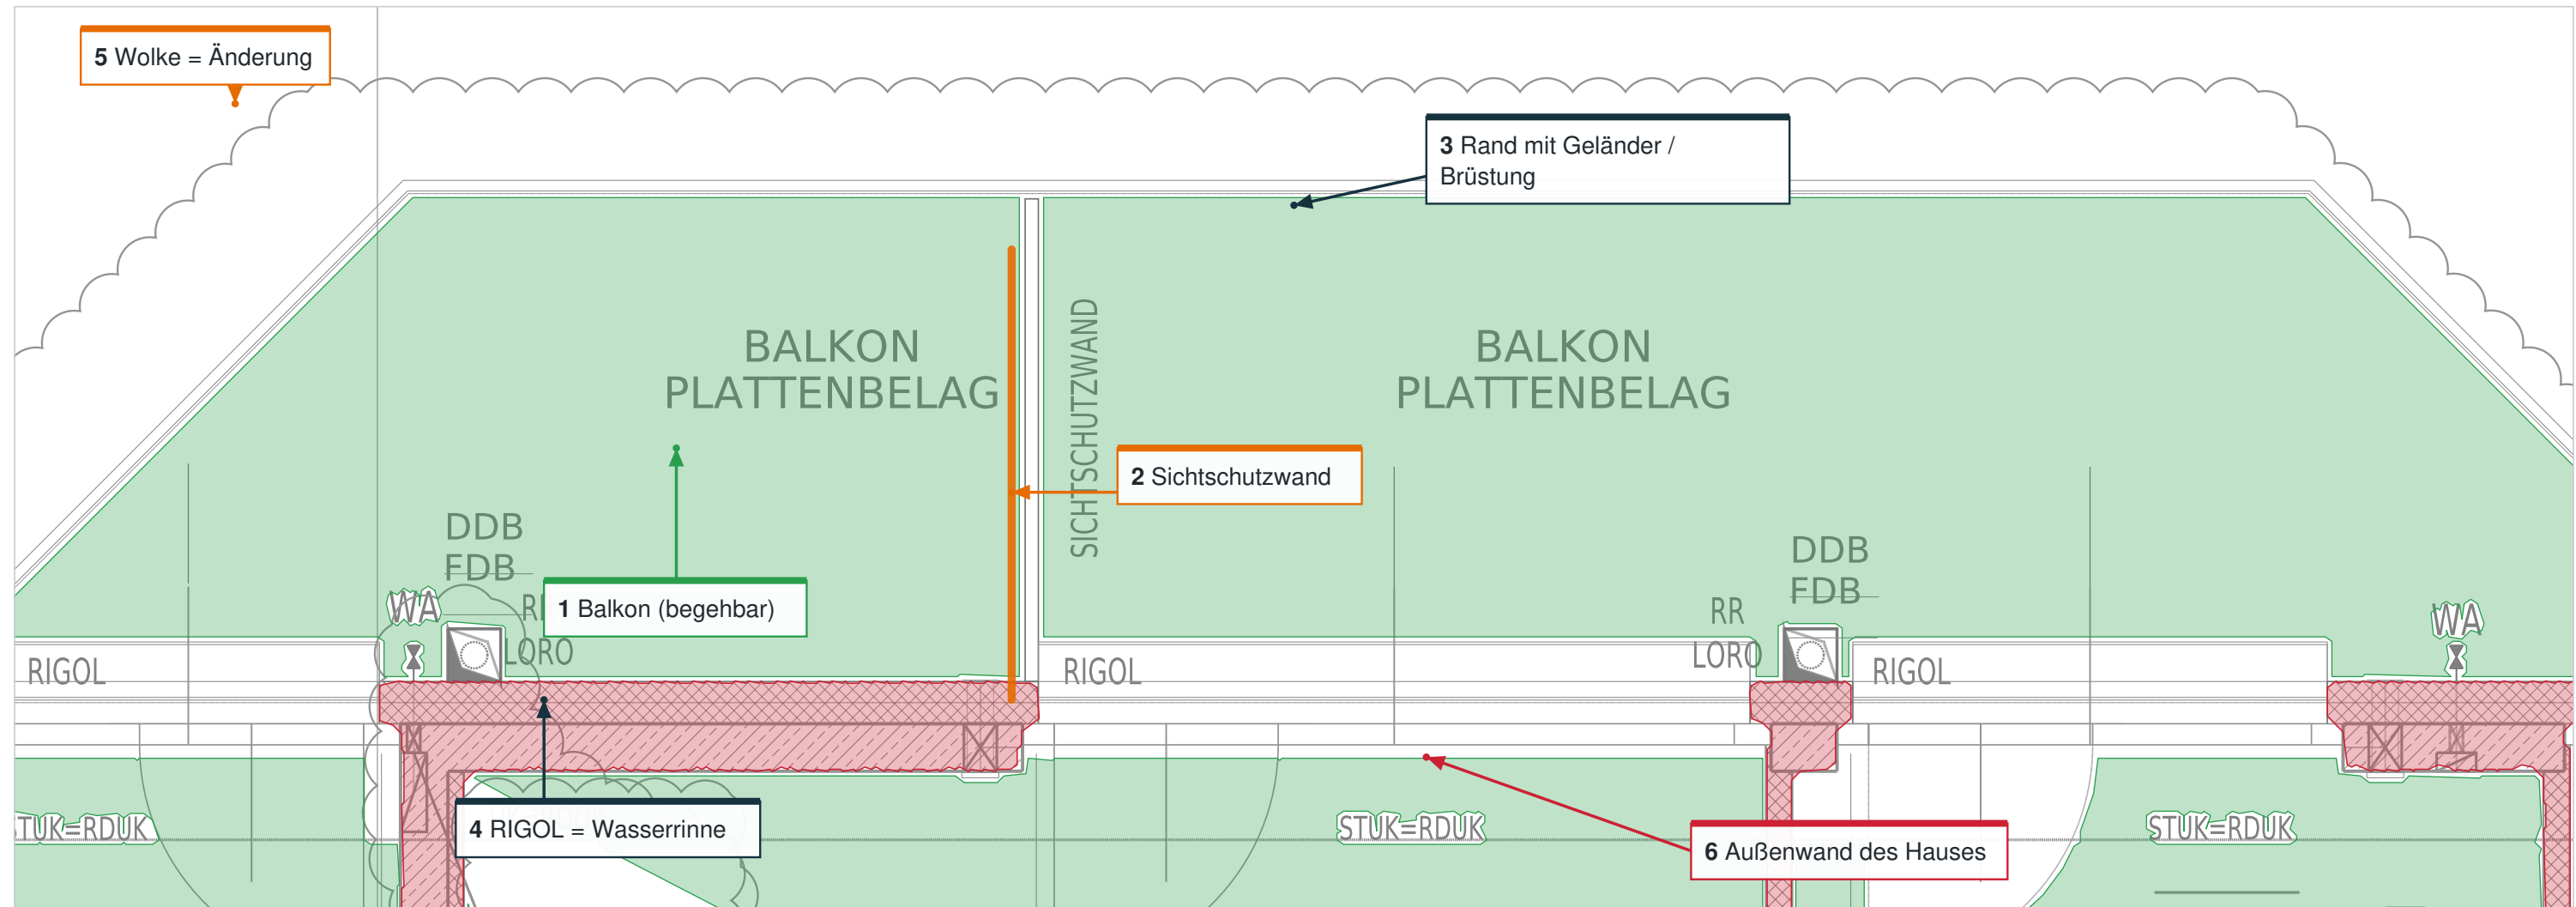

Wo? Oben in der Mitte des Plans, im Hof. Zwei Balkone liegen nebeneinander. Jeder heißt BALKON PLATTENBELAG (Boden aus Platten).

Die Umrandung (3) ist eine doppelte dünne Linie mit schrägen Ecken. Sie zeigt die Außenkante des Balkons, an der ein Geländer oder eine Brüstung steht.

Die Sichtschutzwand (2) trennt die beiden Balkone, damit sich die Nachbarn nicht in die Wohnung schauen. Sie ist eine dünne Wand – man kann nicht hindurch.

Wie bei T26: Auch diese Balkone stehen **vor** der Außenwand (6). Man betritt sie durch Glastüren aus den Wohnungen.


MERKSATZ

Ein **Balkon** ist eine Plattform **vor** der Außenwand. Man betritt ihn durch eine Tür. Sein Rand hat ein Geländer oder eine Brüstung – darüber hinaus geht es in die Tiefe.

29 | Was ist eine Treppe?


Über eine Treppe kommt man zu Fuß in ein anderes Stockwerk.

Von der Seite

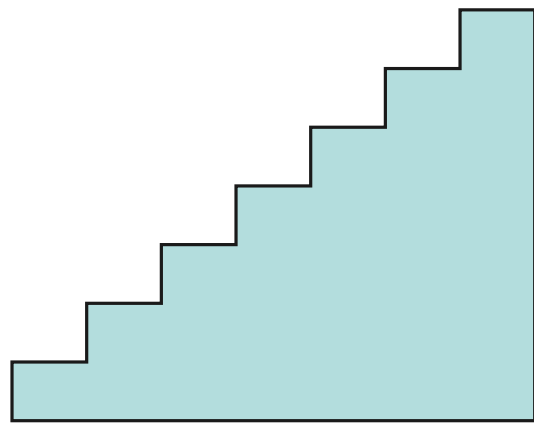

Jede Stufe ist ein kleiner Absatz nach oben.

Von oben (so meist im Grundriss)

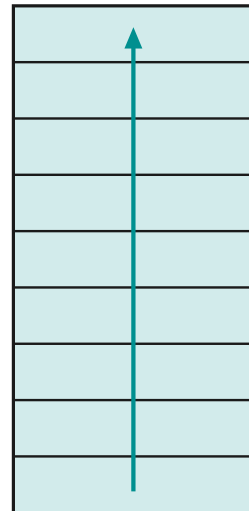

Viele **parallele Linien** = die Kanten der Stufen.

Oft zeigt ein **Pfeil**, in welche Richtung man hinaufgeht.

Die Wörter

Stufe	ein einzelner Tritt nach oben oder unten.
Lauf	eine Reihe von Stufen ohne Pause dazwischen. Eine Treppe hat oft zwei Läufe: einen hinauf bis zur Hälfte, dann umdrehen, dann den zweiten.
Podest	eine ebene Fläche zwischen zwei Läufen oder am Anfang und Ende – dort kann man stehen bleiben.
Stiegenhaus	der Raum, in dem die Treppe liegt (in Österreich sagt man oft „Stiege“ zur Treppe).
Treppenauge / Deckenöffnung	das große Loch in der Decke, durch das die Treppe von einem Stockwerk ins nächste führt.

Was ist das?

Eine **Treppe** verbindet zwei Stockwerke. Man steigt Stufe für Stufe hinauf oder hinunter.

Wie sieht sie im Plan aus?

Von oben sieht man von jeder Stufe nur ihre **Vorderkante**. Viele Stufen ergeben viele **parallele Linien** im gleichen Abstand. Oft zeigt ein **Pfeil** oder eine Linie in der Mitte (die **Lauflinie**), in welche Richtung man hinaufgeht.

Woran erkenne ich eine Treppe?

- viele gleich lange, parallele Linien in gleichem Abstand,
- in einem schmalen Bereich zwischen Wänden,
- im Stiegenhaus (STGH.),
- manchmal mit dem Wort LAUF oder einer Stufenzahl.

Wichtig

Eine Treppe ist **begehbar**, aber nicht eben: Man muss steigen. Deshalb färben wir sie **türkis** und nicht grün.

Nicht verwechseln


Auch Fliesenraster oder Gitterroste bestehen aus parallelen Linien. Eine Treppe erkennt man erst am Ort (im Stiegenhaus) und an den Hinweisen daneben.

MERKSATZ

Treppe = viele **Stufen** hintereinander. Im Grundriss sieht man sie meist als **Reihe paralleler Linien**, oft mit einem Pfeil. Ein Stück Treppe ohne Unterbrechung heißt **Lauf**.

30 | Die Treppe in diesem Plan

Überraschung: In diesem Plan sind die Stufen gar nicht eingezeichnet.

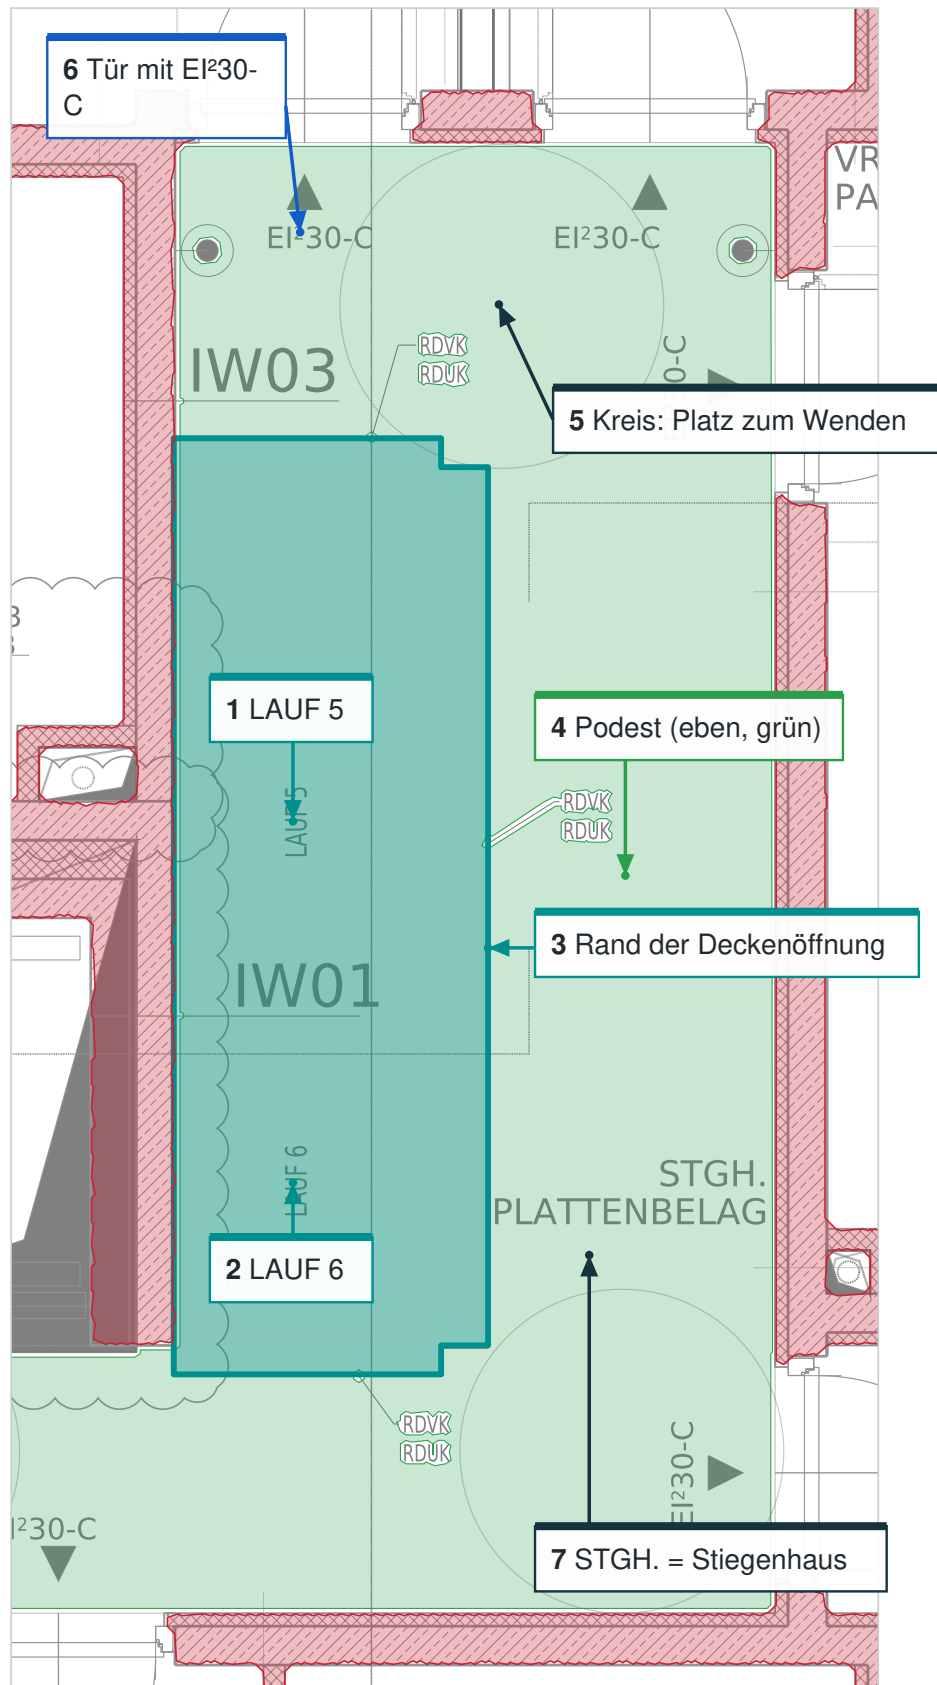

Wo ist das?

In der Mitte rechts des Hauses, dort wo der Gang auf die rechte Gebäudehälfte trifft. Der Raum heißt **STGH.**

PLATTENBELAG: Stiegenhaus mit Plattenboden.

Was siehst du – und was nicht?

Normalerweise würde man hier viele parallele Linien sehen (die Stufen). In diesem Plan sind sie **nicht gezeichnet**. Das kommt vor: Manche Pläne lassen Dinge weg, die für ihren Zweck nicht gebraucht werden.

Trotzdem kann man die Treppe finden:

- **1, 2 · LAUF 5 und LAUF 6:** Hier liegen zwei Treppenläufe nebeneinander. Man geht den einen hinauf und den anderen weiter (oder hinunter). Die Nummern zählen die Läufe im ganzen Haus – deshalb heißen sie im 1. Obergeschoss LAUF 4 und LAUF 5, hier im 2. Obergeschoss LAUF 5 und LAUF 6.
- **3 · Die blaue Randlinie** (türkis hervorgehoben) mit dem Hinweis **RDVK / RDUK:** Dort hat die Decke eine große Öffnung. Die Treppe liegt in dieser Öffnung. RDVK / RDUK sind Angaben zur Kante der Rohdecke (der rohen Betondecke).

Der Rest des Stiegenhauses

4 Podest: der ebene Teil daneben – dort kommt man an und geht weiter in den Gang. **5:** Die großen blauen Kreise zeigen Platz zum Wenden, zum Beispiel für einen Rollstuhl. Sie sind **keine** runden Wände. **6:** Türen mit Brandschutzzeichen (EI²30-C) trennen das Stiegenhaus vom Gang.

Ehrlich gesagt


Wie viele Stufen es gibt und welcher Lauf nach oben führt, zeigt **dieser** Plan nicht. Dafür braucht man eine andere Zeichnung.

MERKSATZ

In diesem Plan zeigen nur die Wörter **LAUF 5** und **LAUF 6** und die blaue Randlinie der Deckenöffnung, wo die Treppe ist. Die einzelnen Stufen fehlen in dieser Zeichnung.

31 | Der Lift

Ein Lift (Aufzug) ist eine Kabine, die in einem Schacht auf und ab fährt.

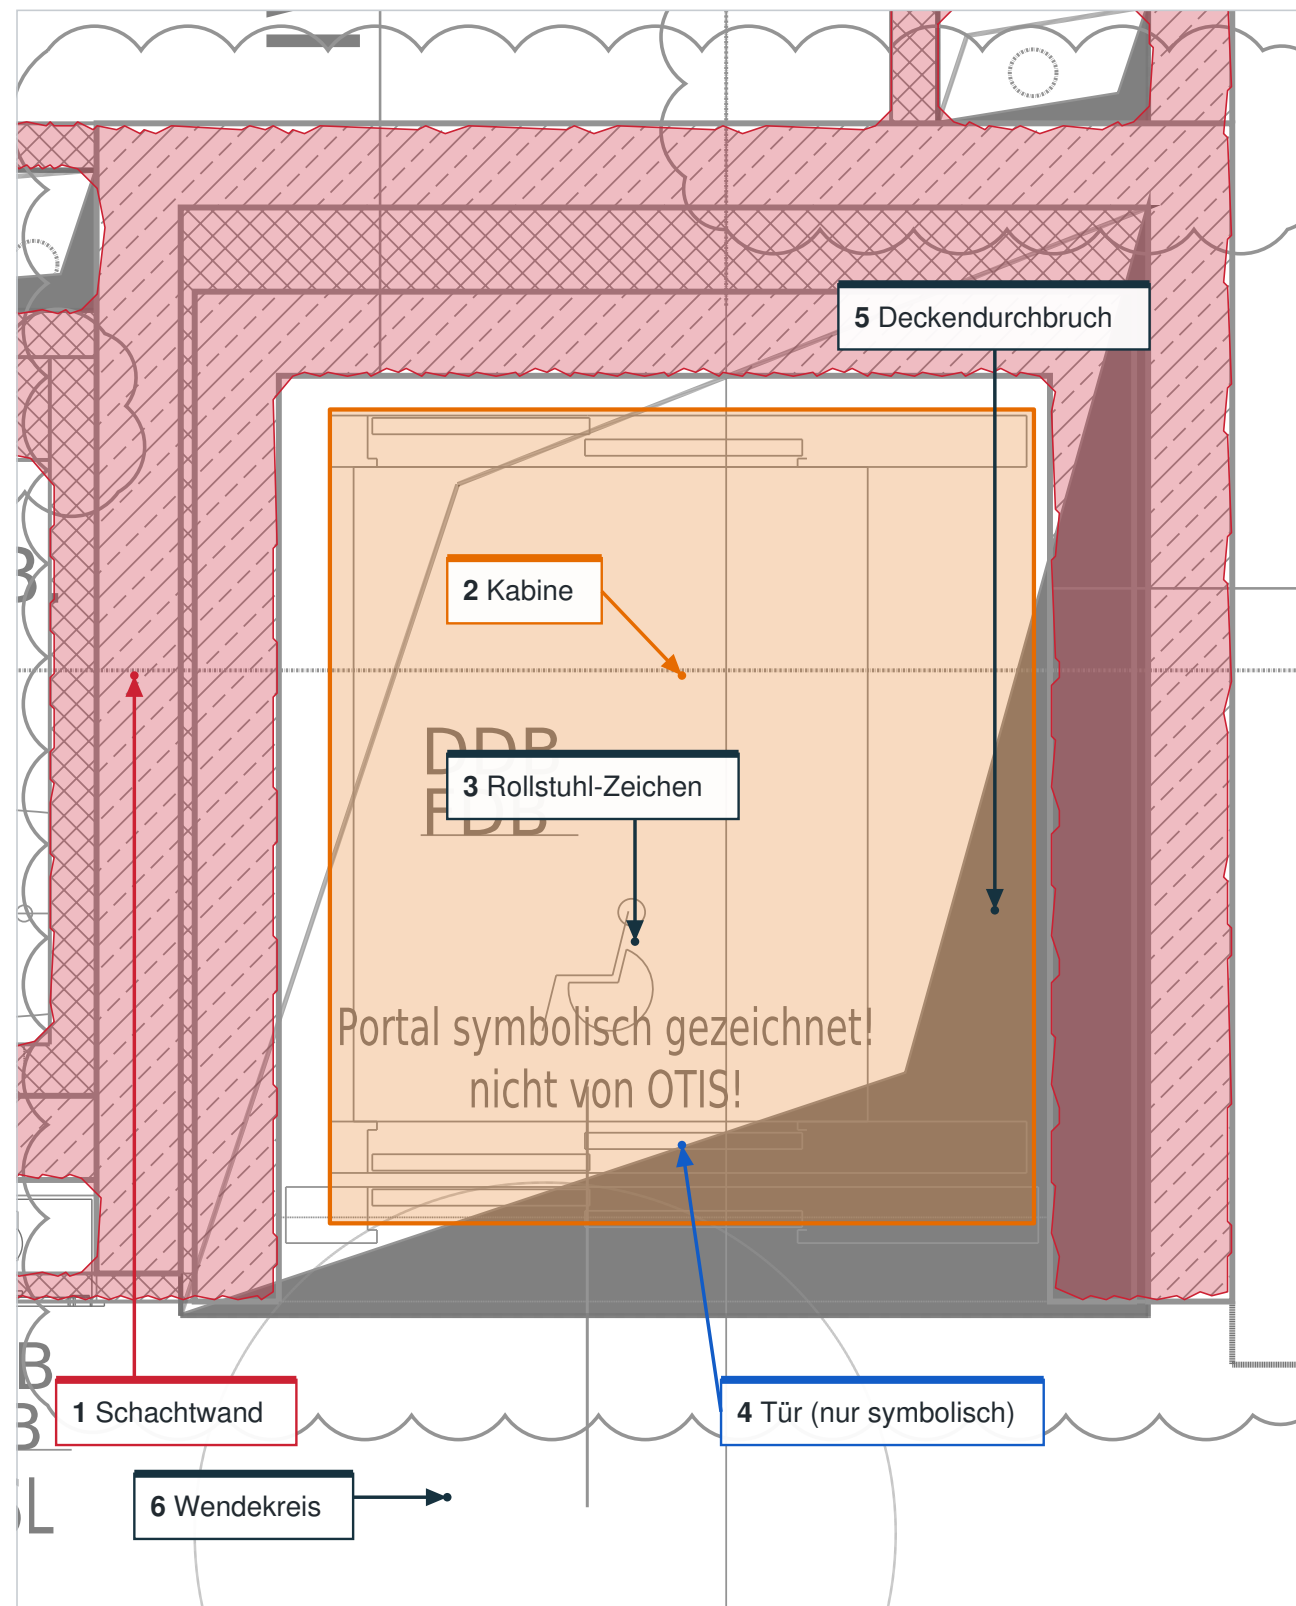

Was ist das?

Ein **Lift** (auch Aufzug) bringt Menschen zwischen den Stockwerken hinauf und hinunter. Die **Kabine** ist ein kleiner Raum, der sich in einem senkrechten Kanal bewegt – dem **Schacht**.

Wo ist das?

Links neben dem Stiegenhaus, direkt am Gang.

Was siehst du?

- **1 Schachtwand** (rot): dicke Wände rundherum.
- **2 Kabine** (orange): das graue Rechteck innen.
- **3**: ein kleines **Rollstuhl-Zeichen** – der Lift ist für Rollstühle geeignet.
- **4 Tür**: Oben und unten sind feine Rahmen gezeichnet. Im Plan steht dazu wörtlich: „Portal symbolisch gezeichnet! nicht von OTIS!“ Das heißt: Die Lifttür (das „Portal“) ist nur ungefähr gezeichnet, noch nicht nach den Unterlagen der Lift-Firma (OTIS ist ein Lift-Hersteller).
- **5**: Die blaue Umrandung mit dem dunklen Dreieck bedeutet eine große Öffnung in der Decke (**DDB** = Deckendurchbruch, **FDB** = Fußbodendurchbruch). Durch diese Öffnung fährt der Lift.
- **6**: Der blaue Kreis vor dem Lift zeigt Platz zum Wenden, etwa mit einem Rollstuhl.

Kann man hier gehen?


Nein – außer in der Kabine, wenn der Lift gerade da ist. Der Schacht ist kein Boden. Deshalb ist der Lift in diesem Buch nicht grün.

MERKSATZ

Ein Lift besteht aus einem ummauerten **Schacht** und der **Kabine** darin. Einsteigen kann man nur an der **Lifttür**.

32 | Schächte und Technik

Entlang des Gangs liegen kleine Kästen mit Wörtern wie HEIZUNG und ELEKTRO.

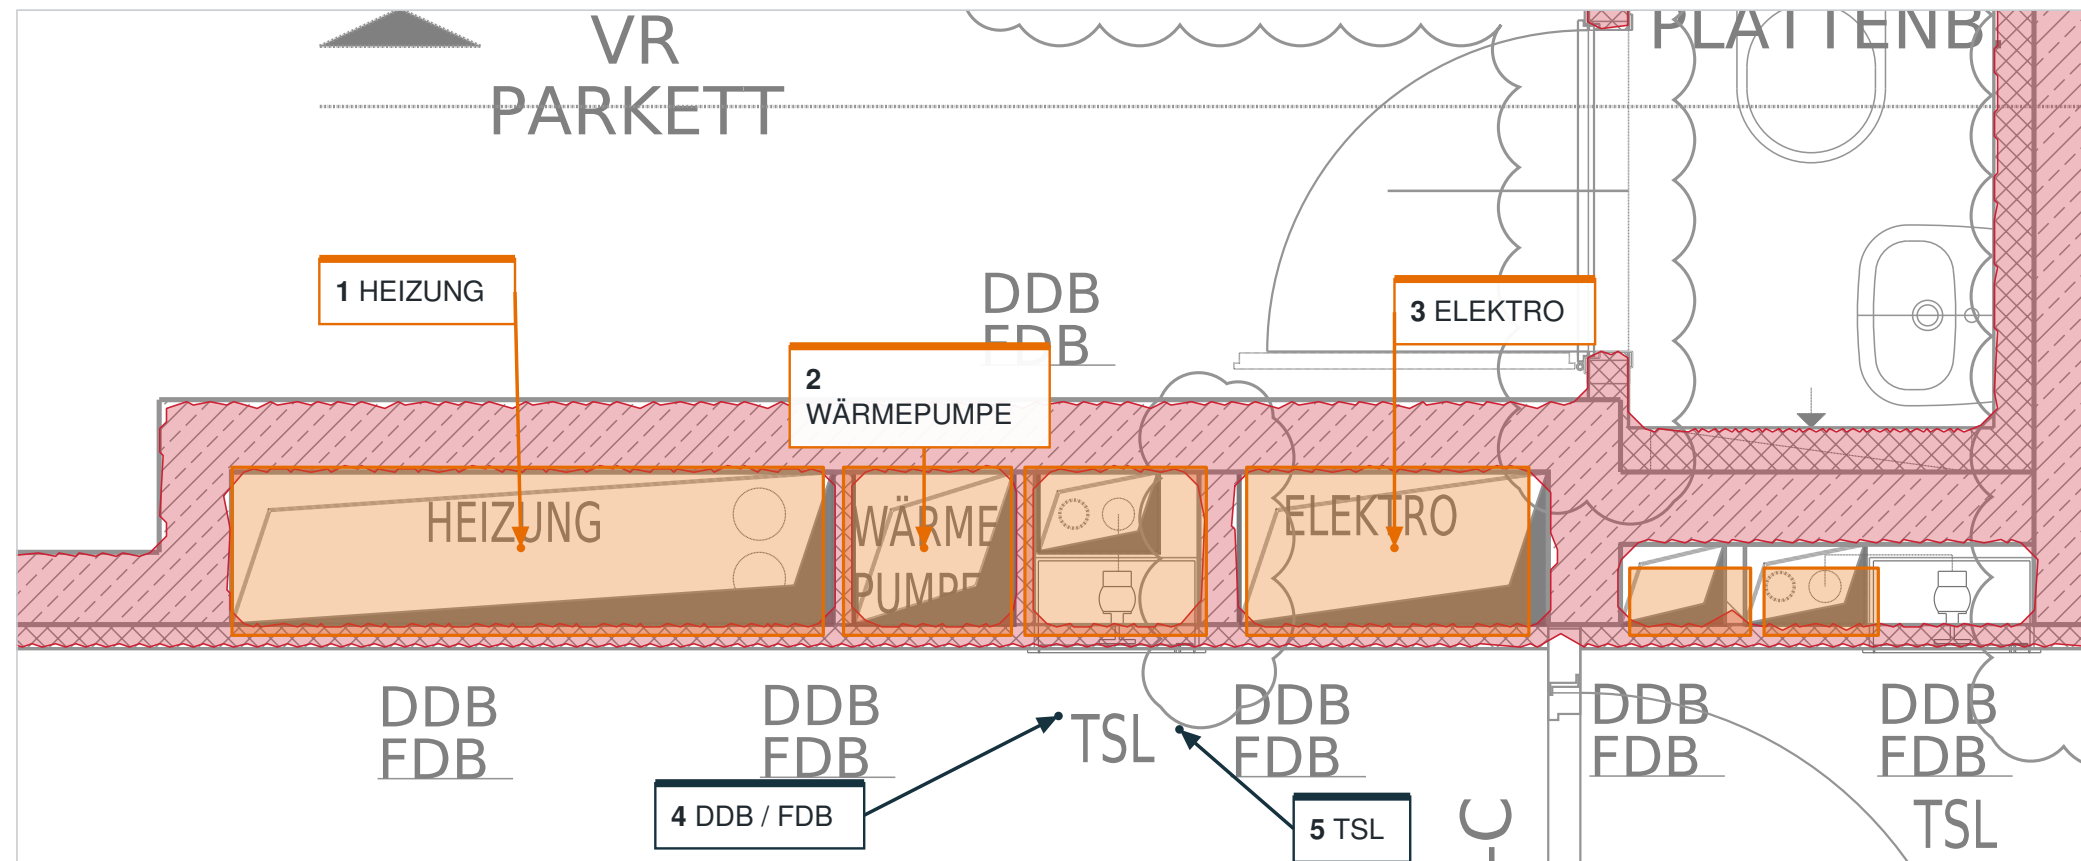

Wo? An der Wand oben am Gang, rechts von der Mitte des Hauses. Die Kästen liegen in einer Reihe **in** der Wand.

1–3: Die Wörter sagen, was durch den jeweiligen Schacht läuft: Leitungen für die **Heizung**, für eine **Wärmepumpe** (ein Gerät, das Wärme für das Haus erzeugt) und für den **Strom** (Elektro).

4 DDB / FDB: Diese Kürzel stehen im ganzen Plan bei den Schächten. Sie bedeuten üblicherweise **Deckendurchbruch** und **Fußbodendurchbruch**: Hier hat die Decke ein Loch für die Leitungen.

5 TSL: wird im Plan nicht erklärt. In Bauplänen steht das Kürzel häufig für eine **Trockensteigleitung** (ein Rohr für die Feuerwehr). Hier ist das nicht sicher belegt.


Für dich wichtig: Schächte sind **keine Räume** und **kein Boden**. Sie sind Hindernisse.

MERKSATZ

Kleine ummauerte Kästen mit einem **dunklen Dreieck** sind **Schächte**: senkrechte Kanäle für Rohre und Kabel. Man kann sie nicht betreten.

33 | Weitere Zeichen im Plan

Buchstaben am Rand, Wolken, Höhenhinweise: Was bedeuten sie?

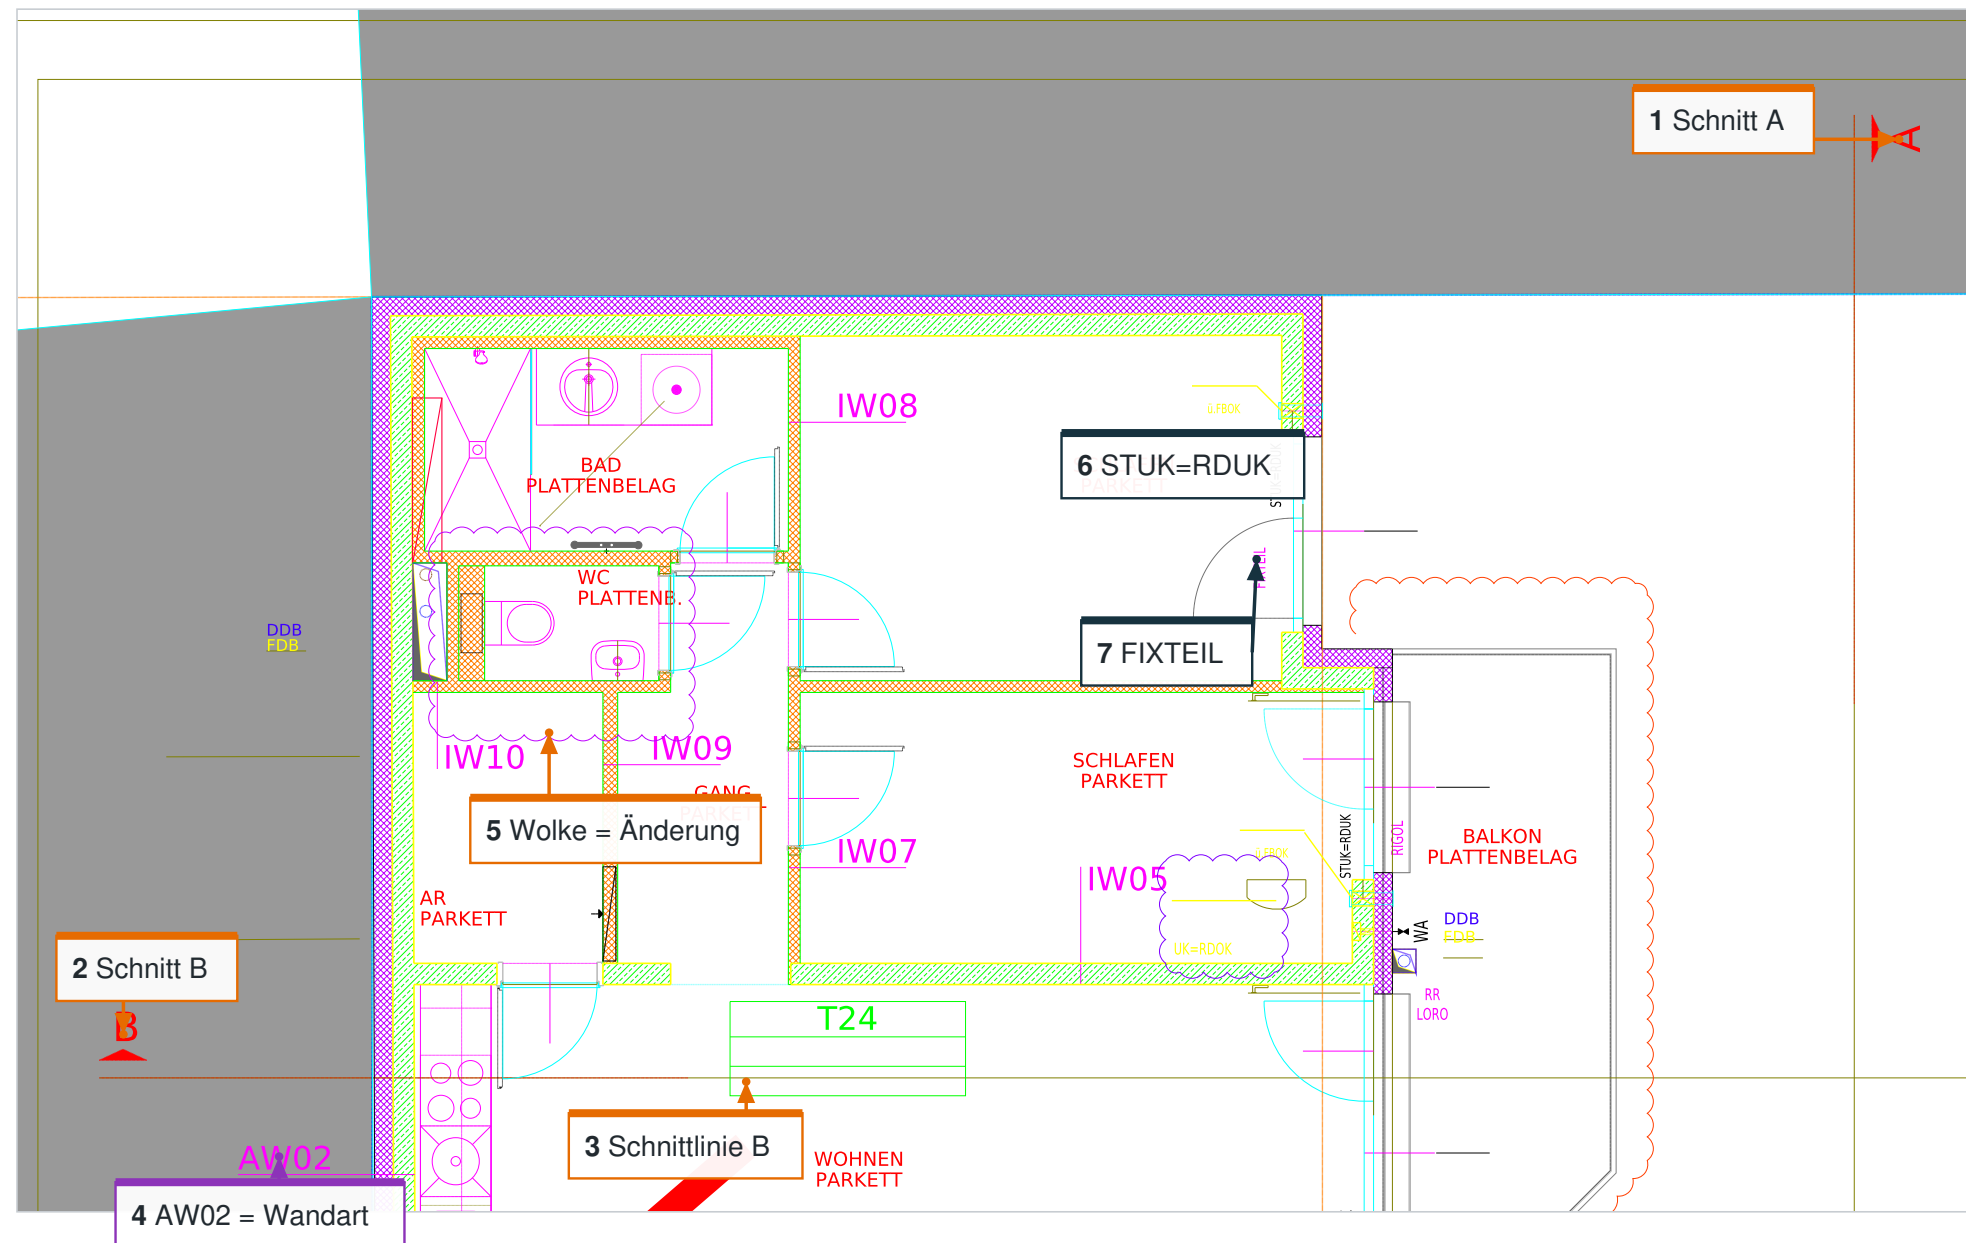

1–3 · Schnitte

Am Rand stehen große Buchstaben mit einem kleinen Dreieck (A, B, D, E, F, G). Von dort läuft eine lange Linie quer durch das Haus. Sie zeigt: Hier gibt es eine **zweite Zeichnung**, einen **Schnitt**. Ein Schnitt zeigt das Haus **von der Seite**, als hätte man es senkrecht durchgeschnitten. Das Dreieck zeigt die Blickrichtung.

4 · Wandkürzel

AW02, **IW03** und ähnliche Kürzel benennen die Art einer Wand (Kapitel 06).

5 · Wolken

Eine Umrandung aus vielen kleinen Bögen heißt **Revisionswolke**. Sie markiert eine Stelle, an der der Plan geändert wurde. Sie ist kein Bauteil.

6 · Höhenangaben

Kürzel wie **STUK=RDUK**, **ü.FBOK** oder **UK=RDOK** beschreiben Höhen: **FBOK** = fertige Bodenoberkante (die Oberseite des fertigen Bodens), **RDOK** / **RDUK** = Ober- bzw. Unterseite der rohen Betondecke, **STUK** = Sturzunterkante (die Unterseite des Wandstücks über einer Öffnung). „**STUK=RDUK**“ bedeutet also: Die Öffnung reicht oben bis an die Decke.

7 · Hinweise an Fenstern

FIXTEIL: ein fester, nicht zu öffnender Teil (Kapitel 19).

Und die dicken roten Schrägbalken?

In vielen Wohnzimmern dieses Geschosses (etwa T24 unten im Bild und T26) liegt ein dicker roter Balken schräg im Raum. Er ist nicht beschriftet. Sicher ist: Er ist **keine Wand** (keine Wandseiten, kein Anschluss an andere Wände).

34 | Das ganze Geschoss auf einen Blick

Jetzt kennst du alle Lernfarben. So sieht der ganze Plan damit aus.



So liest du dieses Bild

1. **Rot** zeigt dir das Gerüst des Hauses: alle Wände.
2. **Grün** zeigt jede Stelle, auf der man stehen kann – in allen 11 Wohnungen, im Gang, im Stiegenhaus, in der Loggia von T25 und auf allen Balkonen.
3. **Türkis** ist die Treppe, **orange** der Lift.
4. **Weiß** innerhalb des Hauses sind Küchen, Bad- und WC-Einrichtung und Schächte.

Übung

Such dir eine Wohnung aus, zum Beispiel **T30** rechts. Finde:

- ihre Wohnungstür (wo berührt ihr Grün das Grün des Gangs oder Stiegenhauses?),
- ihr Wohnzimmer (größte grüne Fläche mit Küche),
- ihren Balkon (grüne Fläche außen vor der Hauswand).

Was grün nicht bedeutet

Grün heißt „hier ist Boden“. Es heißt nicht „hier ist ein Fluchtweg“ oder „das ist breit genug“. Dafür braucht es Maße, und dieser Plan hat keine („ohne Masse“ im Dateinamen).

MERKSATZ

Rot = Wand · Grün = begehbare Boden · Türkis = Treppe · Orange = Lift. Weiß im Haus = Einrichtung und Schächte.

35 | Spickzettel: Was ist das?

Wenn du im Plan etwas nicht erkennst, geh diese Tabelle von oben nach unten durch.


Ich sehe ...	Dann ist es wahrscheinlich ...	Prüfe noch ...	Farbe im Buch
zwei parallele Linien mit Muster dazwischen	eine Wand	Läuft sie bis zu einer Ecke, Wand oder Öffnung? Läuft sie nicht durch andere Wände?	rot
eine Lücke in der Wand, darin nichts	ein Durchgang	Ist auf beiden Seiten Boden?	orange
Lücke + gerader Strich quer zur Wand + Viertelkreis	eine Tür	Beginnt der Bogen am freien Ende des Strichs und endet an der Wand?	blau / violett
Lücke in der Außenwand + feine Doppellinie quer darin	ein Fenster	Steht FIXTEIL dabei? Gibt es einen Flügel mit Bogen?	gelb
sehr feine Linie(n) ohne Muster zwischen zwei Bereichen	Glas	Liegt sie in einer Wandöffnung oder trennt sie Wohnzimmer und Balkon?	hellblau
kleine Formen aus dünnen Linien (Kreise, Ovale, Rechtecke)	Einrichtung	In welchem Raum? BAD, WC, Küche?	orange / weiß
viele gleiche parallele Linien, Wort LAUF, im Stiegenhaus	eine Treppe	Liegt es im STGH.? Gibt es eine Deckenöffnung?	türkis
ummauerter Kasten mit dunklem Dreieck, DDB/FDB	ein Schacht	Steht HEIZUNG, ELEKTRO o. Ä. dabei?	orange
freie Fläche zwischen Wänden mit Raumname	begehbbarer Boden	Kommt man durch eine Tür hinein?	grün
lange Linie quer durch Wände und Räume	Schnitt- oder Hilfslinie	Steht am Rand ein Buchstabe mit Dreieck?	keine
Umrandung aus vielen kleinen Bögen	Revisionswolke	–	keine
Wörter und Kürzel	Beschriftung	Raumname (oben) + Boden (unten)? Kürzel wie IW, DDB, FBOK?	keine

MERKSATZ

Nie nur auf **ein** Merkmal schauen. Erst wenn **Form, Lage und Beschriftung** zusammenpassen, ist die Deutung sicher.

36 | Selbsttest: Kannst du es jetzt selbst?

Das ist die Wohnung T27 – die Nachbarwohnung rechts von T26. Sie ist fast genauso gebaut.

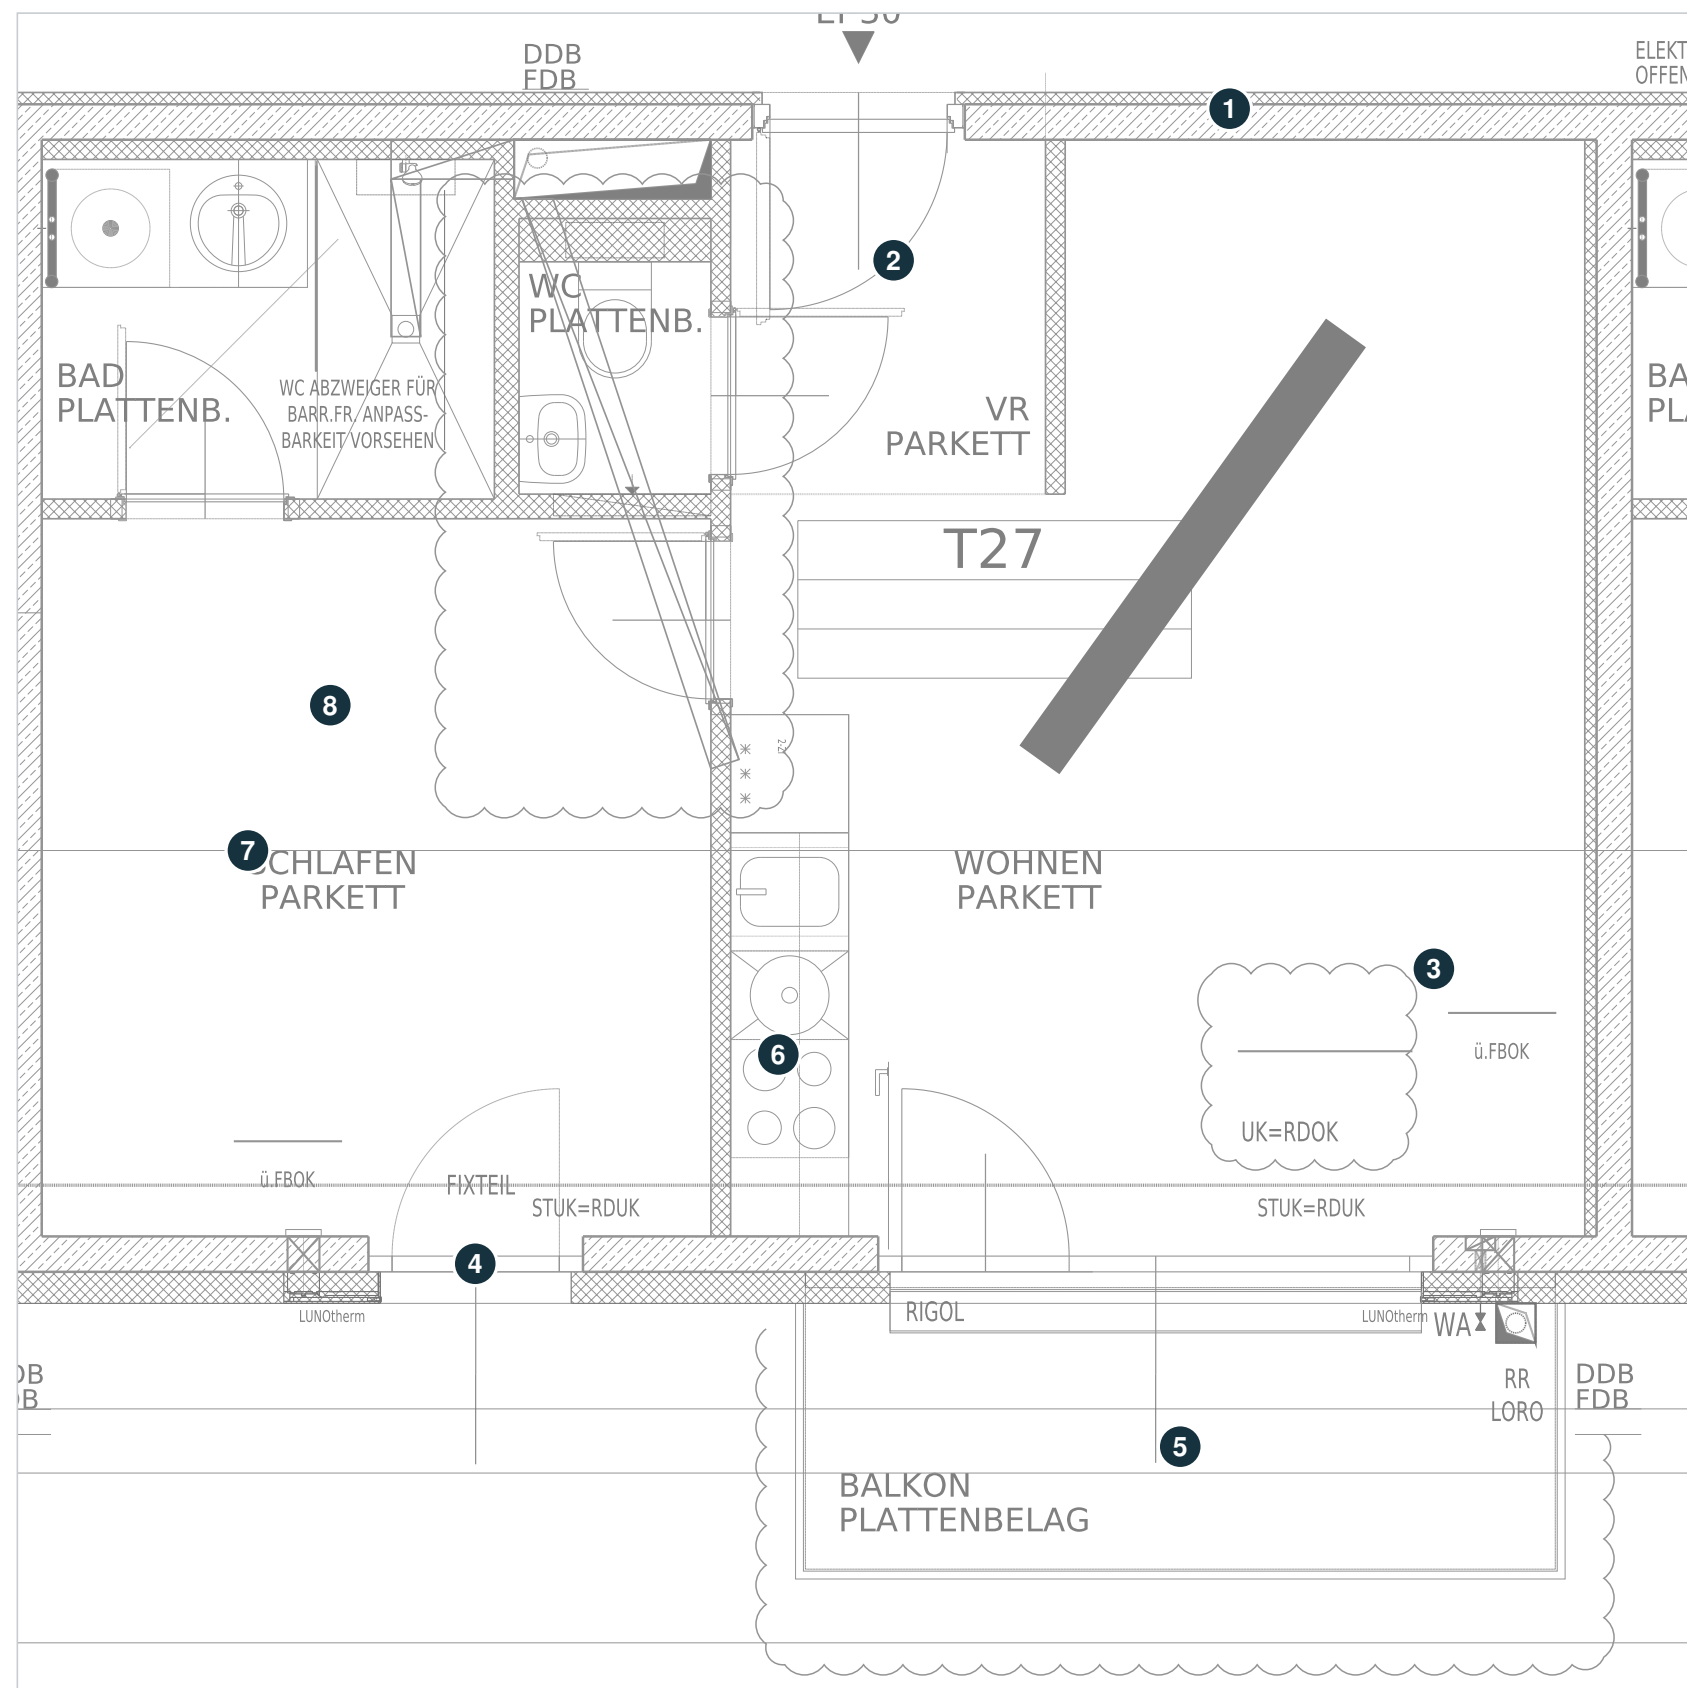

Fragen

1. Was ist der breite gemusterte Streifen bei 1?
2. Was zeigt der Viertelkreis bei 2 – und in welchen Raum geht diese Tür auf?
3. Kann man bei 3 gehen?
4. Was sitzt in der Lücke der Außenwand bei 4?
5. Was ist bei 5 – drinnen oder draußen? Kann man dort stehen?
6. Was sind die Kreise bei 6?
7. Ist die Linie bei 7 eine Wand?
8. Welcher Raum ist bei 8?

Tipp: Vergleiche mit den Seiten zu T26. Die Räume liegen bei T27 an denselben Stellen.

Lösungen: 1 Wand (Gangwand). 2 Wohnungstür, sie geht in den Vorraum auf. 3 ja, freier Boden im Wohnzimmer. 4 ein Fenster (Rahmen + Glas) des Schlafzimmers. 5 der Balkon – draußen, aber begehbar. 6 die Herdplatten der Küche. 7 nein – sie läuft durch Wände hindurch, es ist eine Hilfslinie. 8 das Schlafzimmer (SCHLAFEN PARKETT).

MERKSATZ

Wenn du alle acht Fragen beantworten kannst, kannst du diesen Plan lesen. Die Lösungen stehen unten rechts.

37 | Was dieses Buch zeigt – und was nicht

Ehrliche Grenzen: Was man aus diesem einen Grundriss wissen kann und was nicht.

Sicher aus dem Plan gelesen

- wo Wände stehen und wo sie Lücken haben,
- wo Türen sind und in welche Richtung sie aufgehen,
- wo Fenster und Glaswände sind,
- welche Räume es gibt und wie sie heißen,
- wo freier Boden ist und wo Einrichtung steht,
- wo Stiegenhaus, Treppenöffnung und Lift liegen.

Nicht aus diesem Plan ablesbar

- **Maße:** Der Plan hat keine Maßangaben („ohne Masse“). Wie breit ein Gang oder eine Tür ist, steht nicht da.
- **Höhen:** wie hoch Brüstungen, Fenster und Türen sind.
- **Materialien:** welches Muster welches Material bedeutet.
- **Die Stufen** der Treppe: Sie sind nicht gezeichnet.
- die Bedeutung einiger Kürzel und Zeichen (roter Schrägbalken, lange gelbe und blaue Linien, TSL, WA, LUNOtherm).

Woher kommen die Farben?

Alle Markierungen liegen auf dem **Original-Vektorplan** (2OG_ohne_Masse.pdf). Die grauen Linien sind die unveränderten Linien des Plans, nur neu eingefärbt.

- **Wände (rot)** wurden aus den Wandmustern (Schraffuren) des Plans berechnet.
- **Boden (grün)** wurde als freie Fläche zwischen Wänden, Einrichtung und Glas berechnet. Kleine Ungenauigkeiten an Rändern und Beschriftungen sind möglich.
- **Türen, Fenster, Glas** in T26 sind die **Originalstriche** des Plans, nur farbig nachgezogen.
- Das Zeichenprogramm hat das 2. OG minimal größer und verschoben abgelegt als das 1. OG (um 0,4 %). Für dieses Buch wurde der Plan exakt auf den Maßstab des 1. OG zurückgerechnet; dabei ändert sich keine Linie in ihrer Form.

Wörter, die als „üblich“ erklärt sind

Einige Kürzel (EI²30, DDB, FDB, RR, TSL, IW/AW) erklärt der Plan nicht selbst. Wo dieses Buch sie erklärt, steht „üblicherweise“ oder „vermutlich“ dabei. So bleibt sichtbar, was aus dem Plan selbst stammt und was allgemeines Wissen ist.

Zum Weiterlernen

Nimm dir jetzt eine andere Wohnung vor und geh die Kapitel der Reihe nach durch: erst Wände, dann Öffnungen, dann Türen und Fenster, dann Boden. Genau in dieser Reihenfolge liest man jeden Grundriss.