


2. UNTERGESCHOSS | Freie Bodenflächen

Überarbeitet: rote Wände/Stützen · Türblatt orange · Schwenkbogen blau · CAD-Grundlage grau

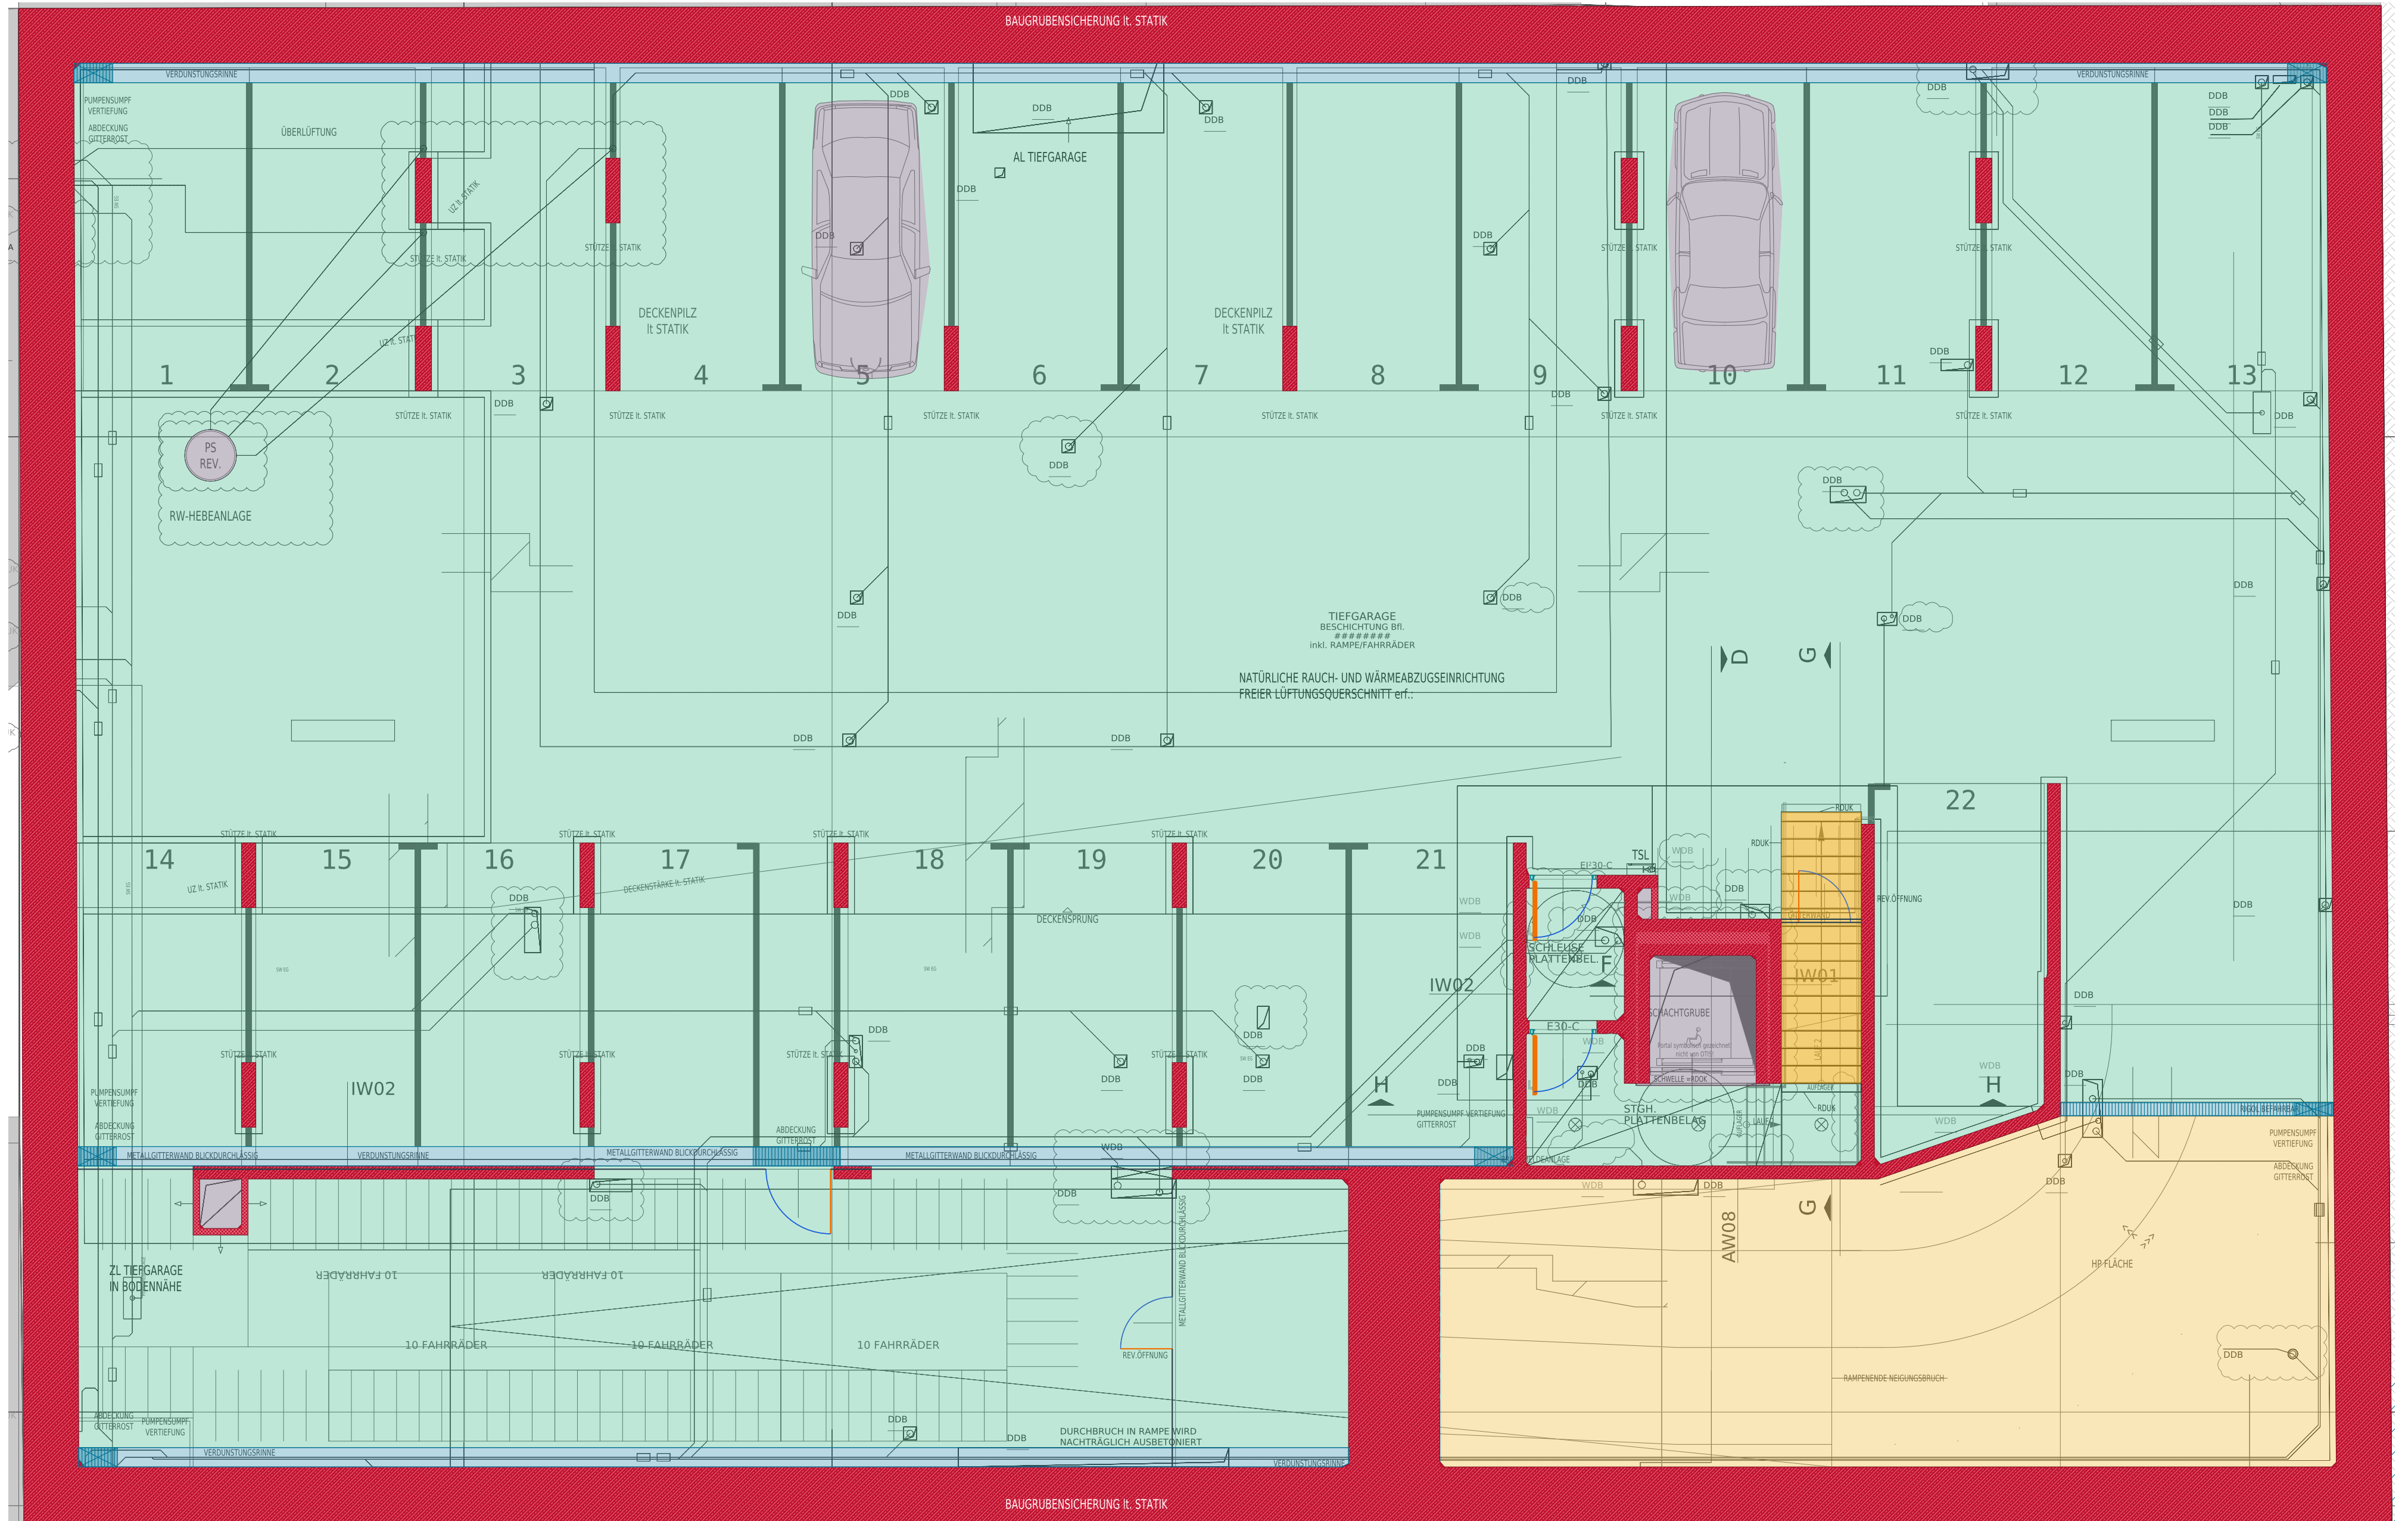


- | | | | | | |
|--|--|--|--|--|---|
| Wand / Stütze | Türblatt | Schwenkbogen | Zarge / Rahmen | freier Boden | Stufenbereich |
| Rampe | Rinne / Rost | Belegung / Schacht | Gittertrennung | Stellplatzlinien | Stufenkante |

Grün zeigt freie Planfläche bei passierbaren Zugängen. Rinnen/Roste sind gesondert; die Rampe ist kein bestätigter Fußweg.

Quelle: 2UG_ohne_Masse(1).pdf | Ausführliche Begründungen und offene Höhenzuordnungen im überarbeiteten Lernbuch | 24.09.2026

2. UNTERGESCHOSS | Bauteile direkt markiert

Überarbeitet: rote Wände/Stützen · Türblatt orange · Schwenkbogen blau · CAD-Grundlage grau

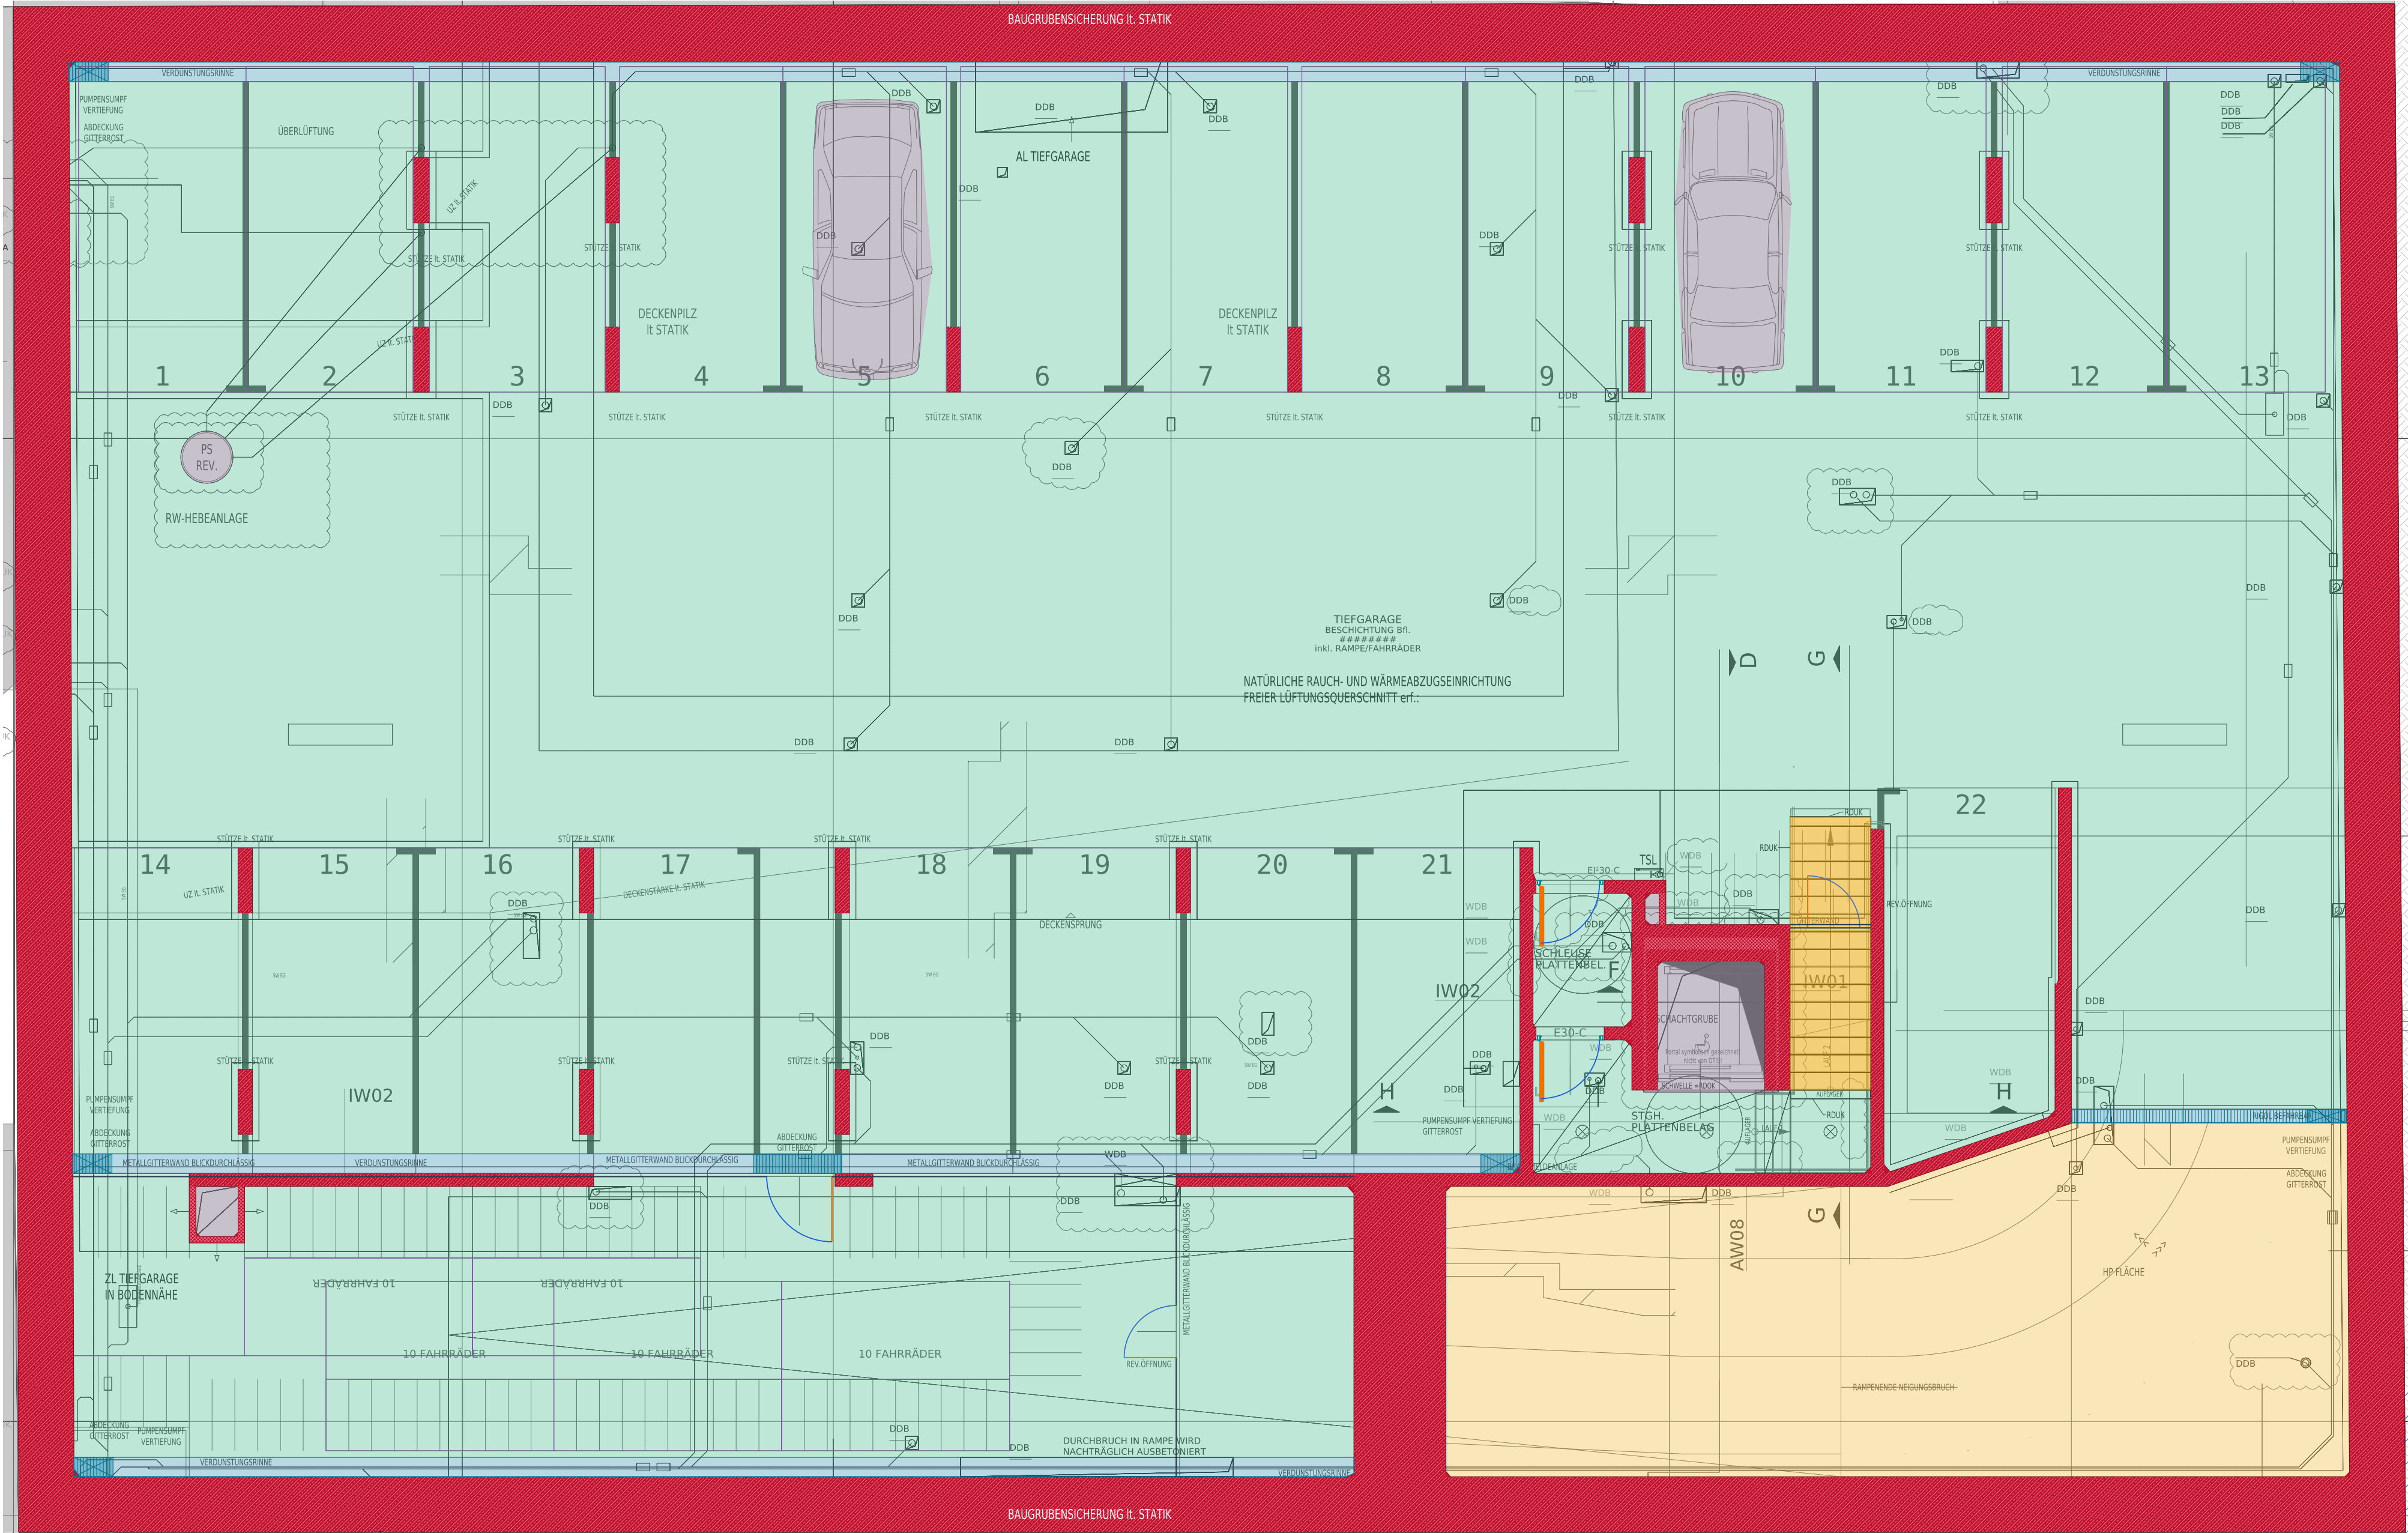

- Wand / Stütze

Türblatt

Schwenkbogen

Zarge / Rahmen

freier Boden

Stufenbereich
- Rampe

Rinne / Rost

Belegung / Schacht

Gittertrennung

Stellplatzlinien

Stufenkante

Grün zeigt freie Planfläche bei passierbaren Zugängen. Rinnen/Roste sind gesondert; die Rampe ist kein bestätigter Fußweg.

Quelle: 2UG_ohne_Masse(1).pdf | Ausführliche Begründungen und offene Höhenzuordnungen im überarbeiteten Lernbuch | 24.09.2026