

Grundriss lesen lernen – 3. Obergeschoss

Ein Erklärplan für Menschen, die noch nie einen Bauplan gesehen haben

Links siehst du den Plan, um den es in diesem Heft geht: das **3. Obergeschoss** eines Wohnhauses an der Ecke **Aichholzgasse / Pöhlgasse**. Der Originalplan liegt unverändert darunter. Die bunten Farben habe ich darübergelegt, damit du die Bauteile auseinanderhalten kannst.


Das Heft geht Schritt für Schritt vor, so wie ein geduldiger Lehrer neben dir:

- 1. Was ist ein Grundriss überhaupt?
- 2. Welche Sprache sprechen die Linien?
- 3. Der Originalplan, ganz ohne Markierung
- 4. Orientierung: Wo ist was?
- 5. Wände
- 6. Türen
- 7. Fenster und Glas
- 8. Wo man gehen kann
- 9. Räume einer Wohnung
- 10. Bad, Küche, Stiegenhaus, Aufzug, Schächte, Gang, Balkon
- 11. Schriften, Zeichen und Abkürzungen
- 12. Was der Plan *nicht* verrät
- 13. Teste dich selbst – mit Lösungen
- 14. Checkliste für jeden weiteren Plan

Bei jedem Bauteil beantwortet das Heft drei Fragen:

Was ist das? · **Wie sieht es auf einem Plan aus?** · **Woran erkenne ich es genau hier?**

Wichtig: Alle Farben sind Lernmarkierungen. Sie wurden aus der Plangeometrie abgeleitet und von Hand geprüft, sind aber keine millimetergenaue Planung. Wo der Plan etwas nicht eindeutig sagt, steht das ausdrücklich dabei.

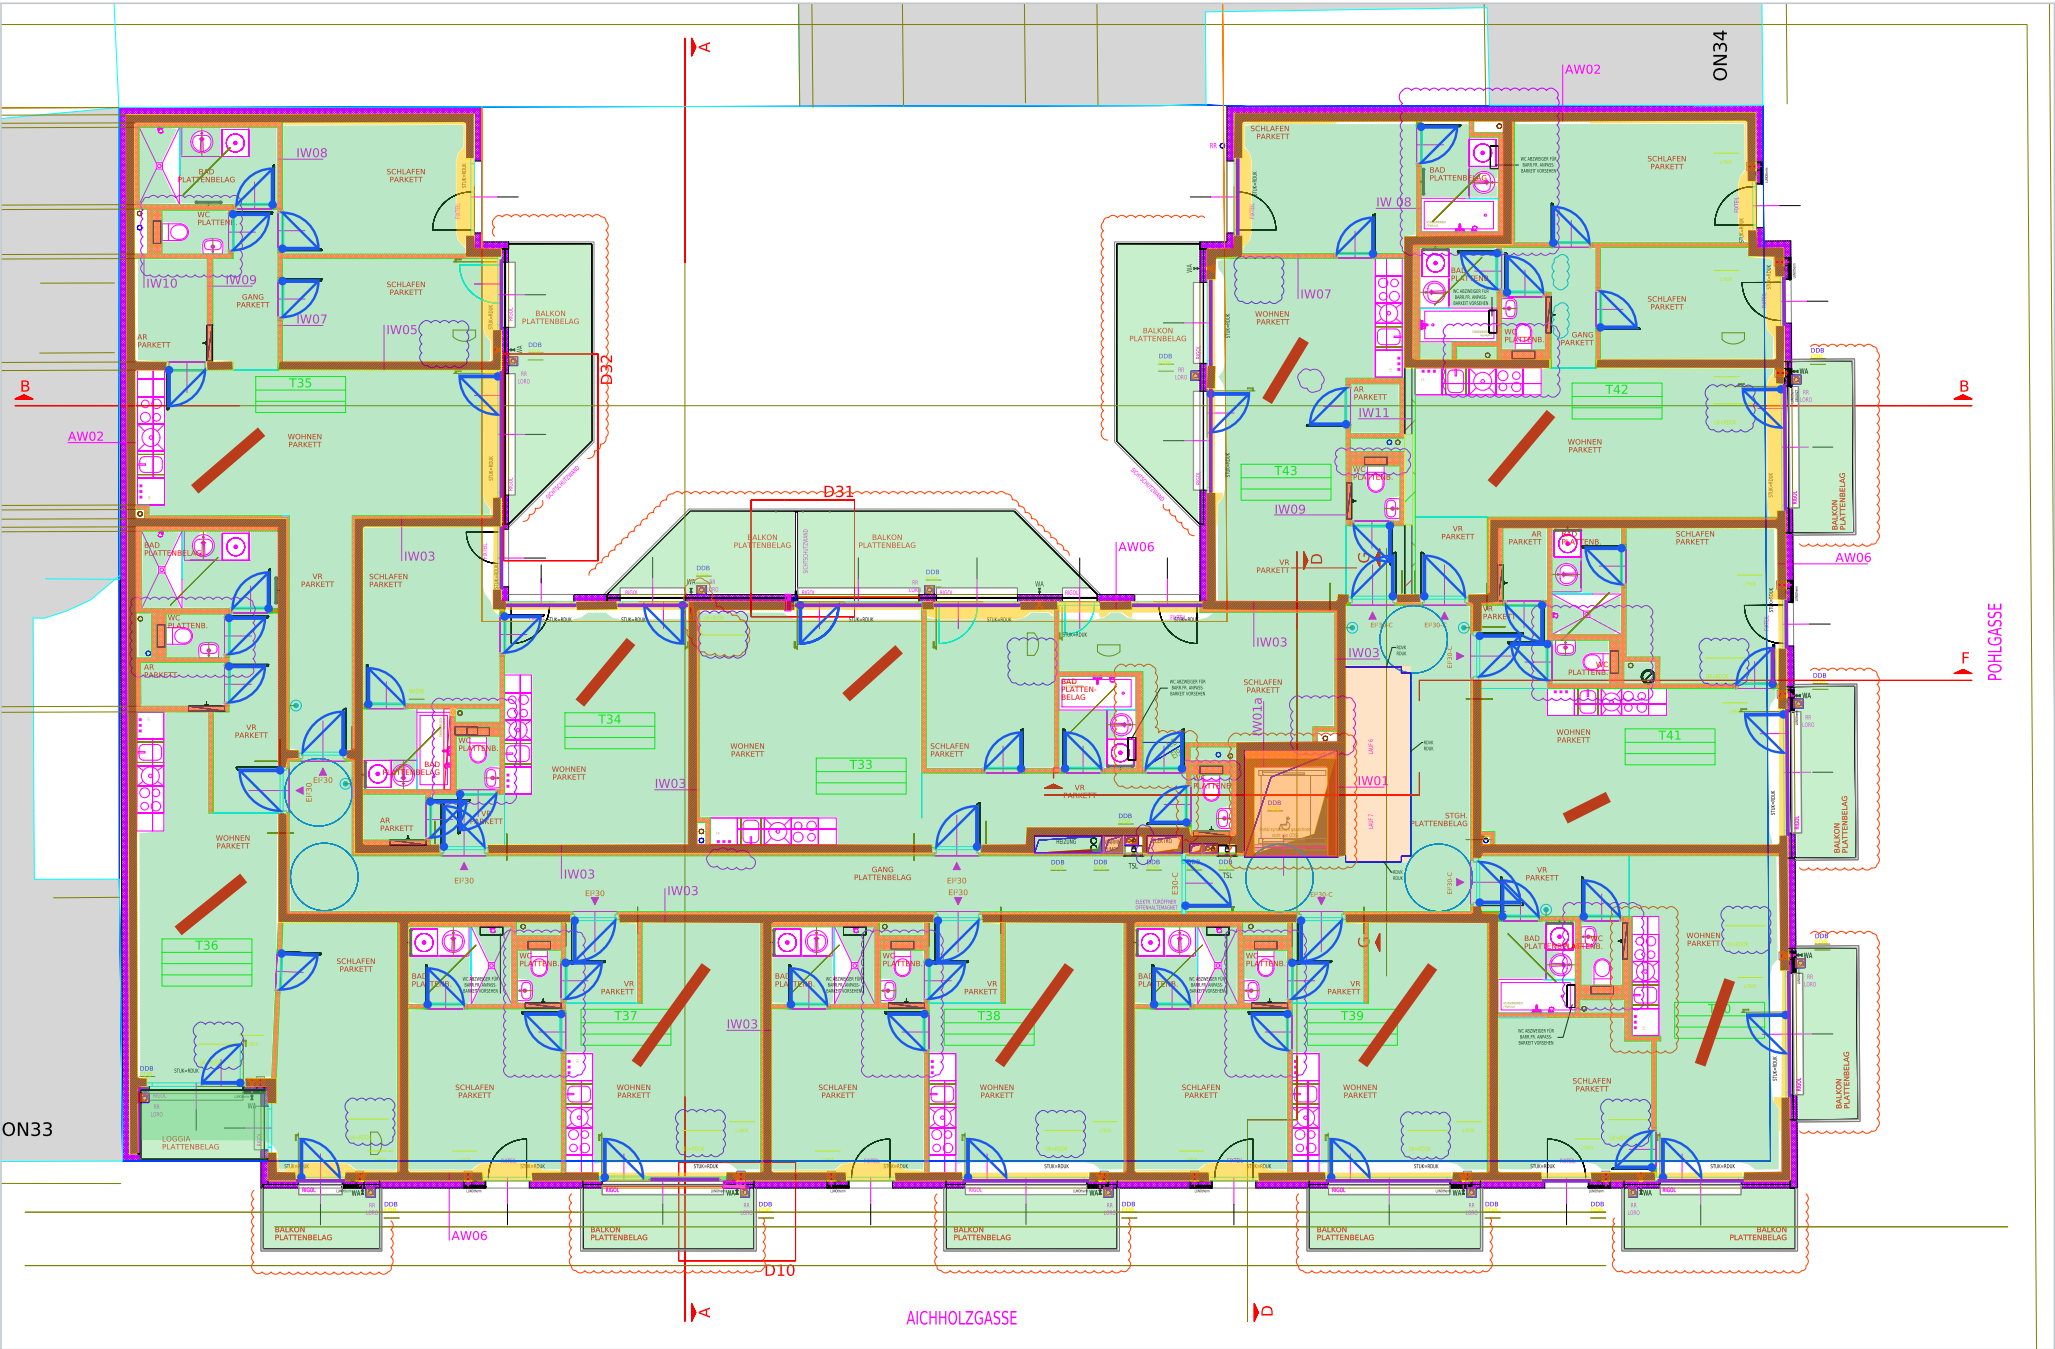

So liest du dieses Heft: Farben und Zeichen

Jede Farbe bedeutet im ganzen Heft immer dasselbe. Wenn du irgendwo Rot siehst, ist dort immer eine Wand – auf jeder Seite. Die Farben sind **durchsichtig**. Darunter siehst du immer noch die Originallinien des Plans. So lernst du, die Originallinien später auch ohne Farbe zu erkennen.

- DUNKELROT - dicke Wand**
Eine feste, massive Wand. Man kann nicht durch sie hindurchgehen. Im Plan: gelbe Umrandung, innen grüne Schrägstriche.
- HELLROT - dünne Wand**
Ebenfalls eine Wand, nur schmaler. Sie trennt meistens Räume innerhalb einer Wohnung. Im Plan: grüne Umrandung, orange Gitterstriche.
- ROSA - Dämmschicht außen**
Eine Schicht außen an der Außenwand, die gegen Kälte schützt. Sie gehört zur Wand. Im Plan: violettes Gittermuster.
- GRÜN - hier kann man gehen**
Fußboden innen, auf dem eine Person stehen und gehen kann.
- HELLGRÜN - begehbar im Freien**
Balkon oder Loggia: Boden draußen, erreichbar über eine Tür.
- GELB - Öffnung in der Außenwand**
Stelle, an der die Außenwand unterbrochen ist, weil dort ein Fenster oder eine Glastür sitzt.
- VIOLETT - Glas**
Die Linie, an der die Glasscheibe liegt. Glas lässt Licht durch, aber man kann nicht hindurchgehen.
- ORANGE - sonstige Bauteile**
Einbauten und Hindernisse: Küche, WC, Waschbecken, Schränke, Schächte, Aufzug, Treppenöffnung.
- TÜRKIS - Schrift und Planzeichen**
Rahmen um Texte, Nummern und Symbole. Das sind keine Bauteile, sondern Informationen.


Die Hilfszeichen

- 1

Nummer: verbindet die Stelle im Plan mit dem Erklärtext rechts.
- Rahmen: umschließt genau das Bauteil, das gerade erklärt wird.
- Pfeil mit Punkt: der Punkt sitzt genau auf dem gemeinten Element.
- Gestrichelt violett: eine gedachte Lage (z. B. die geschlossene Tür). Steht so nicht im Original.
- Türkiser Kreis: hier steht ein Text oder ein Symbol, das erklärt wird.

Und was bedeutet „weiß“?


Weiß heißt nur: **hier habe ich nichts eingefärbt**. Weiß heißt **nicht** automatisch „verboten“ oder „leer“. Unter einem Kasten, einem Bett oder einem Waschbecken ist natürlich auch Boden – aber dort kann man nicht einfach durchgehen, darum ist diese Stelle nicht grün.

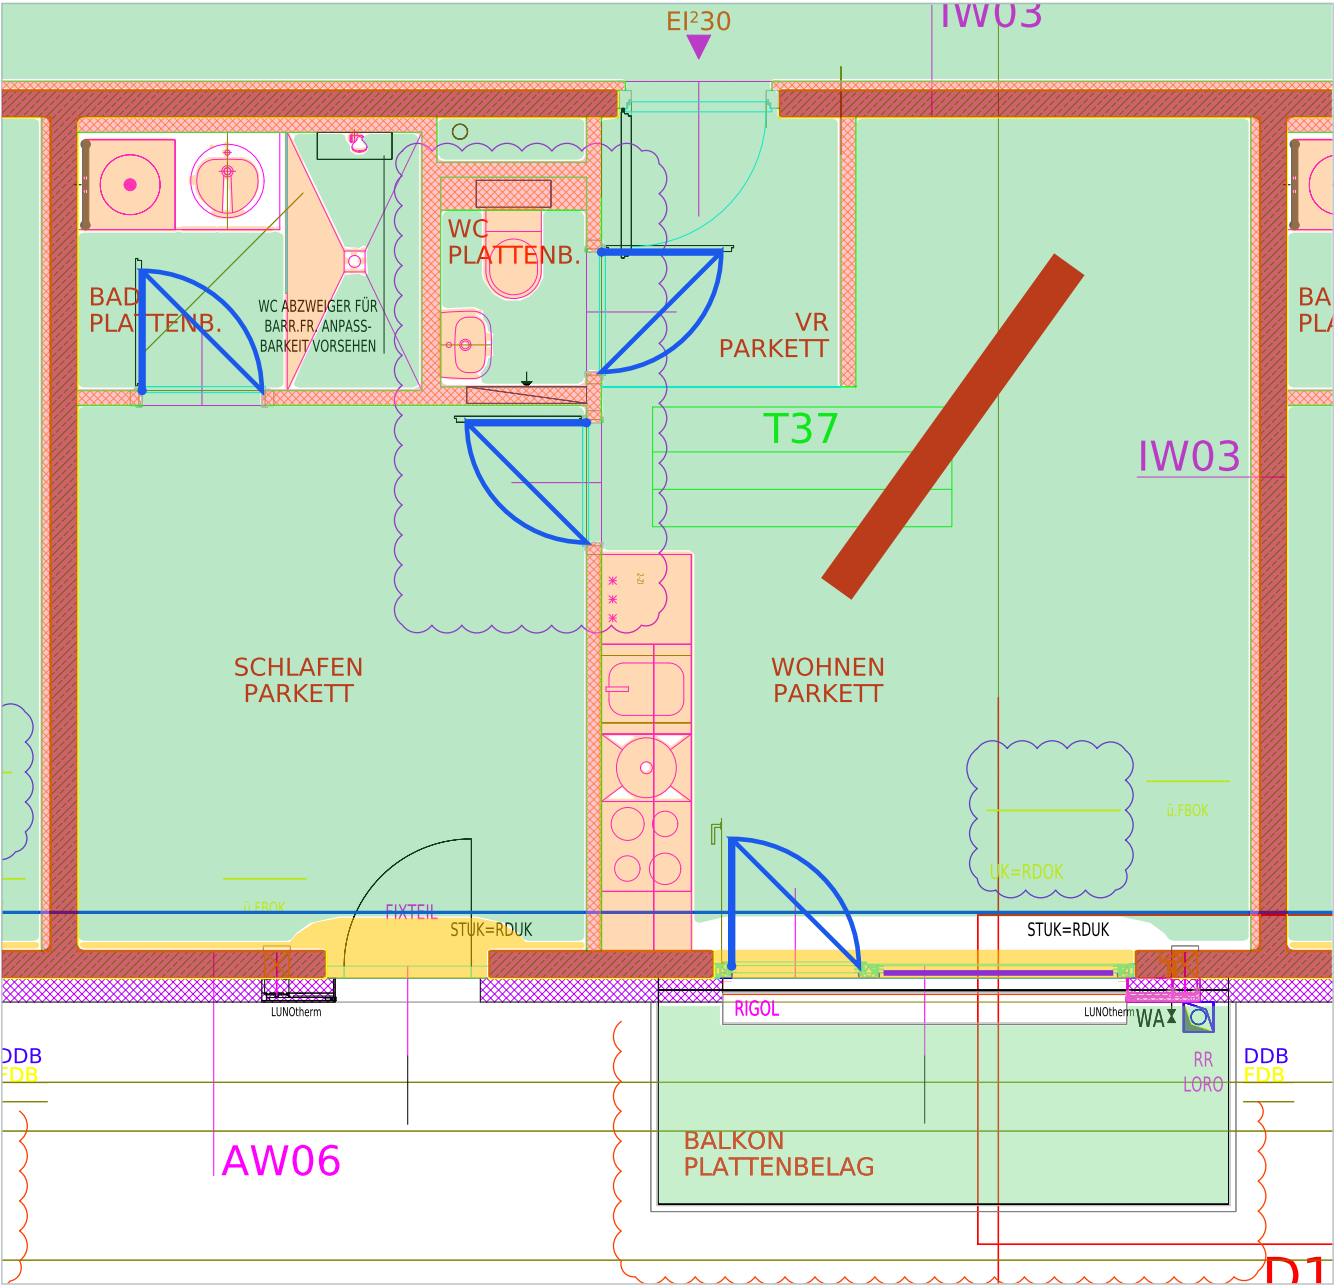


Beispiel: eine ganze Wohnung (Wohnung T37) mit allen Farben

Oben siehst du, wie das Farbsystem zusammenwirkt: **rote Wände** umschließen die Räume, **grüner Boden** füllt die Räume, **blaue Türbögen** zeigen, wo man von einem Raum in den nächsten kommt, **gelb/violett** markiert die Glasfront, **orange** sind Küche und Badeinrichtung. Hellgrün unten ist der Balkon. Diese Wohnung begleitet dich durch das ganze Heft.

Was ist ein Grundriss?

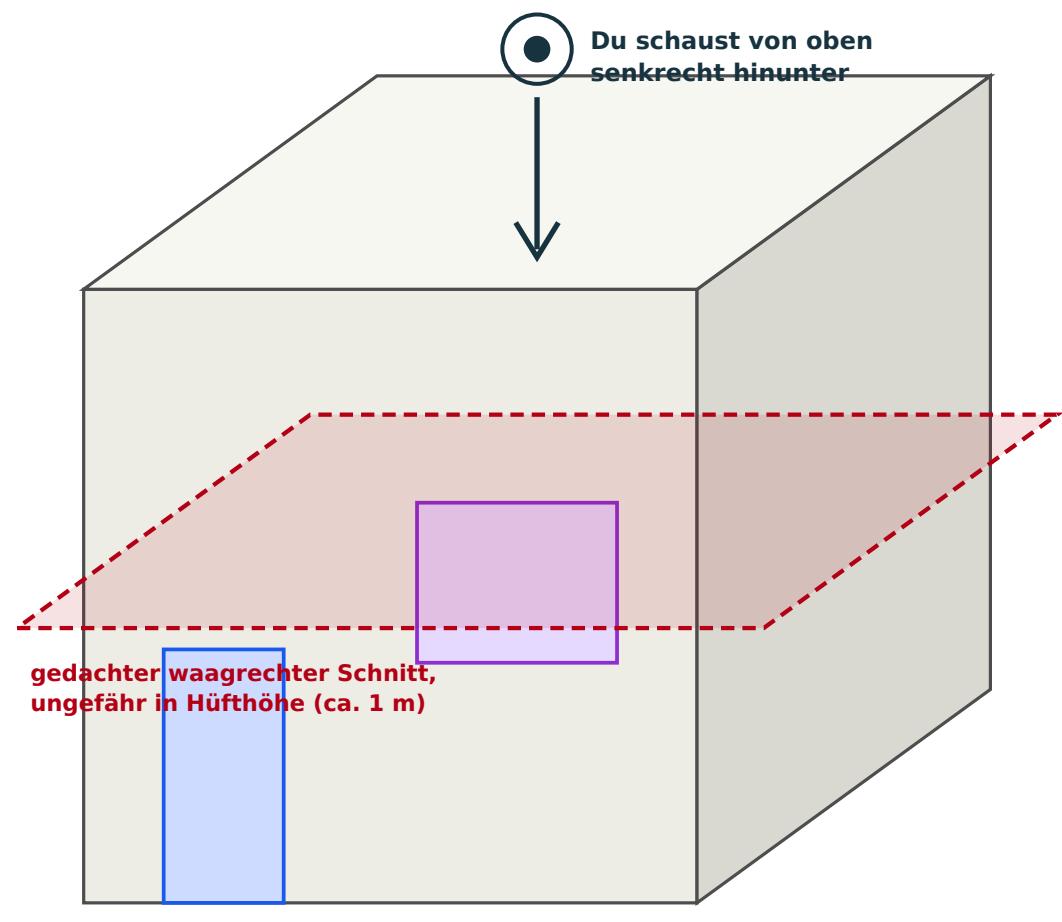

SCHRITT 1: Ein Haus von außen

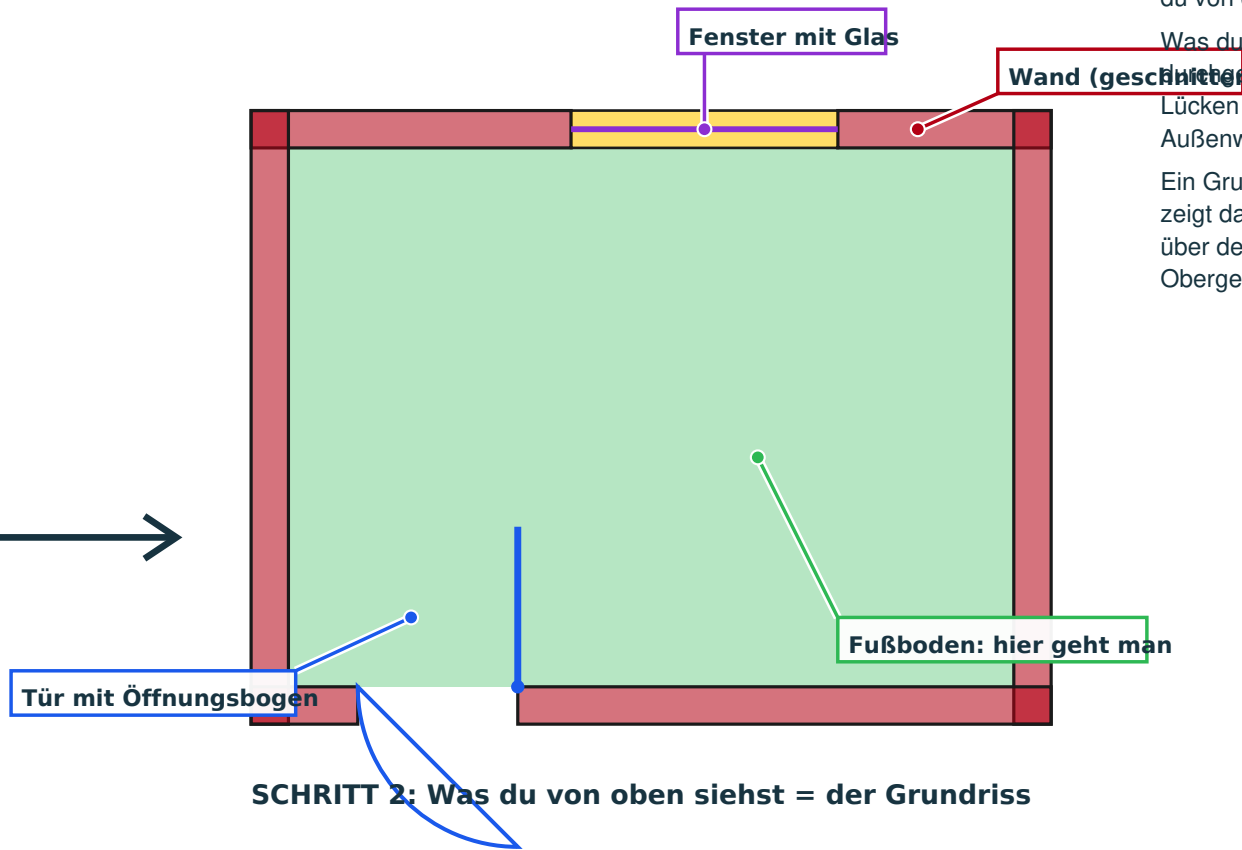

Grundriss = Blick von oben in ein aufgeschnittenes Haus

Stell dir vor, du schneidest ein Haus mit einem riesigen Messer **waagrecht** durch – ungefähr in Hüfthöhe. Den oberen Teil hebst du weg wie einen Deckel. Dann schaust du von oben senkrecht hinunter.

Was du dann siehst, ist ein **Grundriss**: die **Innenwände** geschnittenen Wände als dicke Streifen, Türen als Lücken in den Wänden, Fenster als schmale Linien in der Außenwand, und dazwischen den Fußboden.

Ein Grundriss zeigt immer **nur ein Stockwerk**. Dieses Heft zeigt das **3. Obergeschoss** – das ist das vierte Geschoss über dem Erdgeschoss (Erdgeschoss, 1., 2., 3. Obergeschoss).


Drei Dinge, die Anfänger oft verwechseln

- 1. Der Plan ist verkleinert.** Alles ist im gleichen Verhältnis kleiner gezeichnet. Dieser Plan heißt „ohne Maße“ – es sind keine Maßzahlen eingetragen, darum rechnen wir in diesem Heft keine Längen aus.
- 2. Dicke Striche sind nicht „wichtiger“, sondern „durchgeschnitten“.** Was der gedachte Schnitt trifft (Wände), wird kräftig gezeichnet. Was nur darunter auf dem Boden steht (Möbel, Waschbecken), wird dünn gezeichnet.
- 3. Linien sind keine Wege.** Nicht jede Linie ist eine Wand. Es gibt auch Linien für Bodenbeläge, Deckenkanten, Schnittlinien, Hinweise und Texte. Das Heft zeigt dir, wie du sie unterscheidest.

Die Zeichnung auf dieser Seite ist ein vereinfachtes Lernschema. Sie ist absichtlich nicht dem Gebäude nachgebildet. Ab der nächsten Seite arbeiten wir nur noch mit dem echten Plan.


Die Sprache der Linien: acht Dinge, die du immer wieder siehst

1. Dicke Wand

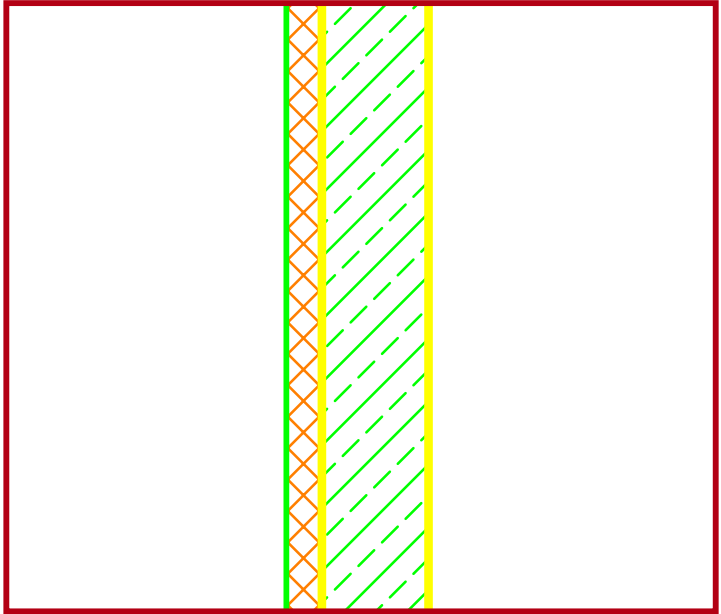


Gelbe Außenlinie, innen grüne Schrägstriche. Zwei parallele Kanten mit Material dazwischen = Wand.

2. Dünne Wand

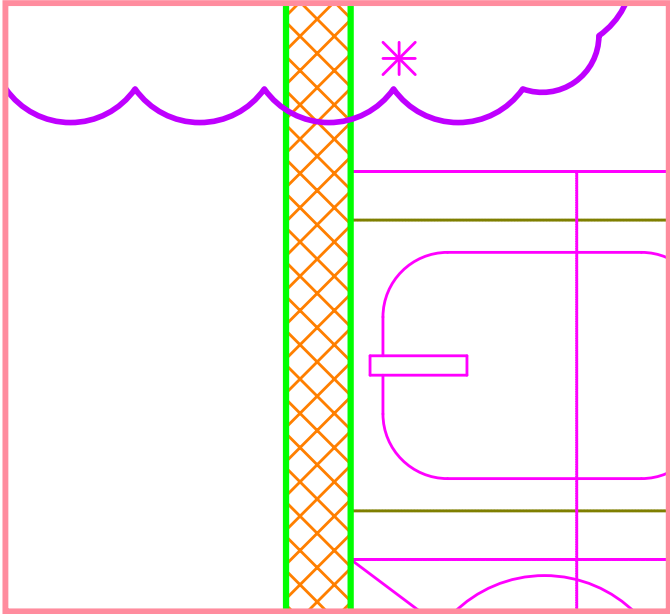


Grüne Außenlinie, innen orange Gitterstriche. Schmäler, aber genauso eine Wand.

3. Tür

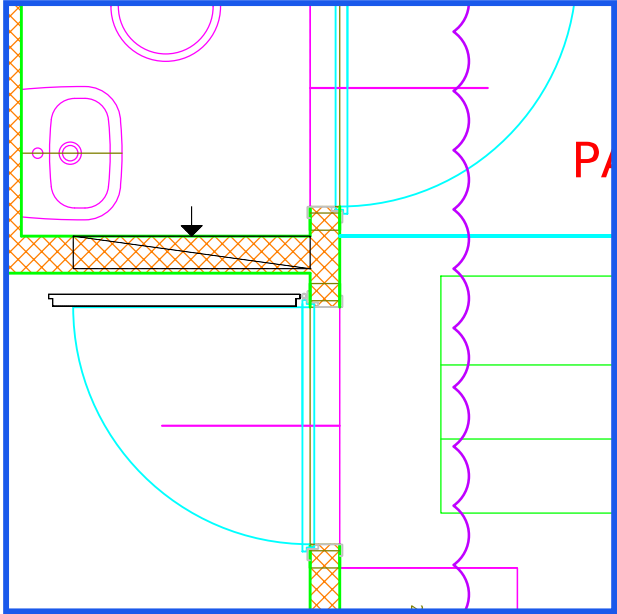

Lücke in der Wand + gerade Linie (Türblatt) + Viertelkreis (Öffnungsweg).

4. Glasfront

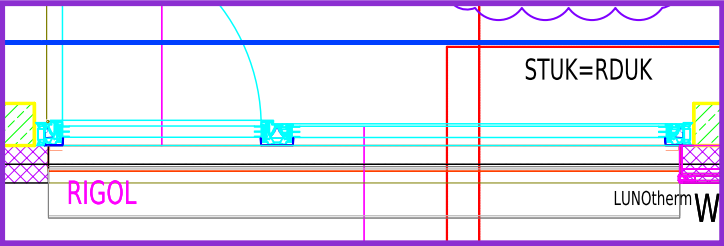


Mehrere sehr dünne, eng nebeneinander liegende hellblaue Linien in einer Lücke der Außenwand.

5. Raumstempel




Rote Schrift im Raum: oben der Raumname (WOHNEN), darunter der Bodenbelag (PARKETT).

6. Küchenzeile

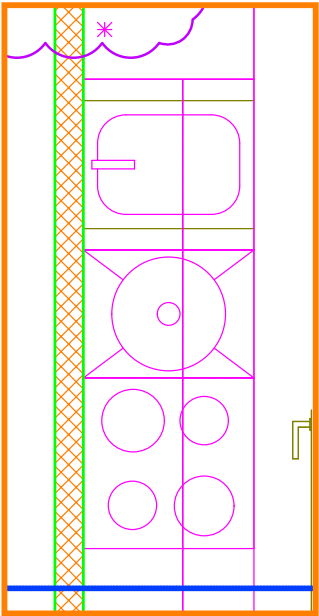


Dünne magenta Linien: Rechtecke mit Kreisen = Herdplatten, Rechteck mit Mulde = Spüle.

7. Bad und WC

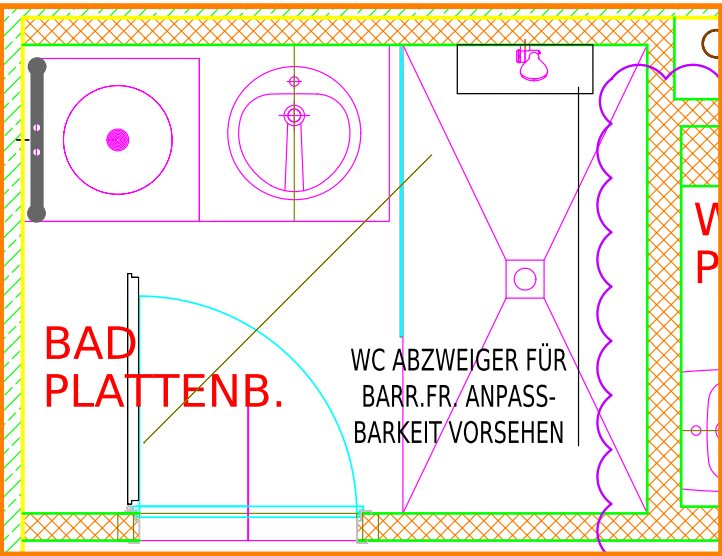

Ovale = WC-Schüssel, runde Formen in Rechtecken = Waschbecken. Dünn gezeichnet, weil sie am Boden stehen.


8. Wandtyp-Kürzel

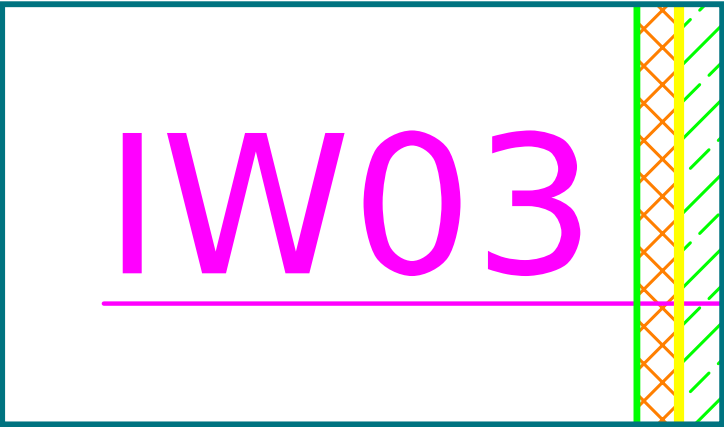

Magenta Schrift wie IW03: Nummer eines Wandtyps. Die genaue Bauart steht in einer anderen Unterlage.


DER AUSGANGSPLAN

Der Originalplan - unverändert

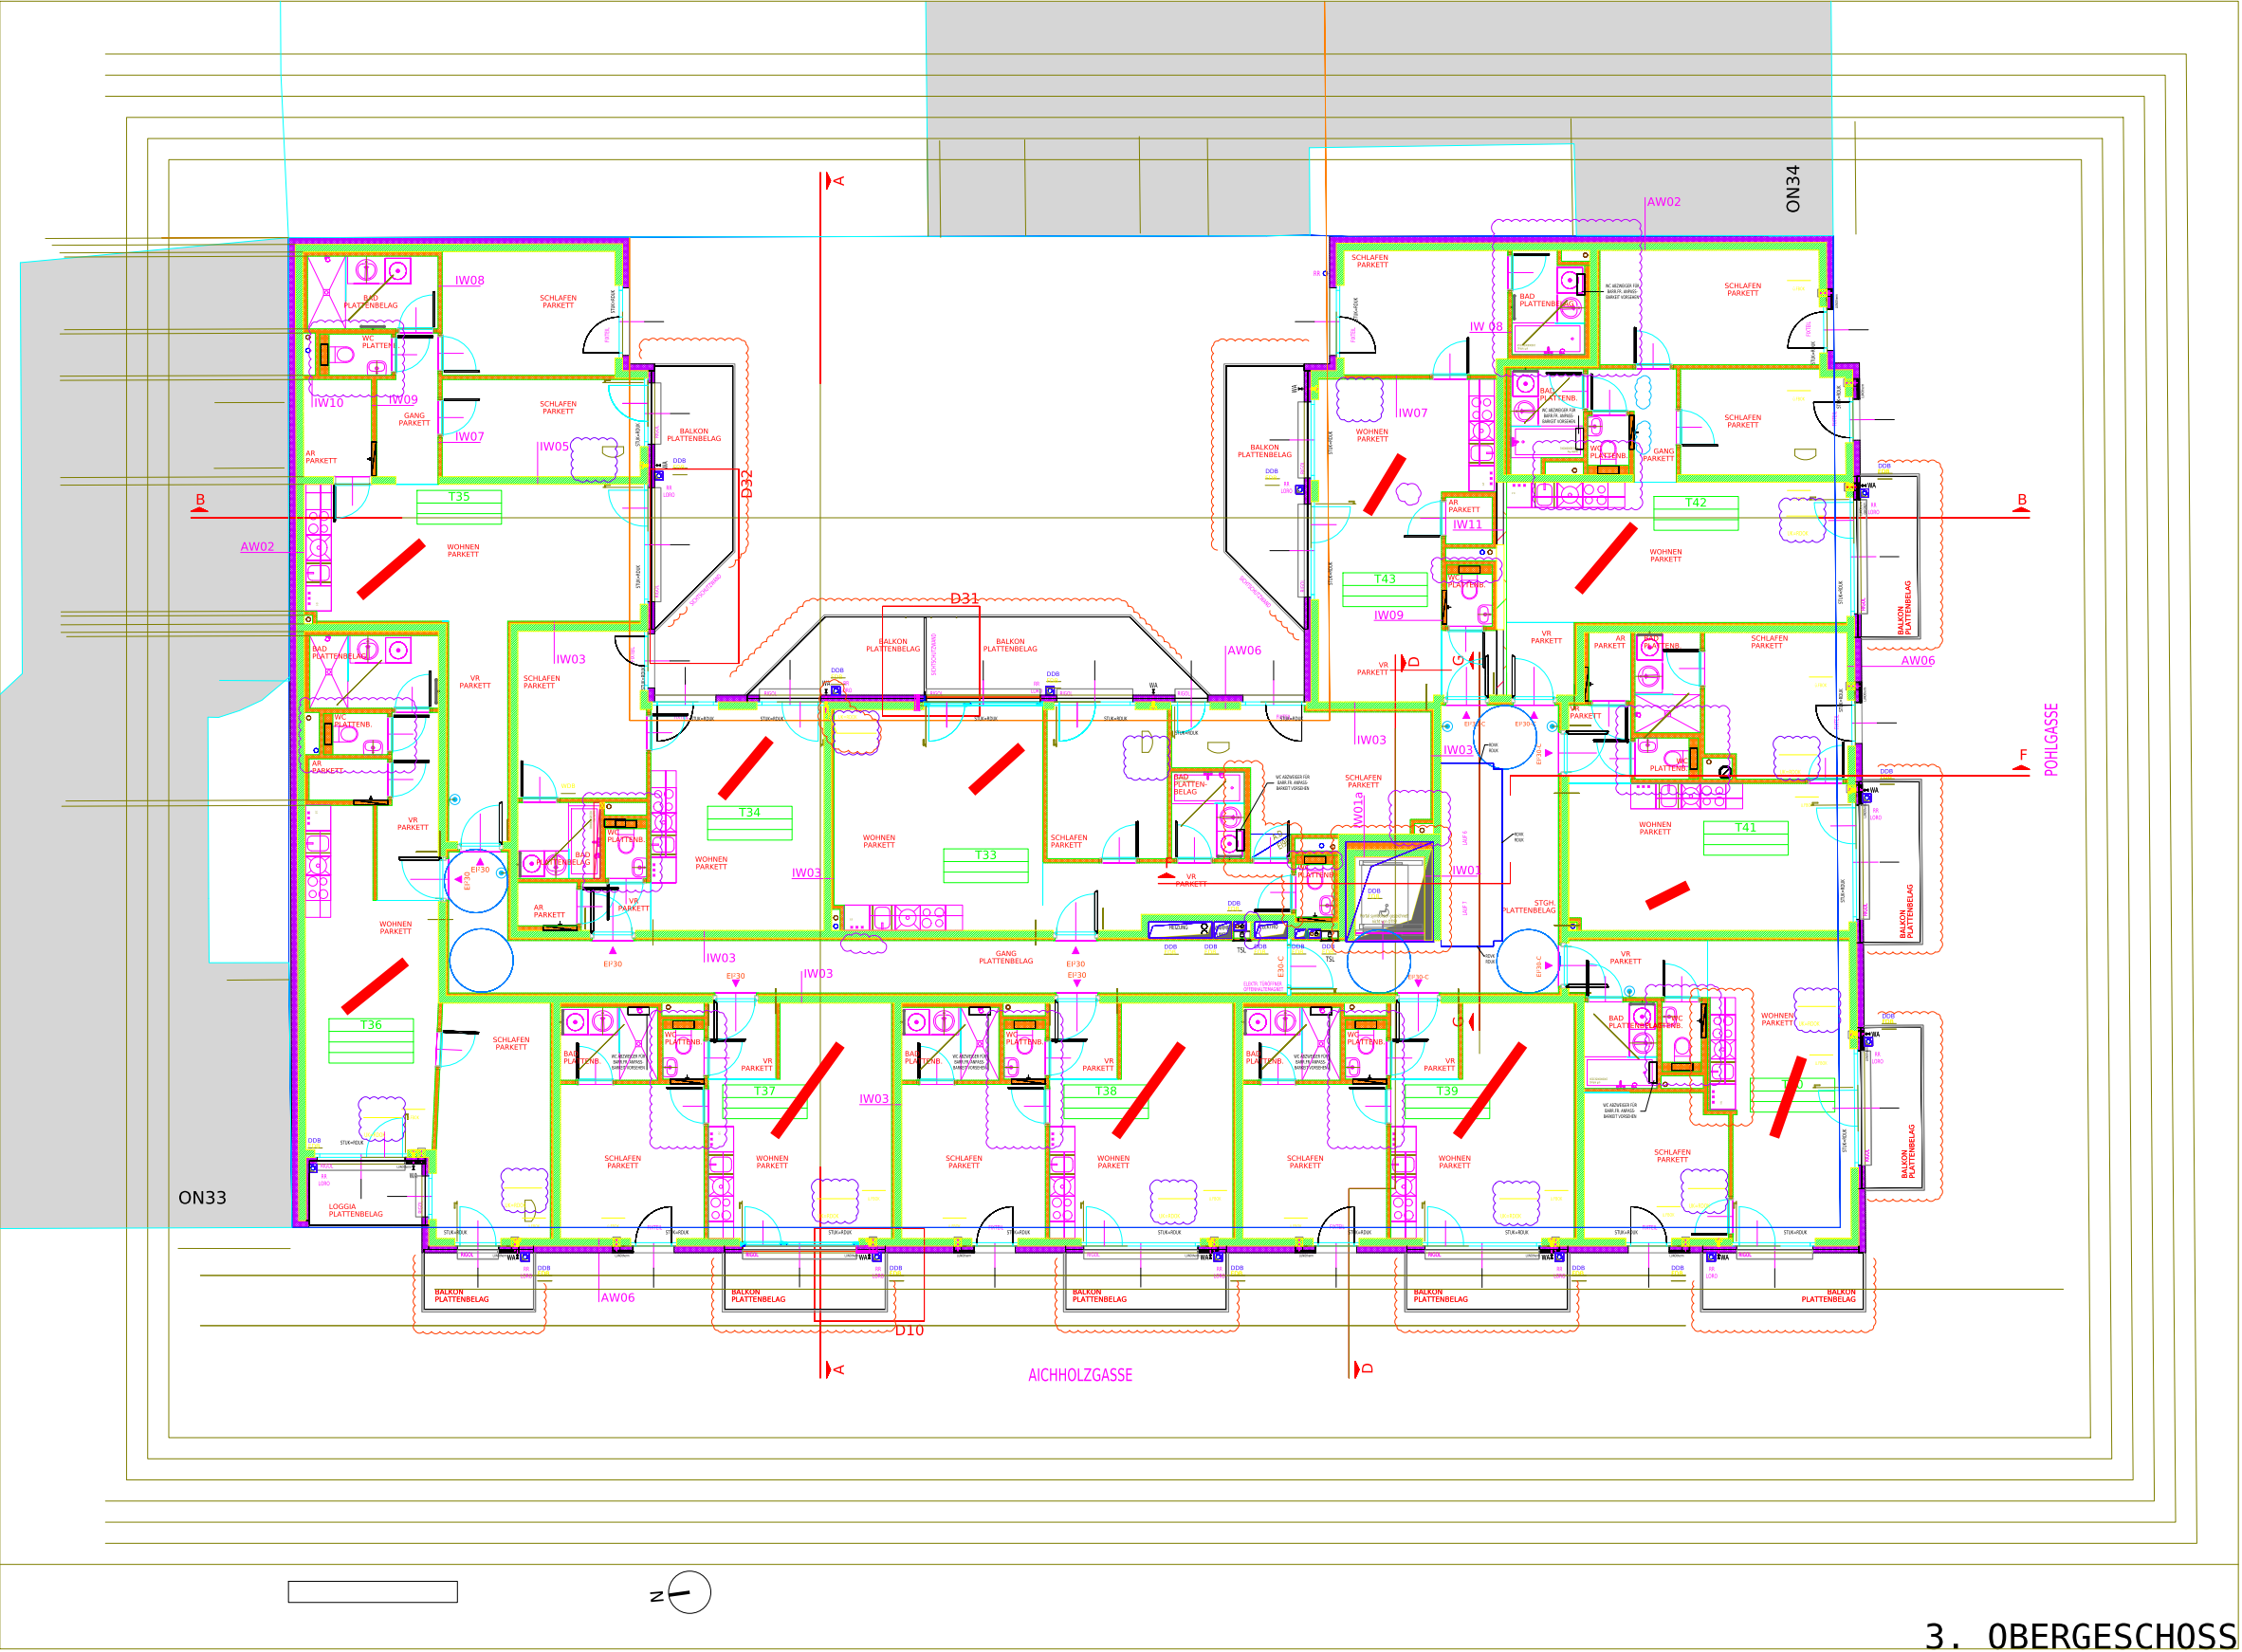

Keine Markierungen auf dieser Seite. So sieht der Plan aus, wenn du ihn ohne Hilfe bekommst.

Wo ist was? Die große Übersicht

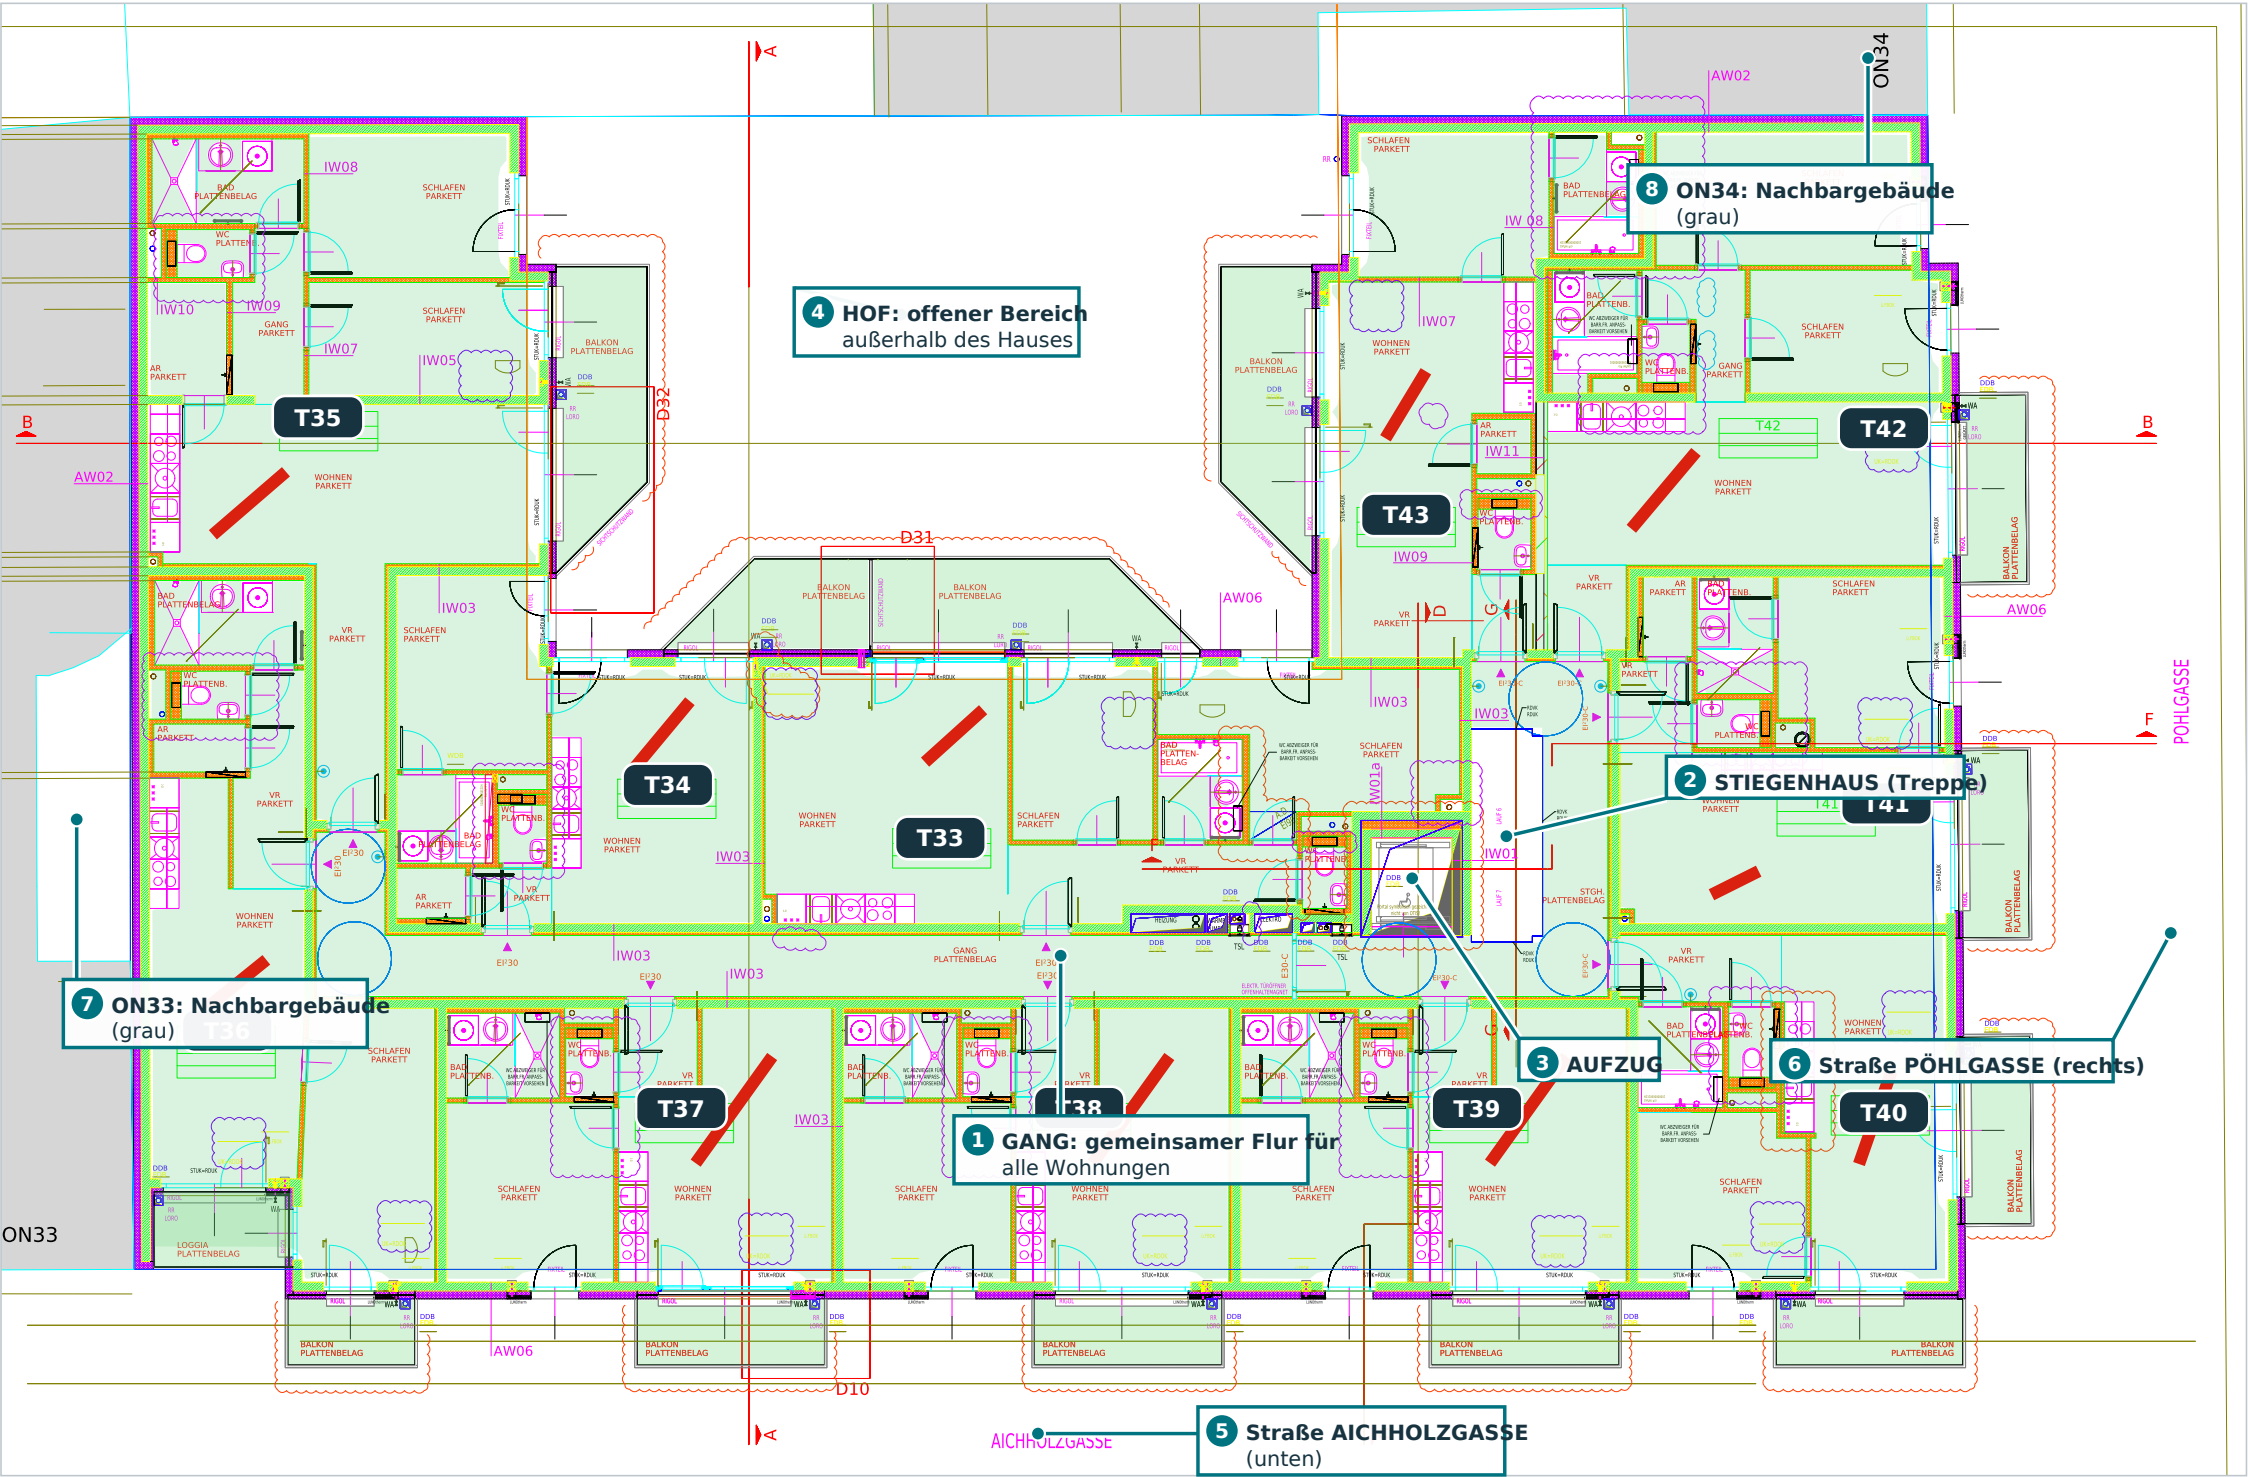

Das Gebäude von oben

Das Haus hat die Form eines **U**: zwei Flügel oben links und oben rechts, dazwischen ein offener **Hof** (weiß, nicht grün – dort ist kein Innenraum).

In diesem Geschoss liegen **11 Wohnungen**. Jede hat eine Nummer, die mit **T** beginnt (T33 bis T43). Im Plan stehen diese Nummern in **grüner Schrift** in einem kleinen Kasten. „T“ steht in Österreich für **Top** = Wohnungsnummer.

Bei der Wohnung rechts unten ist die Nummer im Original teilweise von einem roten Balken verdeckt; lesbar ist „T4...“. Aus der Reihenfolge ist T40 naheliegend, aber nicht sicher.


Alle Wohnungen erreicht man über den **Gang** (1). Der Gang ist mit dem **Stiegenhaus** (2) und dem **Aufzug** (3) verbunden – so kommt man von der Straße in dieses Stockwerk.

Die Namen der Straßen stehen außen am Plan (5, 6). So weißt du, auf welcher Seite des Hauses du gerade bist.

Die **grauen Flächen** am Rand (7, 8) sind Nachbarhäuser. Sie gehören nicht zu diesem Gebäude und sind darum nicht eingefärbt.

Grün ist hier nur blass angedeutet. Die genaue Gehfläche kommt später auf einer eigenen Seite.

Alle Wände im Überblick - rot

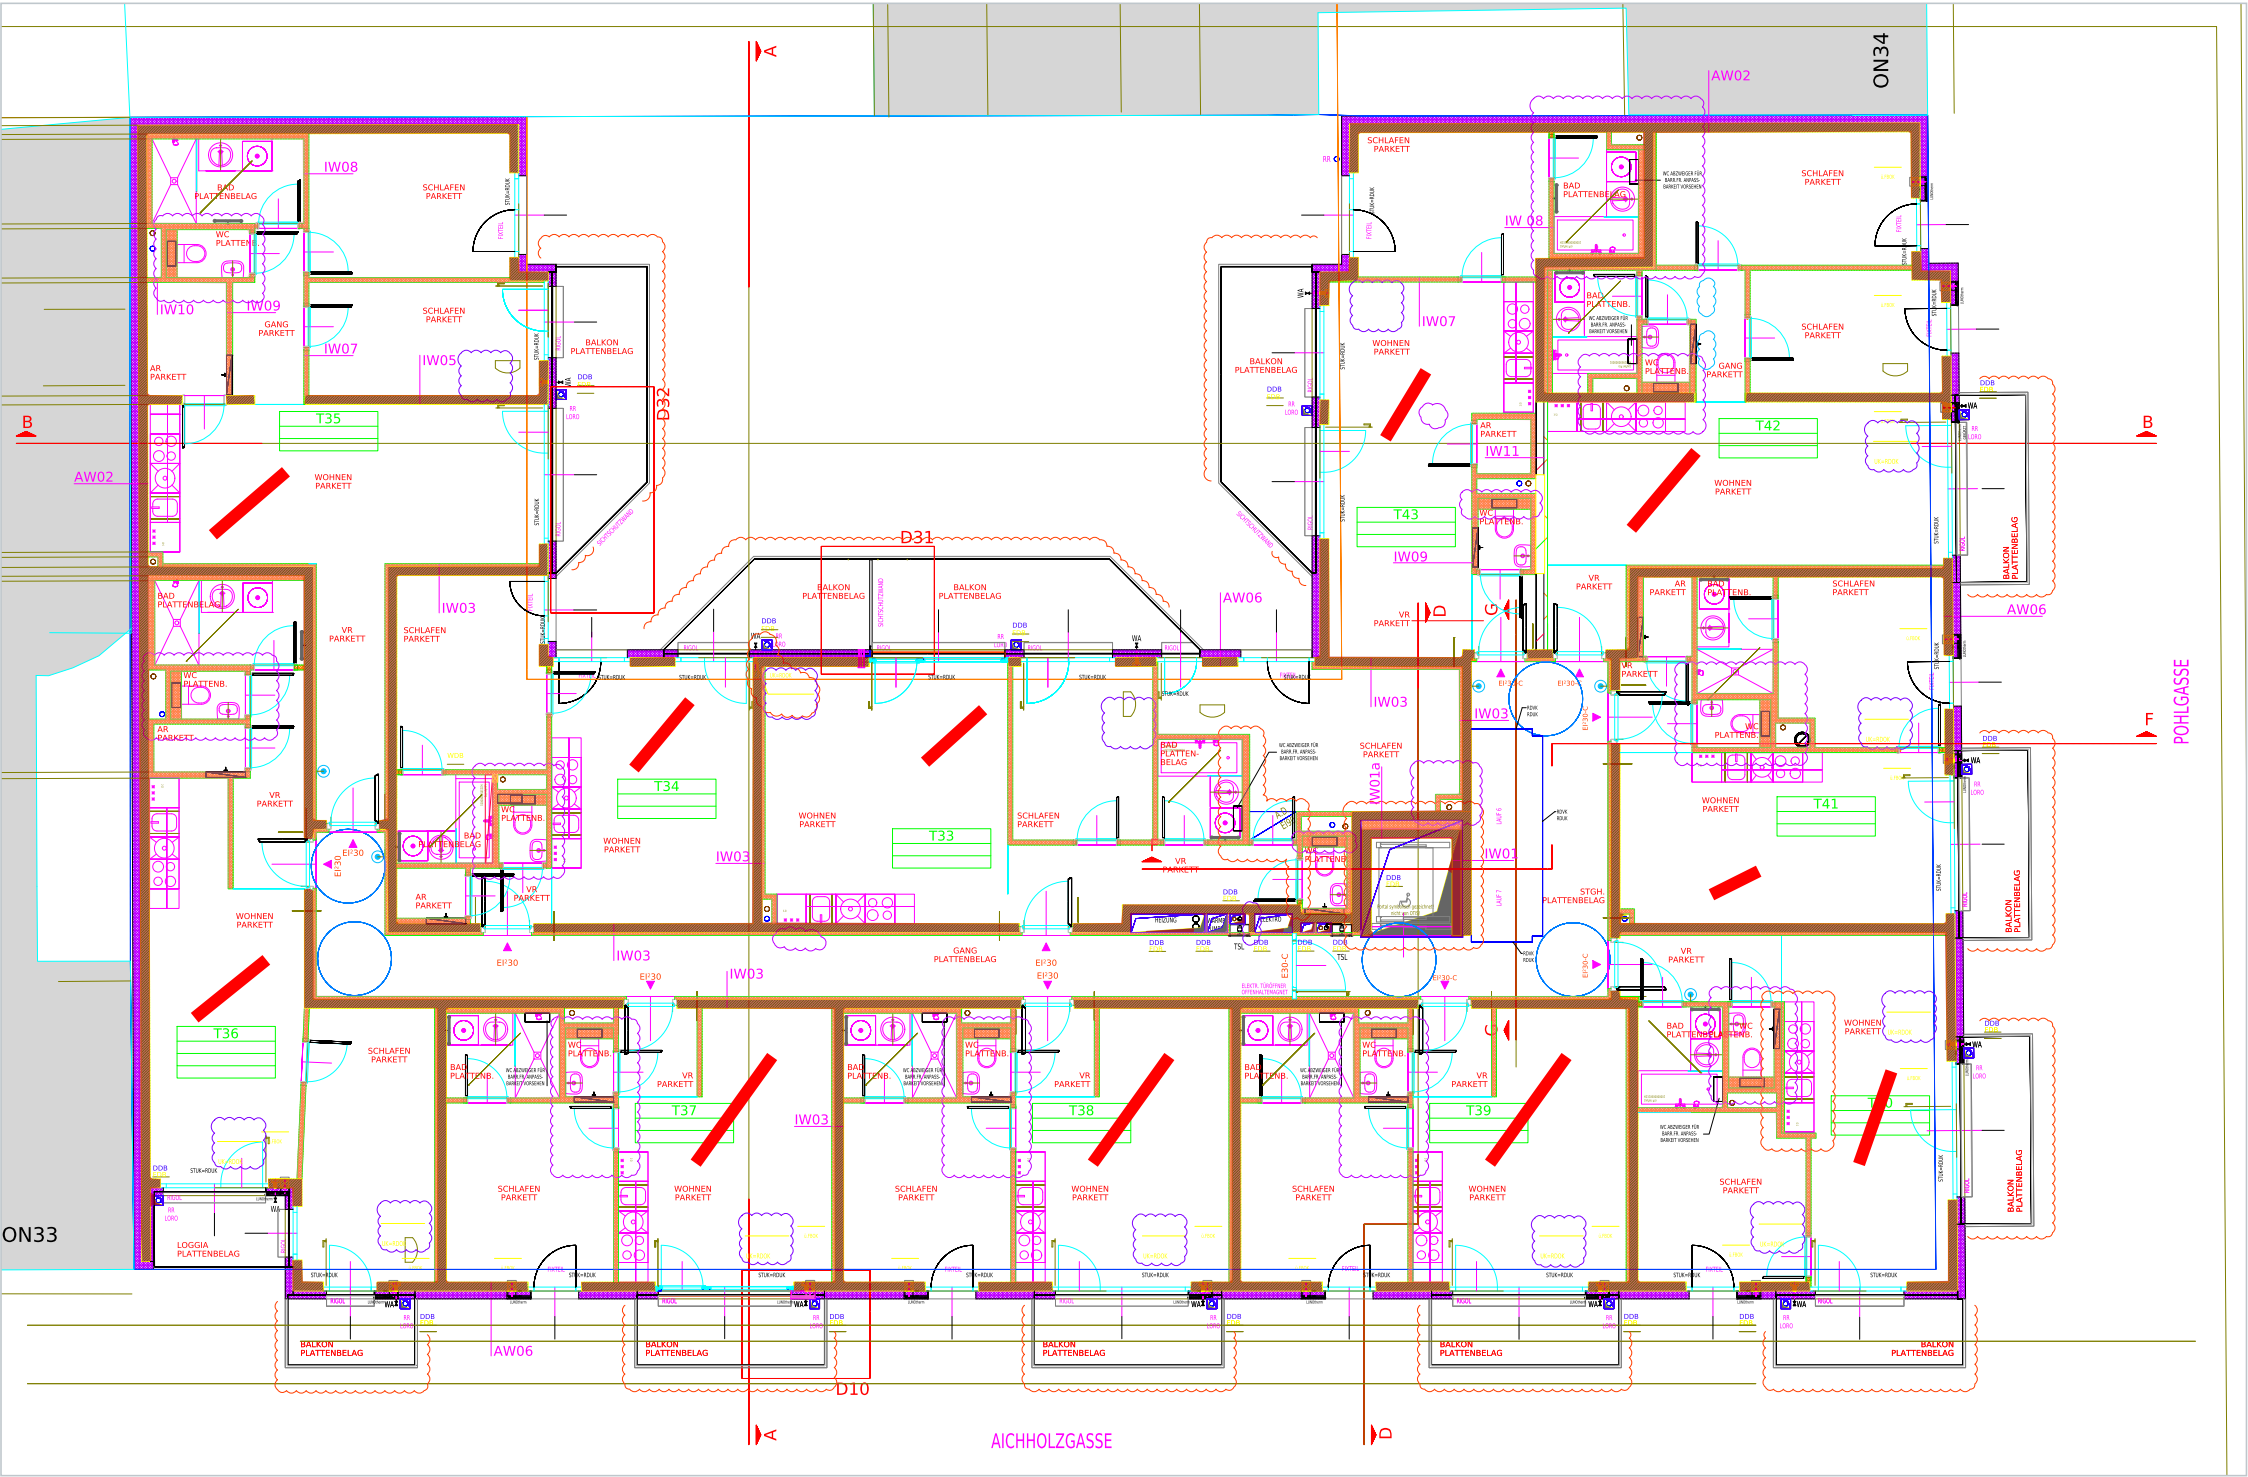

Was ist eine Wand?

Eine Wand ist ein fester, senkrechter Bauteil – zum Beispiel aus Beton oder Ziegel. Sie **trennt** zwei Bereiche voneinander. Man kann **nicht** durch sie hindurchgehen.

Wie sieht eine Wand im Grundriss aus?

Weil der Grundriss ein waagrechter Schnitt ist, siehst du die Wand von oben als **Streifen**: zwei parallele Linien (die beiden Wandseiten), und dazwischen ein Muster (die Schraffur). Das Muster sagt: „Hier ist Material.“

Woran erkenne ich die Wände in diesem Plan?

Dieser Plan benutzt zwei Darstellungen:

Dunkelrot = Streifen mit **gelber** Umrandung und **grünen Schrägstrichen**. Das sind die dicken Wände: Außenwände, Wände zwischen den Wohnungen, Wände am Gang und am Stiegenhaus.

Hellrot = Streifen mit **grüner** Umrandung und **oranen Gitterstrichen**. Das sind die dünnen Wände innerhalb einer Wohnung, z. B. rund um Bad und WC.


Rosa = außen an der Fassade ein violettes Gittermuster: die Dämmschicht.

Wo die rote Farbe aufhört

Überall, wo das Rot **unterbrochen** ist, ist eine Öffnung: eine Tür (innen) oder ein Fenster/eine Glastür (außen). Diese Lücken lernst du auf den nächsten Seiten kennen.

Ob eine Wand **tragend** ist (also das Haus stützt), steht nicht im Plan. Dicke Wände sind oft tragend – das ist aber nur eine Vermutung und hier nicht belegt.

Die Außenwand: ein Paket aus mehreren Schichten

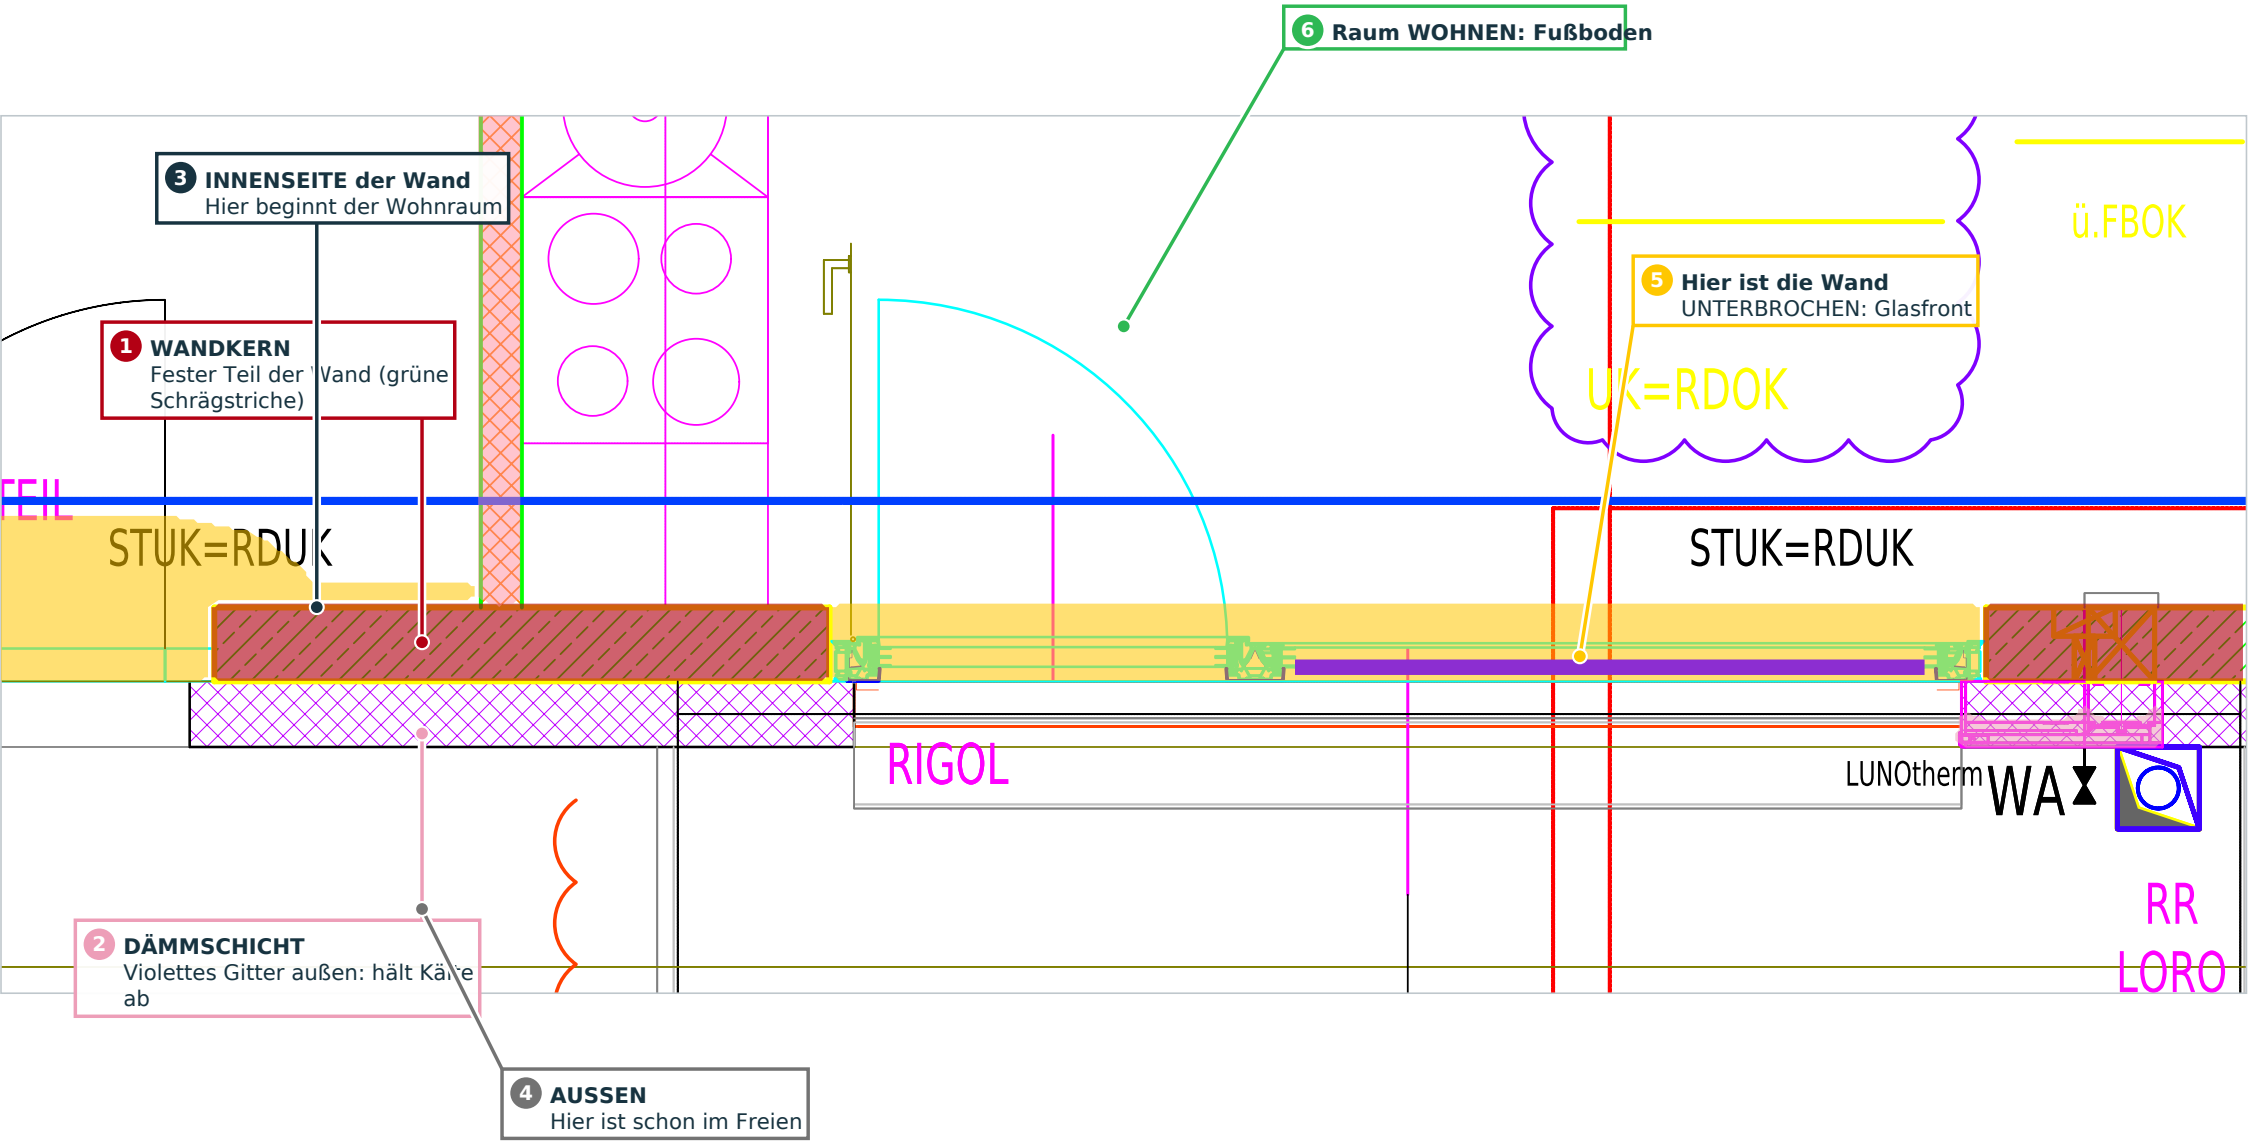

Was ist eine Außenwand?

Die Außenwand ist die Wand zwischen **drinnen** und **draußen**. Sie hält Regen, Wind und Kälte ab.

Wie sieht sie hier aus?

Schau auf den unteren Streifen: Von oben (innen) nach unten (außen) liegen zwei Schichten übereinander:

- (1) **Wandkern** – gelbe Linien außen herum, grüne Schrägstriche innen. Das ist der feste, tragfähige Teil.
- (2) **Dämmschicht** – ein violettes Gittermuster. Das ist eine weiche Schicht gegen Kälte. Sie ist fest mit der Wand verbunden. Man kann dort also auch nicht gehen.


Woran erkenne ich es hier?

Die Linie (3) ist die Innenseite. Alles darüber ist Raum. Die Linie ganz unten (4) ist die Außenseite. Alles darunter ist schon draußen.

Bei (5) hört das Muster plötzlich auf. Dort gibt es keine Schraffur, sondern nur dünne Linien – das ist eine Glasfront mit Tür (siehe Kapitel Fenster).

Aus welchem Material der Kern genau ist (z. B. Beton oder Ziegel), sagt der Plan ohne Legende nicht sicher.

Dicke Wand oder dünne Wand? So unterscheidest du sie

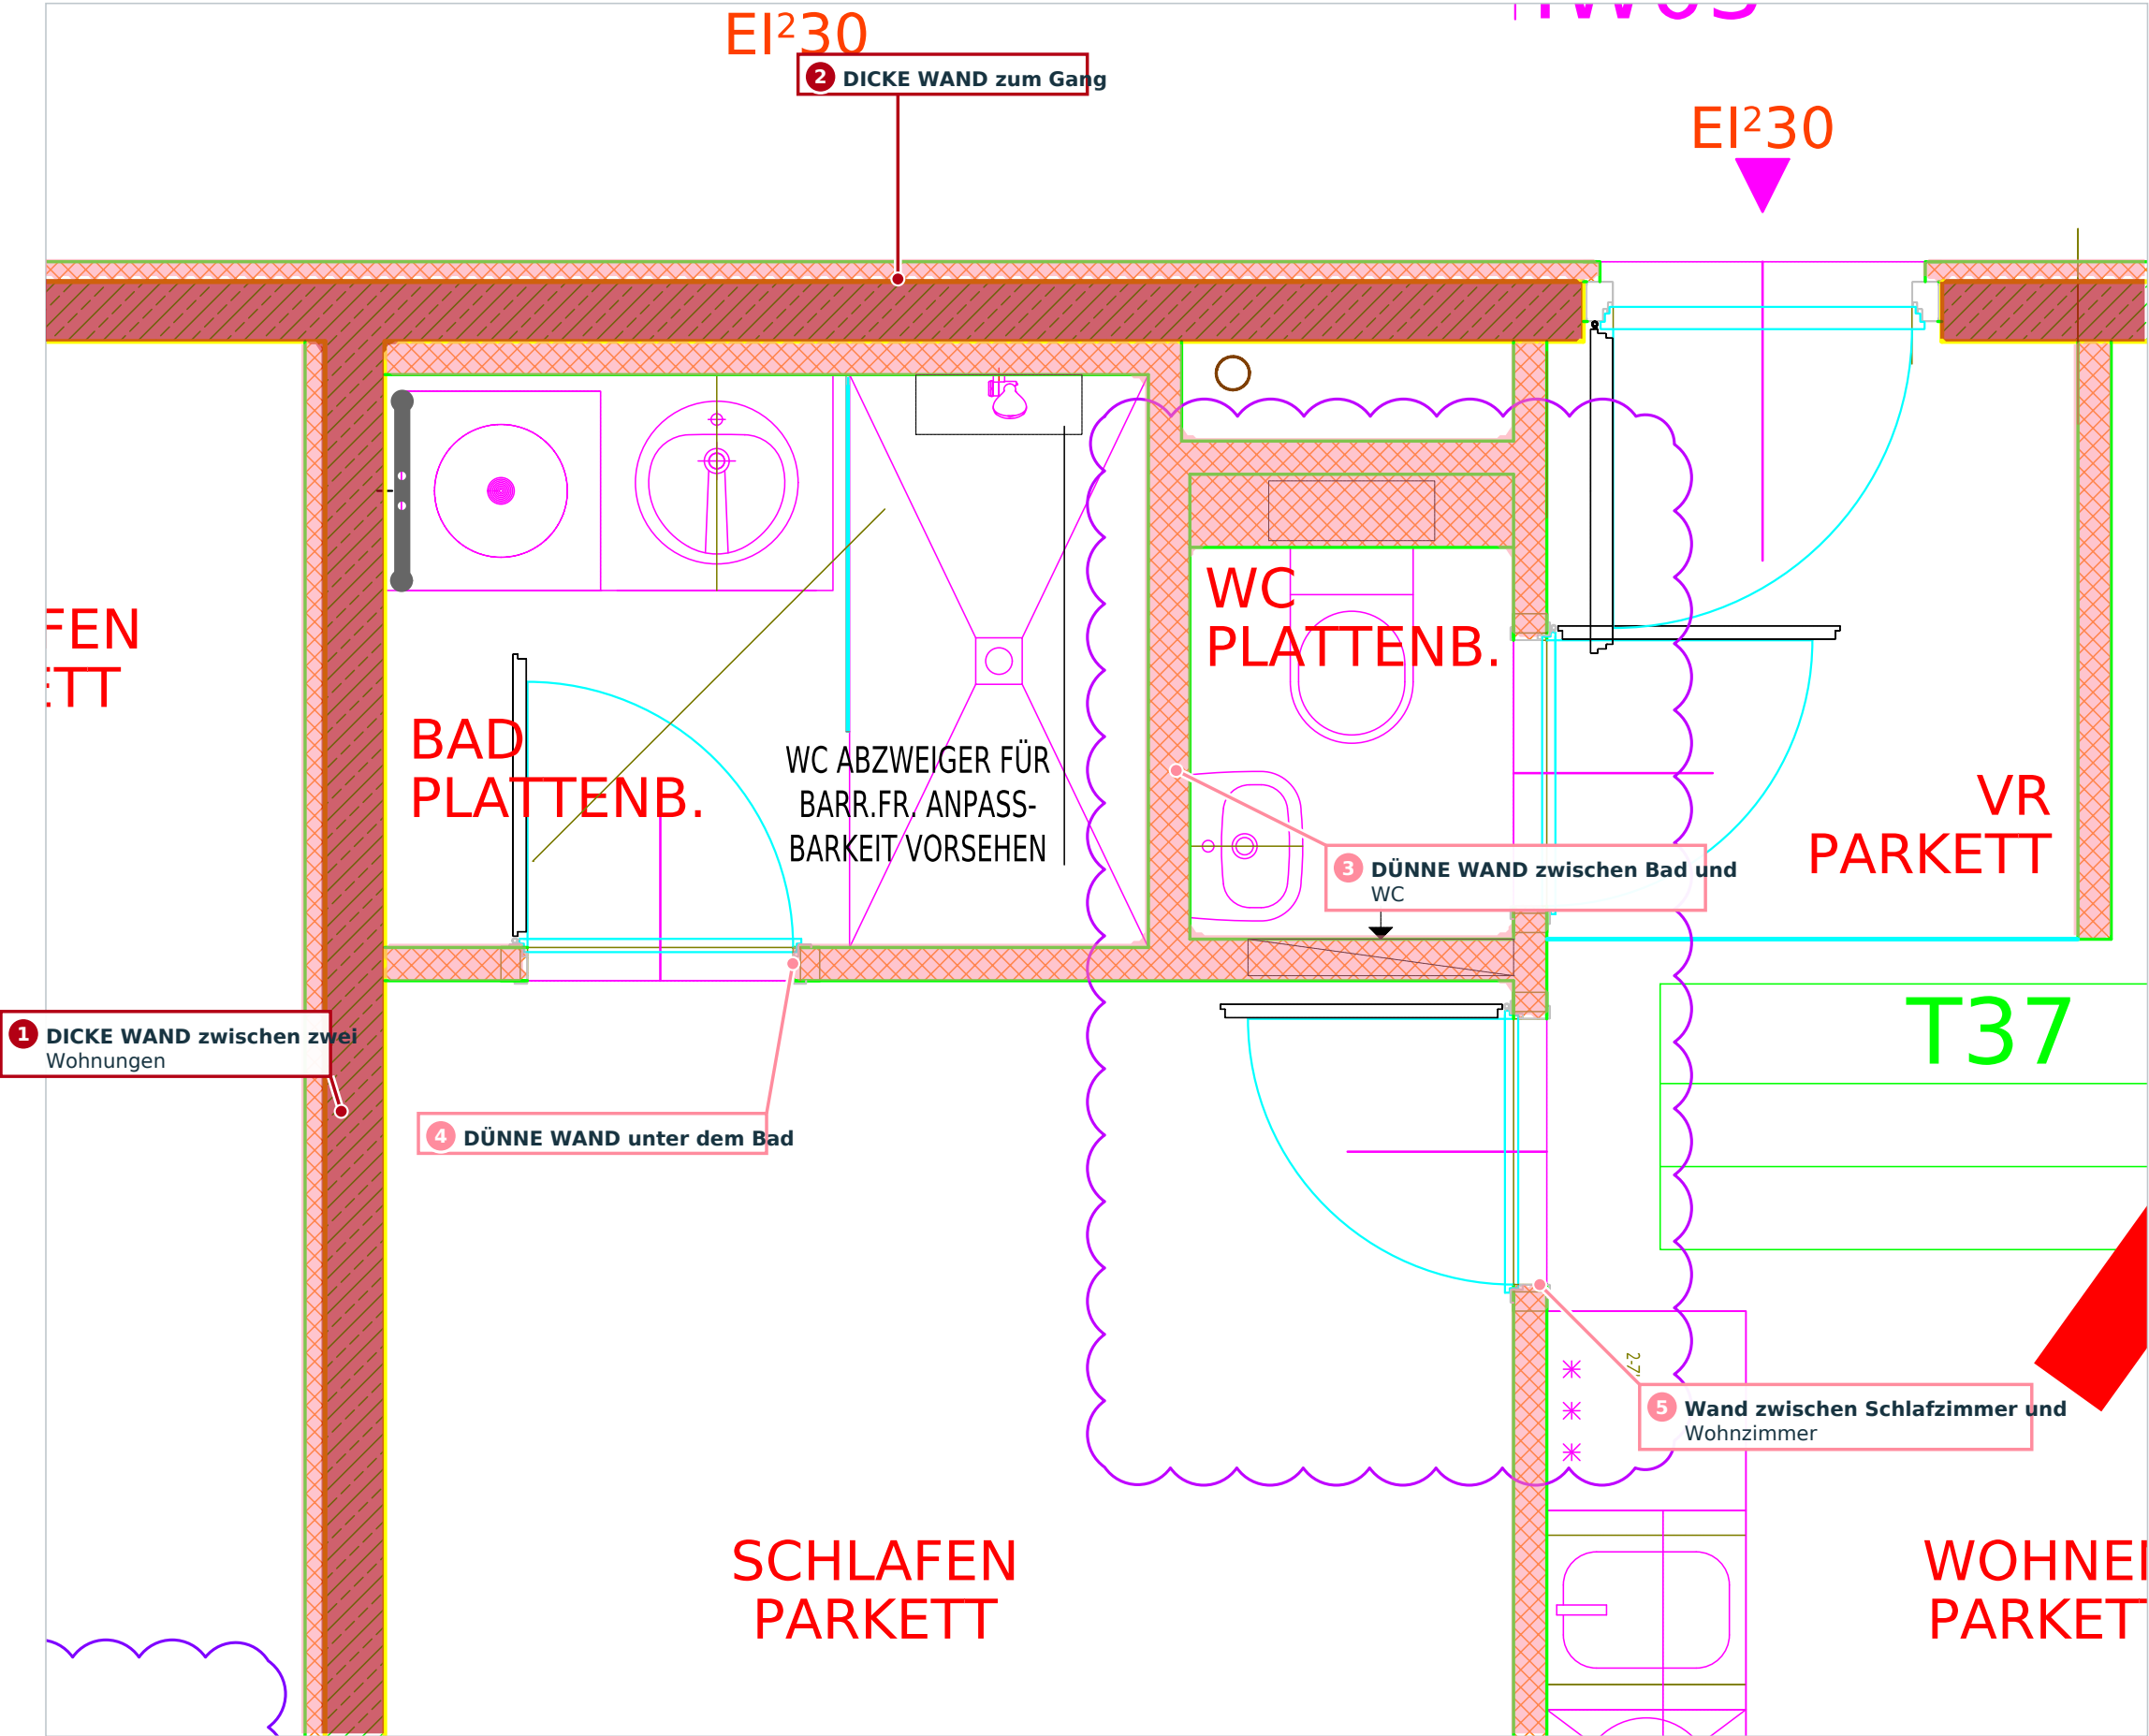

Zwei Arten, beide sind Wände

In diesem Plan sind die Wände in zwei Arten gezeichnet. Für dich als Anfänger ist das Wichtigste: **Beide sind Wände**. Durch beide kann man nicht hindurchgehen.

Dicke Wand (dunkelrot)

Was: eine kräftige, massive Wand. **Wie:** ein breiter Streifen mit gelber Außenlinie und grünen Schrägstrichen. **Hier:** (1) trennt die Wohnung T37 von der Nachbarwohnung, (2) trennt die Wohnung vom Gang.

Dünne Wand (hellrot)


Was: eine schmalere Trennwand innerhalb der Wohnung. **Wie:** ein schmaler Streifen mit grüner Außenlinie und orangen Gitterstrichen. **Hier:** (3) und (4) umschließen Bad und WC.

Der Trick zum Erkennen

Schau immer auf **drei Dinge gemeinsam**: zwei parallele Linien, ein Muster dazwischen, und dass der Streifen an andere Wände anschließt. Eine einzelne dünne Linie ohne Muster ist meistens **keine** Wand.

Die Wandtypen haben Kürzel wie IW03 (siehe Seite „Schrift und Planzeichen“). Welche Bauart dahintersteckt, steht in einem Wandkatalog, der hier nicht beiliegt.

Alle Türen im Überblick - blau und nummeriert (66 Türblätter)

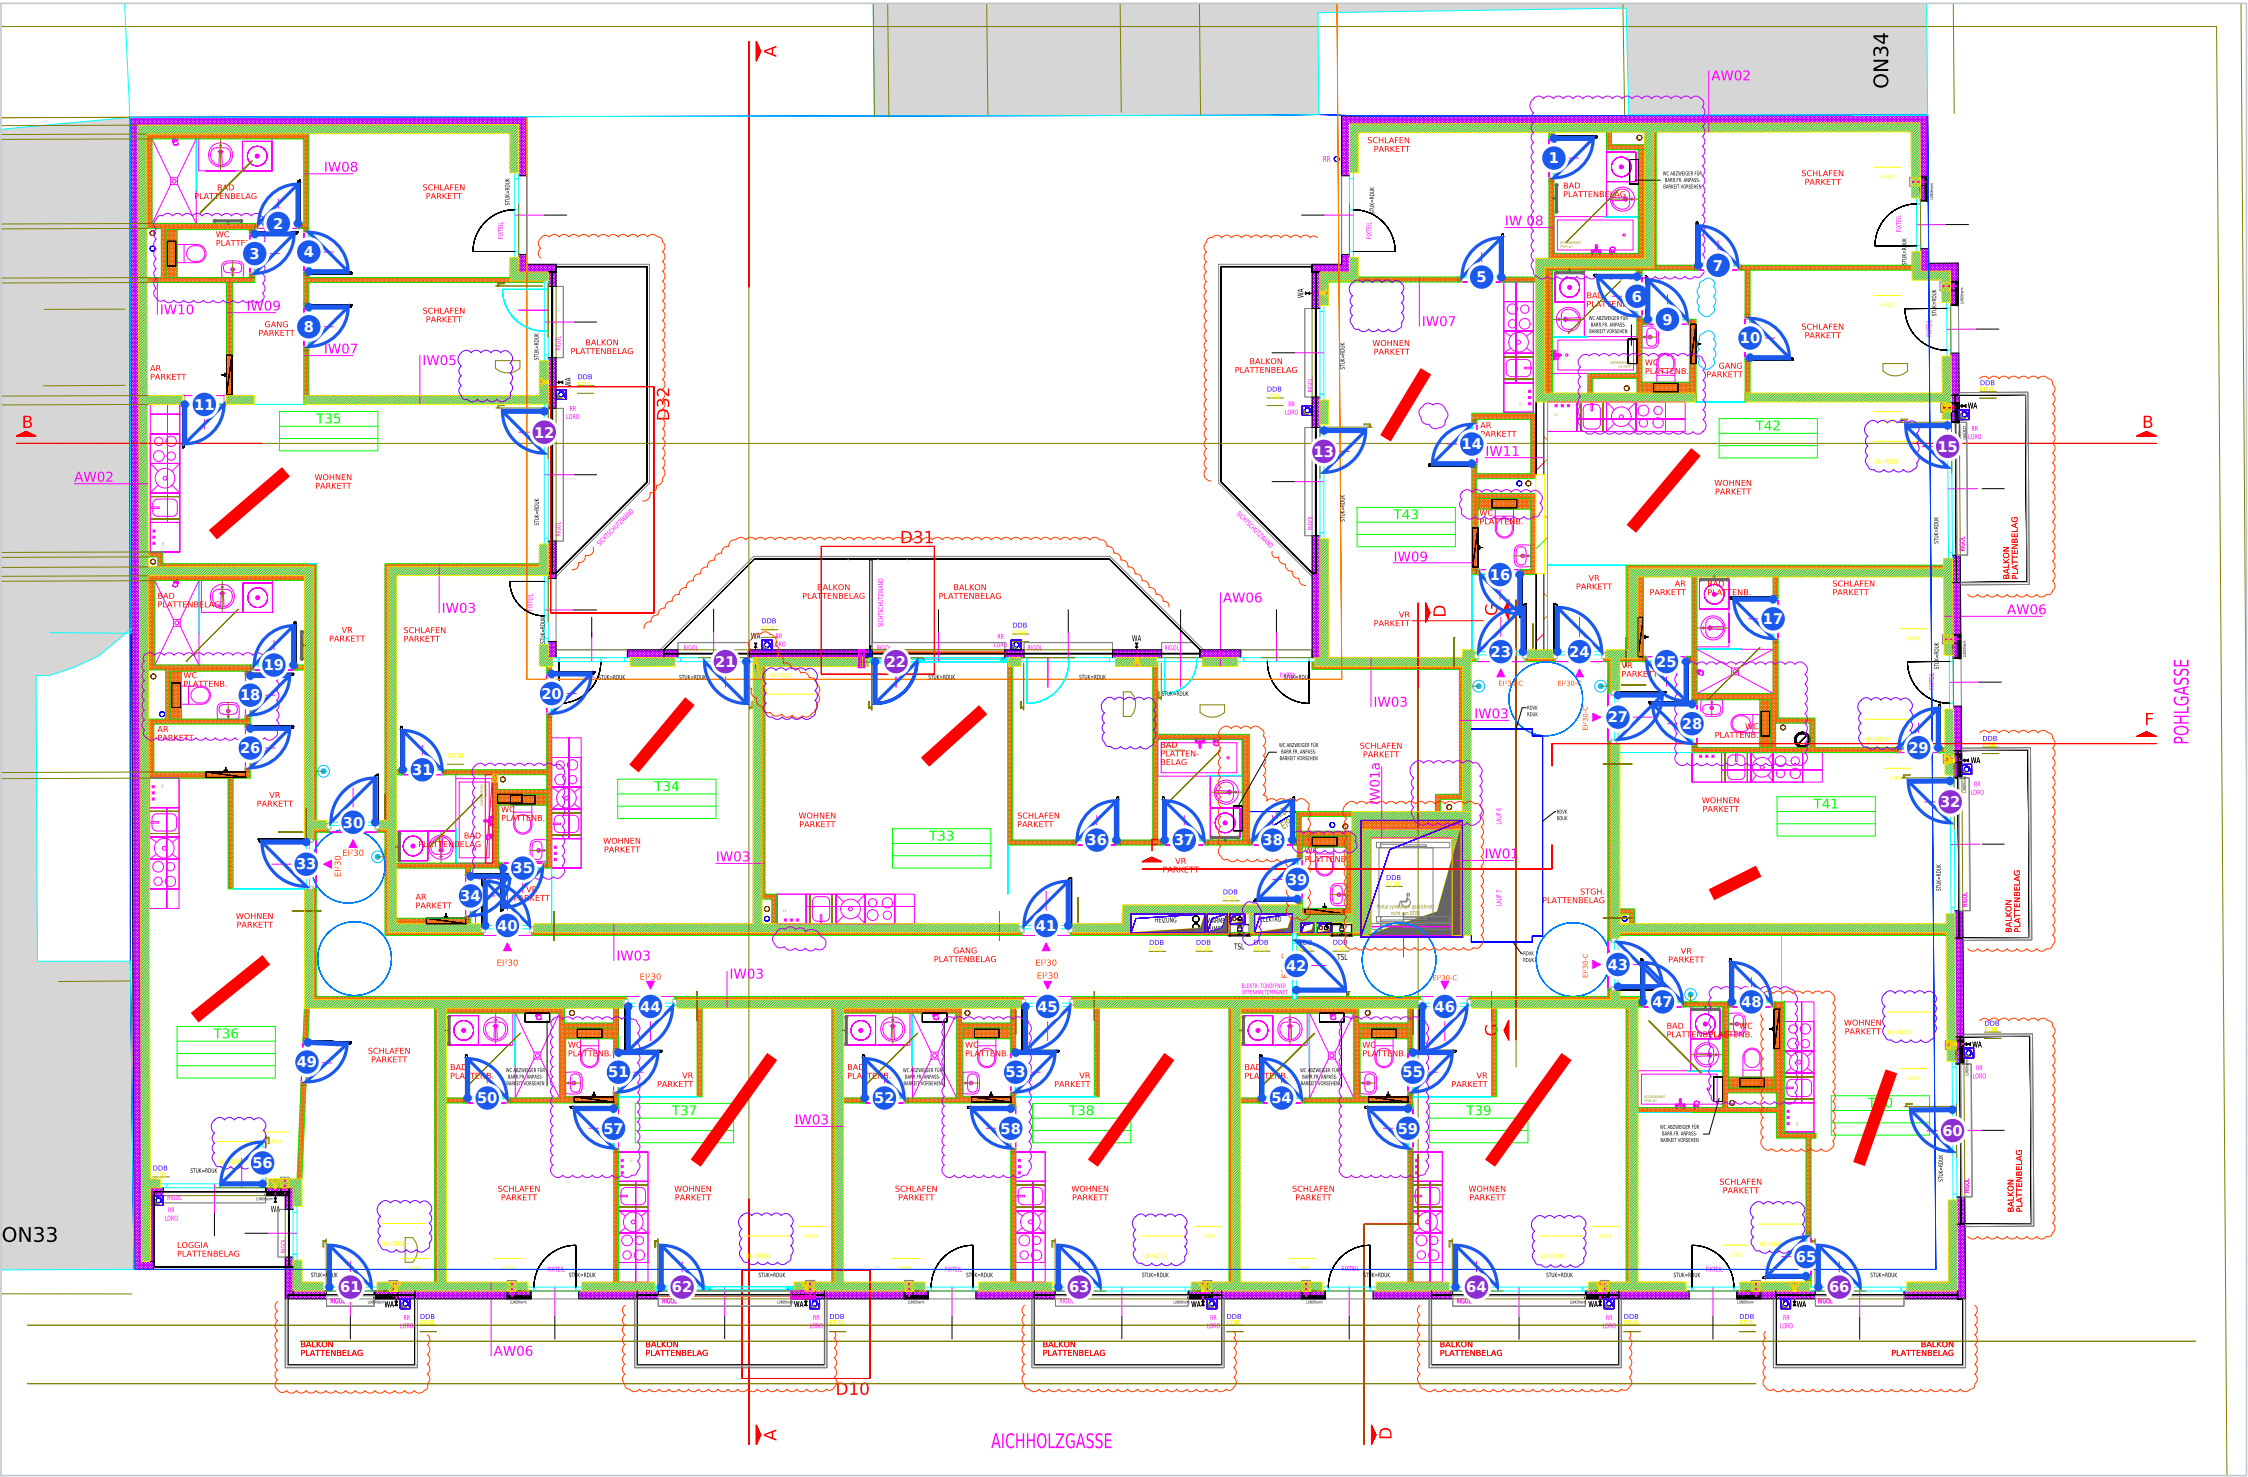

Was ist eine Tür?

Eine Tür ist eine **bewegliche Platte** in einer Lücke der Wand. Ist sie offen, kann man durch die Lücke von einem Raum in den anderen gehen.

Wie sieht eine Tür im Grundriss aus?

Drei Dinge gehören zusammen: 1. eine **Lücke** in der Wand, 2. eine **gerade Linie** – das Türblatt, gezeichnet im offenen Zustand, 3. ein **Viertelkreis** – der Weg, den die Türkante beim Öffnen fährt.

Was zeigt diese Seite?

Jede blaue Nummer steht mitten in einer Türöffnung. Insgesamt wurden **66 Türblätter** gefunden.

Blaue Nummer: Tür zwischen zwei Innenräumen oder zum Gang.


Violette Nummer (12 Stück): Tür in der Außenwand, meist eine Glastür zum Balkon.

Größere Bögen = breitere Türen

Der Radius des Viertelkreises ist so lang wie das Türblatt breit ist. Im Plan kommen **vier verschiedene Bogengrößen** vor. Also gibt es vier verschiedene Türbreiten. Die großen Bögen sitzen z. B. bei den Wohnungseingängen und Balkontüren.

Die Türen wurden aus den Bogenlinien des Originals erkannt. Der Plan zeigt, wie die Türen gebaut werden sollen – nicht, ob sie später offen, zu oder versperrt sind.

Eine Drehtür Stück für Stück lesen

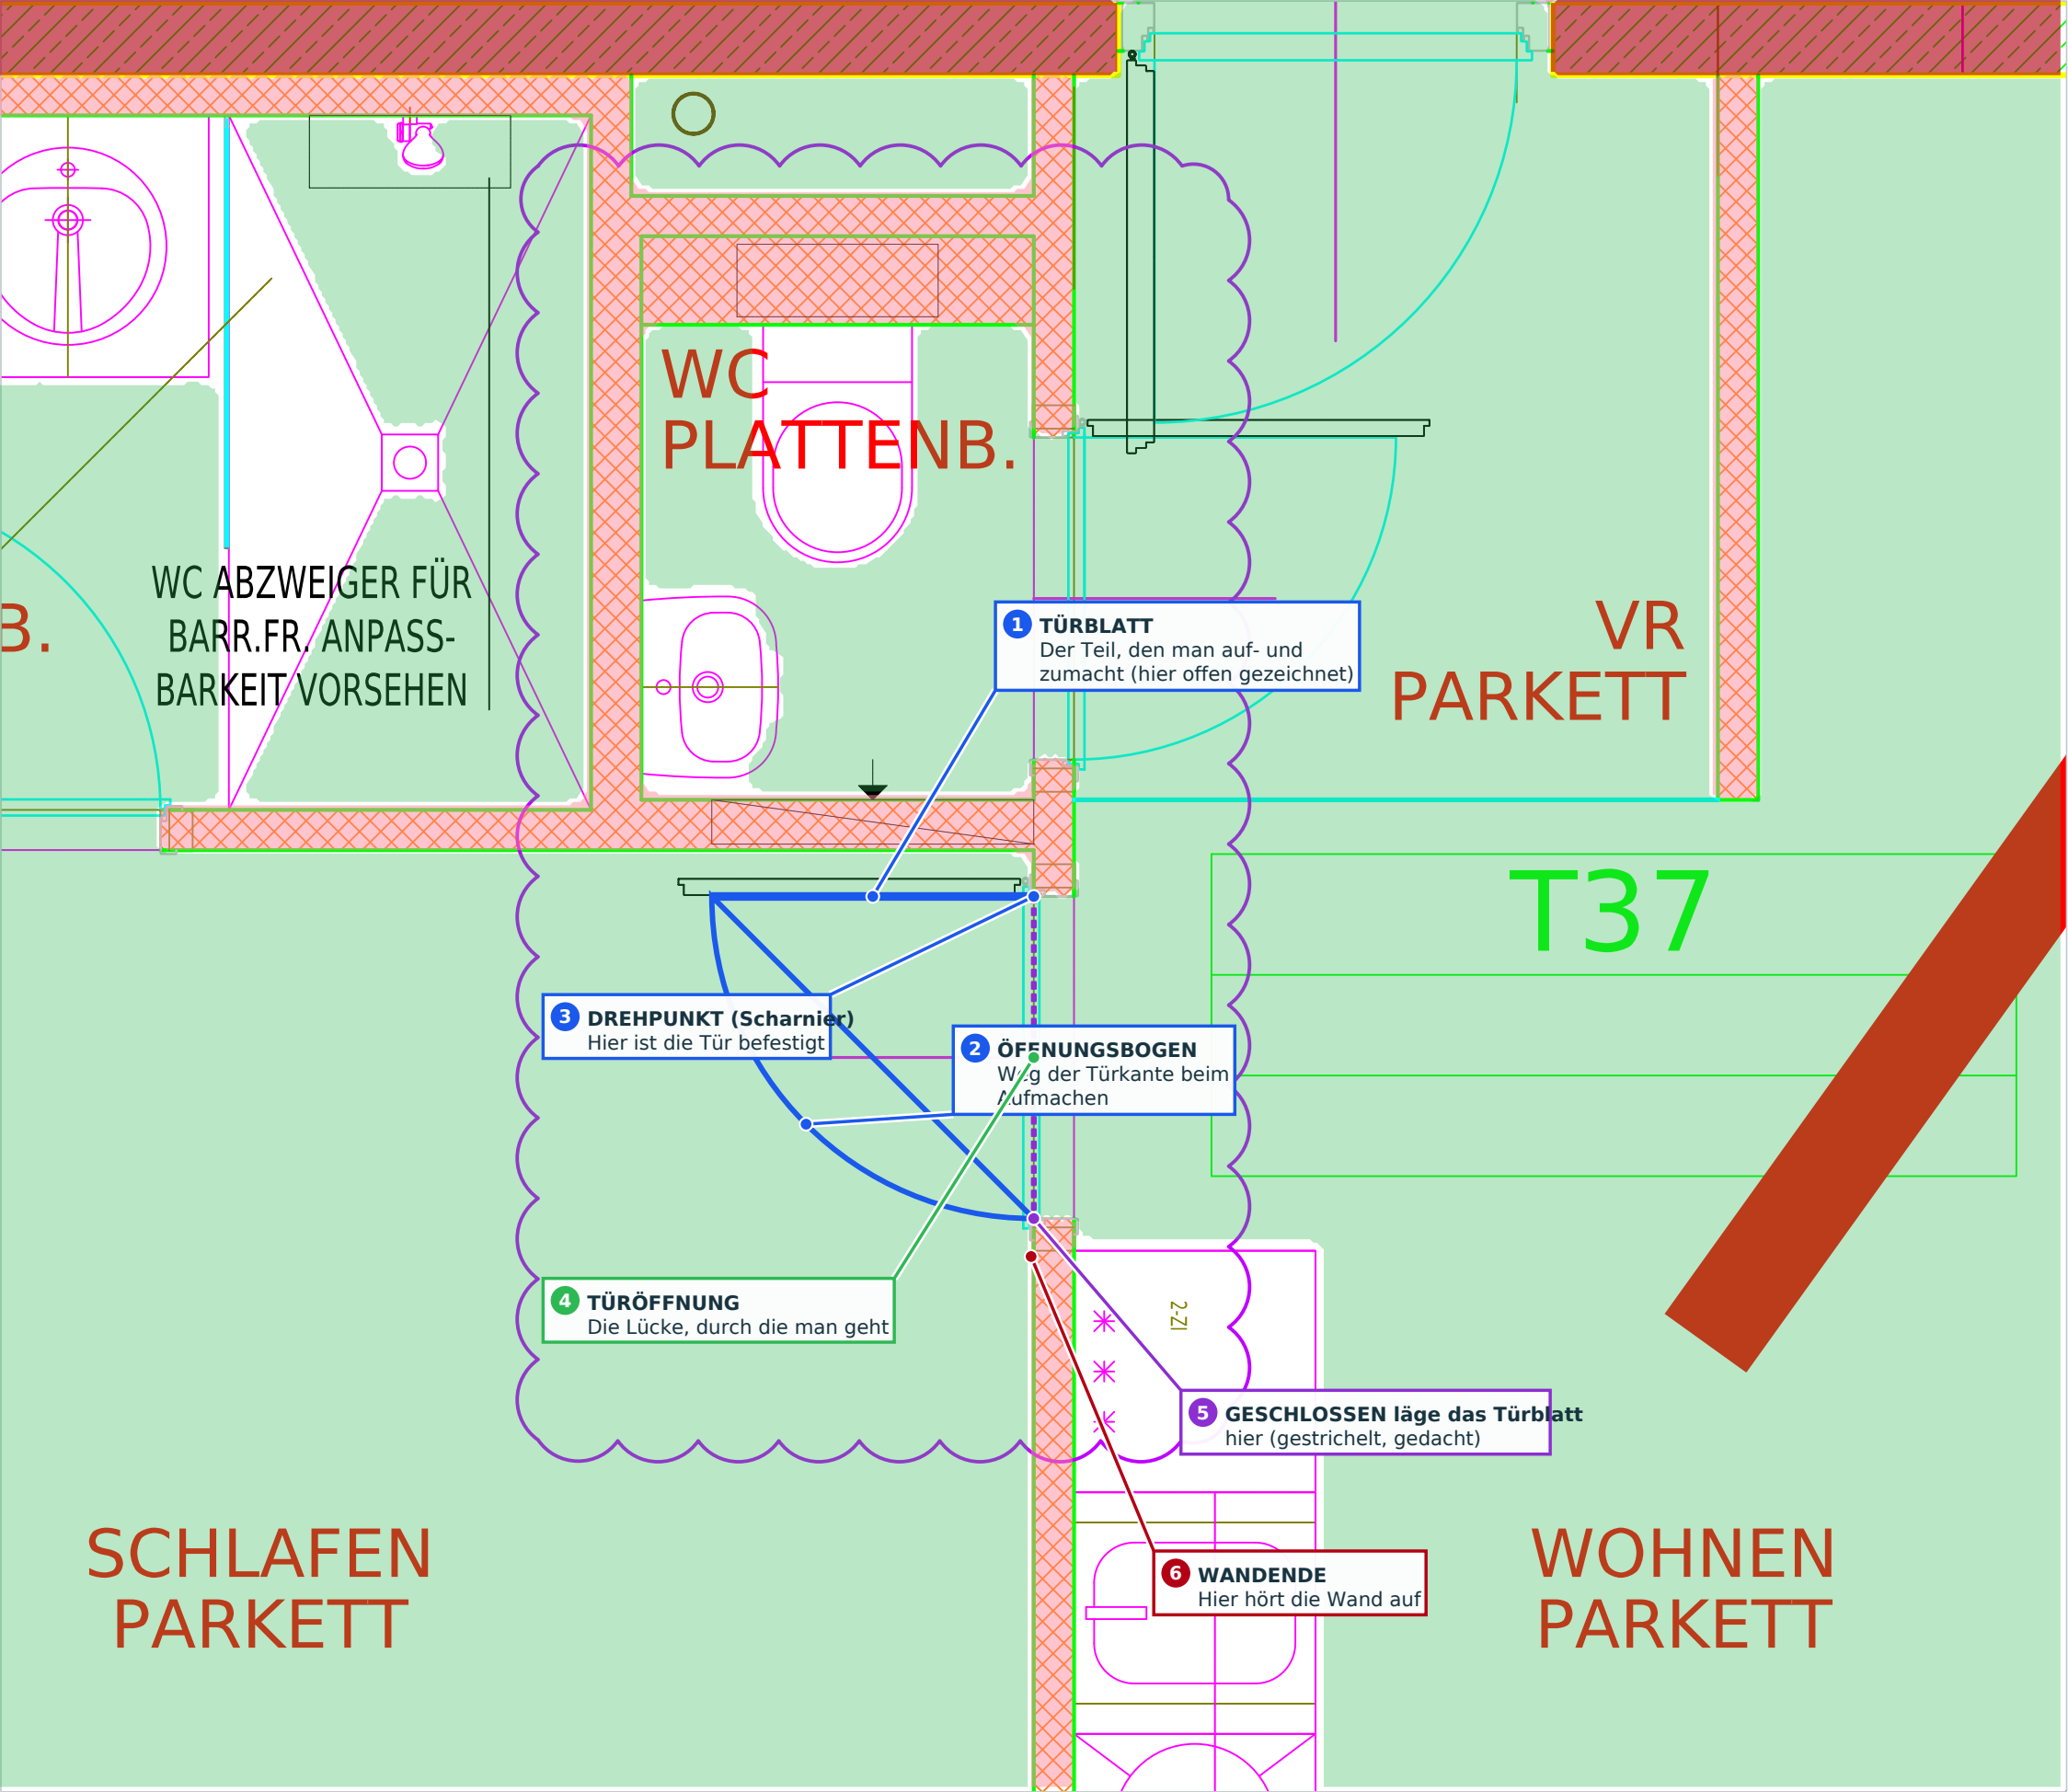

Was ist das?

Eine ganz normale **Drehtür** – die Tür, die man an einer Klinke aufdrückt und die sich um eine Seite dreht. Hier ist es Tür Nr. 57 in der Wohnung T37.

Wie sieht sie im Plan aus?

(4) Die Öffnung: Die rote Wand ist unterbrochen. Zwischen den zwei Wandenden (6) ist eine Lücke.

(1) Das Türblatt ist eine gerade Linie, die quer im Raum steht. Der Plan zeichnet die Tür immer **offen**, damit man sieht, wohin sie aufgeht.

(3) Der Drehpunkt sitzt an einem Wandende. Dort ist die Tür mit Scharnieren befestigt.


(2) Der Viertelkreis zeigt den Weg der Türkante. Der ganze Bereich innerhalb des Bogens muss frei bleiben, damit die Tür aufgeht – dort sollte man z. B. keinen Kasten hinstellen.

(5) Gestrichelt habe ich eingezeichnet, wo das Türblatt liegt, wenn die Tür **zu** ist. Das steht so nicht im Original – es hilft nur beim Verstehen.

In welche Richtung geht sie auf?

Immer **zu der Seite, auf der der Bogen liegt**. Wer von der anderen Seite kommt, muss die Tür von sich weg drücken.

Die Wohnungseingangstür: Tür zwischen Gang und Wohnung

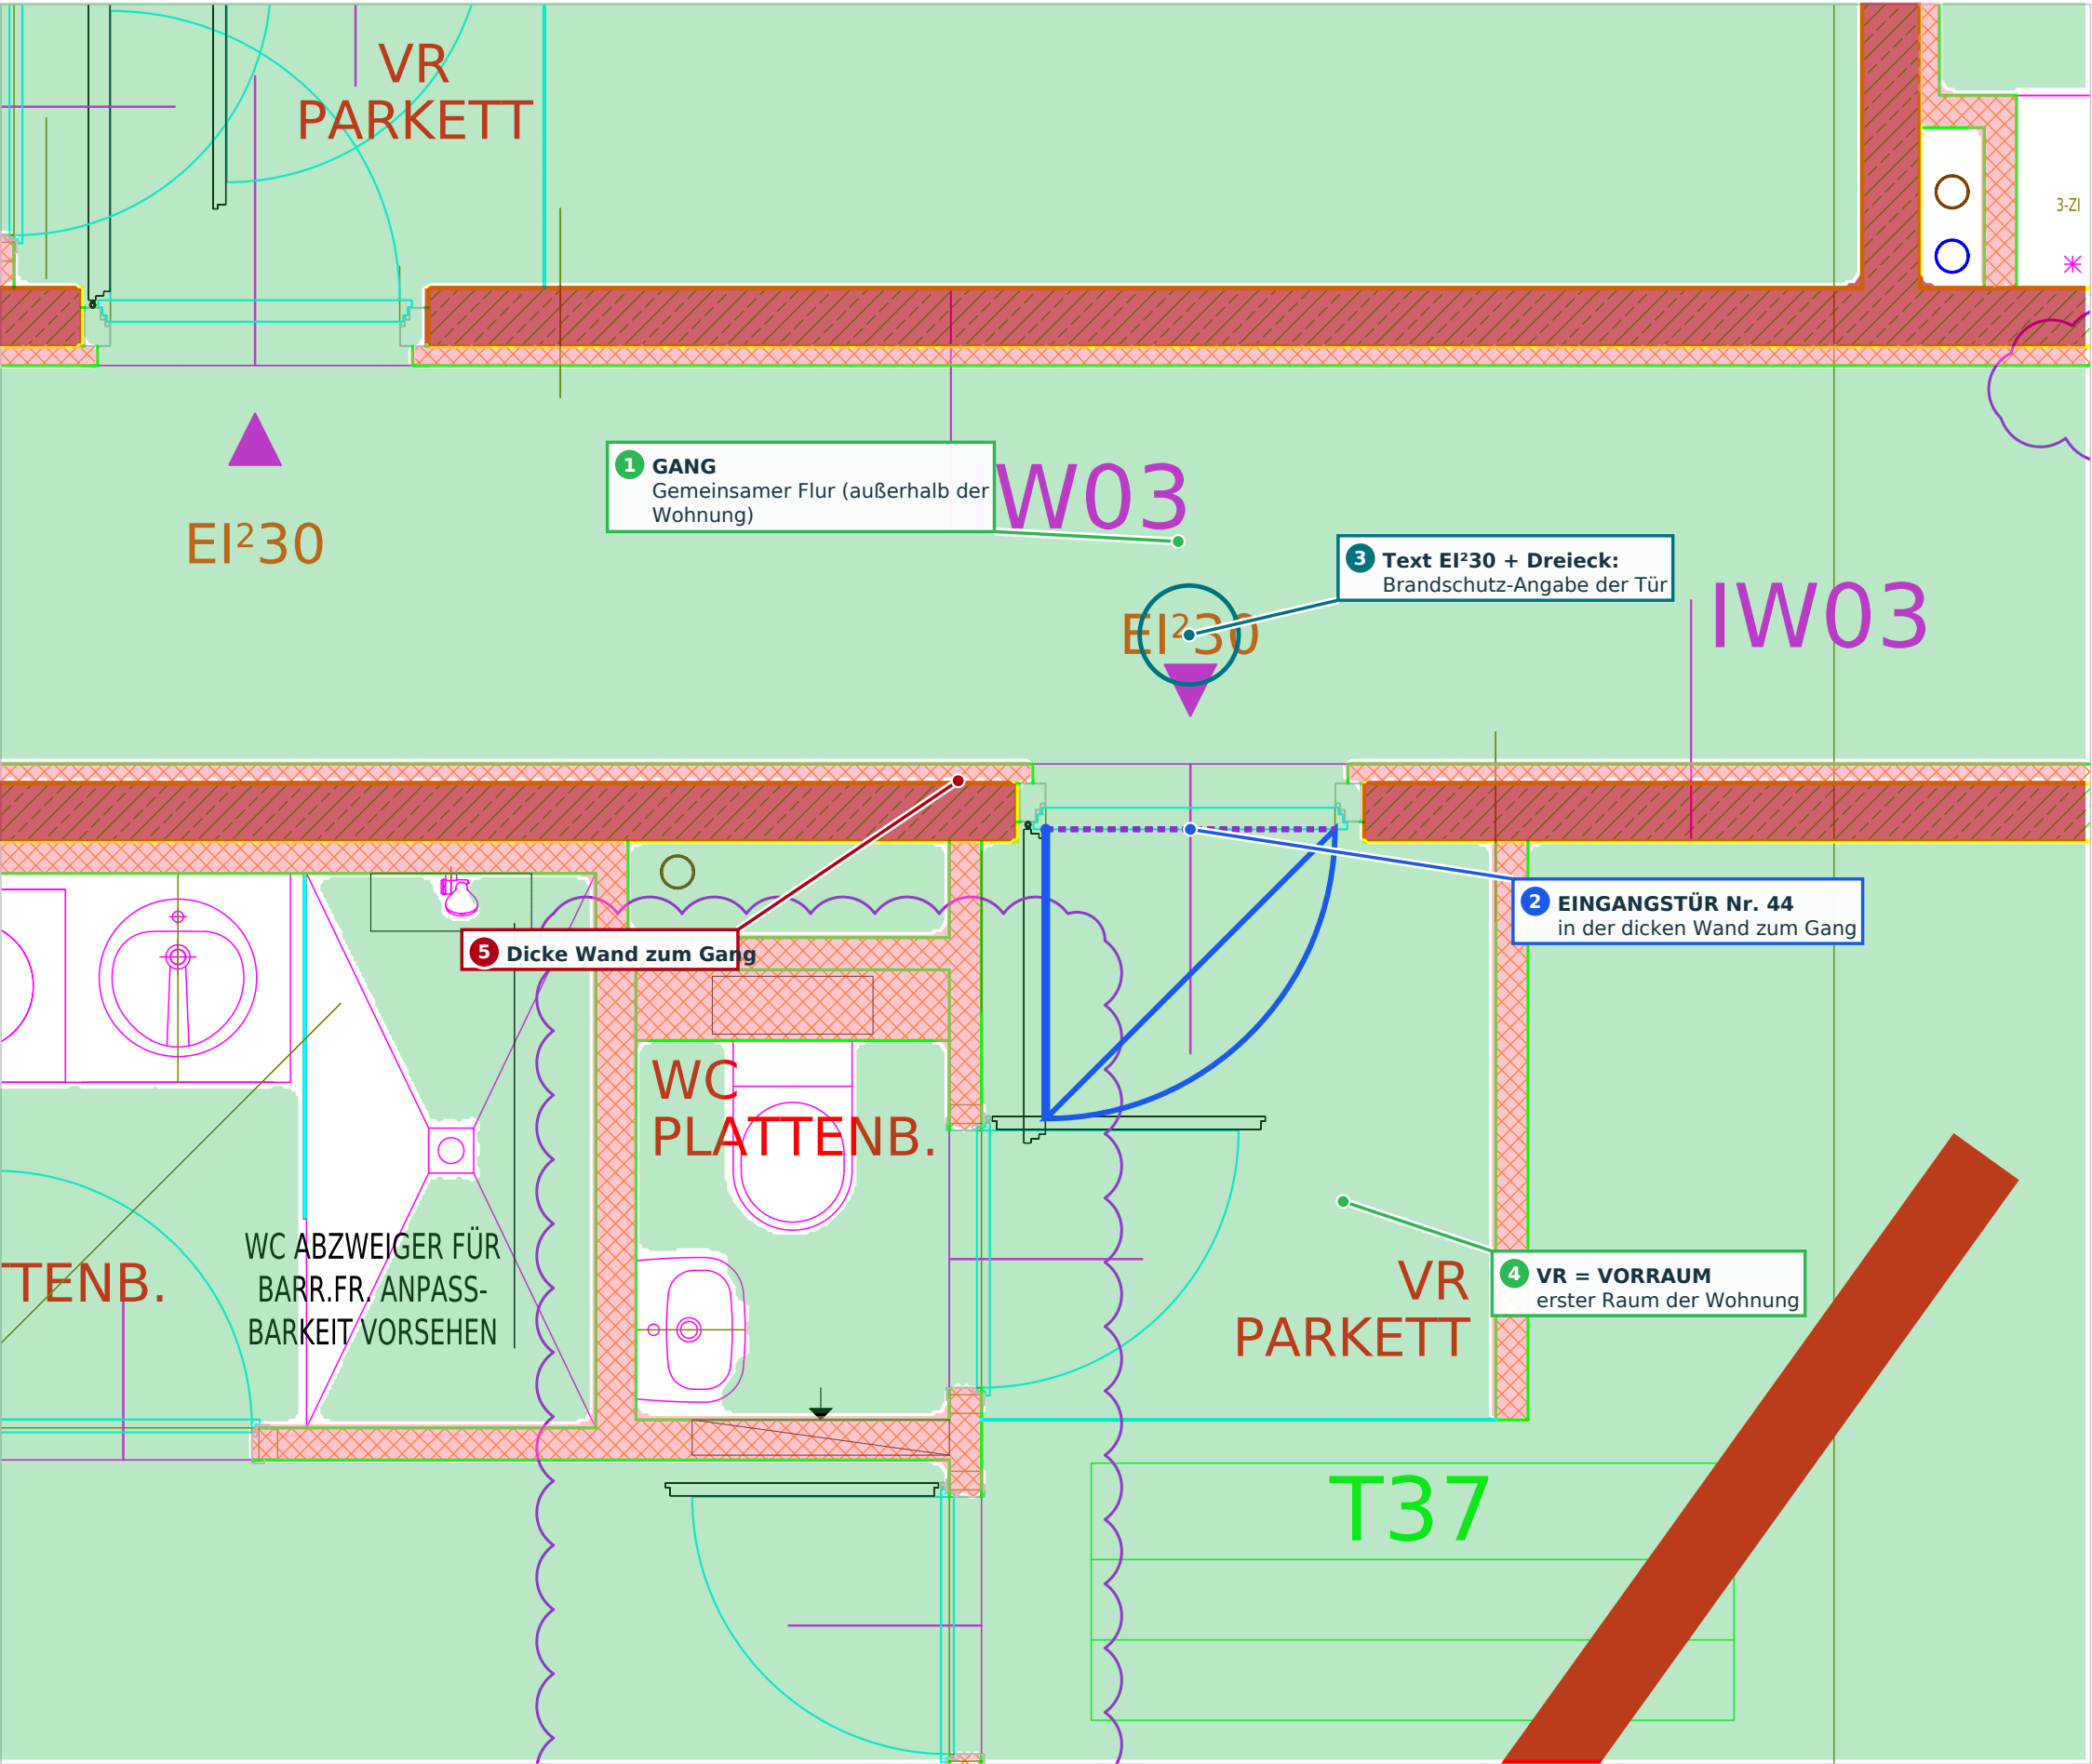

Was ist das?

Die **Wohnungseingangstür** der Wohnung T37. Sie verbindet den **Gang** (1), den alle Bewohner benutzen, mit dem **Vorraum** (4) der Wohnung.

Woran erkenne ich sie hier?

Sie sitzt in der **dicken Wand** (5), die die Wohnung vom Gang trennt. Man erkennt sie wie jede Tür an Lücke, Türblatt und Bogen (2). Der Bogen liegt auf der **Wohnungsseite**: Die Tür geht also **in die Wohnung hinein** auf.


Was bedeutet „EI²30“?

Diese Angabe (3) steht neben fast jeder Wohnungseingangstür. Sie ist eine Brandschutz-Klasse: Die Tür soll ein Feuer **30 Minuten** lang aushalten (E = hält Flammen und Rauchgase ab, I = begrenzt die Hitze auf der anderen Seite). An manchen Türen steht **EI²30-C**: das C bedeutet, dass die Tür **von selbst zufällt**.

Das kleine **magenta Dreieck** daneben ist ein Markierungszeichen für genau diese Tür.

Was das Dreieck im Detail bedeutet (z. B. welche Seite gemeint ist), erklärt der Plan nicht. Wir lesen es nur als „diese Angabe gehört zu dieser Tür“.

Die Balkontür: eine Tür aus Glas in der Außenwand

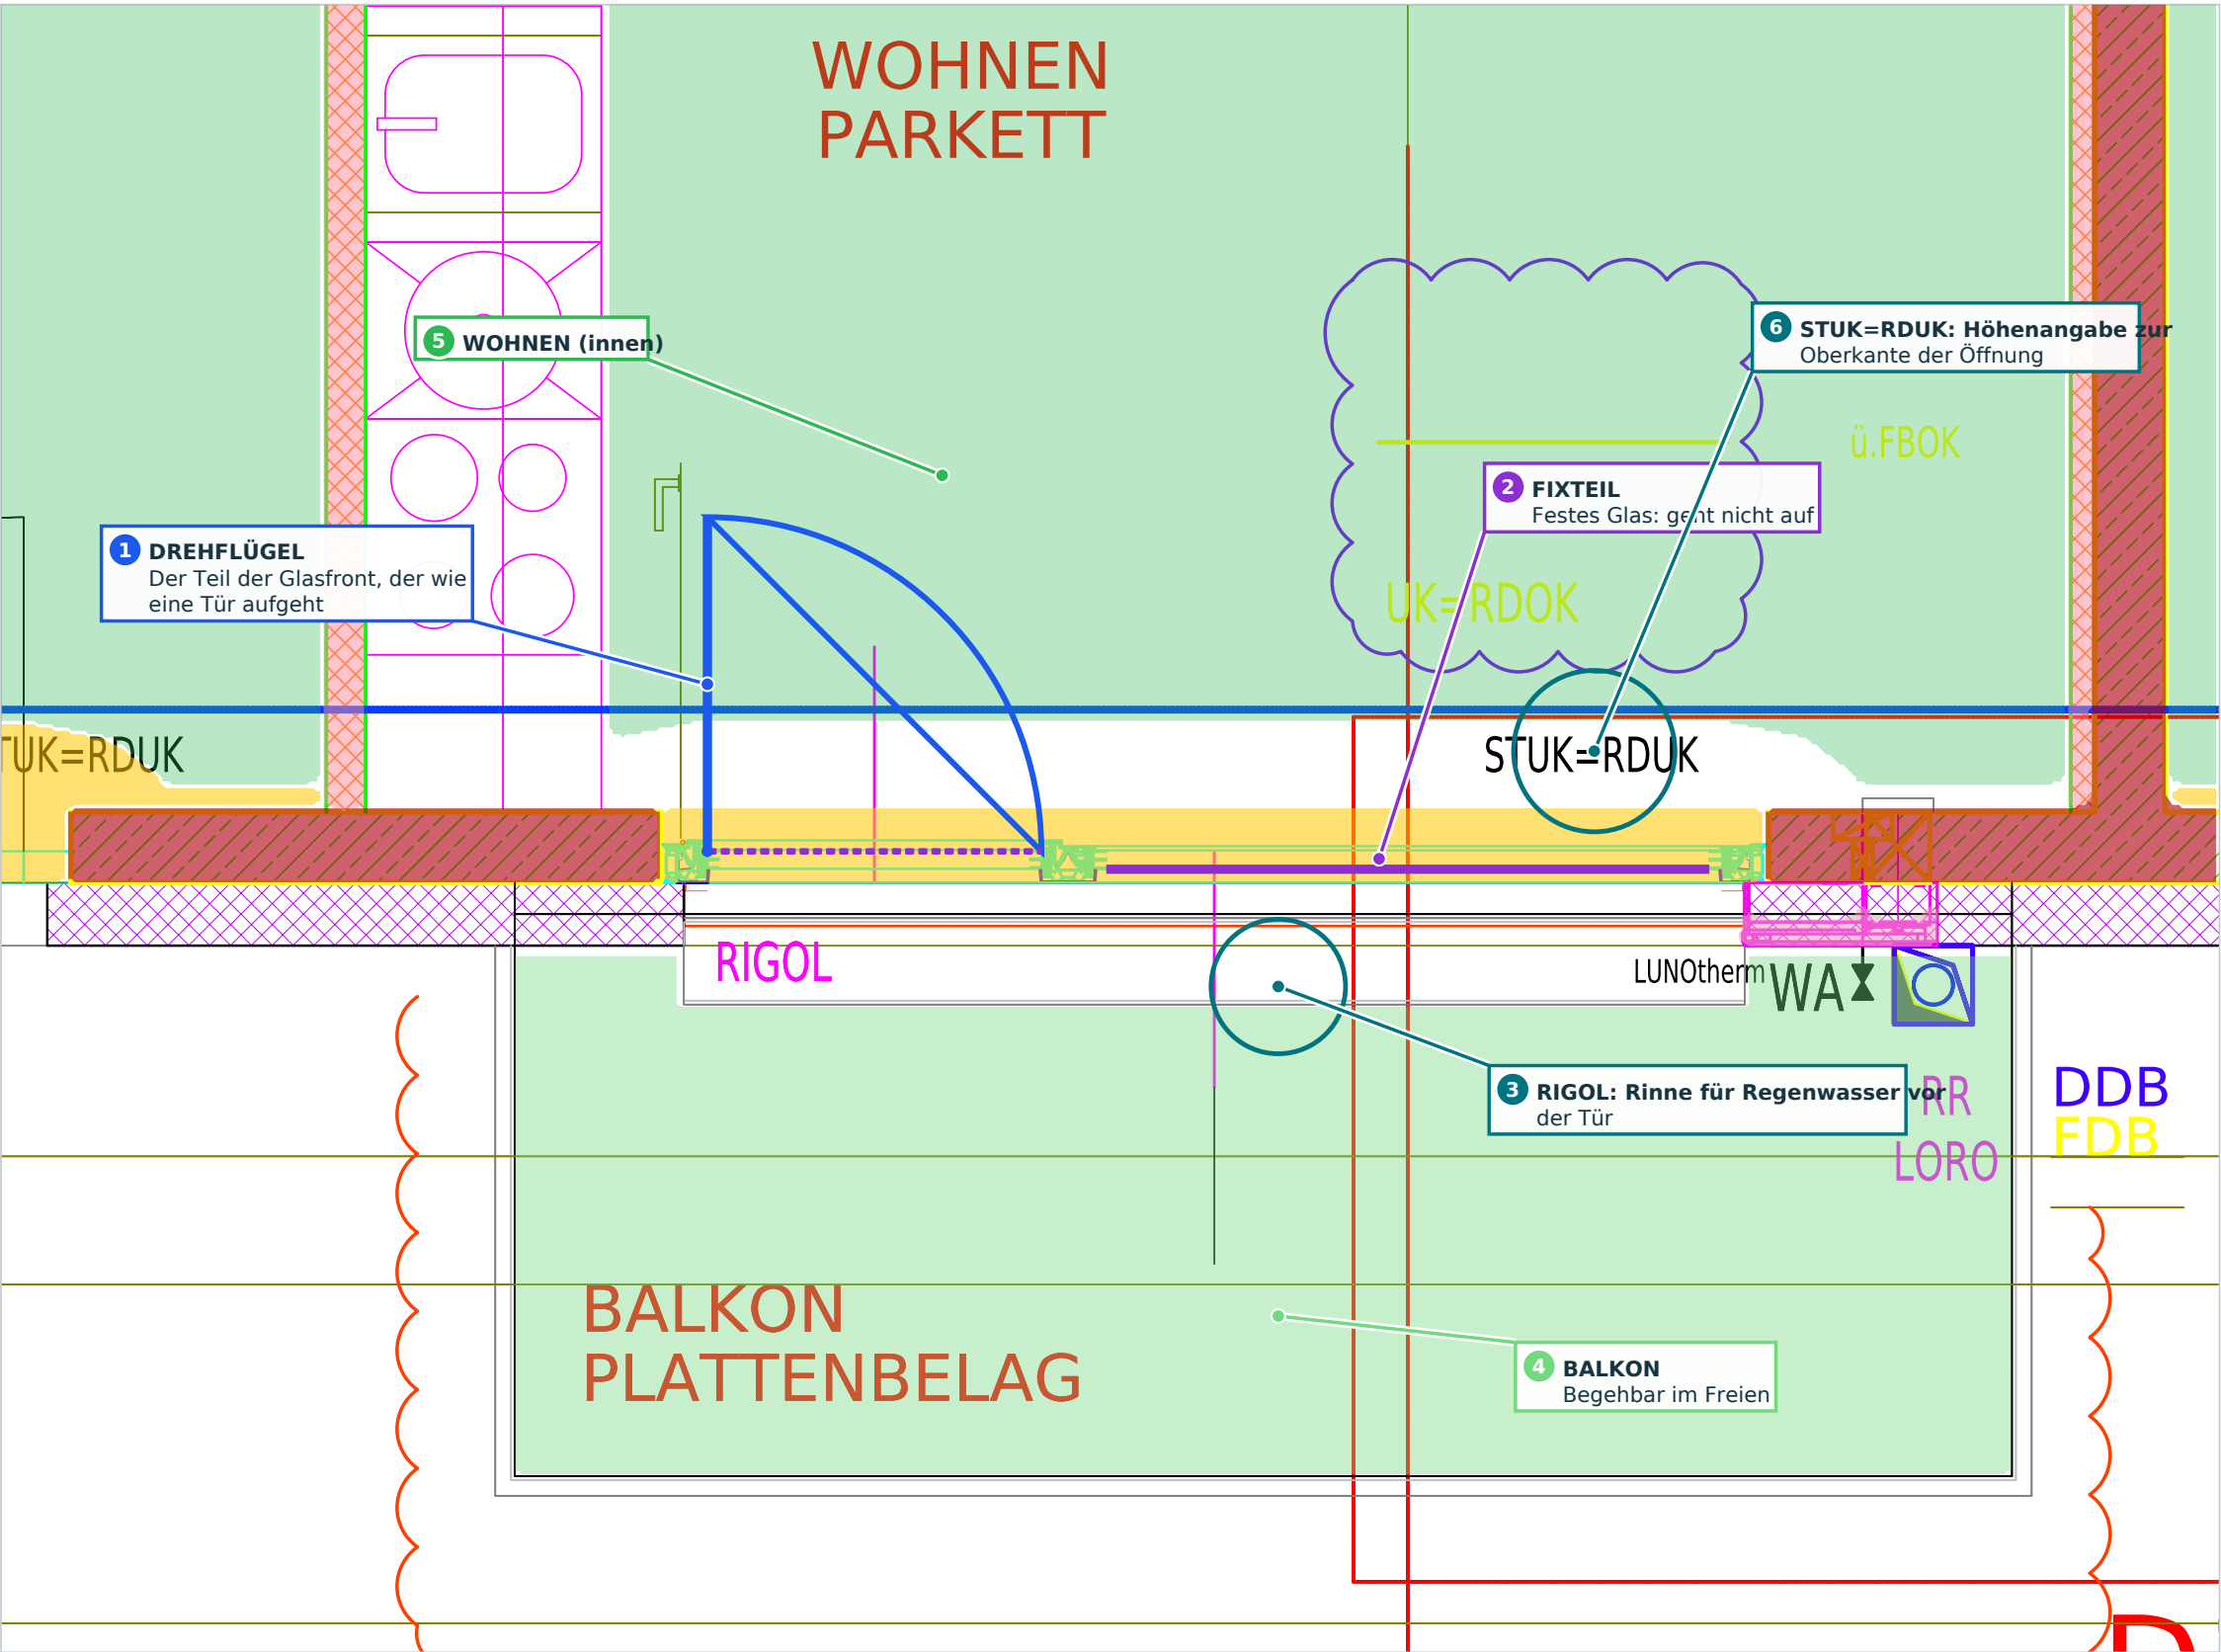

Was ist das?

Eine **Glasfront** zwischen Wohnzimmer (5) und Balkon (4). Ein Teil davon ist eine Tür (1), der Rest ist festes Glas (2).

Wie unterscheide ich Tür und festes Glas?

Tür (1): Es gibt ein Türblatt und einen **Viertelkreis**. Nur wo ein Bogen gezeichnet ist, kann man etwas aufmachen.

Festes Glas (2): nur mehrere dünne, parallele Linien – **kein Bogen**. Im Plan steht an solchen Stellen oft das Wort **FIXTEIL**. Da kann man nicht durchgehen.

Und die Wand?


Links und rechts der Glasfront siehst du wieder die rote Wand mit Muster. Dazwischen (gelb) ist die Wand unterbrochen – dort sitzt das Glaselement.

Was sind die kleinen Texte?

RIGOL (3): eine Rinne vor der Tür, damit Regenwasser nicht hineinläuft. **STUK=RDUK (6):** Die obere Kante der Öffnung liegt auf der Unterseite der Rohdecke.

Der Plan zeigt, dass man vom Wohnzimmer auf den Balkon kommt. Wie hoch die Schwelle genau ist, steht hier nicht.

Alle Öffnungen in der Außenwand - gelb, Glas violett

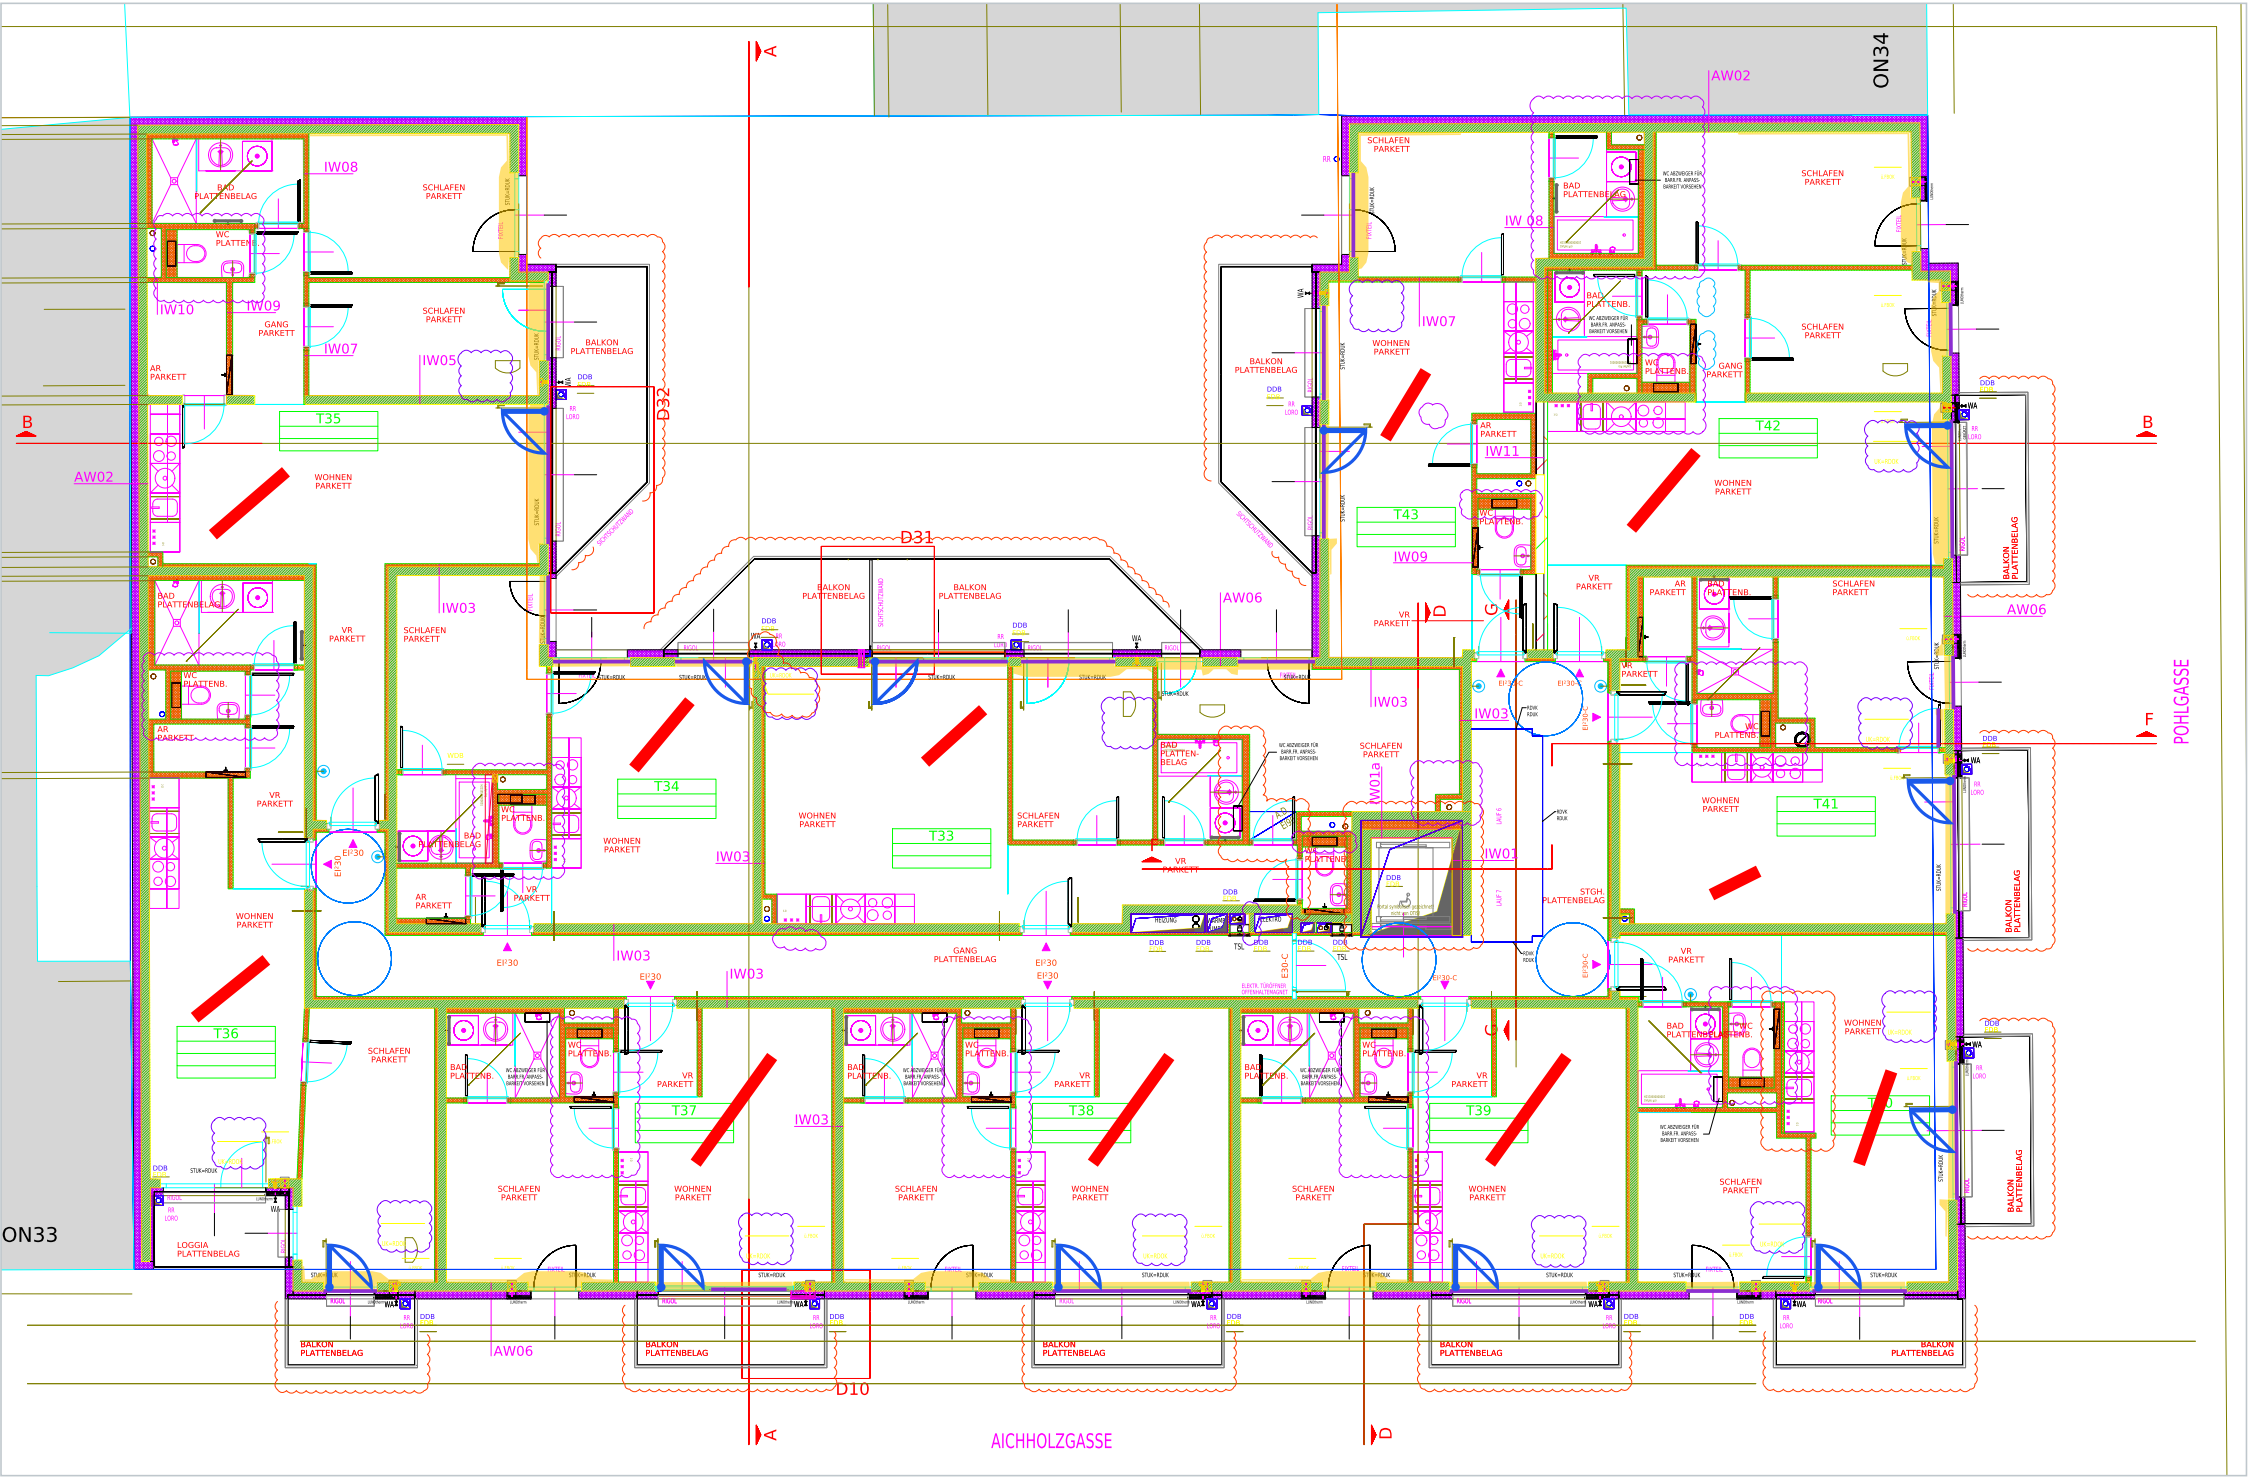

Was ist ein Fenster?

Ein Fenster ist eine Öffnung in der Außenwand, in der eine **Glasscheibe** in einem **Rahmen** sitzt. Es lässt Licht und (wenn man es öffnet) Luft herein. **Hindurchgehen kann man nicht.**

Wie sieht es im Grundriss aus?

Die dicke, gemusterte Wand hört auf. Stattdessen laufen **mehrere sehr dünne Linien** parallel durch die Lücke: außen und innen der Rahmen, in der Mitte das Glas.

Was zeigt diese Seite?


- Gelb:** alle 31 erkannten Unterbrechungen der Außenwand.
- Violett:** bei 23 davon wurde die mittlere Glaslinie gefunden und nachgezogen.
- Blau:** die Türen in der Außenwand (Glastüren zu den Balkonen).

Besonderheit dieses Hauses

Fast alle Öffnungen sind **große Glasfronten**, die vom Boden bis zur Decke reichen. Ein Teil davon ist fest (FIXTEIL), ein Teil geht als Tür auf. Klassische Fenster mit Brüstung (Mauer unter dem Fenster) sind in diesem Plan nicht klar erkennbar.

Die gelben Flächen wurden automatisch aus den Lücken der Außenwand abgeleitet. Kleine Lücken können fehlen. Wie hoch ein Fenster ist, zeigt ein Grundriss nie – dafür braucht man einen Schnitt oder eine Ansicht.

Glas erkennen: Rahmen, Scheibe und die Wand daneben

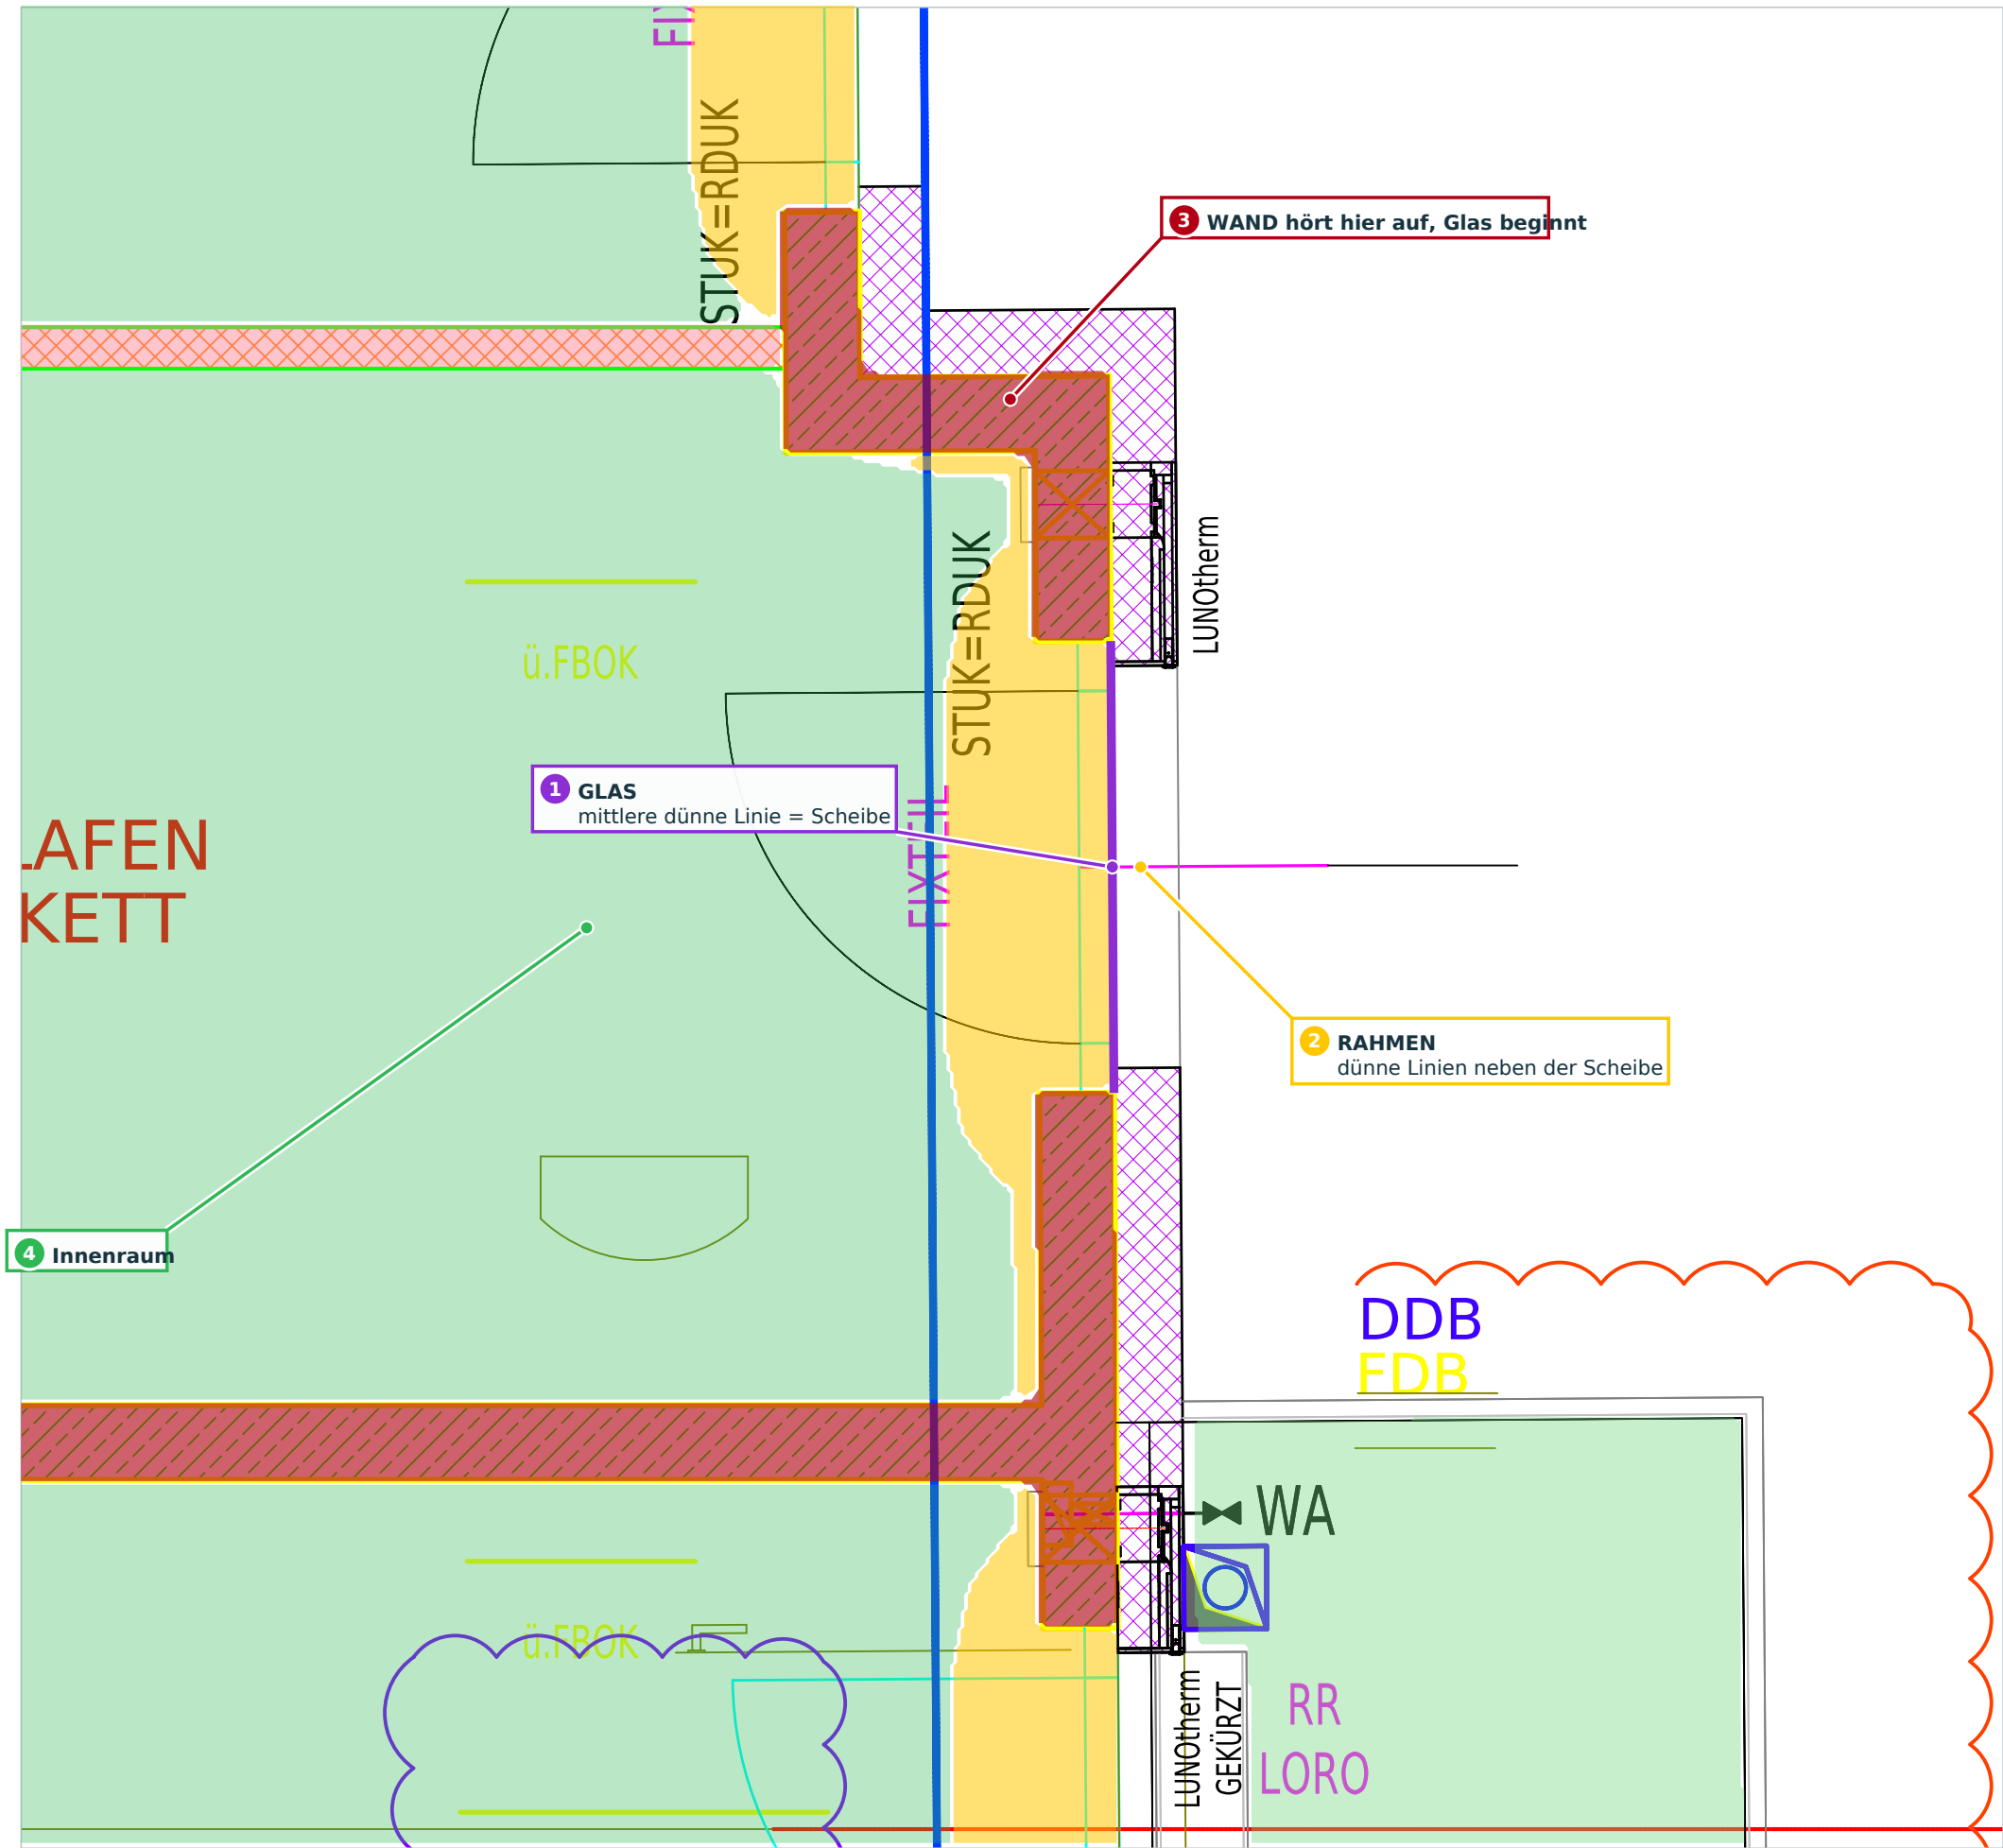

Was ist Glas / Verglasung?

Glas ist ein durchsichtiges, festes Material. Es lässt **Licht** durch. Für eine Person ist es aber wie eine Wand: **Man kann nicht durchgehen.**

Wie sieht Glas im Grundriss aus?

Glas ist nur wenige Millimeter dick. Darum ist es im Plan nur eine **einzelne, sehr dünne Linie** (1). Sie liegt zwischen den Linien des Rahmens (2). Zusammen sieht das aus wie ein Bündel feiner paralleler Striche in einer Lücke der Wand.

Wie unterscheide ich Glas von einer Wand?


Wand (3): breiter Streifen **mit Muster** (Schraffur).
Glas: ganz dünne Linien **ohne Muster**.

Wie unterscheide ich Glas vom Rahmen?

Der Rahmen hält das Glas fest und liegt außen herum. Das Glas liegt in der Mitte. In diesem Plan haben Rahmen und Glas die gleiche hellblaue Farbe – darum habe ich die Scheibe **violett** nachgezogen.

Welche der dünnen Linien genau die Scheibe ist, lässt sich ohne Detailzeichnung nicht zu 100 % sagen. Die violette Linie ist die mittlere Linie des Bündels.

Begehbare Flächen - grün

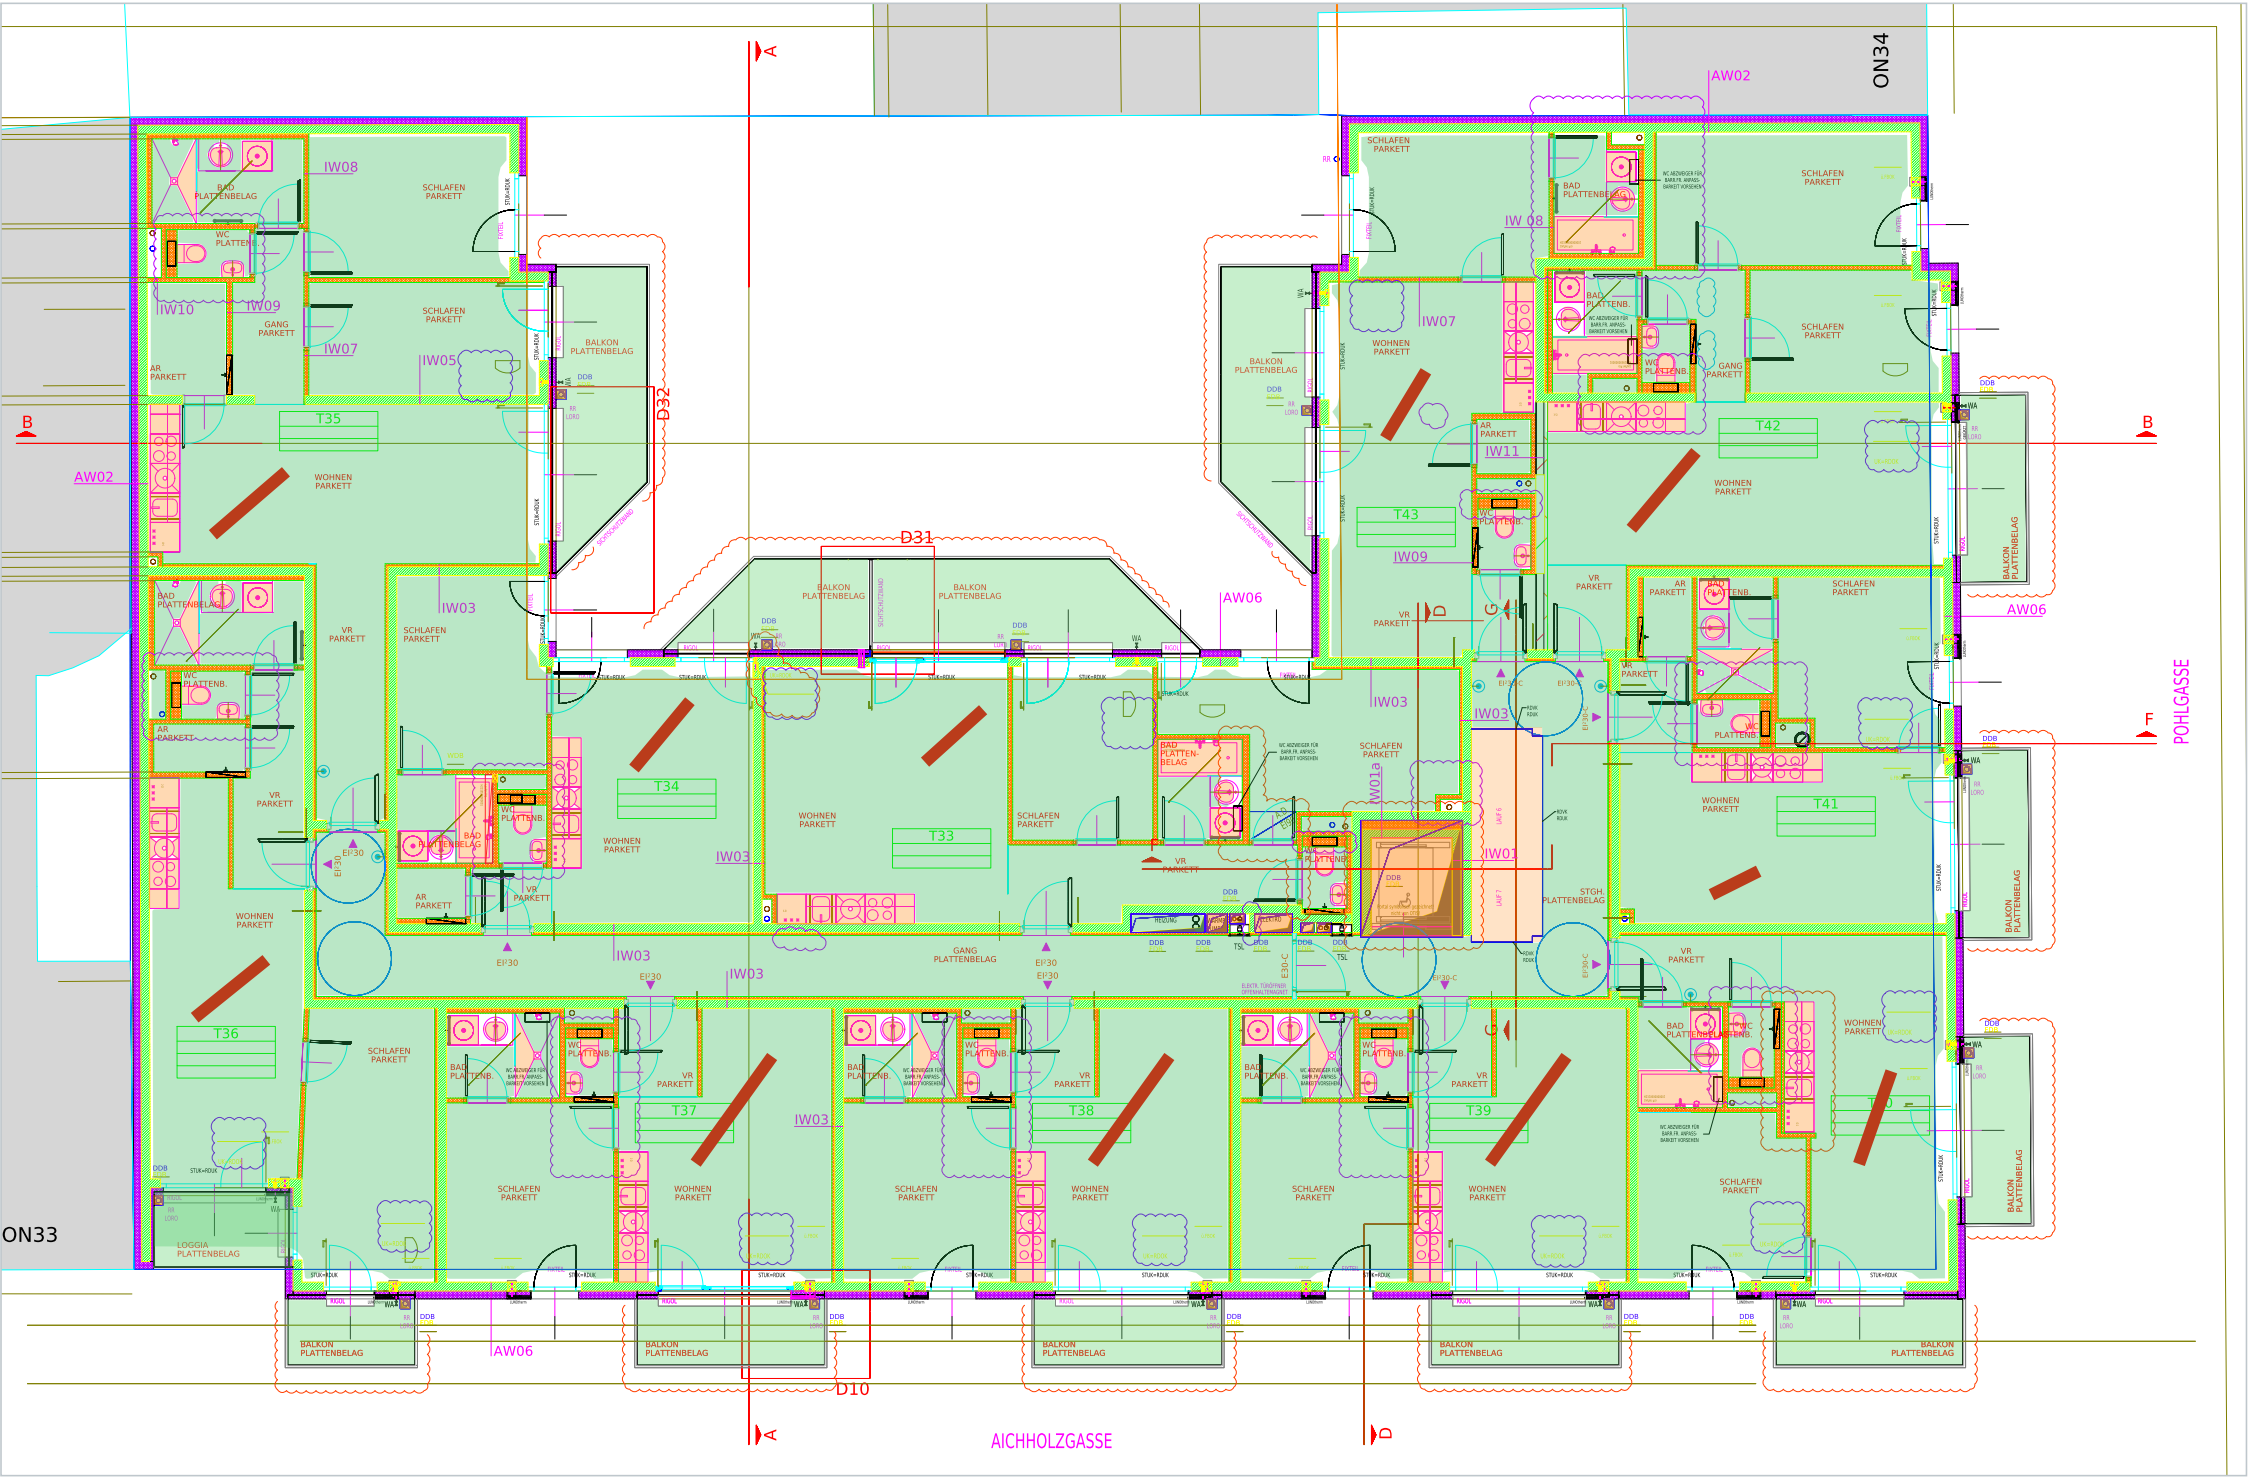

Die wichtigste Frage für Anfänger

Grün heißt: Hier kann ich als Mensch stehen und gehen. Das ist der Fußboden in den Räumen, im Gang und in den Vorräumen.

Hellgrün sind Balkone und die Loggia: Boden im Freien. Man erreicht sie nur durch eine Balkontür.

Was ist NICHT grün – und warum?

Wände (weiß ausgespart): Da ist festes Material.

Orange: Küchen, Waschbecken, WCs, Duschen, Einbaukästen. Darunter ist zwar Boden, aber es steht etwas im Weg.

Orange kräftig: Aufzugsschacht und Leitungsschächte – dort ist gar kein Boden, sondern ein senkrechter Schacht durch das ganze Haus.

Orange blass: die Öffnung, in der die Treppe liegt (Stiegenhaus).


Weiß im Hof: Dort ist kein Innenraum und auf diesem Stockwerk kein Boden.

Wie man von grün zu grün kommt

Zwei grüne Flächen sind nur dort verbunden, wo eine **Tür** in der Wand ist. Das Grün läuft darum durch die Türöffnungen durch – aber nie durch eine Wand oder durch Glas.

Grün ist eine Lernmarkierung. Sie sagt nicht, ob ein Weg breit genug für einen Rollstuhl ist oder als Fluchtweg gilt.

Alles zusammen: Wände, Türen, Glas, Boden, Einbauten

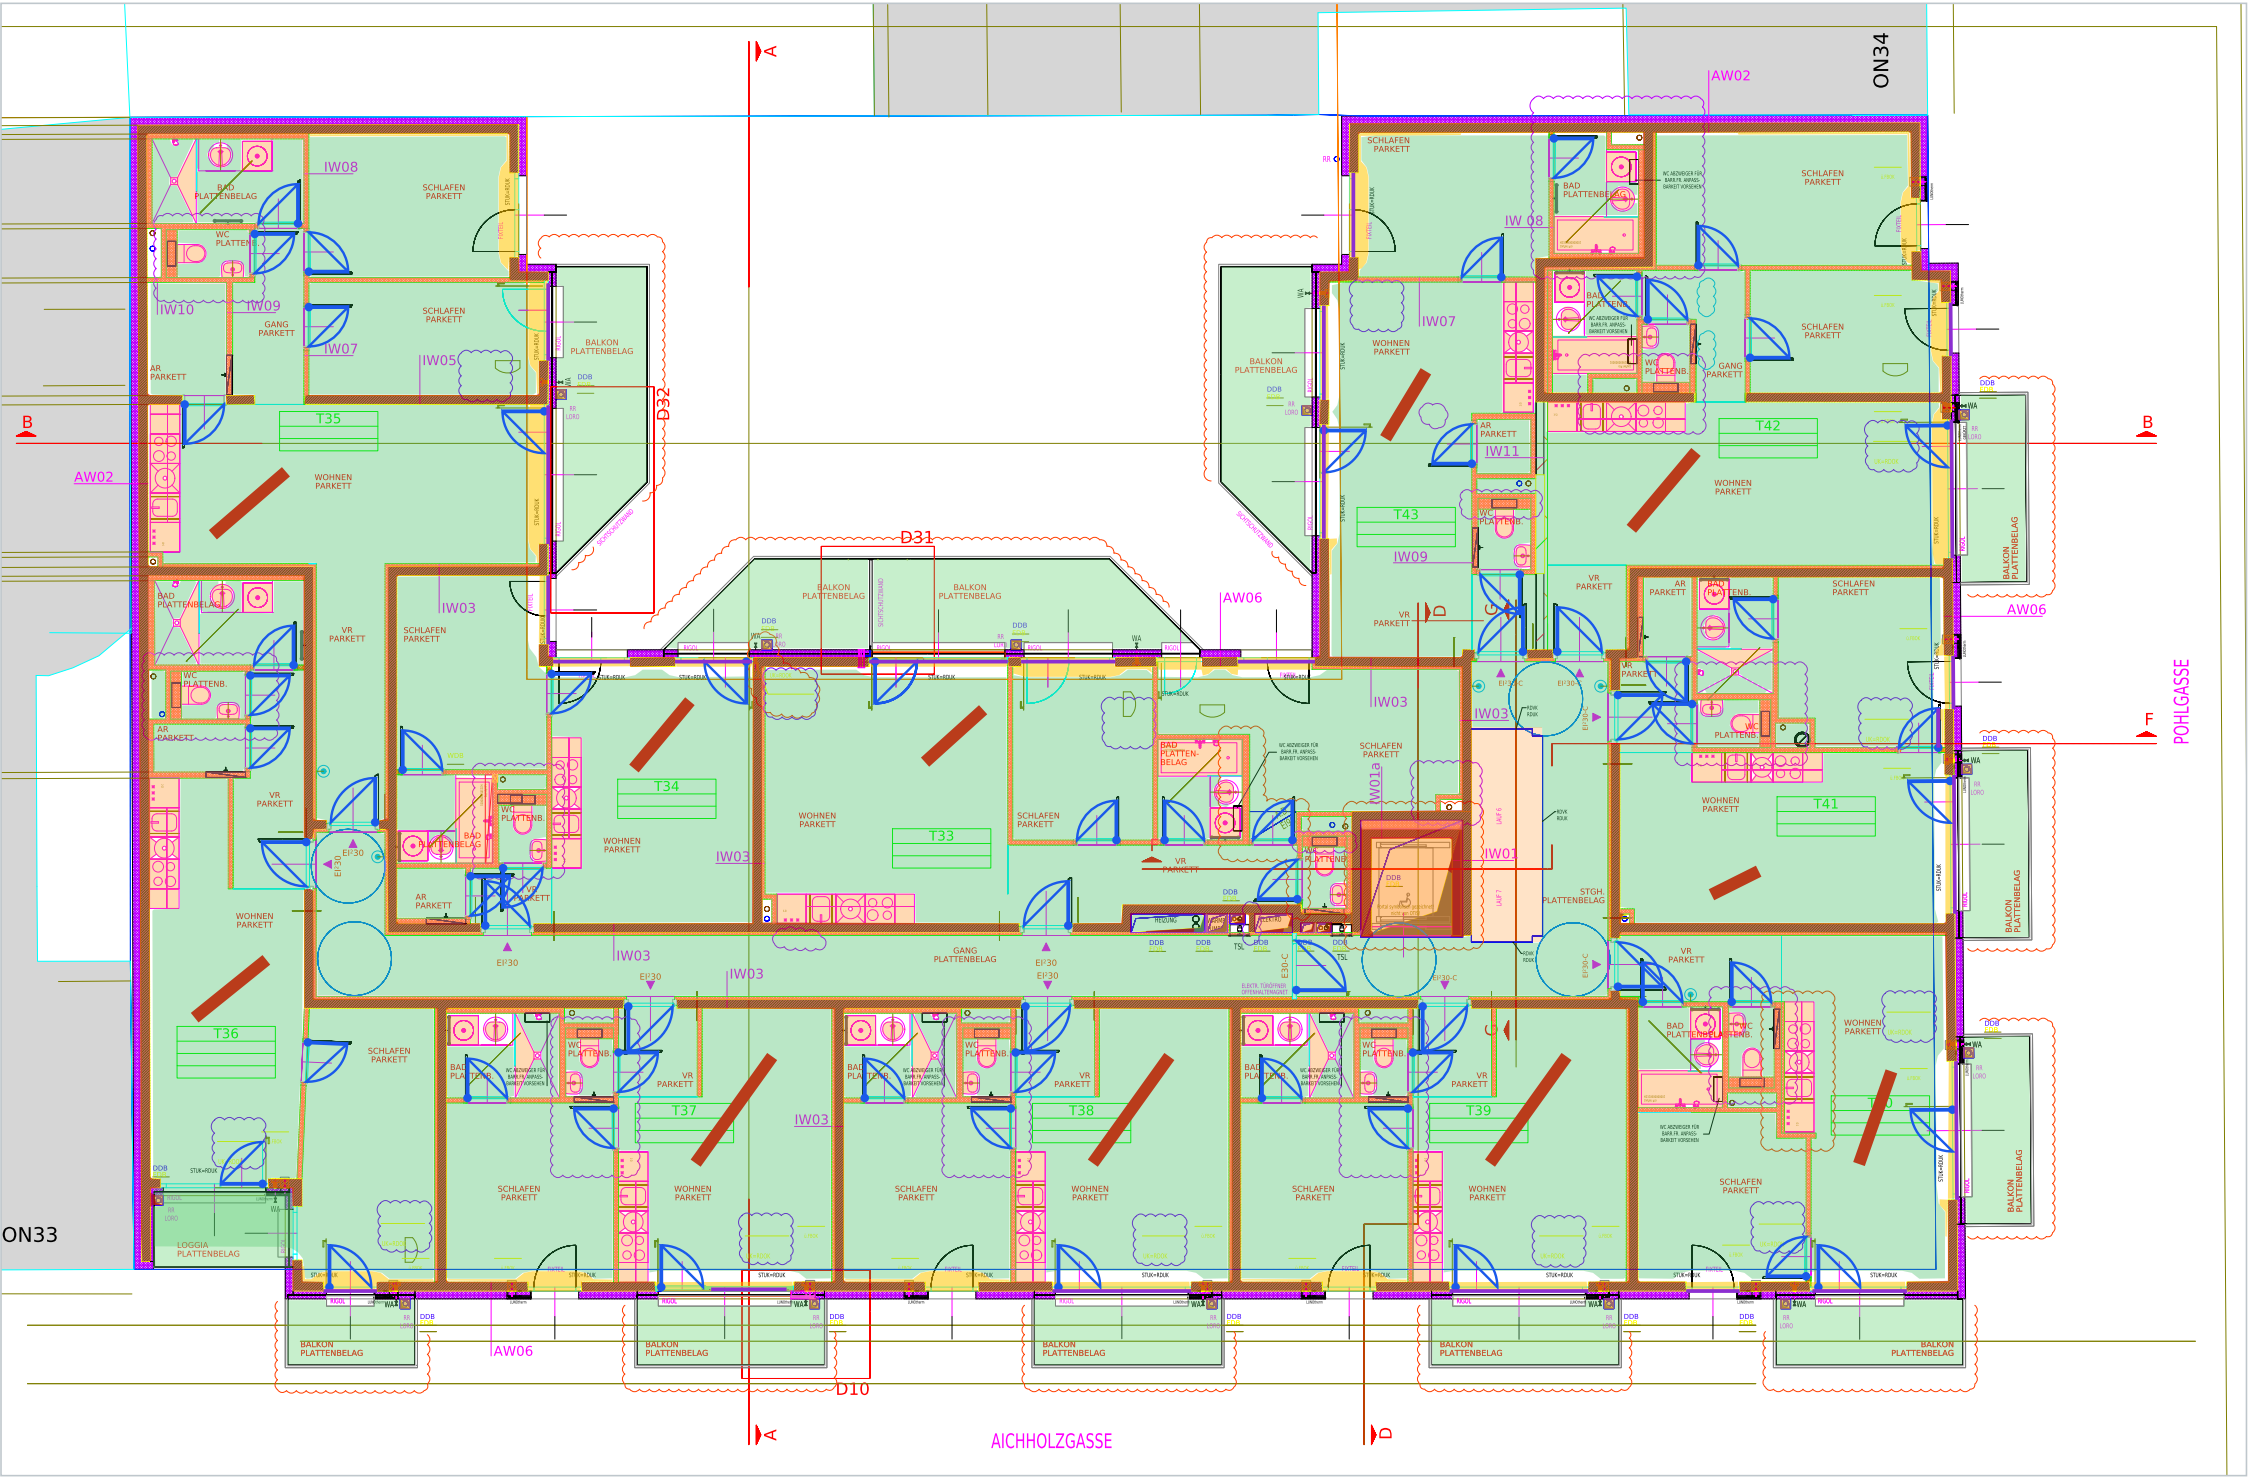

Jetzt kannst du den ganzen Plan lesen

Auf dieser Seite liegen alle Farben gleichzeitig über dem Original. Versuche, deinen Weg mit dem Finger zu verfolgen:

1. Starte im **Stiegenhaus** rechts von der Mitte.
2. Geh auf dem **grünen Gang** nach links.
3. Such eine **blaue Tür** in der dicken roten Wand – das ist ein Wohnungseingang.
4. Geh hinein in den **Vorraum**, von dort durch weitere Türen in die Zimmer.
5. Im Wohnzimmer findest du eine **Glasfront** (gelb/violett) mit einer **Tür** zum hellgrünen **Balkon**.


Wenn dein Finger dabei nie durch Rot, Violett oder Orange muss, hast du den Plan richtig gelesen.

Merksatz

Rot trennt. **Blau** verbindet. **Grün** trägt dich. **Violett** lässt Licht durch, aber keine Menschen. **Orange** steht im Weg.

Die nächsten Seiten zoomen in einzelne Bereiche hinein und erklären Räume, Einbauten, das Stiegenhaus und alle Texte.

Ein Weg durch die Wohnung T37 - Schritt für Schritt

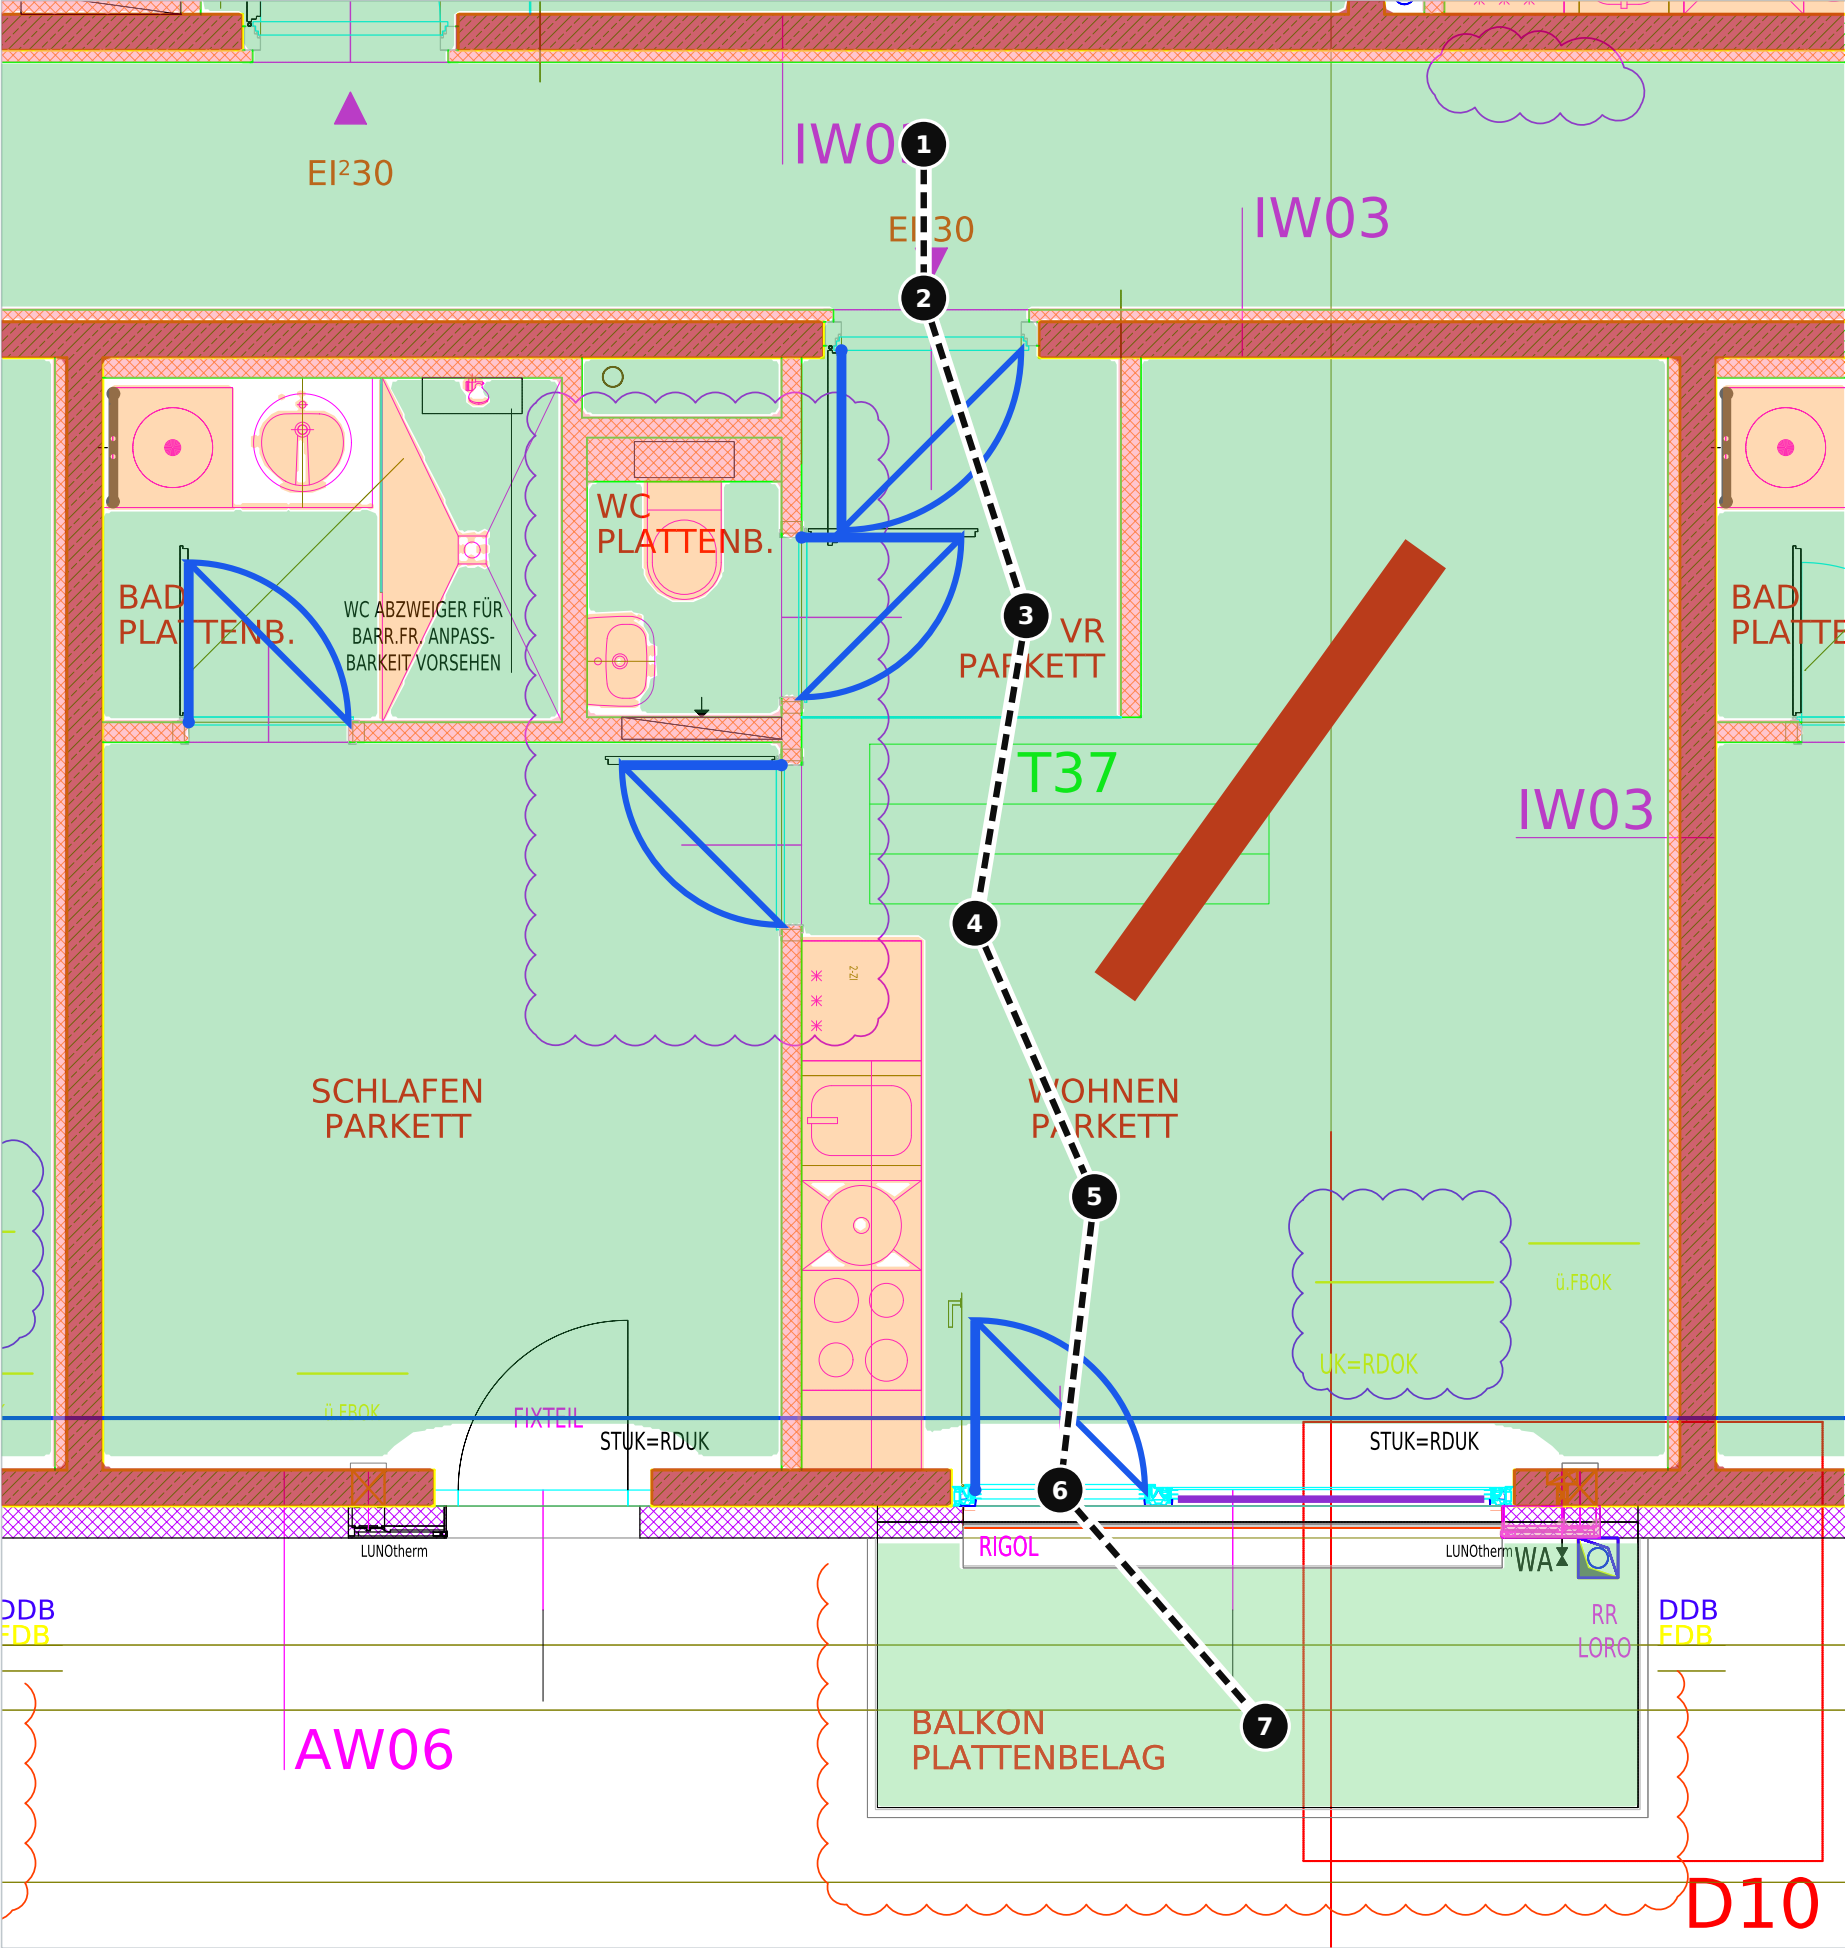


So „gehst“ du durch einen Plan

Die schwarzen Nummern zeigen einen möglichen Weg vom Gang bis auf den Balkon. Jeder Schritt bleibt auf Grün oder geht durch eine blaue Tür.

- 1 – Du stehst im **Gang**. Er ist grün: Hier darf jeder Bewohner gehen.
- 2 – Vor dir ist eine **Lücke in der dicken roten Wand** mit Türblatt und Bogen: die Eingangstür der Wohnung T37.
- 3 – Du bist im **Vorraum (VR)**. Von hier gehen Türen zu WC, Bad und den Zimmern ab.
- 4 – Du folgst dem Grün weiter nach unten, dort wo keine Wand im Weg ist.
- 5 – Du bist im **Wohnzimmer**. Die orange Fläche links an der Wand ist die Küche. Um sie musst du herumgehen.
- 6 – Unten ist die Glasfront. Nur dort, wo der blaue Bogen ist, geht eine Tür auf.
- 7 – Du stehst auf dem **Balkon** (hellgrün). Weiter geht es nicht – der Balkon ist eine **Sackgasse**: Zurück kommst du nur durch dieselbe Tür.

Das ist ein Lernbeispiel zum Planlesen, kein geprüfter Rettungs- oder Fluchtweg.

Räume erkennen: die Wohnung T37 und ihre Zimmer

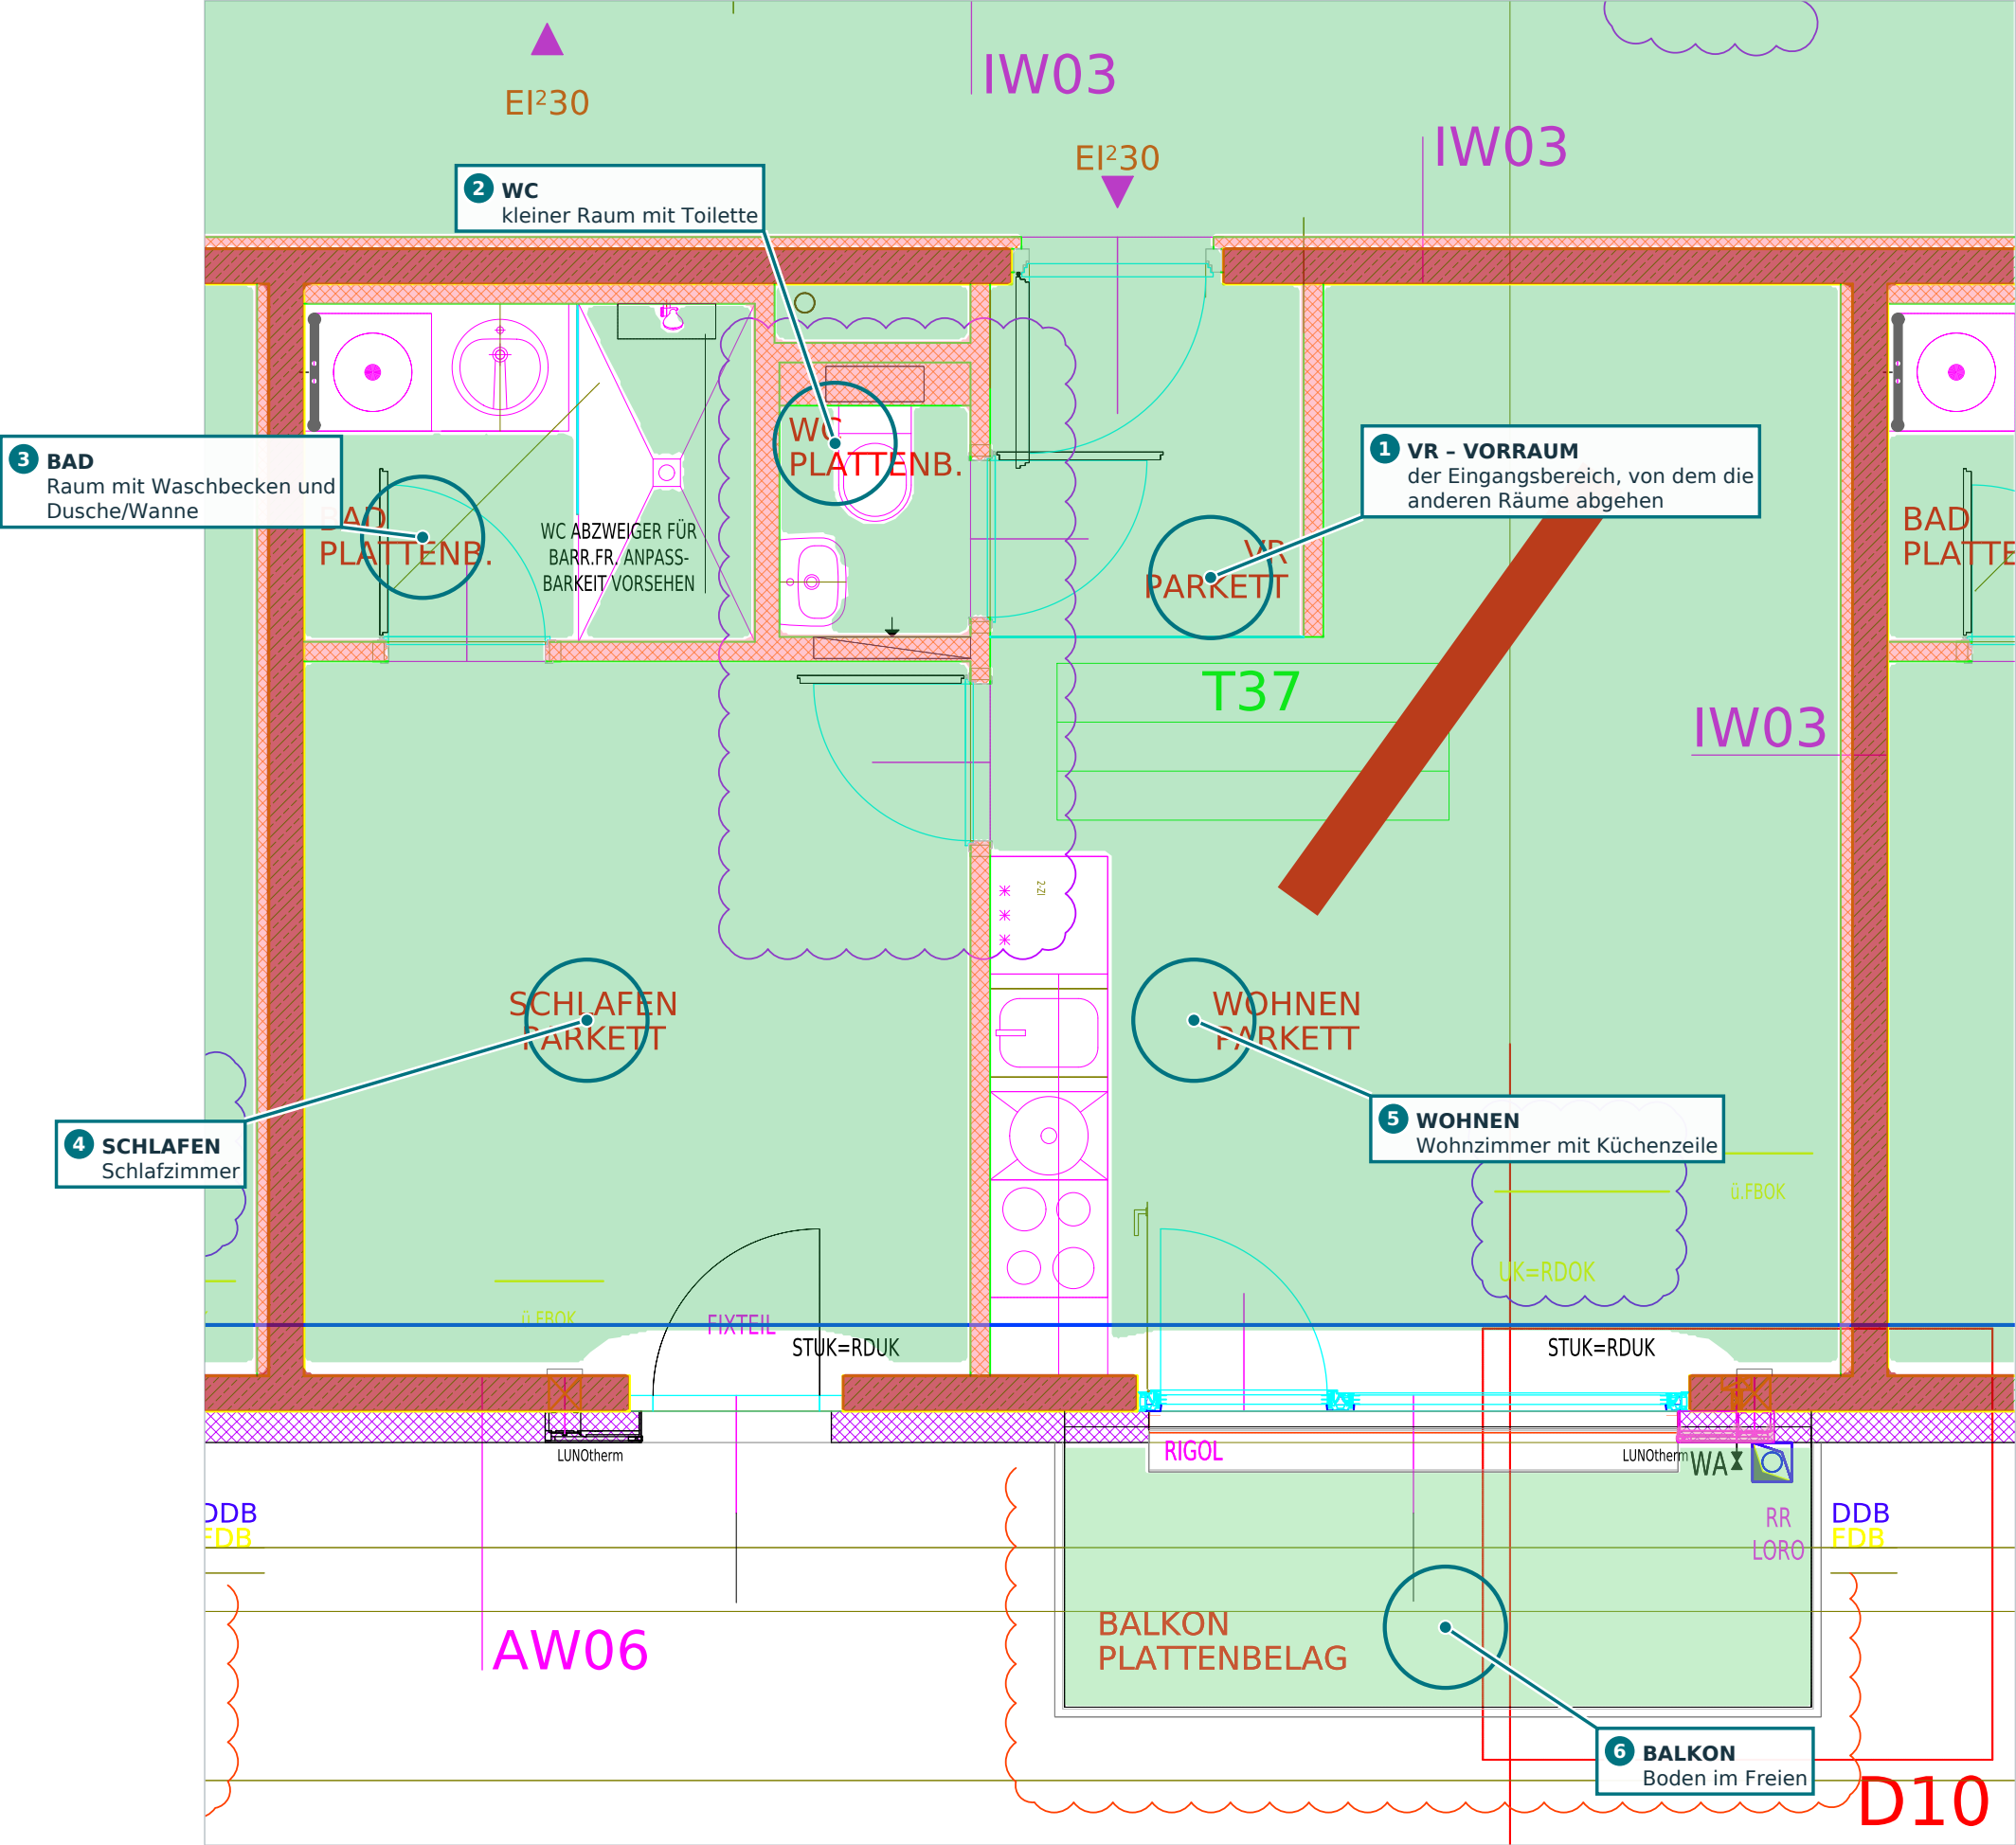

Was ist ein Raum?

Ein Raum ist ein Stück Fußboden, das rundherum von **Wänden** (rot) umschlossen ist. Hinein und hinaus kommt man durch **Türen**.

Woran erkenne ich, wo ein Raum beginnt und endet?

Folge mit dem Finger der roten Wand rund um eine grüne Fläche. Wo du wieder am Anfang bist, ist der Raum zu Ende. Wo die Wand eine Lücke mit Türbogen hat, geht es in den nächsten Raum.

Woher weiß ich, wie ein Raum heißt?

In jedem Raum steht ein **Raumstempel** in roter Schrift. Oben steht der **Name**, darunter der **Bodenbelag**:


PARKETT = Holzboden · **PLATTENBELAG** oder **PLATTENB.** = Fliesen/Platten (in Bad, WC, Gang, Balkon).

Die Wohnung T37 hat:

(1) Vorraum, (2) WC, (3) Bad, (4) Schlafzimmer, (5) Wohnzimmer mit Küche und (6) einen Balkon.

Die Namen stammen direkt aus den Raumstempeln des Plans. Ich habe keinem Raum eine Funktion dazu erfunden. Raumgrößen (m²) sind in diesem Plan nicht eingetragen.

Bad und WC: Was dünn gezeichnet ist, steht am Boden

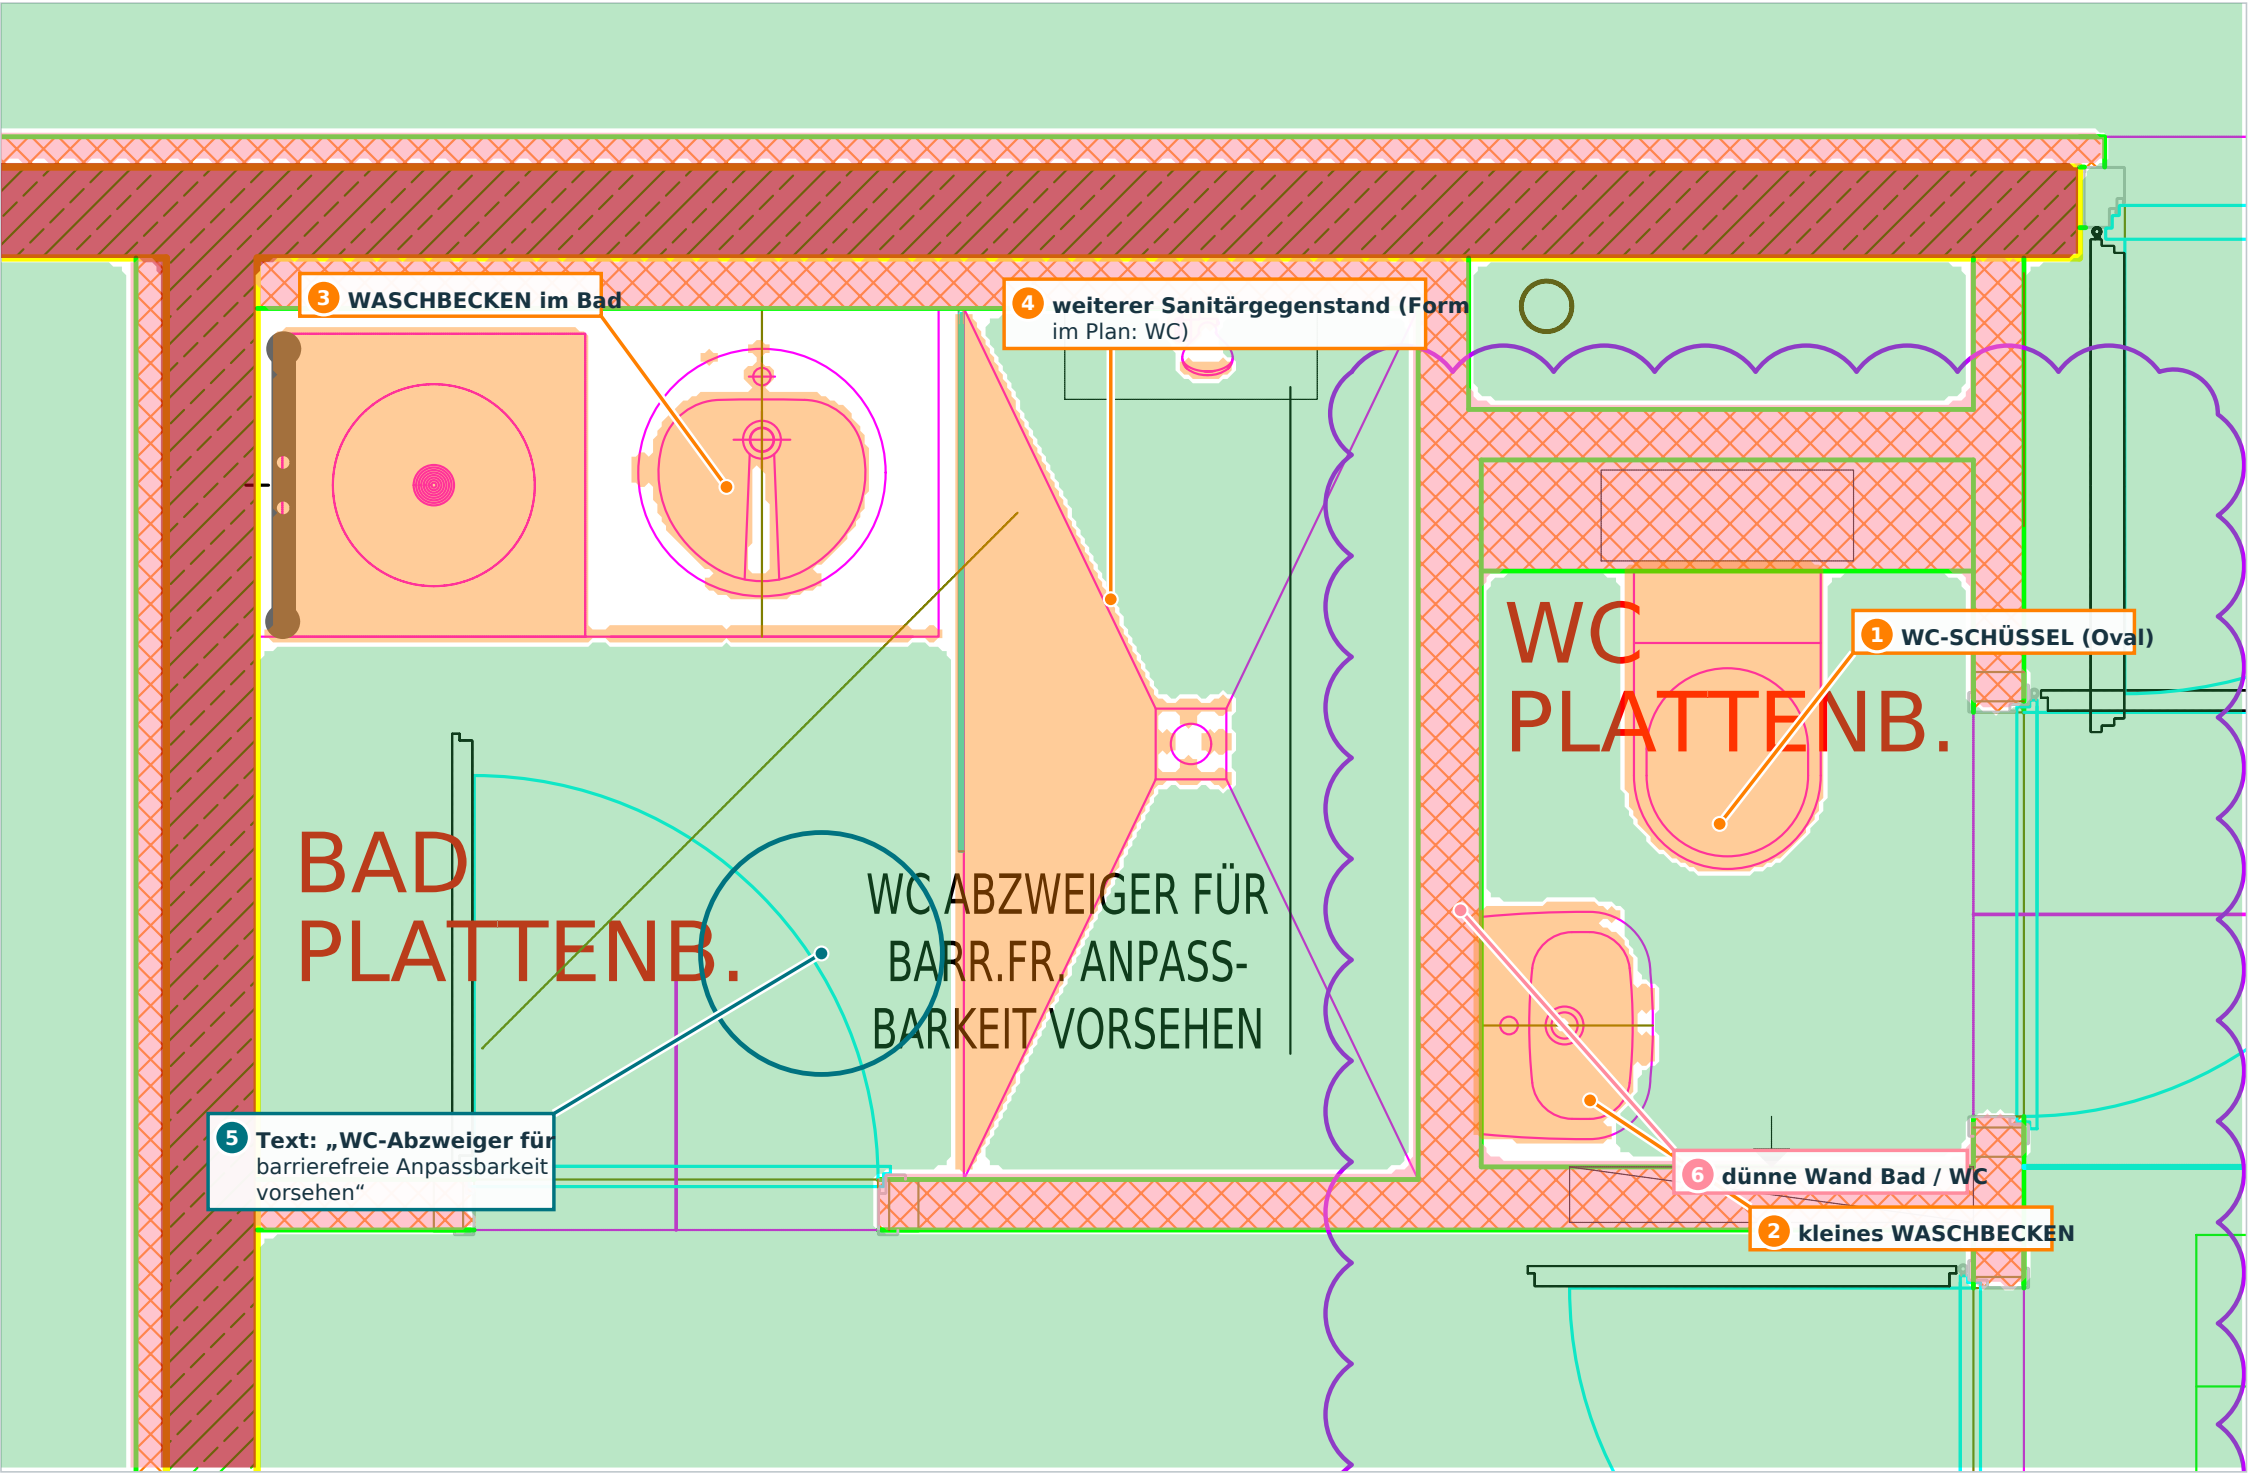

Was sind Einbauten?

Einbauten sind Dinge, die fest im Raum stehen: WC, Waschbecken, Dusche, Badewanne, Küchenzeile, eingebaute Kästen. Sie sind **keine Wände** – aber sie stehen im Weg.

Wie sehen sie im Plan aus?

Sie werden mit **dünnen Linien** gezeichnet (hier magenta), weil sie unterhalb der gedachten Schnitthöhe stehen. Man sieht sie also „von oben drauf“.

Oval in einem abgerundeten Rechteck = WC-Schüssel (1).

Kreis in einem Rechteck = Waschbecken (2, 3).


Orange sind diese Flächen im Heft ausgespart: Dort kann man nicht gehen.

Der Text (5)

Im Bad steht ein Hinweis für die Baufirma: Es soll ein Anschluss vorbereitet werden, damit man das Bad später **barrierefrei** umbauen kann. Das ist eine Bauanweisung, kein Gegenstand.

Welche Form genau eine Dusche oder Wanne ist, lässt sich bei so kleinen Symbolen nicht in jedem Fall sicher sagen. Ich benenne nur, was die Form eindeutig zeigt.

Die Küchenzeile im Wohnzimmer

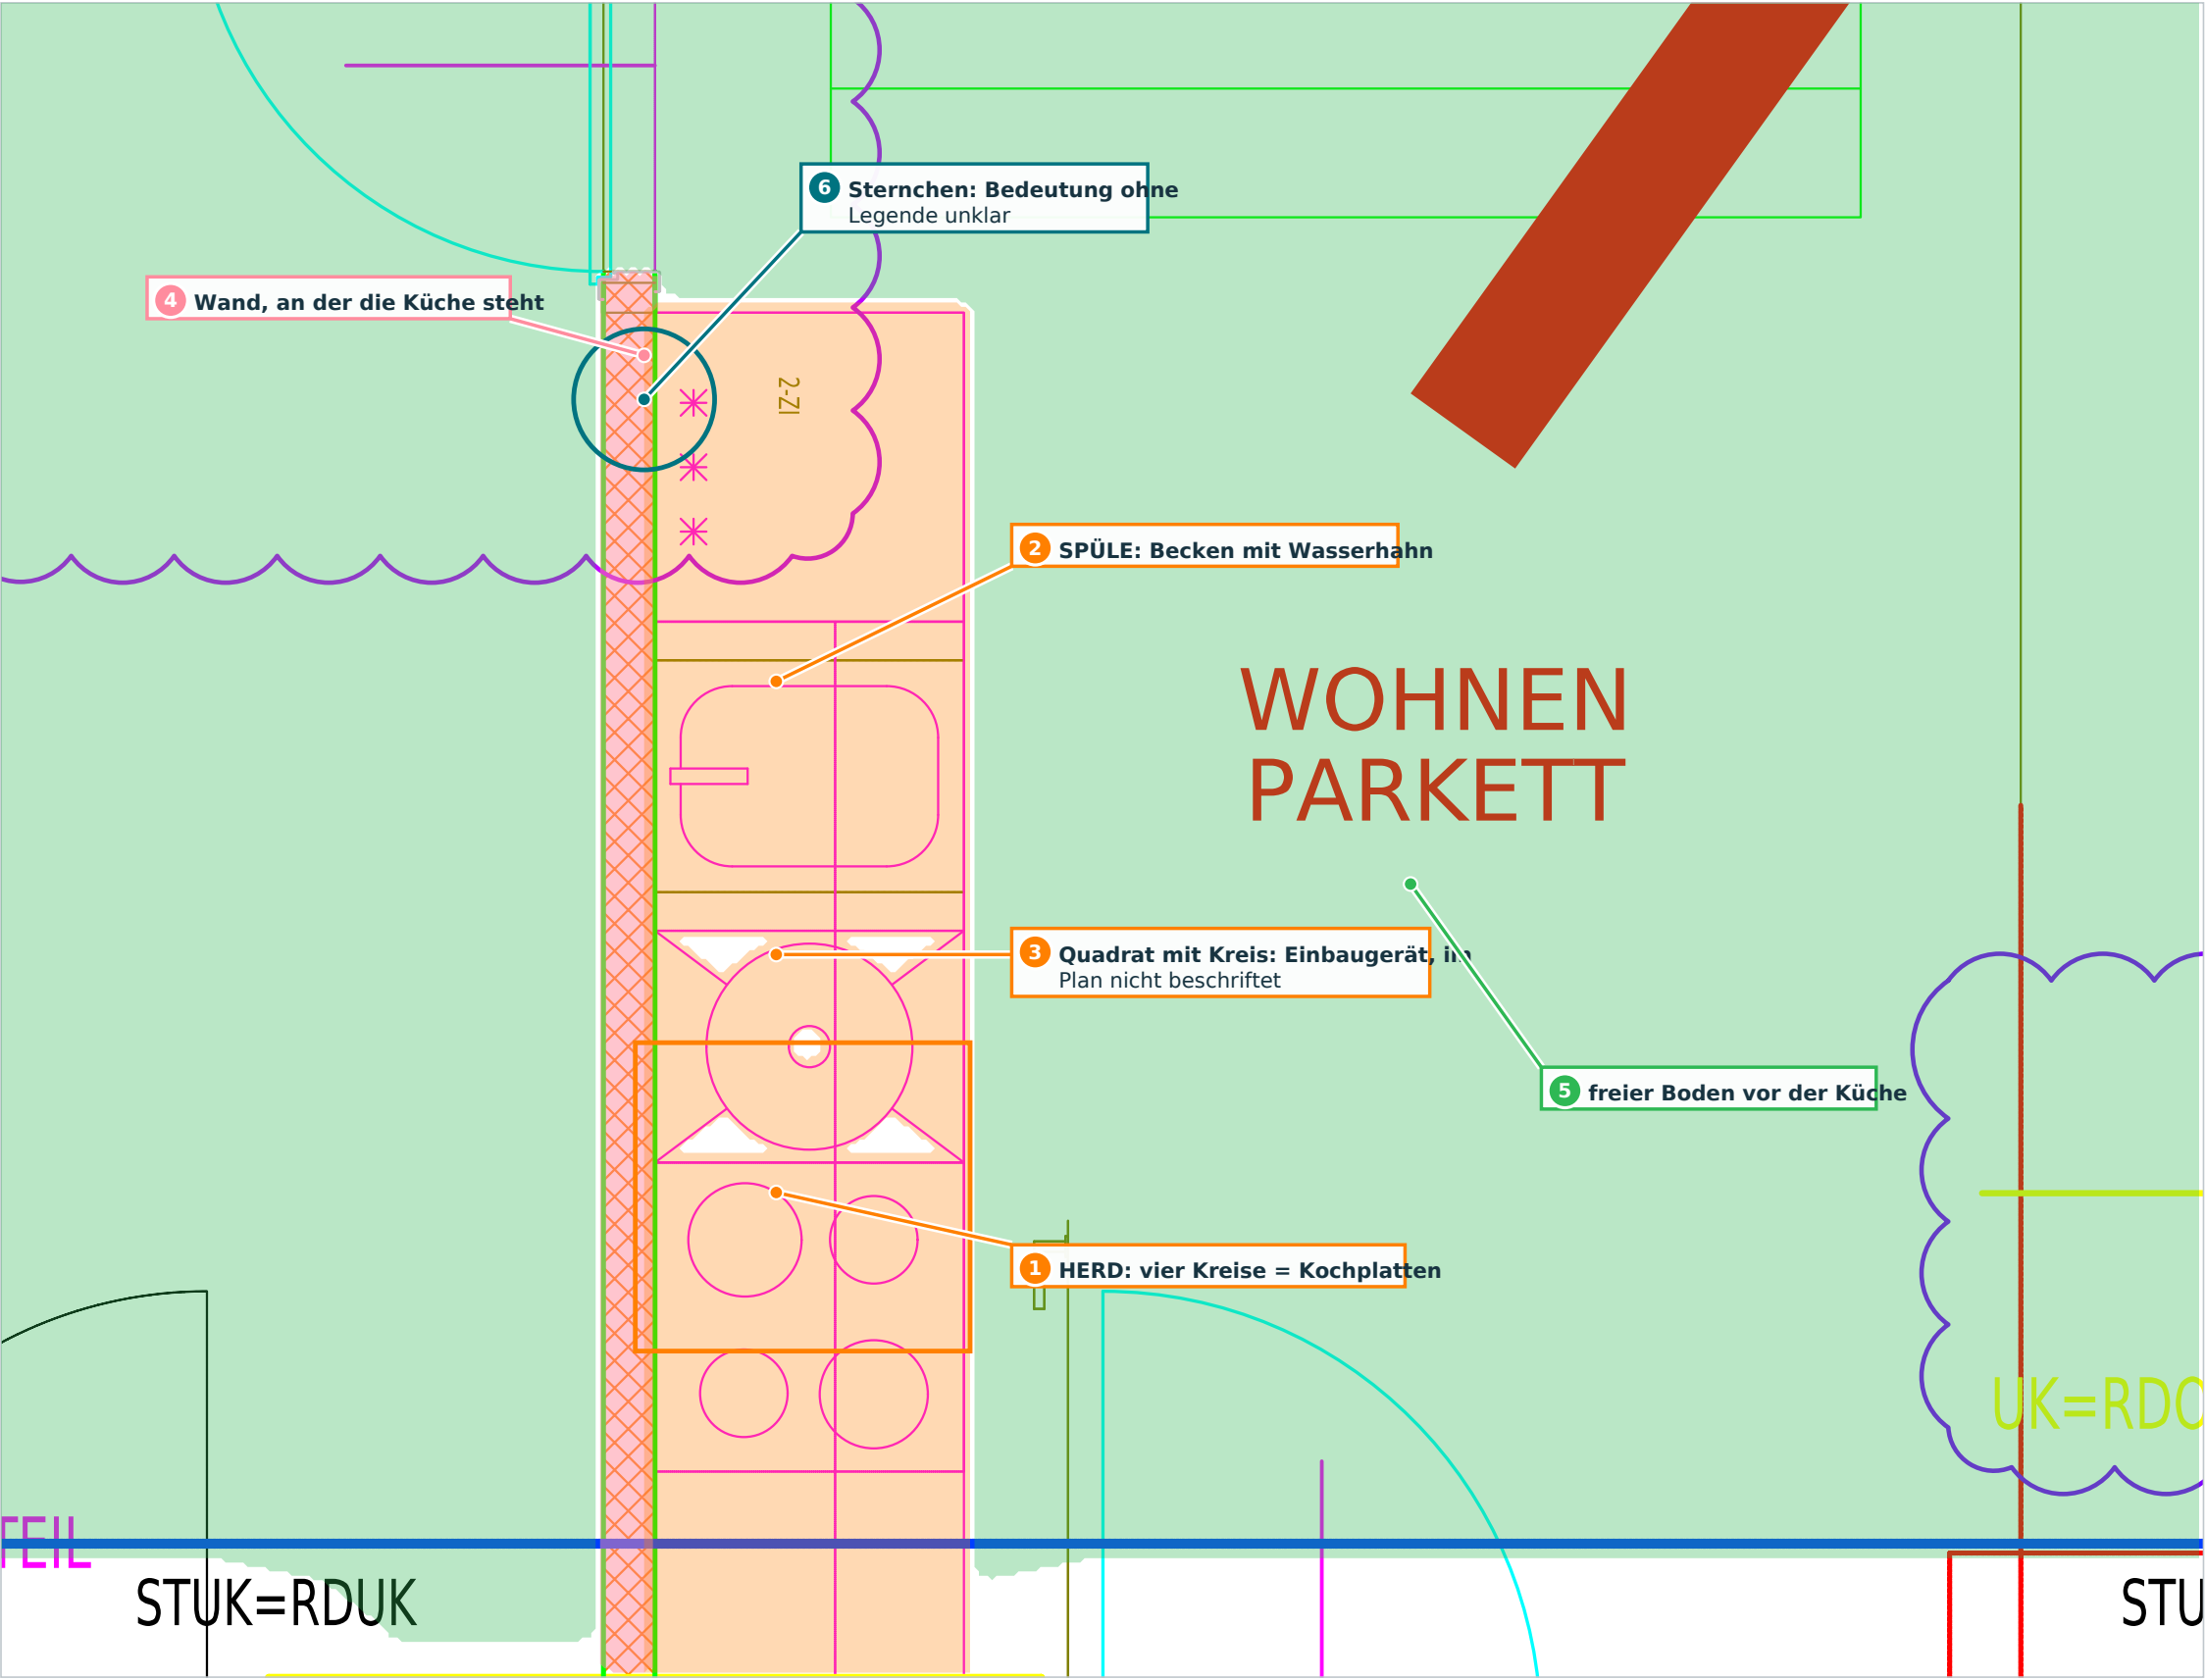

Was ist das?

Eine **Küchenzeile**: Küchenschränke in einer Reihe an einer Wand, mit Spüle und Herd. Sie gehört zum Raum WOHNEN.


Woran erkenne ich sie?

Ein langer, schmaler Streifen direkt an der Wand, unterteilt in Rechtecke (die einzelnen Schränke). In einem Rechteck liegen **vier Kreise** – das sind die Kochplatten eines Herds (1). Ein abgerundetes Becken mit einem kleinen Balken (Wasserhahn) ist die Spüle (2). Das Quadrat mit Kreis (3) ist ein Einbaugerät; welches genau, steht nicht dabei. Die Sternchen (6) werden nicht erklärt.

Was bedeutet das für das Gehen?

Die Küche ist ein **Hindernis** (orange). Man steht **davor** auf dem grünen Boden (5), um zu kochen. Die Küche teilt aber den Raum nicht – das Wohnzimmer bleibt ein einziger Raum.

Die genaue Einteilung der Küchenschränke ist im Plan nur angedeutet; es ist ein Einrichtungsvorschlag, keine fertige Küchenplanung.

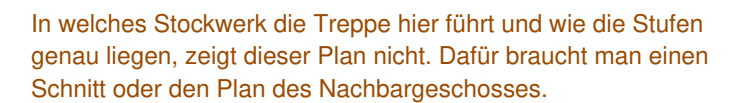

Der Gang: die „Straße“ im Inneren des Hauses

Was ist ein Gang?

Ein Gang (auch Flur oder Verkehrsfläche) ist ein langer, schmaler Raum, der **andere Räume miteinander verbindet**. Man hält sich dort nicht lange auf – man geht durch.

Woran erkenne ich ihn hier?


Ein langes grünes Band zwischen zwei **dicken** roten Wänden (2, 3). In der Mitte steht der Raumstempel **GANG PLATTENBELAG** (1).

In beiden Wänden sind in regelmäßigen Abständen **Türen**. Das sind die Eingänge zu den Wohnungen. Neben jeder dieser Türen steht die Brandschutzangabe **EI²30**.


Warum sind die Wände hier dick?

Sie trennen den gemeinsamen Gang von den privaten Wohnungen. Solche Wände müssen stabil, schallschützend und brandschützend sein. (Genauere Anforderungen stehen nicht im Plan.)

Die grüne Fläche zeigt den Boden. Ob der Gang als Fluchtweg zugelassen ist, kann ein Grundriss allein nicht beweisen.

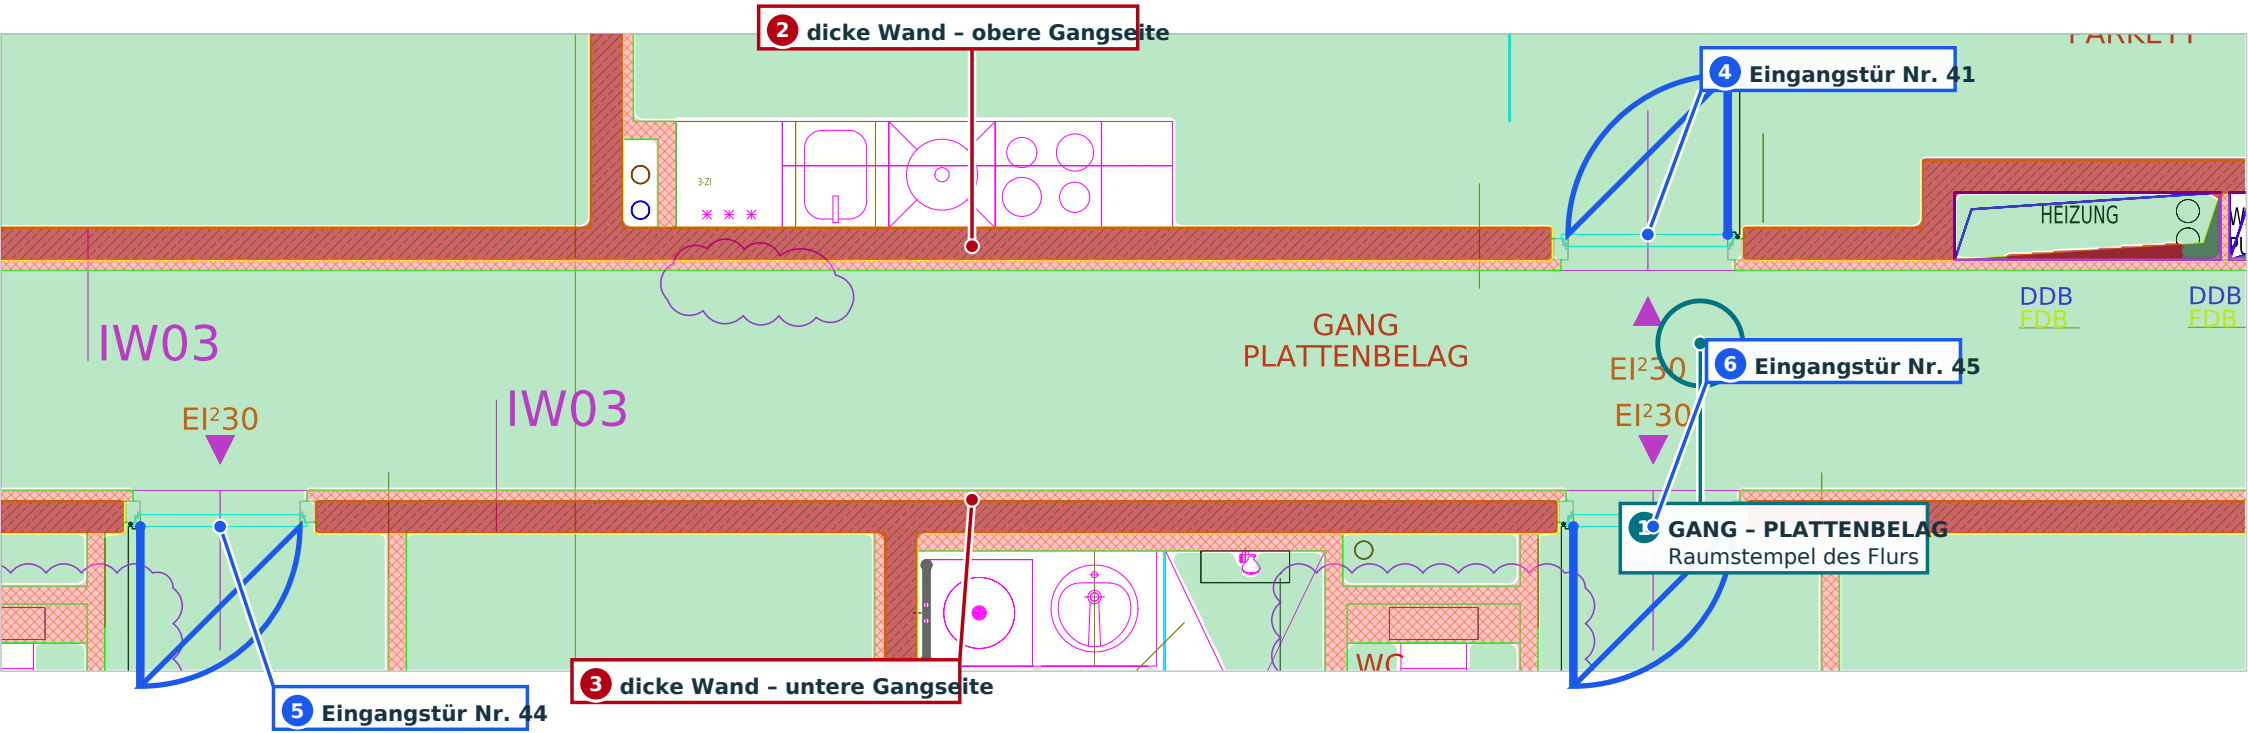

Draußen und doch begehbar: Balkon und Loggia

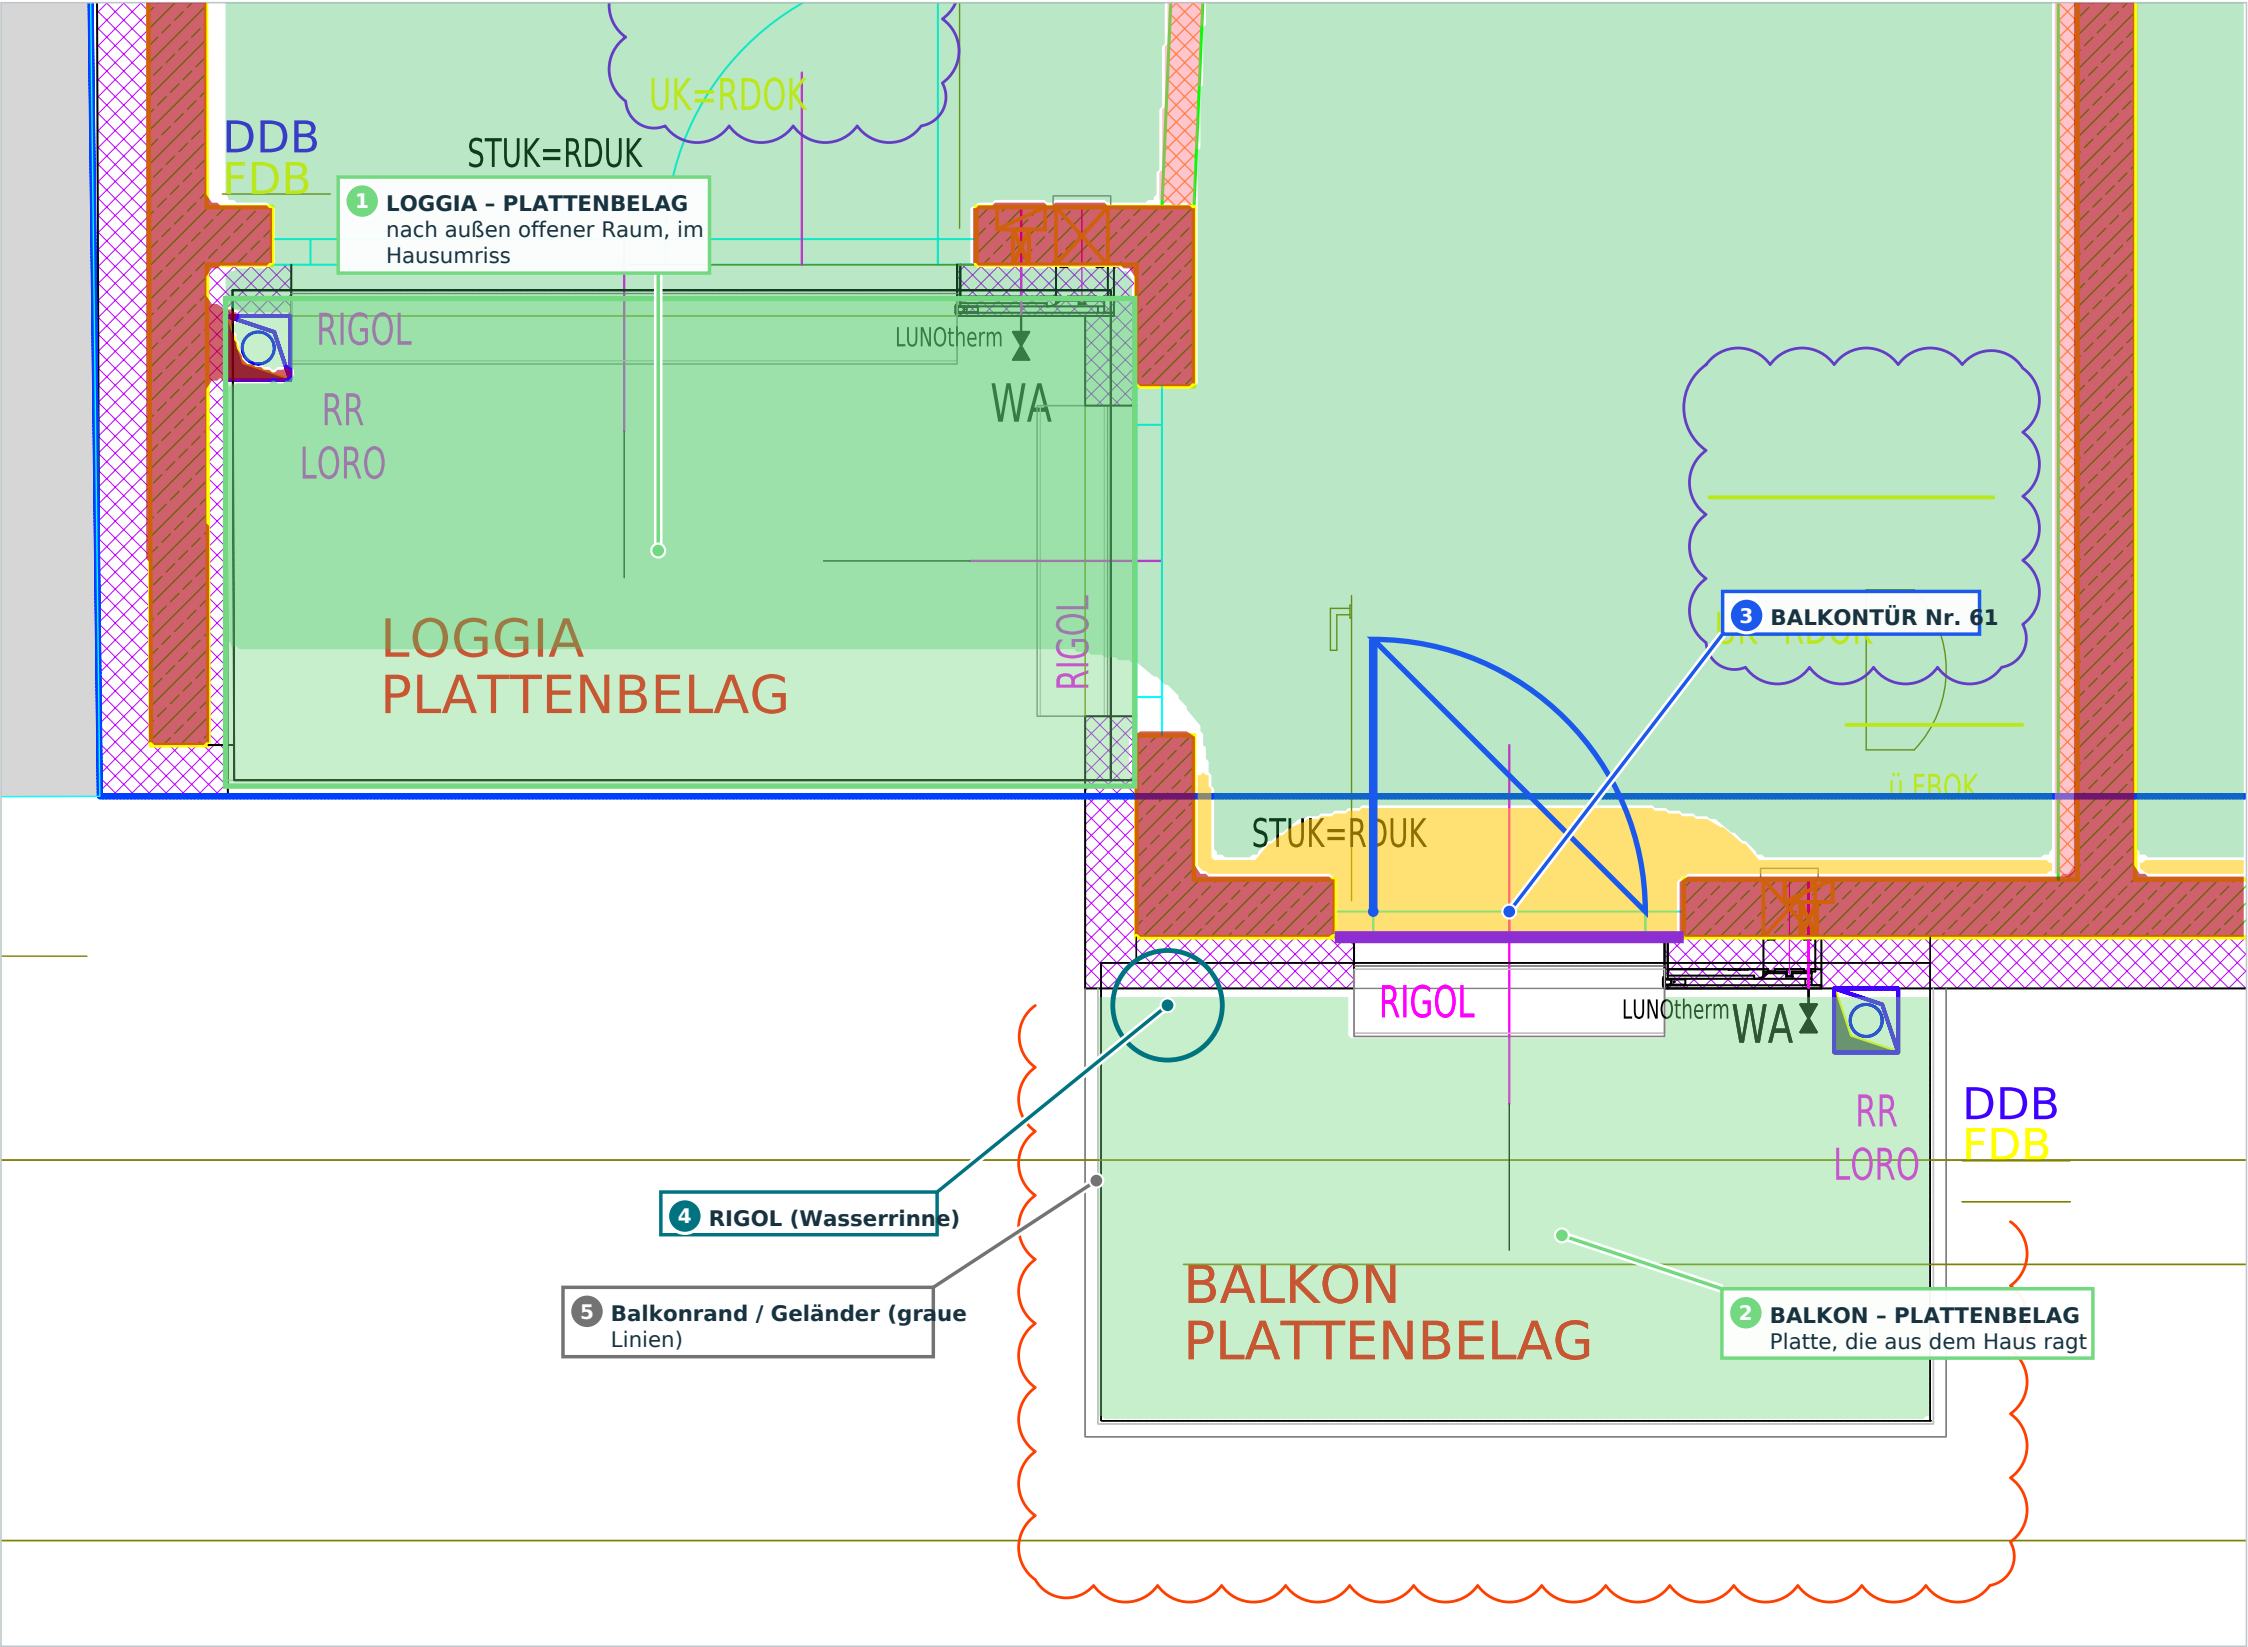

Balkon (2)

Was: eine Bodenplatte **außen** vor der Fassade, mit Geländer.
Wie im Plan: ein Rechteck aus grauen Linien außerhalb der Außenwand, darin der Text **BALKON PLATTENBELAG**.
Zugang: nur über die Balkontür (3) aus der Wohnung.

Loggia (1)

Was: ähnlich wie ein Balkon, aber **in** das Gebäude hineingeschnitten – also an mehreren Seiten von Wänden umgeben und nur zu einer Seite offen. **Hier:** links unten bei der Wohnung T36, Text **LOGGIA PLATTENBELAG**.

Warum hellgrün?


Man kann darauf gehen, aber es ist **draußen**: Regen, Wind, kein Heizkörper. Zudem ist es eine Sackgasse – weiter geht es nur zurück in die Wohnung.

Die Linien am Rand (5)

Die grauen Doppellinien am Rand zeigen die Kante der Platte bzw. das Geländer. **Über das Geländer** geht kein Weg.

Wo genau das Geländer steht und wie hoch es ist, steht nicht eindeutig im Plan.

Was die Texte im Plan bedeuten - direkt am Beispiel

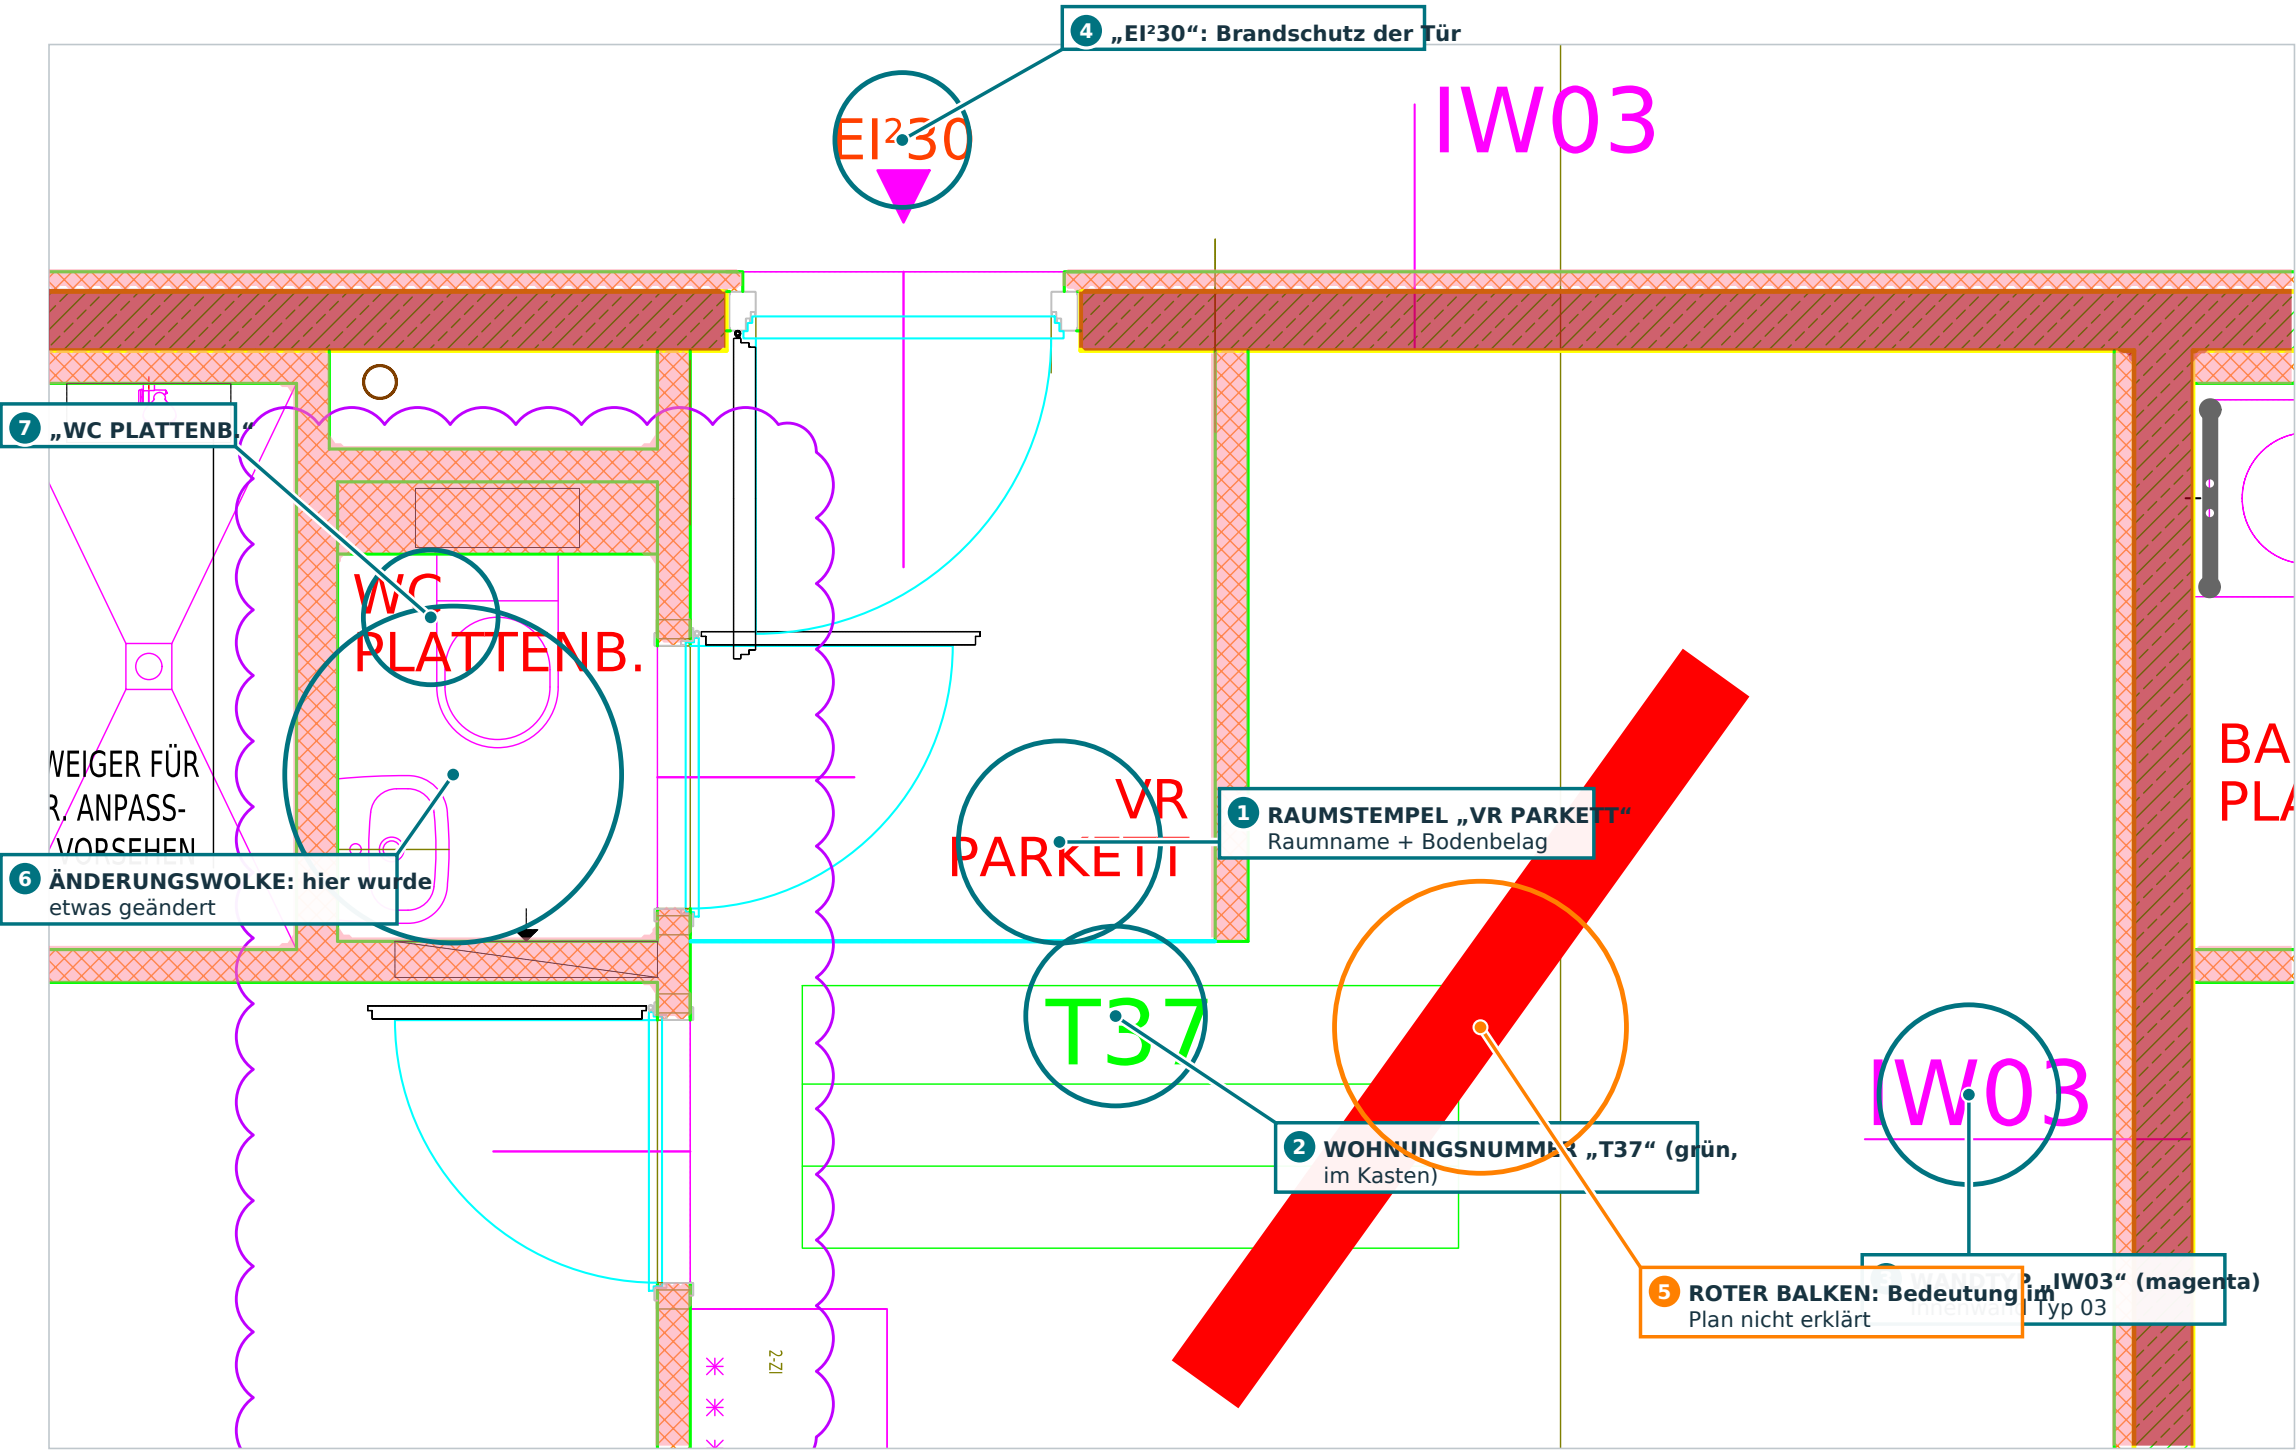

Schrift ist kein Bauteil

Texte und Symbole sind **Informationen**. Man kann sie nicht anfassen. Sie erklären, was an einer Stelle ist oder gemacht werden soll.

(1) **Raumstempel** – rot, zweizeilig: Name + Bodenbelag. VR = Vorraum.

(2) **Wohnungsnummer** – grün in einem Kasten mit Linien. Die leeren Zeilen im Kasten sind vermutlich für weitere Angaben (z. B. Fläche) vorgesehen, hier aber leer.

(3) **Wandtyp** – magenta, beginnt mit **IW** (Innenwand) oder **AW** (Außenwand) und einer Nummer.

(4) **EI²30** – Brandschutzklasse der Tür (30 Minuten).

(6) **Wolke** – Planer zeichnen solche Wolkenlinien um Stellen, die sich seit der letzten Fassung geändert haben. Sie sind **keine Wände** und keine Möbel.

(7) **PLATTENB.** ist eine Abkürzung für Plattenbelag.

(5) **Die dicken roten Schrägbalken** gibt es in fast jeder Wohnung. Der Plan hat keine Legende dafür. Ich deute sie deshalb **nicht**. Sicher ist nur: Sie sind kein Bauteil, das man im Grundriss begehen oder umgehen müsste.

Hinweiszeichen im ganzen Plan

Zeichen, die auf andere Pläne verweisen

Ein Grundriss ist fast nie der einzige Plan eines Hauses. Viele Zeichen sagen: „**Schau in einem anderen Plan nach.**“

Schnittlinien (1–4): Ein Buchstabe mit einem kleinen Dreieck an beiden Enden einer langen dünnen Linie. Dort ist das Haus in einem anderen Plan **senkrecht** aufgeschnitten gezeichnet. Das Dreieck zeigt die Blickrichtung. In diesem Plan gibt es die Schnitte A, B, D, F und G.


Detailverweise (5–7): D mit Nummer, oft mit einem Rahmen. Dort gibt es eine vergrößerte Zeichnung dieser Stelle.

Wandtypen (8): AW = Außenwand, IW = Innenwand. Die Nummer verweist auf eine Liste mit dem Wandaufbau.

Änderungswolken (9): markieren geänderte Stellen.

(10) Eine dicke blaue Linie läuft außen entlang des Gebäudes. Ohne Legende ist nicht eindeutig, was sie darstellt (z. B. eine Deckenkante). Sie ist jedenfalls keine Wand im Schnitt.

Die Positionen der Zeichen sind hier eingekreist. Die Linien selbst sind im Original sehr dünn und laufen über das ganze Blatt.

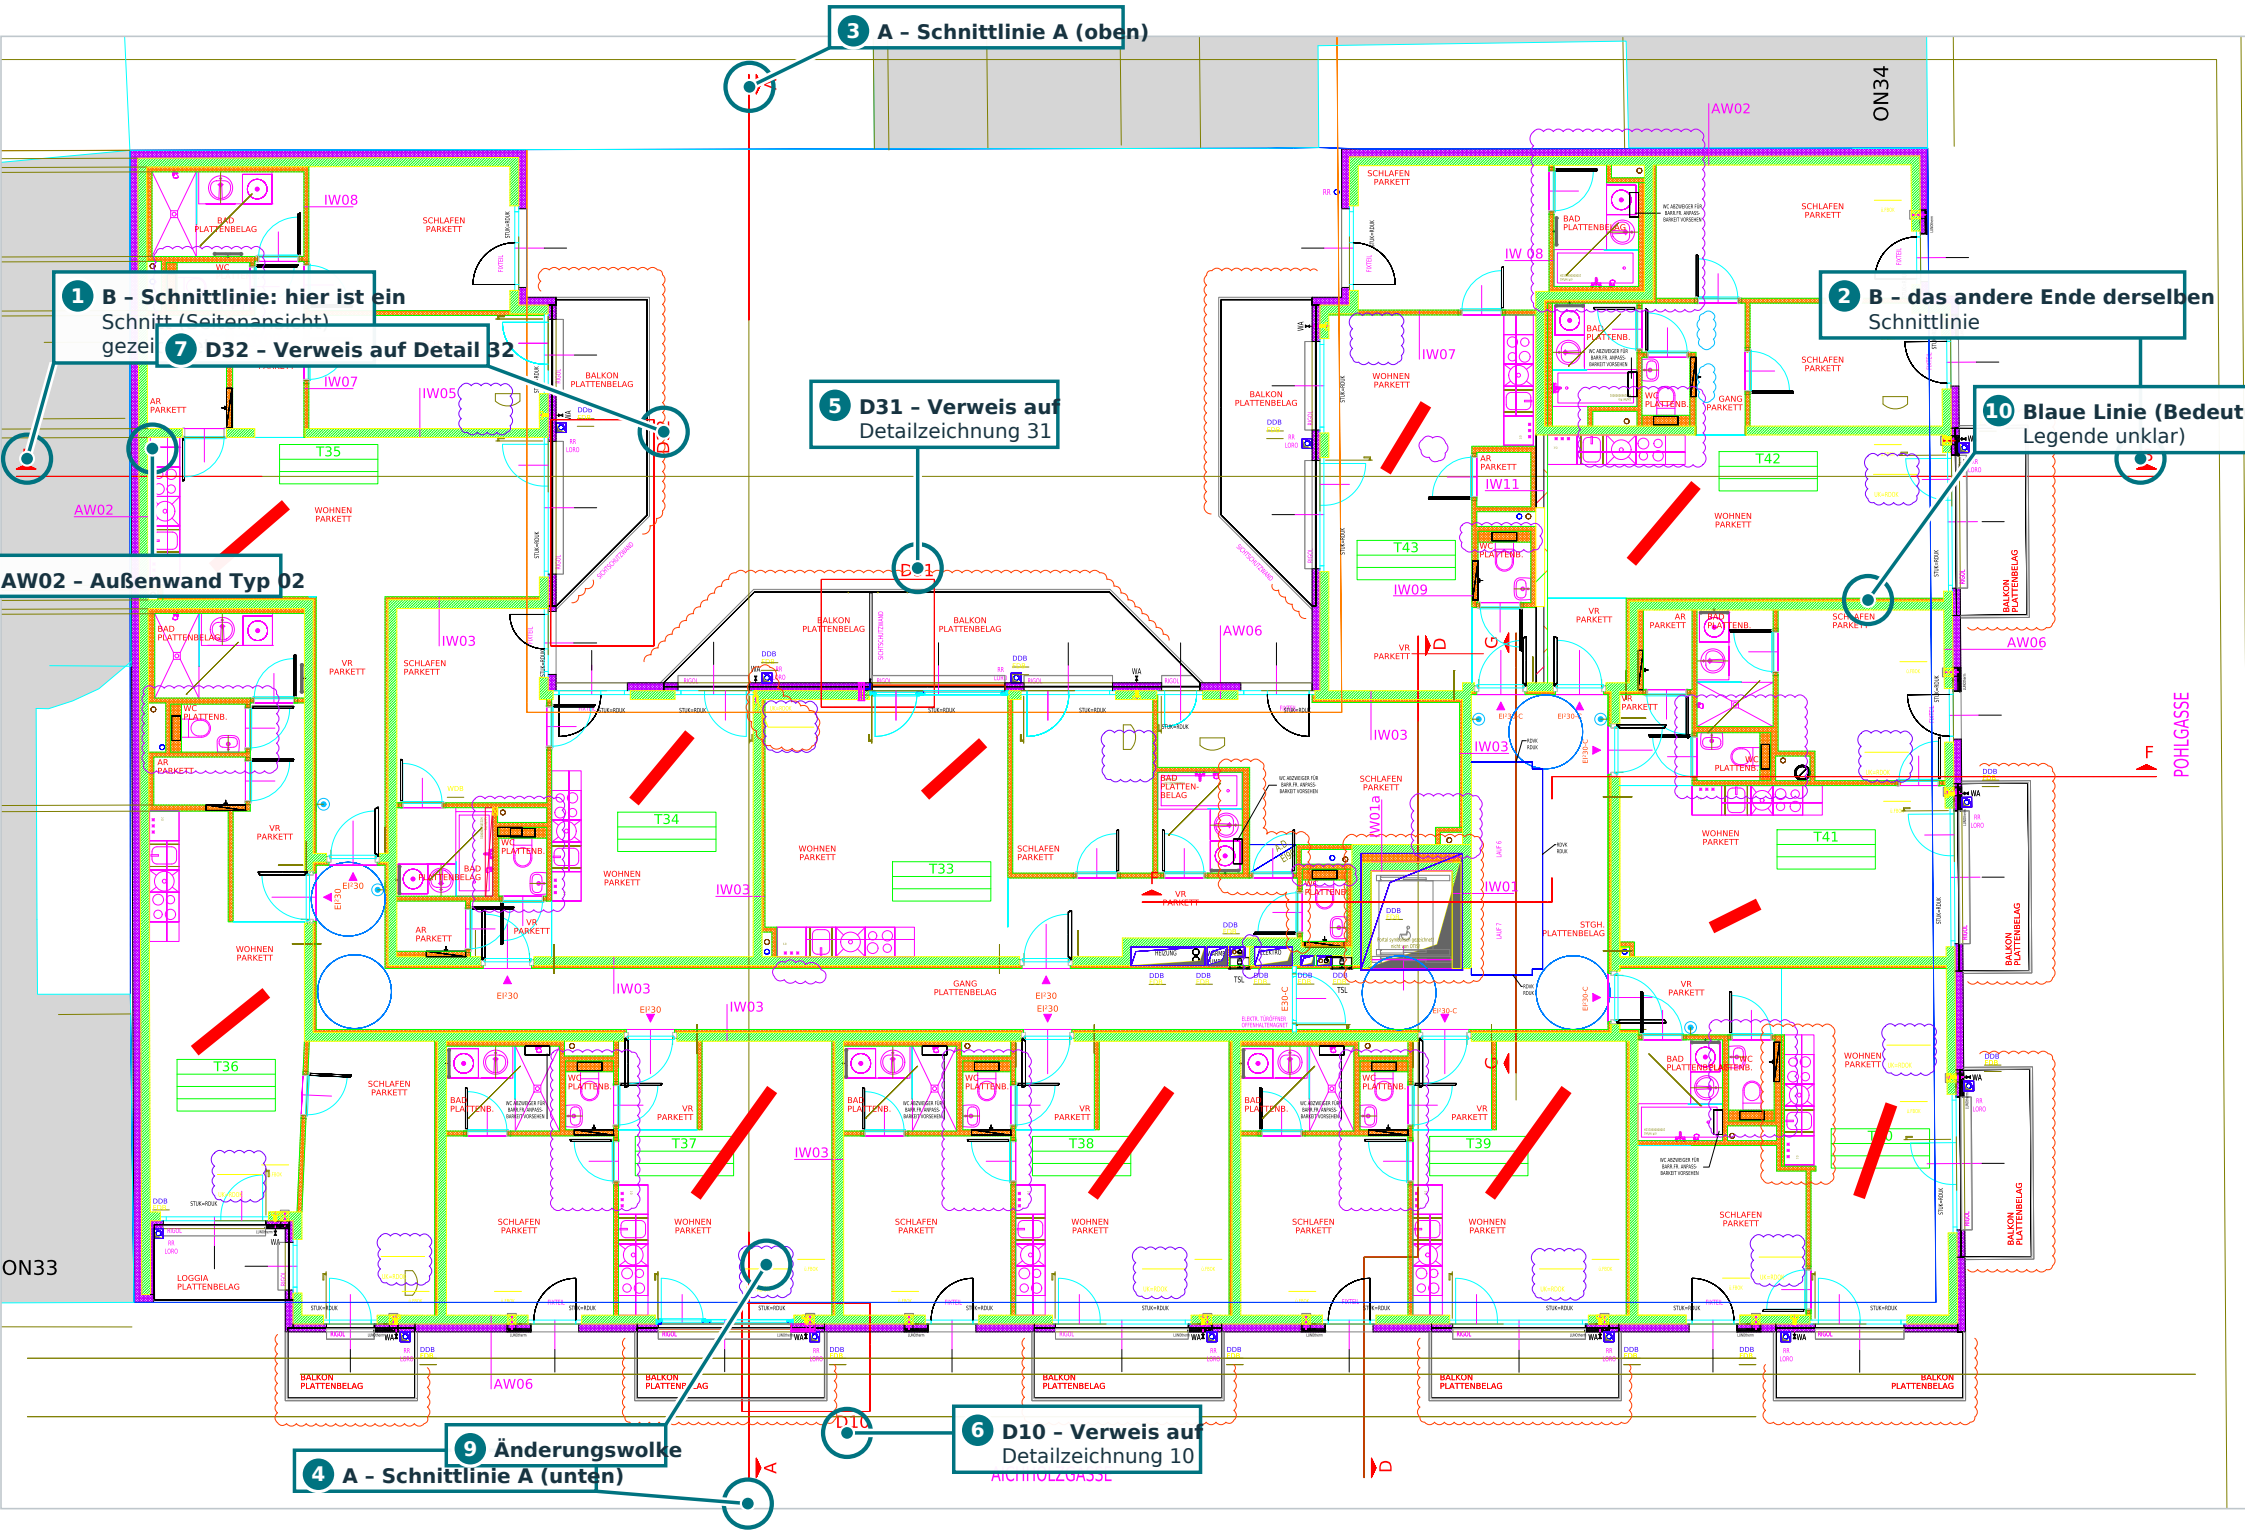

Lexikon: alle Abkürzungen aus diesem Plan

Im Plan steht	Bedeutung in einfachen Worten	Wie sicher?
VR	Vorraum – Eingangsbereich der Wohnung	sicher (Raumstempel)
AR	Abstellraum – kleiner Raum für Vorräte, Staubsauger usw.	sicher (übliche Abkürzung)
WC / BAD	Toilette / Badezimmer	sicher
SCHLAFEN, WOHNEN	Schlafzimmer, Wohnzimmer	sicher
GANG	Flur, der die Wohnungen erschließt	sicher
STGH.	Stiegenhaus (Treppenhaus)	sicher
LAUF 6 / LAUF 7	Treppenlauf Nr. 6 und 7 – ein Treppenstück ohne Unterbrechung	sicher
PARKETT	Holzfußboden	sicher
PLATTENBELAG, PLATTENB.	Boden aus Fliesen oder Platten	sicher
BALKON, LOGGIA	begehbare Flächen im Freien	sicher
T33 ... T43	Top = Wohnungsnummer	sicher
IW01 ... IW11	Innenwand-Typ mit Nummer	sicher (Aufbau steht nicht im Plan)
AW02, AW06	Außenwand-Typ mit Nummer	sicher (Aufbau steht nicht im Plan)
EI²30	Brandschutzklasse: 30 Minuten raumabschließend und wärmedämmend	sicher (Norm-Bezeichnung)
EI²30-C	wie oben, zusätzlich selbstschließend	sicher (Norm-Bezeichnung)
FIXTEIL	fest eingebautes Glas, das nicht aufgeht	sicher
RIGOL	Entwässerungsrinne vor Balkontüren	sicher
STUK=RDUK	Sturzunterkante = Rohdeckenunterkante: Oberkante der Öffnung liegt an der Deckenunterseite	sehr wahrscheinlich
UK=RDOK, ü.FBOK	Höhenangaben: Unterkante = Rohdeckenoberkante; „über Fertigfußbodenoberkante“	wahrscheinlich
RDVK, RDUK	Rohdecken-Vorderkante / Rohdecken-Unterkante (an der Treppenöffnung)	wahrscheinlich
DDB / FDB	Deckendurchbruch / Fußbodendurchbruch (Loch für Leitungen)	wahrscheinlich
RR LORO	RR = Regenrohr, LORO = vermutlich Herstellername	wahrscheinlich
WA	bei der Fassade, Bedeutung nicht erklärt (evtl. Wasseranschluss)	unsicher
SICHTSCHUTZWAND	Wand am Balkon gegen Einblick vom Nachbarn	sicher
HEIZUNG, WÄRMEPUMPE, ELEKTRO	Beschriftung der Leitungsschächte	sicher
TSL	Bedeutung ohne Legende nicht eindeutig	unsicher
A.D. EI90	Brandschutz 90 Minuten bei einem Bauteil im Kern; „A.D.“ nicht erklärt	teilweise unsicher
ON33, ON34	Bezeichnung der grauen Nachbargebäude/Nachbargrundstücke	wahrscheinlich
D10, D31, D32	Verweis auf Detailzeichnung Nr. 10, 31, 32	sicher
A, B, D, F, G	Schnittlinien (Verweis auf Schnittpläne)	sicher

Was dieser Plan NICHT verrät

Ein guter Planleser weiß nicht nur, was im Plan steht – sondern auch, **was fehlt**. Bei diesem Plan fehlt:

1. Maße

Der Dateiname sagt „ohne Masse“: Es gibt keine Maßketten. Wie breit ein Raum oder eine Tür genau ist, lässt sich nicht ablesen. Darum habe ich in diesem Heft keine Längen angegeben.

2. Eine Legende

Es gibt keine Erklärung der Farben und Muster. Die Zuordnung „gelb/grün schraffiert = dicke Wand“ habe ich aus dem Plan selbst abgelesen: Diese Streifen verhalten sich überall wie Wände.

3. Tragende Wände

Welche Wand das Haus trägt, steht nicht im Plan. Dafür braucht man den Statik-/Tragwerksplan.

4. Materialien

Ob eine Wand aus Beton, Ziegel oder Gipskarton ist, geht nur aus dem Wandkatalog (IW/AW-Typen) hervor, der nicht beiliegt.

5. Höhen

Ein Grundriss zeigt nur „von oben“. Wie hoch Räume, Fenster, Brüstungen oder Schwellen sind, zeigen Schnitte und Ansichten.

6. Die Treppenstufen

Das Stiegenhaus ist nur als Öffnung mit „LAUF 6 / LAUF 7“ gezeichnet. Stufen, Laufrichtung und Zielgeschoss fehlen.

7. Einige Zeichen

Die roten Schrägbalken, die dicke blaue Linie, „TSL“, „WA“ und „A.D.“ sind ohne Legende nicht eindeutig. Ich habe sie markiert, aber nicht gedeutet.

8. Der wirkliche Zustand

Der Plan zeigt, wie gebaut werden **soll**. Ob eine Tür später offen, zu oder versperrt ist, ob Möbel anders stehen – das weiß kein Plan.

9. Fluchtwege und Barrierefreiheit

Die grünen Flächen zeigen Boden. Sie sind **keine** geprüfte Freigabe als Fluchtweg und keine Prüfung, ob ein Rollstuhl durchpasst.

10. Wie die Farben entstanden sind

Wände, Türbögen, Wandöffnungen und Bodenflächen wurden aus der Vektorgeometrie des Original-PDFs abgeleitet (nach Linienfarbe und -art), danach an vielen Stellen mit dem Original verglichen. Balkone wurden von ihrer Beschriftung aus bis zur Randlinie gefüllt. Kleine Abweichungen an Kanten sind möglich.

Merke: Wenn der Plan etwas nicht eindeutig zeigt, ist die richtige Antwort „steht nicht im Plan“ – nicht raten.

Quiz: Was ist an den zehn nummerierten Stellen?

So geht das Quiz

Auf dem Plan links ist **keine Farbe**. Du siehst nur das Original – so wie in echt.


Schau dir jede nummerierte Stelle an und frag dich:

- 1. Was ist das?
- 2. Woran erkenne ich es?
- 3. Kann ich dort gehen?


Schreib dir deine Antworten auf. Die Lösungen stehen auf der nächsten Seite – mit Farben.

Zur Auswahl stehen

Tür · dicke Wand · dünne Wand · Glas · Balkon · Aufzug · Leitungsschacht · Raumstempel · Küchenzeile · Gang
Tipp: Blättere zurück zu „Die Sprache der Linien“, wenn du unsicher bist.

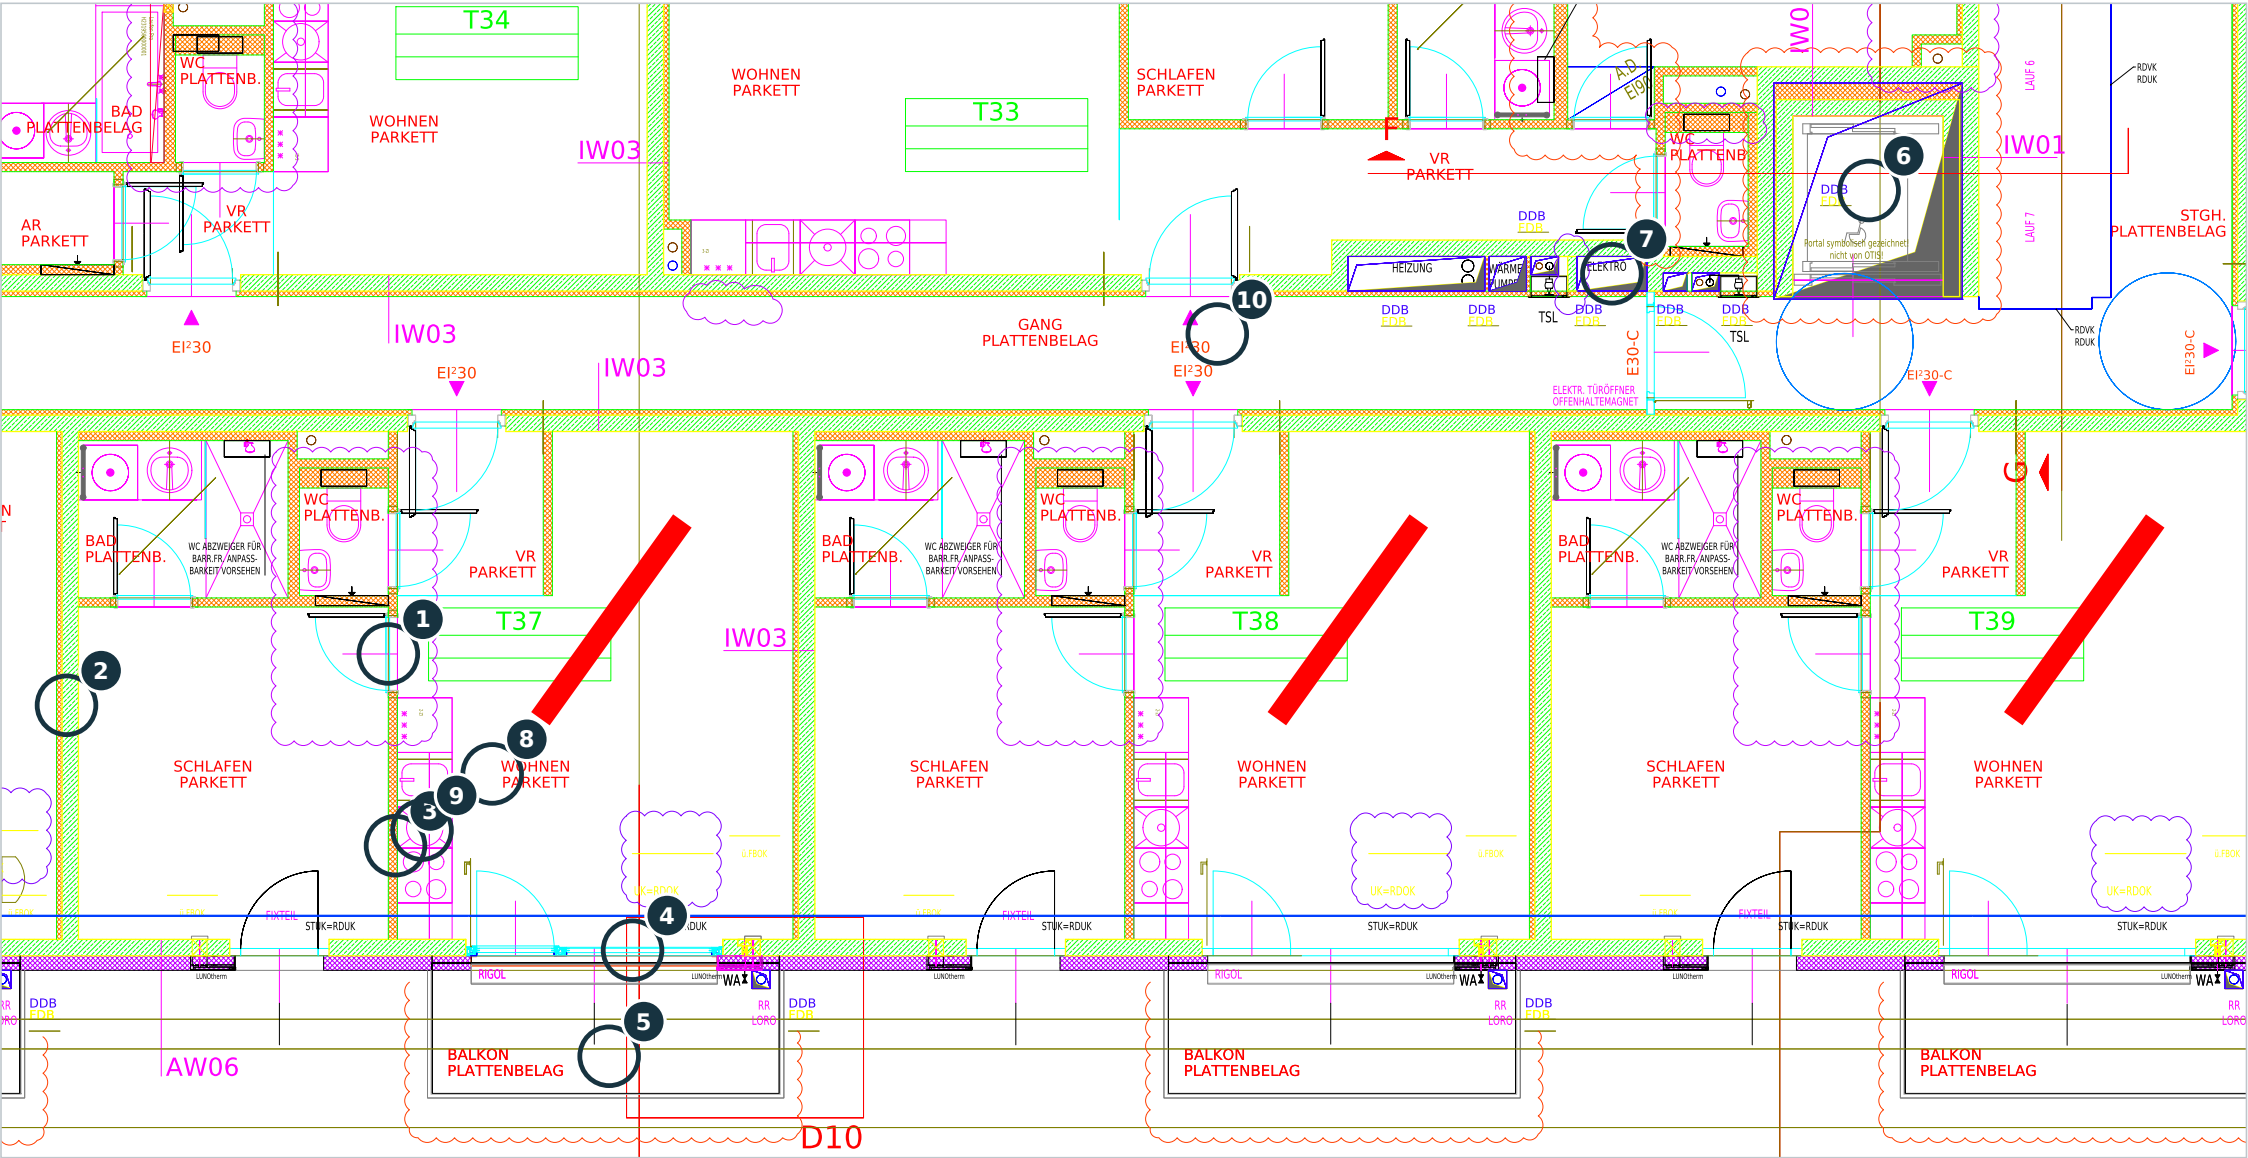

Lösungen: So hättest du es erkennen können

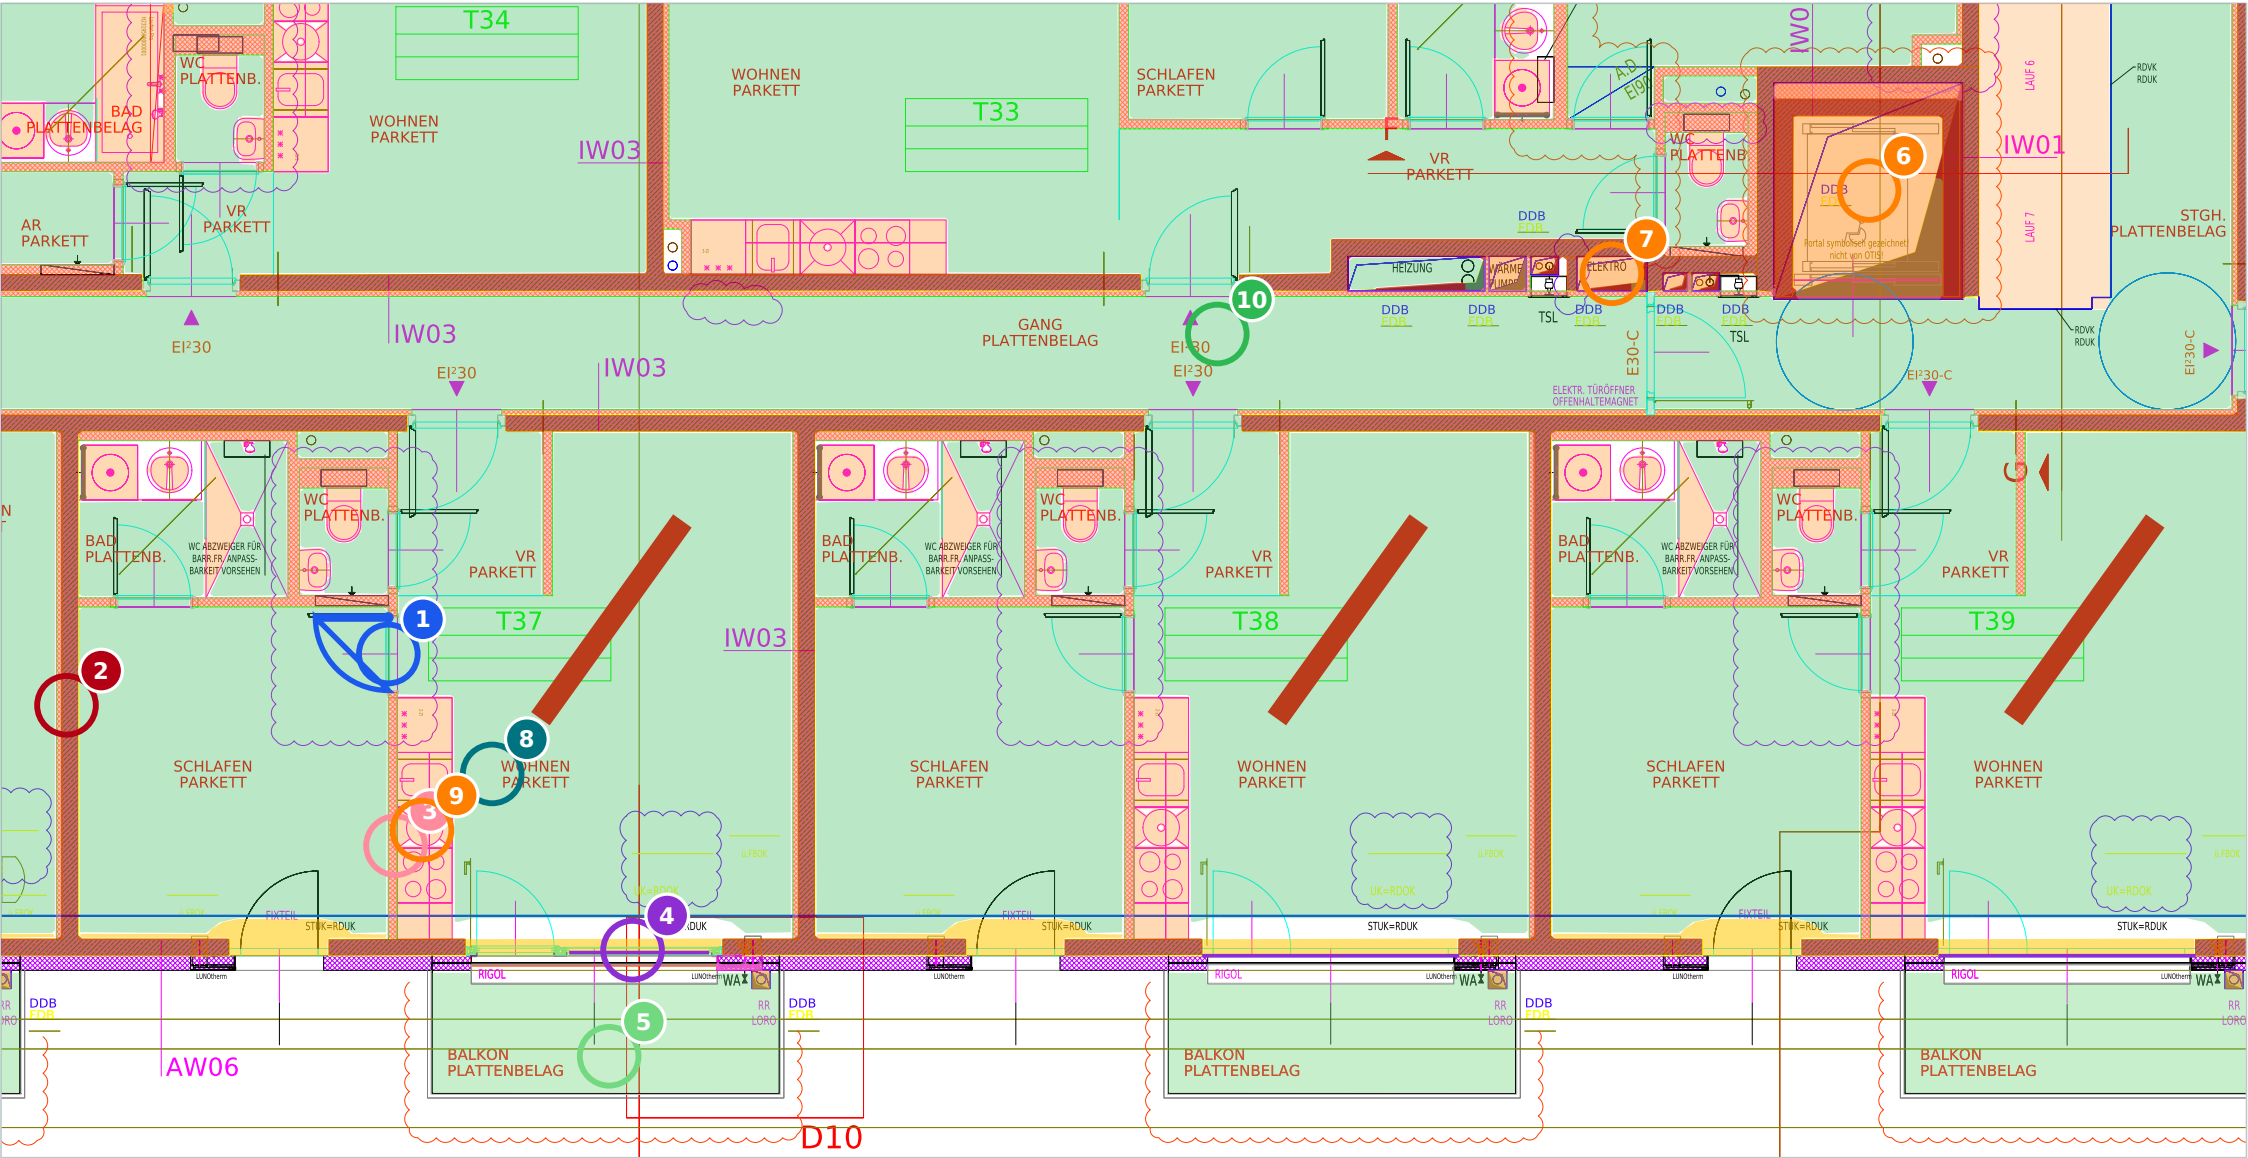

Die Antworten

- 1. Tür** – Lücke in der Wand + Türblatt + Viertelkreis. *Begehbar: ja.*
 - 2. dicke Wand** – gelbe Kanten, grüne Schrägstriche. *Begehbar: nein.*
 - 3. dünne Wand** – grüne Kanten, oranges Gitter. *Begehbar: nein.*
 - 4. Glas (Fixteil)** – dünne parallele Linien ohne Muster, kein Bogen. *Begehbar: nein.*
 - 5. Balkon** – außen, graue Randlinien, Text BALKON. *Begehbar: ja.*
 - 6. Aufzug** – Schacht mit Kabine und Rollstuhlsymbol. *Begehbar: nein.*
 - 7. Leitungsschacht** – kleines Kästchen mit Schräglinie, Texte wie ELEKTRO. *Begehbar: nein.*
 - 8. Raumstempel** – rote Schrift: WOHNEN PARKETT. *Begehbar: Text – darunter ist Boden.*
 - 9. Küchenzeile** – Rechtecke an der Wand, Herd mit 4 Kreisen. *Begehbar: nein.*
 - 10. Gang** – langer grüner Streifen zwischen dicken Wänden. *Begehbar: ja.*
- 8 oder mehr richtig? Dann kannst du diesen Grundriss lesen.

Checkliste: So liest du jeden Grundriss

Schritt 1 – Überblick

Plantitel suchen (hier unten rechts: „3. OBERGESCHOSS“). Welches Stockwerk? Wo sind Straßen und Nachbarhäuser? Gibt es einen Nordpfeil?

Schritt 2 – Außenwand finden

Die äußerste dicke, gemusterte Linie rund um das Haus. Alles darin ist innen.

Schritt 3 – Innenwände verfolgen

Streifen mit zwei Kanten und Muster. Dicke Streifen trennen meist Wohnungen, dünne trennen Zimmer.

Schritt 4 – Türen suchen

Lücke + gerade Linie + Viertelkreis. Der Bogen zeigt, wohin die Tür aufgeht.

Schritt 5 – Fenster und Glas

Lücke in der Außenwand mit mehreren dünnen Linien. Bogen = Glastür, kein Bogen = festes Glas.

Schritt 6 – Räume benennen

Raumstempel lesen: Name oben, Bodenbelag unten.

Schritt 7 – Einbauten erkennen

Dünne Linien im Raum: Küche, WC, Waschbecken, Kästen. Sie stehen im Weg, teilen aber keinen Raum.

Schritt 8 – Kern finden

Treppe (Stufen oder Öffnung mit „Lauf“), Aufzug (Schacht mit Kabine), Leitungsschächte (kleine Kästchen).

Schritt 9 – Weg gehen

Mit dem Finger vom Stiegenhaus über den Gang durch Türen in die Räume. Nie durch Wand, Glas oder Schacht.

Schritt 10 – Grenzen kennen

Was nicht eindeutig im Plan steht, als „unklar“ markieren. Höhen, Material und Tragwerk stehen in anderen Plänen.

Der Anfänger-Test

Kannst du jetzt, ohne Farben, auf dem Originalplan (Seite 5) zeigen, wo die Wohnung T38 ihre Eingangstür, ihr Bad und ihren Balkon hat? Wenn ja: Gratulation – du liest Grundrisse.