

Grundriss lesen lernen - 4. Obergeschoss

Ein Erklärplan für Menschen, die noch nie einen Bauplan gesehen haben

Links siehst du das **4. Obergeschoss** des Wohnhauses an der Ecke **Aichholzgasse / Pöhlgasse** – das Stockwerk direkt über dem 3. Obergeschoss. Der Originalplan liegt unverändert darunter, die Farben liegen durchsichtig darüber.


So ist das Heft aufgebaut:

- A. **Grundlagen:** Was ist ein Grundriss? Welche Sprache sprechen die Linien?
- B. **Schicht für Schicht:** Ein Stück Plan wird vor deinen Augen Farbe für Farbe aufgebaut.
- C. **Überblick:** Wo ist was? Welche Wohnungen gibt es?
- D. **Bauteile:** Wände, Türen, Fenster, Glas – jeweils Gesamtplan und Nahaufnahmen.
- E. **Gehen:** Wo kann man gehen, ein Weg durch eine Wohnung, Räume erkennen.
- F. **Besondere Orte:** Bad, Küche, Stiegenhaus, Aufzug, Schächte, Gang, Balkon, Loggia.
- G. **Schrift und Zeichen,** Lexikon, **typische Anfängerfehler.**
- H. **Vergleich** mit dem 3. Obergeschoss, **Fragen und Antworten,** Quiz, Checkliste.

Jede Nahaufnahme hat unten rechts eine **kleine Lagekarte:** Das rote Kästchen zeigt dir, wo im Haus du gerade bist.

Bei jedem Bauteil beantwortet das Heft drei Fragen: **Was ist das?** · **Wie sieht es auf einem Plan aus?** · **Woran erkenne ich es genau hier?**

Wichtig: Die Farben sind Lernmarkierungen. Sie wurden aus der Geometrie des Original-PDFs abgeleitet und an vielen Stellen geprüft, sind aber keine millimetergenaue Planung. Wo der Plan etwas nicht eindeutig sagt, steht das ausdrücklich dabei.

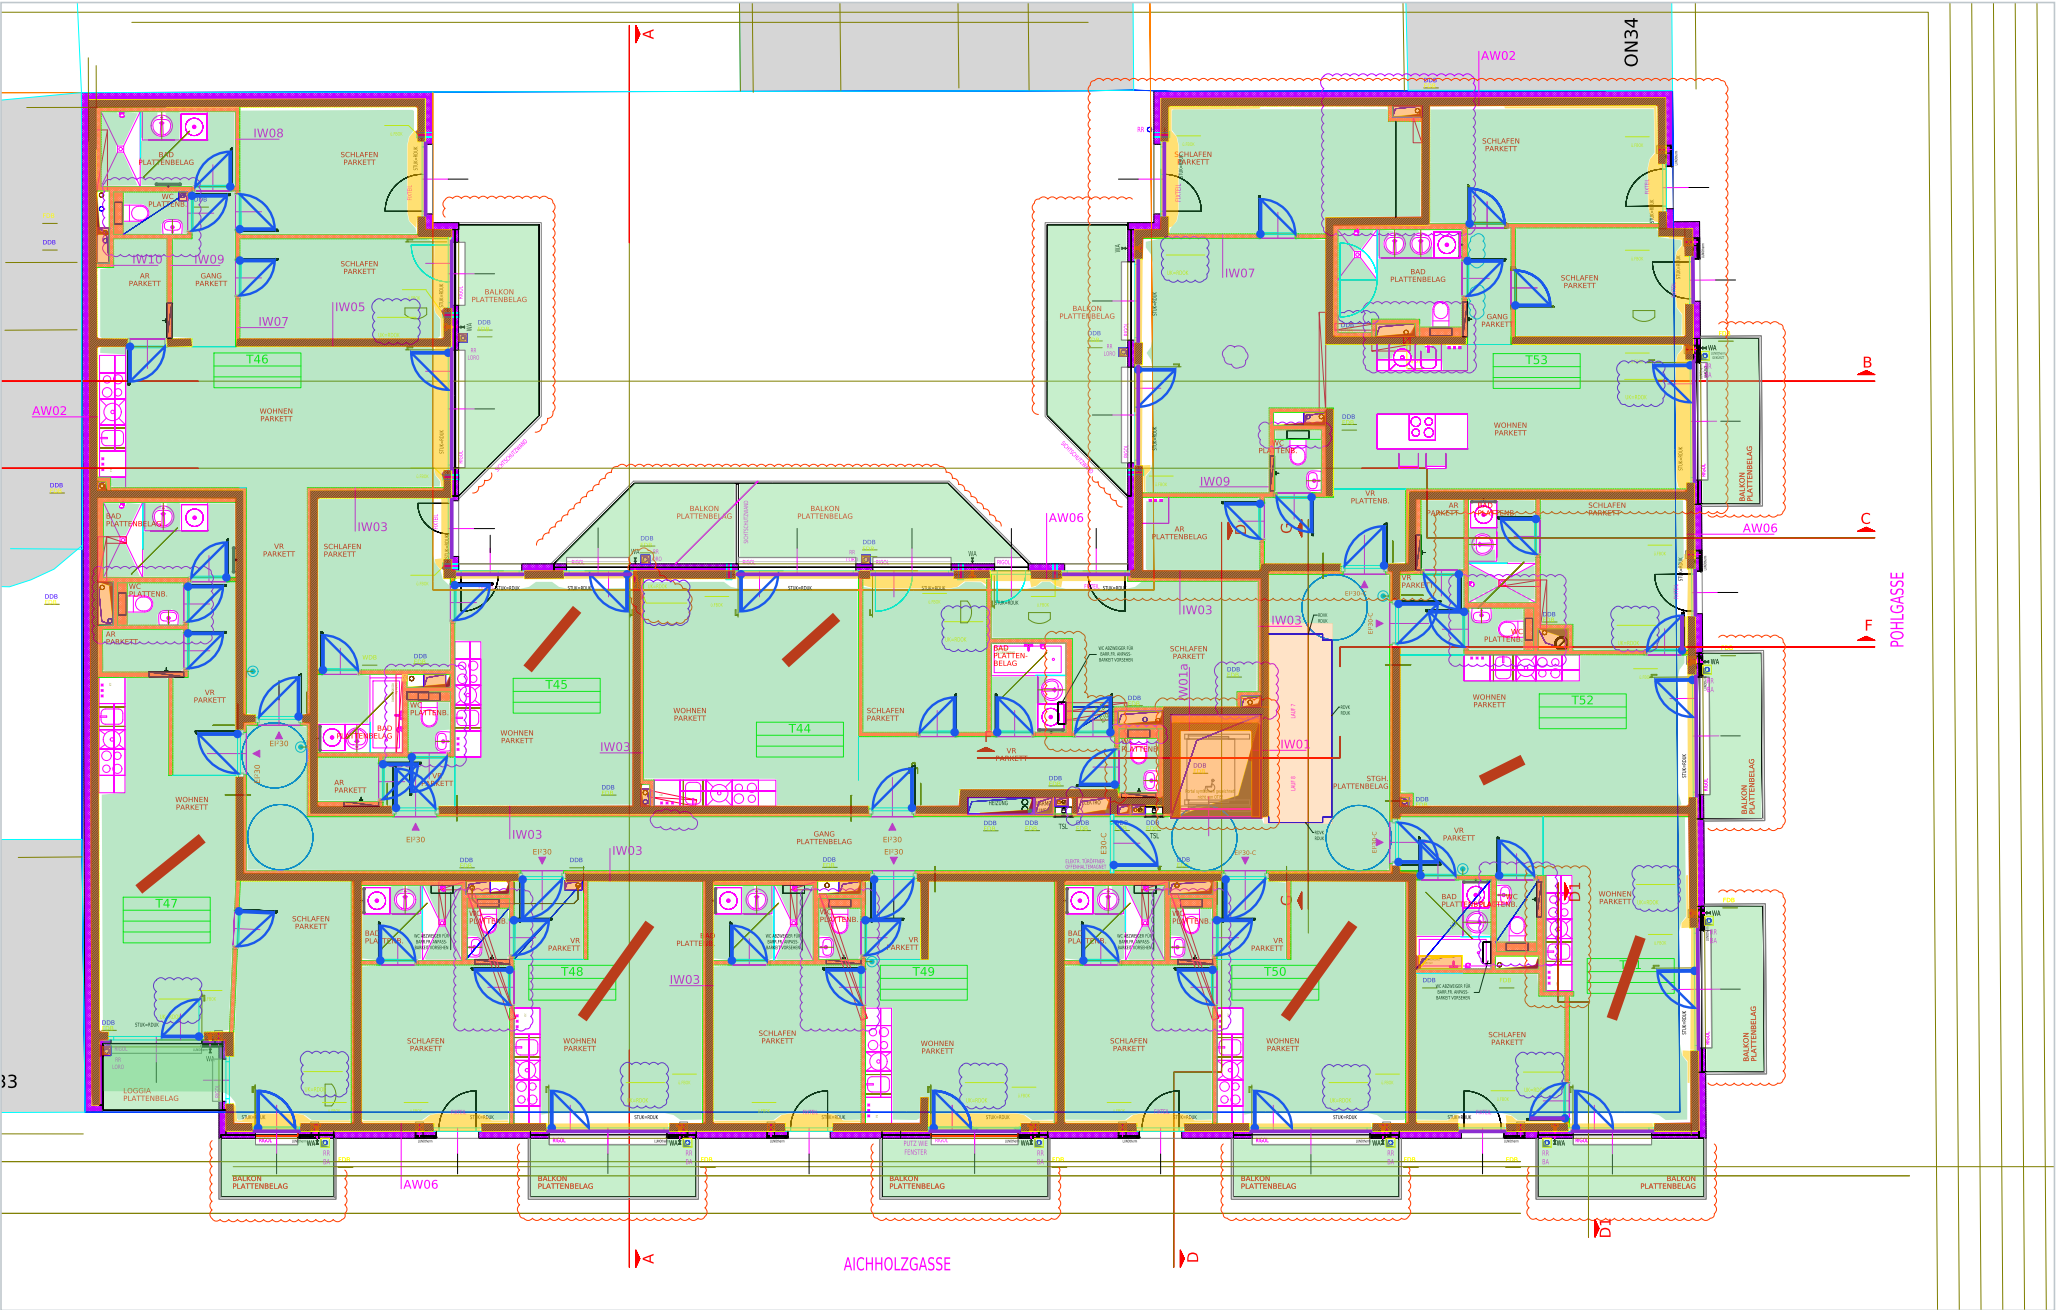

So liest du dieses Heft: Farben und Zeichen

Jede Farbe bedeutet im ganzen Heft **immer dasselbe**. Wenn du irgendwo Rot siehst, ist dort immer eine Wand – auf jeder Seite. Die Farben sind **durchsichtig**: Darunter siehst du immer die Originallinien. So lernst du, die Originallinien später auch ohne Farbe zu erkennen.

Die Farben sind so gewählt, dass sie zu Fragen passen, die du dir beim Lesen stellst: **Rot = Stopp** (hier ist Material), **Grün = Los** (hier kann ich gehen), **Blau = Durchgang** (hier kann ich wechseln).

- DUNKELROT - dicke Wand**
Feste, massive Wand. Kein Durchgang. Im Plan: gelbe Umrandung, innen grüne Schrägstriche.
- HELLROT - dünne Wand**
Schmalere Wand, meist innerhalb einer Wohnung. Im Plan: grüne Umrandung, orange Gitterstriche.
- ROSA - Dämmschicht außen**
Schicht gegen Kälte außen an der Außenwand. Gehört zur Wand. Im Plan: violettes Gittermuster.
- GRÜN - hier kann man gehen**
Fußboden innen, auf dem man stehen und gehen kann.
- HELLGRÜN - begehbar im Freien**
Balkon oder Loggia: Boden draußen, nur über eine Tür erreichbar.
- GELB - Öffnung in der Außenwand**
Stelle, an der die Außenwand für ein Fenster oder eine Glastür unterbrochen ist.
- ORANGE - Hindernisse & Einbauten**
Küche, WC, Waschbecken, Kästen, Schächte, Aufzug, Treppenöffnung.
- BLAU - Tür**
Viertelkreis = Weg des Türblatts. Dicke Linie = Türblatt. Punkt = Drehpunkt (Scharnier).
- HELLGRÜN - begehbar im Freien**
Balkon oder Loggia: Boden draußen, nur über eine Tür erreichbar.
- VIOLETT - Glas**
Linie, an der die Scheibe liegt. Licht geht durch – Menschen nicht.
- TÜRKIS - Schrift und Planzeichen**
Rahmen um Texte, Nummern und Symbole. Keine Bauteile, sondern Informationen.


Die Hilfszeichen

- 1

Nummer: verbindet die Stelle im Plan mit dem Erklärtext rechts.
- Rahmen: umschließt genau das Bauteil, das gerade erklärt wird.
- Pfeil mit Punkt: der Punkt sitzt genau auf dem gemeinten Element.
- Gestrichelt violett: gedachte Lage (z. B. geschlossene Tür). Steht so nicht im Original.
- Türkiser Kreis: hier steht ein Text oder Symbol, das erklärt wird.
- Rotes Kästchen in der Lagekarte: der Ausschnitt, den du gerade ansiehst.

Und was bedeutet „weiß“?


Weiß heißt nur: **hier ist nichts eingefärbt**. Weiß heißt **nicht** automatisch „verboten“ oder „leer“. Unter einem Kasten oder Waschbecken ist auch Boden – dort kann man nur nicht einfach durchgehen.

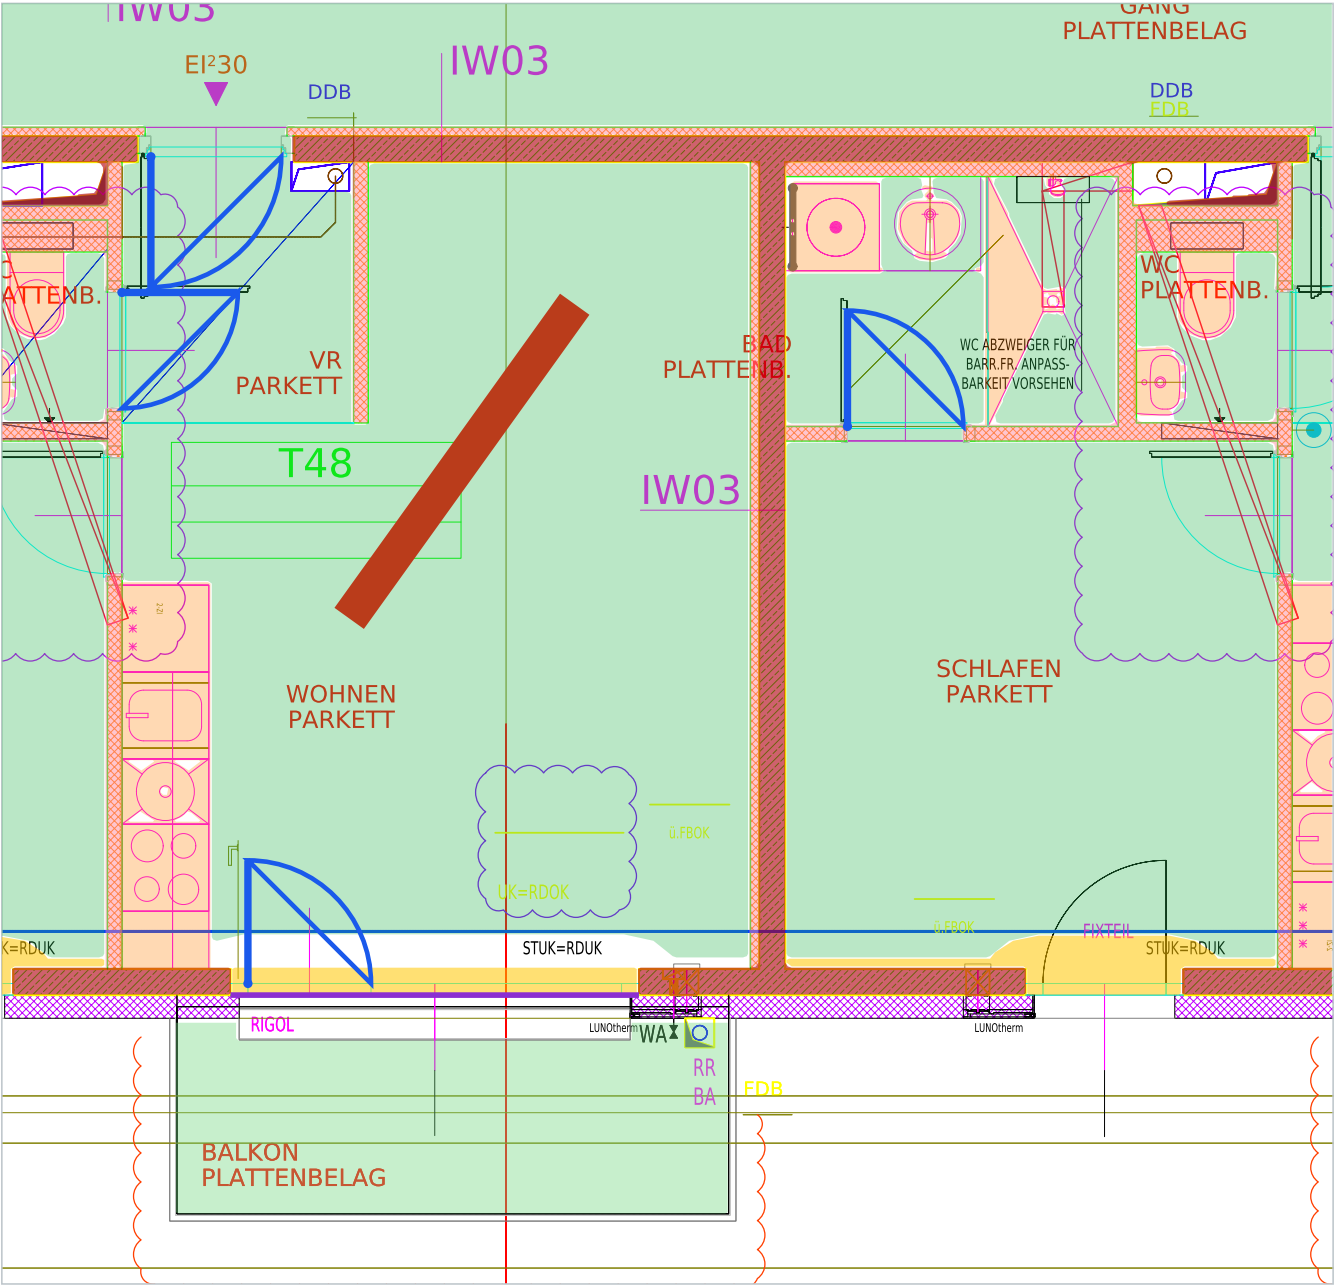

Beispiel: die Wohnung T48 mit allen Farben

Rote Wände umschließen die Räume, **grüner Boden** füllt sie, **blaue Türbögen** zeigen, wo man von Raum zu Raum kommt, **gelb/violett** ist die Glasfront, **orange** sind Küche und Badeinrichtung. Hellgrün unten ist der Balkon. Diese Wohnung begleitet dich durch das ganze Heft.

Was ist ein Grundriss?

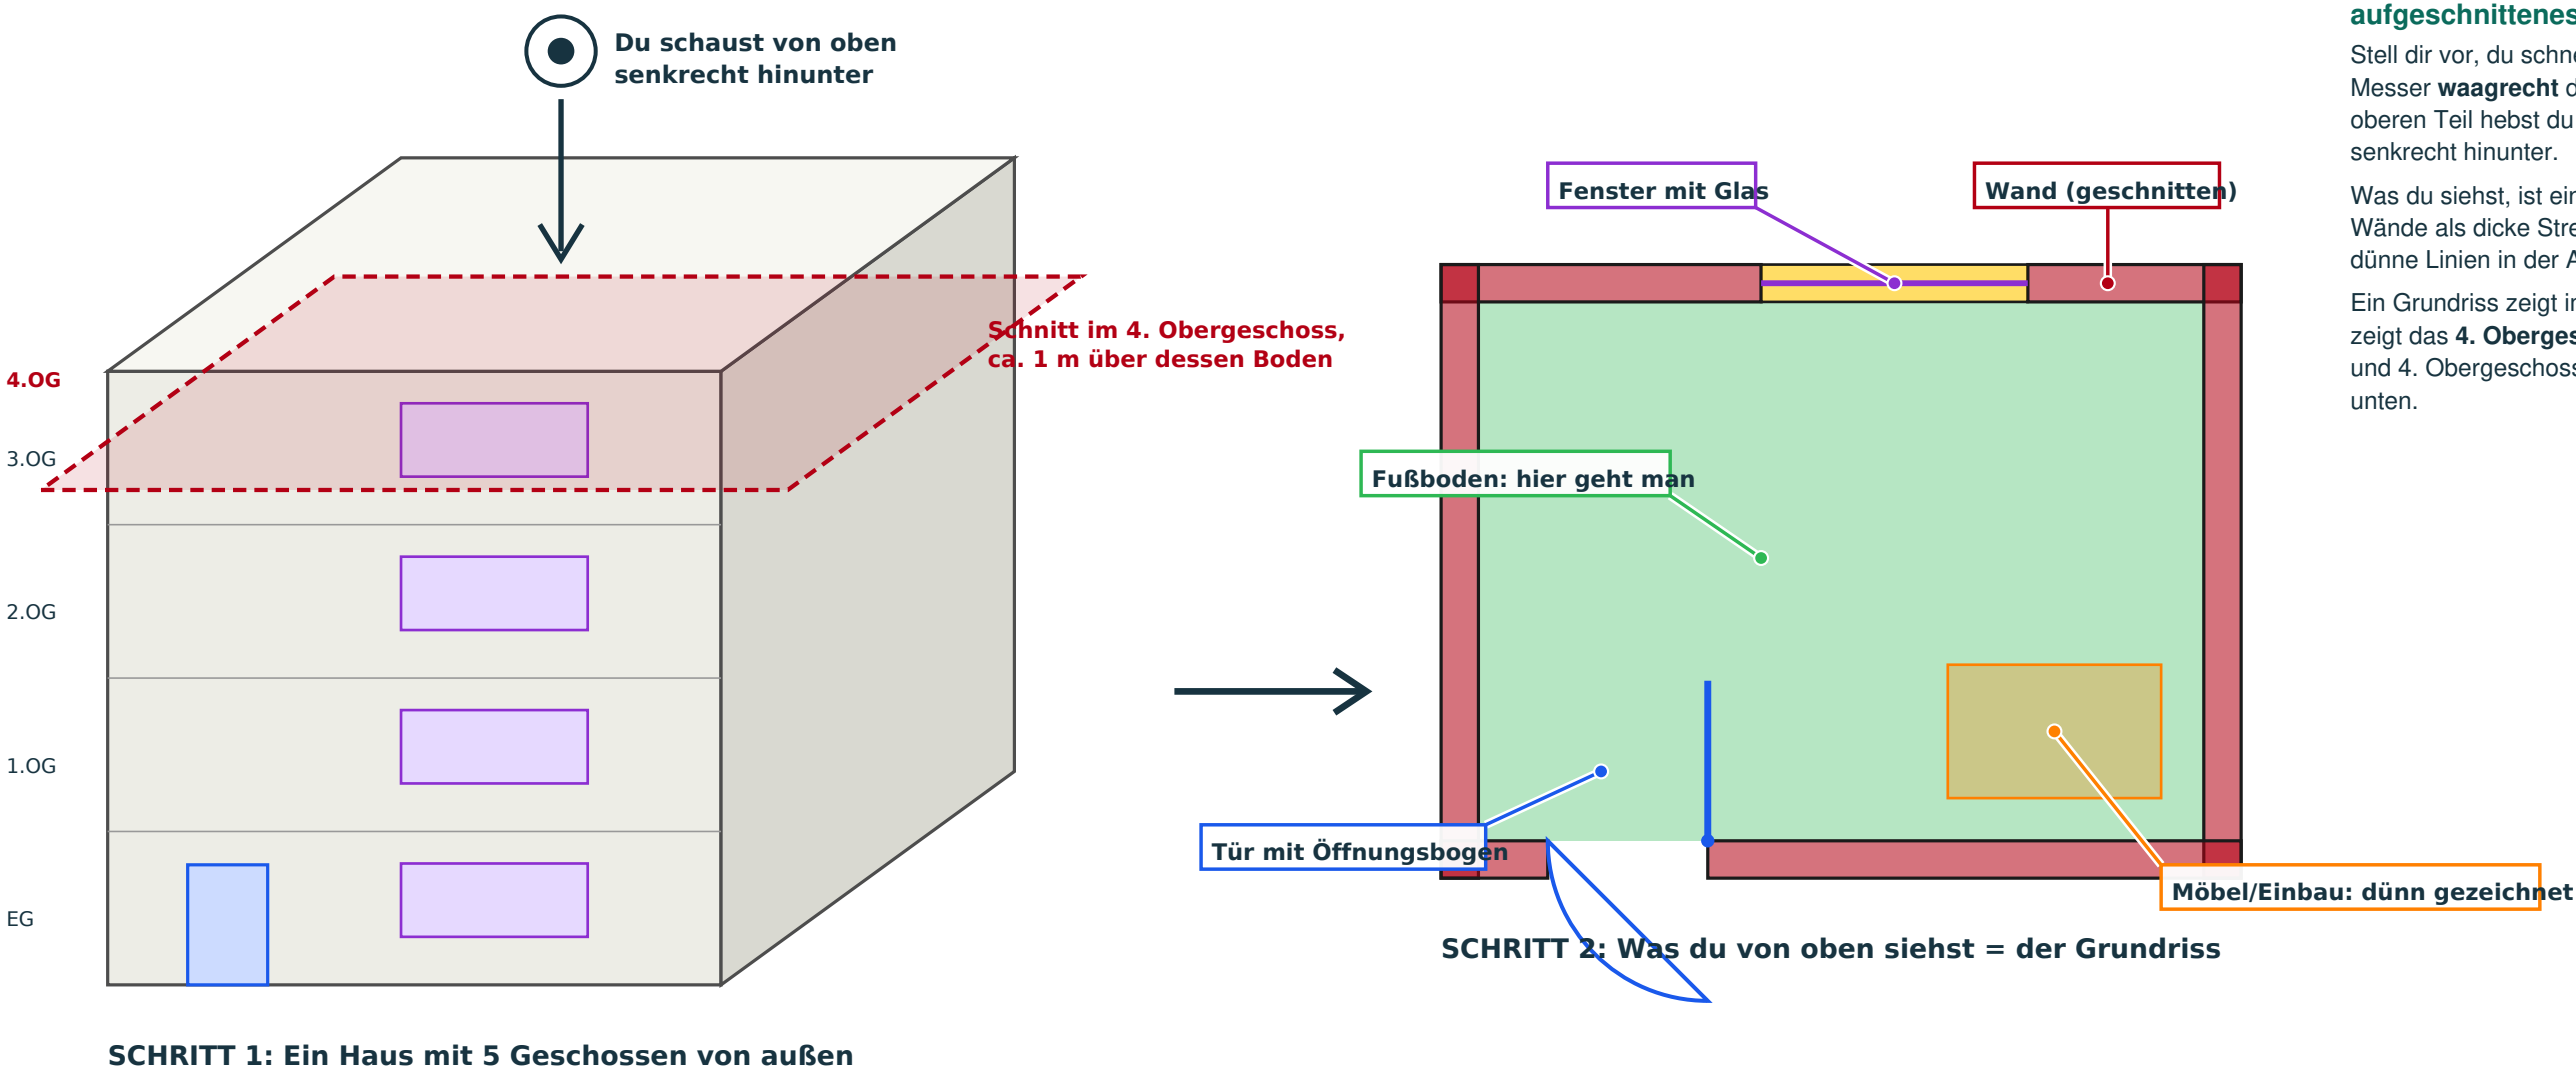

Grundriss = Blick von oben in ein aufgeschnittenes Haus

Stell dir vor, du schneidest ein Haus mit einem riesigen Messer **waagrecht** durch – ungefähr in Hüfthöhe. Den oberen Teil hebst du weg wie einen Deckel und schaust senkrecht hinunter.

Was du siehst, ist ein **Grundriss**: die durchgeschnittenen Wände als dicke Streifen, Türen als Lücken, Fenster als dünne Linien in der Außenwand, dazwischen der Boden.

Ein Grundriss zeigt immer **nur ein Stockwerk**. Dieses Heft zeigt das **4. Obergeschoss**: Erdgeschoss, dann 1., 2., 3. und 4. Obergeschoss. Es ist also das **fünfte** Geschoss von unten.


Drei Dinge, die Anfänger oft verwechseln

- 1. Der Plan ist verkleinert.** Alles ist im gleichen Verhältnis kleiner gezeichnet. Dieser Plan ist „ohne Maße“: Es gibt keine Maßzahlen, darum rechnet das Heft keine Längen aus.
- 2. Dicke Striche = durchgeschnitten, dünne Striche = darunter.** Was der gedachte Schnitt trifft (Wände), wird kräftig gezeichnet. Was nur auf dem Boden steht (Möbel, Waschbecken), wird dünn gezeichnet.
- 3. Linien sind keine Wege – und nicht jede Linie ist eine Wand.** Es gibt auch Linien für Deckenkanten, Schnittlinien, Änderungen und Hinweise. Die Seite „Typische Anfängerfehler“ zeigt dir die häufigsten Verwechslungen.

Die Zeichnung auf dieser Seite ist ein vereinfachtes Lernschema, nicht dieses Gebäude. Ab der nächsten Seite wird nur noch mit dem echten Plan gearbeitet.


Die Sprache der Linien: acht Dinge, die du immer wieder siehst

1. Dicke Wand

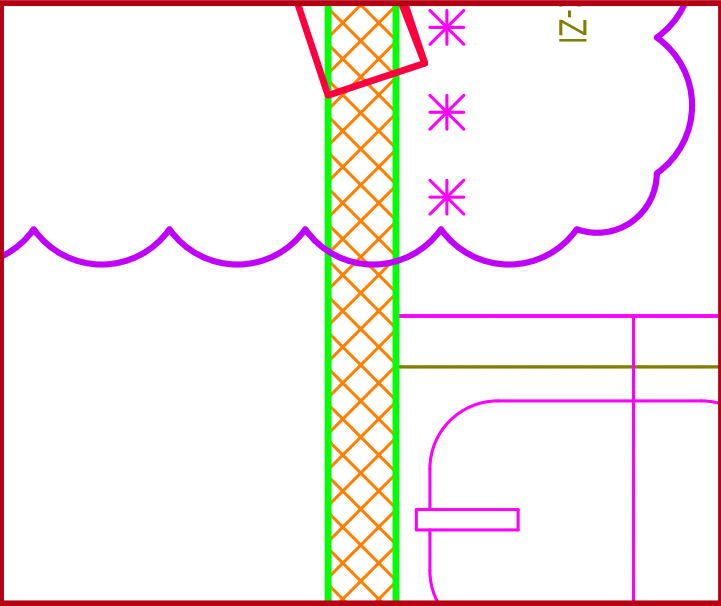


Gelbe Außenlinie, innen grüne Schrägstriche. Zwei Kanten mit Material dazwischen = Wand.

2. Dünne Wand

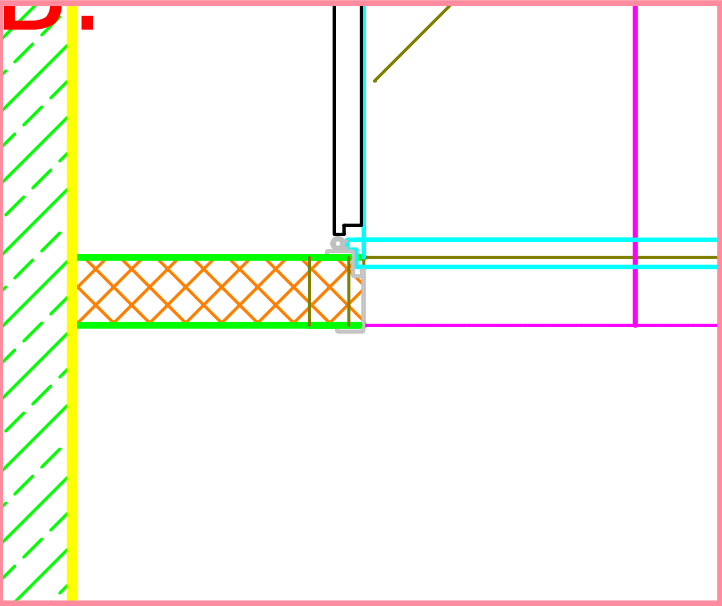


Grüne Außenlinie, innen orange Gitterstriche. Schmäler, aber genauso eine Wand.

3. Tür

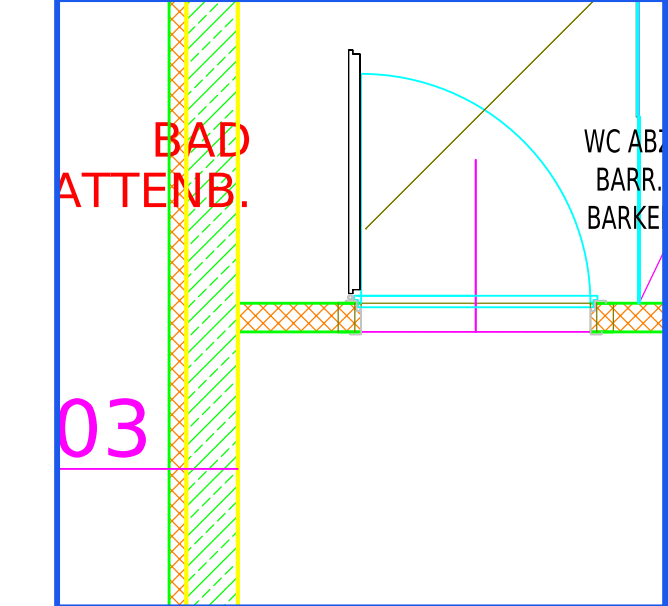

Lücke in der Wand + gerade Linie (Türblatt) + Viertelkreis (Öffnungsweg).

4. Glasfront

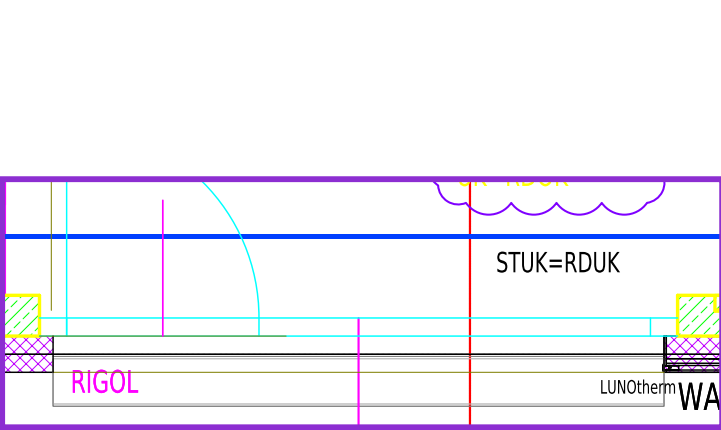


Sehr dünne, eng nebeneinander liegende hellblaue Linien in einer Lücke der Außenwand.

5. Raumstempel




Rote Schrift im Raum: oben der Raumname (WOHNEN), darunter der Bodenbelag (PARKETT).

6. Küchenzeile

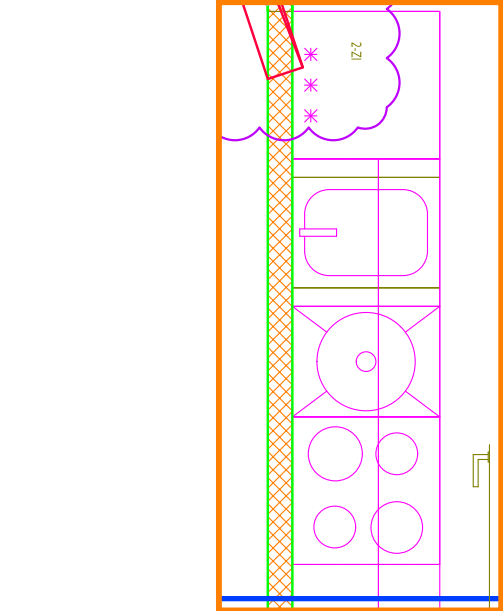


Dünne magenta Linien: Becken mit Hahn = Spüle, vier Kreise = Herd.

7. Bad und WC

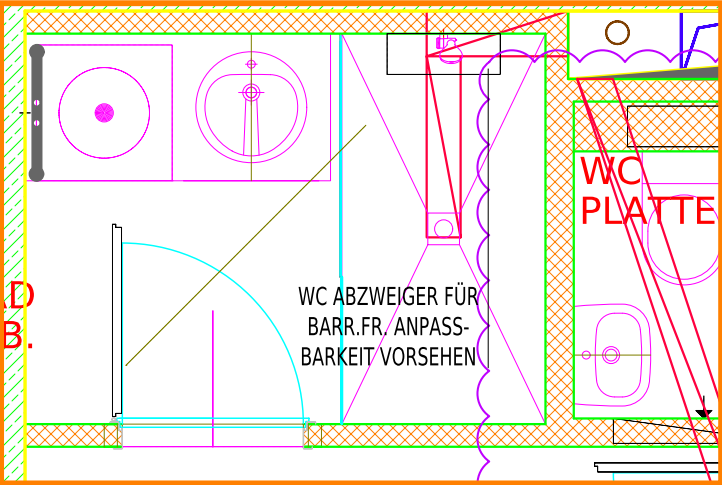

Ovale = WC, runde Formen in Rechtecken = Waschbecken. Dünn gezeichnet, weil sie am Boden stehen.


8. Wandtyp-Kürzel

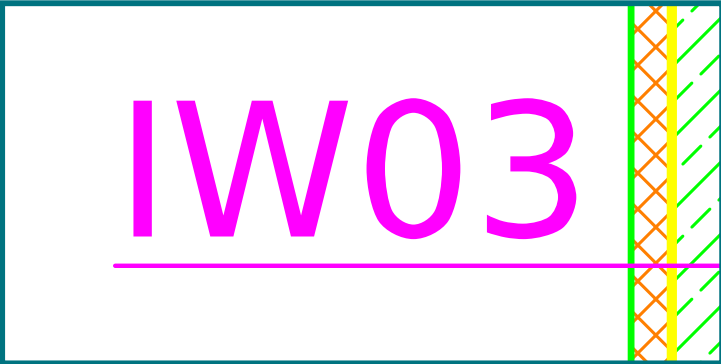

Magenta Schrift wie IW03: Nummer eines Wandtyps. Die Bauart steht in einer anderen Unterlage.


So entsteht das Verständnis: ein Plan in vier Schritten

1. Nur das Original

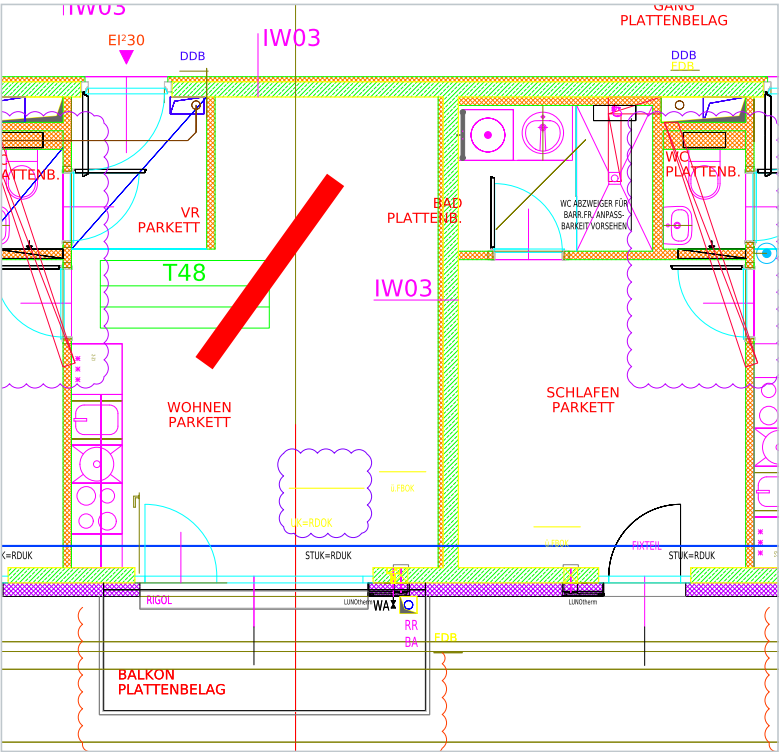


So bekommst du den Plan. Viele Linien, viele Farben – noch ohne Bedeutung.

2. Erst die Wände

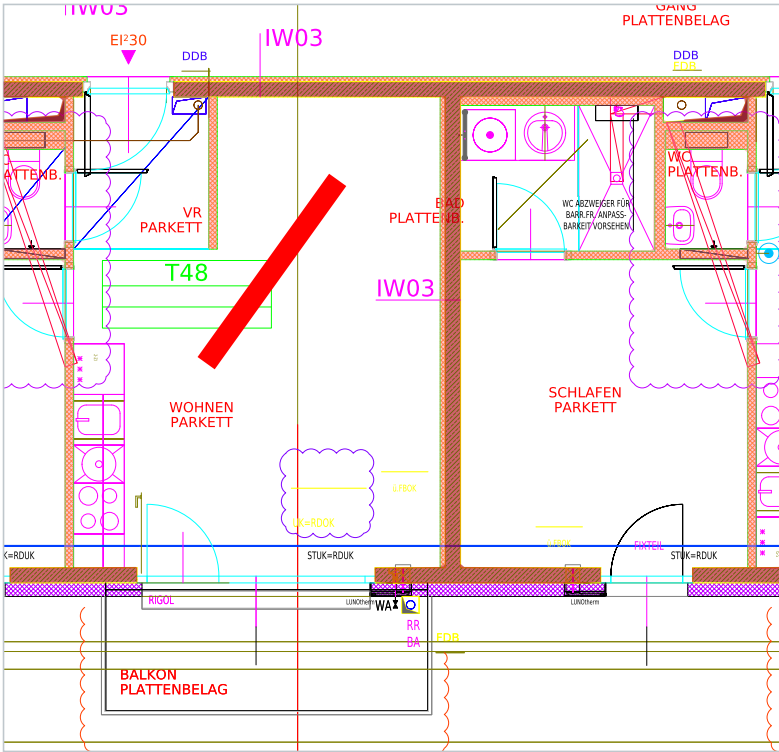


Zuerst suchst du die Streifen mit Muster. Jetzt siehst du Räume als „Kästchen“.

3. Dann Türen und Glas

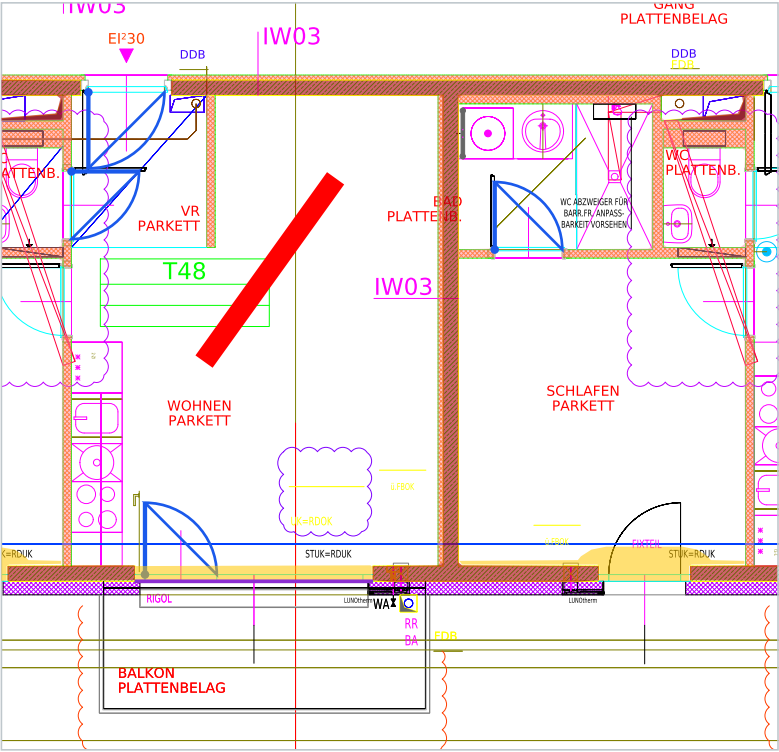

Wo die Wand Lücken hat: Bogen = Tür, dünne Linien ohne Bogen = Glas.


4. Zum Schluss der Boden

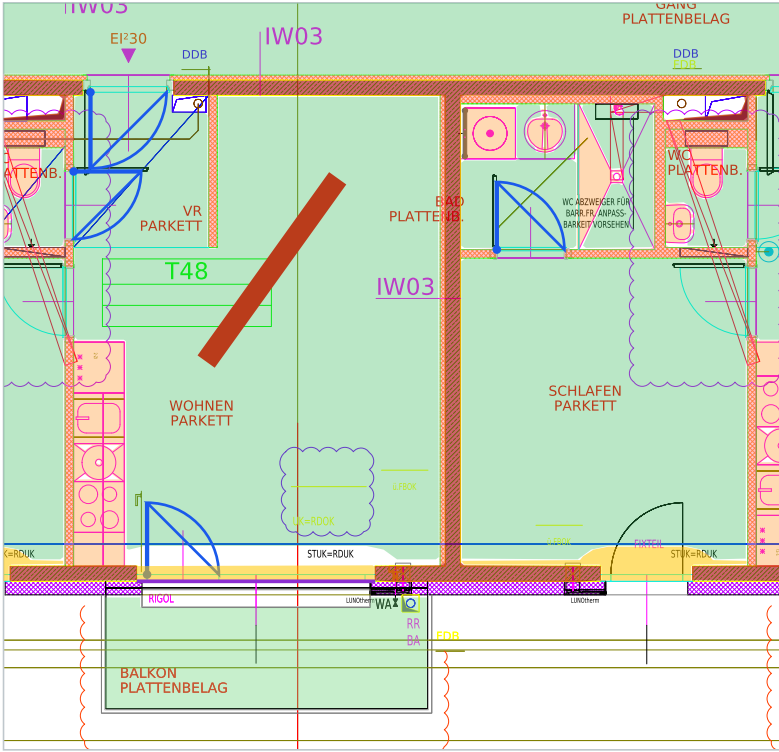

Grün bleibt übrig: der Platz zum Gehen. Orange: was im Weg steht.

DER AUSGANGSPLAN


Der Originalplan - unverändert

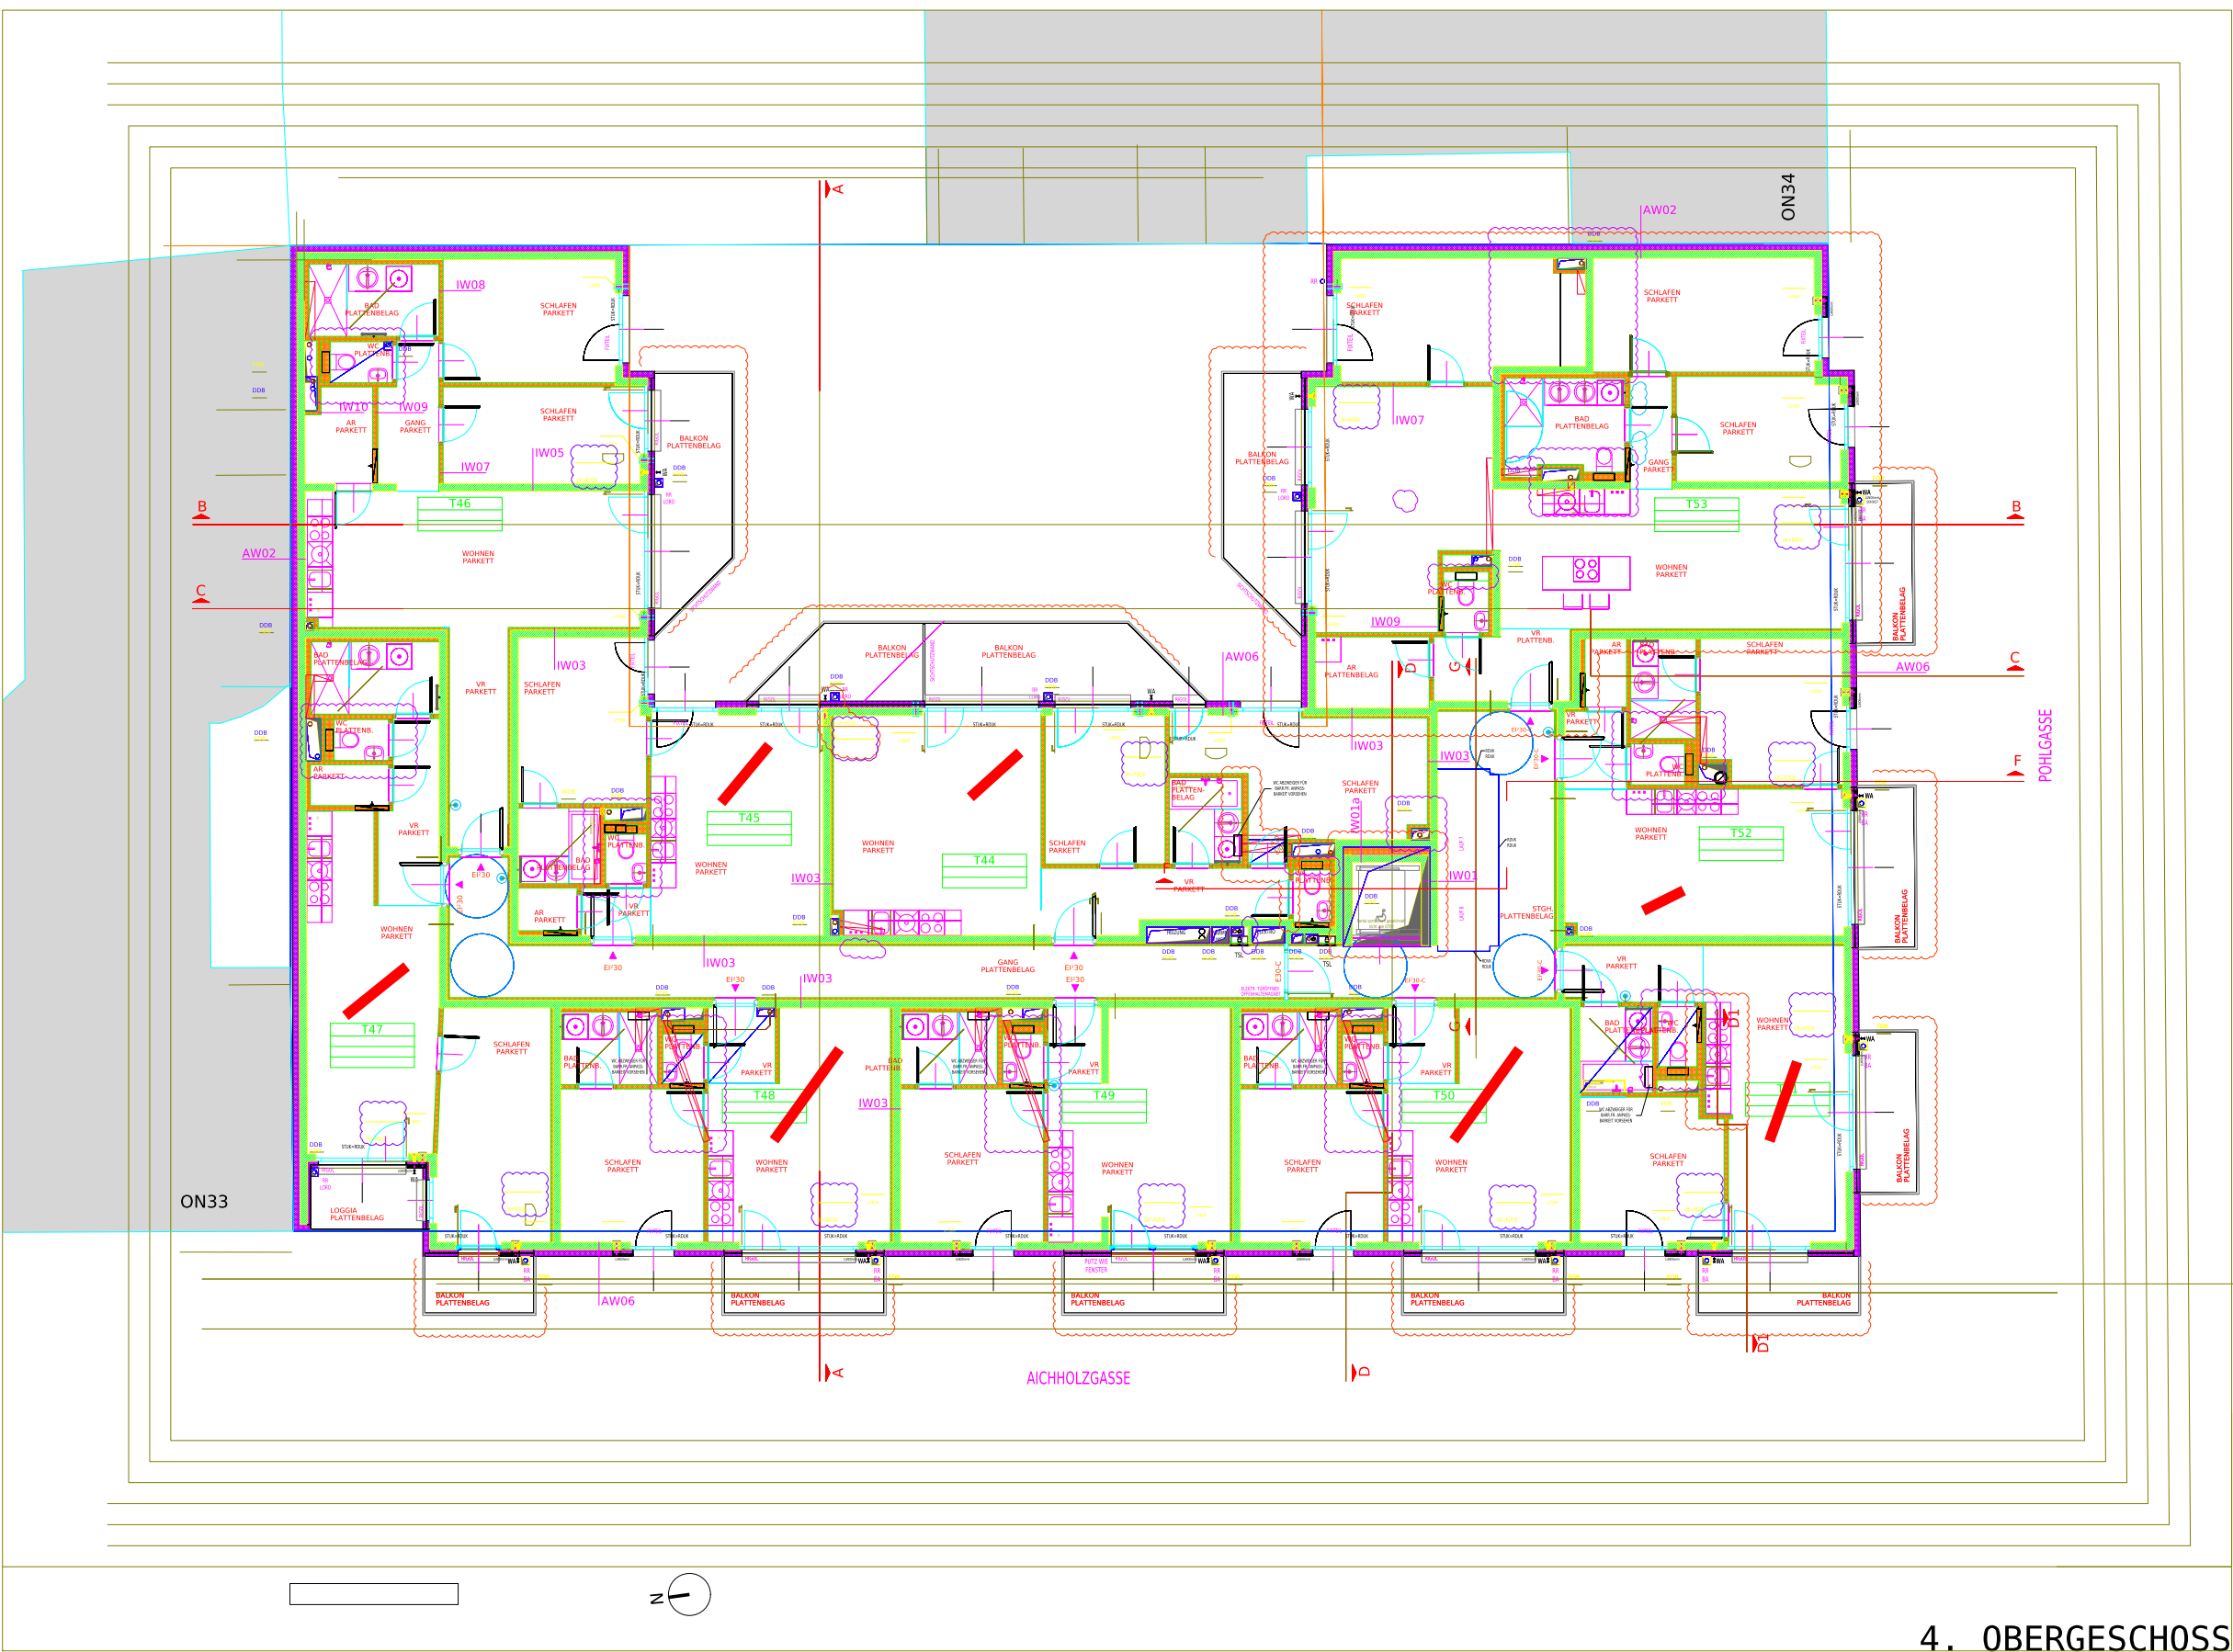

4. OBERGESCHOSS

Keine Markierungen auf dieser Seite. So sieht der Plan aus, wenn du ihn ohne Hilfe bekommst.

Wo ist was? Die große Übersicht

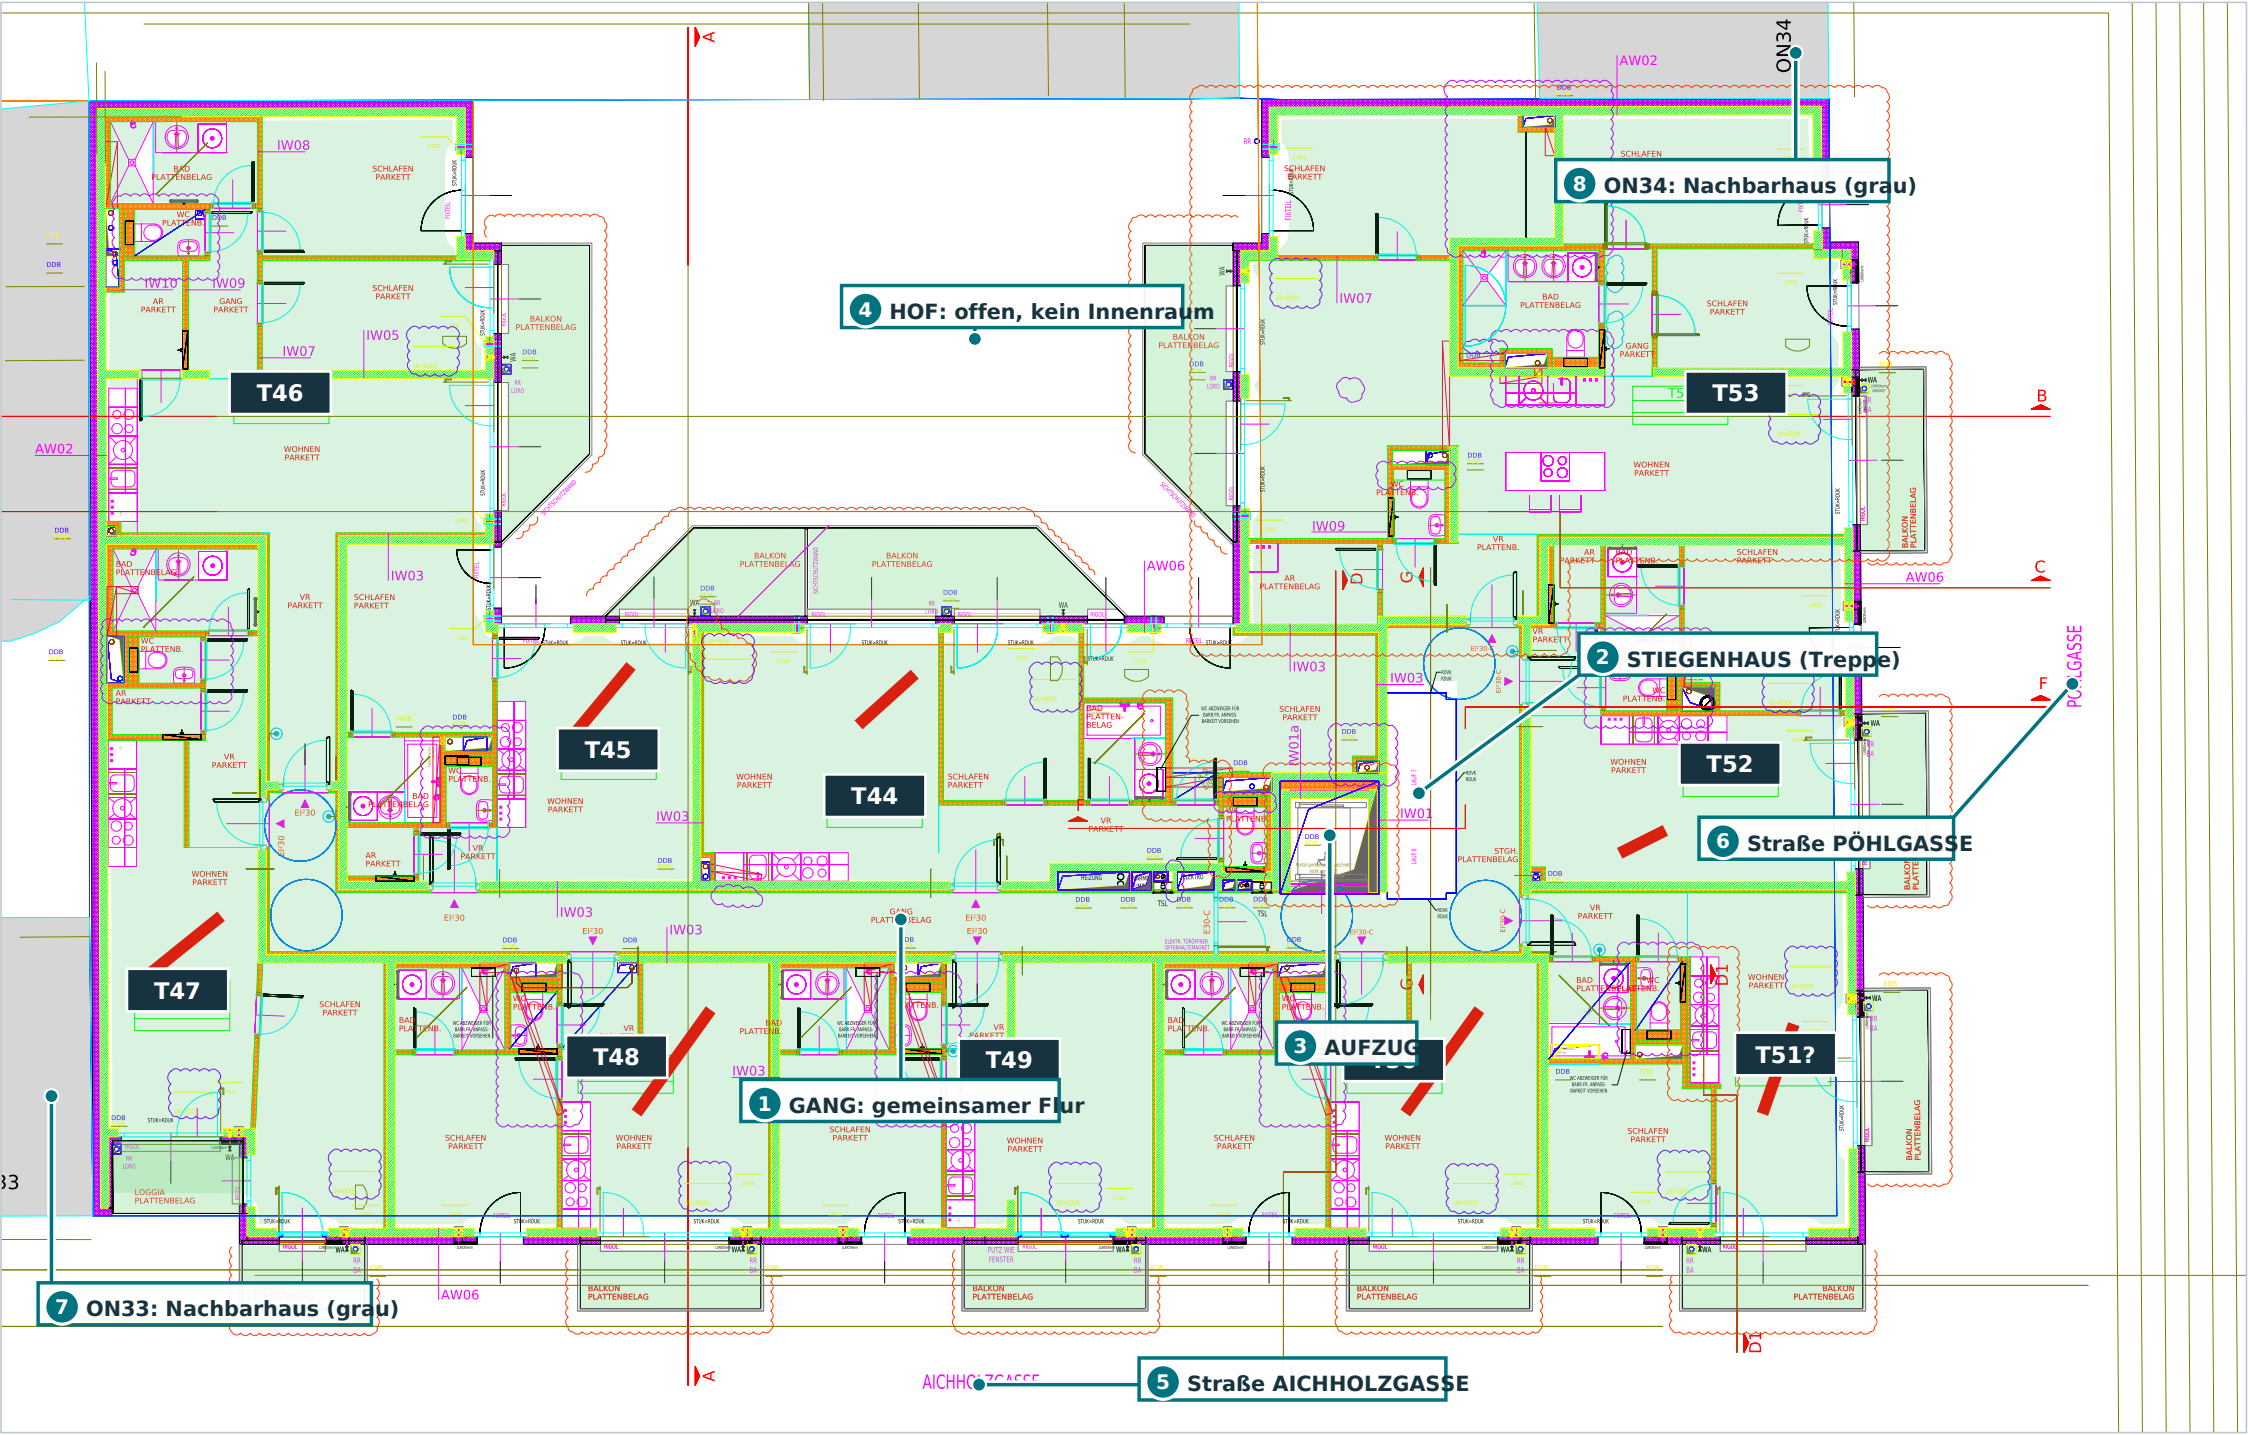

Das Gebäude von oben

Das Haus hat die Form eines **U**: zwei Flügel oben, dazwischen ein offener **Hof** (7-ähnlich weiß: dort ist kein Innenraum).

In diesem Geschoss stehen **10 Wohnungsnummern**, von **T44 bis T53**. „T“ heißt in Österreich **Top** = Wohnungsnummer. Im Plan steht jede Nummer in grüner Schrift in einem kleinen Kasten.

Rechts unten ist die Nummer im Original von einem roten Balken teilweise verdeckt. Lesbar ist „T5...“; aus der Reihenfolge ist **T51** sehr naheliegend – darum „T51?“.

Alle Wohnungen erreicht man über den **Gang** (1). Der Gang hängt am **Stiegenhaus** (2) und am **Aufzug** (3). So kommt man von der Straße bis in dieses Stockwerk.


Die **Straßennamen** (5, 6) stehen außen am Plan. So weißt du, zu welcher Straße eine Wohnung schaut.

Die **grauen Flächen** (7, 8) sind Nachbarhäuser – nicht Teil dieses Gebäudes.

Frag dich selbst

Welche Wohnung liegt an der Ecke der beiden Straßen? (Antwort: rechts unten, T51?)

Alle Wände im Überblick - rot

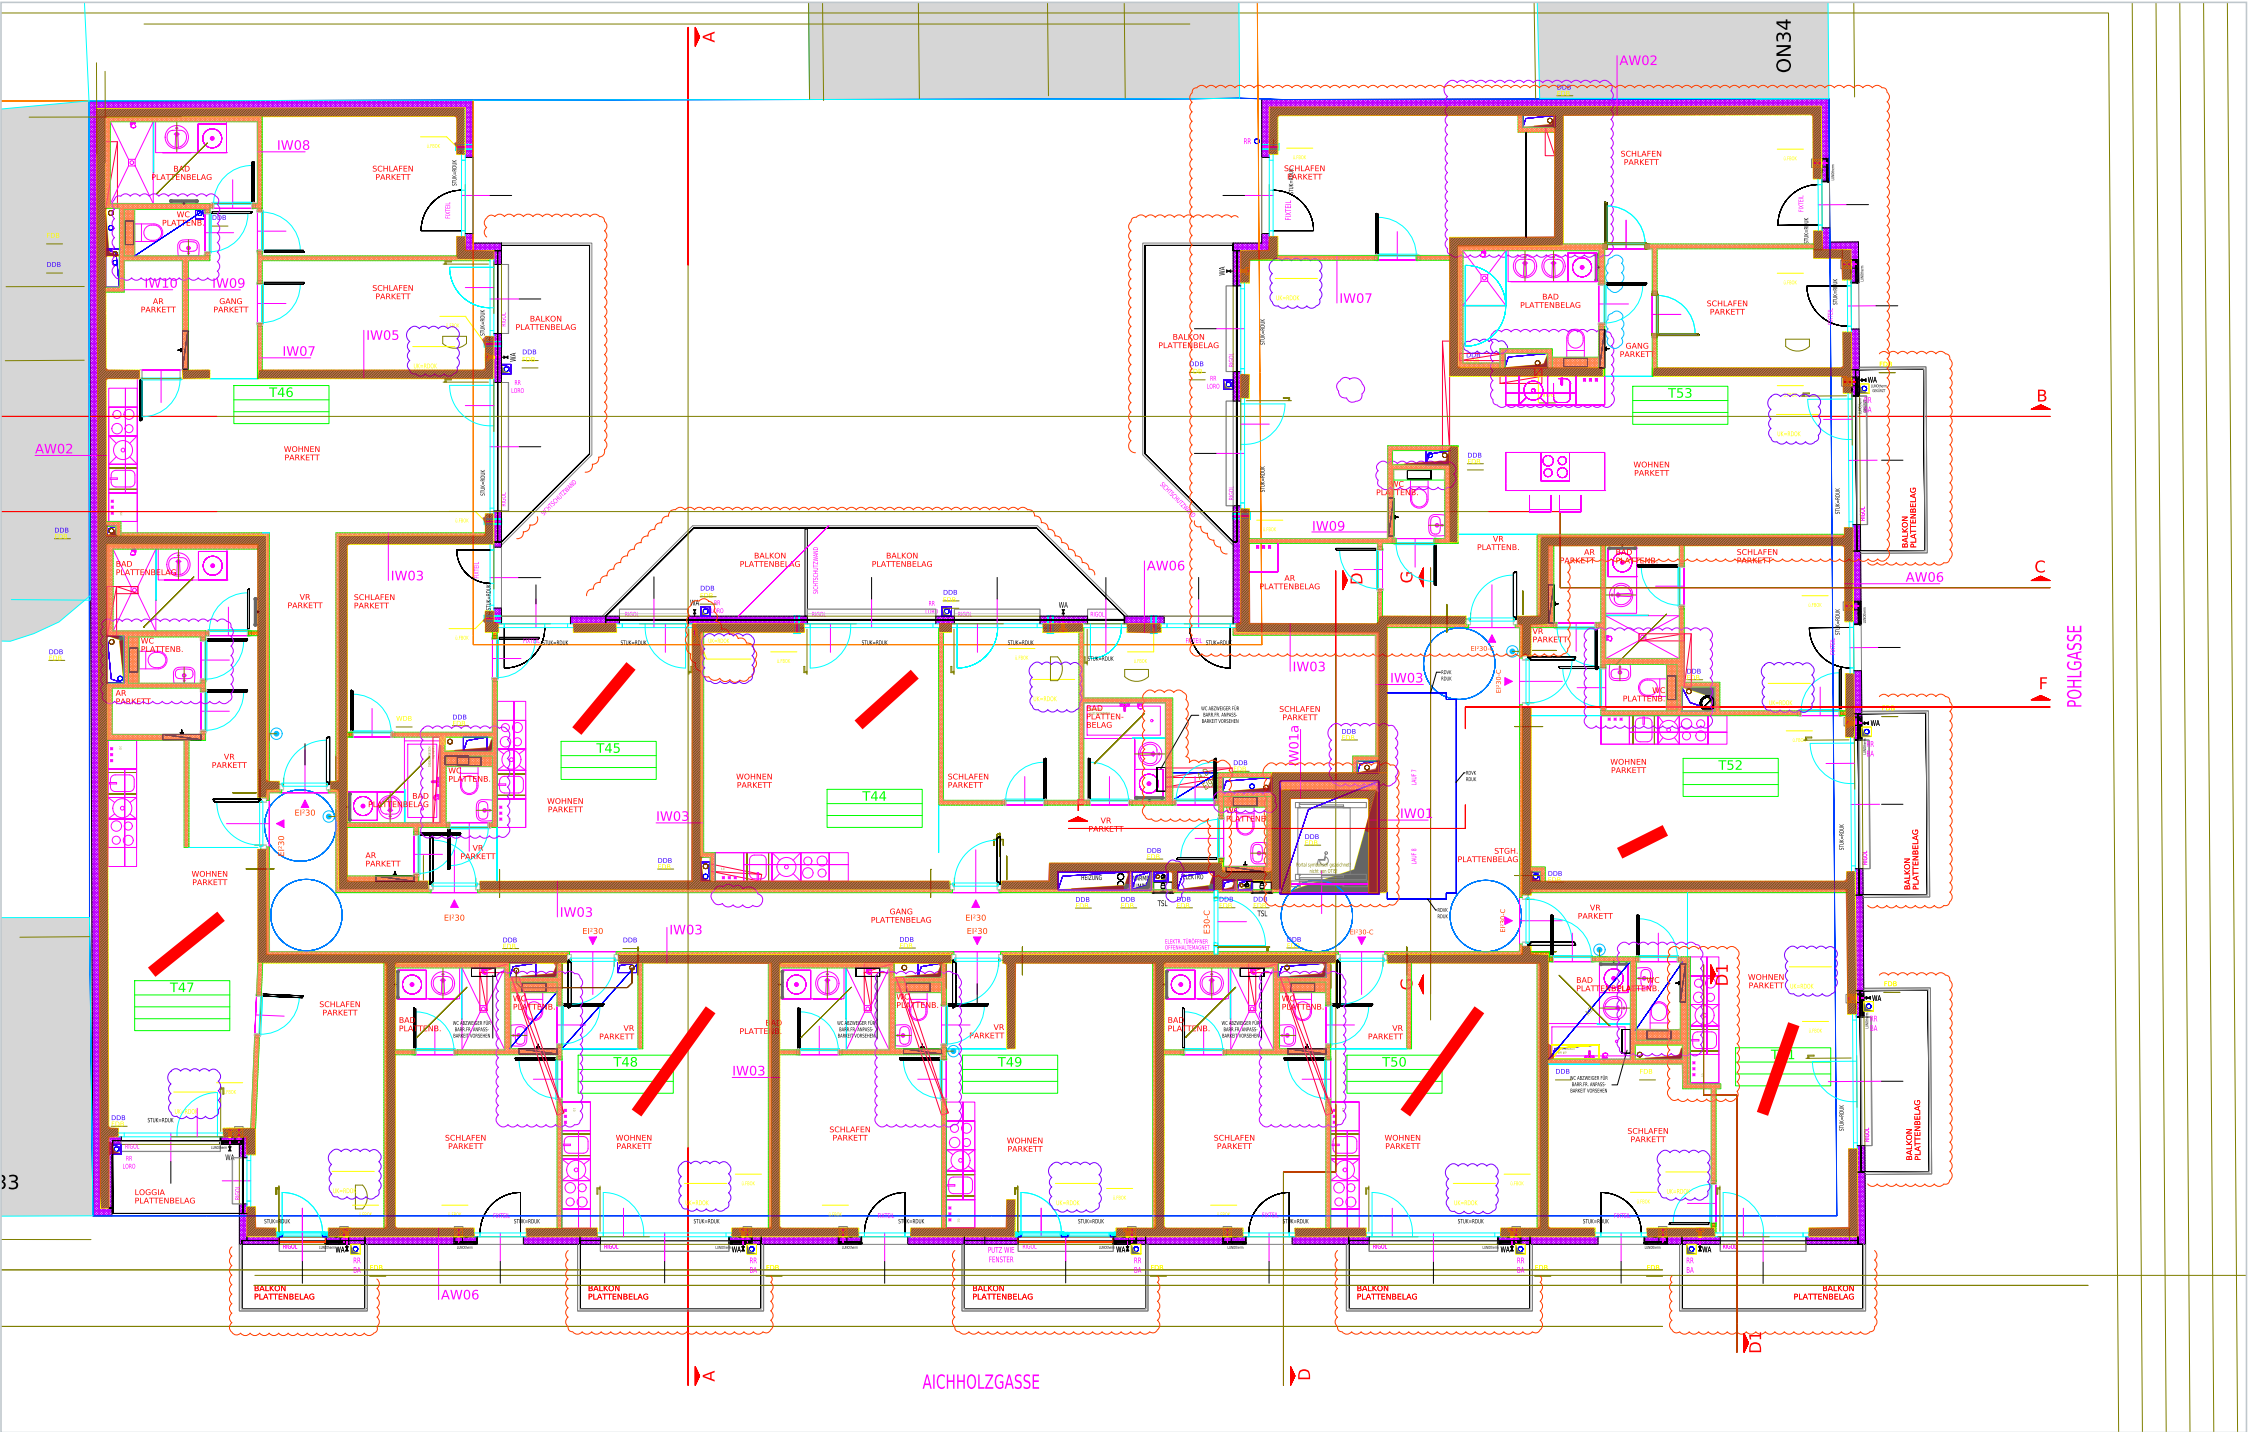

Was ist eine Wand?

Ein fester, senkrechter Bauteil – z. B. aus Beton oder Ziegel. Sie trennt zwei Bereiche. Man kann **nicht** durch sie hindurchgehen.

Wie sieht sie im Grundriss aus?

Als **Streifen**: zwei parallele Linien (die beiden Wandseiten), dazwischen ein Muster (die Schraffur). Das Muster sagt: „Hier ist Material.“

Woran erkenne ich die Wände hier?

Dunkelrot = gelbe Umrandung + grüne Schrägstriche: dicke Wände. Außenwände, Wände zwischen Wohnungen, Wände am Gang und am Stiegenhaus.

Hellrot = grüne Umrandung + orange Gitterstriche: dünne Wände in den Wohnungen, z. B. um Bad und WC.

Rosa = violettes Gittermuster außen an der Fassade: die Dämmschicht.

Wo Rot aufhört

Jede **Unterbrechung** im Rot ist eine Öffnung: innen eine Tür, außen ein Fenster oder eine Glastür.

Übung

Fahre mit dem Finger die äußerste rote Linie einmal ganz um das Haus. So findest du die Außenform – ein „U“.

Ob eine Wand **tragend** ist, steht nicht im Plan. Dicke Wände sind oft tragend, das ist hier aber nicht belegt.


Die Wand zwischen **drinnen** und **draußen**. Sie hält Regen, Wind und Kälte ab.

Von innen nach außen liegen zwei Schichten nebeneinander:

(2) Dämmschicht – violettes Gittermuster: eine Schicht gegen Kälte. Sie ist fest mit der Wand verbunden, also auch nicht begehbar.


Bei (3) ist die Innenseite, darüber beginnt das Wohnzimmer. Bei (4) ist die Außenseite. Bei (5) hört das Muster plötzlich auf: Dort sitzt die Glasfront mit der Balkontür.

Aus welchem Material der Kern ist (Beton, Ziegel ...), sagt der Plan ohne Legende nicht sicher.

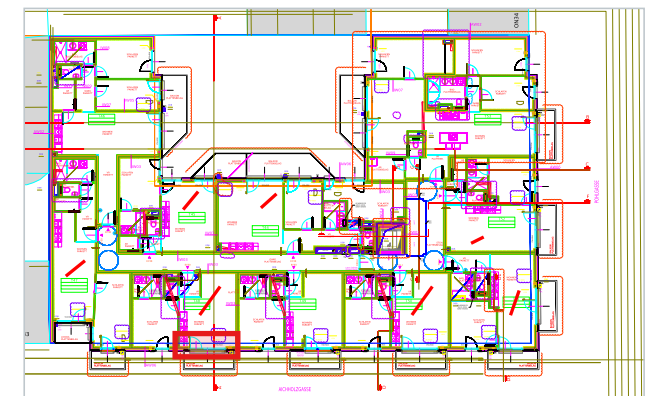

Ausschnitt: Außenwand der Wohnung T48 zur Aichholzgasse.

Dicke Wand oder dünne Wand? So unterscheidest du sie

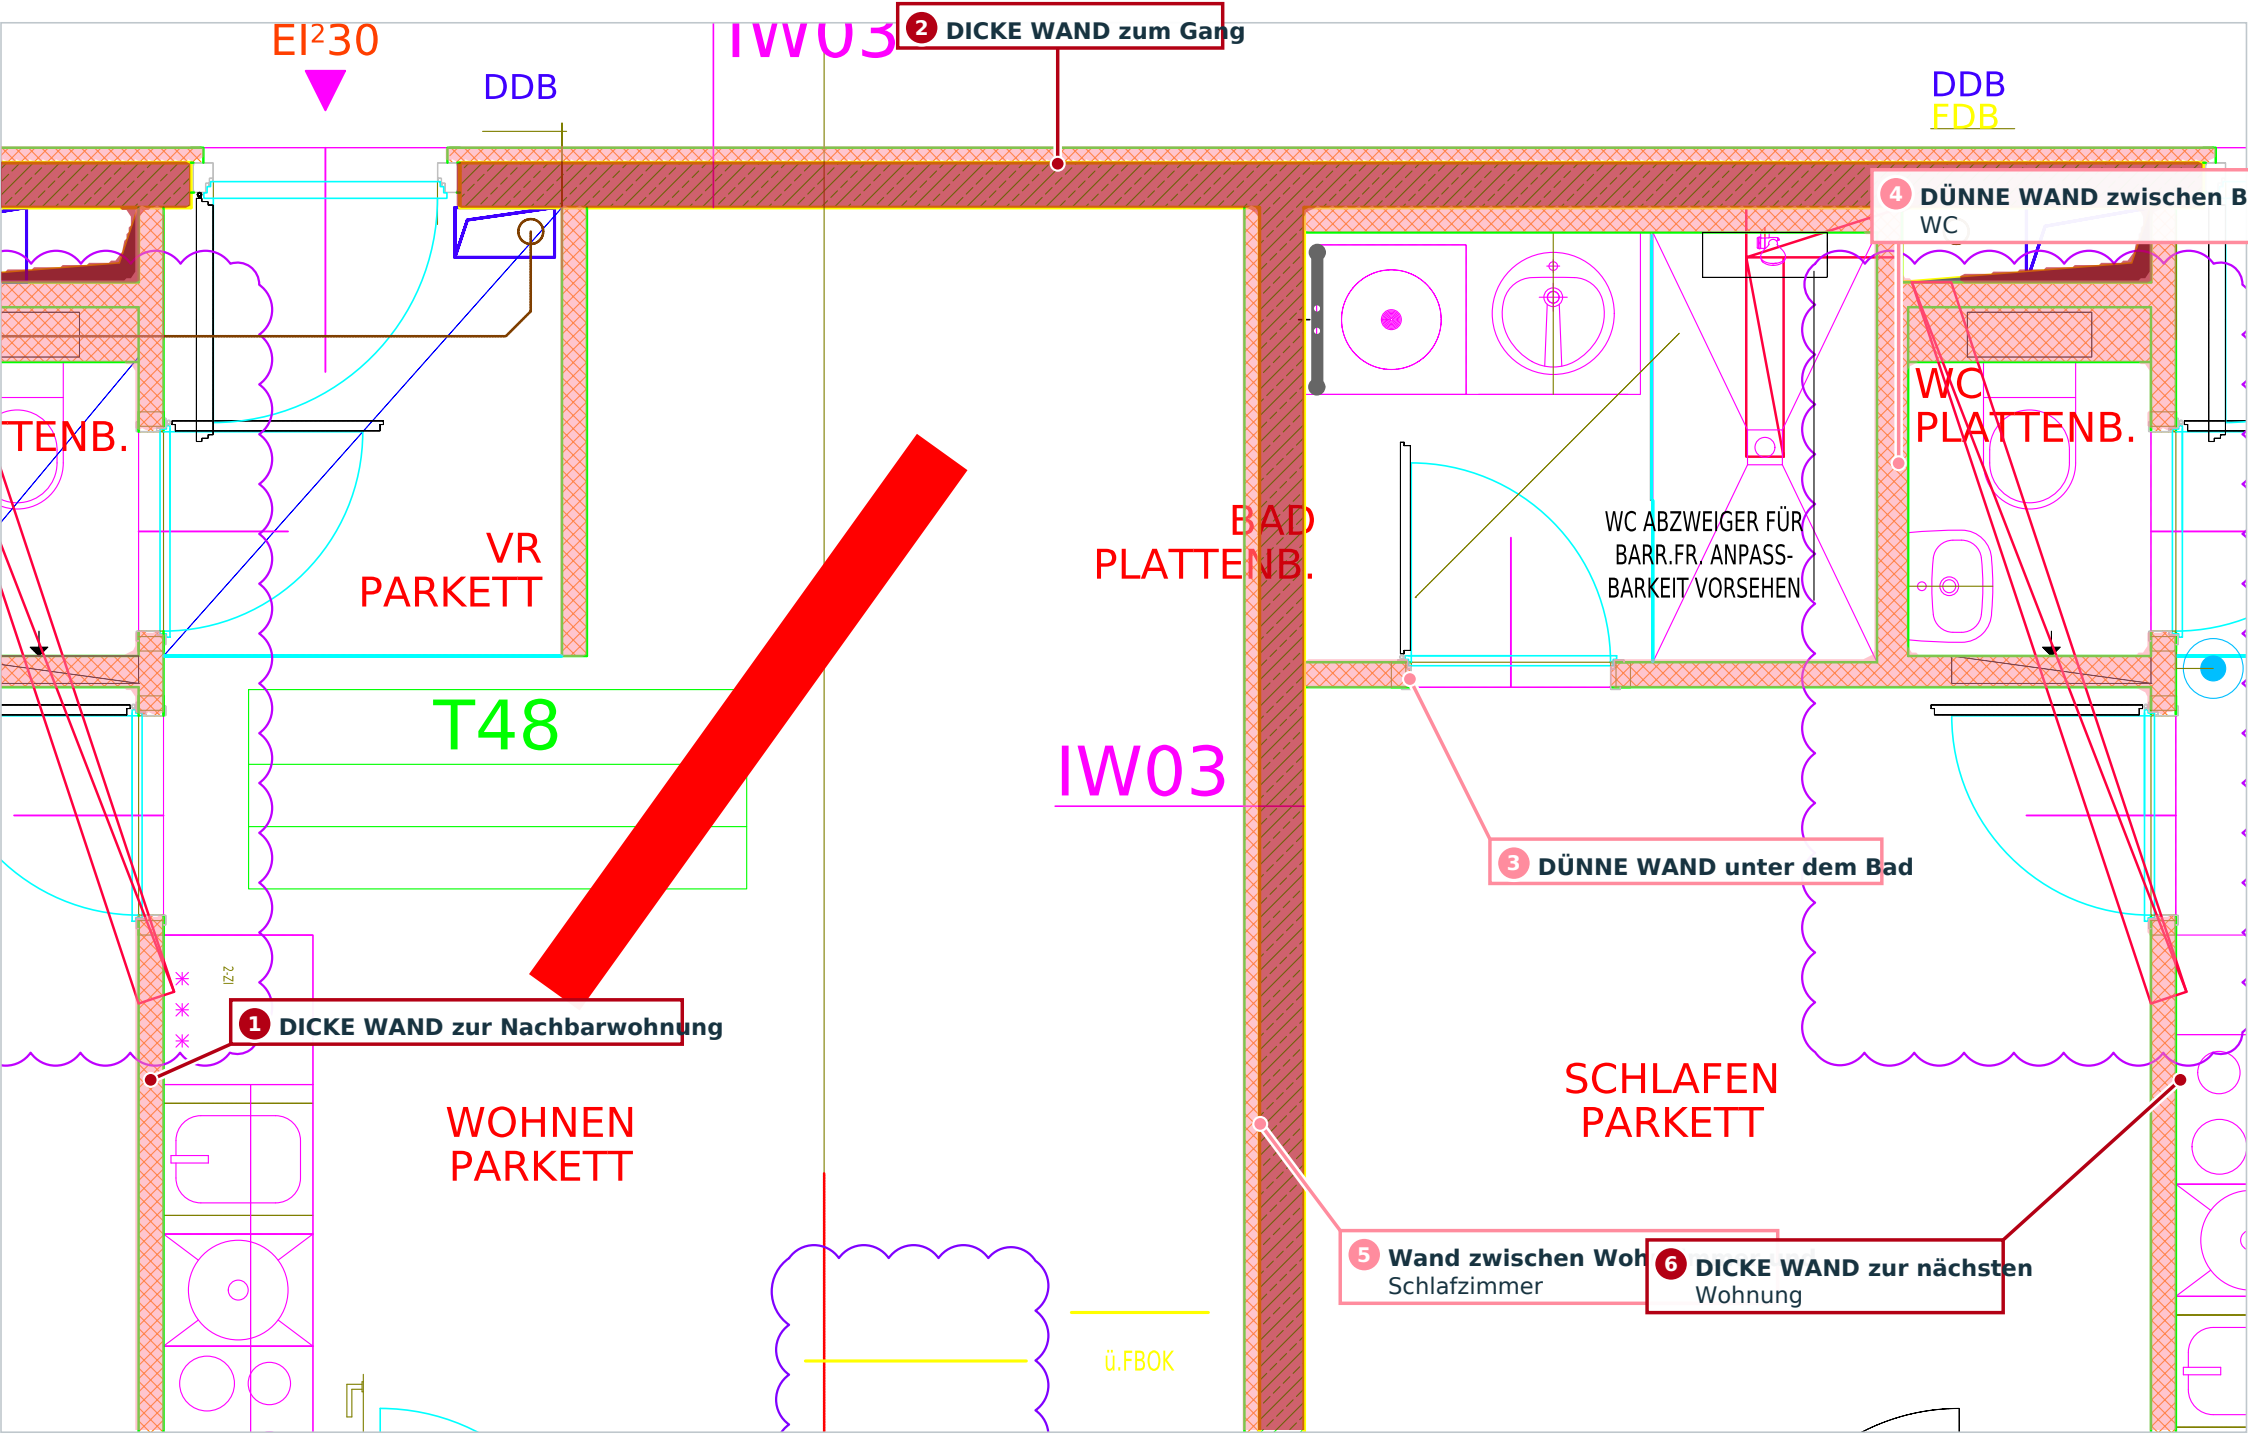

Zwei Arten, beide sind Wände

Für dich als Anfänger ist das Wichtigste: **Beide sind Wände.** Durch keine kann man gehen.

Dicke Wand (dunkelrot)

Was: eine kräftige, massive Wand. **Wie:** breiter Streifen, gelbe Außenlinie, grüne Schrägstriche. **Hier:** (1) und (6) trennen die Wohnung T48 von den Nachbarn, (2) trennt sie vom Gang.

Dünne Wand (hellrot)


Was: eine schmalere Trennwand in der Wohnung. **Wie:** schmaler Streifen, grüne Außenlinie, orange Gitterstriche. **Hier:** (3) und (4) um Bad und WC.

Der Drei-Punkte-Trick


1. Zwei parallele Linien? 2. Muster dazwischen? 3. Schließt der Streifen an andere Wände an? Nur wenn alles „ja“ ist, ist es eine Wand.

Die Kürzel wie IW03 nennen den Wandtyp. Die Bauart steht in einem Wandkatalog, der nicht beiliegt.

Hier bist du im Grundriss:

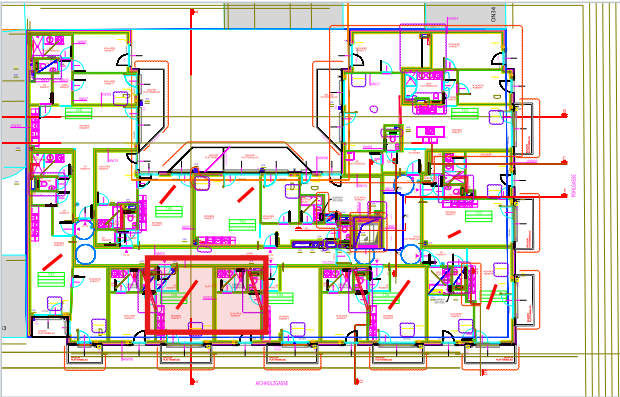

Alle Türen im Überblick - blau und nummeriert (63 Türblätter)

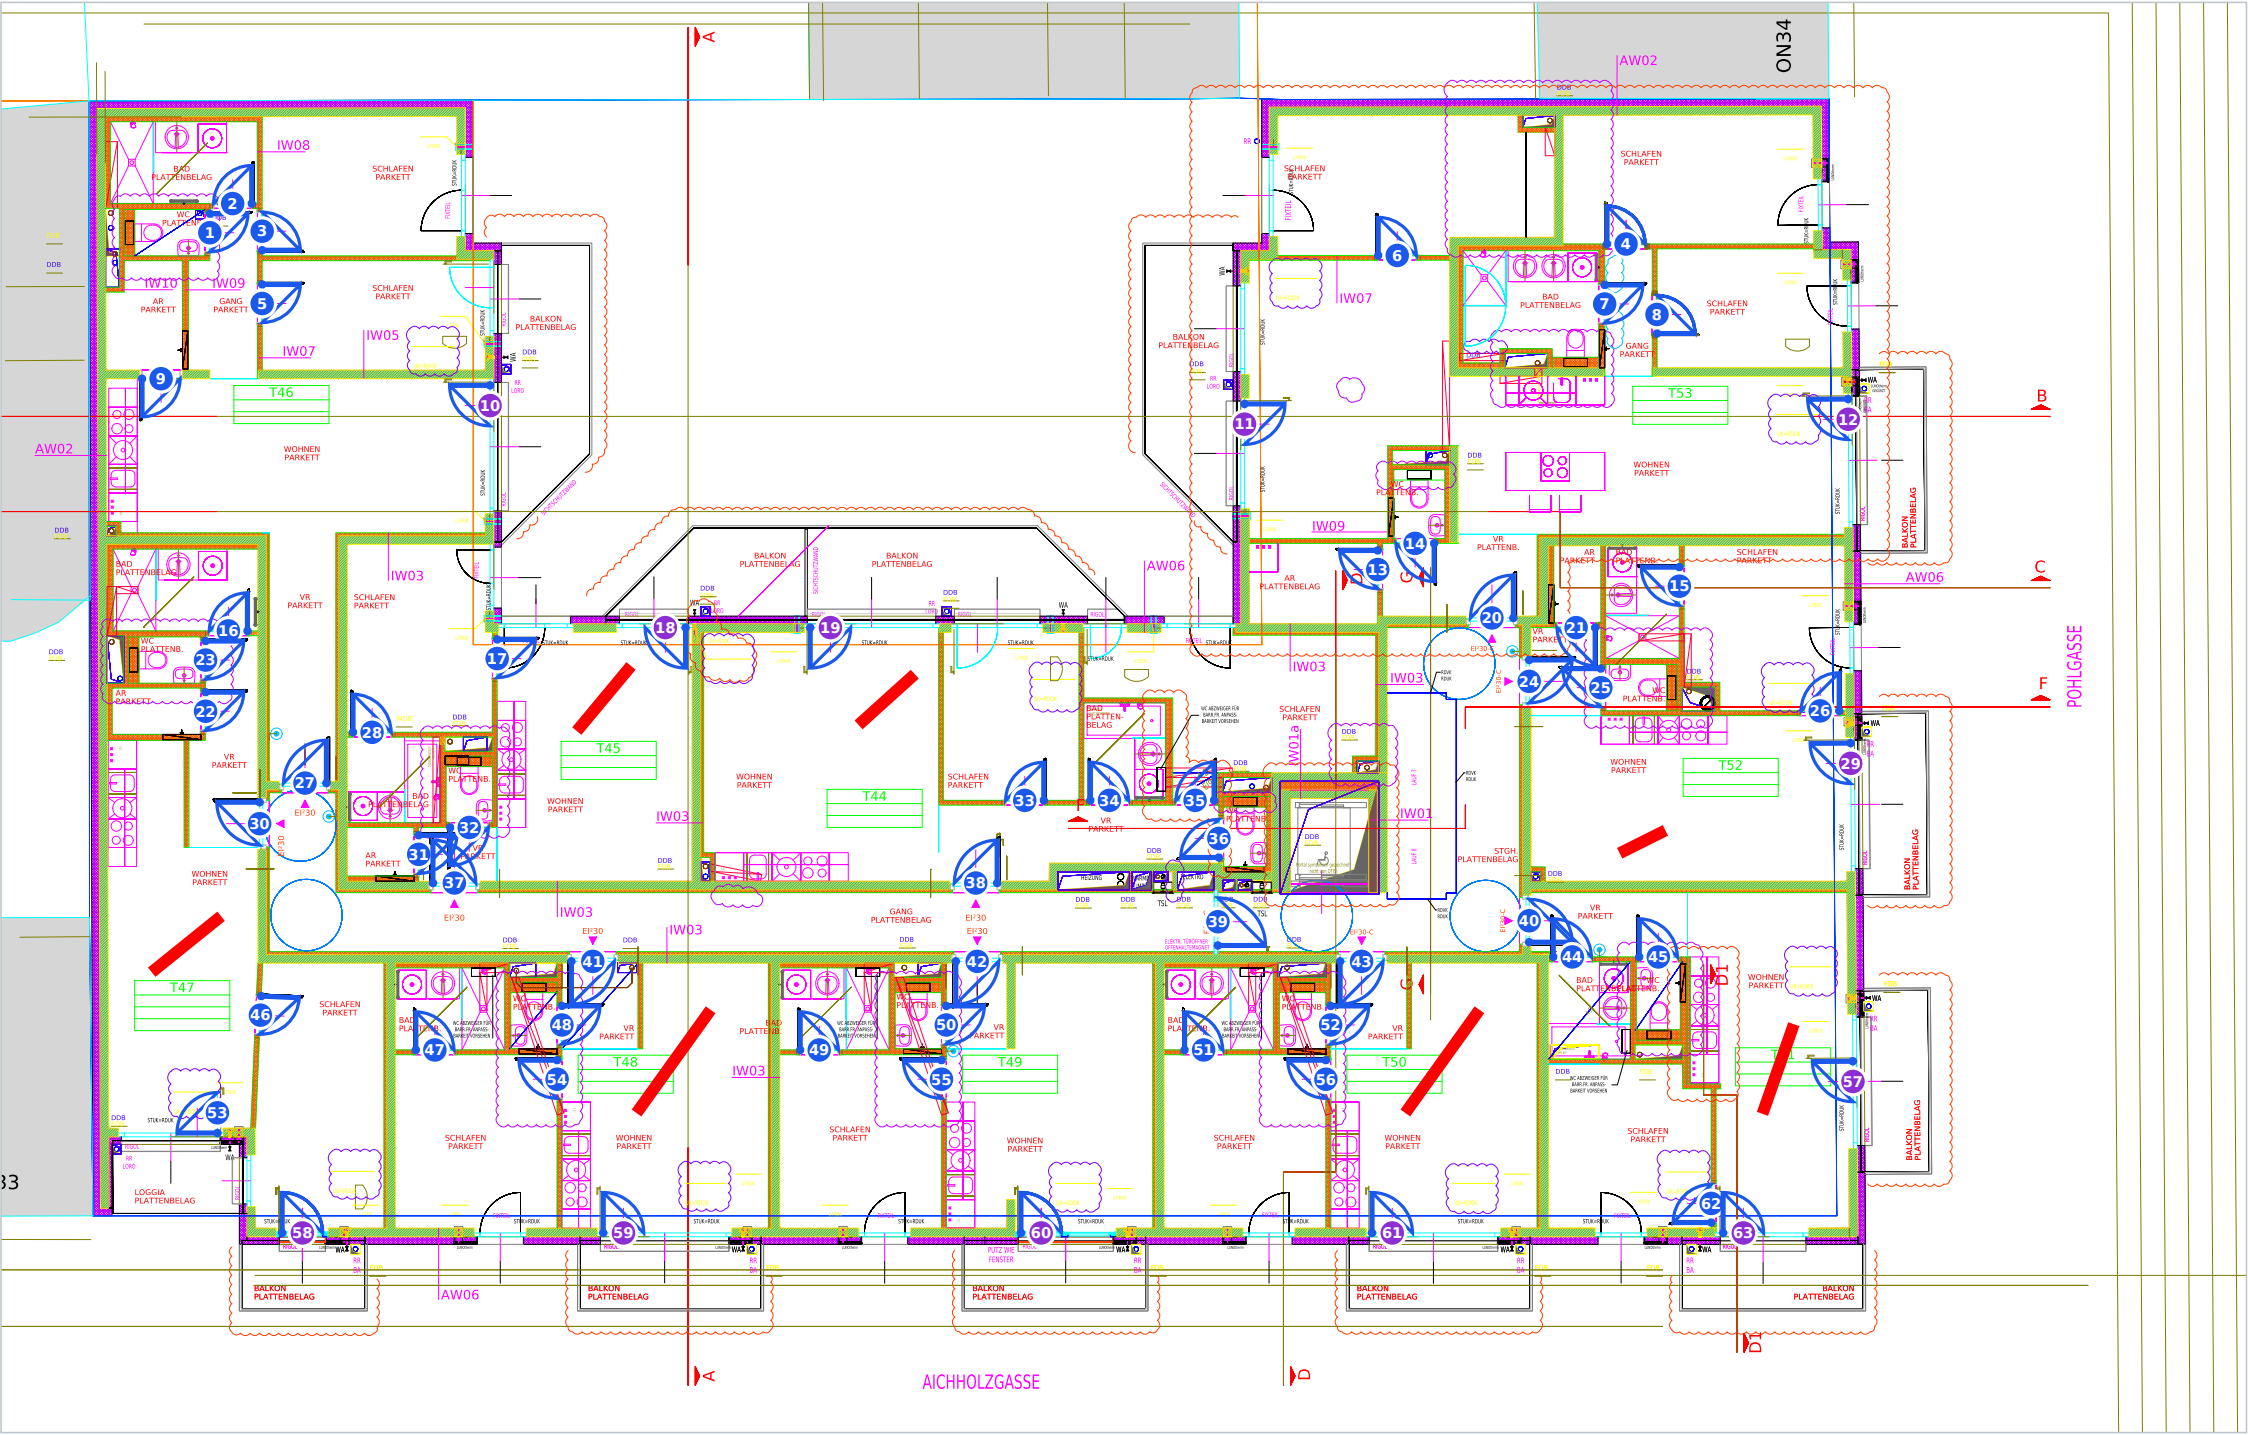

Was ist eine Tür?

Eine **bewegliche Platte** in einer Lücke der Wand. Ist sie offen, kann man von einem Raum in den anderen gehen.

Wie sieht sie im Grundriss aus?

Drei Dinge gehören zusammen: 1. **Lücke** in der Wand, 2. **gerade Linie** = Türblatt (offen gezeichnet), 3. **Viertelkreis** = Weg der Türkante.

Was zeigt diese Seite?

Jede Nummer steht mitten in einer Türöffnung: **63 Türblätter** insgesamt.

Blaue Nummer: Tür zwischen Innenräumen oder zum Gang.
Violette Nummer (12 Stück): Tür in der Außenwand, meist eine Glastür zum Balkon.

Größere Bögen = breitere Türen


Der Radius des Bogens ist so lang wie das Türblatt breit ist. Es kommen **vier Bogengrößen** vor – also vier Türbreiten. Die kleinsten sitzen meist bei WC und Abstellraum.

Übung

Such die Tür Nr. 41. Sie ist der Eingang der Wohnung T48. Auf welcher Seite liegt ihr Bogen?

Die Türen wurden aus den Bogenlinien erkannt. Der Plan zeigt nicht, ob eine Tür später offen oder versperrt ist.

Eine Drehtür Stück für Stück lesen (Tür zum Bad der Wohnung T48)

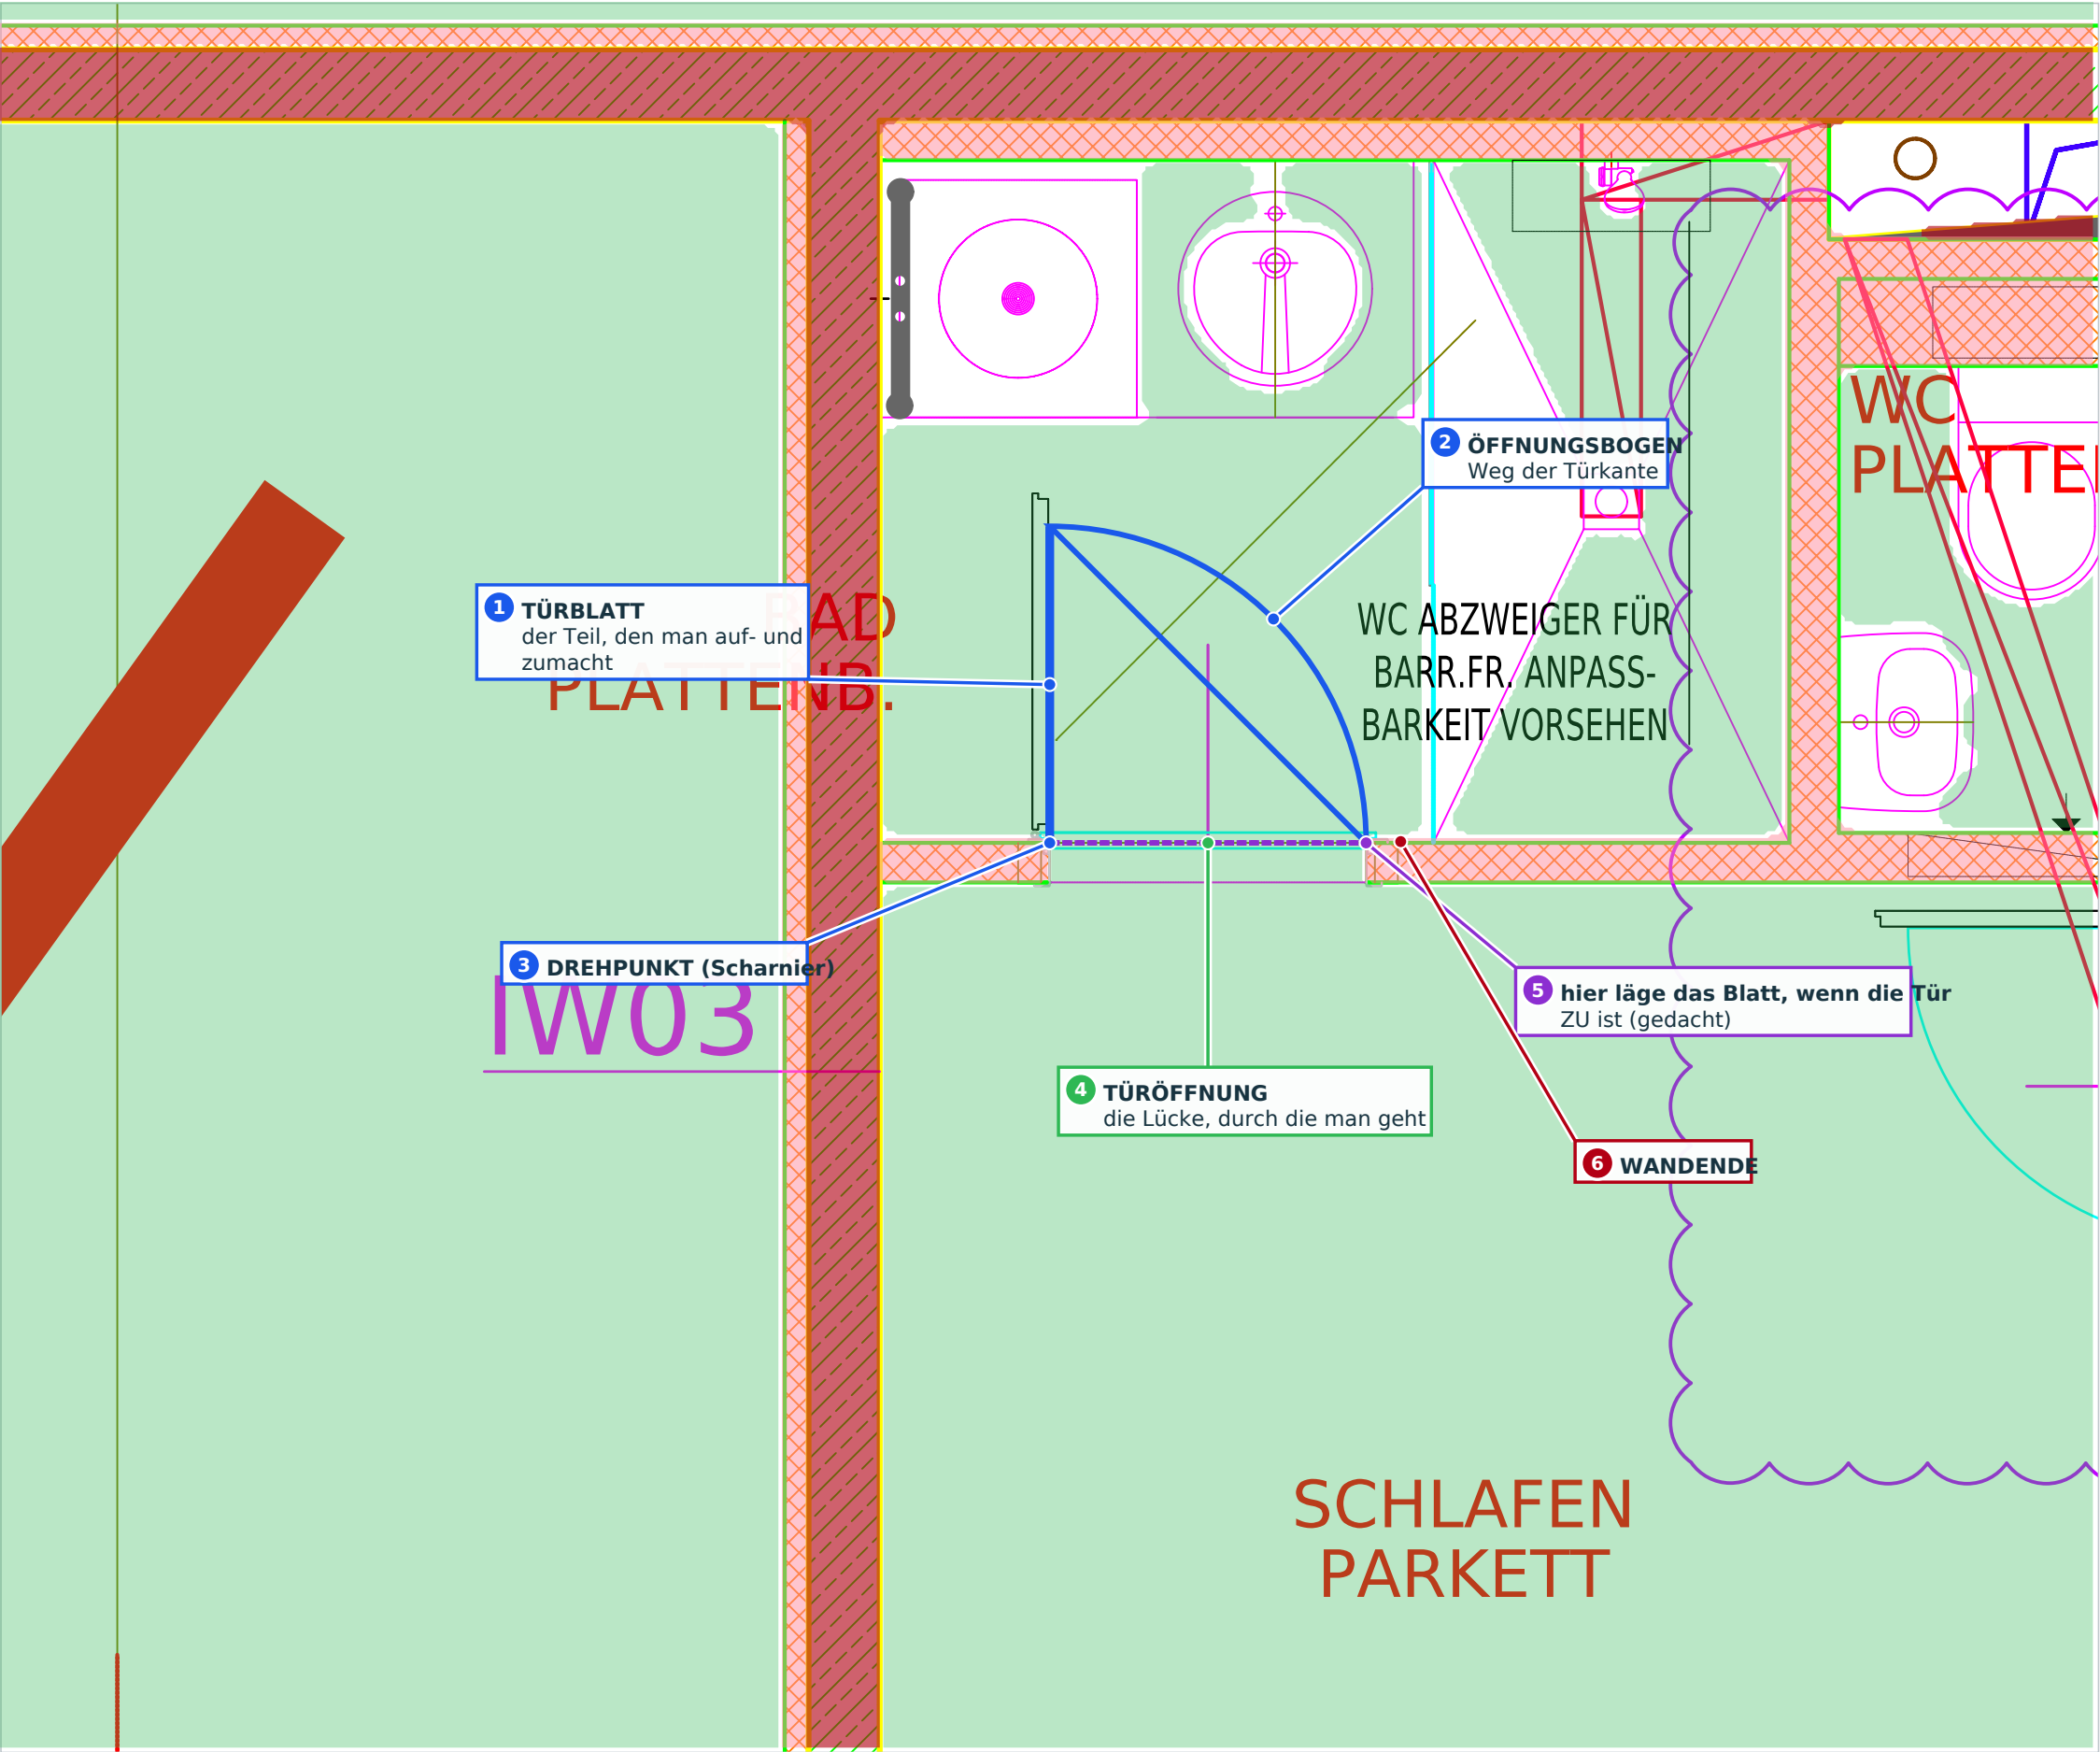

Was ist das?

Eine ganz normale **Drehtür** – man drückt die Klinke, und die Tür dreht sich um eine Seite. Hier: Tür Nr. 49, die Tür zum Bad der Wohnung T48.

Wie sieht sie im Plan aus?

(4) Die Wand ist unterbrochen. Zwischen den Wandenden ist die Lücke.

(1) Das Türblatt ist eine gerade Linie. Der Plan zeichnet Türen immer **offen**.

(3) Am Drehpunkt ist die Tür befestigt.


(2) Der Viertelkreis zeigt den Weg der Türkante. Innerhalb des Bogens muss Platz bleiben, sonst geht die Tür nicht auf.

(5) Gestrichelt: So läge das Blatt bei geschlossener Tür. Das steht nicht im Original.


In welche Richtung geht sie auf?

Immer **zur Seite des Bogens**. Diese Tür geht laut Plan ins Bad hinein auf.

Hier bist du im Grundriss:

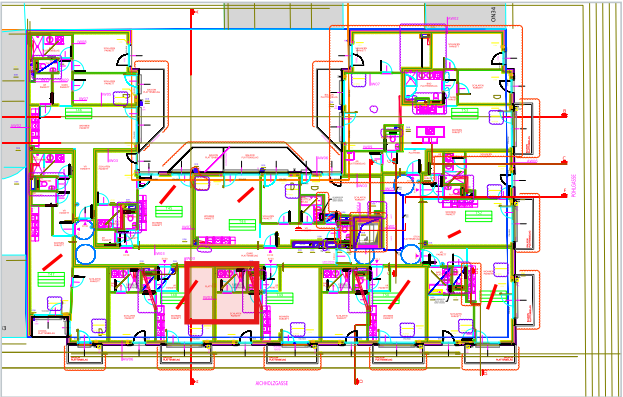

Die Wohnungseingangstür: zwischen Gang und Wohnung

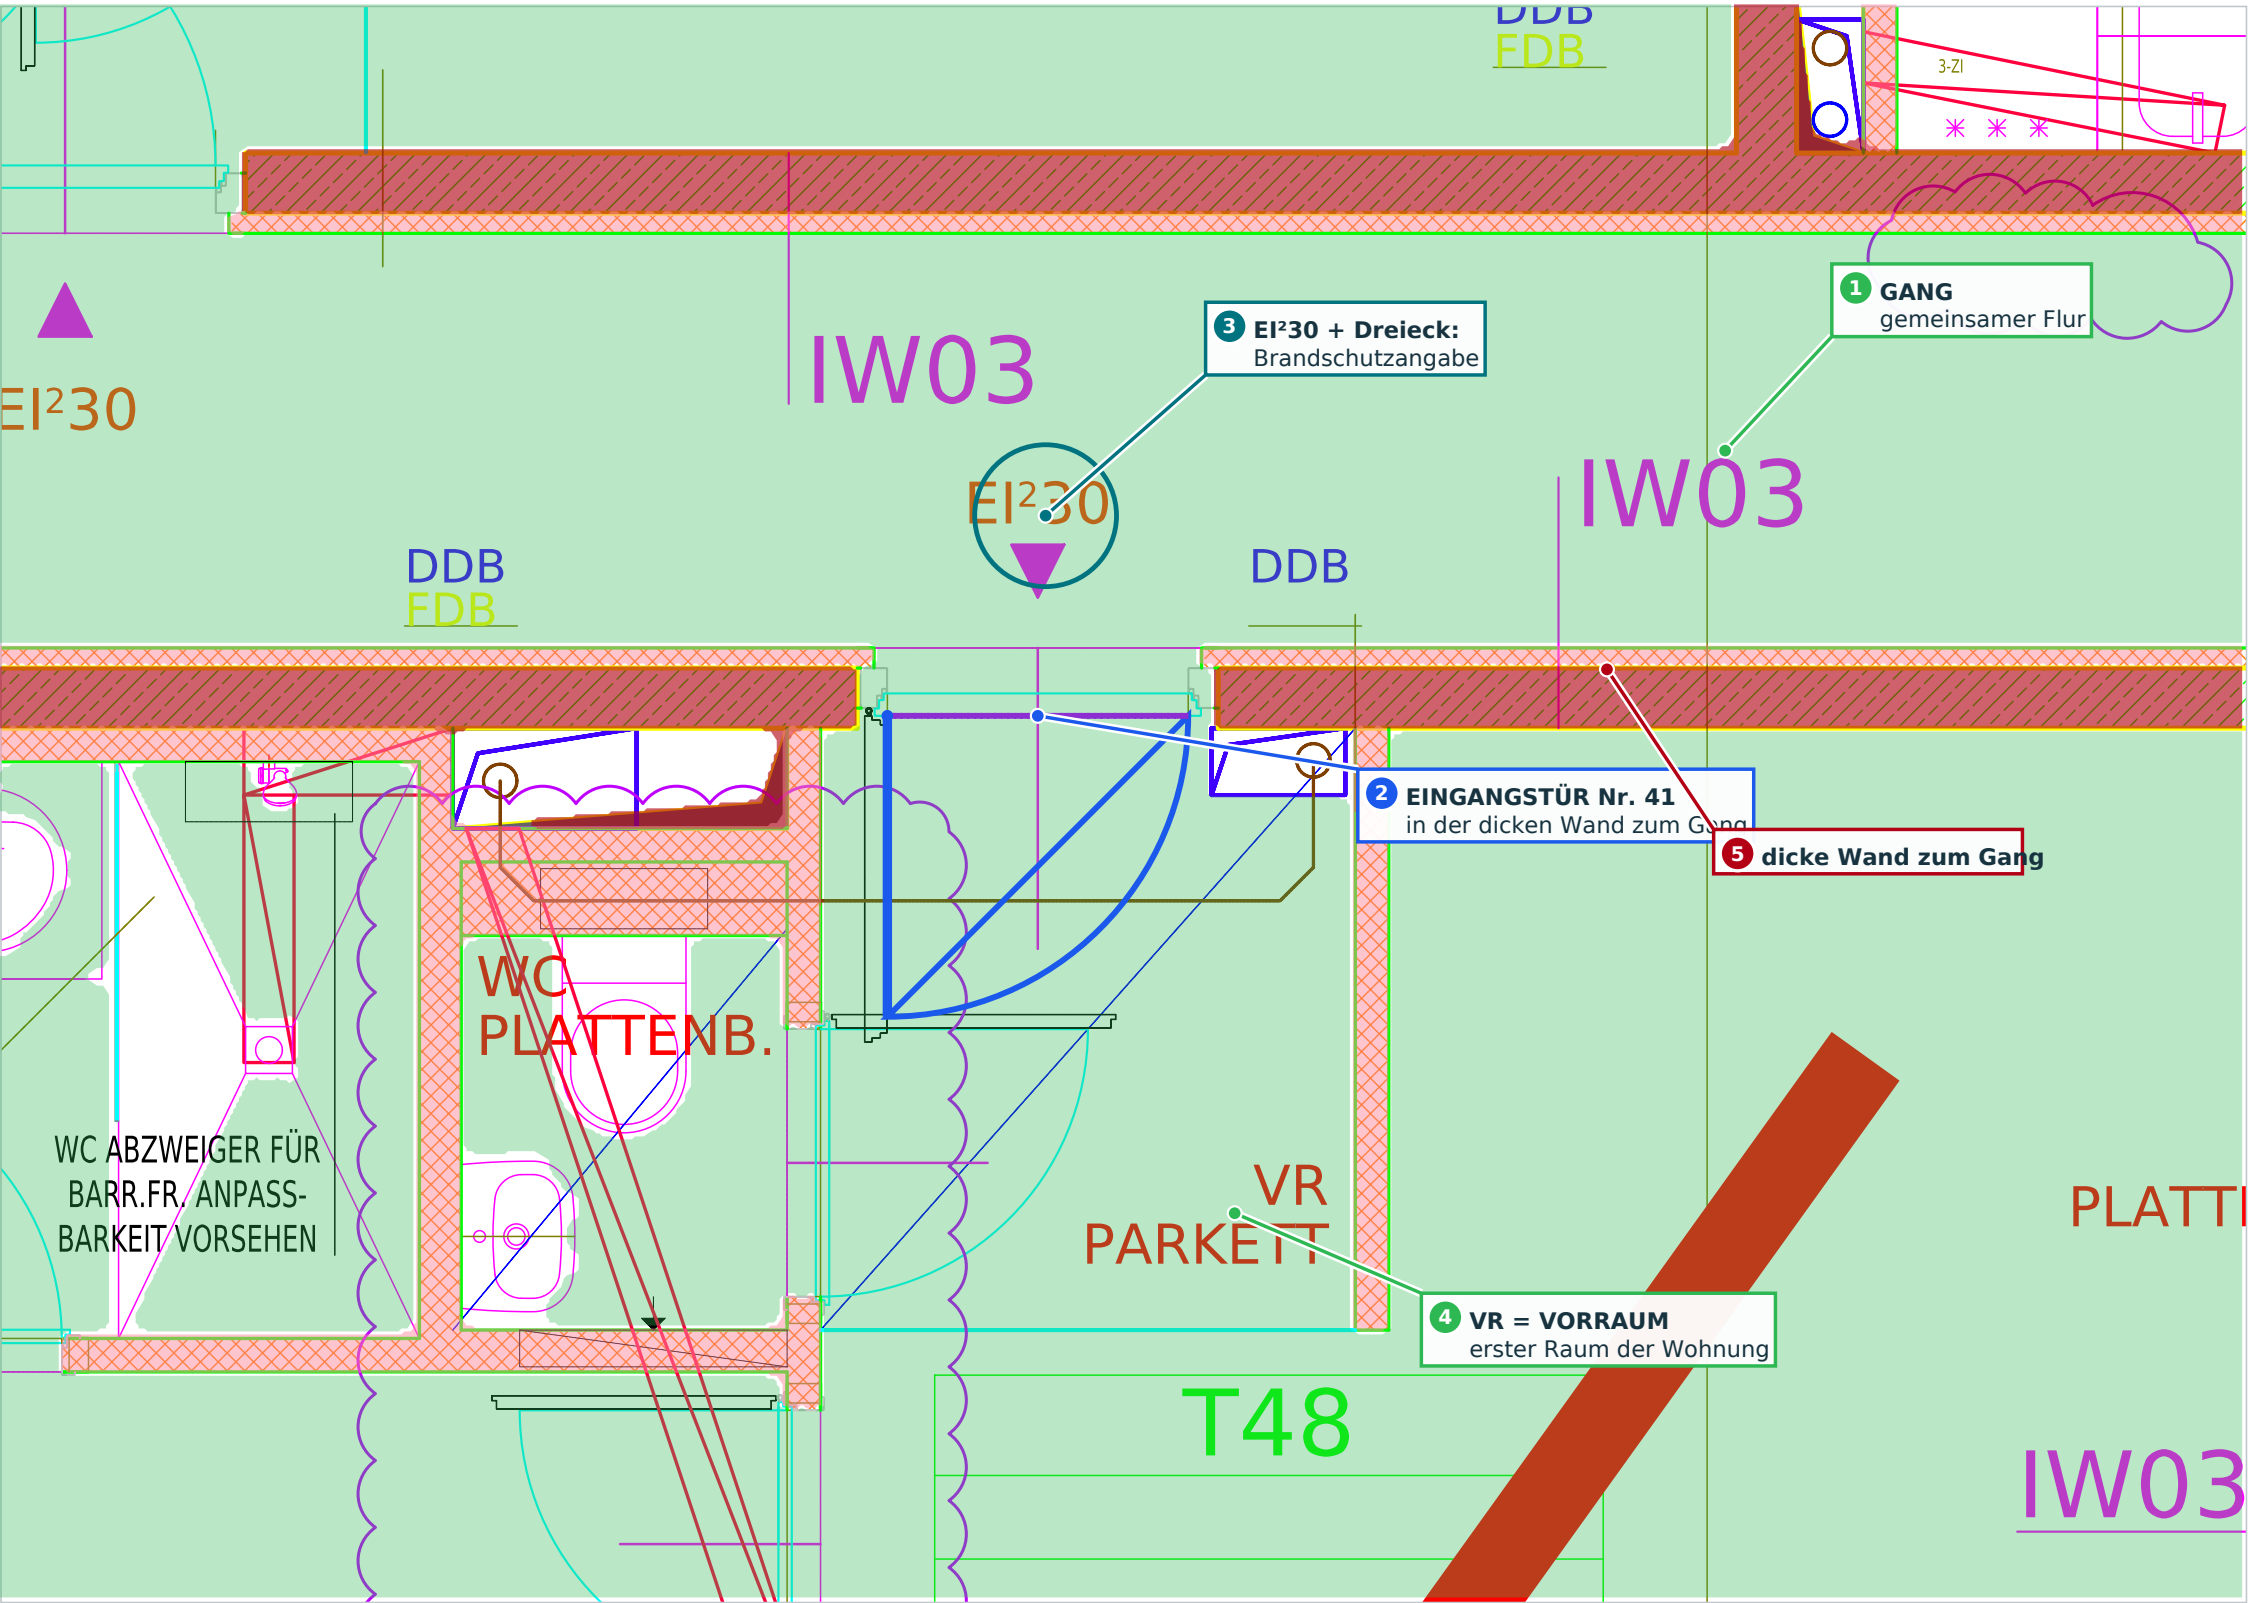

Was ist das?

Die **Wohnungseingangstür** der Wohnung T48. Sie verbindet den **Gang** (1) mit dem **Vorraum** (4).

Woran erkenne ich sie?

Sie sitzt in der **dicken Wand** (5) zwischen Gang und Wohnung, mit Lücke, Türblatt und Bogen (2). Der Bogen liegt auf der **Wohnungsseite**: Die Tür geht also **in die Wohnung hinein** auf.

Was bedeutet „EI²30“?

Eine **Brandschutzklasse** (3): Die Tür soll ein Feuer **30 Minuten** aushalten. E = hält Flammen und Rauchgase ab, I = begrenzt die Hitze auf der anderen Seite. Steht **EI²30-C**, schließt die Tür zusätzlich **von selbst** (z. B. am Stiegenhaus).


Das kleine **magenta Dreieck** markiert, zu welcher Tür die Angabe gehört.

Warum ist das wichtig?


Der Gang ist der Weg aller Bewohner nach draußen. Brandschutztüren verhindern, dass Feuer aus einer Wohnung schnell in den Gang kommt.

Was das Dreieck im Detail bedeutet, erklärt der Plan nicht.

Hier bist du im Grundriss:

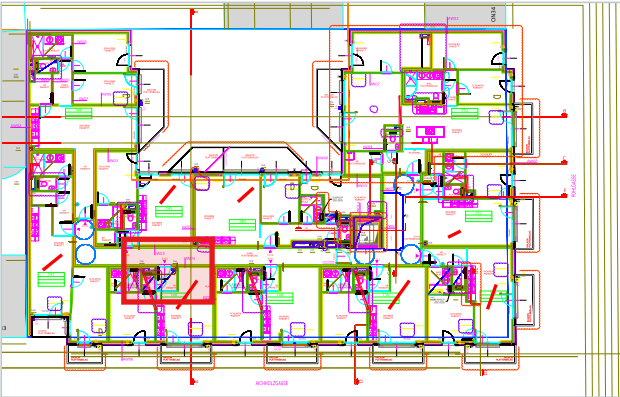

Die Balkontür: eine Tür aus Glas in der Außenwand

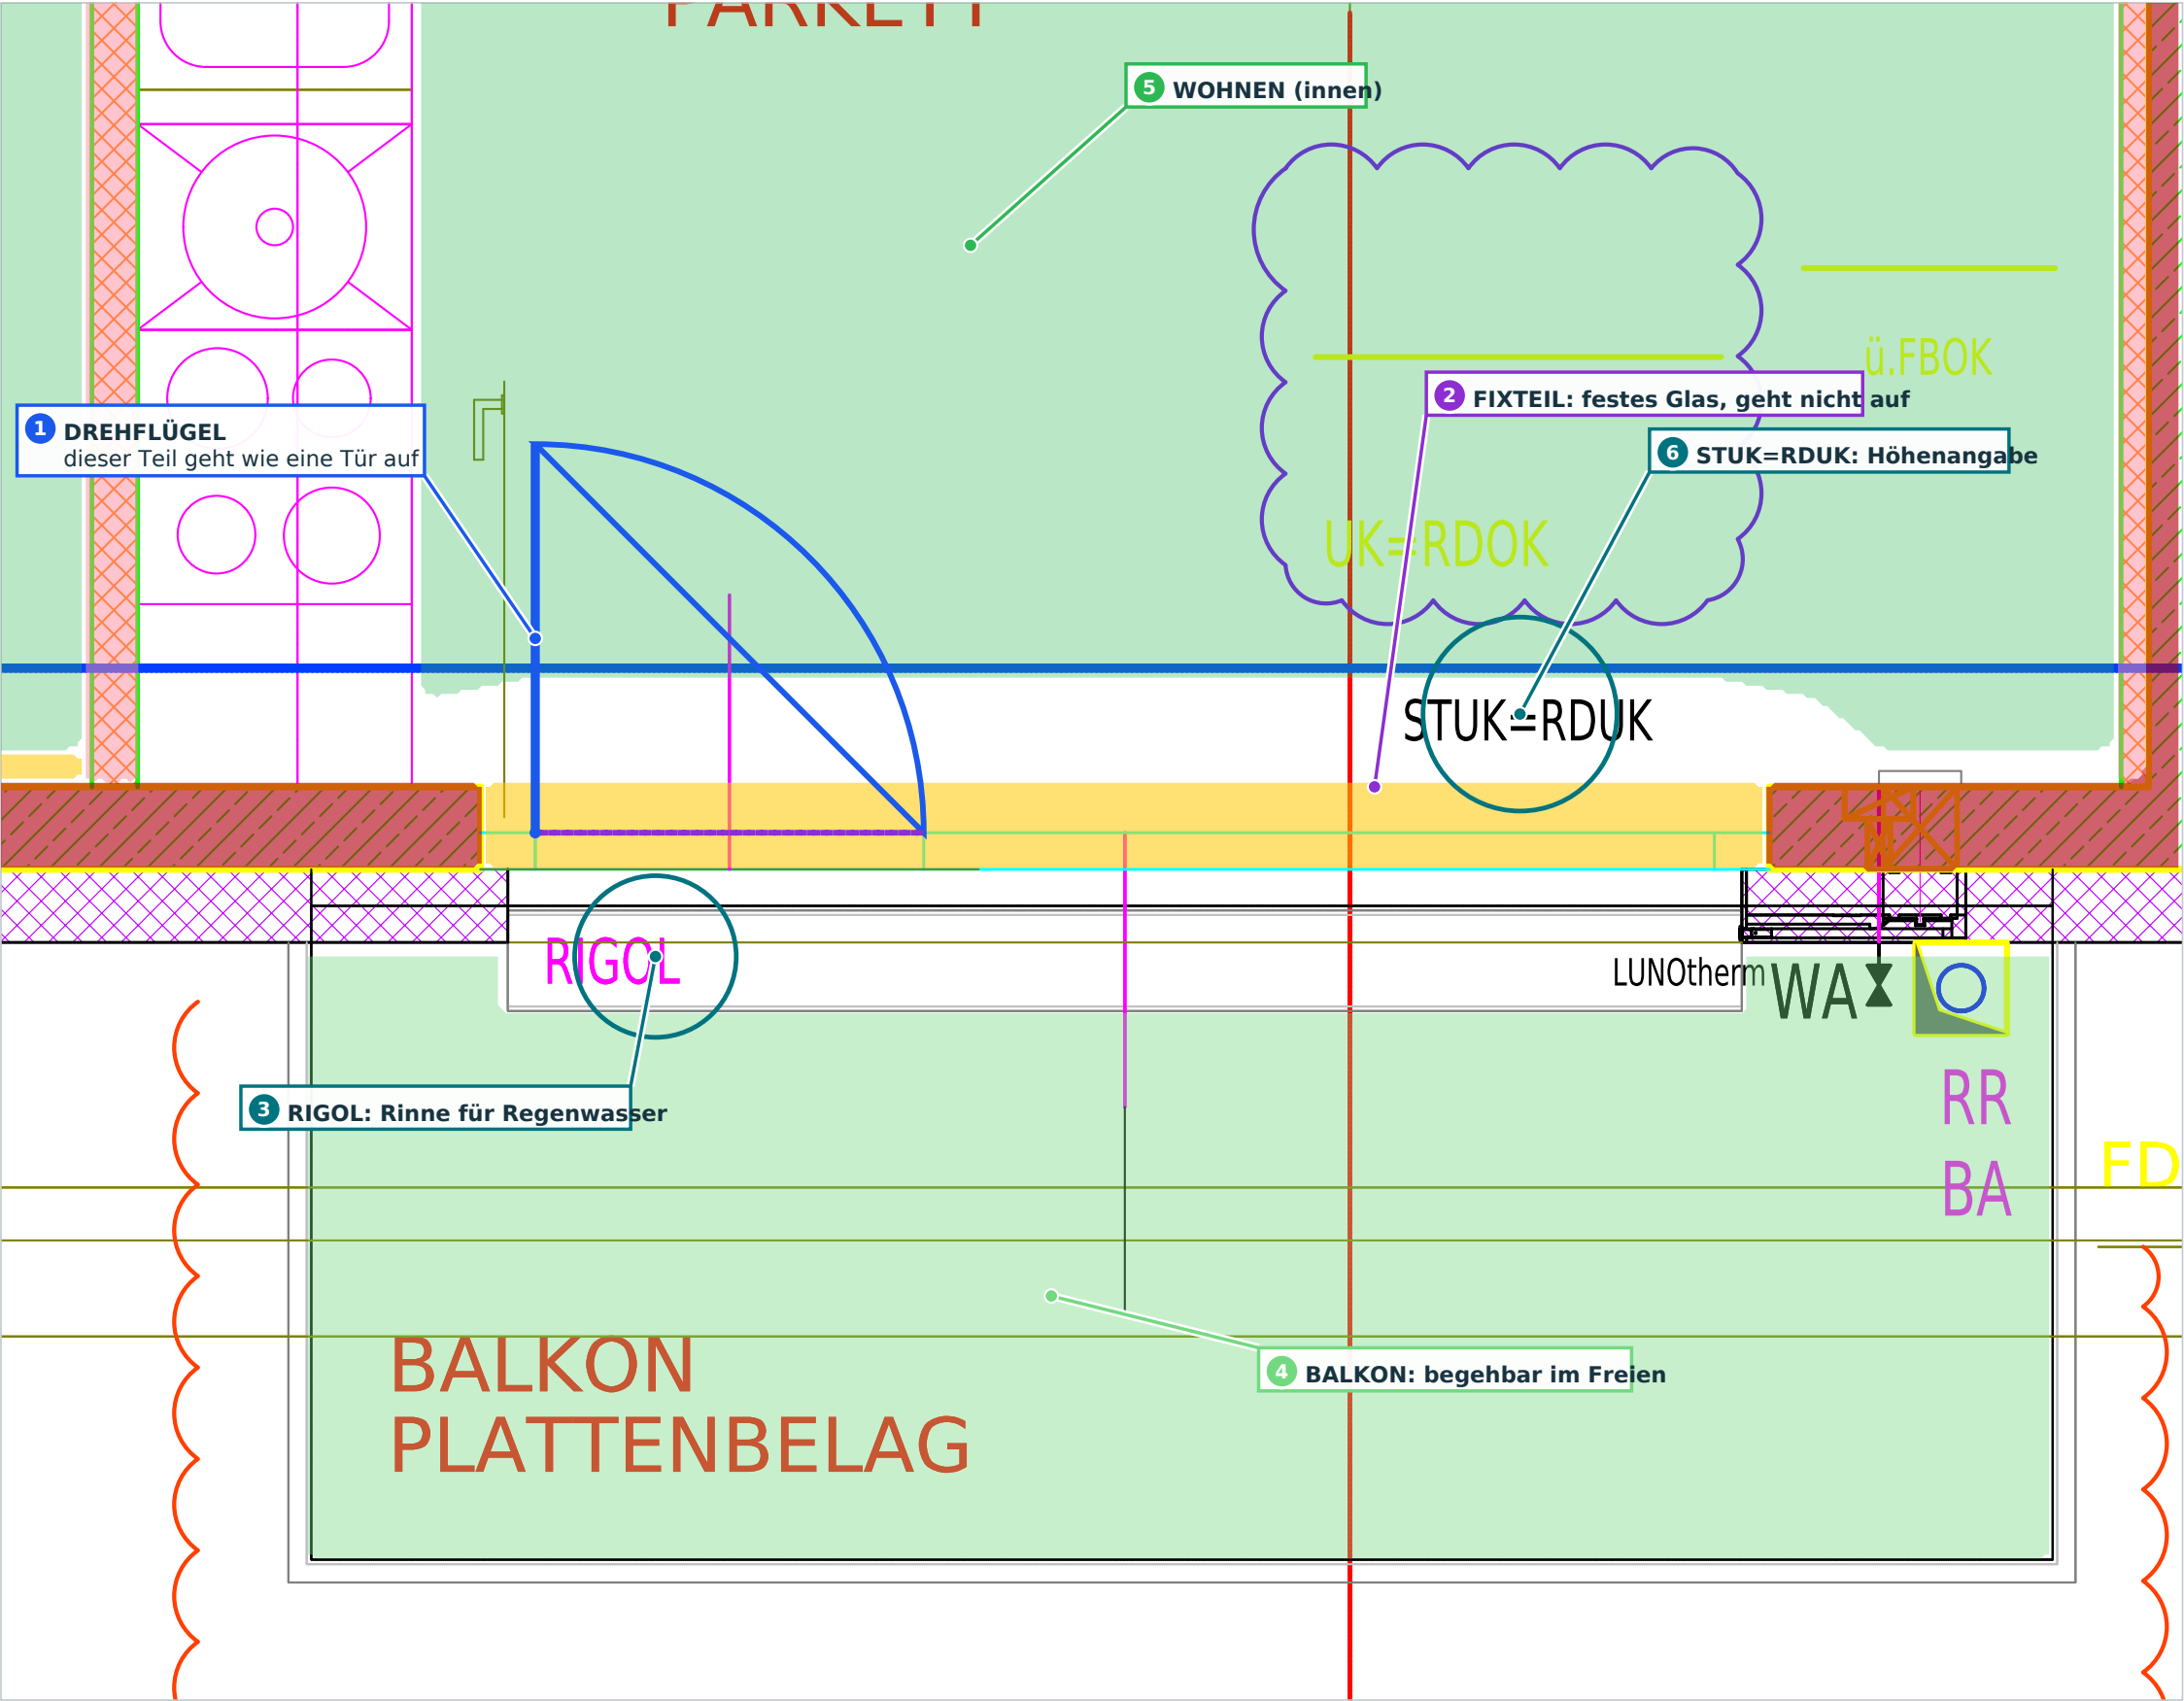

Was ist das?

Eine **Glasfront** zwischen Wohnzimmer (5) und Balkon (4). Ein Teil ist eine Tür (1), der Rest festes Glas (2).

Tür oder festes Glas?

Tür (1): Türblatt und **Viertelkreis**. Nur wo ein Bogen ist, geht etwas auf.

Festes Glas (2): nur dünne, parallele Linien, **kein Bogen**. Im Plan steht oft **FIXTEIL**. Da kann man nicht durchgehen.

Und die Wand?


Links und rechts der Glasfront siehst du die rote Wand mit Muster. Dazwischen (gelb) ist die Wand für das Glaselement unterbrochen.

Die kleinen Texte


RIGOL (3): Rinne vor der Tür gegen Regenwasser. **STUK=RDUK** (6): Die Oberkante der Öffnung liegt an der Unterseite der Rohdecke.

Wie hoch die Schwelle ist, zeigt der Grundriss nicht.

Hier bist du im Grundriss:

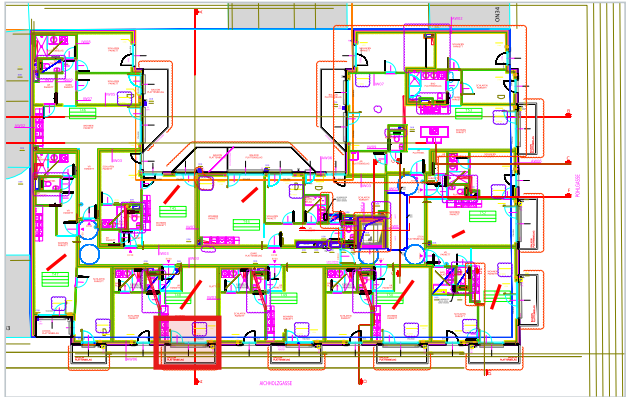

Alle Öffnungen in der Außenwand - gelb, Glas violett

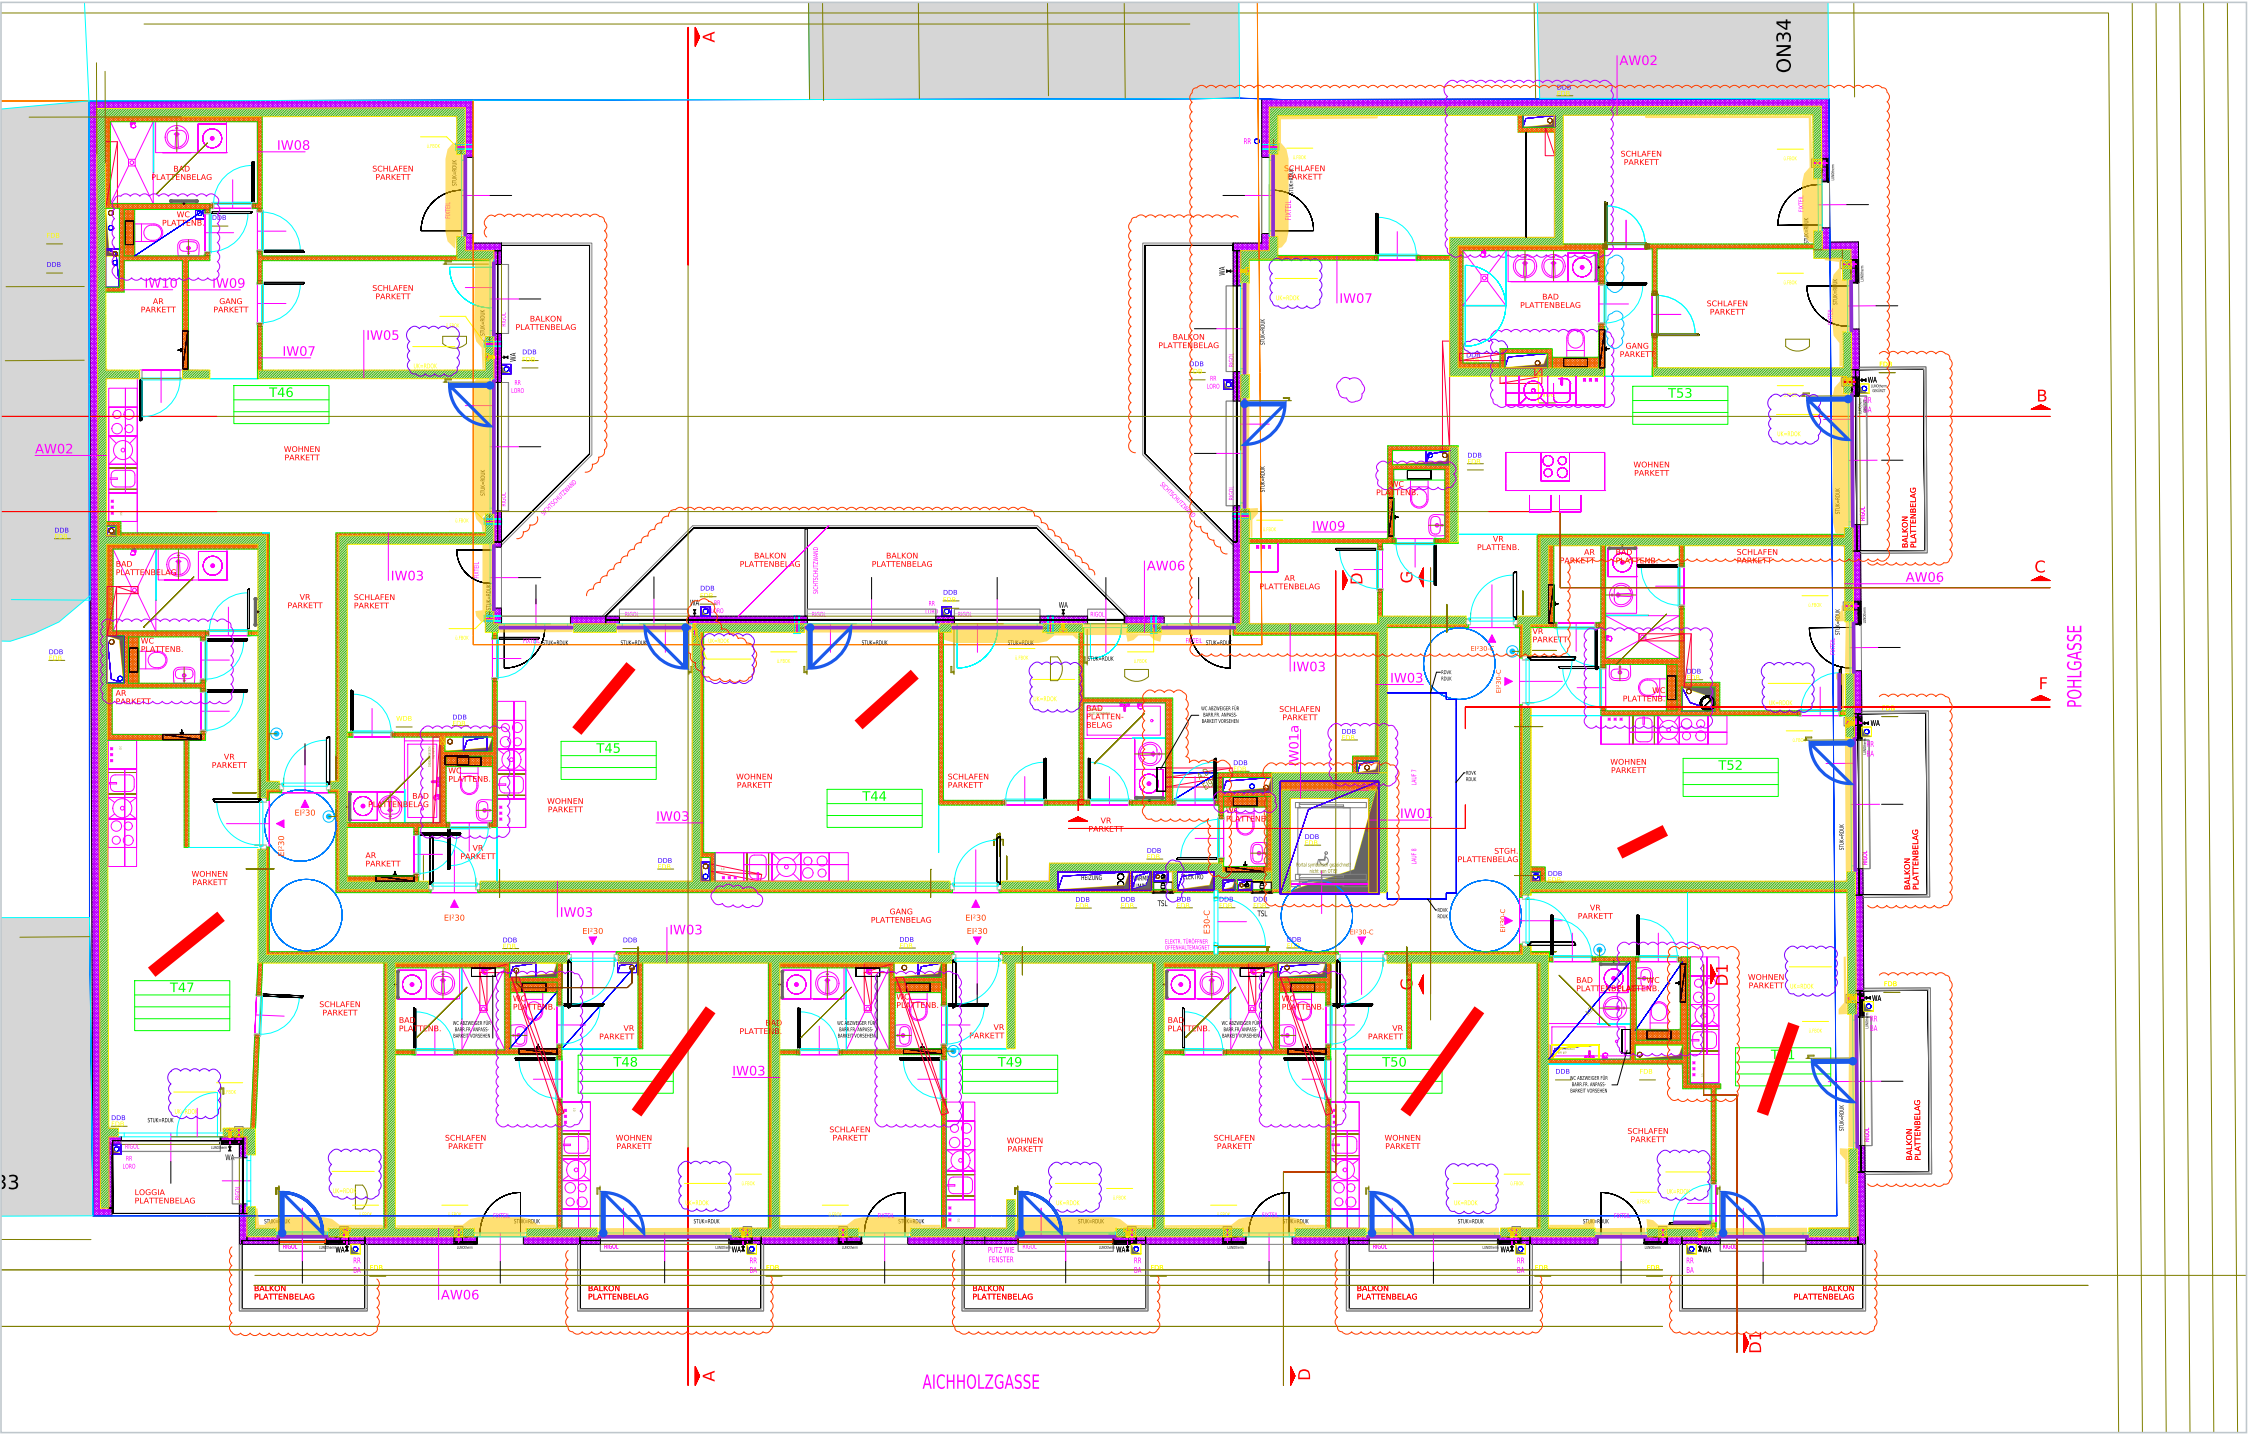

Was ist ein Fenster?

Eine Öffnung in der Außenwand, in der eine **Glasscheibe** in einem **Rahmen** sitzt. Licht und Luft kommen herein. **Hindurchgehen kann man nicht.**

Wie sieht es im Grundriss aus?

Die dicke, gemusterte Wand hört auf. Stattdessen laufen **mehrere sehr dünne Linien** durch die Lücke: außen und innen der Rahmen, in der Mitte das Glas.


Was zeigt diese Seite?

- Gelb:** 34 erkannte Unterbrechungen der Außenwand.
- Violett:** bei 25 davon wurde die mittlere Glaslinie gefunden.
- Blau:** Glastüren zu den Balkonen.

Besonderheit dieses Hauses

Fast alle Öffnungen sind **große Glasfronten** vom Boden bis zur Decke, teils fest (FIXTEIL), teils als Tür. Klassische Fenster mit gemauerter Brüstung sind im Plan nicht klar erkennbar. Gelb wurde automatisch aus den Wandlücken abgeleitet; kleine Lücken können fehlen. Fensterhöhen zeigt ein Grundriss nie.

Glas erkennen: Rahmen, Scheibe und die Wand daneben

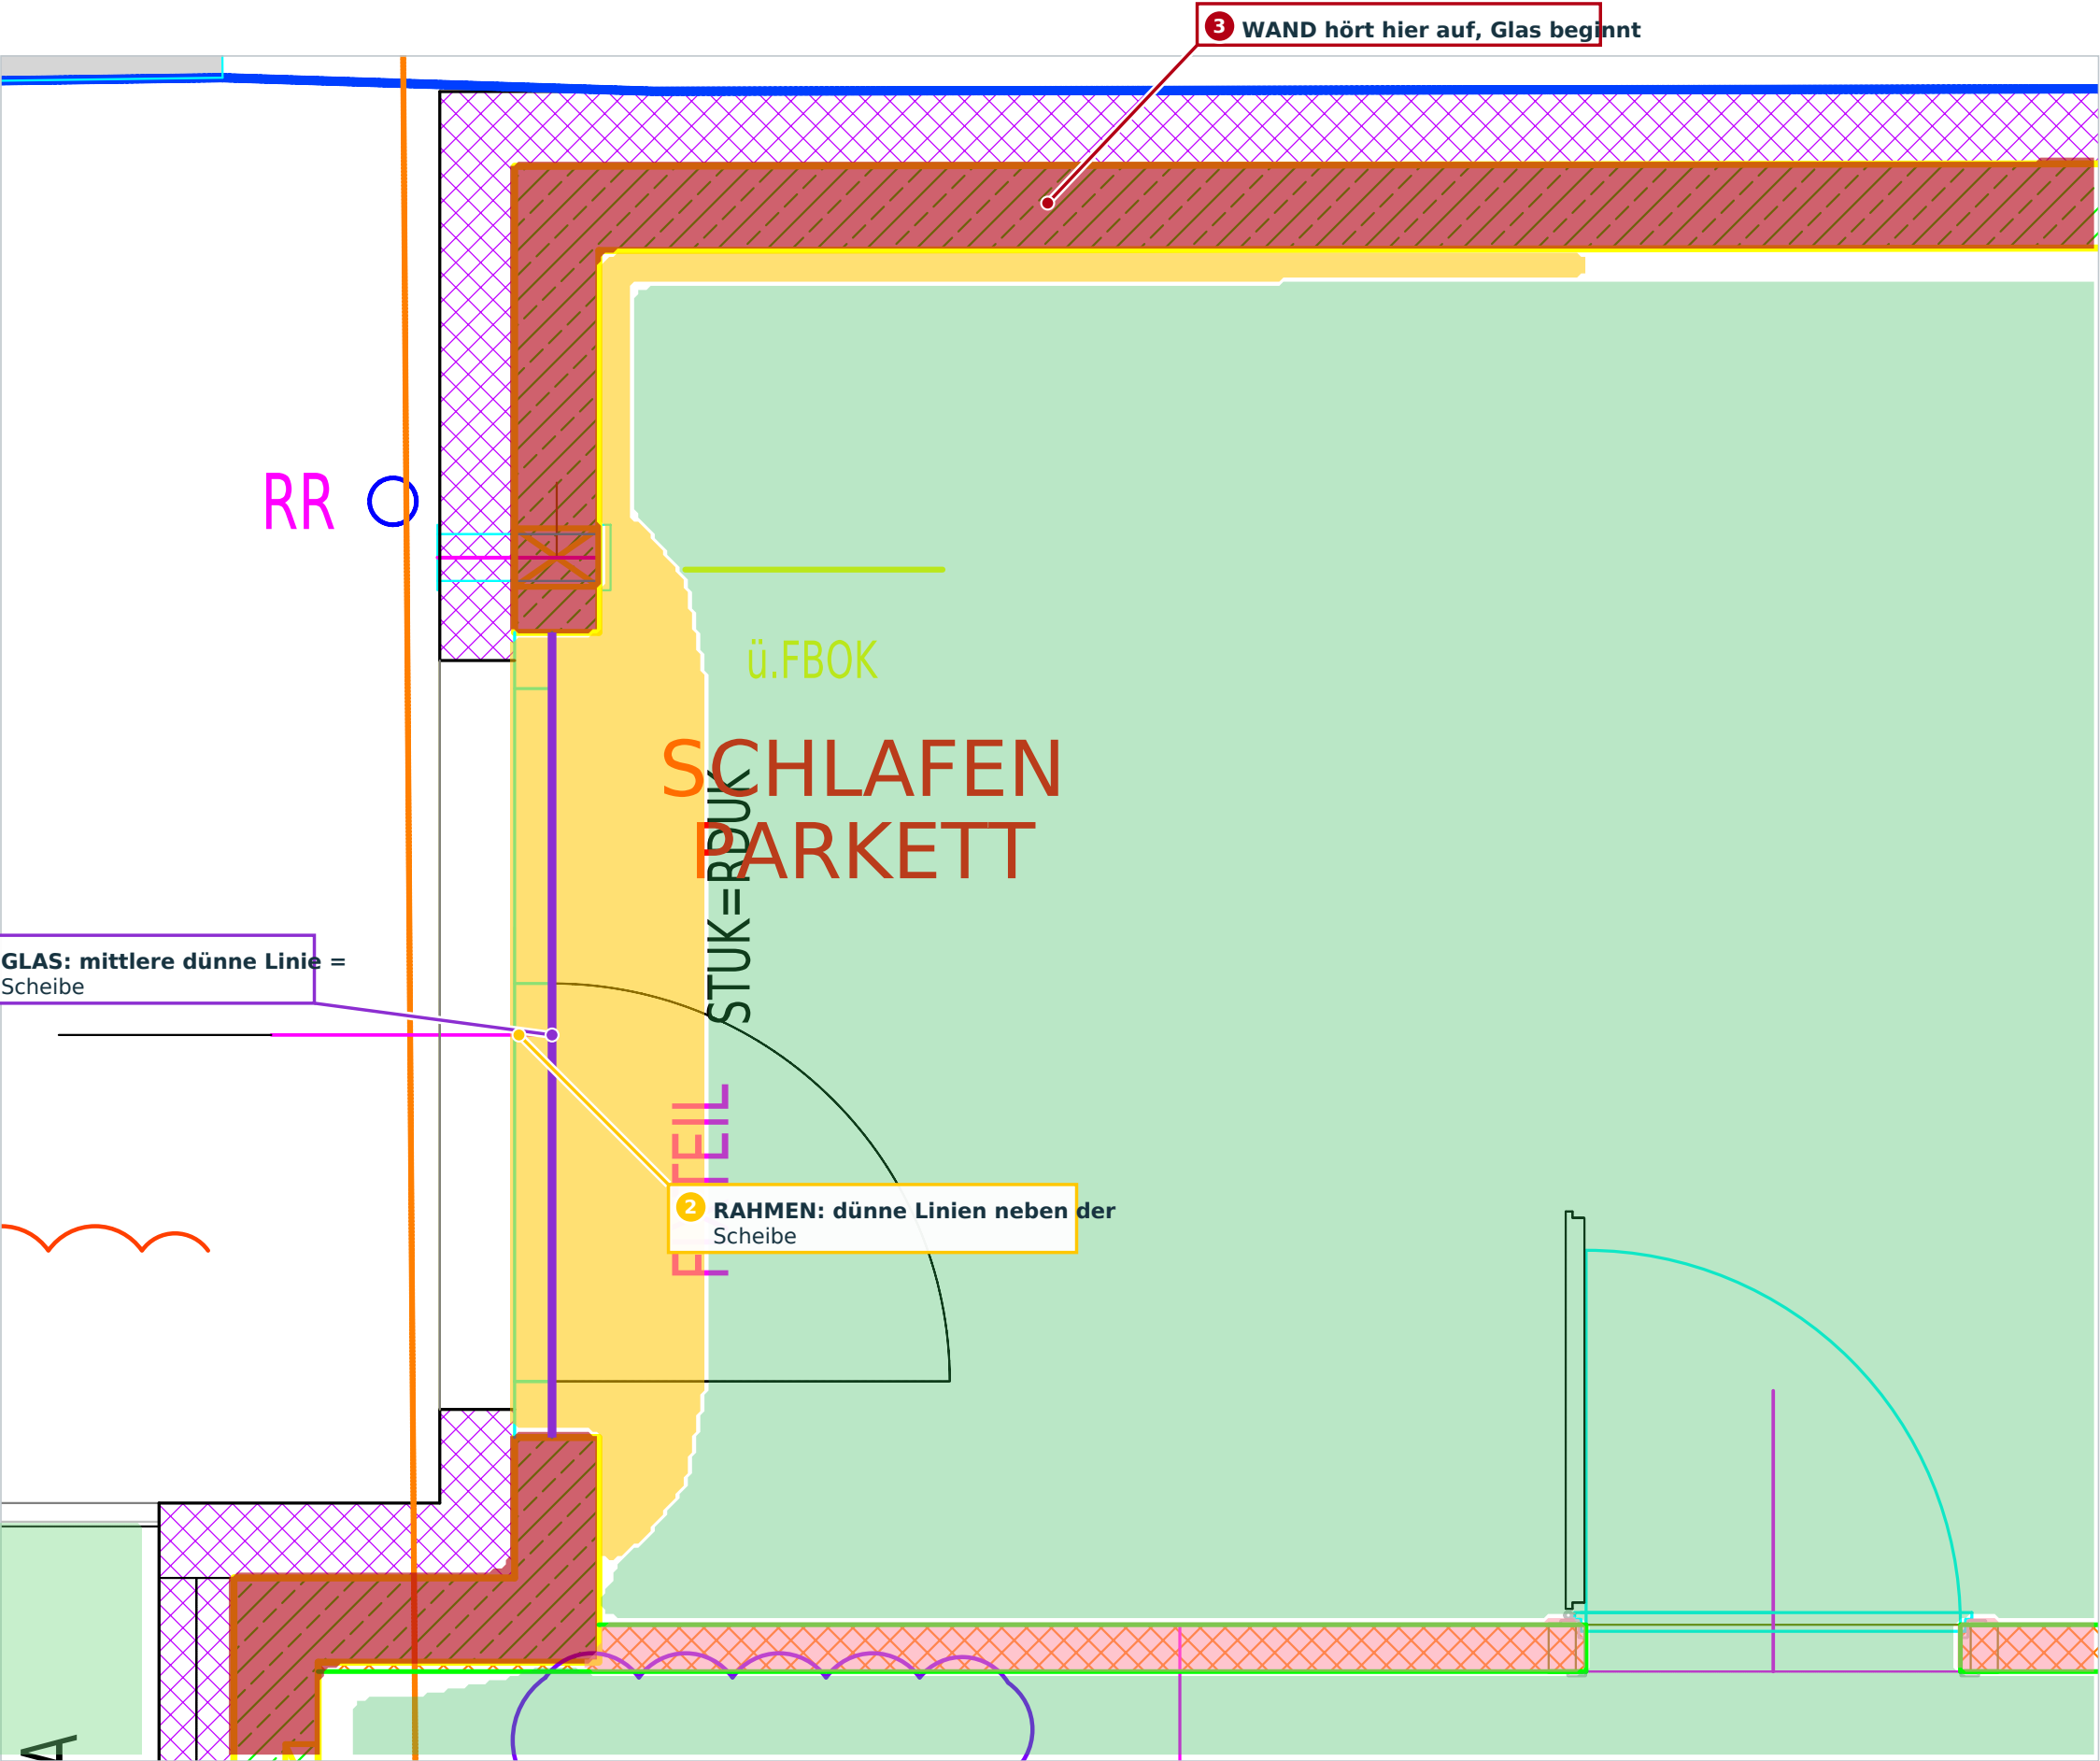

Was ist Glas?

Ein durchsichtiges, festes Material. Es lässt **Licht** durch. Für eine Person ist es aber wie eine Wand: **kein Durchgang**.

Wie sieht Glas im Grundriss aus?

Glas ist nur wenige Millimeter dick – im Plan eine **einzelne, sehr dünne Linie** (1) zwischen den Linien des Rahmens (2).

Glas oder Wand?


Wand (3): breiter Streifen **mit Muster**. **Glas:** ganz dünne Linien **ohne Muster**.

Glas oder Rahmen?


Der Rahmen hält das Glas und liegt außen herum, das Glas liegt in der Mitte. Im Original haben beide dieselbe hellblaue Farbe – darum ist die Scheibe hier **violett** nachgezogen.

Welche Linie genau die Scheibe ist, lässt sich ohne Detailzeichnung nicht zu 100 % sagen. Violett = die mittlere Linie des Bündels.

Hier bist du im Grundriss:

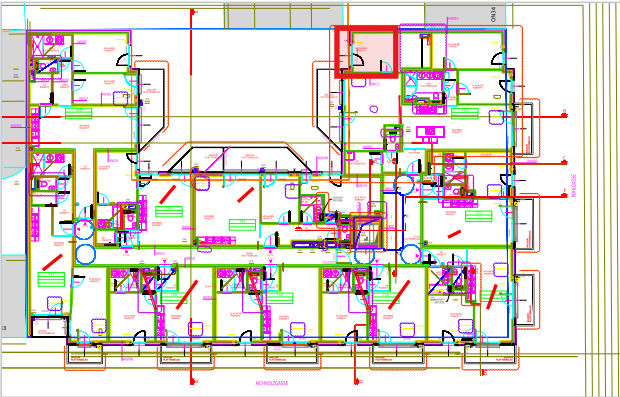

Begehbare Flächen - grün

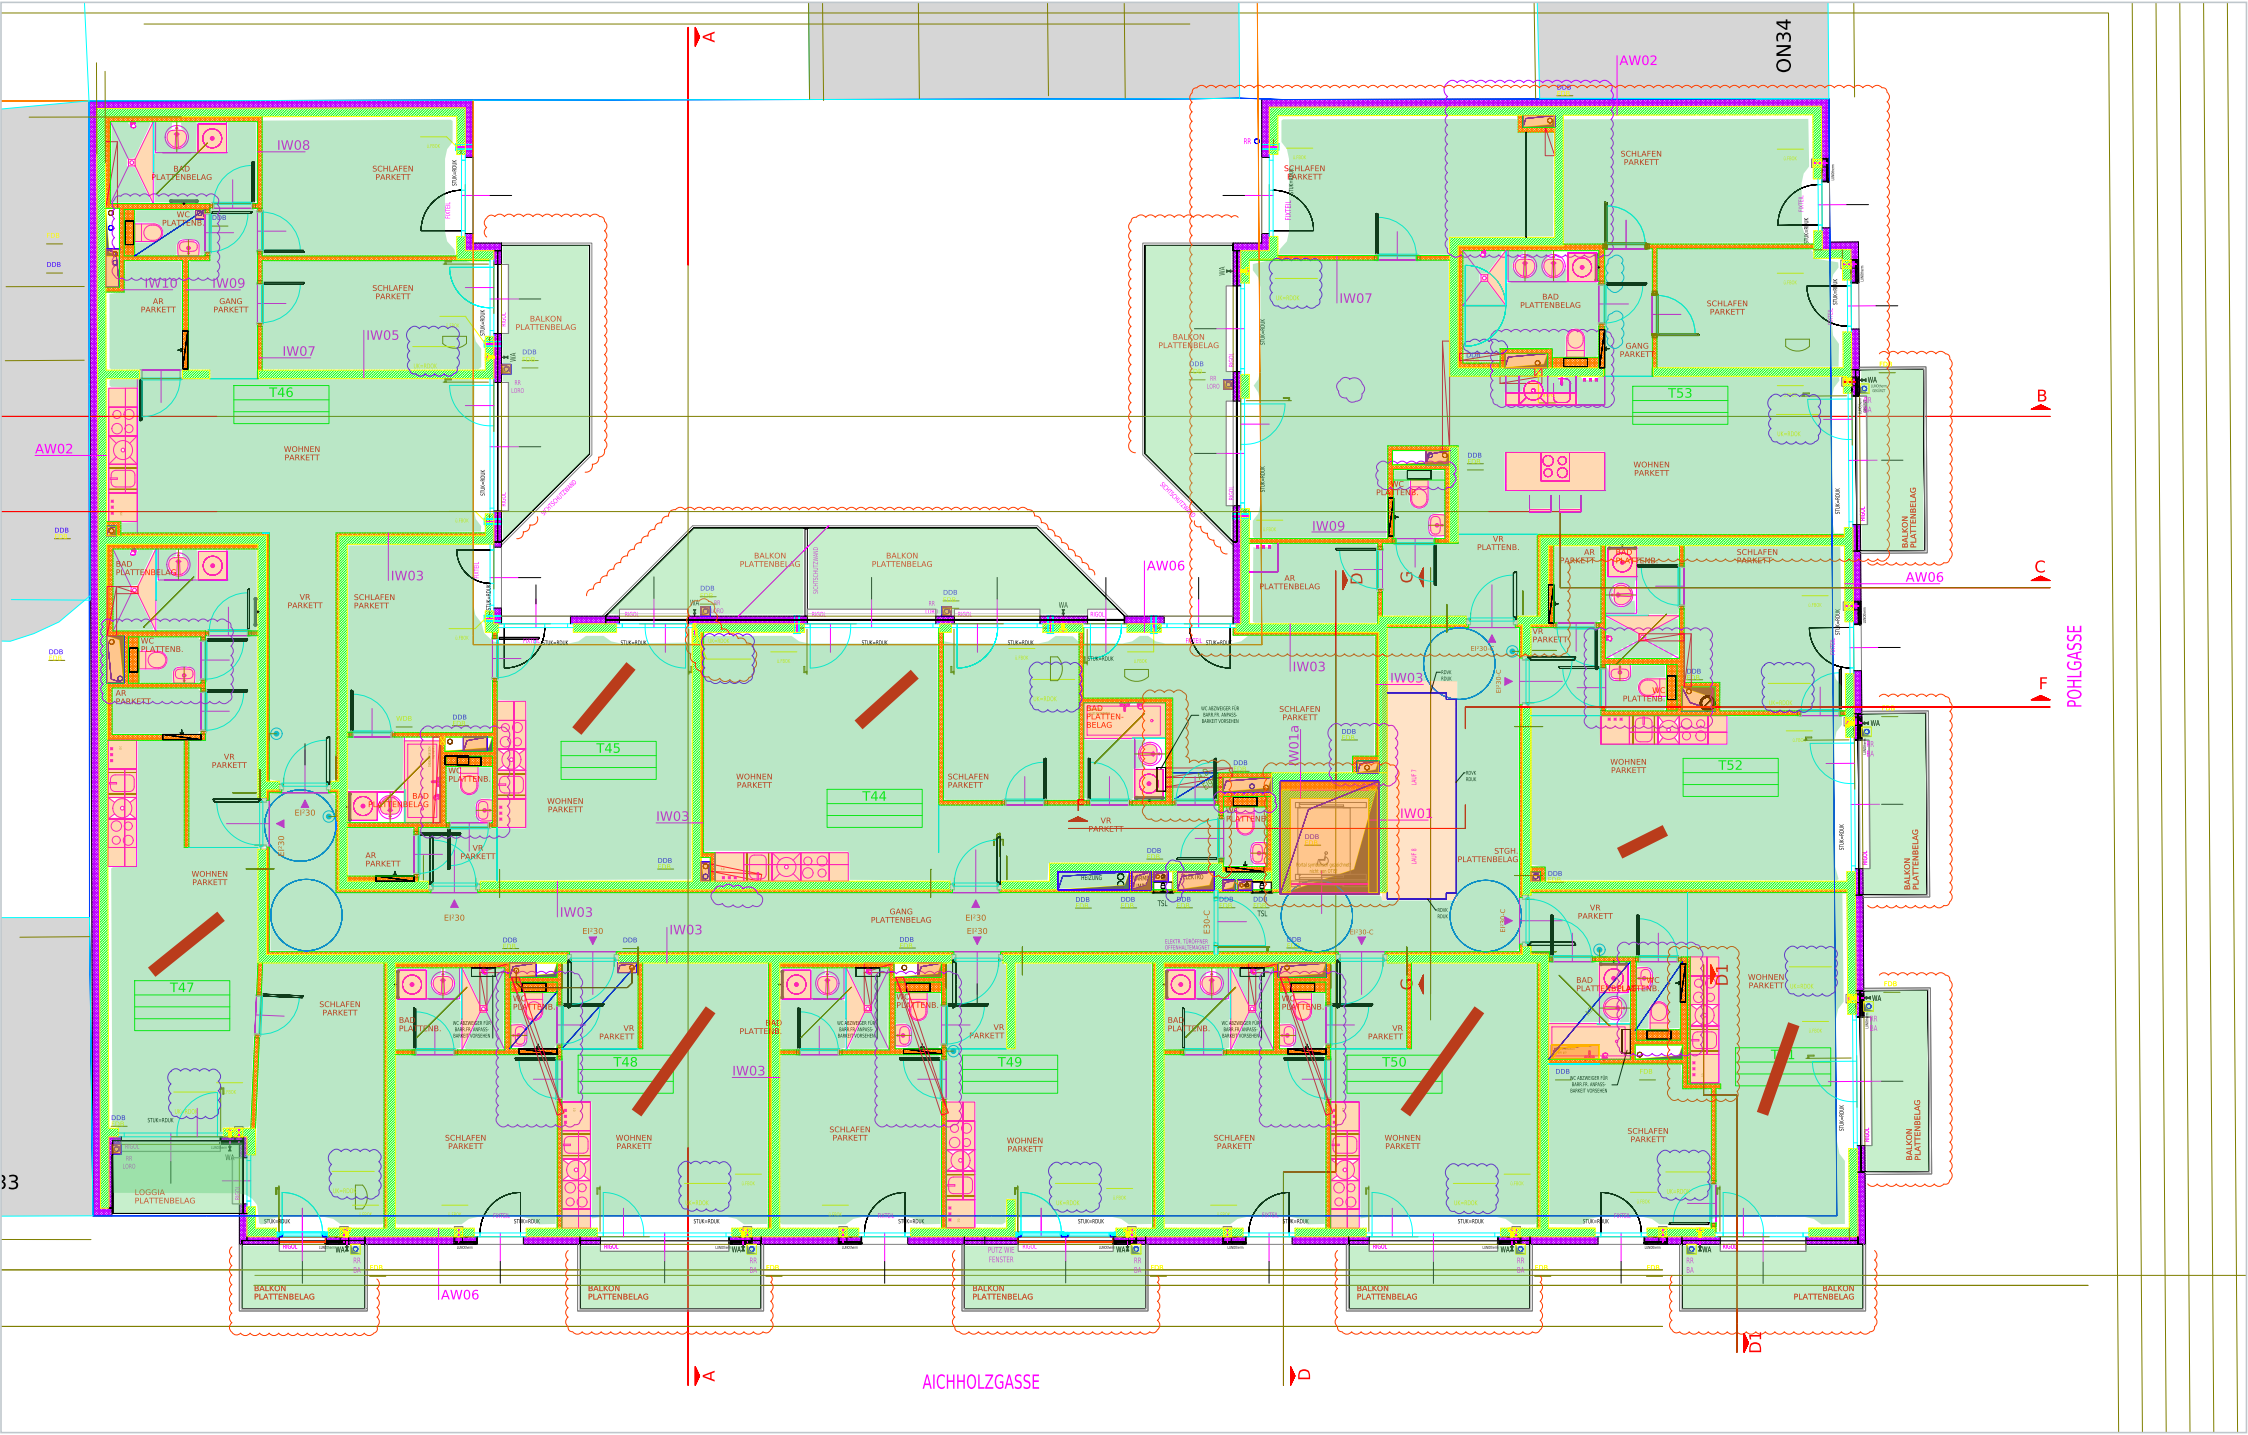

Die wichtigste Frage für Anfänger

Grün heißt: Hier kann ich stehen und gehen. Boden in Räumen, Gang und Vorräumen.
Hellgrün: Balkone und Loggia – Boden im Freien, nur über eine Tür erreichbar.

Was ist NICHT grün – und warum?

- Wände** (weiß ausgespart): festes Material.
- Orange:** Küchen, WC, Waschbecken, Duschen, Einbaukästen. Darunter ist Boden, aber etwas steht im Weg.
- Orange kräftig:** Aufzug und Leitungsschächte – dort ist **kein** Boden, sondern ein Schacht durch das ganze Haus.
- Orange blass:** die Öffnung, in der die Treppe liegt.
- Weiß im Hof:** kein Innenraum, auf diesem Stockwerk kein Boden.

Wie kommt man von Grün zu Grün?

Nur durch eine **Tür**. Das Grün läuft deshalb durch Türöffnungen durch, aber nie durch Wand oder Glas.
Grün ist eine Lernmarkierung. Sie sagt nicht, ob ein Weg rollstuhlgerecht oder ein zugelassener Fluchtweg ist.

Alles zusammen: Wände, Türen, Glas, Boden, Einbauten

Jetzt kannst du den ganzen Plan lesen


Alle Farben liegen gleichzeitig über dem Original. Verfolge deinen Weg mit dem Finger:

- 1. Start im **Stiegenhaus** rechts von der Mitte.
- 2. Auf dem **grünen Gang** nach links.
- 3. Eine **blaue Tür** in der dicken roten Wand = Wohnungseingang.
- 4. Durch den **Vorraum** in die Zimmer.
- 5. Im Wohnzimmer eine **Glasfront** mit Tür zum hellgrünen **Balkon**.


Musst du dabei nie durch Rot, Violett oder Orange, hast du den Plan richtig gelesen.

Merksatz

Rot trennt. **Blau** verbindet. **Grün** trägt dich. **Violett** lässt Licht durch, aber keine Menschen. **Orange** steht im Weg.

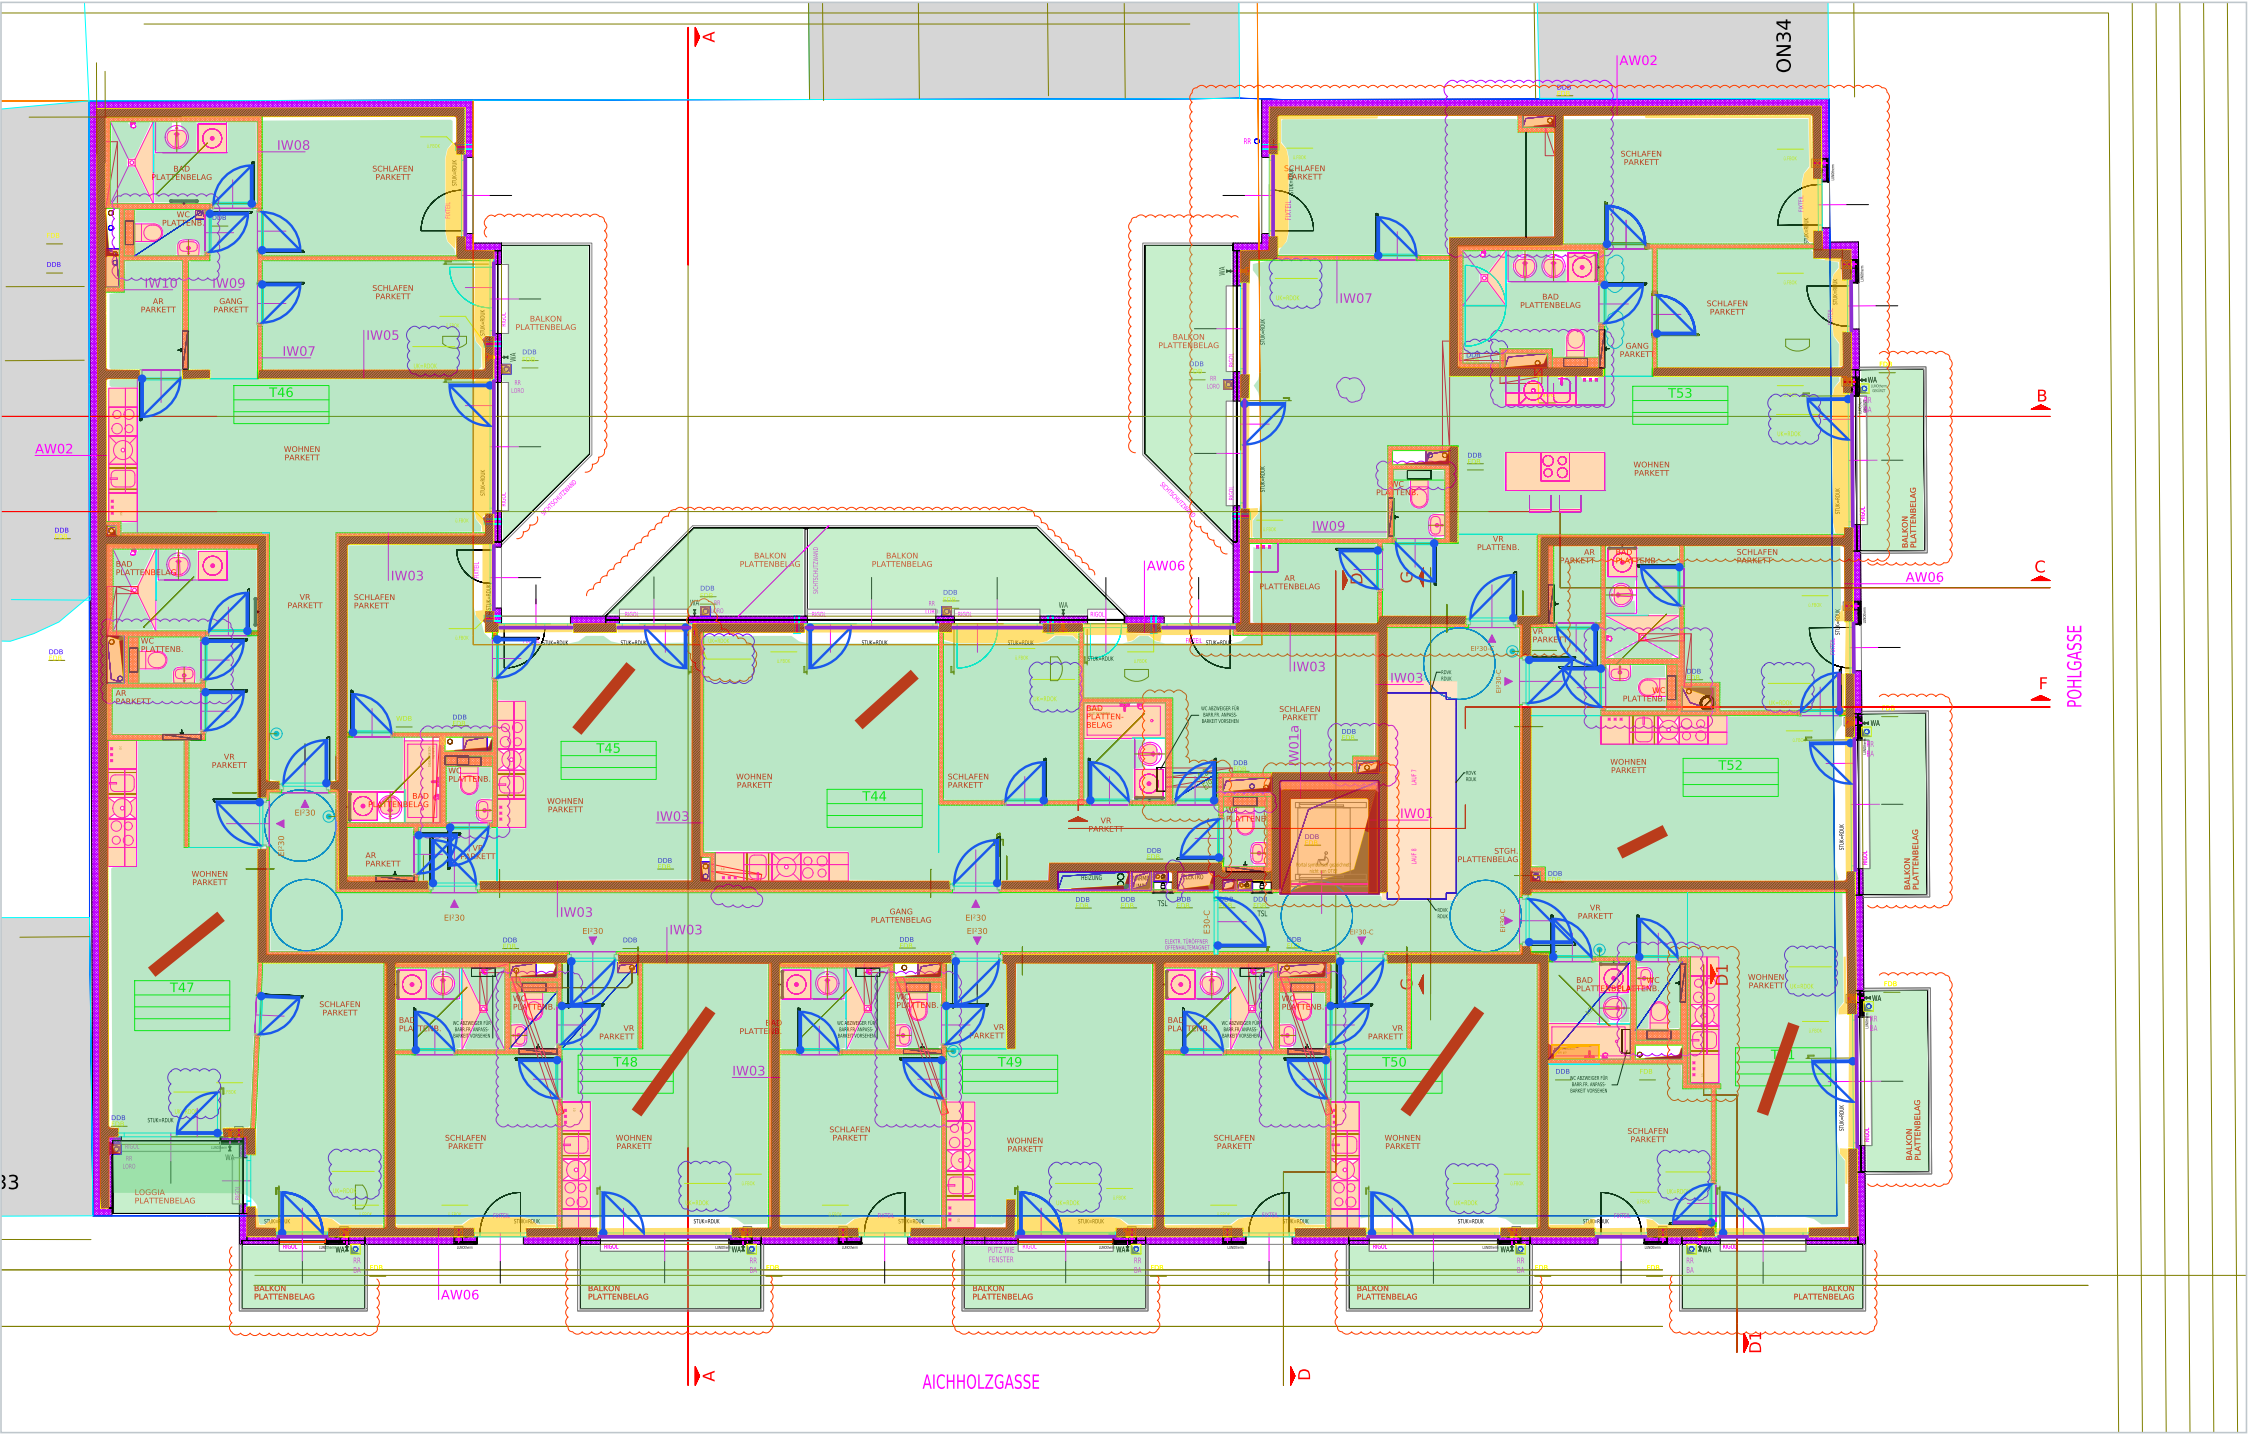

Ein Weg durch die Wohnung T48 - Schritt für Schritt

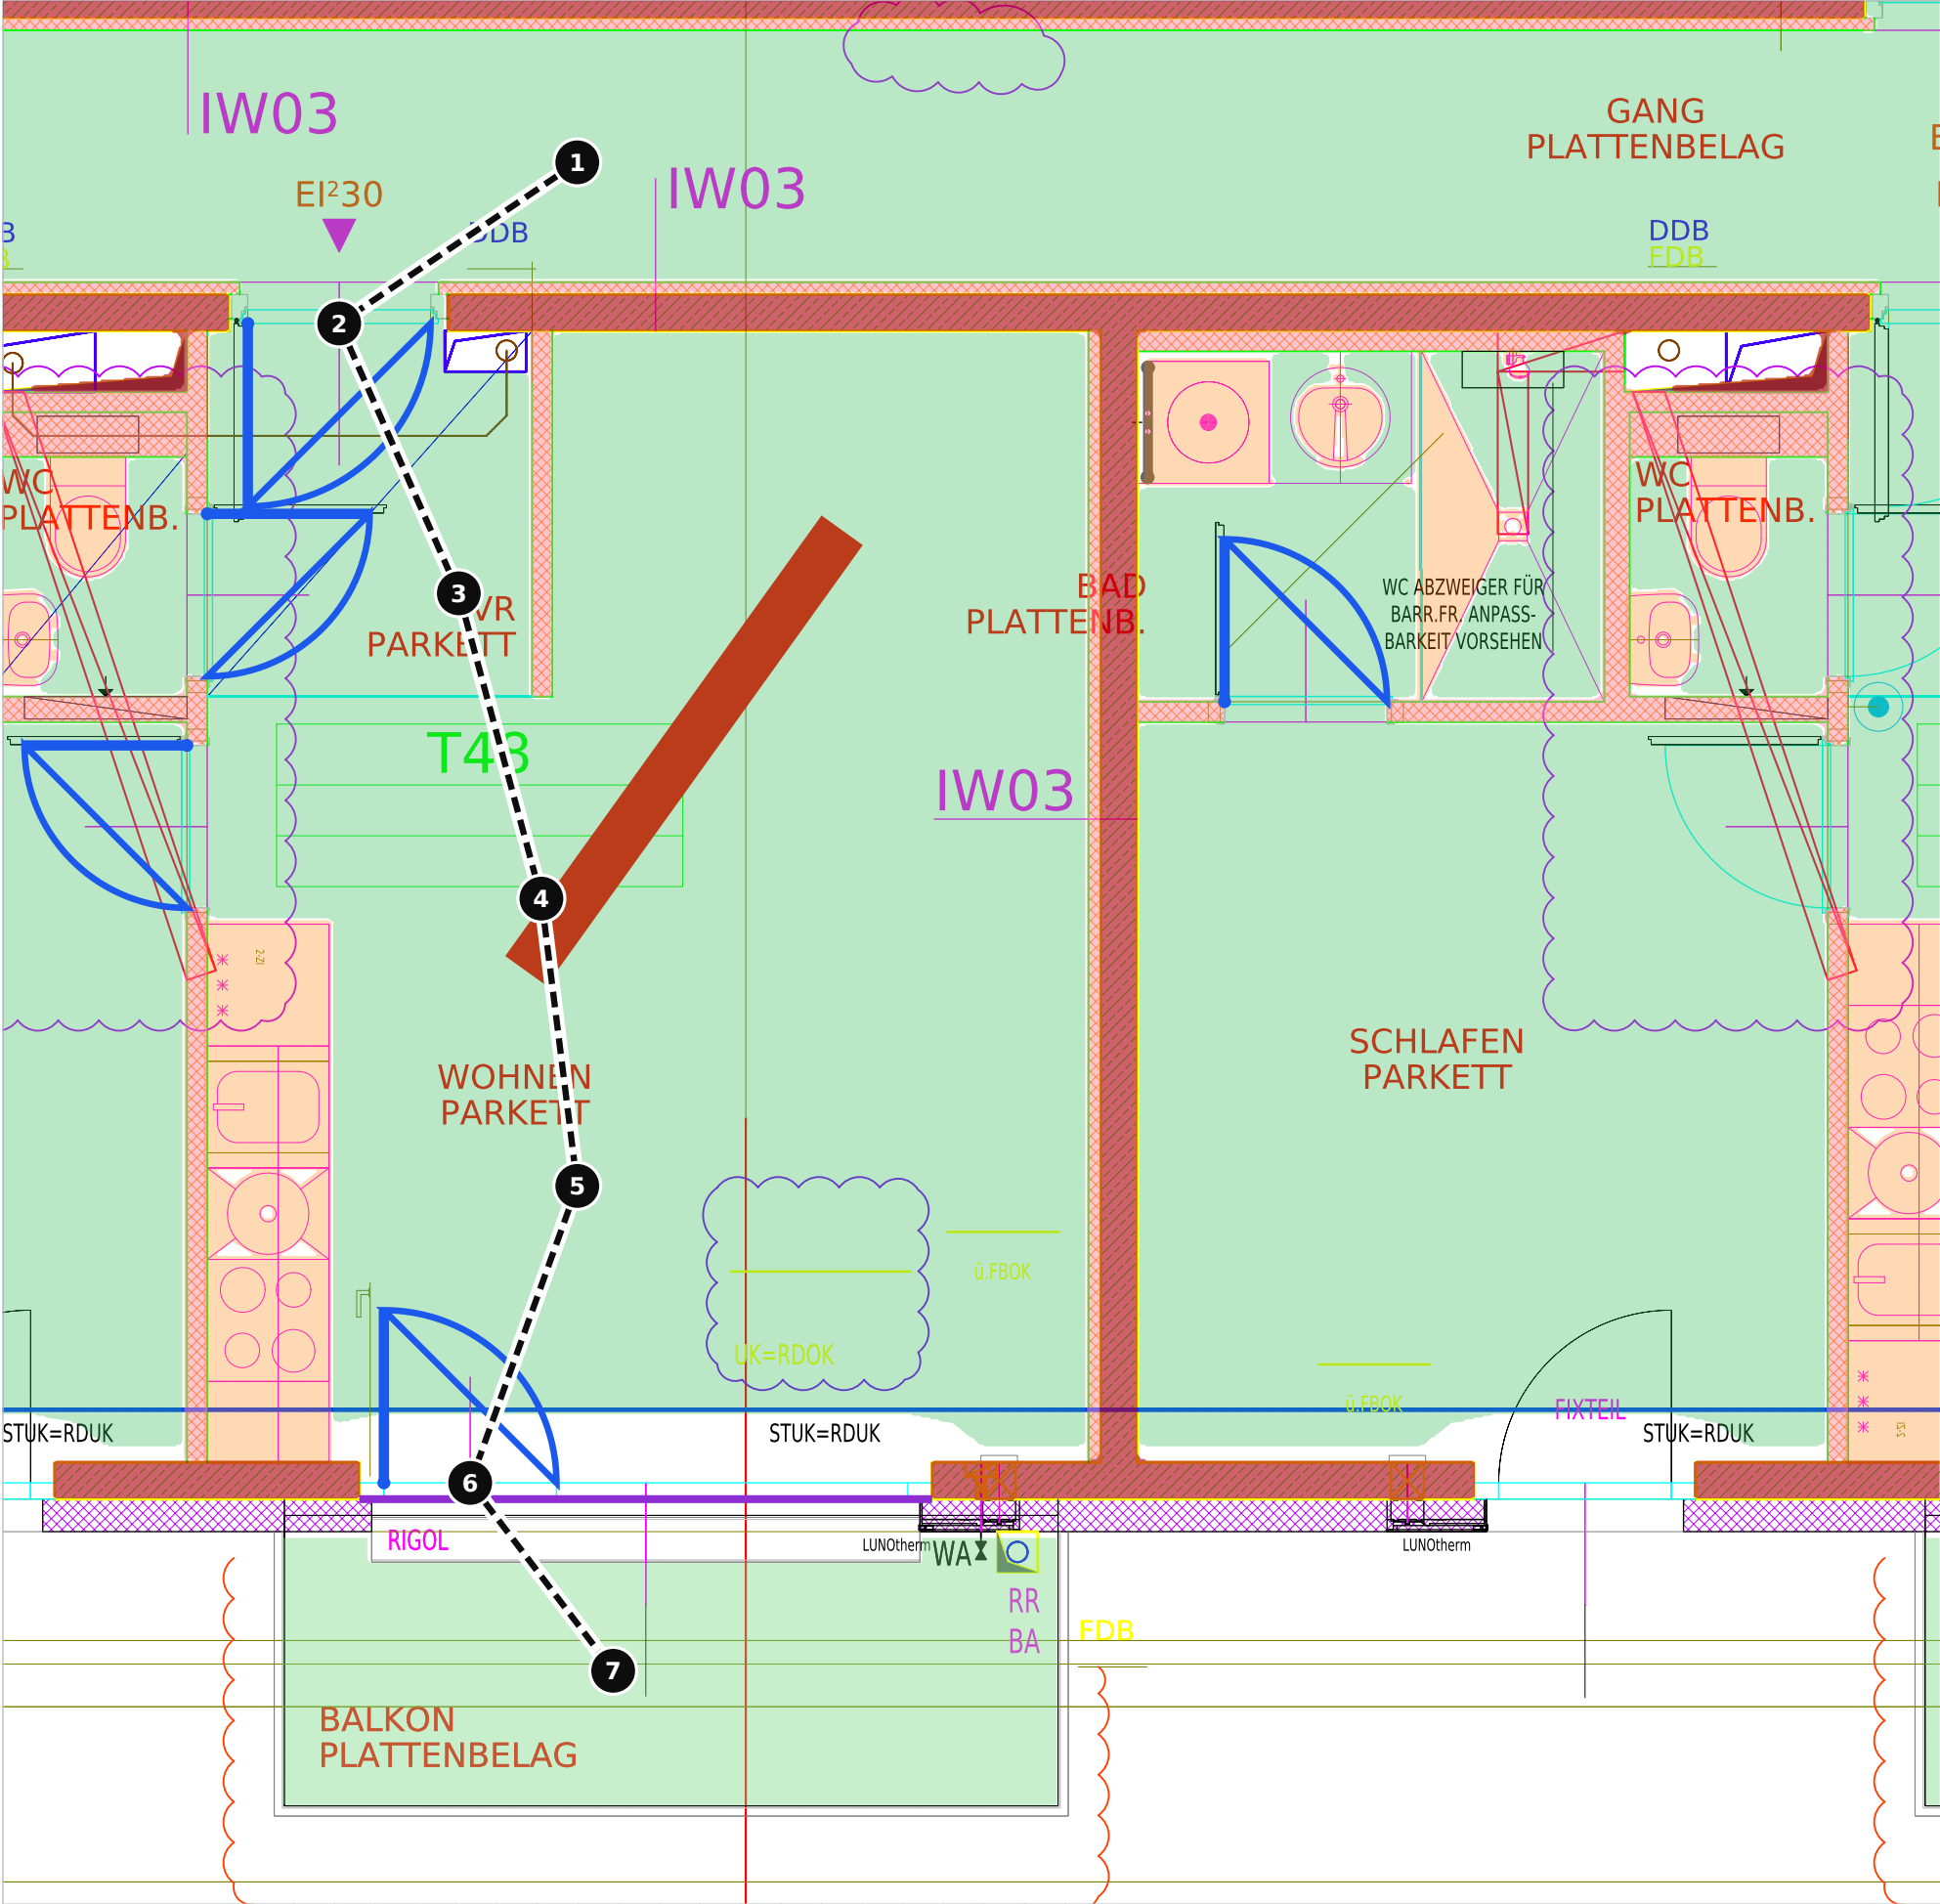


So „gehst“ du durch einen Plan


Die schwarzen Nummern zeigen einen möglichen Weg vom Gang bis auf den Balkon. Jeder Schritt bleibt auf Grün oder geht durch eine blaue Tür.

- 1 – Du stehst im **Gang** (grün): Hier darf jeder Bewohner gehen.
- 2 – Eine Lücke in der dicken roten Wand mit Türblatt und Bogen: die Eingangstür von T48.
- 3 – Du bist im **Vorraum (VR)**. Von hier gehen Türen zu Bad, WC und Zimmern ab.
- 4–5 – Du folgst dem Grün ins **Wohnzimmer**. Die orange Fläche an der linken Wand ist die Küche – um sie herum.
- 6 – Unten die Glasfront: Nur wo der blaue Bogen ist, geht eine Tür auf.
- 7 – Du stehst auf dem **Balkon**. Weiter geht es nicht: Der Balkon ist eine **Sackgasse** – zurück nur durch dieselbe Tür.

Lernbeispiel zum Planlesen, kein geprüfter Rettungs- oder Fluchtweg.

Hier bist du im Grundriss:

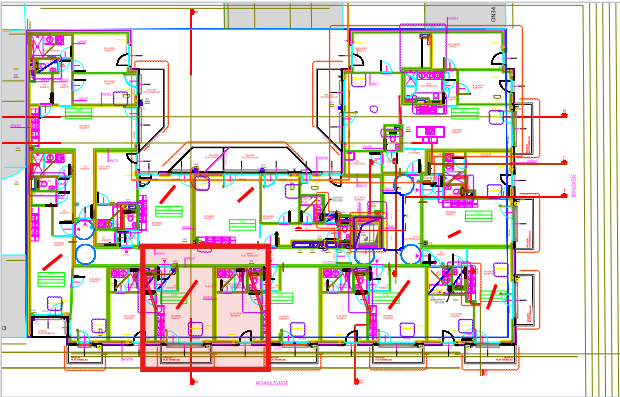

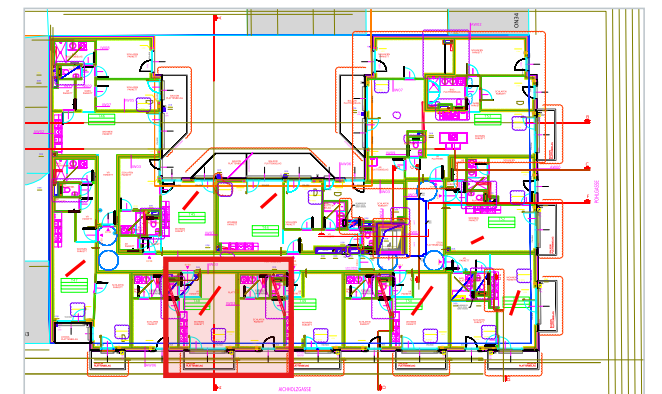

Welche Wohnung beginnt wo? Eingänge vom Gang

Wie finde ich die Grenzen einer Wohnung?

Eine Wohnung ist eine Gruppe von Räumen, die **nur über eine einzige Tür** mit dem Gang verbunden ist: die **Wohnungseingangstür**.

Die blau eingekreisten Türen liegen in den Wänden des Gangs – jede ist ein Eingang.


So gehst du vor

- 1. Such den grünen Gang.
- 2. Folge ihm und finde die Türen in seinen Wänden.
- 3. Geh gedanklich durch eine Tür und sammle alle Räume, die du erreichst, **ohne** wieder in den Gang zu gehen.
- 4. Das Ergebnis ist eine Wohnung. Ihre Nummer (T...) steht irgendwo darin.


Die dicken Wände helfen

Zwischen zwei Wohnungen liegt immer eine **dicke** Wand ohne Tür. Dünne Wände liegen nur innerhalb einer Wohnung.

Hervorgehoben sind Türen in einem Streifen entlang des Hauptgangs. Einige Wohnungen an den Flügeln haben ihren Eingang an kurzen Seitengängen und sind hier nicht alle eingekreist.

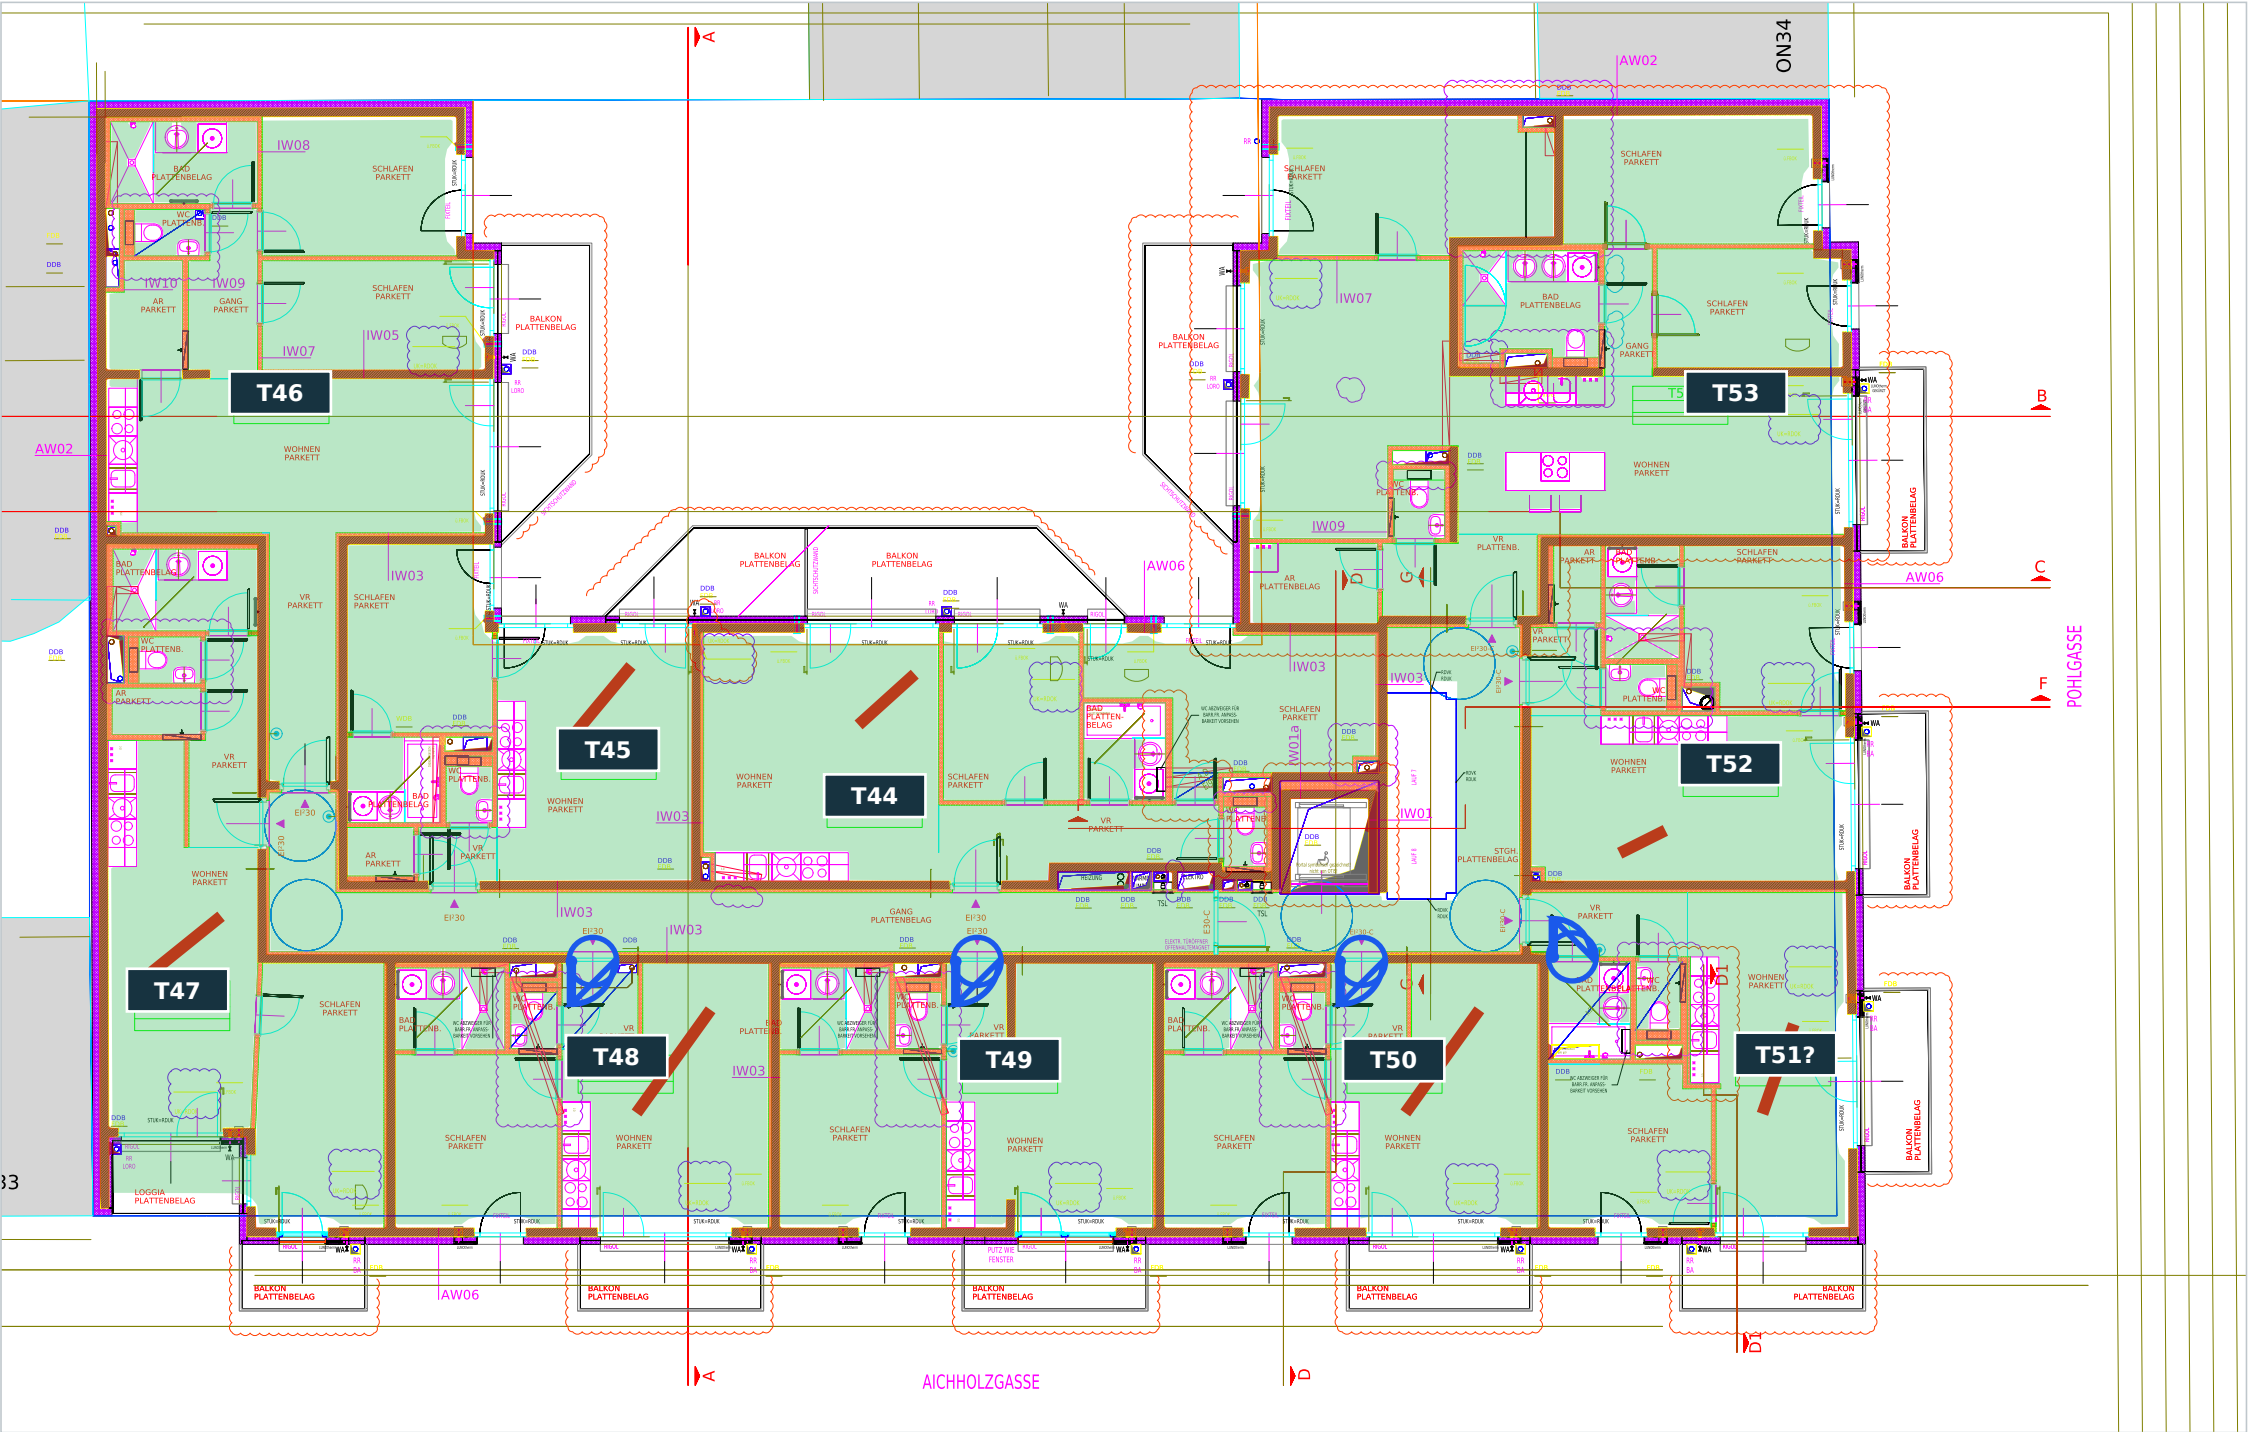

Bad und WC: Was dünn gezeichnet ist, steht am Boden

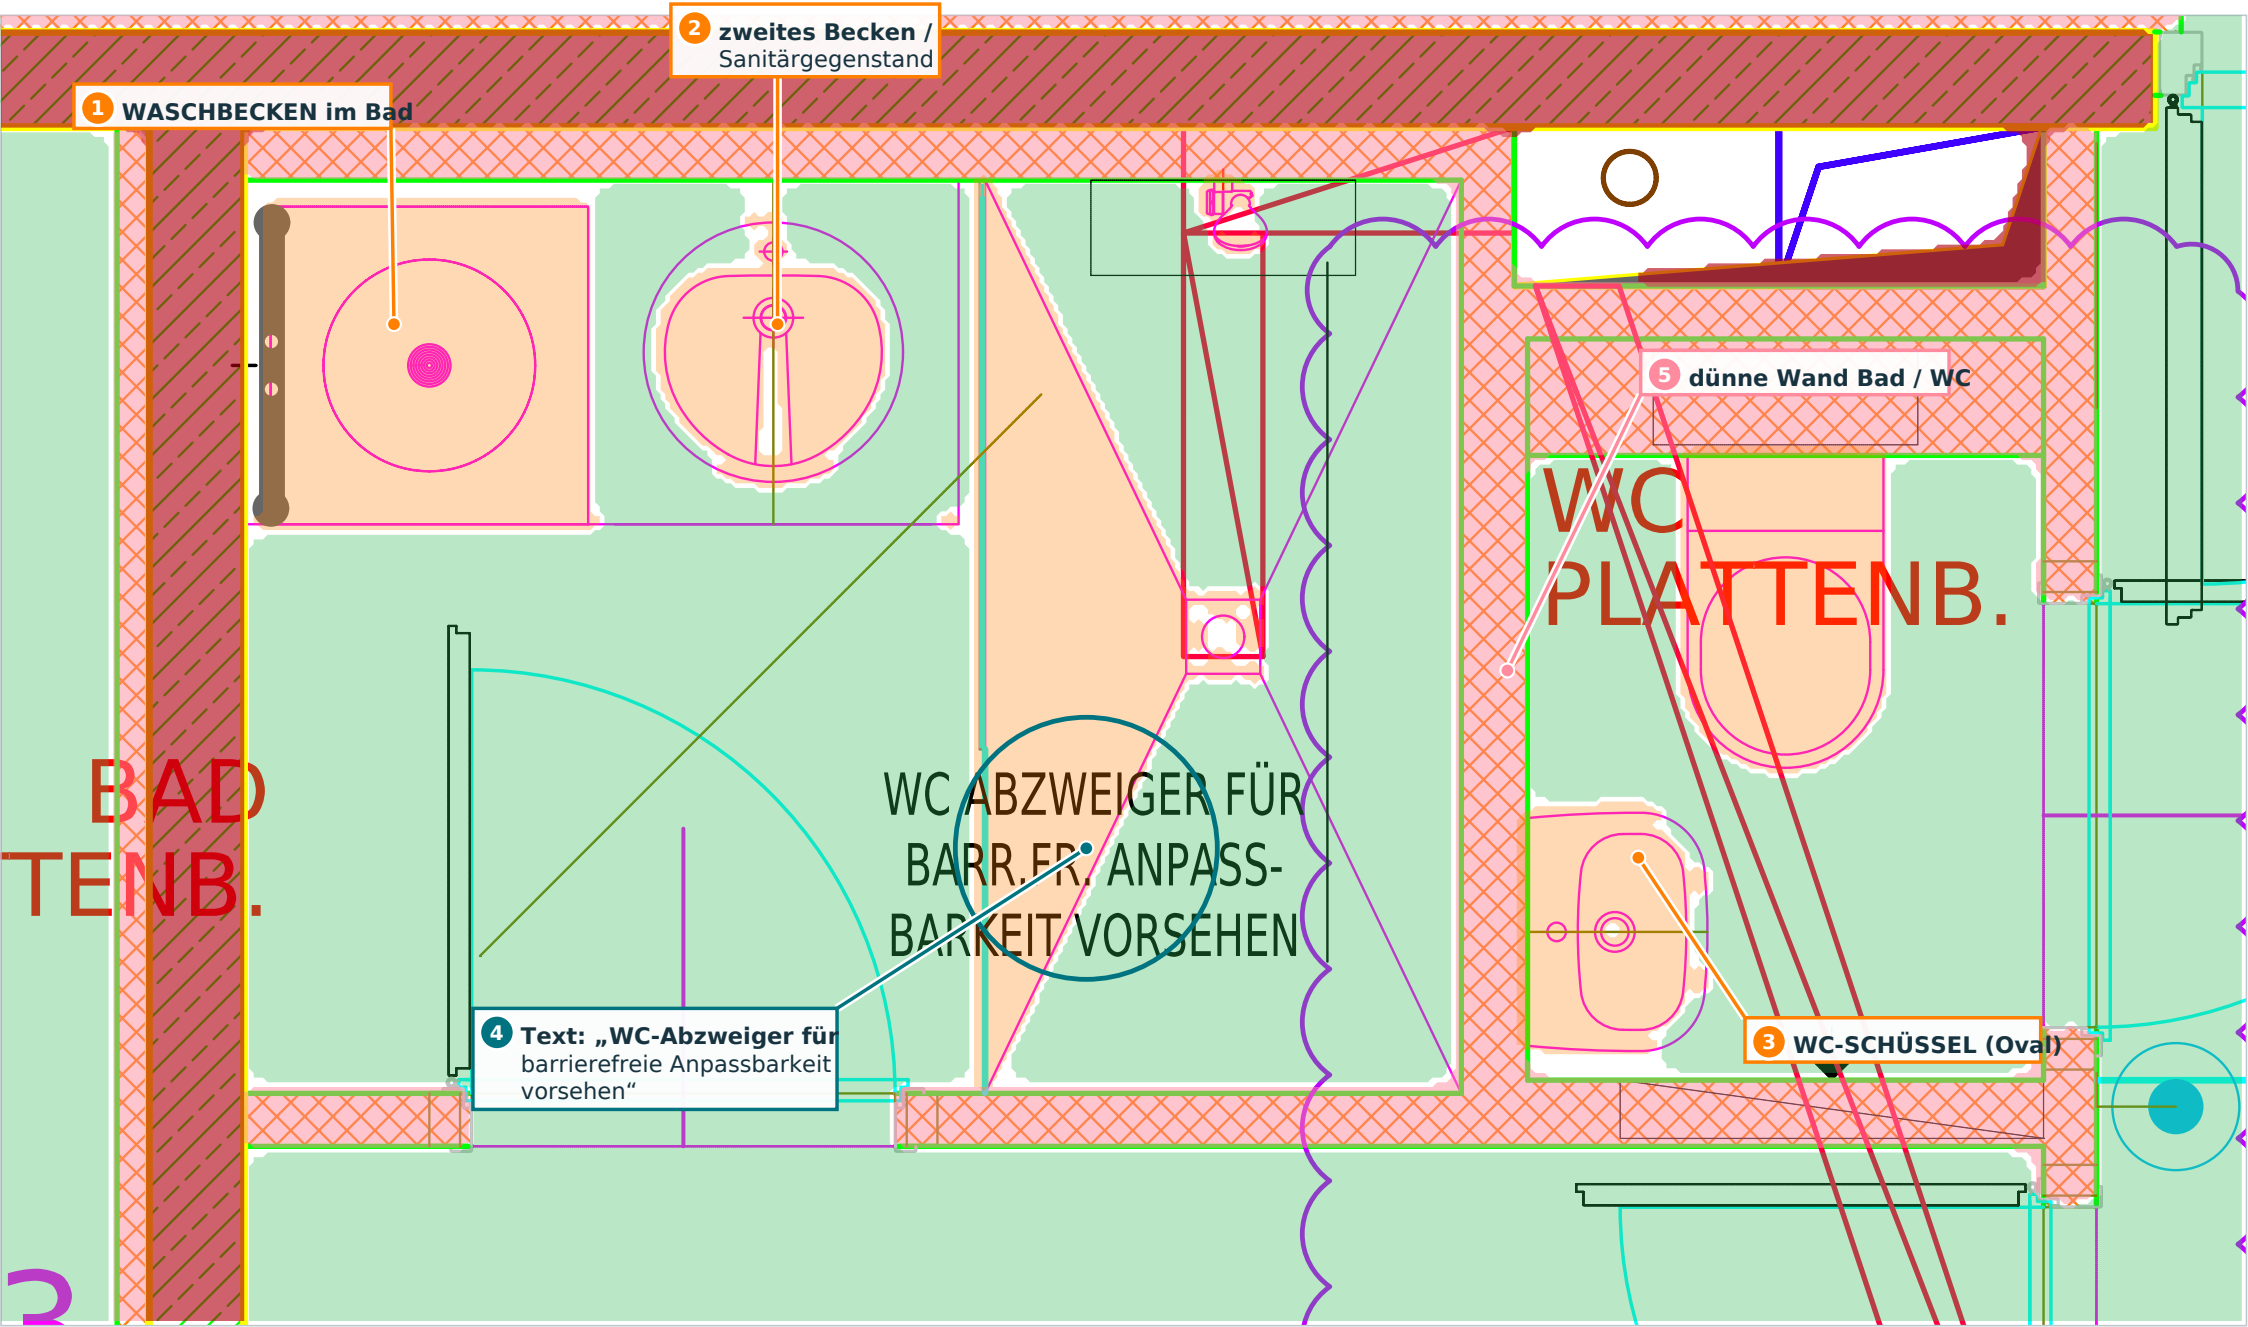

Was sind Einbauten?
Dinge, die fest im Raum stehen: WC, Waschbecken, Dusche, Wanne, Küchenzeile, eingebaute Kästen. Sie sind **keine Wände** – aber sie stehen im Weg.


Wie sehen sie im Plan aus?
Mit **dünnen magenta Linien**, weil sie unterhalb der Schnitthöhe stehen – man sieht sie „von oben drauf“.

Oval in einem abgerundeten Rechteck = WC-Schüssel (3).
Kreis in einem Rechteck = Waschbecken (1).
Im Heft sind diese Flächen orange und nicht grün.


Der Text (4)
Ein Hinweis an die Baufirma: Es soll ein Anschluss vorbereitet werden, damit das Bad später **barrierefrei** umgebaut werden kann. Das ist eine Bauanweisung, kein Gegenstand.

Bei sehr kleinen Symbolen ist nicht jedes Teil sicher bestimmbar. Benannt wird nur, was die Form eindeutig zeigt.

Hier bist du im Grundriss:

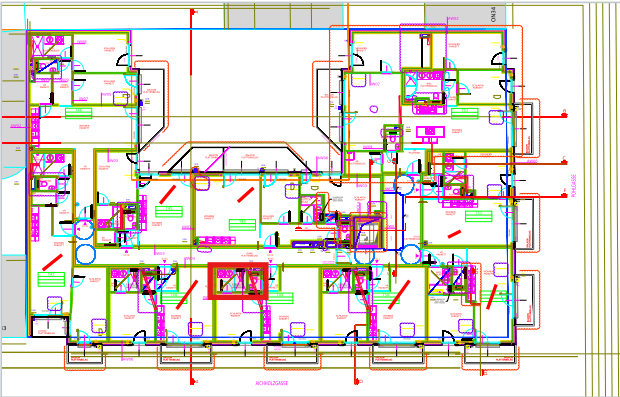

Die Küchenzeile im Wohnzimmer

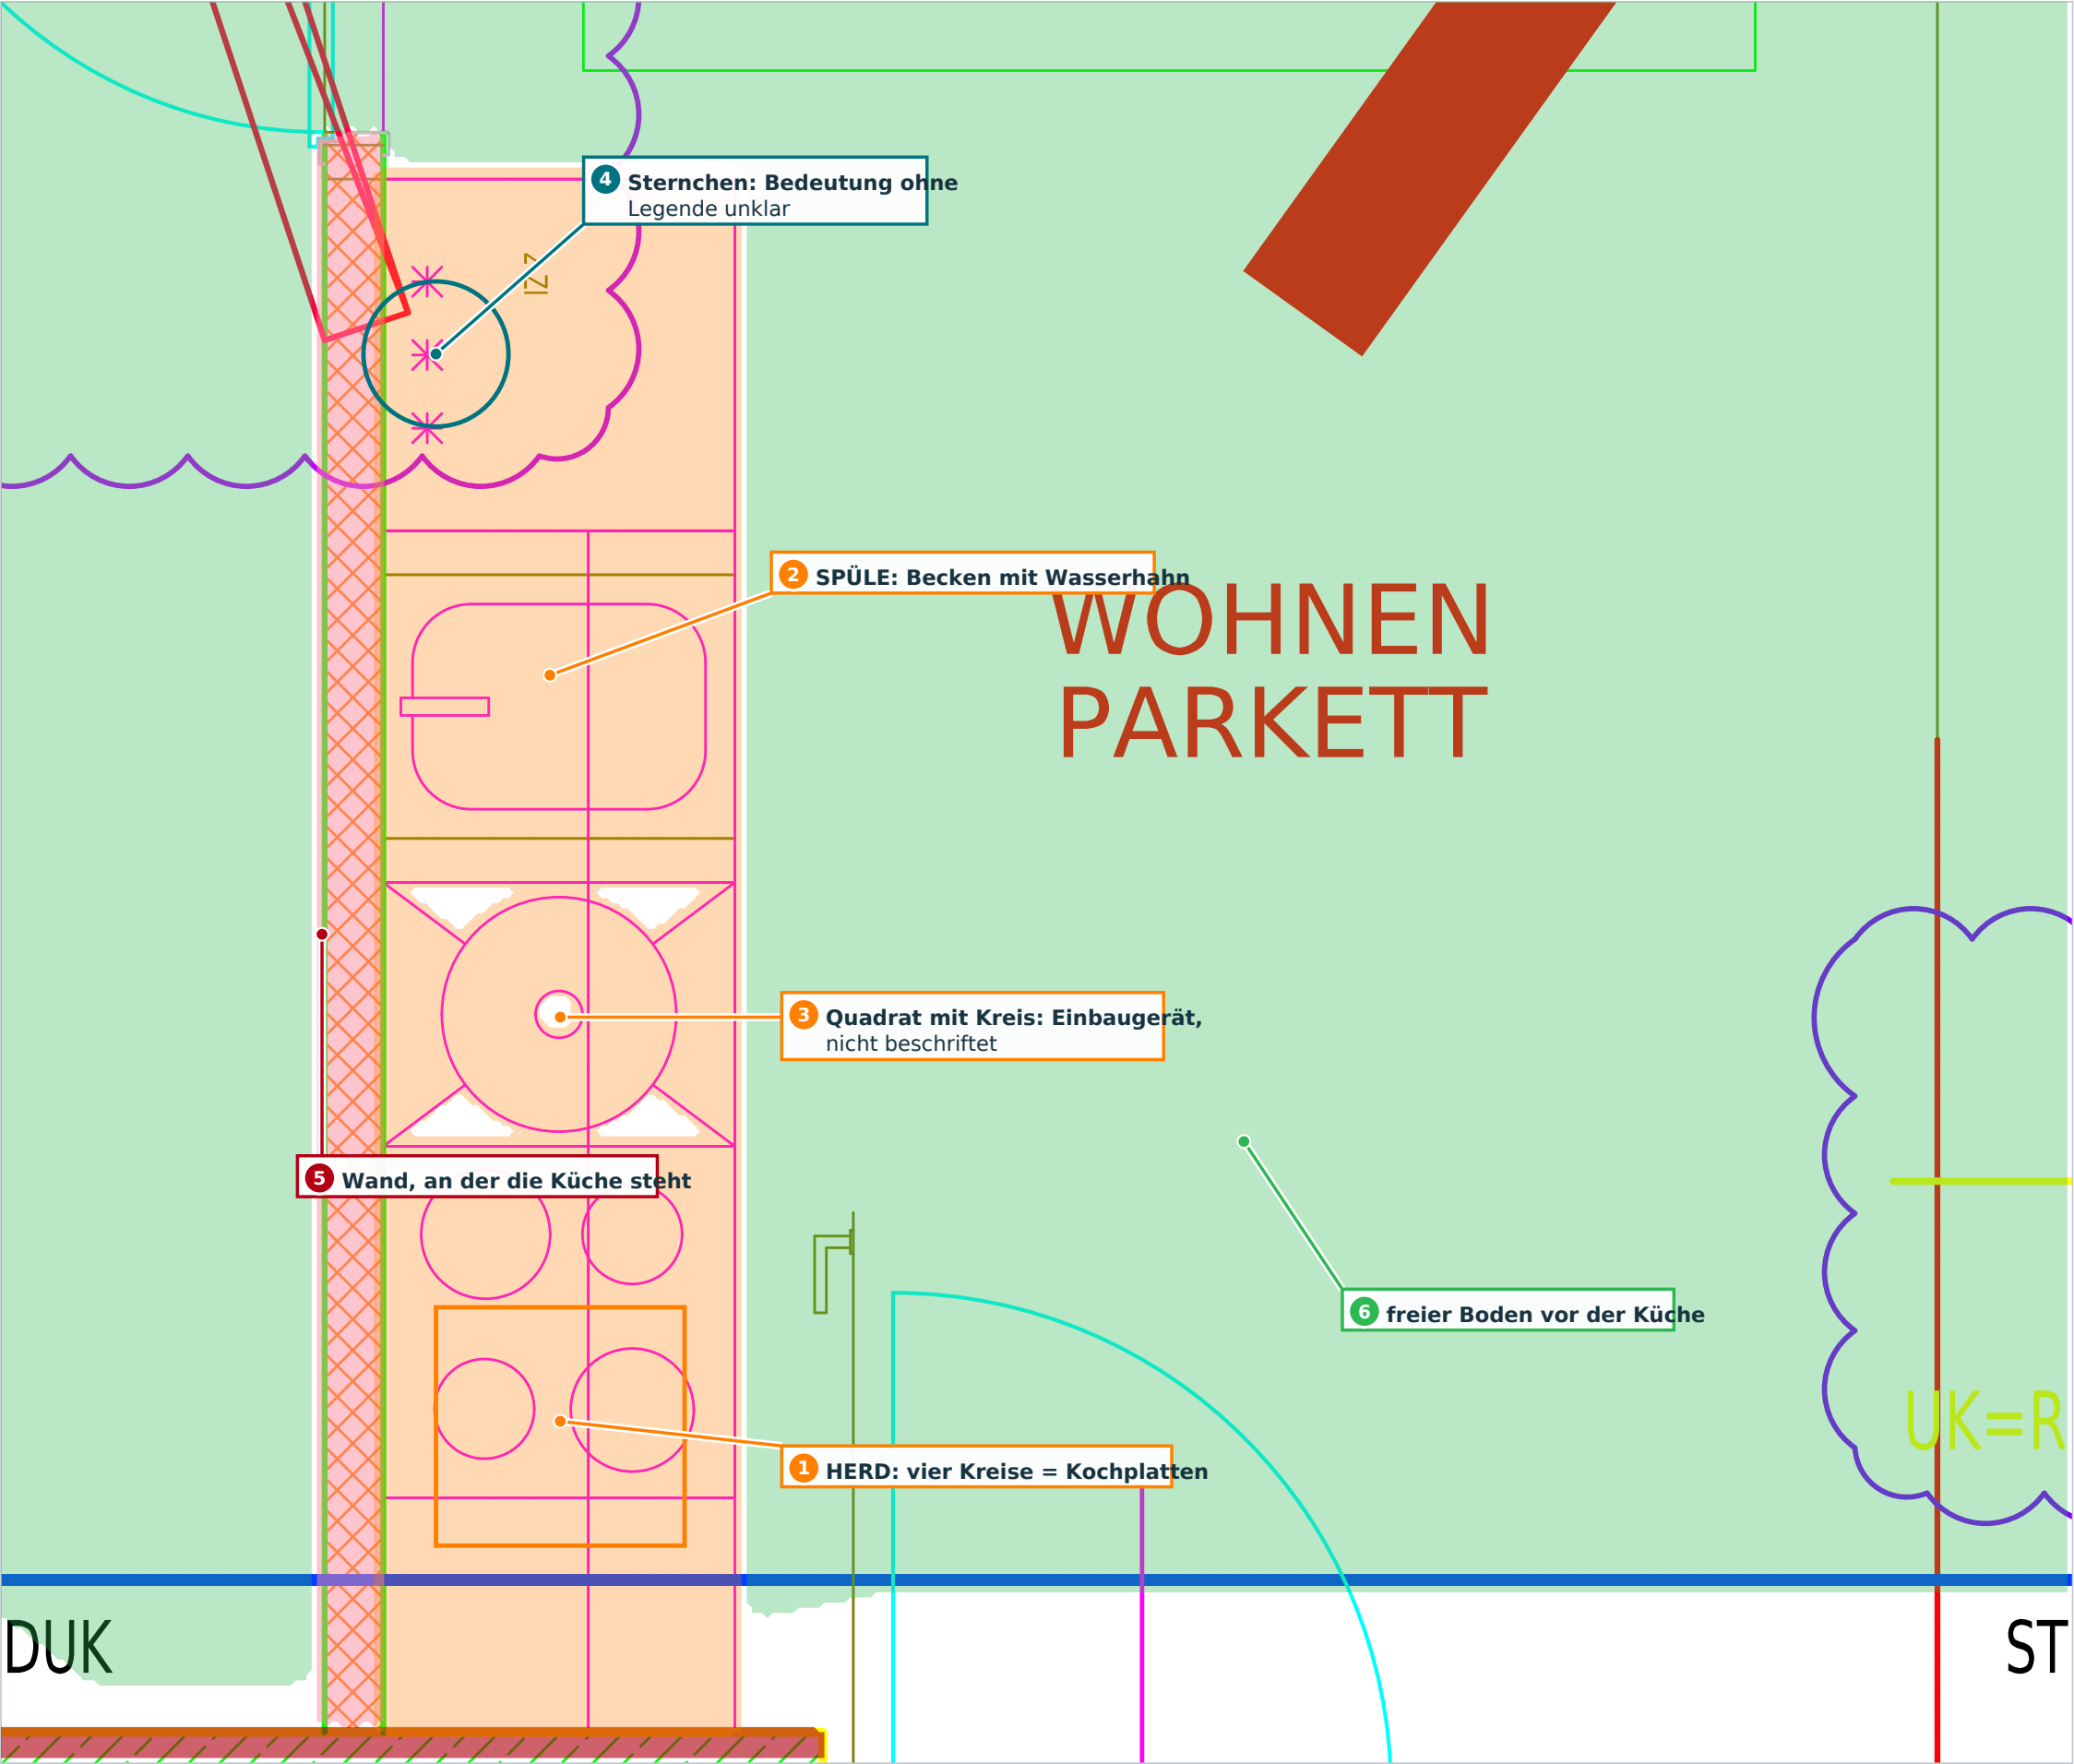

Was ist das?

Eine **Küchenzeile**: Küchenschränke in einer Reihe an der Wand, mit Spüle und Herd. Sie gehört zum Raum WOHNEN.

Woran erkenne ich sie?


Ein langer, schmaler Streifen direkt an der Wand, in Rechtecke unterteilt (die Schränke). **Vier Kreise** = Kochplatten (1). Ein abgerundetes Becken mit kleinem Balken (Hahn) = Spüle (2). Das Quadrat mit Kreis (3) ist ein Einbaugerät; welches, steht nicht dabei.

Was bedeutet das für das Gehen?


Die Küche ist ein **Hindernis** (orange). Man steht **davor** auf dem Boden (6). Sie teilt den Raum aber nicht – das Wohnzimmer bleibt ein Raum.

Die Einteilung der Schränke ist nur angedeutet; es ist ein Einrichtungsvorschlag.

Hier bist du im Grundriss:

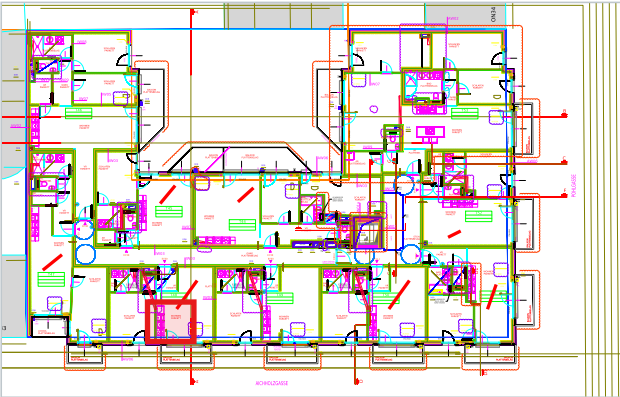

Der Kern des Hauses: Treppe, Aufzug und Schächte

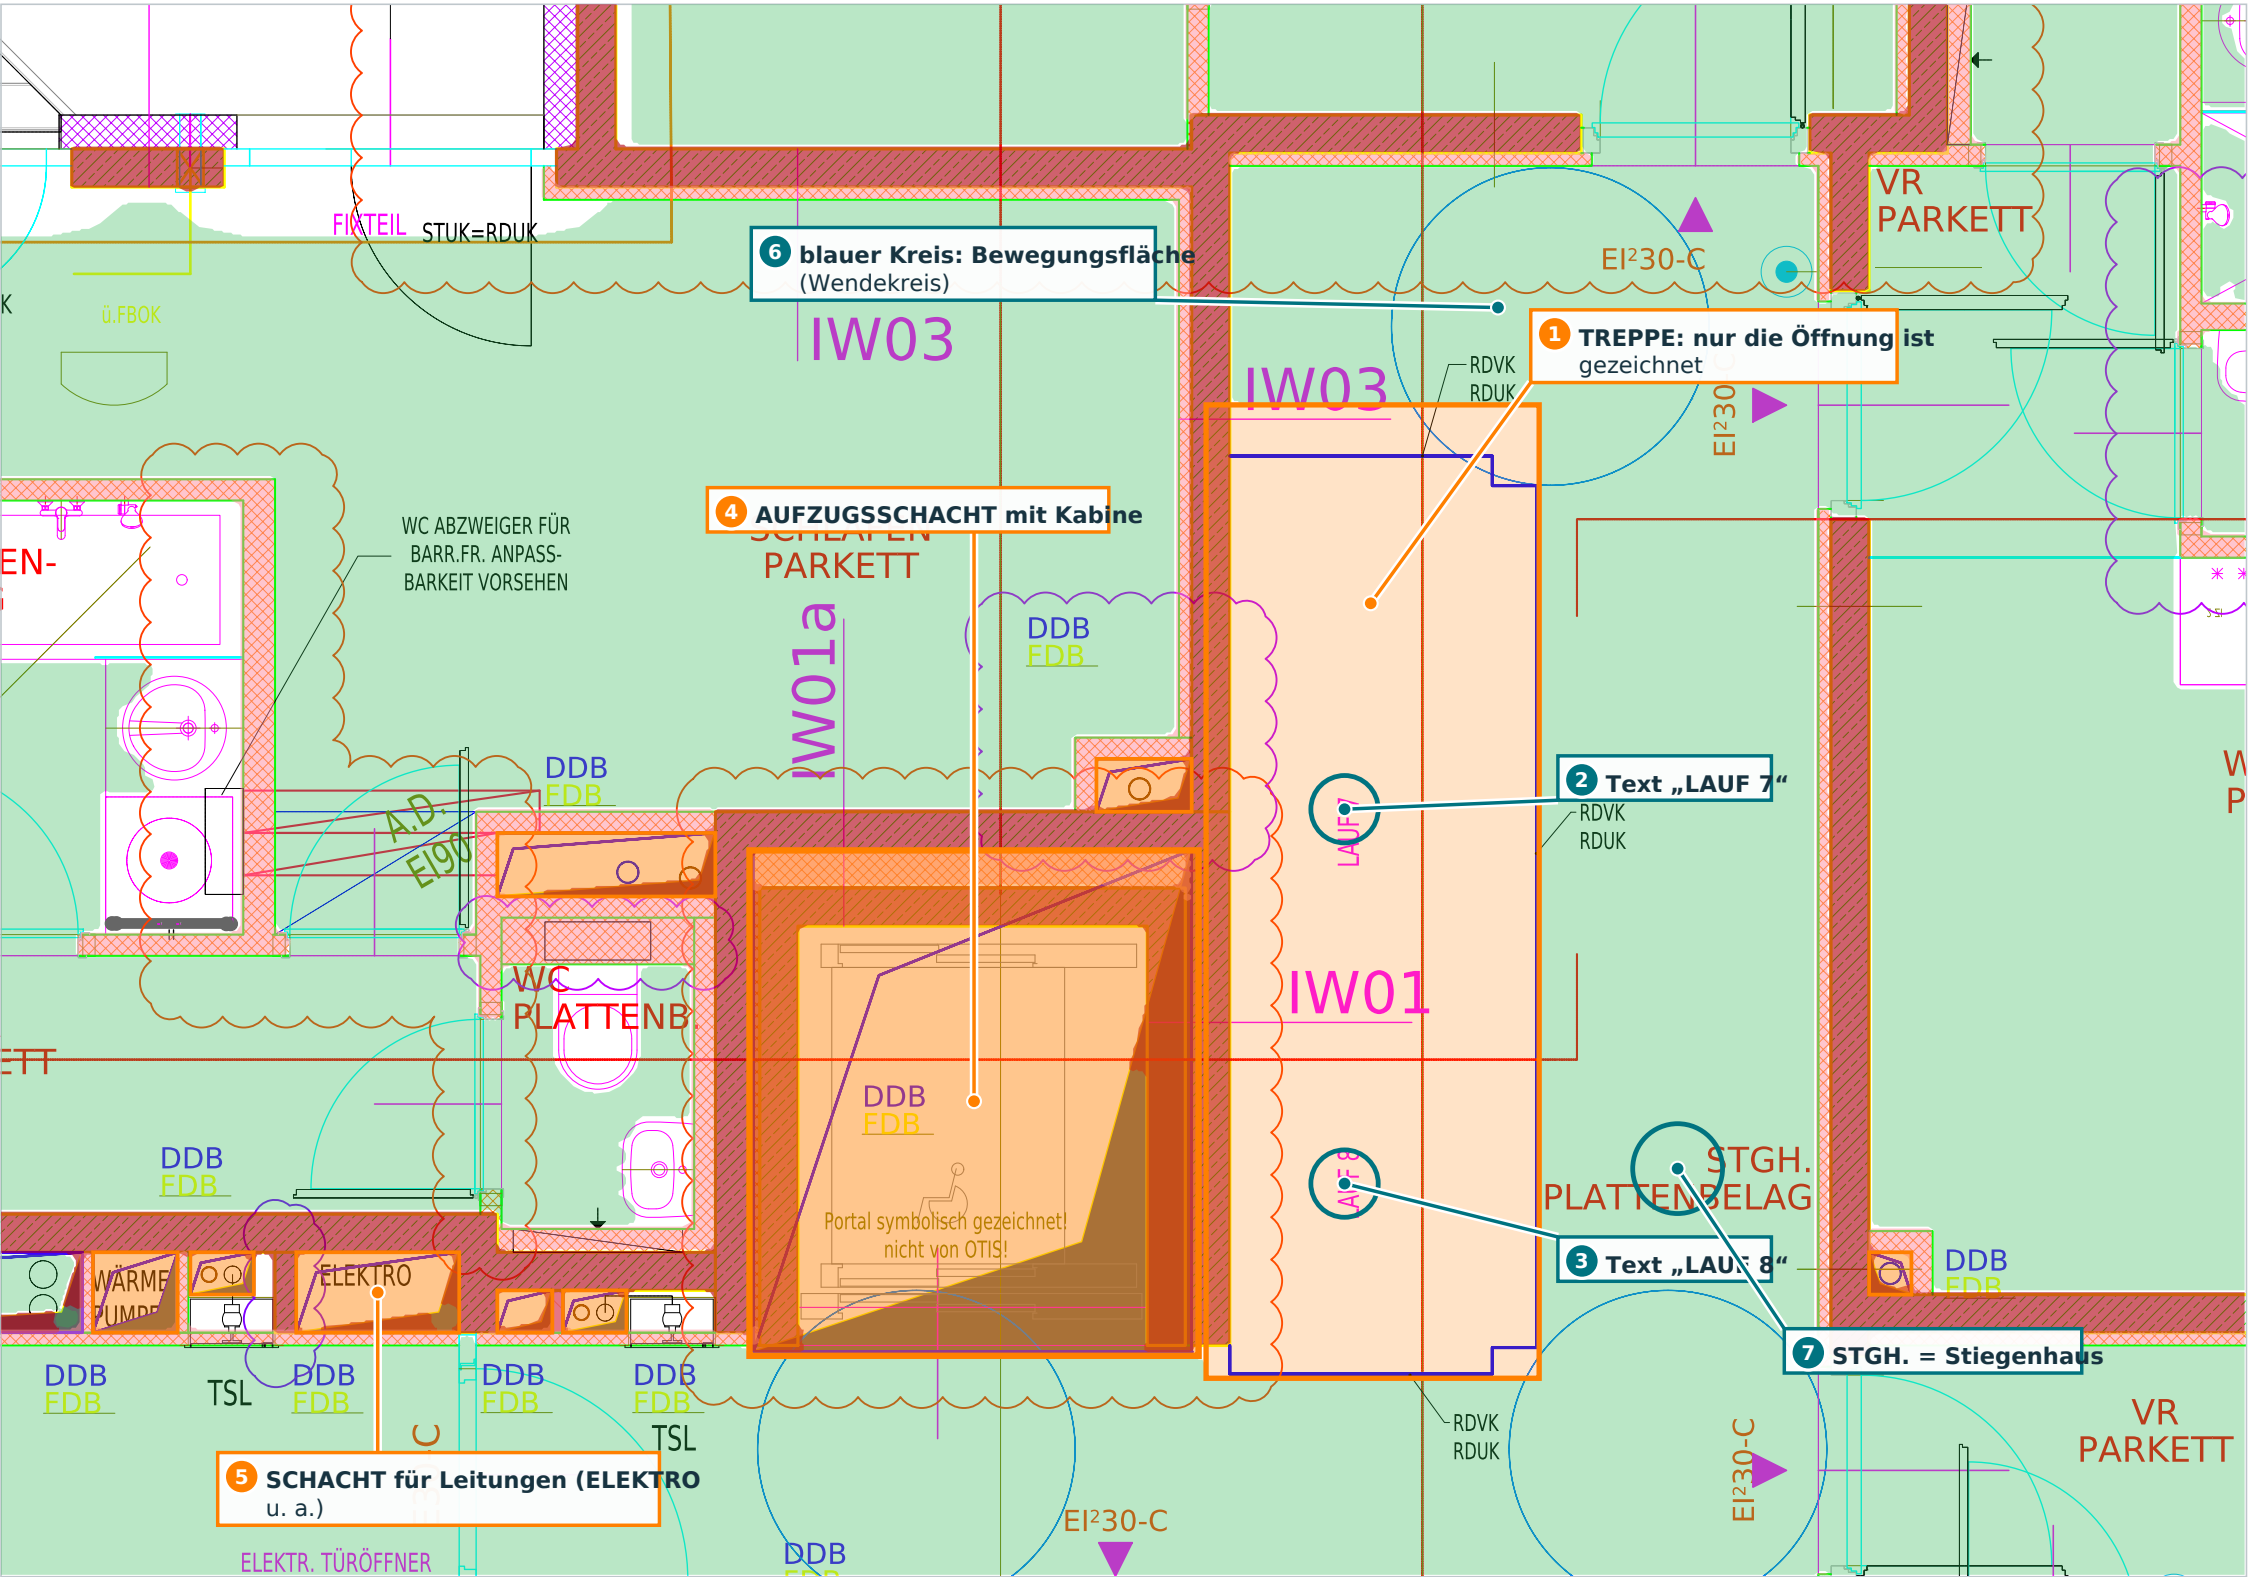

Treppe (1–3)

Was: Stufen in ein anderes Stockwerk. **Normalerweise** zeigt ein Grundriss viele parallele Querlinien – jede eine Stufenkante.

Besonderheit hier: Es sind **keine Stufen gezeichnet**. Man sieht nur die **blaue Umrisslinie** der Deckenöffnung, in der die Treppe liegt, und die Texte **LAUF 7** und **LAUF 8**. Ein „Lauf“ ist ein Treppenstück ohne Unterbrechung. Im 3. OG standen an derselben Stelle LAUF 6 und 7 – die Nummern zählen also nach oben weiter.

Aufzug (4)


Fast quadratischer Schacht mit dicken Wänden, darin ein Rechteck (Kabine) und ein Rollstuhlsymbol. Eine Notiz sagt, dass das Tor nur symbolisch gezeichnet ist.

Schächte (5)

Kleine Kästchen mit Schräglinie und Texten wie WÄRMEPUMPE oder ELEKTRO: senkrechte Kanäle für Leitungen durch alle Stockwerke. **Kein Boden.**

Wohin die Treppe genau führt und wie die Stufen liegen, zeigt dieser Plan nicht.

Hier bist du im Grundriss:

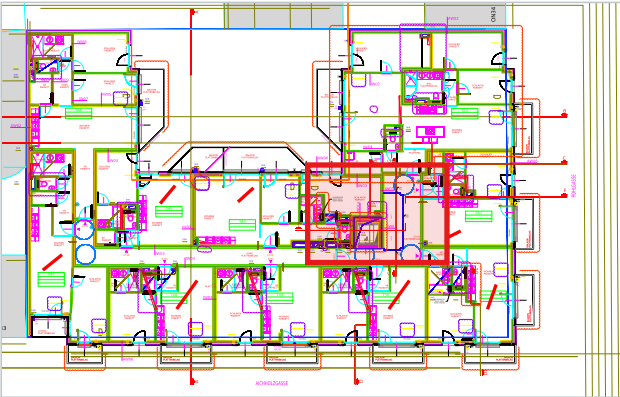

Der Gang: die „Straße“ im Inneren des Hauses

Was ist ein Gang?

Ein langer, schmaler Raum, der **andere Räume verbindet** – ein Flur oder eine Verkehrsfläche. Man hält sich dort nicht auf, man geht durch.

Woran erkenne ich ihn?


Ein langes grünes Band zwischen **dicken** roten Wänden. In der Mitte steht **GANG PLATTENBELAG** (1).

In den Wänden sind in Abständen **Türen** – die Wohnungseingänge. Daneben steht jeweils **EI²30**.


Warum dicke Wände?

Sie trennen den gemeinsamen Gang von privaten Wohnungen. Solche Wände müssen stabil, schall- und brandschützend sein. (Die genauen Anforderungen stehen nicht im Plan.)


Ob der Gang als Fluchtweg zugelassen ist, kann ein Grundriss allein nicht beweisen.

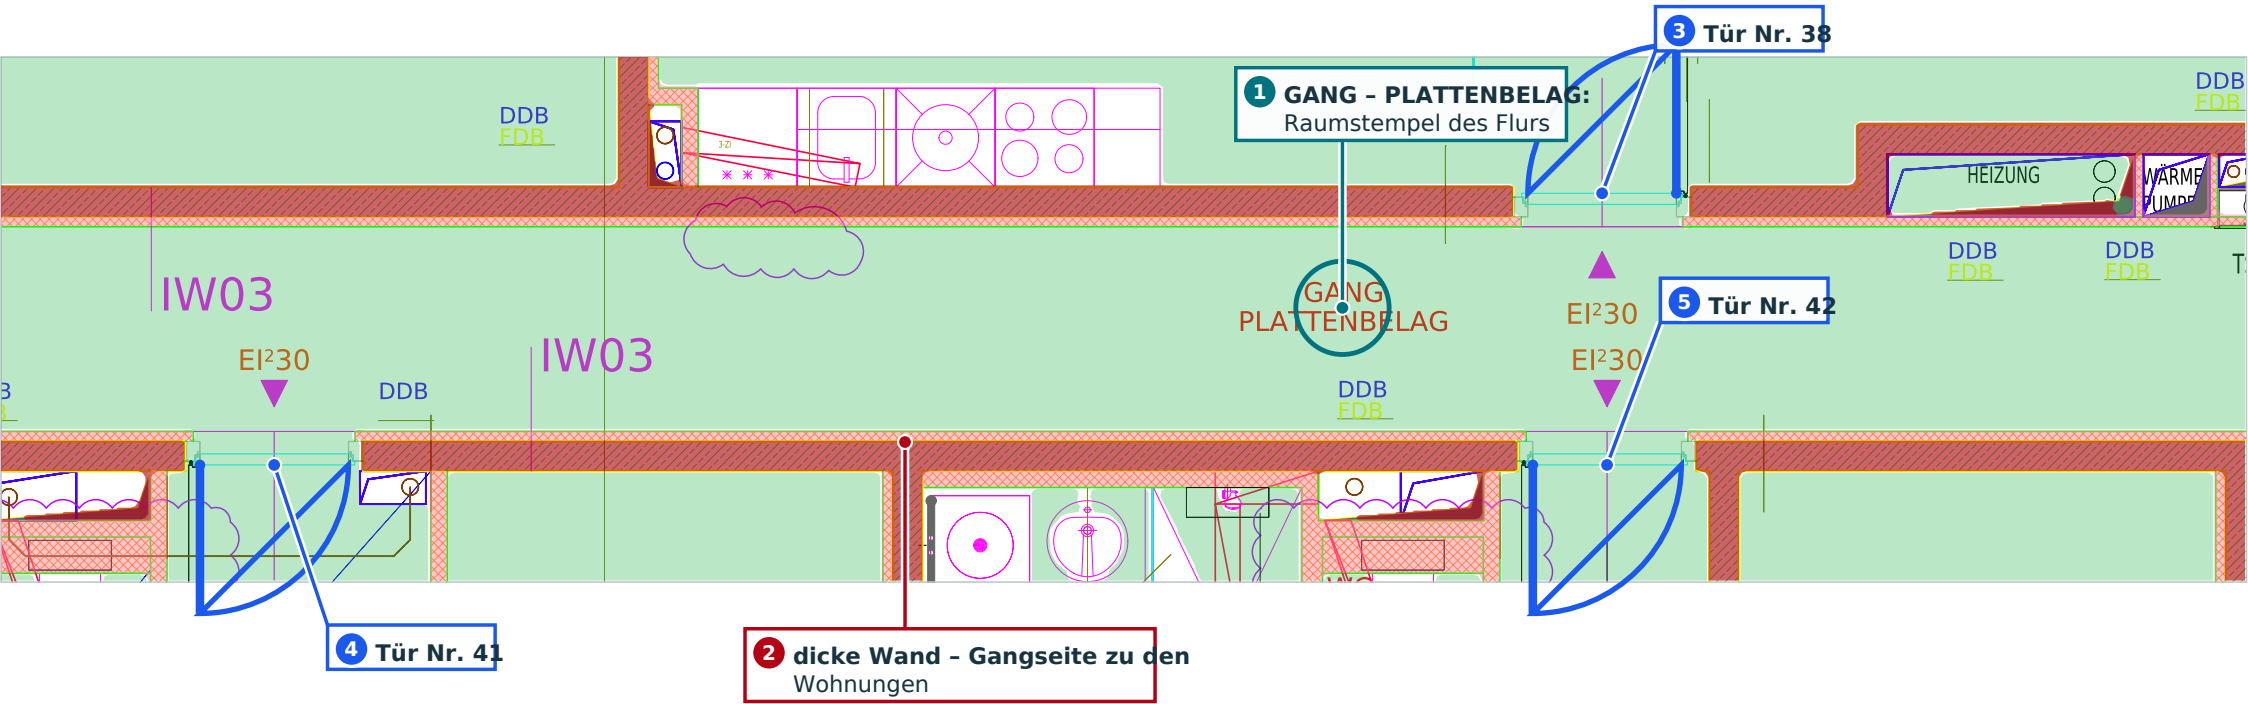

Hier bist du im Grundriss:

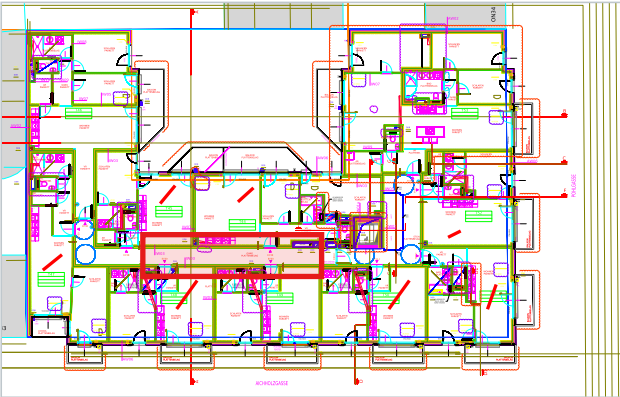

Draußen und doch begehbar: Balkon und Loggia

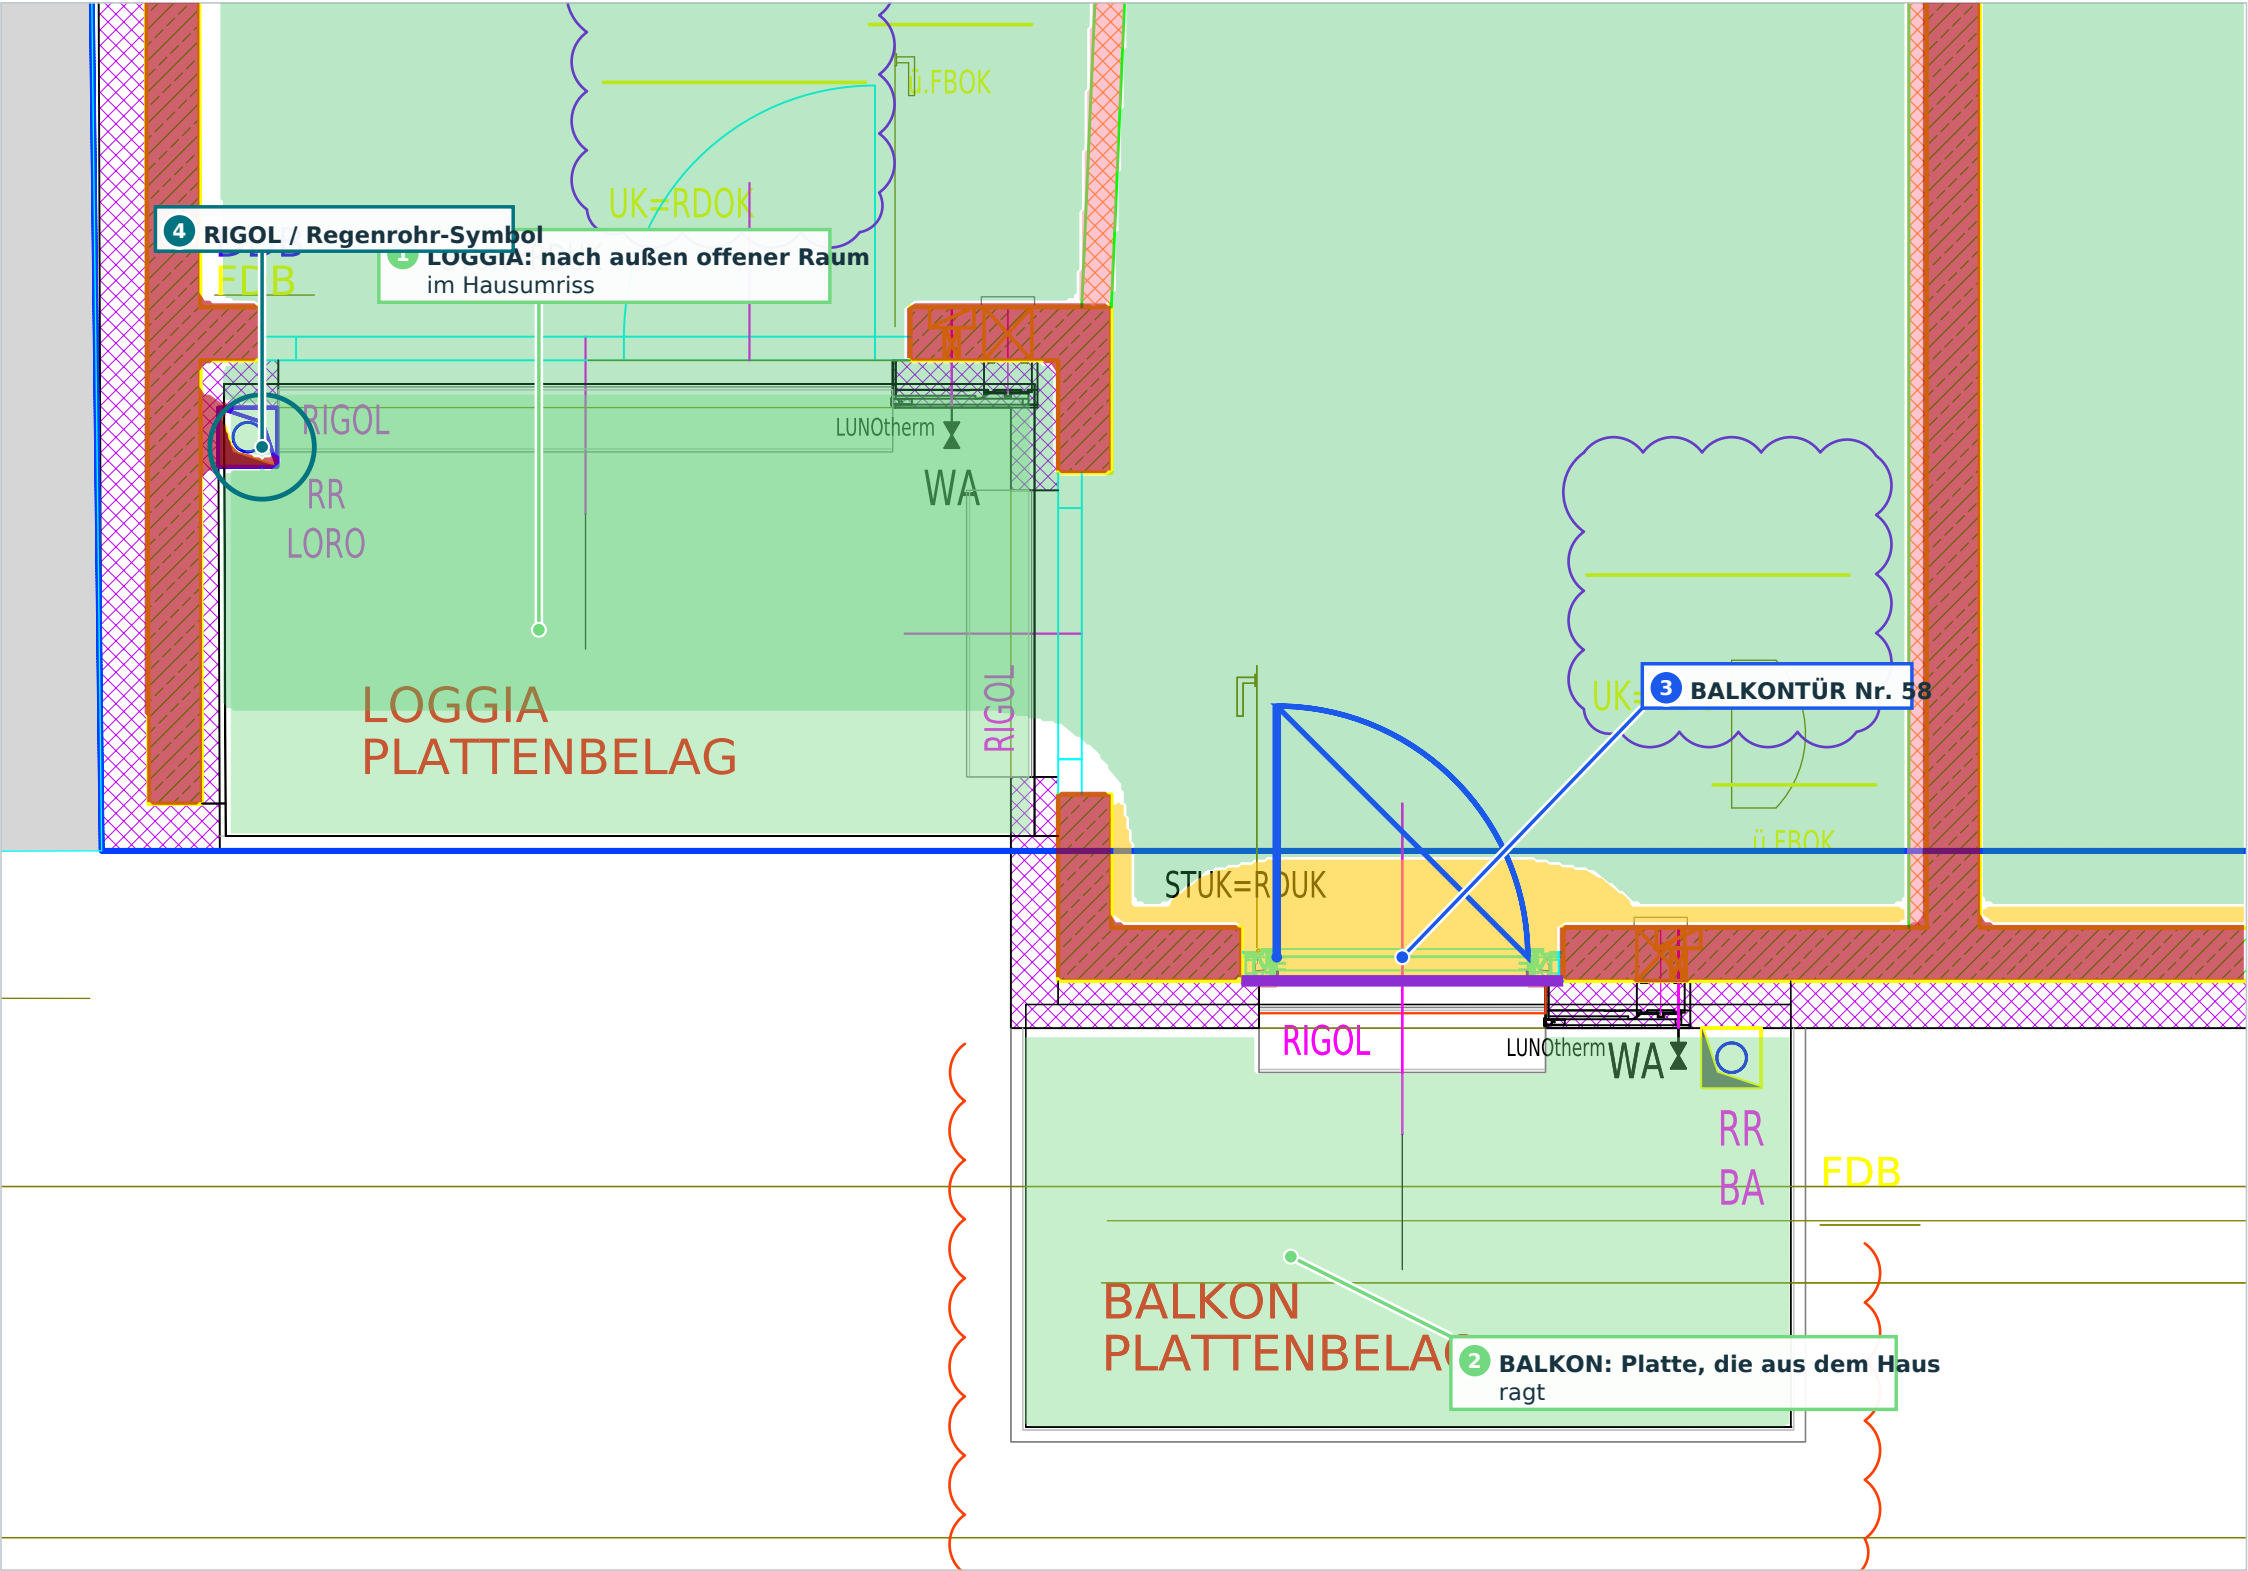

Balkon (2)

Was: eine Bodenplatte **außen** vor der Fassade, mit Geländer.
Wie im Plan: ein Rechteck aus grauen Linien außerhalb der Außenwand, darin **BALKON PLATTENBELAG**. **Zugang:** nur über die Balkontür (3).

Loggia (1)

Was: wie ein Balkon, aber **in** das Gebäude hineingeschnitten – an mehreren Seiten von Wänden umgeben, zu einer Seite offen.
Hier: links unten bei T47, Text **LOGGIA PLATTENBELAG**.

Warum hellgrün?


Man kann darauf gehen, aber es ist **draußen**. Und es ist eine Sackgasse – zurück geht es nur in die Wohnung.

Die Linien am Rand


Graue Doppellinien = Kante der Platte bzw. Geländer. Darüber hinaus führt kein Weg.

Lage und Höhe des Geländers sind im Grundriss nicht eindeutig angegeben.

Hier bist du im Grundriss:

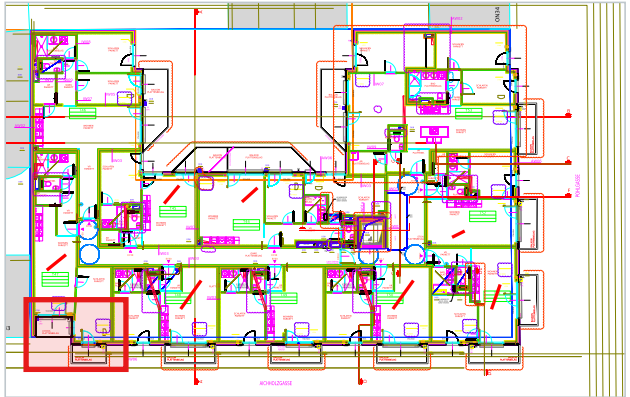

Was die Texte im Plan bedeuten - direkt am Beispiel

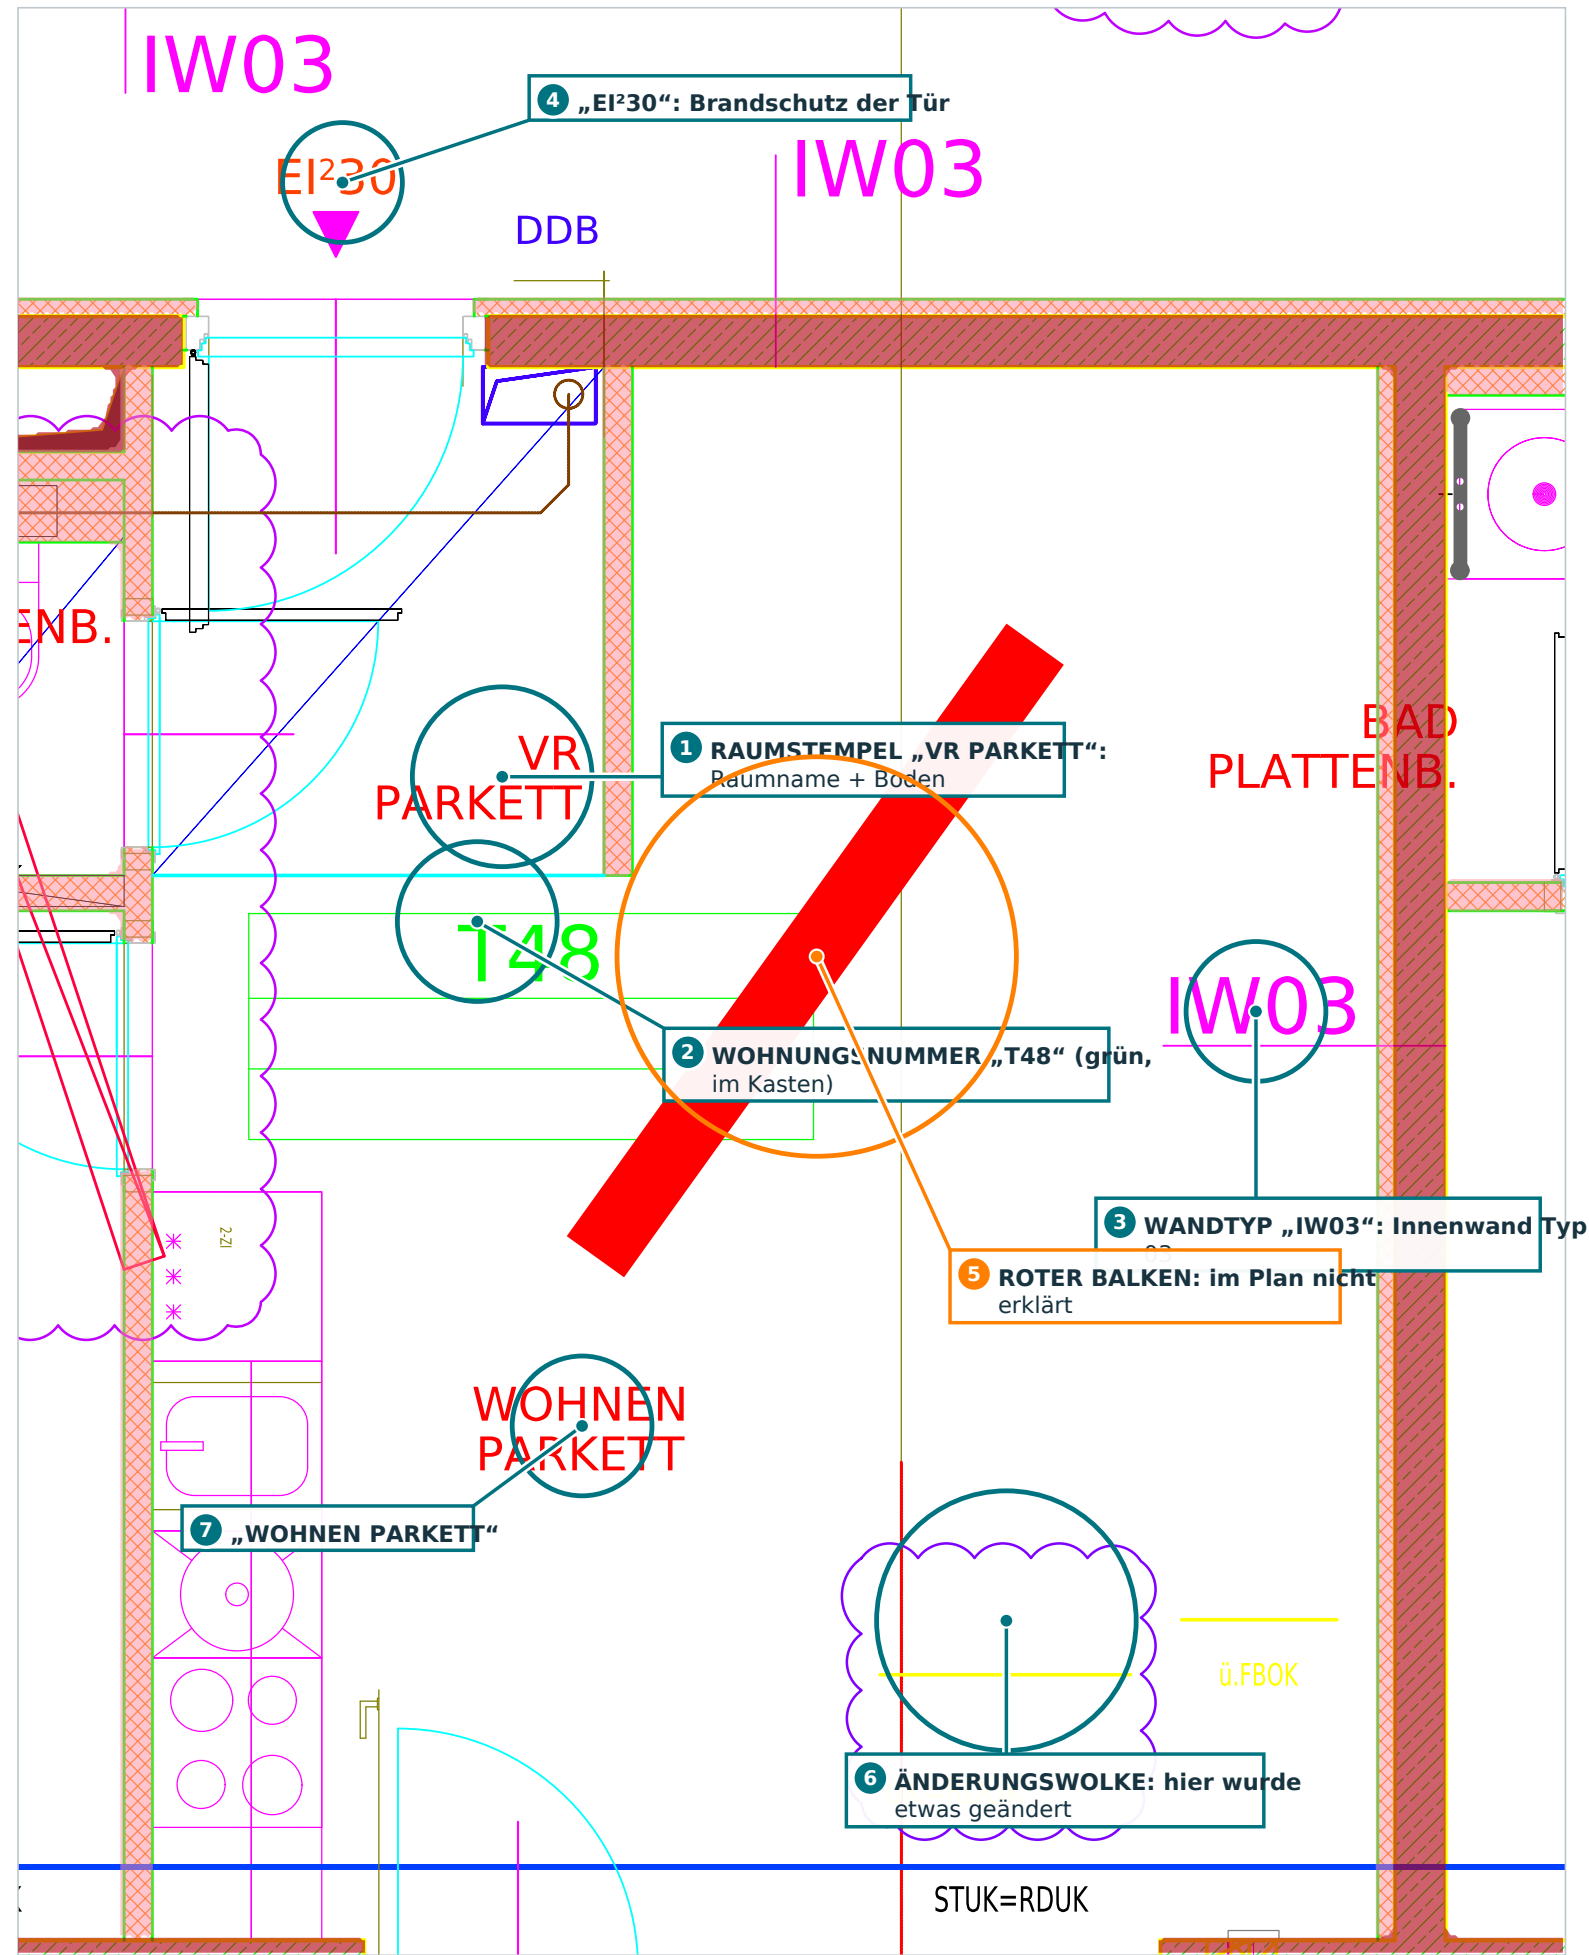

Schrift ist kein Bauteil

Texte und Symbole sind **Informationen**. Sie erklären, was an einer Stelle ist oder gemacht werden soll.

(1, 7) **Raumstempel** – rot, zweizeilig: Name + Bodenbelag.

(2) **Wohnungsnummer** – grün in einem Kasten. Die leeren Zeilen im Kasten sind vermutlich für weitere Angaben (z. B. Fläche) gedacht, hier leer.


(3) **Wandttyp** – magenta, **IW** = Innenwand, **AW** = Außenwand, plus Nummer.

(4) **EI²30** – Brandschutzklasse der Tür.


(6) **Wolke** – markiert Stellen, die seit der letzten Planfassung geändert wurden. Keine Wand, kein Möbel.

(5) **Die dicken roten Schrägbalken** gibt es in fast jeder Wohnung. Ohne Legende deute ich sie **nicht**. Sicher ist nur: Sie sind kein Bauteil, das man umgehen müsste.

Hier bist du im Grundriss:

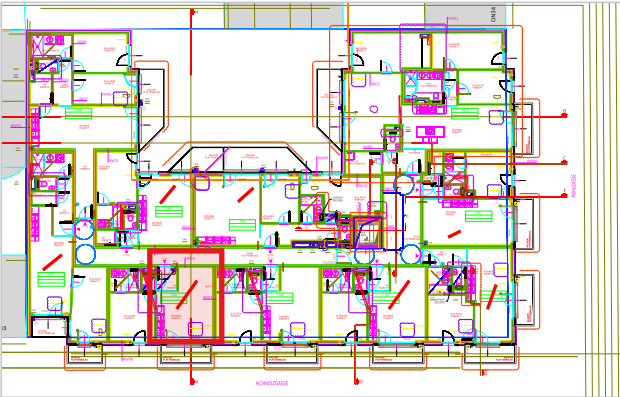

Hinweiszeichen im ganzen Plan

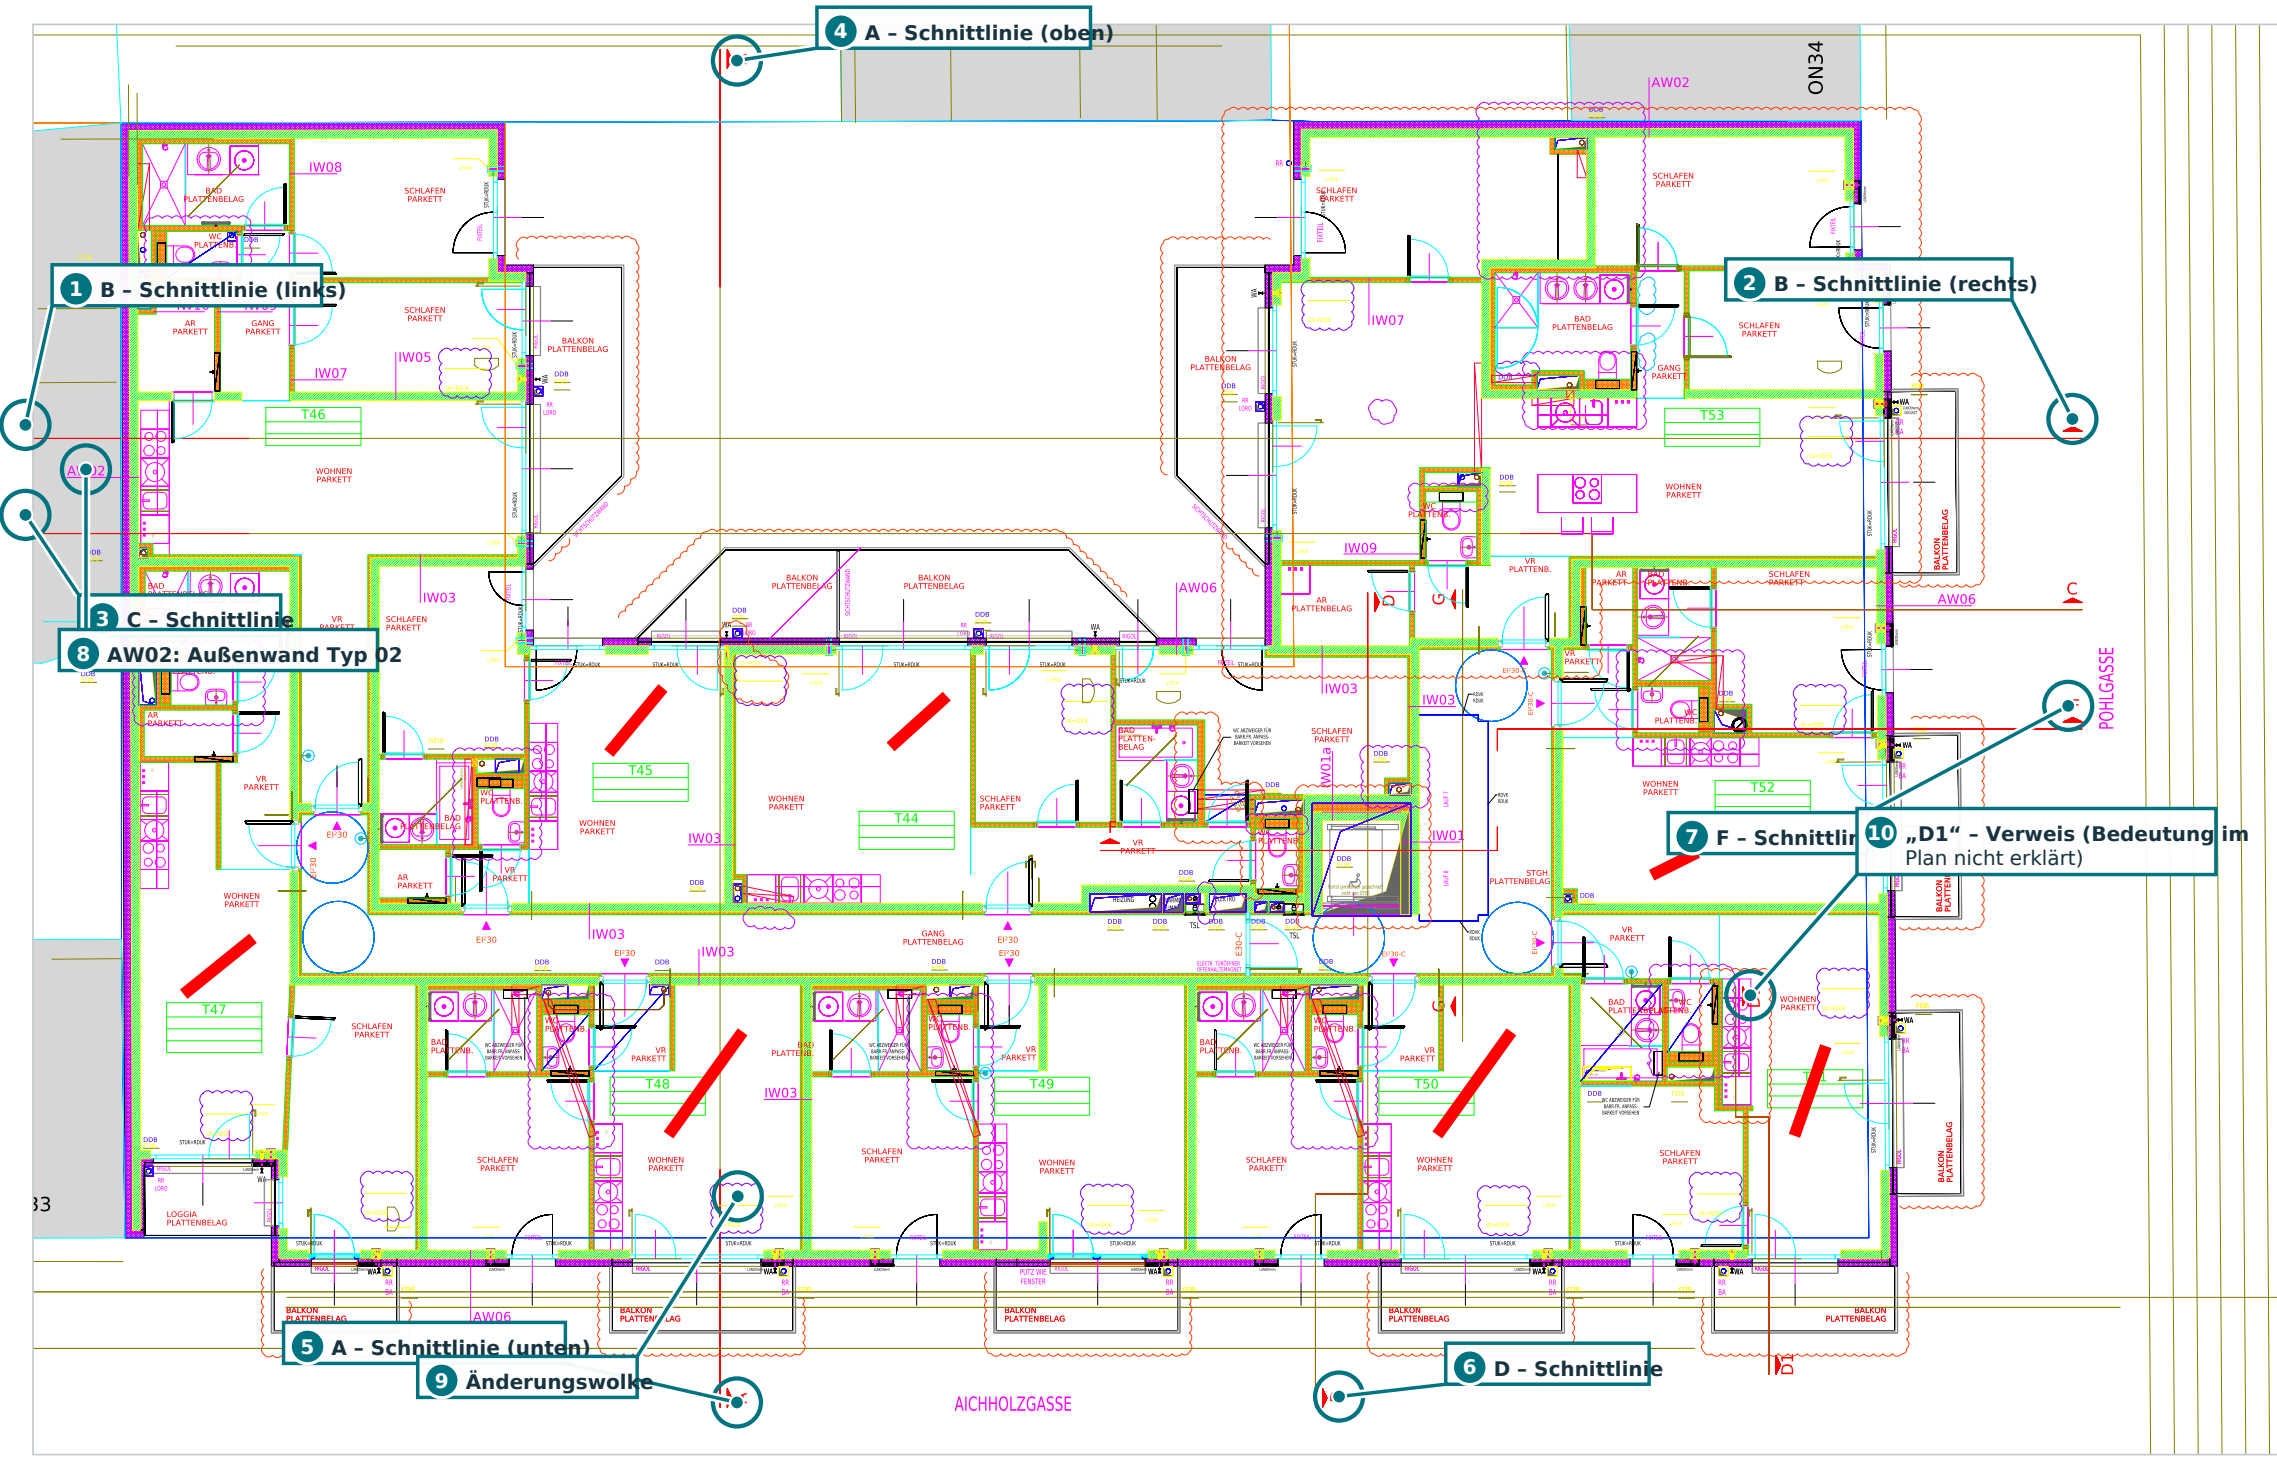

Zeichen, die auf andere Pläne verweisen

Ein Grundriss ist fast nie der einzige Plan eines Hauses. Viele Zeichen sagen: „**Schau in einem anderen Plan nach.**“

Schnittlinien (1–7): Ein Buchstabe mit einem Dreieck an den Enden einer langen dünnen Linie. Dort ist das Haus in einem anderen Plan **senkrecht** aufgeschnitten gezeichnet (wie eine aufgeschnittene Torte von der Seite). Das Dreieck zeigt die Blickrichtung. Hier gibt es die Schnitte A, B, C, D, F und G.

Wandtypen (8): AW = Außenwand, IW = Innenwand. Die Nummer verweist auf eine Liste mit dem Wandaufbau.


Änderungswolken (9): markieren geänderte Stellen.

(10) Bei „D1“ ist nicht eindeutig, ob es ein Detailverweis oder eine andere Markierung ist. Ebenso ist die dicke blaue Linie entlang der Fassade ohne Legende nicht sicher deutbar.

Die Linien selbst sind im Original sehr dünn und laufen über das ganze Blatt; eingekreist sind die Beschriftungen.


Typische Anfängerfehler: sieht aus wie eine Wand - ist aber keine

1. Änderungswolke

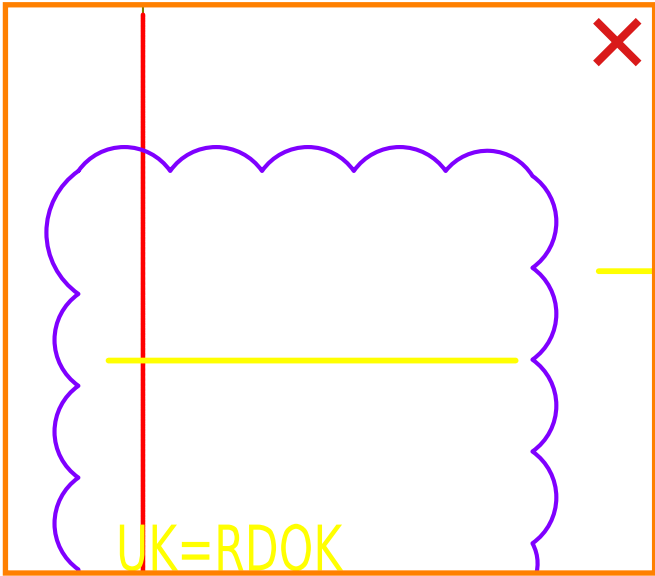


Sieht aus wie: eine runde Mauer.
Ist: eine Markierung „hier wurde geändert“. Wolkenförmige, dünne Linie.

2. Schnittrlinie

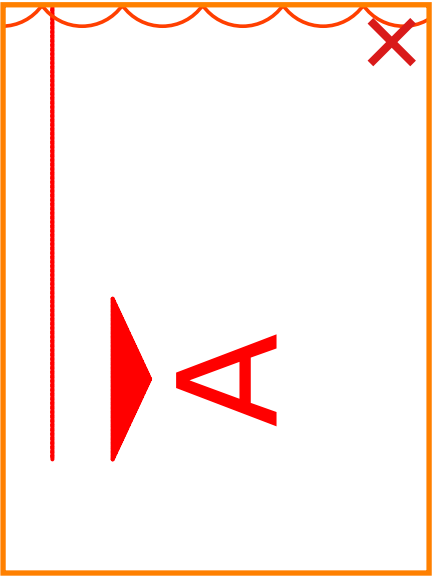


Sieht aus wie: eine lange dünne Wand.
Ist: ein Verweis auf einen Schnittplan. Erkennbar an Buchstabe und Dreieck am Ende.

3. Türbogen

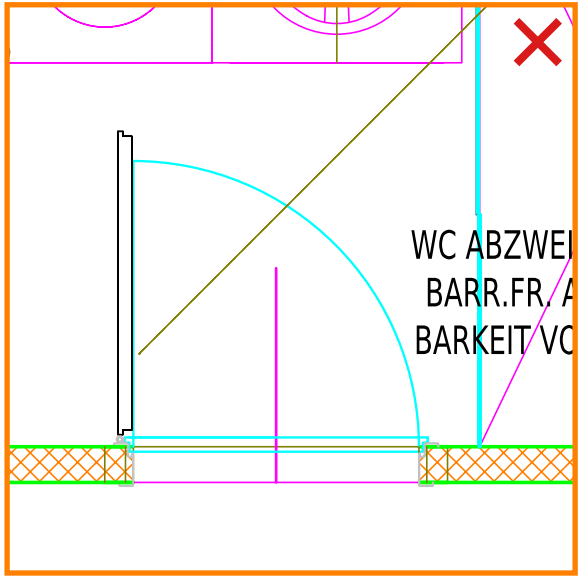


Sieht aus wie: eine gebogene Wand.
Ist: nur der Weg der Türkante. Dort ist sogar Platz zum Durchgehen.

4. Blaue lange Linie

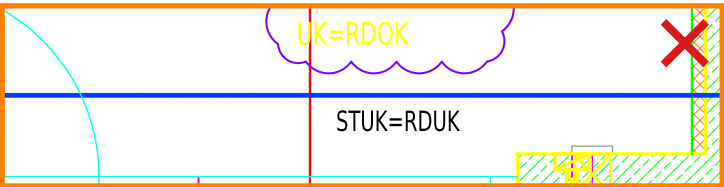


Sieht aus wie: eine Wandkante.
Ist: keine Wand im Schnitt; läuft ohne Muster durch Räume. Bedeutung ohne Legende unklar.

5. Nummernkasten

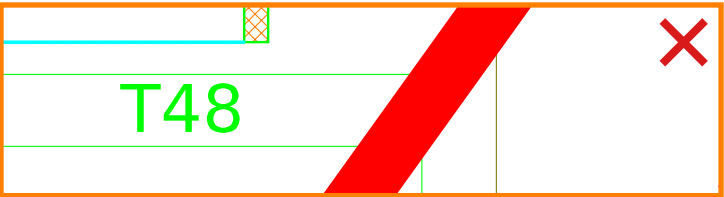


Sieht aus wie: ein kleines Zimmer.
Ist: der Kasten der Wohnungsnummer T48 – Schrift, kein Raum.

6. Roter Balken

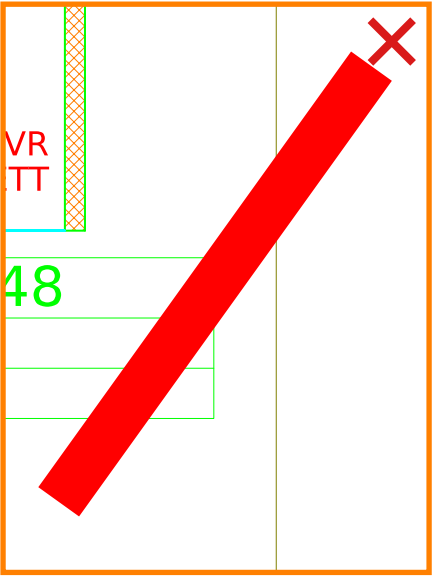


Sieht aus wie: ein schräges Bauteil.
Ist: ein Planzeichen ohne Legende. Keine Wand (kein Muster, keine Kanten).

7. Küchenzeile

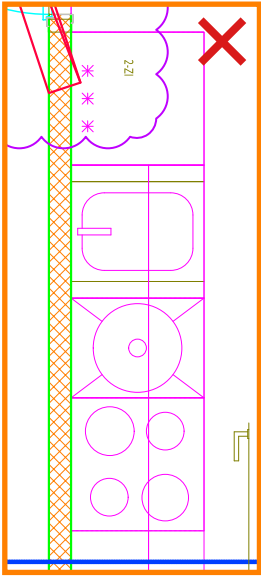

Sieht aus wie: eine dicke Wand.
Ist: Möbel, dünn gezeichnet, mit Kreisen (Herd) und Becken (Spüle).

8. Deckenöffnung

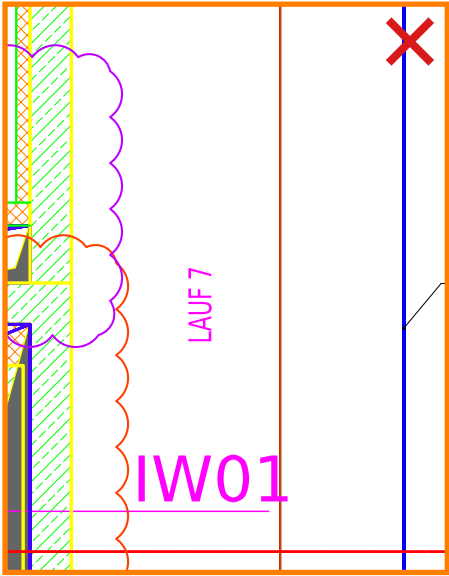


Sieht aus wie: ein leerer Raum.
Ist: das Loch in der Decke für die Treppe (Text LAUF). Kein ebener Boden.

Lexikon: alle Abkürzungen aus diesem Plan


Im Plan steht	Bedeutung in einfachen Worten	Wie sicher?
VR	Vorraum – Eingangsbereich der Wohnung	sicher
AR	Abstellraum	sicher (übliche Abkürzung)
WC / BAD	Toilette / Badezimmer	sicher
SCHLAFEN, WOHNEN	Schlafzimmer, Wohnzimmer	sicher
GANG	Flur, der die Wohnungen erschließt	sicher
STGH.	Stiegenhaus (Treppenhaus)	sicher
LAUF 7 / LAUF 8	Treppenlauf Nr. 7 und 8 (Treppenstücke ohne Unterbrechung)	sicher
PARKETT	Holzfußboden	sicher
PLATTENBELAG, PLATTENB.	Boden aus Fliesen oder Platten	sicher
BALKON, LOGGIA	begehbare Flächen im Freien	sicher
T44 ... T53	Top = Wohnungsnummer	sicher
IW01 ... IW10	Innenwand-Typ mit Nummer	sicher (Aufbau steht nicht im Plan)
AW02, AW06	Außenwand-Typ mit Nummer	sicher (Aufbau steht nicht im Plan)
EI²30	Brandschutz: 30 Minuten raumabschließend und wärmedämmend	sicher (Normbezeichnung)
EI²30-C	wie oben, zusätzlich selbstschließend	sicher (Normbezeichnung)
FIXTEIL	fest eingebautes Glas, geht nicht auf	sicher
RIGOL	Entwässerungsrinne vor Balkontüren	sicher
STUK=RDUK	Sturzunterkante = Rohdeckenunterkante	sehr wahrscheinlich
UK=RDOK, ü.FBOK	Unterkante = Rohdeckenoberkante; „über Fertigfußbodenoberkante“	wahrscheinlich
RDVK, RDUK	Rohdecken-Vorderkante / -Unterkante (an der Treppenöffnung)	wahrscheinlich
DDB / FDB	Deckendurchbruch / Fußbodendurchbruch (Loch für Leitungen)	wahrscheinlich
RR, LORO	RR = Regenrohr, LORO = vermutlich Herstellername	wahrscheinlich
WA	an der Fassade, nicht erklärt (evtl. Wasseranschluss)	unsicher
WÄRMEPUMPE, ELEKTRO	Beschriftung der Leitungsschächte	sicher
TSL	ohne Legende nicht eindeutig	unsicher
A.D. EI90	Brandschutz 90 Minuten an einem Bauteil im Kern; „A.D.“ unklar	teilweise unsicher
ELEKTR. TÜRÖFFNER	Tür wird elektrisch geöffnet (Beschriftung am Kern)	sicher
ON33, ON34	Bezeichnung der grauen Nachbargebäude/-grundstücke	wahrscheinlich
A, B, C, D, F, G	Schnittlinien (Verweis auf Schnittpläne)	sicher
D1	Verweis, Bedeutung nicht eindeutig	unsicher

Vergleich: 3. Obergeschoss und 4. Obergeschoss

3. Obergeschoss (Wände rot)

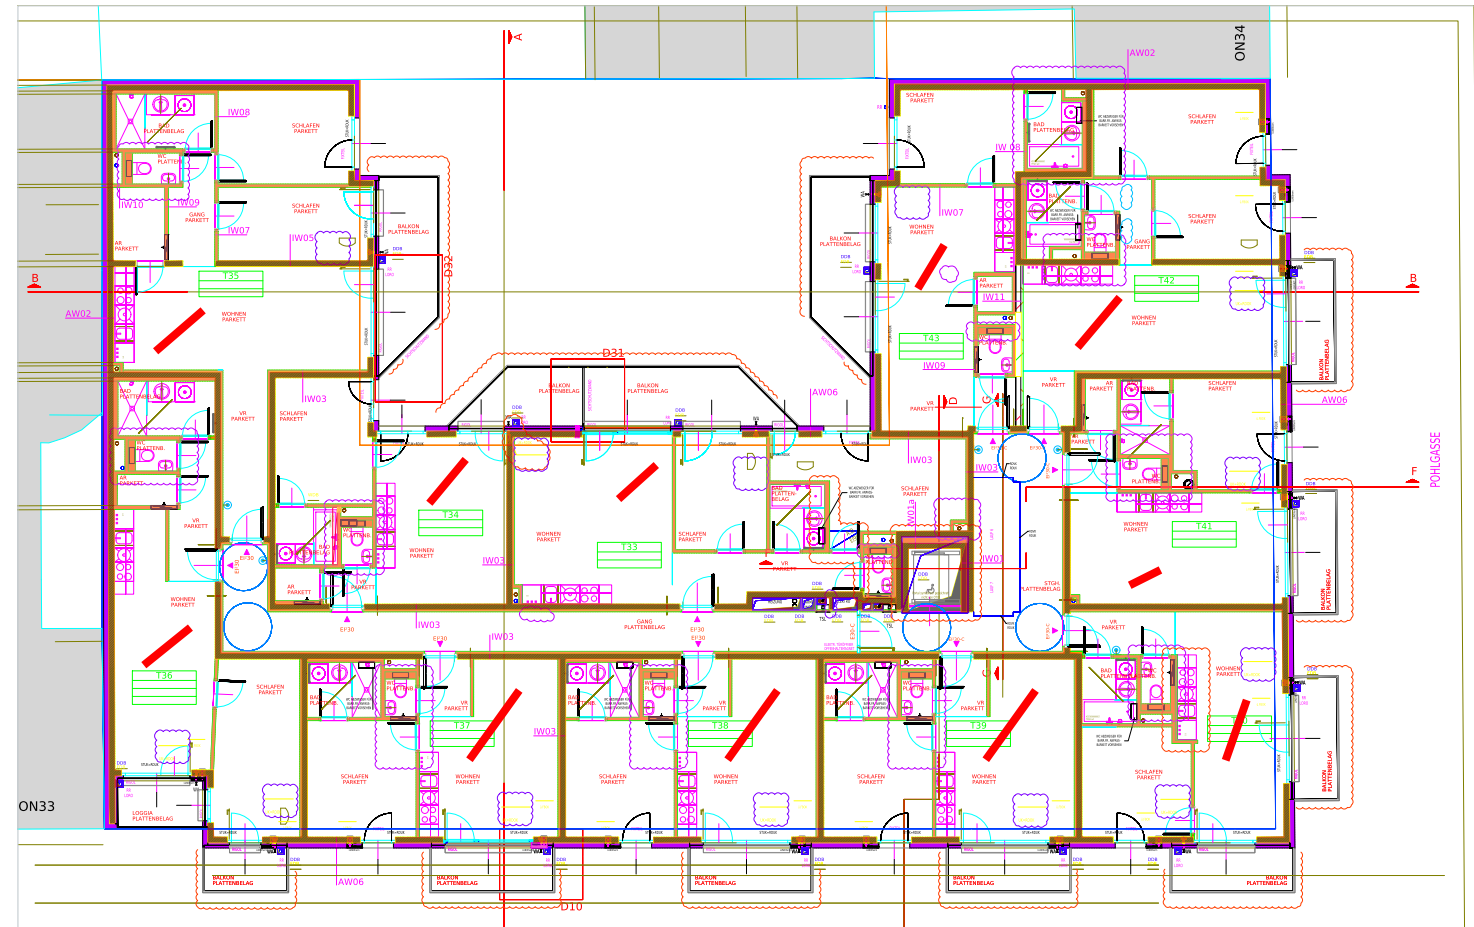

4. Obergeschoss (Wände rot)

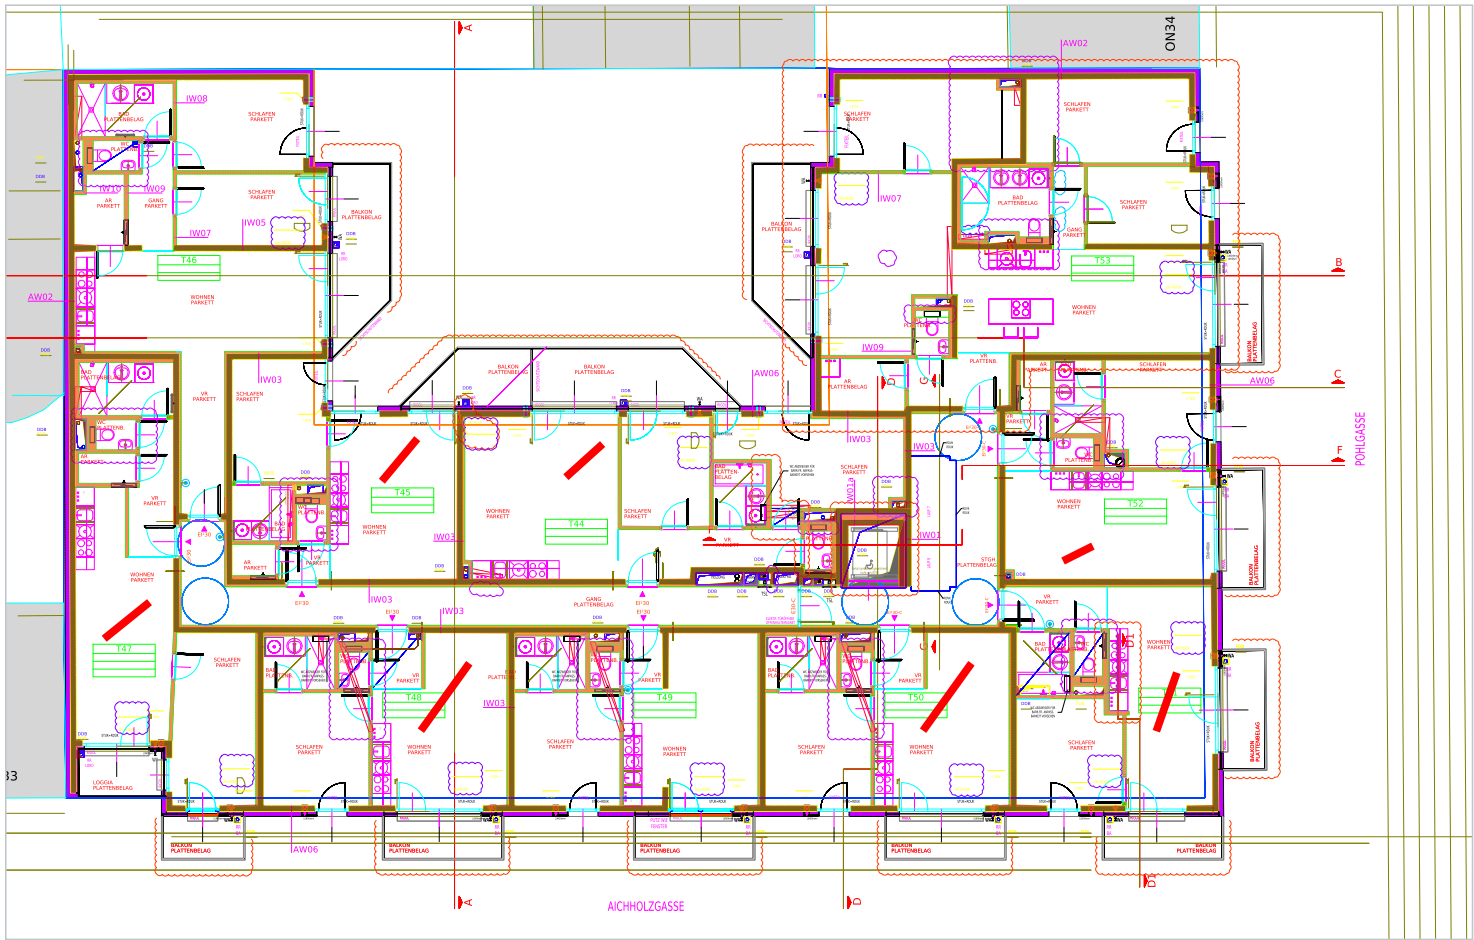

Warum vergleichen?

In einem Wohnhaus liegen die Stockwerke übereinander. Viele Dinge müssen genau übereinander liegen: **Stiegenhaus, Aufzug, Leitungsschächte** und die meisten **dicken Wände** (sie tragen die Stockwerke darüber). Wer zwei Geschosse vergleicht, versteht das Haus als Ganzes.

Gleich geblieben: Die U-Form, der Gang, das Stiegenhaus mit dem Aufzug in der Mitte, die Balkone zur Aichholzgasse und die meisten dicken Wände liegen an denselben Stellen.

Die Treppe zählt weiter: Im 3. OG steht an der Treppe „LAUF 6 / LAUF 7“, im 4. OG „LAUF 7 / LAUF 8“. Man erkennt daran, dass man ein Stockwerk höher ist.

Die Wohnungsnummern zählen weiter: 3. OG: T33 bis T43 (11 Nummern). 4. OG: T44 bis T53 (10 Nummern).

Unterschied im rechten oberen Flügel: Im 3. OG stehen dort zwei Wohnungsnummern (T42, T43), im 4. OG nur eine (T53). Die Wände sind dort anders angeordnet. Ob der Flügel im 4. OG eine einzige große Wohnung ist, lässt sich nur durch genaues Verfolgen der Türen bestätigen – gezählt habe ich die Nummernkästen.

Türen: Im 4. OG wurden 63 Türblätter erkannt (3. OG: 66).

Hinweis: Die beiden Pläne haben unterschiedliche Blattgrößen. Die Abbildungen hier sind jeweils einzeln eingepasst und nicht exakt deckungsgleich.

Fragen, die Anfänger wirklich stellen – und die Antworten

„Warum sind manche Linien bunt und manche schwarz?“

Das Programm des Planers ordnet jede Art von Linie einer Ebene (Layer) mit eigener Farbe zu: Wände, Türen, Möbel, Texte ... Die Farben im Original haben also eine Ordnung, sind aber nicht erklärt. Dieses Heft legt eine eigene, einfache Farbordnung darüber.

„Wo ist oben und unten im Haus?“

Ein Grundriss hat kein Oben und Unten – du schaust von oben drauf. „Oben“ auf dem Blatt heißt nur „weiter hinten auf dem Grundstück“. Orientierung geben die Straßennamen.

„Ist das Grüne ein Teppich?“

Nein. Grün ist nur die Lernfarbe für „hier kann man gehen“. Welcher Boden wirklich liegt, steht im Raumstempel (PARKETT, PLATTENBELAG).

„Warum ist die Tür offen gezeichnet?“

Damit man sieht, wohin sie aufgeht und wie viel Platz sie braucht. Das ist eine Zeichenregel, kein Zustand.

„Wie groß ist ein Zimmer?“

Das steht in diesem Plan nicht – er ist „ohne Maße“. Im Maßplan stehen Längen und Flächen.

„Kann ich durch ein Fenster auf den Balkon?“

Nur dort, wo ein **Türbogen** gezeichnet ist. Festes Glas (FIXTEIL) geht nicht auf.

„Warum gibt es keine Treppenstufen?“

In diesem Plan ist das Stiegenhaus nur als Öffnung mit LAUF-Nummern dargestellt. Die Stufen zeigt ein anderer Plan (Treppenplan oder Schnitt).

„Was ist der Unterschied zwischen Balkon und Loggia?“

Ein Balkon ragt aus dem Haus heraus. Eine Loggia ist in das Haus hineingeschnitten und an mehreren Seiten von Wänden umgeben.

„Welche Wand darf man herausreißen?“

Das sagt ein Grundriss nicht! Ob eine Wand tragend ist, steht im Tragwerksplan. Nie nur nach der Dicke entscheiden.

„Warum sind Bad und WC oft in allen Stockwerken gleich?“

Weil Wasser- und Abwasserleitungen senkrecht durch die Schächte laufen. Bäder liegen daher meist übereinander – vergleiche die Seite „3. OG und 4. OG“.

Was dieser Plan NICHT verrät

Ein guter Planleser weiß auch, **was fehlt**. Bei diesem Plan fehlt:

1. Maße

„ohne Masse“: keine Maßketten. Breiten und Längen sind nicht ablesbar.

2. Eine Legende

Farben und Muster sind nicht erklärt. Die Zuordnung „gelb/grün schraffiert = dicke Wand“ ist aus dem Plan selbst abgelesen: Diese Streifen verhalten sich überall wie Wände.

3. Tragende Wände

Stehen im Tragwerksplan, nicht hier.

4. Materialien

Nur über den Wandkatalog (IW/AW-Typen), der nicht beiliegt.

5. Höhen

Raumhöhen, Fenster, Schwellen: nur in Schnitten und Ansichten.

6. Treppenstufen

Nur Öffnung mit „LAUF 7 / LAUF 8“, keine Stufen, keine Laufrichtung.

7. Einige Zeichen

Rote Schrägbalken, dicke blaue Linie, „TSL“, „WA“, „A.D.“, „D1“: ohne Legende nicht eindeutig. Markiert, aber nicht gedeutet.

8. Der wirkliche Zustand

Der Plan zeigt, wie gebaut werden **soll** – nicht, ob Türen später offen oder Möbel anders stehen.

9. Fluchtwege und Barrierefreiheit

Grün ist Boden – keine geprüfte Freigabe als Fluchtweg oder für Rollstühle.

10. Wie die Farben entstanden sind

Wände, Türbögen, Wandöffnungen und Bodenflächen wurden aus der Vektorgeometrie des Original-PDFs abgeleitet (nach Linienfarbe und -art) und mit dem Original verglichen. Balkone wurden von ihrer Beschriftung aus bis zur Randlinie gefüllt. Kleine Abweichungen an Kanten sind möglich.

Merke: Wenn der Plan etwas nicht eindeutig zeigt, lautet die richtige Antwort „steht nicht im Plan“ – nicht raten.

Quiz: Was ist an den zwölf nummerierten Stellen?

So geht das Quiz

Links ist **keine Farbe** – nur das Original, wie in echt.

Frag dich bei jeder Nummer:


- 1. Was ist das?
- 2. Woran erkenne ich es?
- 3. Kann ich dort gehen?

Schreib deine Antworten auf. Die Lösungen stehen auf der nächsten Seite.

Zur Auswahl

Tür · dicke Wand · dünne Wand · Glas · Balkon · Aufzug · Leitungsschacht · Raumstempel · Küchenzeile · Gang · Treppenöffnung · Änderungswolke

Tipp: Seite „Die Sprache der Linien“ und „Typische Anfängerfehler“ helfen dir.

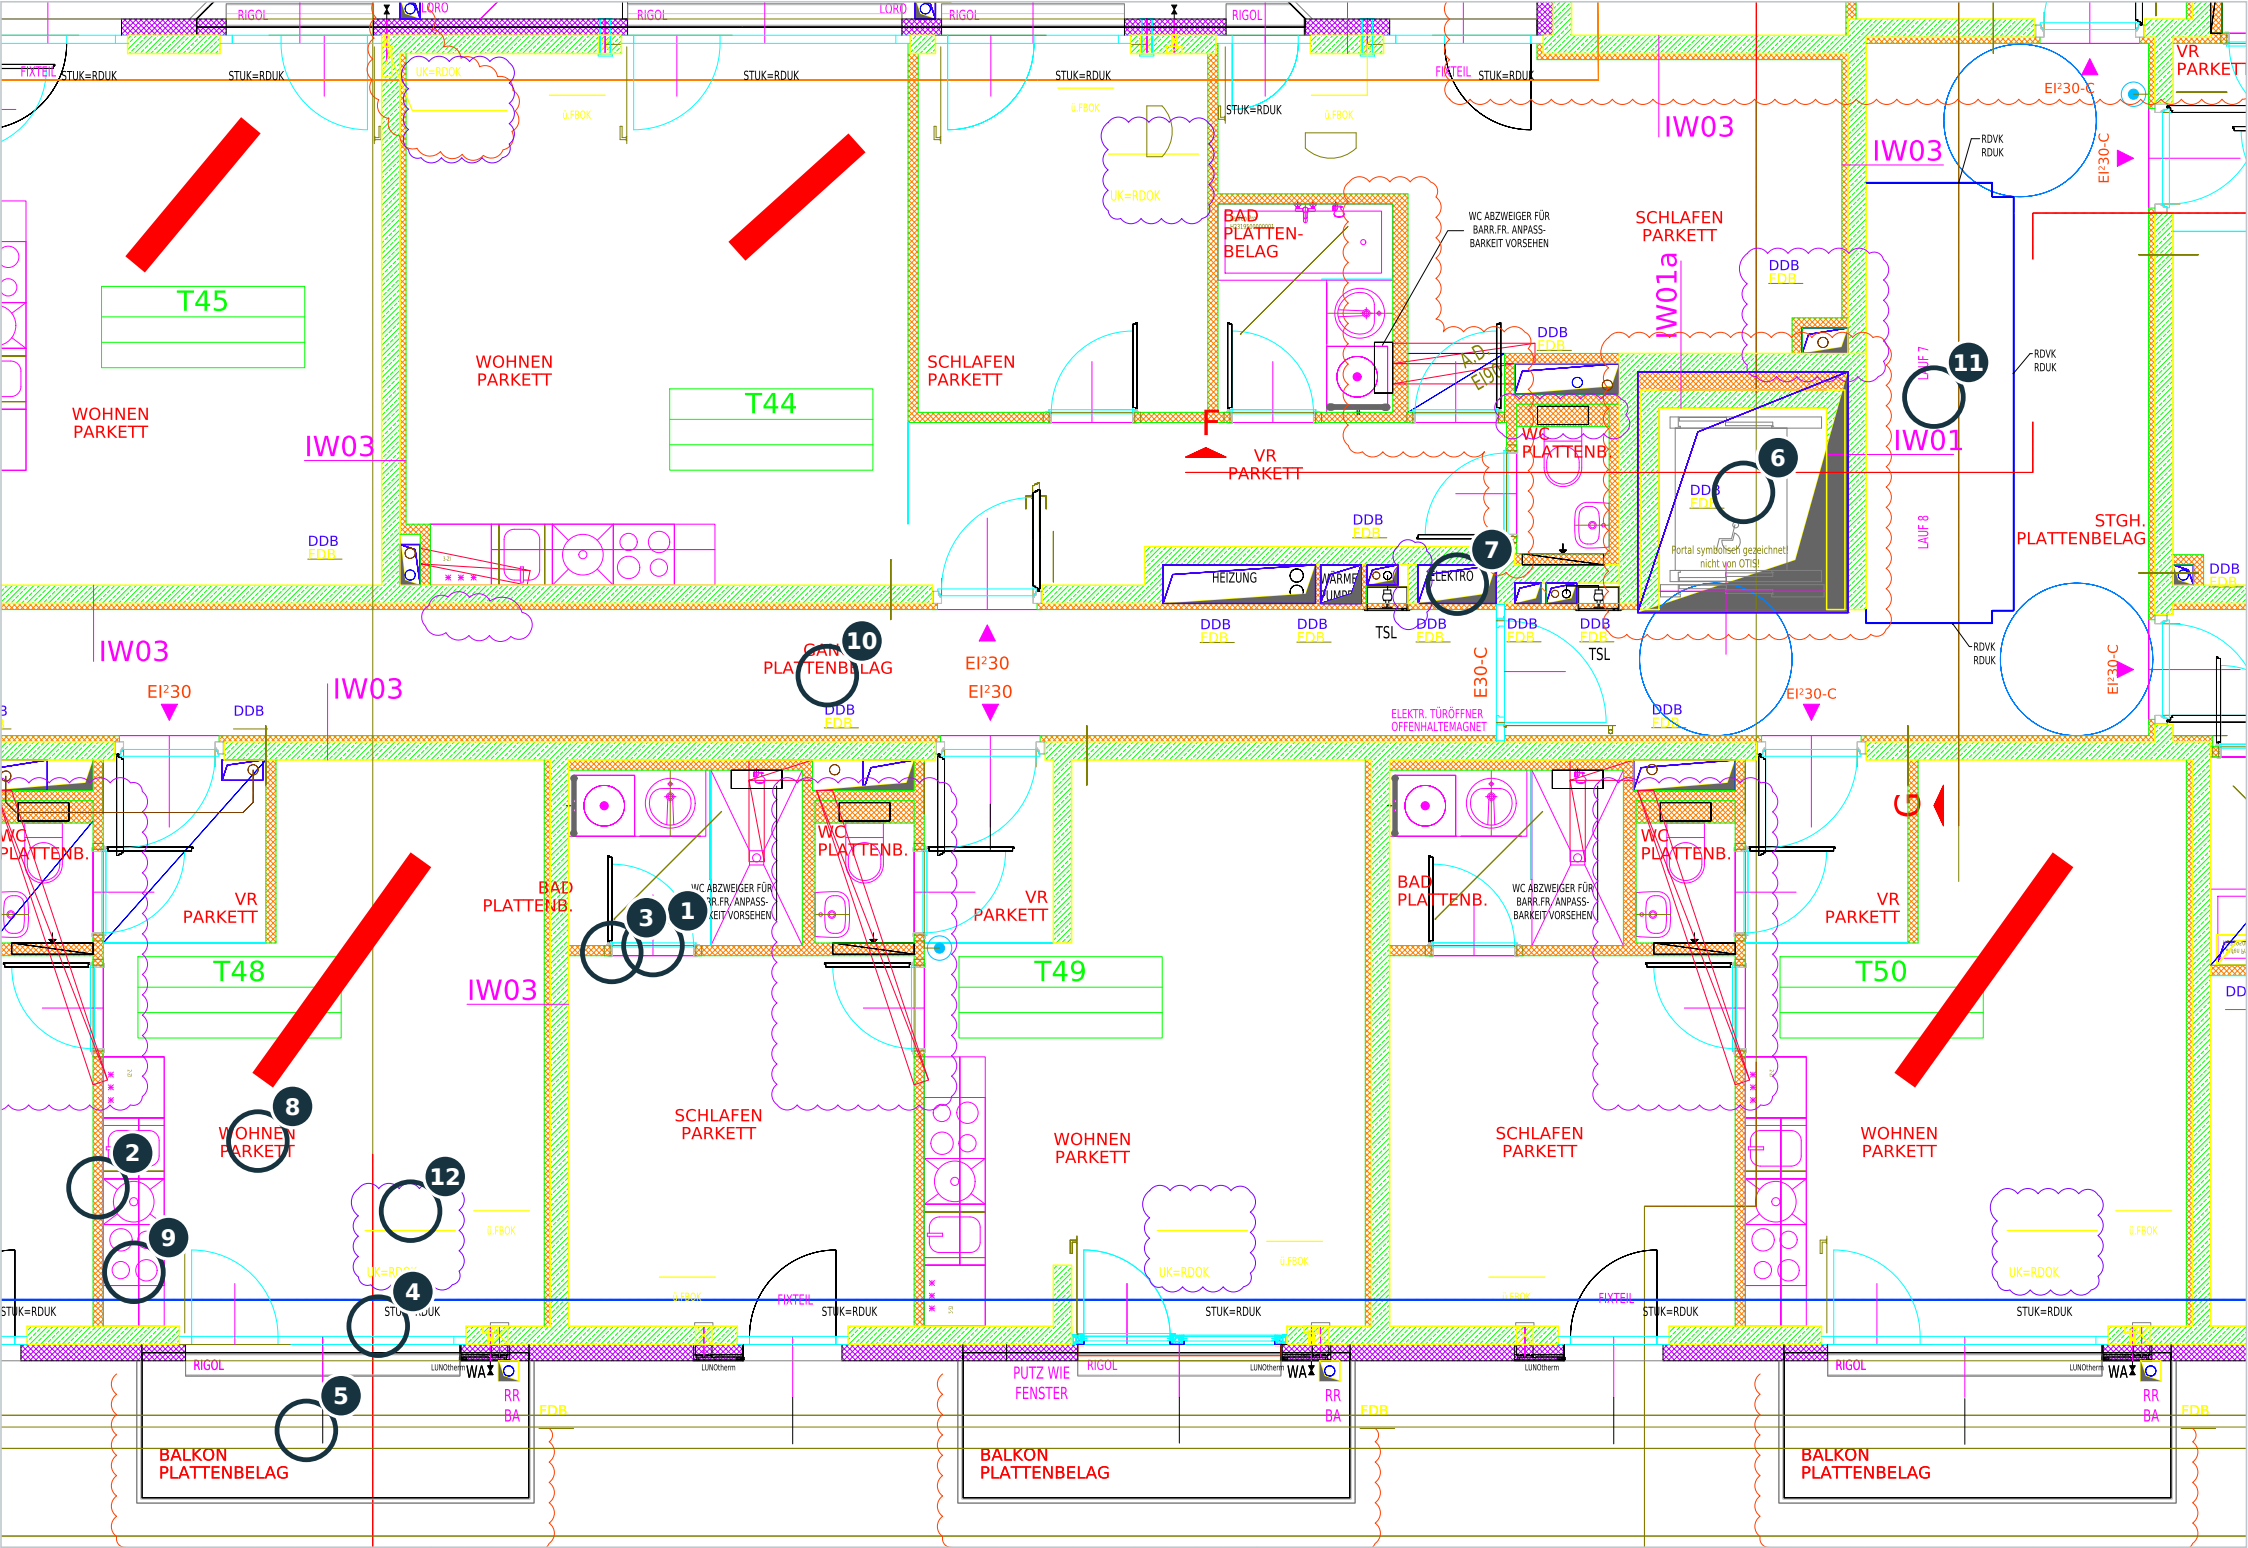



1. **Tür** – Lücke + Türblatt + Viertelkreis. *Begehrbar: ja (durch).*
 2. **dicke Wand** – gelbe Kanten, grüne Schrägstriche. *Begehrbar: nein.*
 3. **dünne Wand** – grüne Kanten, oranges Gitter. *Begehrbar: nein.*
 4. **Glas (Fixteil)** – dünne parallele Linien ohne Muster, kein Bogen. *Begehrbar: nein.*
 5. **Balkon** – außen, graue Randlinien, Text BALKON. *Begehrbar: ja.*
 6. **Aufzug** – Schacht mit Kabine und Rollstuhlsymbol. *Begehrbar: nein.*
 7. **Leitungsschacht** – Kästchen mit Schräglinie, Text wie ELEKTRO. *Begehrbar: nein.*
 8. **Raumstempel** – rote Schrift WOHNEN PARKETT. *Begehrbar: Text – darunter ist Boden.*
 9. **Küchenzeile (Herd)** – Rechteck mit vier Kreisen an der Wand. *Begehrbar: nein.*
 10. **Gang** – langer grüner Streifen zwischen dicken Wänden. *Begehrbar: ja.*
 11. **Treppenöffnung** – blauer Umriss mit Text LAUF. *Begehrbar: nur über die Treppe.*
 12. **Änderungswolke** – dünne Wellenlinie – keine Wand. *Begehrbar: Zeichen – darunter ist, was dort gebaut ist.*
- 10 oder mehr richtig? Dann kannst du diesen Grundriss lesen.

Checkliste: So liest du jeden Grundriss

Schritt 1 – Überblick

Plantitel suchen (hier unten rechts: „4. OBERGESCHOSS“). Welches Stockwerk? Wo sind Straßen und Nachbarhäuser?

Schritt 2 – Außenwand finden

Die äußerste dicke, gemusterte Linie rund um das Haus. Alles darin ist innen.

Schritt 3 – Innenwände verfolgen

Streifen mit zwei Kanten und Muster. Dicke trennen meist Wohnungen, dünne trennen Zimmer.

Schritt 4 – Türen suchen

Lücke + gerade Linie + Viertelkreis. Der Bogen zeigt, wohin die Tür aufgeht.

Schritt 5 – Fenster und Glas

Lücke in der Außenwand mit dünnen Linien. Bogen = Glastür, kein Bogen = festes Glas.

Schritt 6 – Nicht reinlegen lassen

Wolken, Schnittlinien, Nummernkästen, Balken und Möbel sind keine Wände (Seite „Anfängerfehler“).

Schritt 7 – Räume benennen

Raumstempel: Name oben, Bodenbelag unten.

Schritt 8 – Kern finden

Treppe (Stufen oder Öffnung mit „LAUF“), Aufzug (Schacht mit Kabine), Leitungsschächte (Kästchen).

Schritt 9 – Wohnungen abgrenzen

Vom Gang durch eine Eingangstür – alle erreichbaren Räume ohne zurück in den Gang = eine Wohnung.

Schritt 10 – Weg gehen

Mit dem Finger vom Stiegenhaus über den Gang durch Türen in die Räume. Nie durch Wand, Glas oder Schacht.

Schritt 11 – Grenzen kennen

Was nicht eindeutig im Plan steht, als „unklar“ markieren. Höhen, Material, Tragwerk stehen in anderen Plänen.

Der Abschlusstest

Nimm die Seite „Der Originalplan – unverändert“ und zeige ohne Farben: Wo hat die Wohnung **T49** ihre Eingangstür, ihr Bad, ihre Küche und ihren Balkon? Wenn du das kannst: Gratulation – du liest Grundrisse.